


标识系统：让“人有最终决定权”可被看见

原创概念标识、颜色、应用规则与证据字段；不代表主办方或政府徽标

v0.2 · 概念建议

概念标识 / CONCEPT MARK

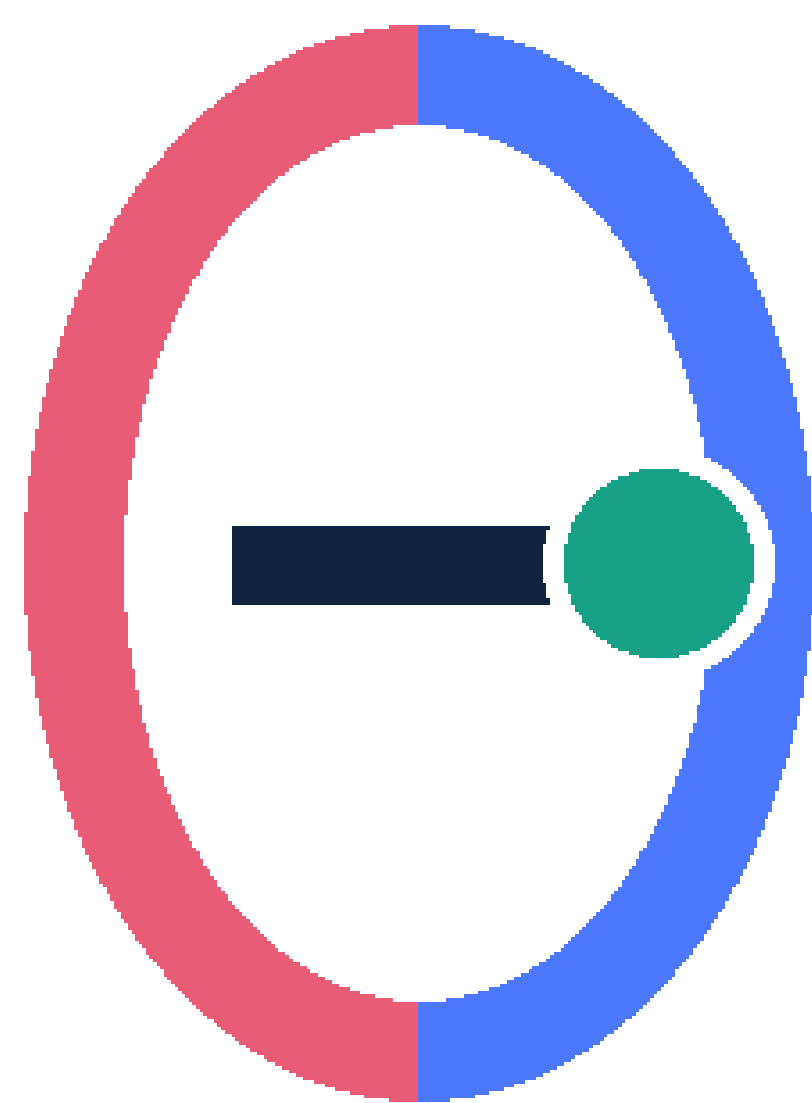

京张人本城市操作系统

从 AI 展台到 AI 时代人的城

- 开放括号：可调用接口
- 轨道线：百年连续性
- 人工确认点：最终决定权在人
- 红色：停止/申诉；蓝色：受约束的机器接口；绿色：硬约束；橙色：外溢

颜色与应用规则



人的尊严 / stop



机器可调用 / interface



算电气候 / limits



势能外溢 / spillover



版本记录 / readable record

每张空间卡必须同时显示：

空间动作

受影响人群

人工替代

进入证据

停止条件

版本/责任类别/更新时间


任务书—空间响应一页图

三大定位 · 五大功能 · 三区两翼 · 四条差异化价值链

PACKAGE v1.9

CONCEPT / PROVISIONAL

三大定位

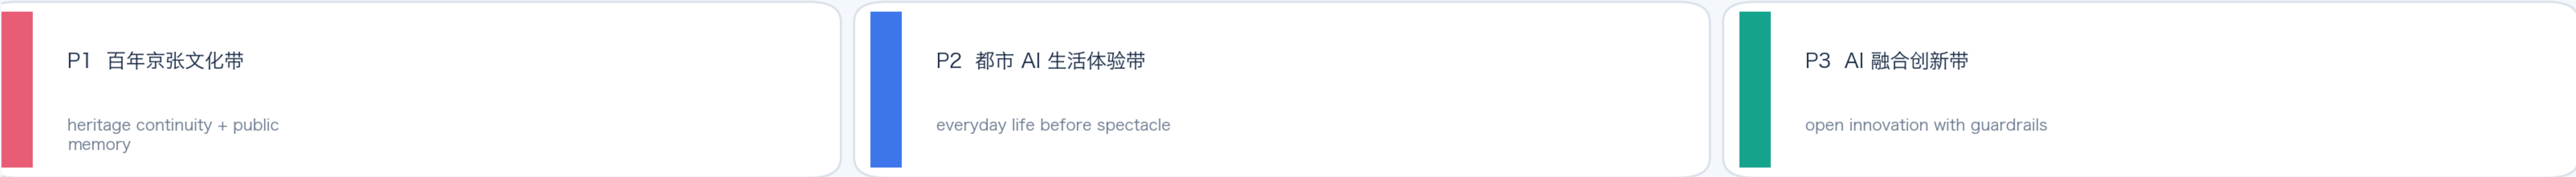

五大功能



三区两翼：把任务书落到空间动作



四条差异化主线 → 最短证据路径



所有空间建议均为概念建议 / 参考方案，供专业团队深化研究；边界为 official_boundary=false、geometry_role=provisional_constraint。图中证据是包内可回读路径，不是官方评分、现场结果或实施授权。

人本城市操作系统 | 城市 API 六步可回放序列

目录 → 授权 → 调用 → 日志 → 审计 → 退出 · 仅为概念证据

PACKAGE v2.3

概念 / 未授权 / 未运行



回放契约 / 评审者可核对什么

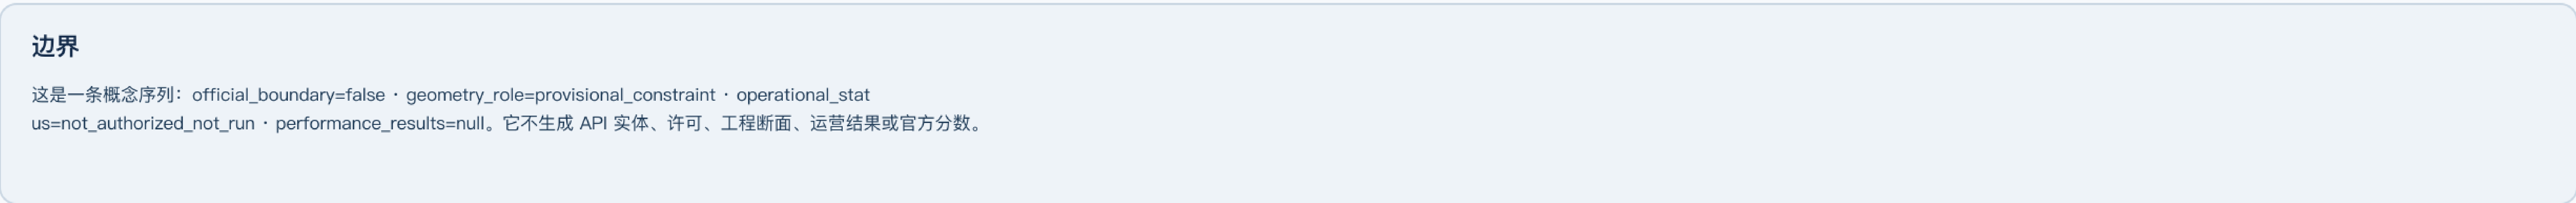


图 07

资料就绪度：把“缺什么”变成可关闭的发布门

7 条资料路径连接假设、场景、指标和回退动作；资料缺失时保持 unknown 或概念状态。

DR-01

空间、权属与可逆空间底图

任一空间化研究前

最低资料

清权 GIS/CAD · 坐标/范围 · 版本/权利

缺失时

保留临时几何；不作官方红线或法定控制结论

DR-02

社区保留与就业转型基线

v0.1 基线后

最低资料

经同意基线 · 带薪路径 · 预先声明随访

缺失时

空间值仍为概念；保留、就业和工资结果为 unknown

DR-03

人工通道与无障碍等效性

数字服务主张前

最低资料

服务目录 · 同等替代 · 无障碍走读

缺失时

保留人工/电话/纸本；等效性与可及性为 unknown

DR-04

城市 API、公共数据与治理授权

v0.2 受限试点前

最低资料

授权目录 · 影响评估 · 日志/接管/退出

缺失时

仅模拟/匿名/纸面协议；不处理真实敏感数据

DR-05

人机通行、低空与事故安全

v0.2 受限试点前

最低资料

许可路径 · 行人优先/停机 · 保险/演练

缺失时

仅概念服务廊；不作路权、低空或机器人安全主张

DR-06

算电、绿电与余热计量

v0.2 审核前

最低资料

IT 负荷 · 计量边界 · 绿电凭证 · 热需求

缺失时

保留政策门与审计概念；PUE/绿电/余热为 unknown

DR-07

小月河水文、蓝线与气候校准

v0.2 审核前

最低资料

蓝线 · 排水/事件资料 · 校准模型

缺失时

仅概念蓝绿公共空间；不作行洪、排水或内涝效益主张

统一触发

可追溯输入 → 全量重算 → 专业复核

只有资料来源、允许用途、范围、时间、版本和专业复核可追溯，才可替换概念输入；空间输入变化先重算几何、指标、图件、HTML、PDF 与 self-check。

图件由 geometry/*.geojson 与结构化证据派生；普通人服务链、空间接口、人本验收图谱和评审导航均只做离线引用或路径核验与预期 FAIL 负测，资料不足仍为 unknown 或概念状态。

人本城市验收图谱：谁能进入、谁能停止

六类使用者、16 张场景卡、临时空间锚点与三段发布门在一张图中重解；不是服务运营面板或实施承诺。

16完整场景卡

6人物路径

10代表性场景链接

3发布门

P-01原住民、租住者与老人

使用者SC-A01 / SC-A03锚点SC-A01

人本底线人工/纸本/电话通道、可理解的协商与退出、不得以空间代理冒充真实保留率。

人工替代纸本、电话和现场人工咨询始终可用。

停止 / 回退无知情同意、无法解释资格或出现排斥性影响时，停止展示和收集。

P-02被替代风险劳动者

使用者SC-A02锚点SC-A02

人本底线自愿参加、人工咨询、可删除记录、不以培训人次替代就业结果。

人工替代可跳过自动匹配并获得人工职业咨询。

停止 / 回退若只统计到课而无岗位路径，或自动分流造成歧视，暂停并修订。

P-03夜班 AI 从业者与夜间服务人员

使用者SC-A04锚点SC-A04

人本底线不持续定位、不做情绪画像、匿名反馈可用。

人工替代现场求助、人工陪行和匿名反馈优先于持续定位。

停止 / 回退无人工求助、无安全核验或存在追踪风险时，停止相关技术功能。

P-04OPC、小商户与小团队

使用者SC-D01 / SC-D03锚点SC-D01

人本底线不以平台评分替代人工协商；不指定供应商或企业名单。

人工替代人工申请、解释和争议处理不被平台评分取代。

停止 / 回退若形成封闭俱乐部或绑定供应商，暂停并重设规则。

P-05公共服务人员与数据责任人

使用者SC-B01 / SC-B04 / SC-C04锚点SC-B01

人本底线AI 不得自主作出规划许可、断供、执法或个人权利决定。

人工替代人工复核、撤销授权和非数字服务并列。

停止 / 回退未授权访问、不可解释输出或无接管能力即冻结。

P-06行动不便者、照护者与低数字能力使用者

使用者SC-A03 / SC-B02 / SC-D03锚点SC-B02

人本底线每个数字入口应有同等人工替代；无障碍使用者参与走读与复盘。

人工替代行人优先、人工陪同和一键停机。

停止 / 回退任何接触、险情、投诉或无许可状态均回到纸面协议。

临时几何走廊图

16 个点 = 完整场景清单；P1-P6 = 人物路径的代表性临时锚点。

地图仅为提交临时几何的概念阅读，不是服务点、道路或工程定位。

三个共同发布门：缺证据就停在概念状态

v0.1观察、基线与公众共识

不通过发现误导性宣传、无人工通道、未经同意的资料使用或无法解释的群体伤害时，撤下相关展示并修订。

v0.2可逆试点与独立评估

不通过出现安全事件、未授权数据、能源或气候证据不足、无障碍障碍、公众反对或不可撤回风险时，停止场景并回到资料补齐或纸面协…

v1.0经审查后扩展与标准外溢

不通过若证据不可复核、公共利益不成立、群体权益受损或基础条件变化，撤回扩展建议在 release note 说明原因。

图件由 geometry/*.geojson 与结构化证据派生；普通人服务链、空间接口、人本验收图谱和评审导航均只做离线引用或路径核验与预期 FAIL 负测，资料不足仍为 unknown 或概念状态。

图 08

人机接口原型：把停止动作放进空间层

两种非尺度化概念接口：人工优先、资料门与独立复核先于测试；不是工程断面、道路红线或运行许可。



图件由 geometry/*.geojson 与结构化证据派生；普通人服务链、空间接口、人本验收图谱和评审导航均只做离线引用或路径核验与预期 FAIL 负测，资料不足仍为 unknown 或概念状态。



三处重点区

Three focus areas

每个放大框都回指同一临时 geometry，并把动作、人工边界与机器边界并列 · each zoom returns to the same provisional geometry; actions sit beside human and machine boundaries

PACKAGE v1.7
CONCEPT / PROVISIONAL


03 / 位置与关系

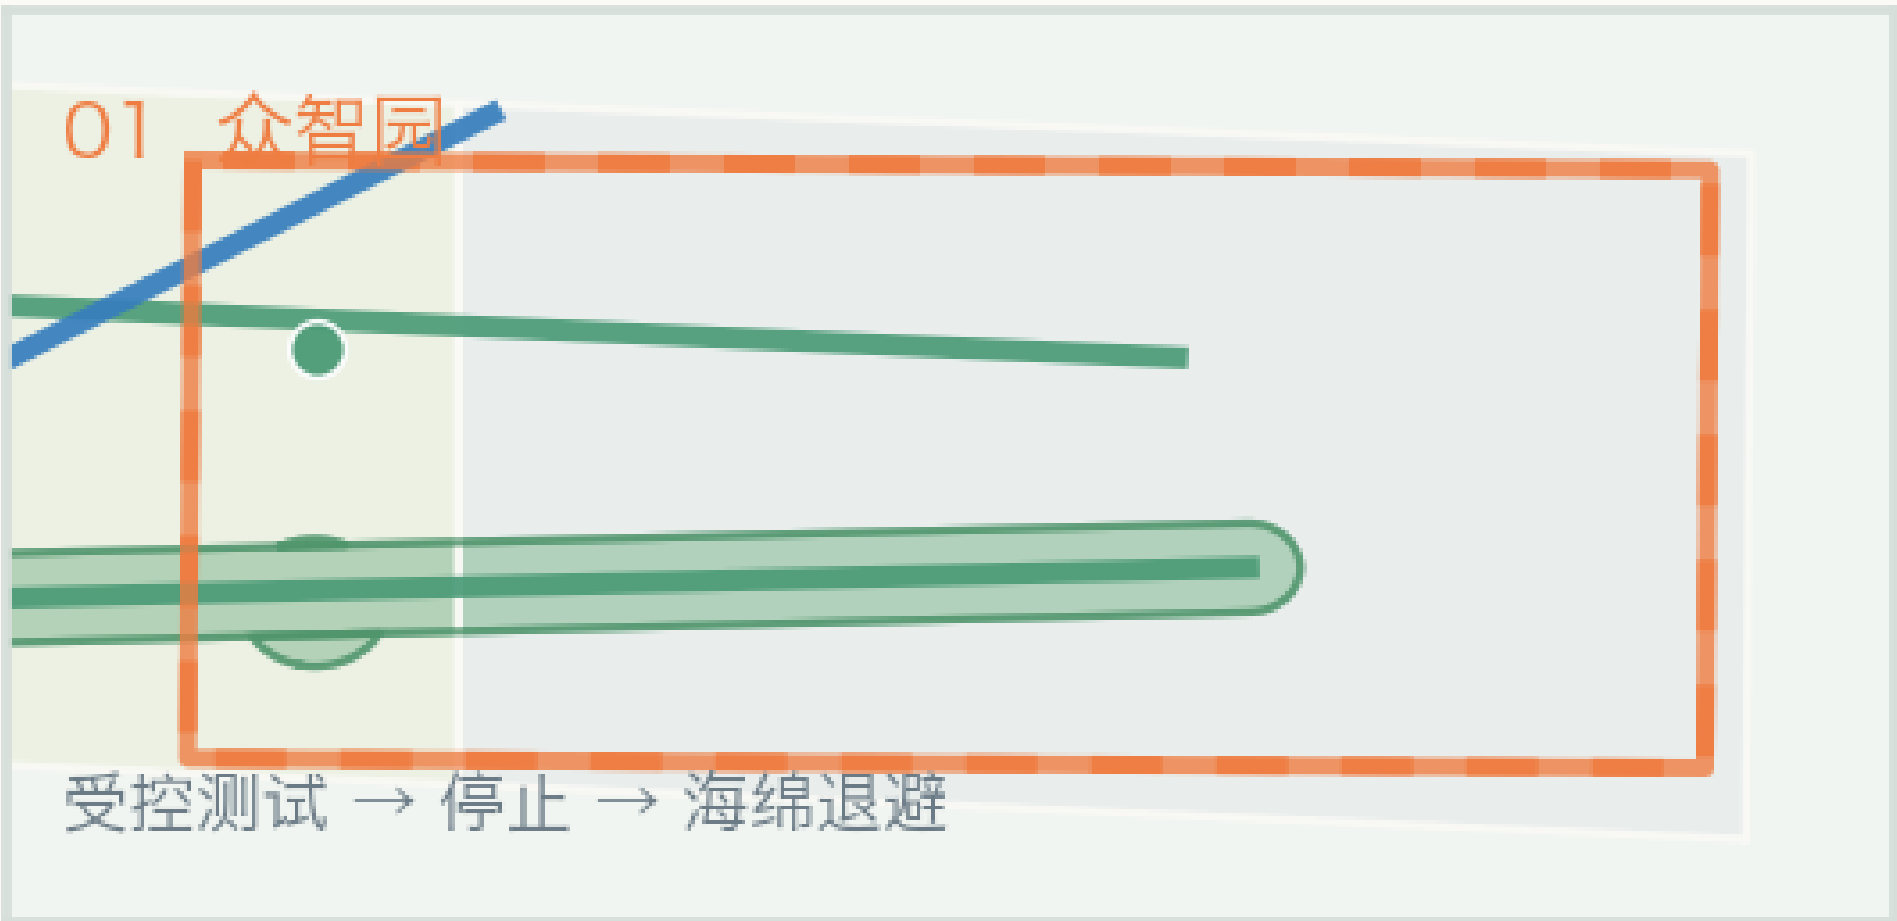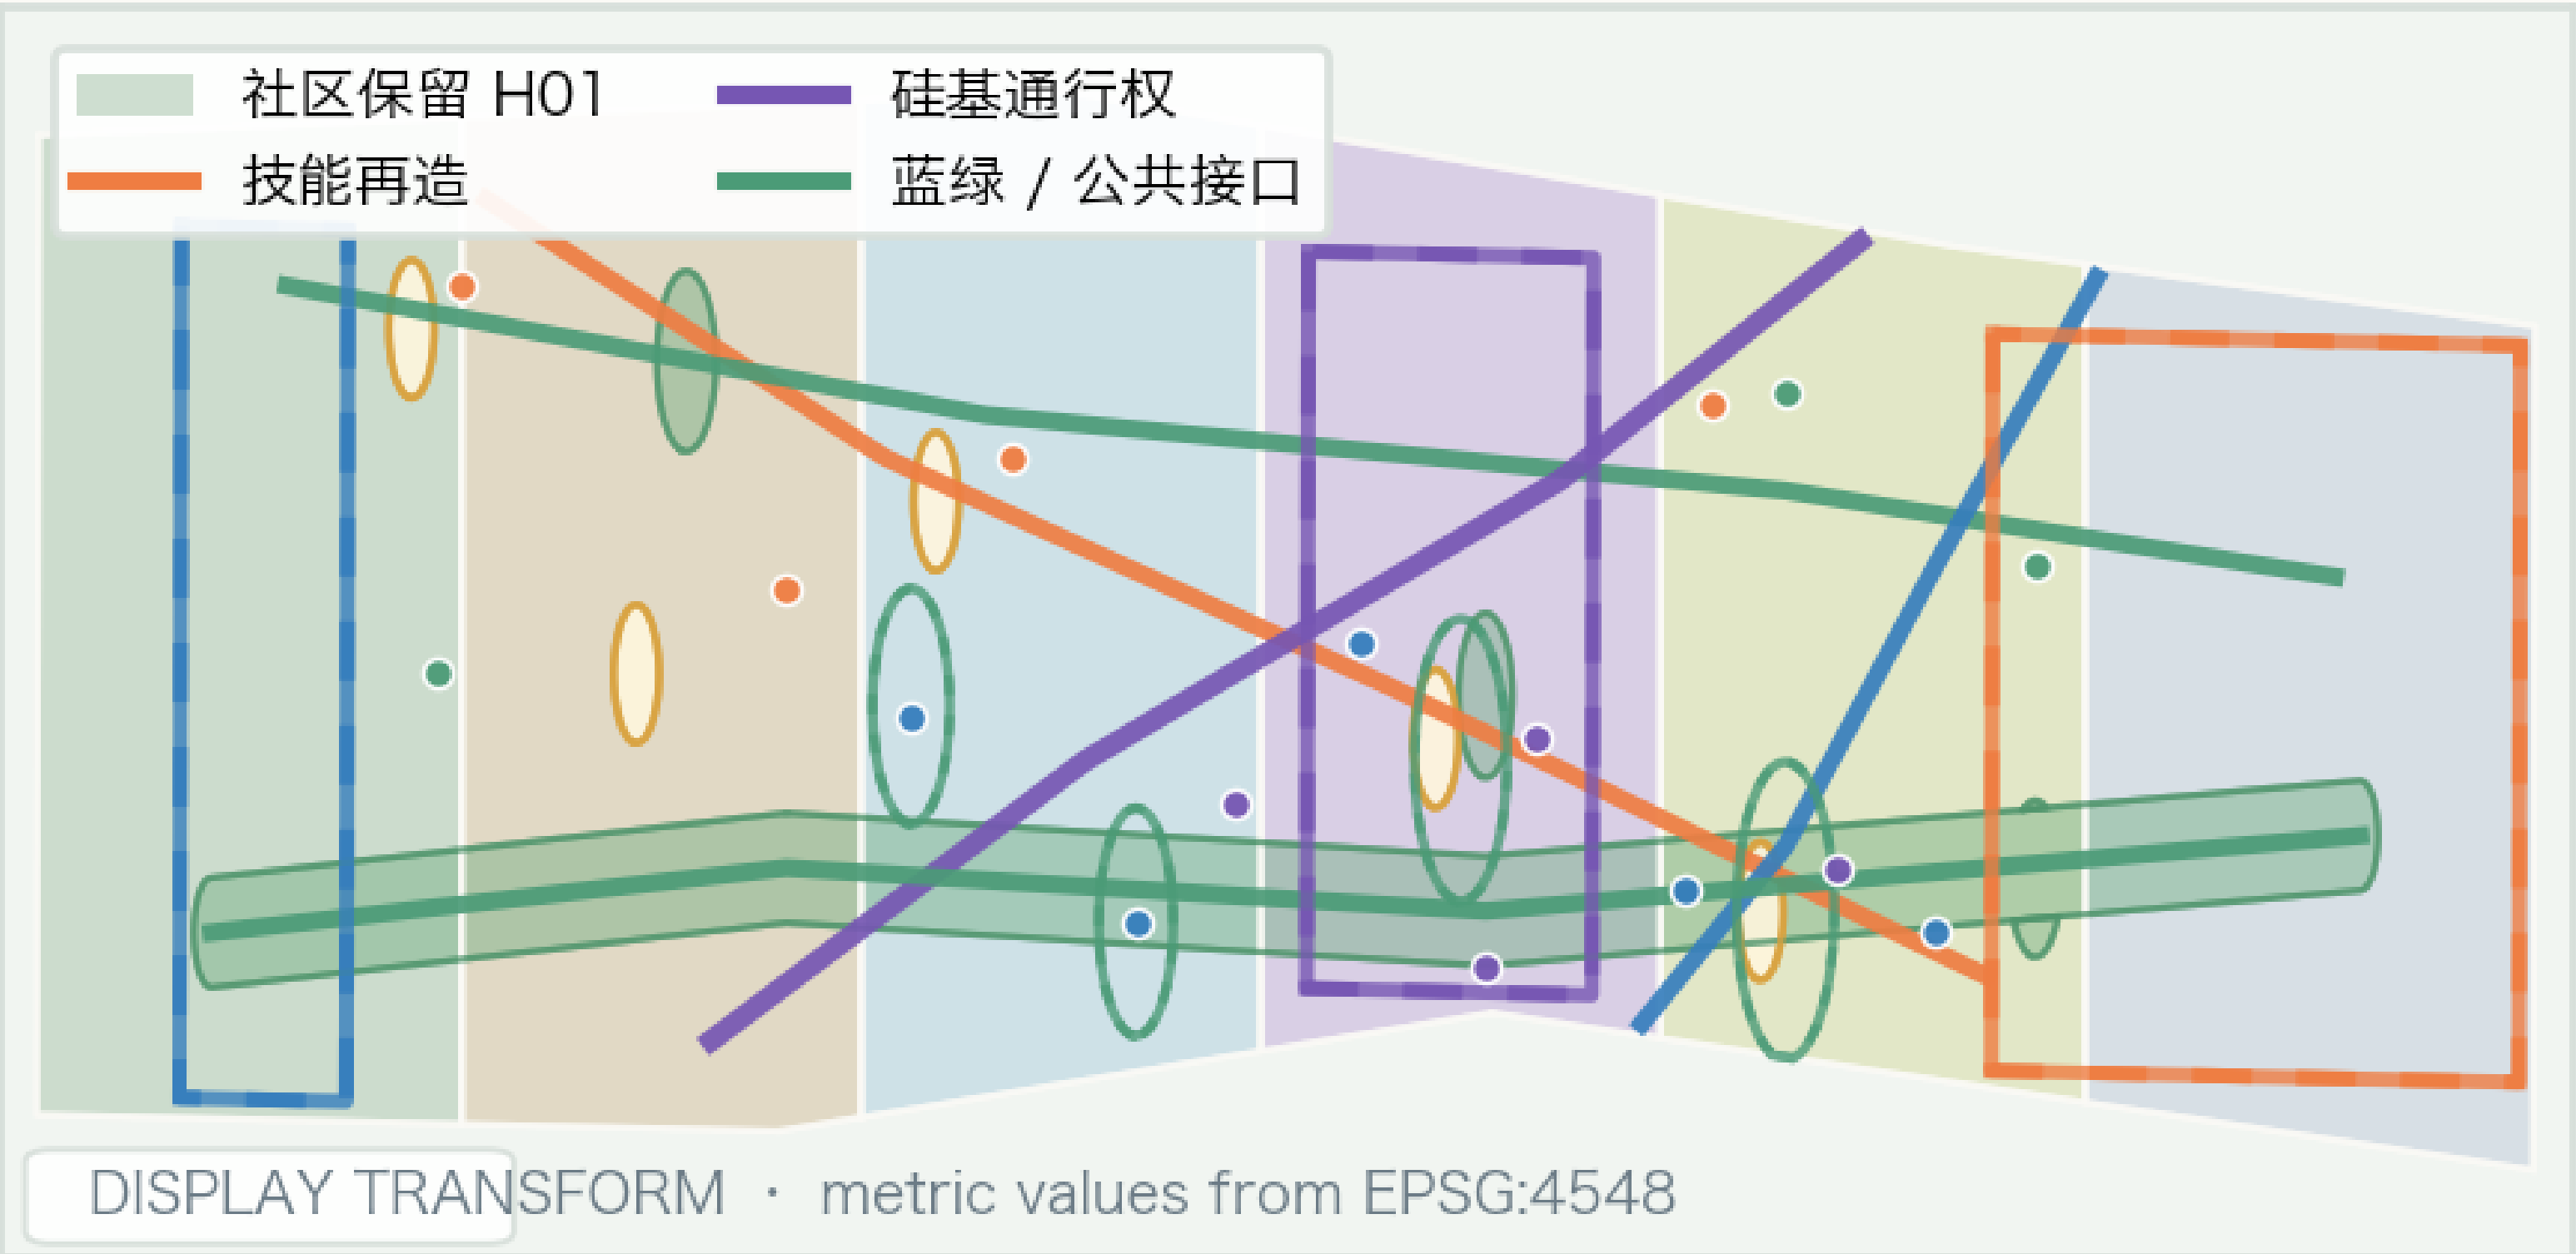

空间动作 / Zhongzhiyuan

受控测试 → 停止 → 海绵退避


临时锚点 · 不构成运营结论

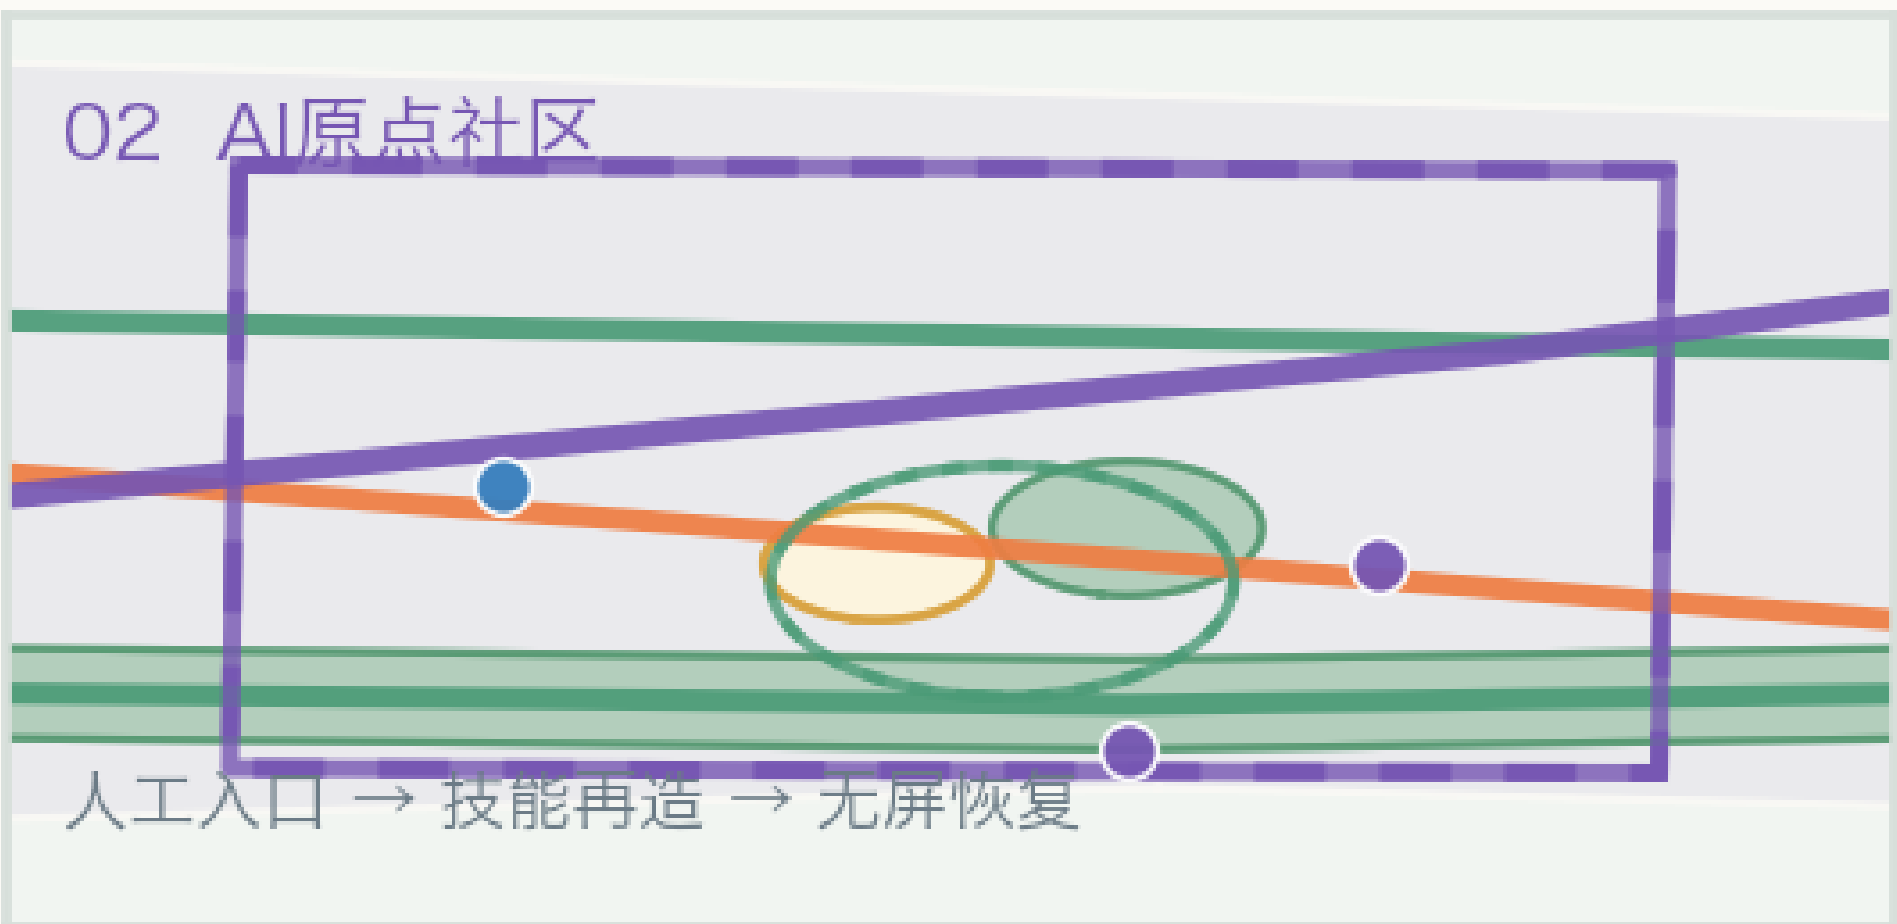

空间动作 / AI Origin Community

人工入口 → 技能再造 → 无屏恢复

临时锚点 · 不构成运营结论

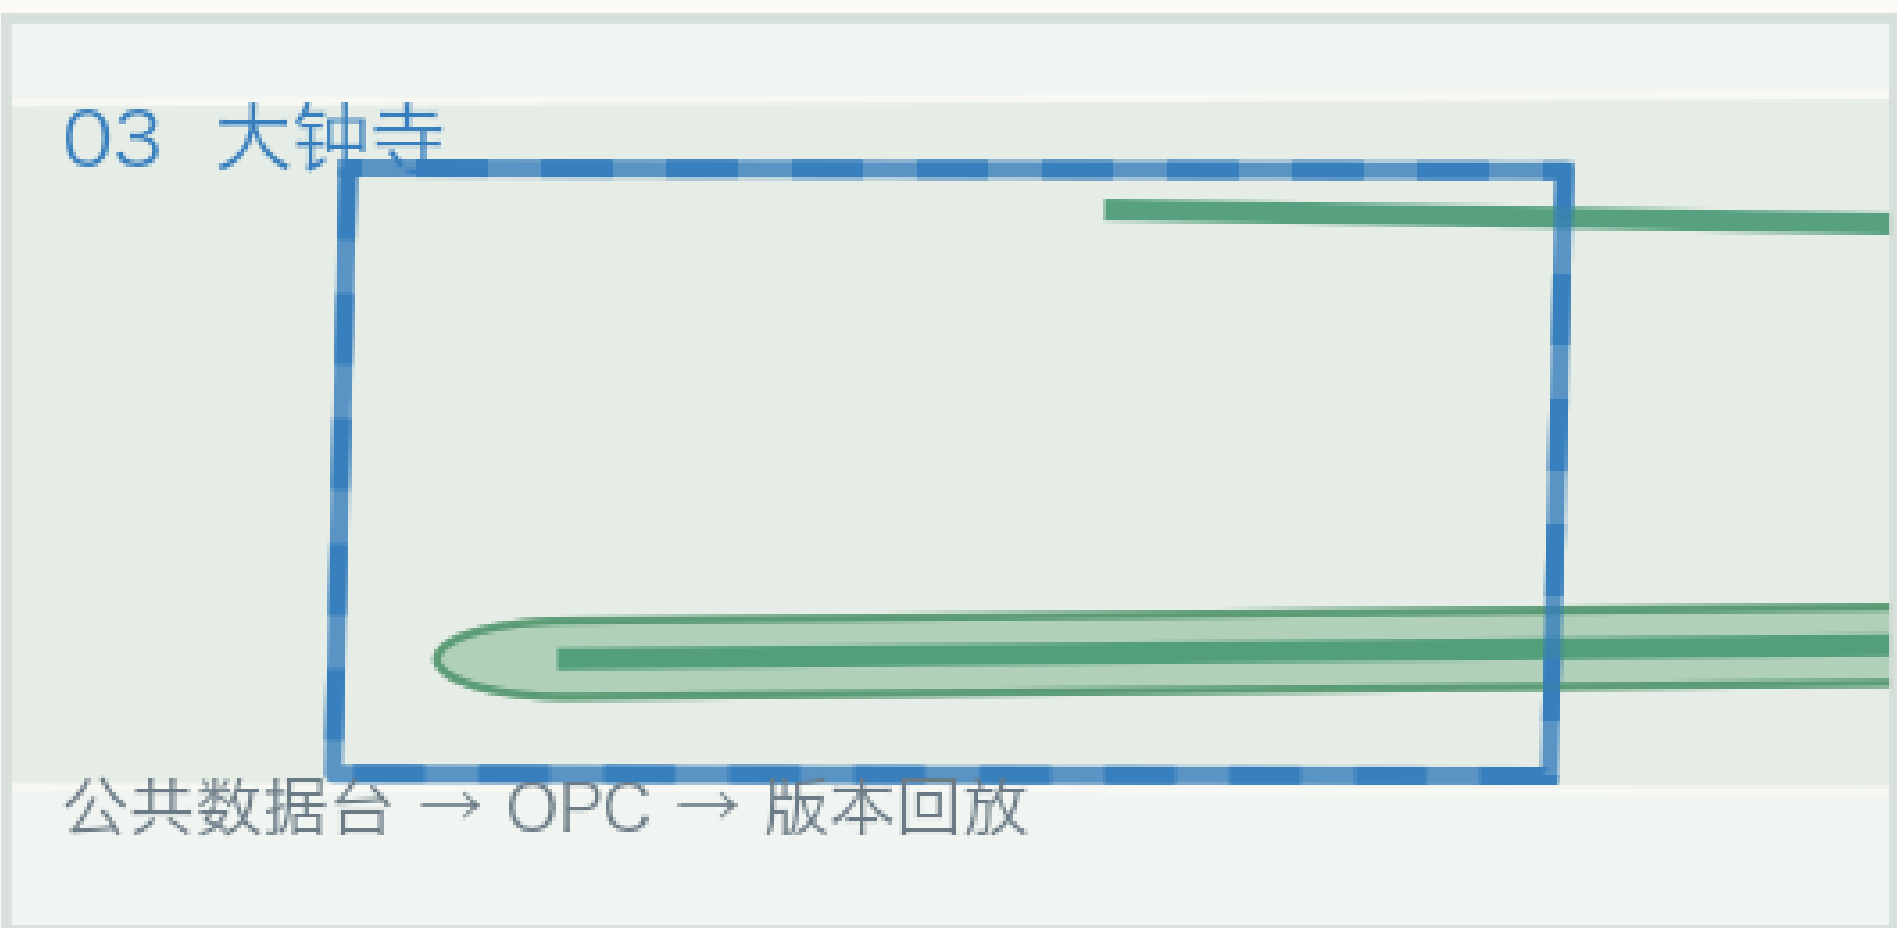

空间动作 / Dazhongsi

公共数据台 → OPC → 版本回放

临时锚点 · 不构成运营结论

official_boundary=false · geometry_role=provisional_constraint · all actions are conceptual suggestions for professional deepening

六层分区


Six-layer spatial operating system

相邻多边形共享边界；面积与占比只来自 GeoJSON / EPSG:4548 · shared edges; areas and shares come only from GeoJSON / EPSG:4548

PACKAGE v1.7

CONCEPT / PROVISIONAL

02 / 六层分区

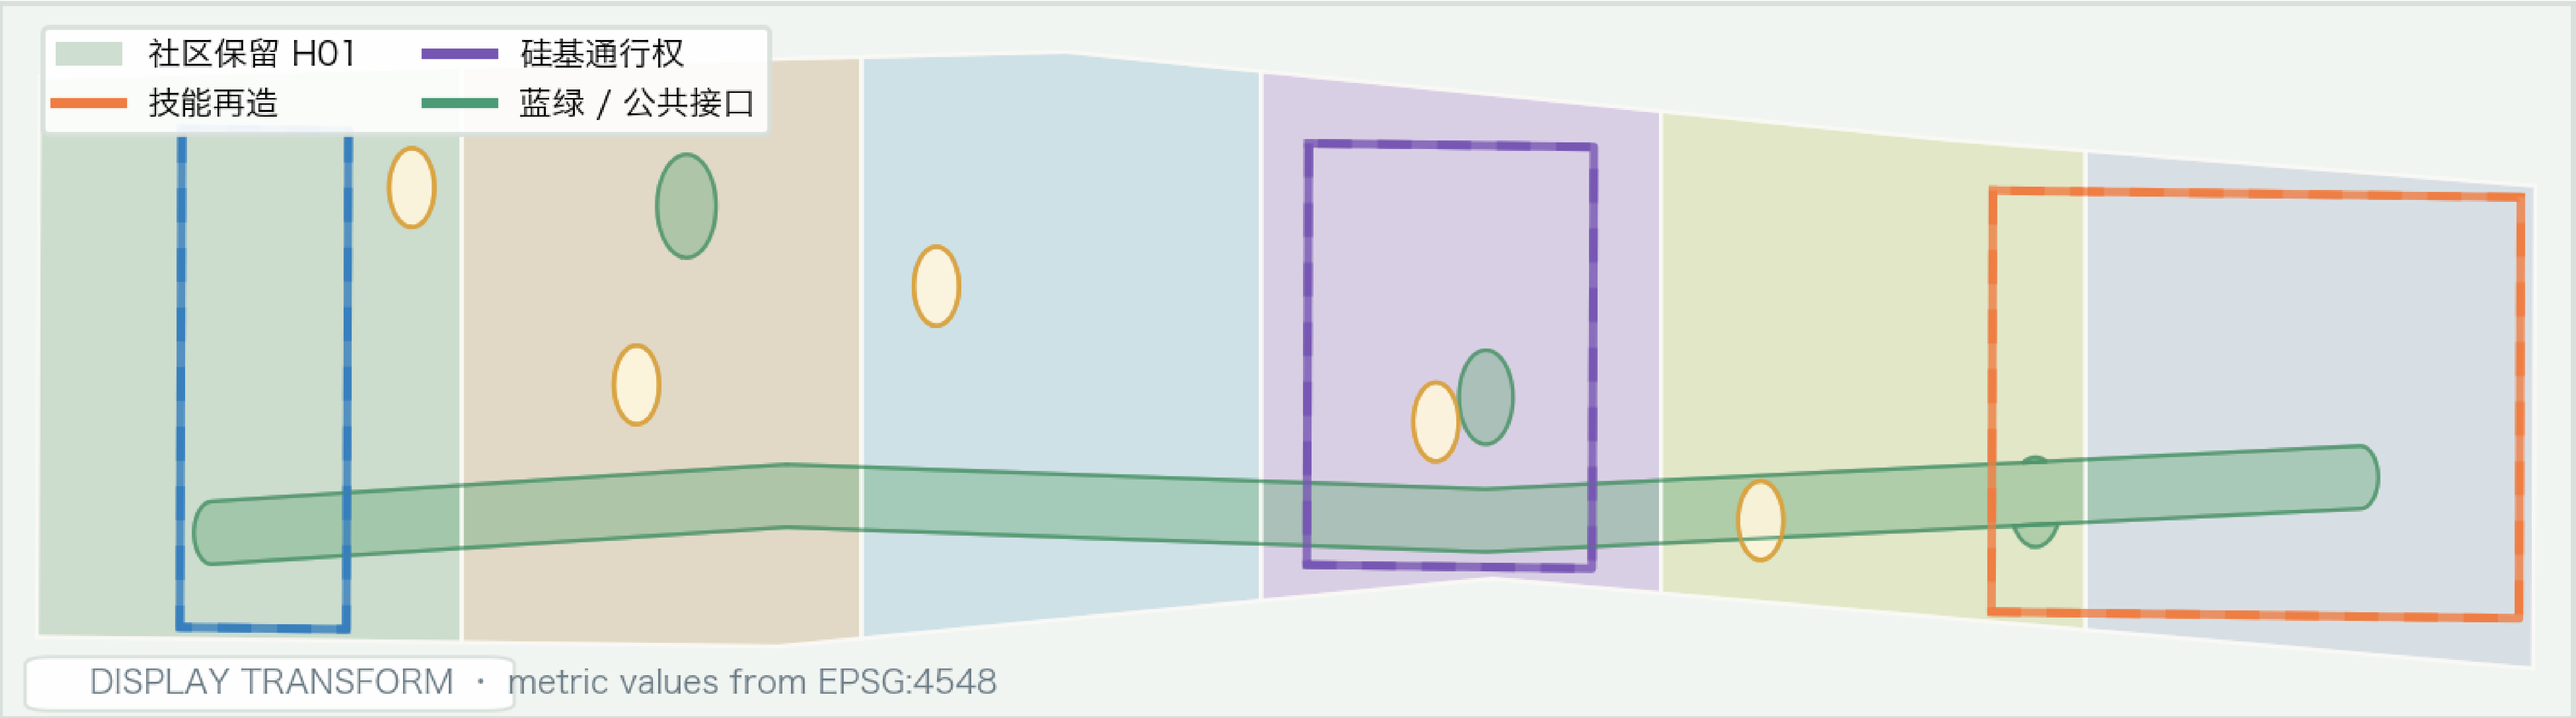

六个可回读单元

H01 原住民保留与社区服务织补
2.09 km2 · 18.28%
D01 国际服务与小团队生态区
2.02 km2 · 17.68%
C01 技能再造与公共数据学习区
1.95 km2 · 17.06%
B01 可逆留白与临时使用区
1.72 km2 · 15.09%
B02 城市 API 与具身智能研发区
1.77 km2 · 15.48%
C02 无屏绿地与气候韧性区
1.87 km2 · 16.40%

100% 覆盖 · 无重叠 · 相邻面共享坐标

仅为概念分配，不含容积率、建筑高度、施工或拆改结论

official_boundary=false · geometry_role=provisional_constraint · all actions are conceptual suggestions for professional deepening


指标与证据

Metrics + evidence

数字只来自几何回算；未知控制条件单列，不用代理值填空 · numbers come from geometry replay; unknown controls remain visible rather than filled by proxies

PACKAGE v1.7
CONCEPT / PROVISIONAL

05 / 几何 → 指标 → 缺口

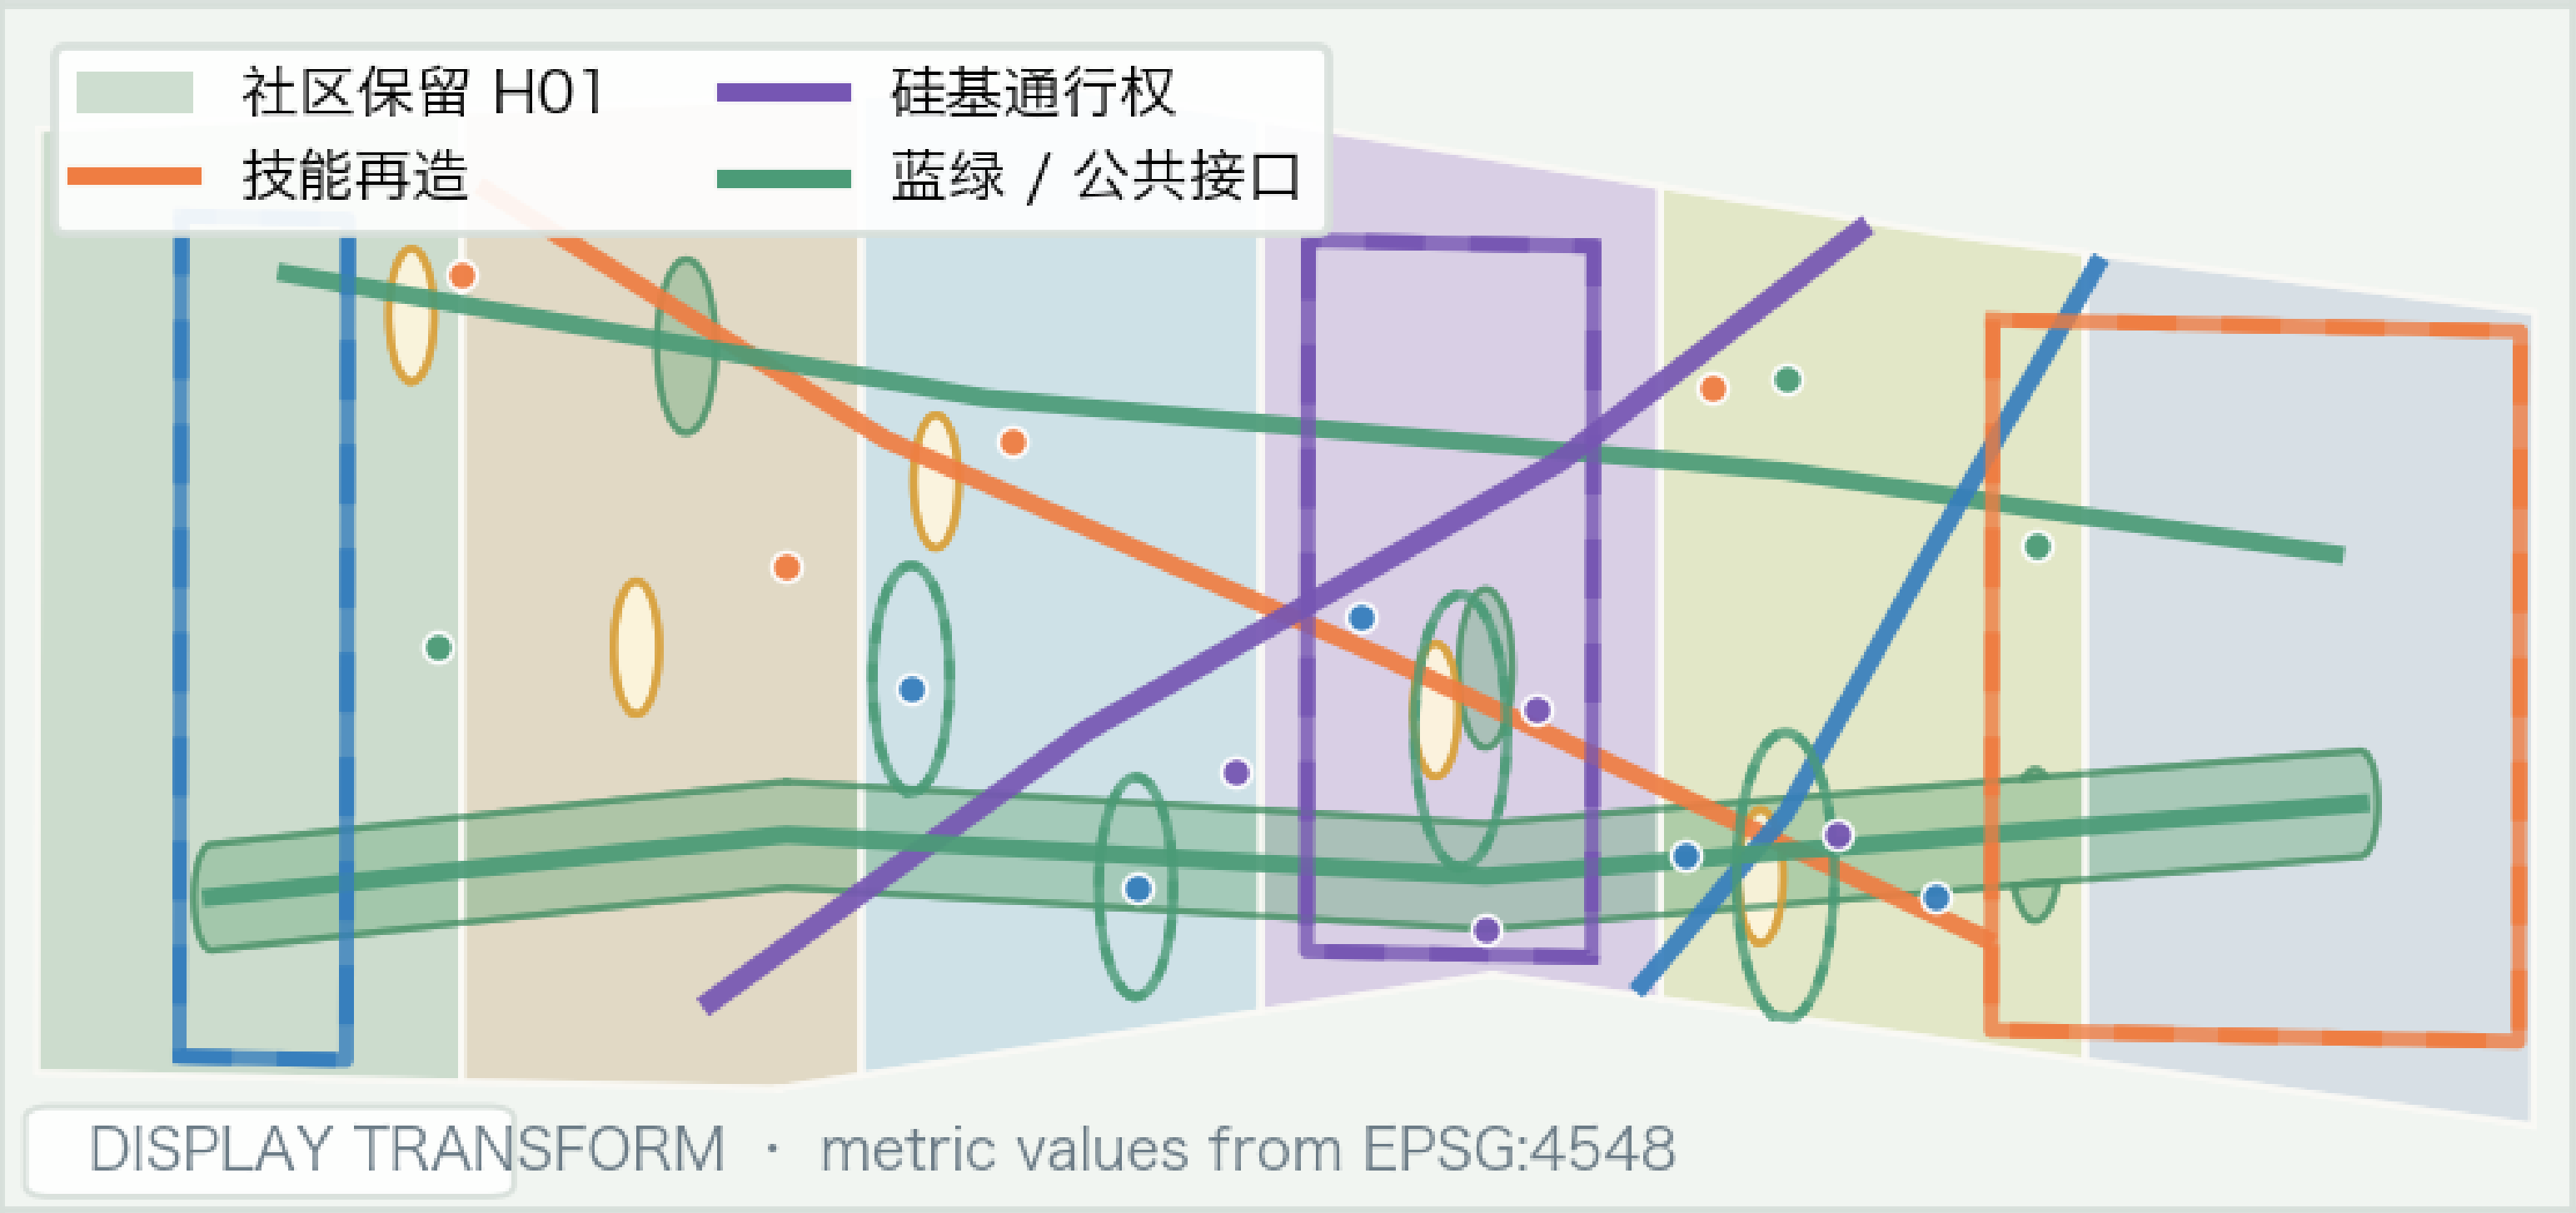

可重算值

Site area 11.41 km2 site_boundary.geojson · EPSG:4548	Land-use coverage 100.00% six polygons · shared edges
Green space 11.12% 1,269,257 m2	Public space 1.06% 121,447 m2
Skill corridor 5.919 km ROAD-A-SKILL	Scenario nodes 16 constraints.geojson

unknown / 待补数据

官方边界 · 容积率/高度控制 · 居民保留率 · 就业转型持续率 · 人工服务等效性 · PUE · 绿电占比 · 余热回收

每个 unknown 都是下一道资料门，不是被隐藏的假设。

official_boundary=false · geometry_role=provisional_constraint · all actions are conceptual suggestions for professional deepening

人机共行与蓝绿韧性


Human-machine co-presence + blue-green resilience

四条概念廊道与三处节点交叉；人行优先、人工接管、退避与回放并列 · four conceptual corridors meet three nodes; pedestrian priority, human takeover, retreat and replay are explicit

PACKAGE v1.7

CONCEPT / PROVISIONAL

04 / 廊道与交叉节点

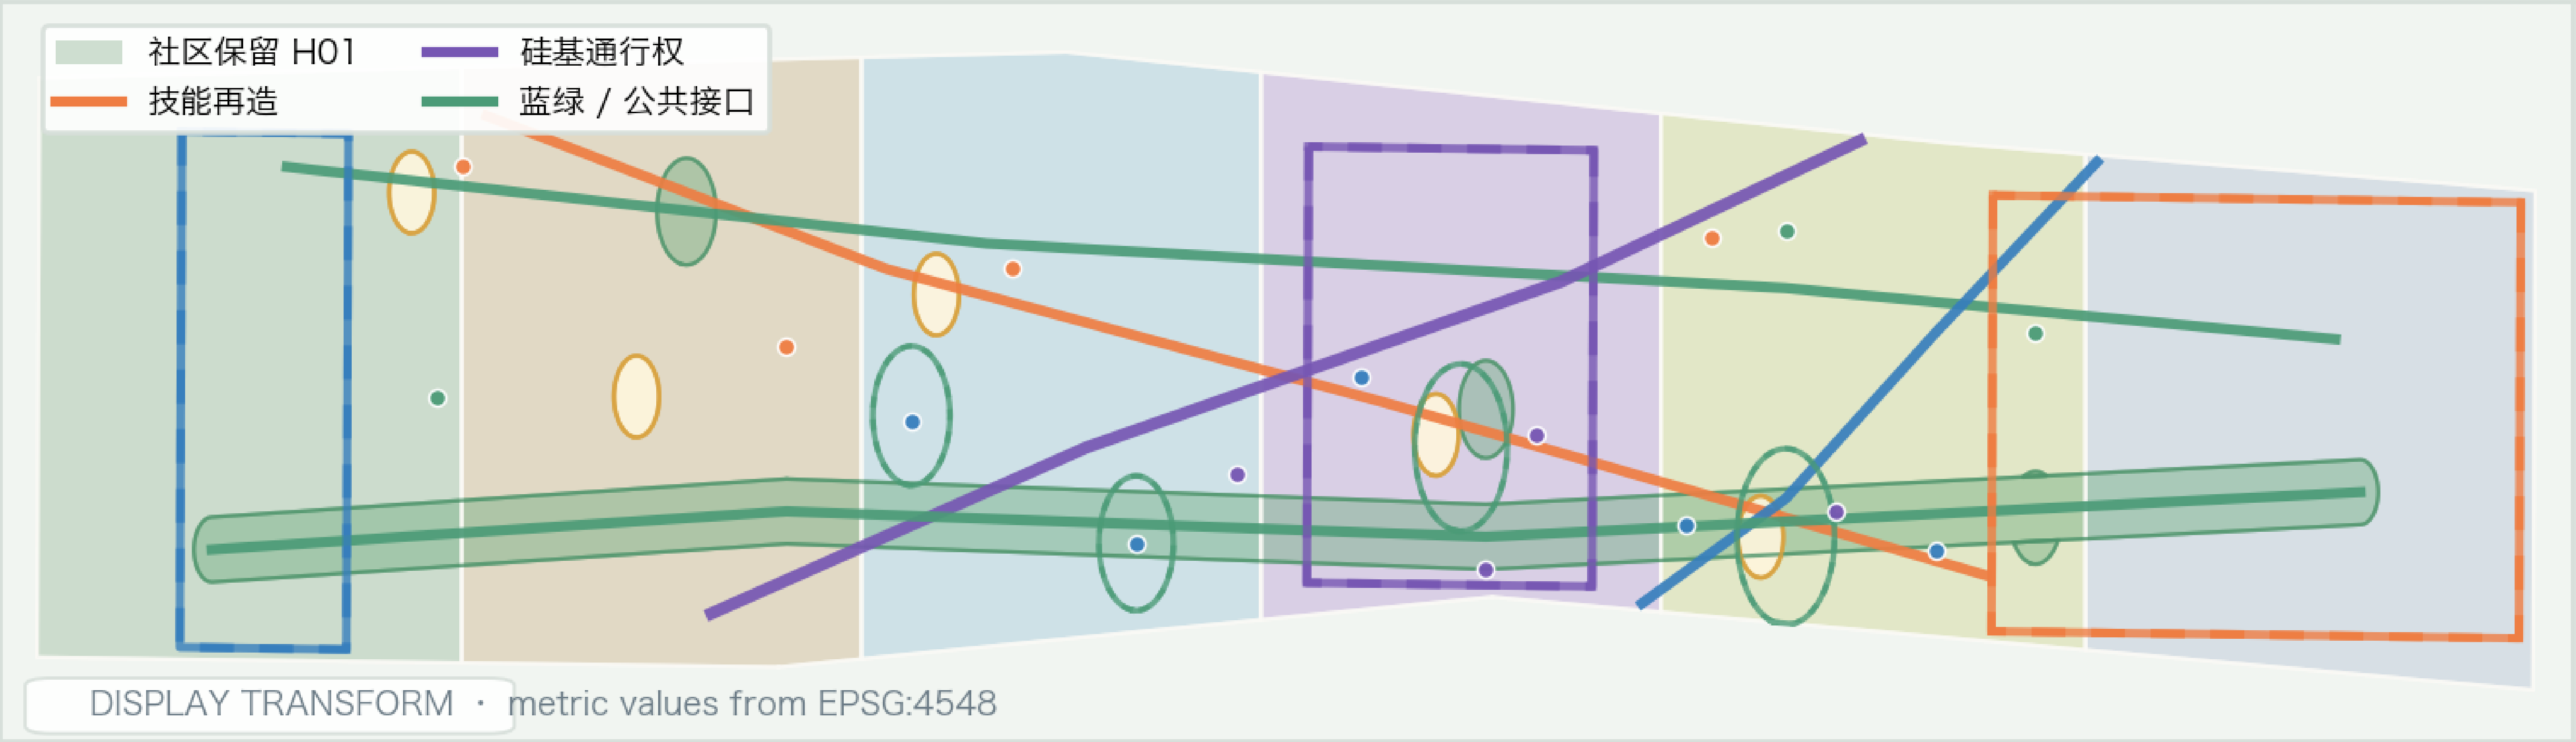

四条空间规则

SKILL / 技能再造

5.919 km

retraining → new work

SILICON / 硅基通行权

4.586 km

human priority + controlled test

LOW-AIR / 低空分层

2.015 km

conceptual layer; later review

SPONGE / 小月河

area / line

floodway + sponge inspection

每个交叉点保留：可视状态、低速暂停、人工接管、事故回放。

概念廊道；不是工程线位或已批准路线

official_boundary=false · geometry_role=provisional_constraint · all actions are conceptual suggestions for professional deepening

参数化空间取舍 | 基线、人本优先与机器协同


同一临时边界 · 六层概念功能带 · 面积公式可复算

v0.8

概念建议


六层面积参数

share × 临时 site_area_sqm

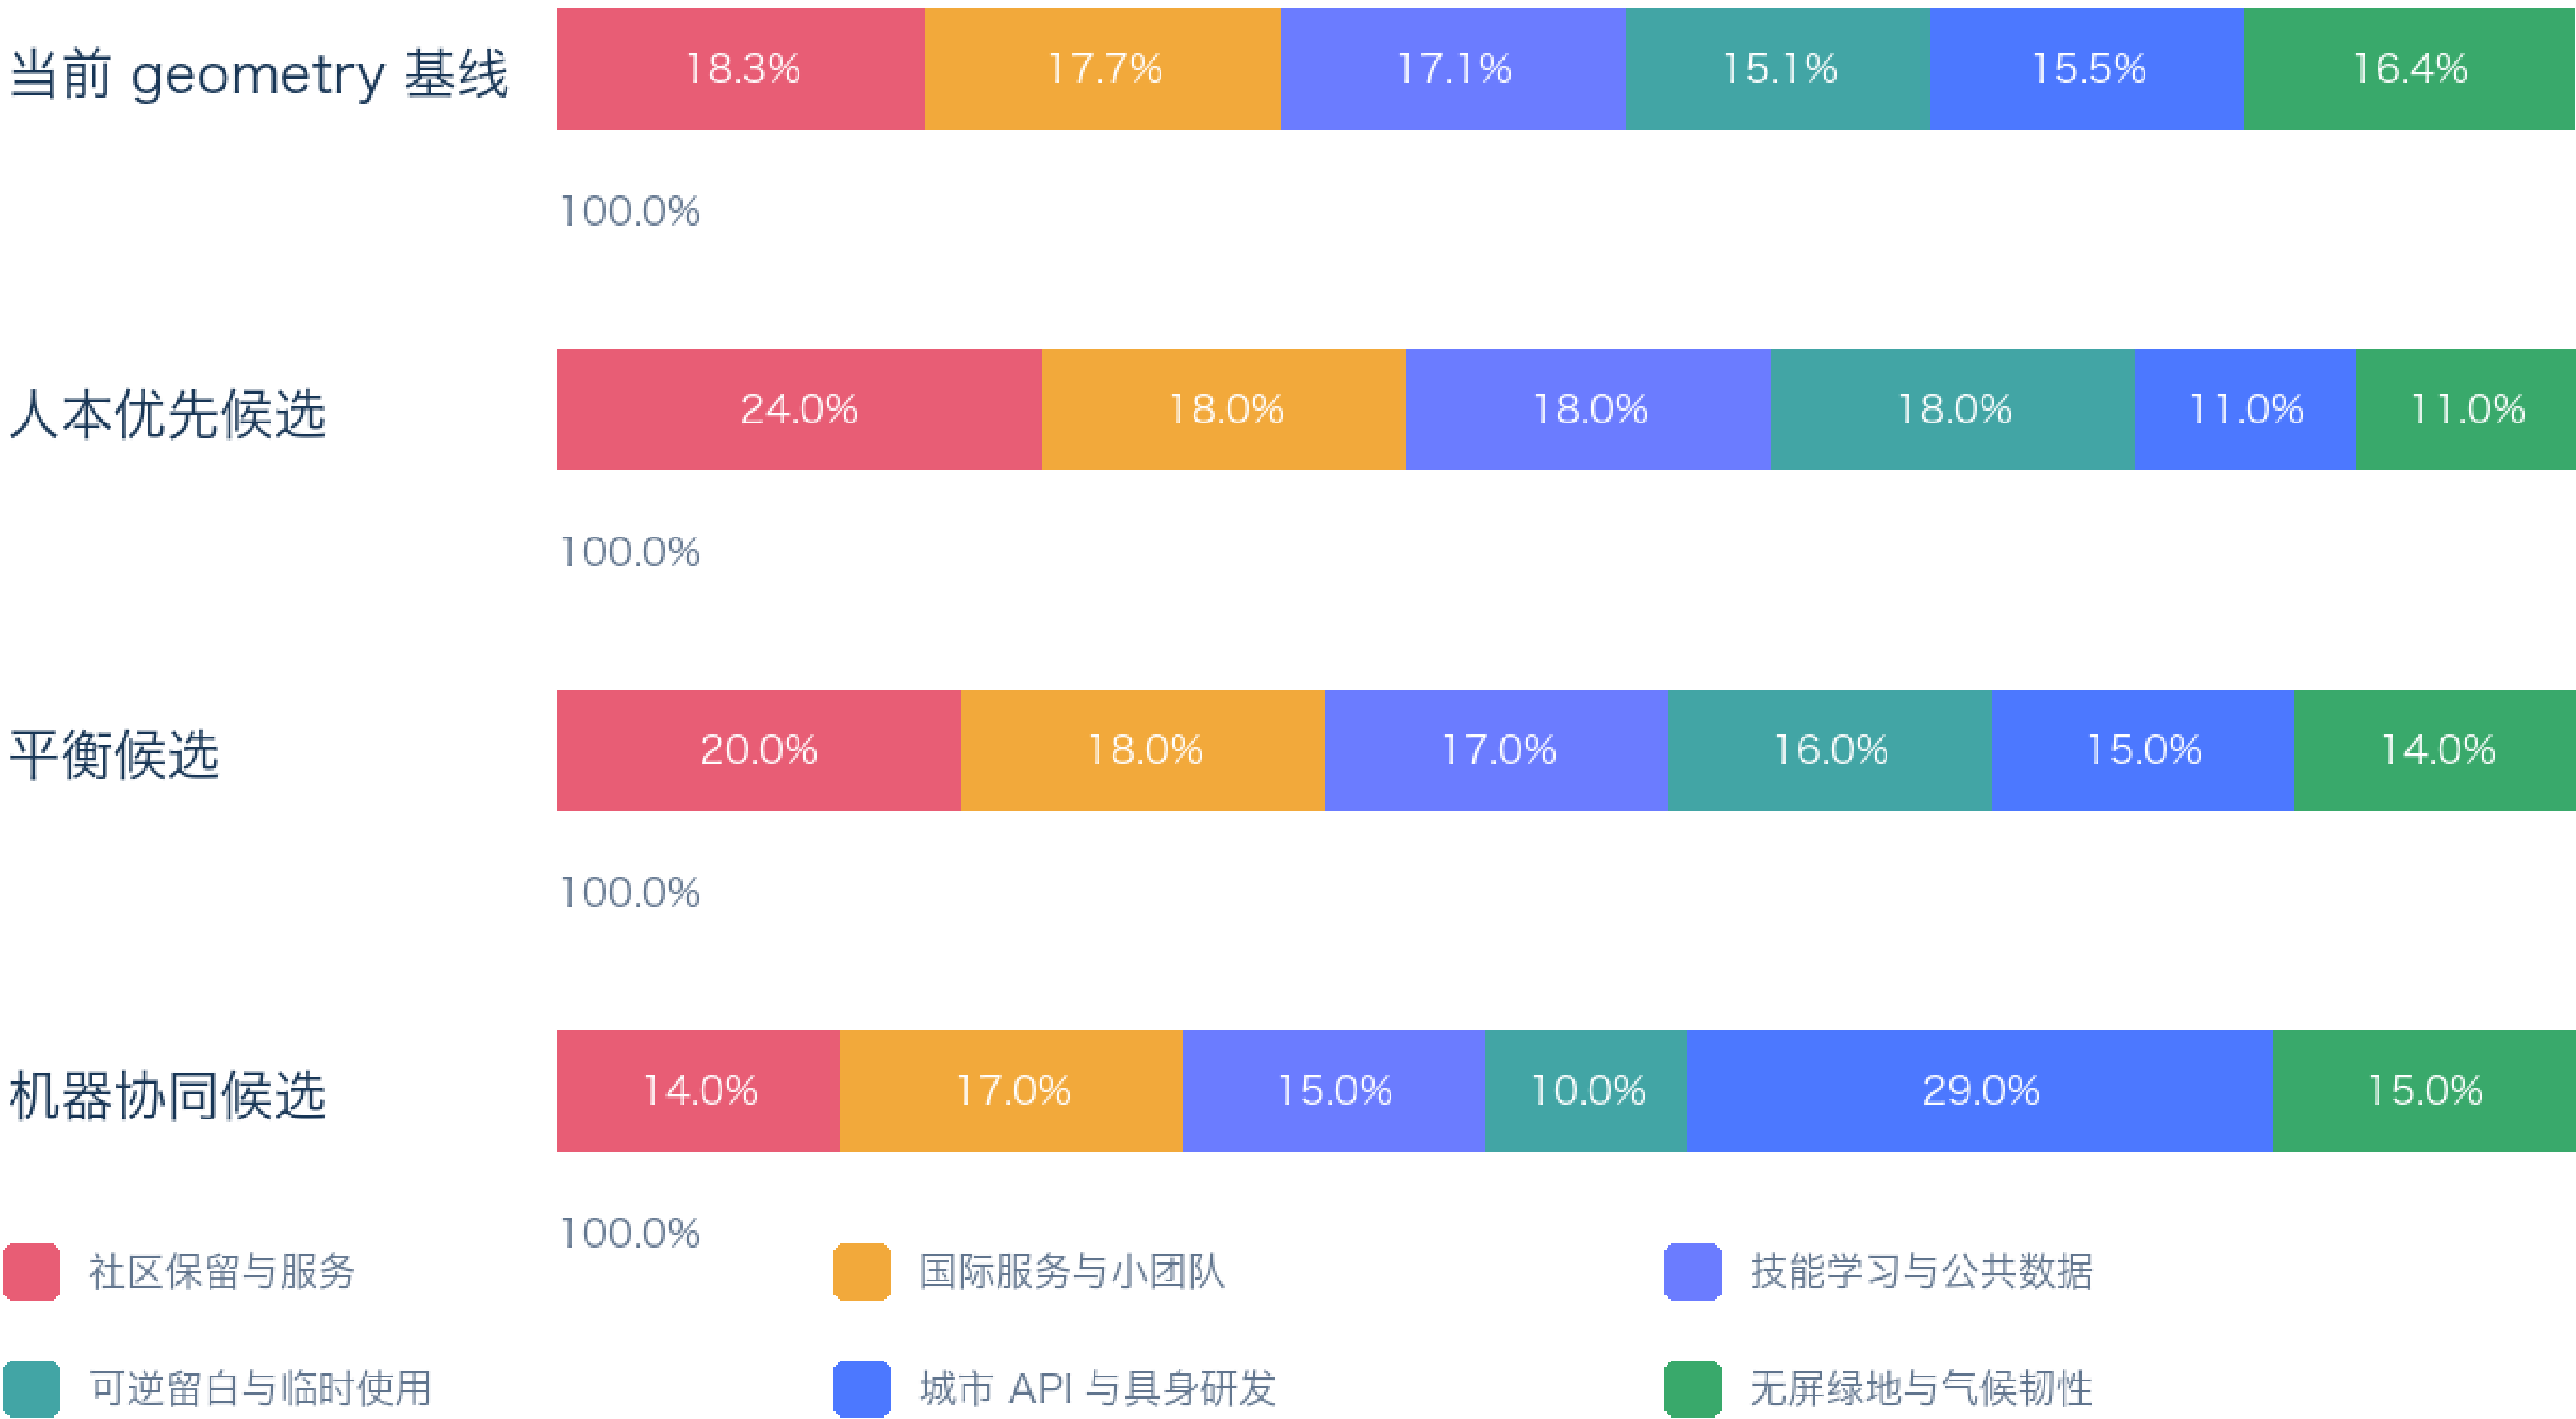

评审读法

当前 baseline

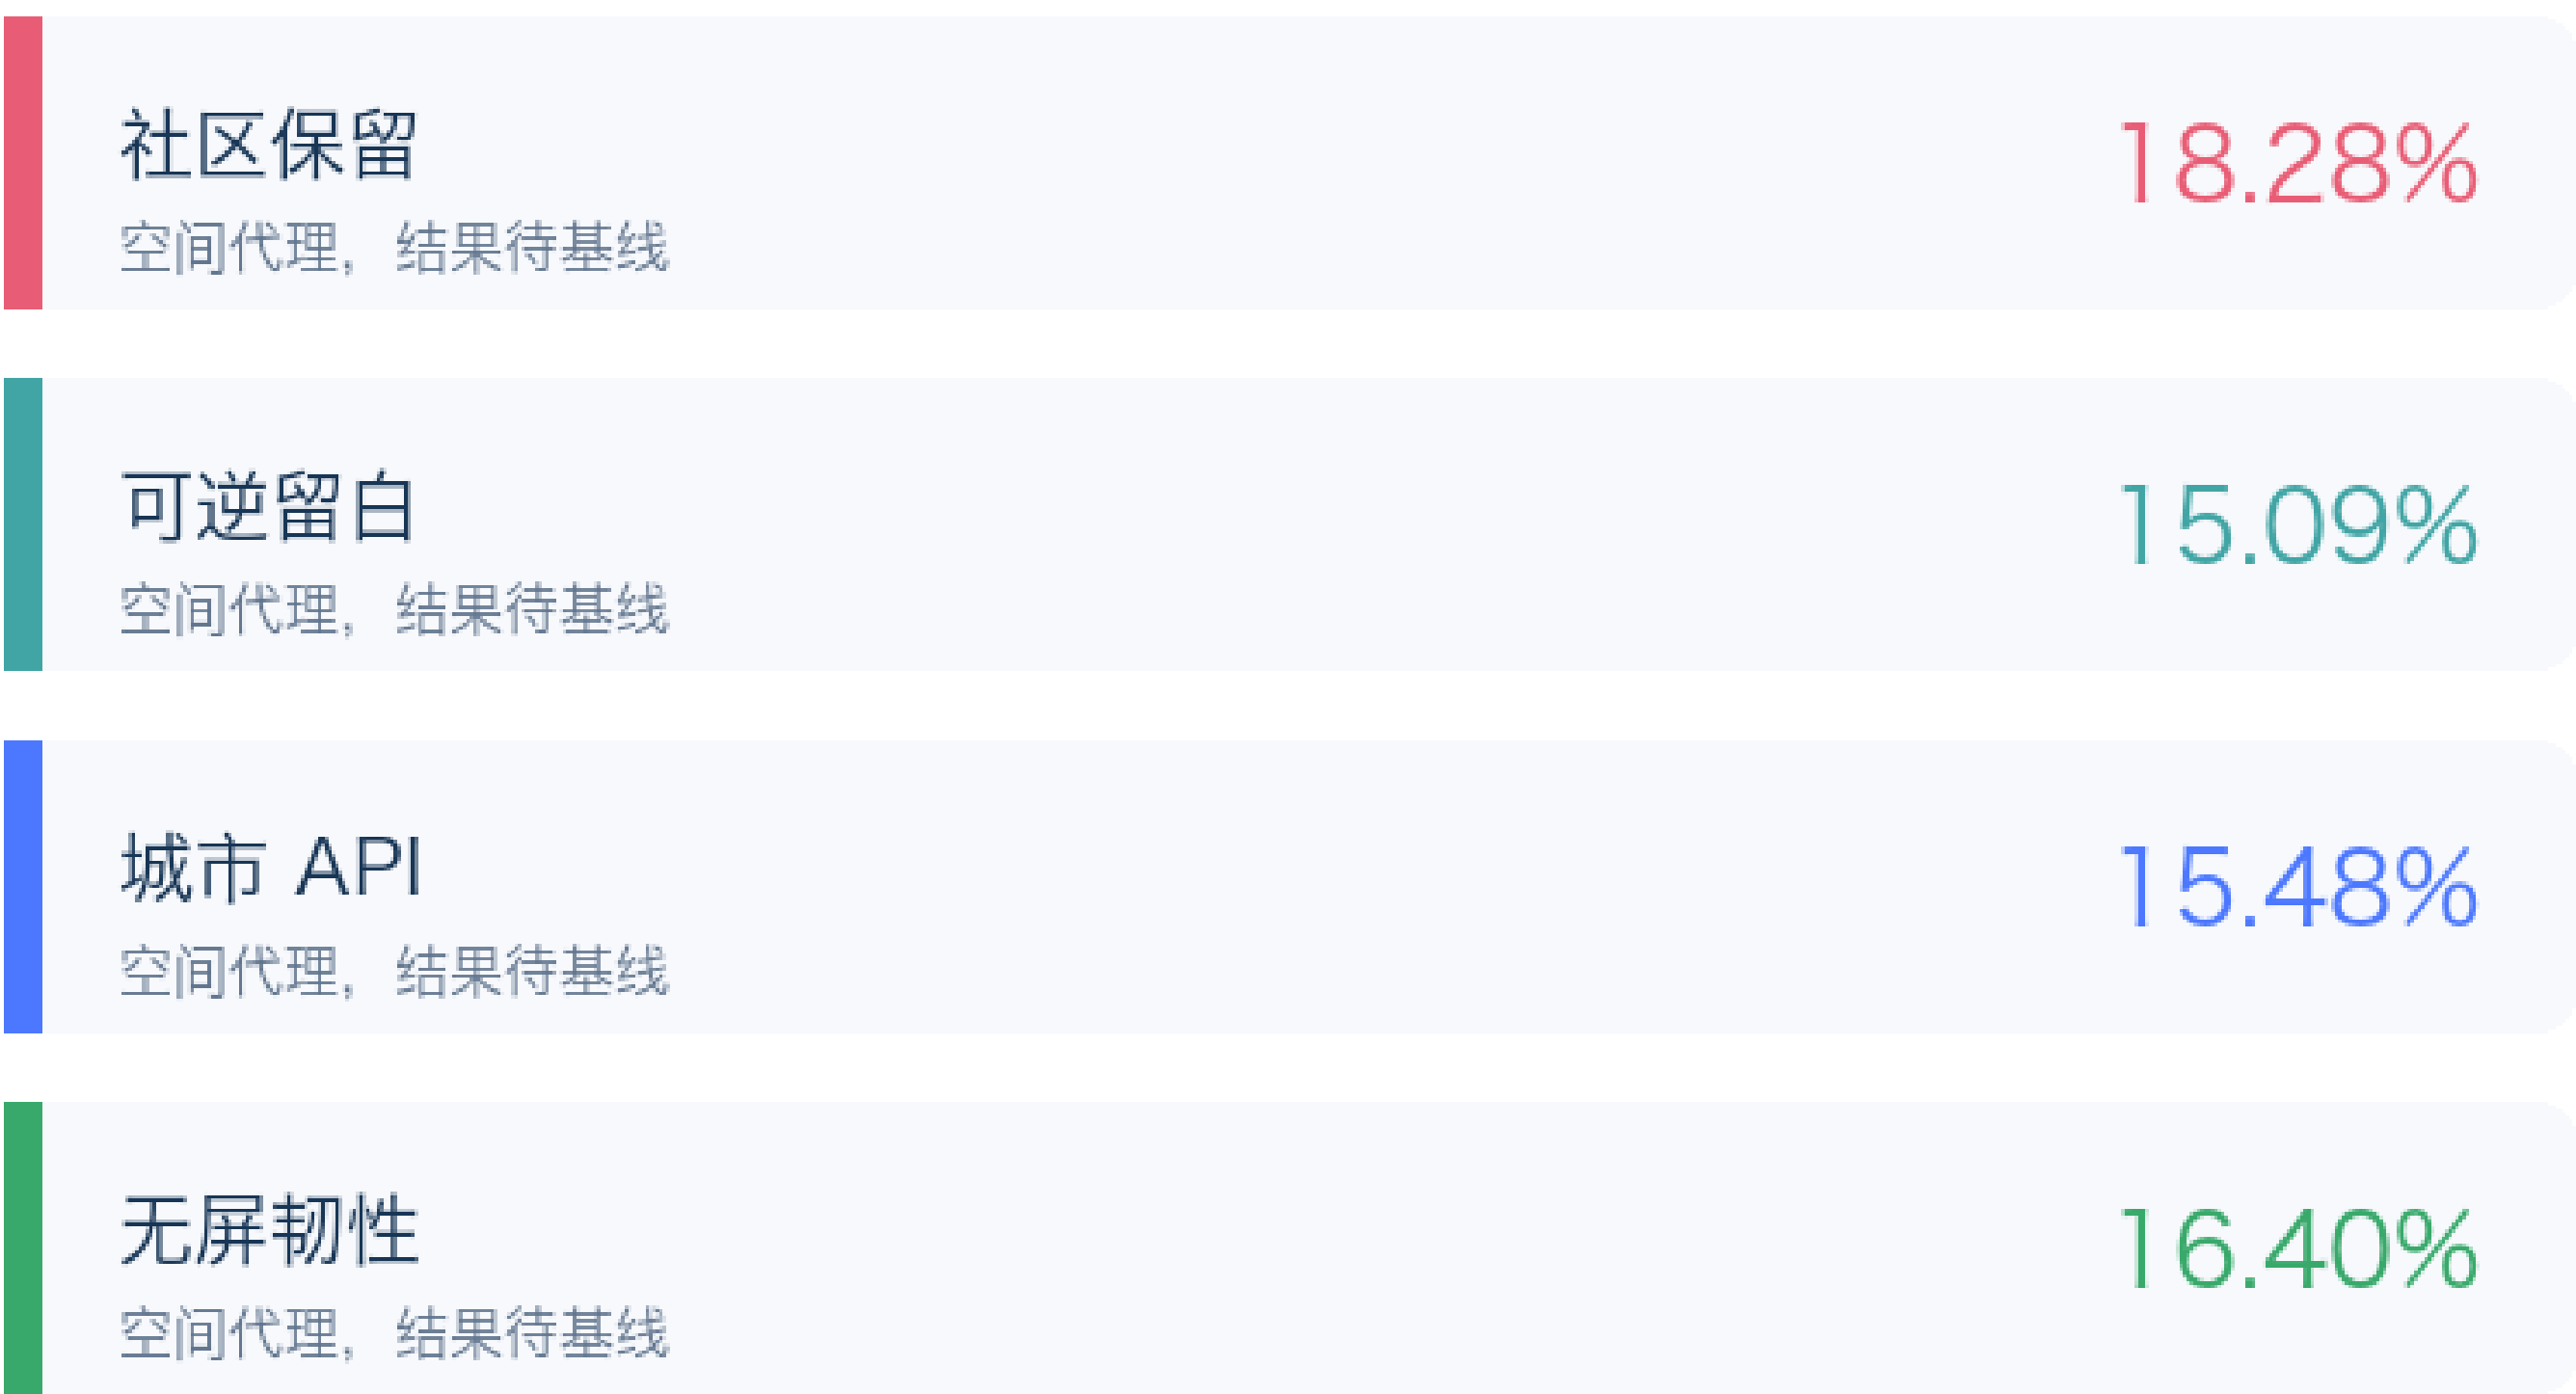

三组候选

- 人本优先：增加社区、学习与留白讨论权重
- 平衡：作为下一轮专业校准的中位比较组
- 机器协同：提高 API 讨论权重，保留人工与韧性底线

三组参数均为概念建议；不产生 FAR、建筑高度、工程、投资或政策结论。
formula: area = share × 临时边界面积

来源: geometry/land_use.geojson · metrics.json · EPSG:4548 内部复算 · confidence: low

公共空间—文化—运营年度图谱

三座概念地标 · 四季运营节奏 · 五个项目族

PACKAGE v2.0

CONCEPT / NO OPERATOR

三座可读地标：文化叙事进入日常公共空间

L1 人的版本大厅

issue · change · retract
SC-C05
/ PROV-KEY-002 · 概念锚点

L2 轨道接口钟

rail time · version change · public
explanation
SC-D02 / PROV-KEY-003
· 概念锚点

L3 无屏恢复灯塔

shade · sound · night safety ·
no forced interaction
GREEN-A-QUIET-1
/ PROV-KEY-002 · 概念锚点

四季运营节奏：以版本治理把城市周期与 AI 迭代衔接

春 城市问题开源周

居民与服务人员提交问题，公开资料边界与人工问答。

夏 城市 API 与具身测试月

仅在地点、时间、数据、责任四限定下做可退出概念验证。

秋 工作转型与 OPC 共创季

被替代风险劳动者、导师、小团队和专业人员共同回放路径。

冬 城市版本大会

发布年度体检、issue 回复、撤回记录和下一版本资料门。

五个项目族 → 空间承接与发布门

PF-A 人本缓冲与社区保留

A2 / v0.1 · 概念承接

PF-B 城市 API 与可逆空间

A3 / v0.2 · 概念承接

PF-C 人机测试、气候与算电门槛

A1 + W2 / v0.2 · 概念承接

PF-D 公共数据授权与版本治理

L1 / v0.1 - v1.0 · 概念承接

PF-E 生态毛细血管与外溢

A3 + W1 / v1.0 · 概念承接

文化语法：钢轨一时间一接口

钢轨承接百年京张连续性；时间刻度承接年度版本；接口节点把数据、机器与人的解释权放进公共空间。

所有地标与运营节奏均为概念建议 / 参考方案，供专业团队深化研究。official_boundary=false; geometry_role=provisional_constraint；不主张运营主体、许可、资金、容量或现场结果。

南北贯通 + 东西缝合 · 公共贡献展示 · 社群到版本发布的转化链

连接策略

只复用既有锚点；方向是阅读规则，不是测绘线位。



停止：缺授权、无障碍复核、责任或回放 → 留在上一道门，不扩展。

可复用公共空间组件

- 人工入口
- 代际共学
- 无屏恢复
- 贡献回放
- 暂停回退

开发者 / 社区转化（仅为概念机制）



仅为概念建议 · official_boundary=false · provisional_constraint · 不表达尺度 / 运营者 / 审批 / 绩效

区域协同接口：先交换问题，再谈外溢

带内—城内—市域—区域四层接口；不把接口写成既有合作或资源承诺

v0.2 · 概念建议



五个接口卡 / Five interface cards



接口为概念建议；不代表签约、行政分工、企业名单、投资、采购或实施承诺。

城市发布门：每一次扩展都可被否决

16 个场景从观察、受限试点到扩展，均以资料边界、人工兜底、审查证据和退出条件为前提。



图件由 geometry/*.geojson 与结构化证据派生；普通人服务链、空间接口、人本验收图谱和评审导航均只做离线引用或路径核验与预期 FAIL 负测，资料不足仍为 unknown 或概念状态。

图 10

评审证据地图：13 项任务书问题，7 项 workflows 问题

两套问题各自保留来源与边界；本页只显示离线阅读路径，不产生评分、官方结论或实施承诺。

13/13 任务书统一评审维度

7/7 仓库 formal workflows 问题

42/42 包内证据路径解析

非评分 不推断主办方权重或结果

先读 13 项任务书问题的概念与证据入口；再按 7 项仓库 formal scorecard workflows 复核。后者的百分比仅在 JSON 中登记为仓库模板来源，绝非主办方评分。

01 目标契合度

从全球 AI 产业高地与朝圣地目标，到三层范围、四条价值链和可回滚城…

路径 proposal.md

02 功能匹配度

三大定位、五大功能和三区两翼通过三处临时重点区、场景卡与空间锚点相互…

路径 proposal.md

03 品牌识别度

“Jingzhang Human City OS” 把轨道、开放接口与…

路径 proposal.md

04 区域协同性

以技术、标准、知识、OPC 与国际服务的外溢机制，连接京津冀研究与应…

路径 proposal.md

05 规划创新性

以人机接口、可逆留白、城市 API 与发布门把空间、产业与治理放在同…

路径 proposal.md

06 产业支撑度

技能再造、受控测试、OPC 共享实验、数据授权和算电审计均写入前置资…

路径 visual/assets/scenario-cards.json

07 场景可感知度

16 张场景卡与 6 类使用者、10 条代表性路径和三段发布门在同一…

路径 visual/assets/scenario-cards.json

08 空间明确性

三处重点区、概念服务廊、蓝绿空间和显示变换均能回到同一 GeoJSON…

路径 geometry/key_areas.geojson

09 可转化性

发布门、资料缺口、人工接管和重算触发器把下一步交给有权专业、运营与…

路径 visual/assets/release-gate-ledger.json

10 表达完整性

双语正文、图件、图册、网页与结构化台账通过 manifest 和本地…

路径 proposal.md

11 公开合规性

来源、许可边界、临时几何、unknown 与禁用结论在结构化台账中分…

路径 sources.json

12 国际传播力

双语交付、国际服务客厅与全球案例比较为外部阅读和对话提供概念入口。

路径 proposal.md

13 长期运营价值

年度体检、公众 issue、release note、事故复盘与标准…

路径 visual/assets/release-gate-ledger.json

五条可回放证据脊：路径解析通过，不等于事实、绩效或许可通过



图件由 geometry/*.geojson 与结构化证据派生；普通人服务链、空间接口、人本验收图谱和评审导航均只做离线引用或路径核验与预期 FAIL 负测，资料不足仍为 unknown 或概念状态。

七维评审证据地图

Seven-dimension review evidence map

评审顺序：问题 → 证据入口 → 不能证明什么 → 下一道核验

七个维度 · 已登记的工作流问题

01 任务书相关性	模板权重 20%	临时边界、设计分区和概念成果不等于官方红线、法定控制或实施方案。
证据：proposal.md		
02 原创性	模板权重 10%	契约级回放证明结构可审阅，不证明真实服务绩效、公众接受或已部署能力
证据：proposal.md		
03 AI 与规划创新性	模板权重 15%	本地脚本只做离线结构和负测；不调用外部系统，也不替代专业模型、许可或现场测试
证据：assets/run-human-city-ordinary-journey....		
04 可实施性	模板权重 20%	建议角色不是已确认运营方；资料缺失、保险、审批、预算、真实 OD 与现场基线仍须由有权主体补齐。
证据：assets/implementation-operation-matrix....		
05 公共利益与包容性	模板权重 10%	包内是设计要求与离线契约；真实覆盖率、群体体验、同意与结果必须通过真实走读抽样和独立评估获得。
证据：assets/personas-and-fairness.json		
06 风险与合规	模板权重 10%	来源登记和用途边界不等于取得许可、权属清理、数据授权或安全审查。
证据：assumptions.json		
07 表达完整度	模板权重 15%	导航完整度不提升证据等级；HTML、图纸和台账仍不能替代正式资料或现场验证
证据：proposal.md		

PACKAGE v1.8

EVIDENCE / NO SCORE

如何使用这张图

1 · 先读问题

先打开该维度对应的正文段落。

2 · 回到证据

沿最短路径回到几何、指标、台账或图纸。

3 · 看边界

不要把概念建议或 unknown 读成绩效结果。

4 · 补下一证据

专业深化前先补齐对应的资料门。

本图不生成任何分数。

仅为仓库工作流模板权重 · 不是主办方评分 · 临时几何与 unknown 继续作为资料门


人本城市操作系统 | 评审首屏空间证据图谱

一张同源显示变换几何底图 + 三处重点区 × 五段人本空间动作

PACKAGE v2.2

概念 / 临时约束

01 / 同源空间底图

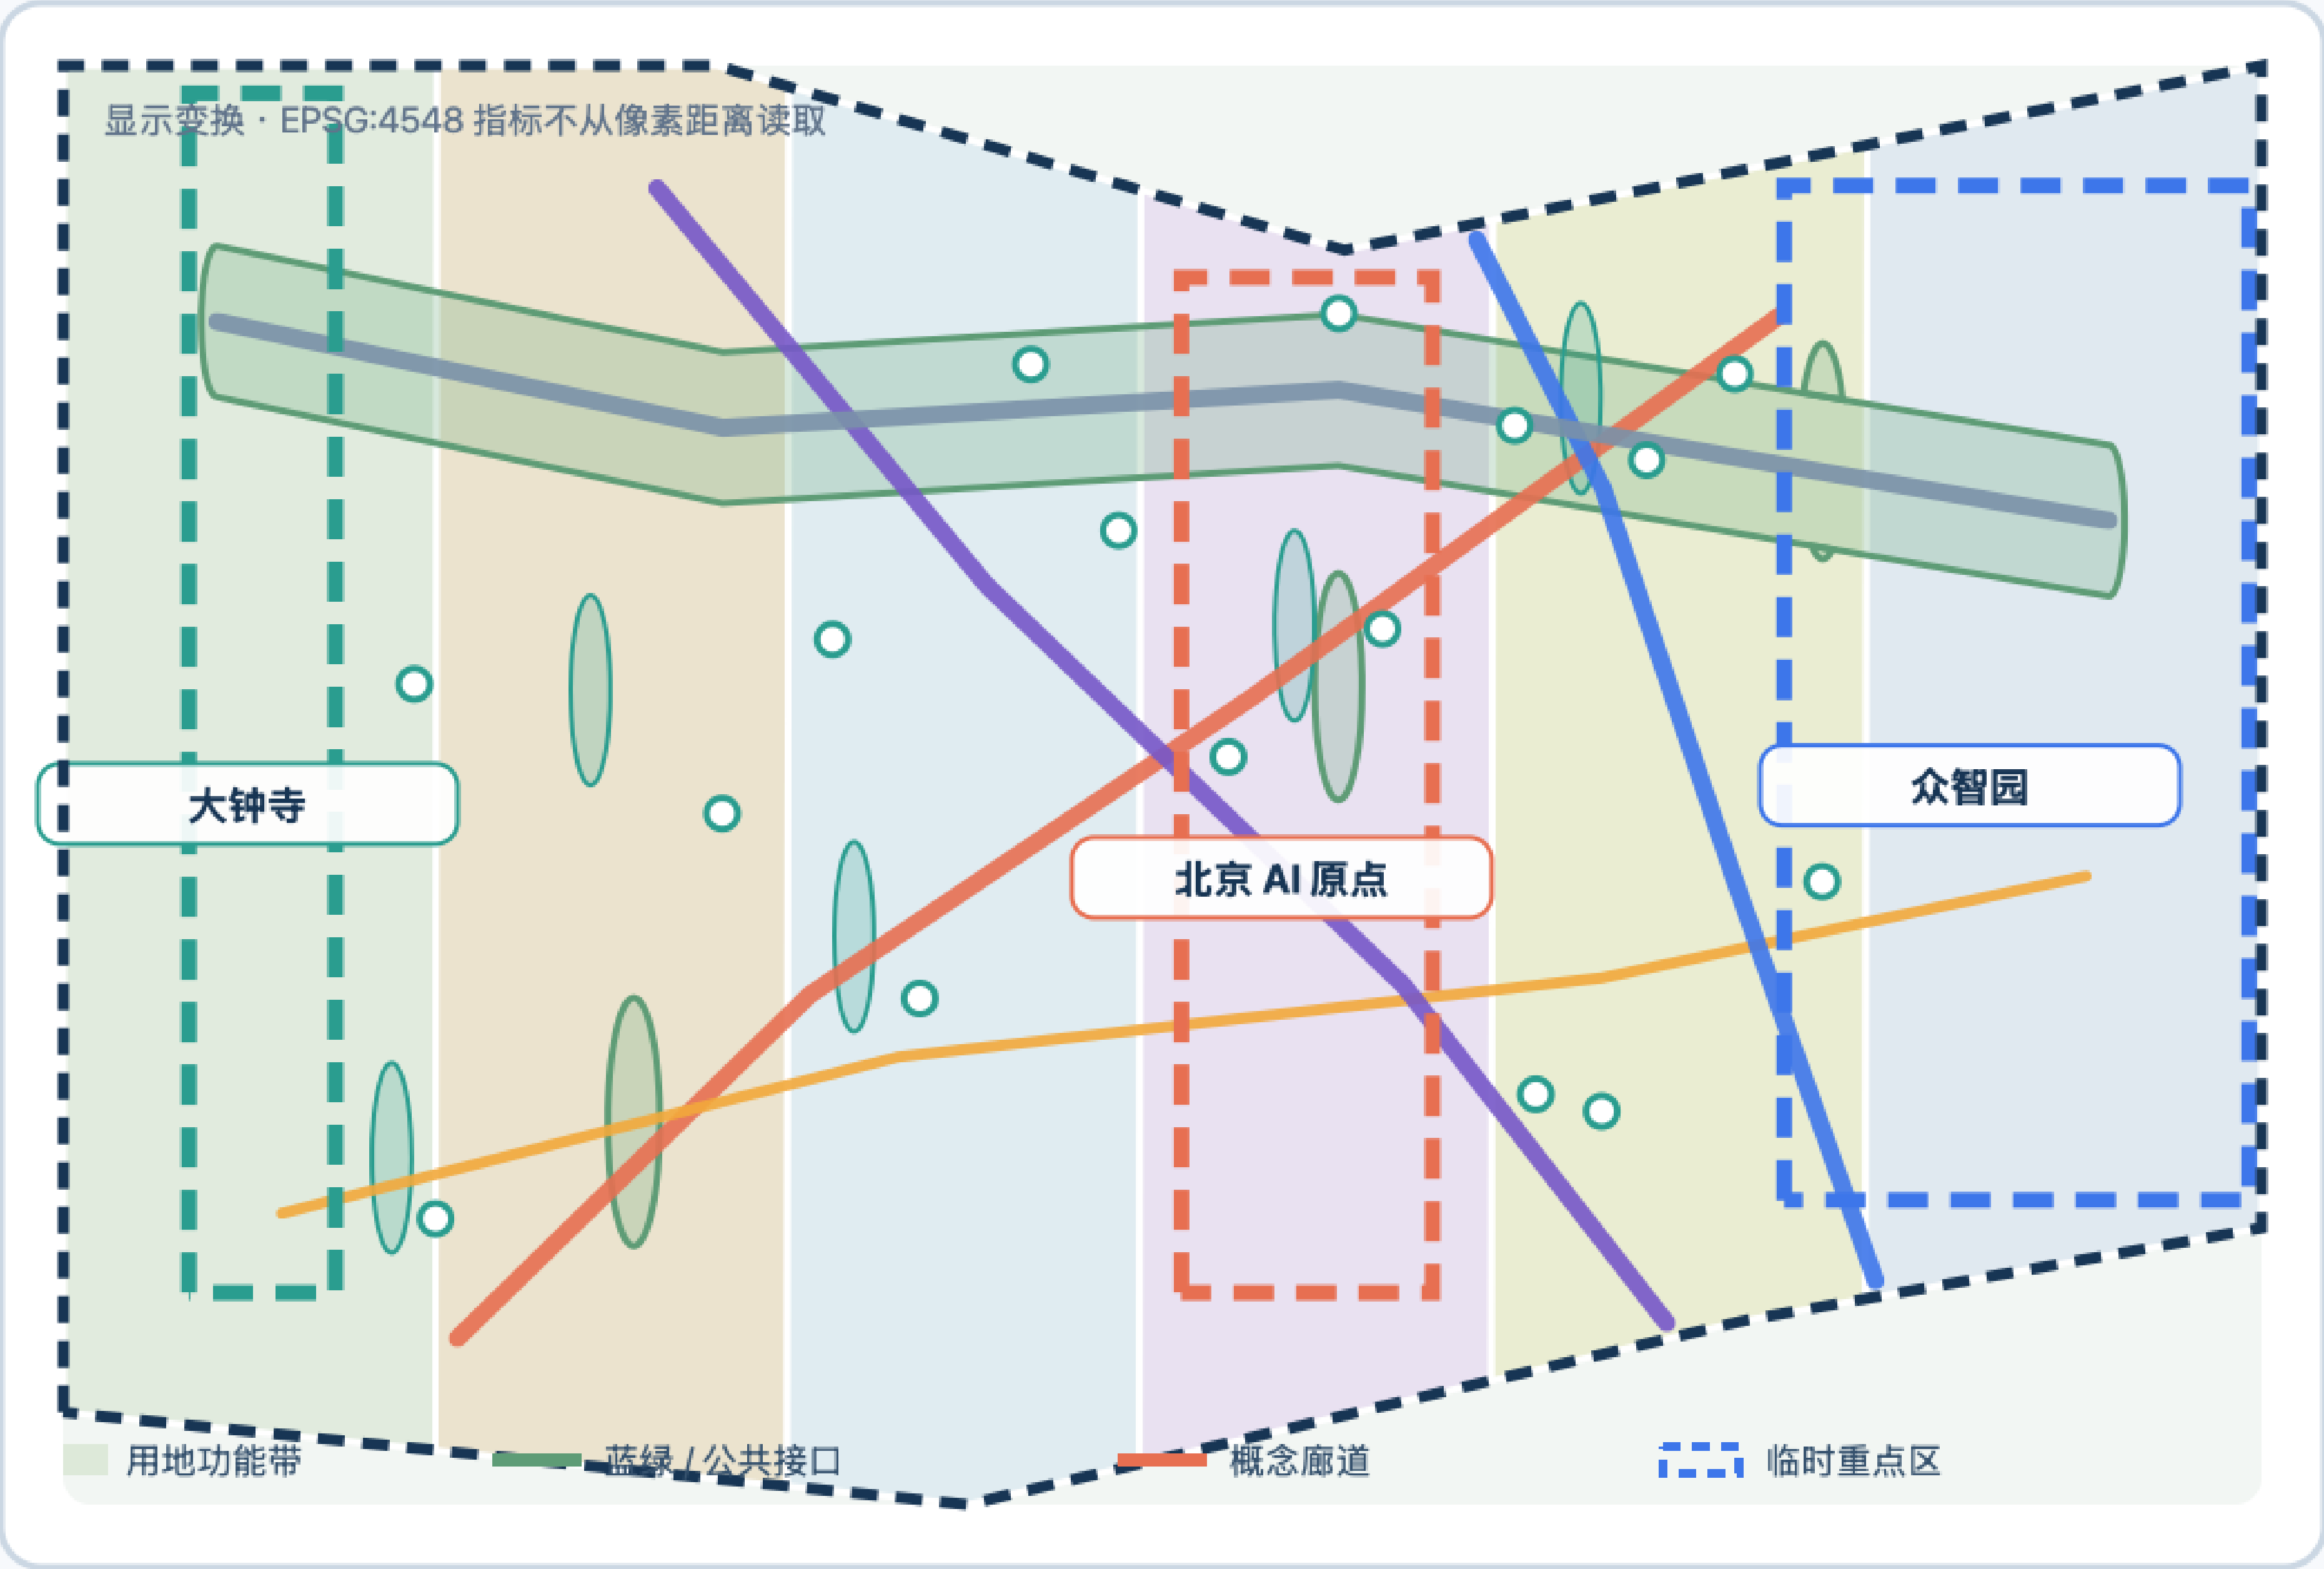

02 / 可读空间动作房间

	到达	解释	受限	停留	退出 / 回放
北京 AI 原点社区 PROV-KEY-002 official_boundary=false 普通人怎样先不用 AI 也能办事、学习与退出？ 人工等效 + 停止 / 回退	01 · 人工 先看到人工柜台、纸面和电话入口。 人工工作人员 / 纸面 / 电话 停止 / 回退	02 · 选择 把保留账本、小商户回迁议事放在可见公共空间。 人工居民代表解释 / 申诉 停止 / 回退	03 · 受限 登记 → 再培训 → 带薪岗位路径逐一。 人工人工职业咨询 / 岗位转介 停止 / 回退	04 · 无屏 用树荫、声音、静态导视和夜间安心边界。 人工现场求助 / 陪行 停止 / 回退	05 · 回放 保留纸面凭证、版本差异和异议入口。 人工人工答复 / 删除 停止 / 回退
众智园 PROV-KEY-001 official_boundary=false 机器测试怎样在公共空间里被接管并退出？ 人工等效 + 停止 / 回退	01 · 人工 把普通步行、人工求助与测试入口分开标识。 人工步行 / 静态提示 / 人工引导 停止 / 回退	02 · 选择 把最小字段、日志、撤销和异议放到公共空间。 人工工作人员解释用途 停止 / 回退	03 · 受限 只在可关闭的概念单元记录进入、接管和退出。 人工停机 / 疏散 / 事故复盘 停止 / 回退	04 · 无屏 把行洪、海绵和无屏退避作为机器界面的替代。 人工避险导视 / 人工巡检 停止 / 回退	05 · 回放 公开可删减的事件记录，决定修复、撤回。 人工独立复核 / 公众异议 停止 / 回退
大钟寺 AI 产业聚集区 PROV-KEY-003 official_boundary=false 创新怎样变成可理解、可质疑用的日常公共服务？ 人工等效 + 停止 / 回退	01 · 人工 把问题、资料边界和人工解释做成可读入口。 人工人工登记 / 纸面目录 停止 / 回退	02 · 选择 把一人公司、小团队的公平申请和冲突披露。 人工公开申请 / 人工预约 停止 / 回退	03 · 受限 把通过回放的路权、数据和适老模板登记。 人工人工审阅 / 异议窗口 停止 / 回退	04 · 无屏 以多语、医疗导航和知识产权清单支持访问。 人工人工翻译 / 线下转介 停止 / 回退	05 · 回放 年度体检、变更、撤回和待补资料一起进入。 人工责任回复 / 公众复核 停止 / 回退

几何

7 个 GeoJSON 图层 · 仅显示变换

指标

11.41 km² 临时输入 · EPSG:4548

人工路径

纸面 / 电话 / 人工申诉保留

缺口

官方边界 · 权属 · 安全 · 能源 · 现场基线

阅读规则

每一行都沿用同一条评审契约：到达 → 人工解释 → 受限接口 → 无屏停留 → 人工退出 / 回放。任何卡片都不是运营结果，也不是官方红线。

official_boundary=false · geometry_role=provisional_constraint · 概念建议，供专业团队深化研究


三处重点区：空间动作先于口号

把“做什么、谁接手、何时停止”放进临时空间证据；三处均不构成官方红线

v0.2 · 概念建议

01 众智园 AI 自主创新加速区

机器进入前先交出停止权

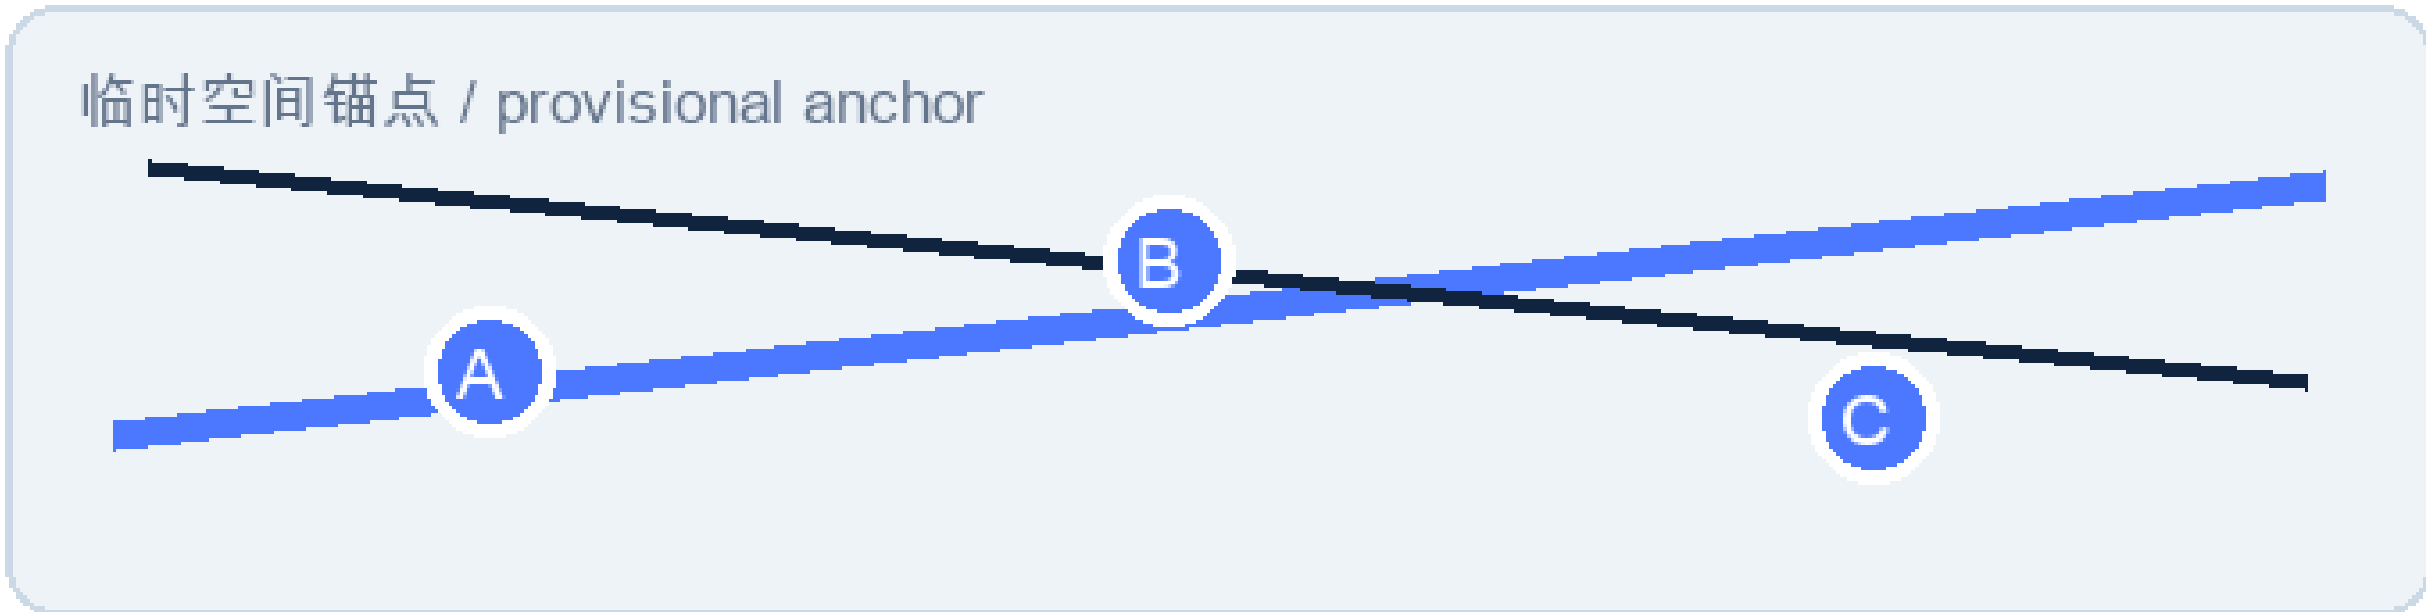


- 1 人工前场
行人、无障碍和人工求助先进入
- 2 受控测试
低速、限时、可撤回
- 3 事故复盘
正负结果、异议与删除
- 4 海绵缓冲
模拟与巡检，不宣称性能

空间引用：PROV-KEY-001 · SC-B02 · SC-C03 · ROAD-B-SILICON · GREEN-C-SPONGE

角色类别：交通/能源/水务/安全/公众观察

02 北京 AI 原点社区

让转型和公共服务留在日常路径

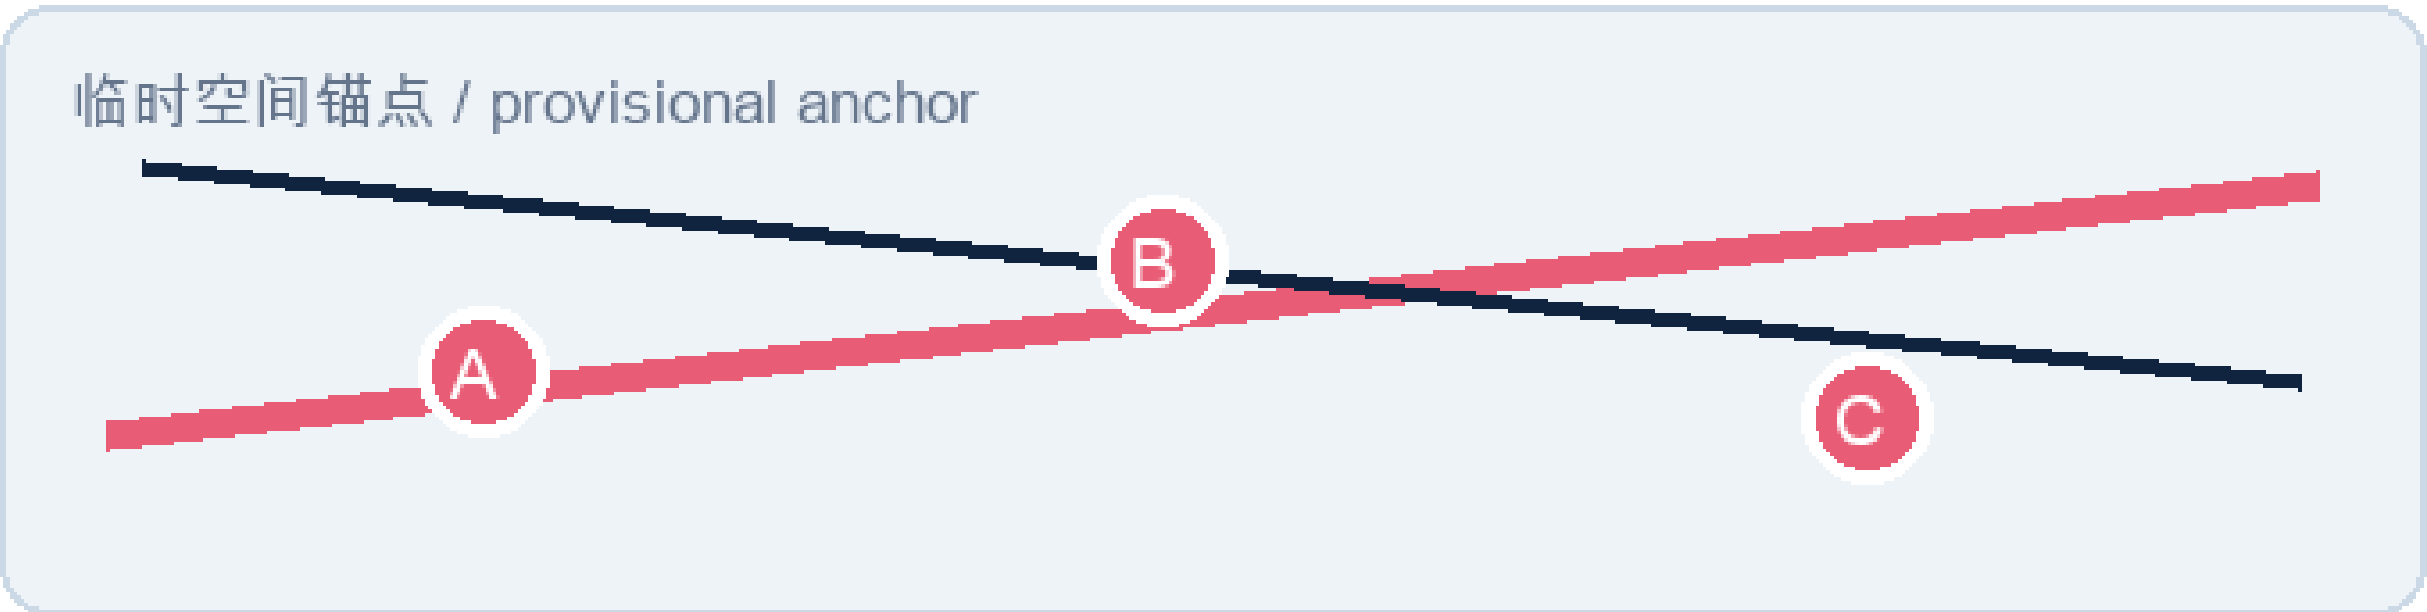


- 1 人工入口
柜台、电话、纸面不被迁走
- 2 技能再造
能力—带薪培训—试岗—新角色
- 3 社区保留
空间支持不等于保留率
- 4 版本发布
问题、暂停、待补资料公开

空间引用：PROV-KEY-002 · SC-A02 · SC-A03 · ROAD-A-SKILL · PUBLIC-A-INCLUSION

角色类别：社区/就业/无障碍/资料责任

03 大钟寺 AI 产业聚集区

把数据、算电和国际服务变成可读接口

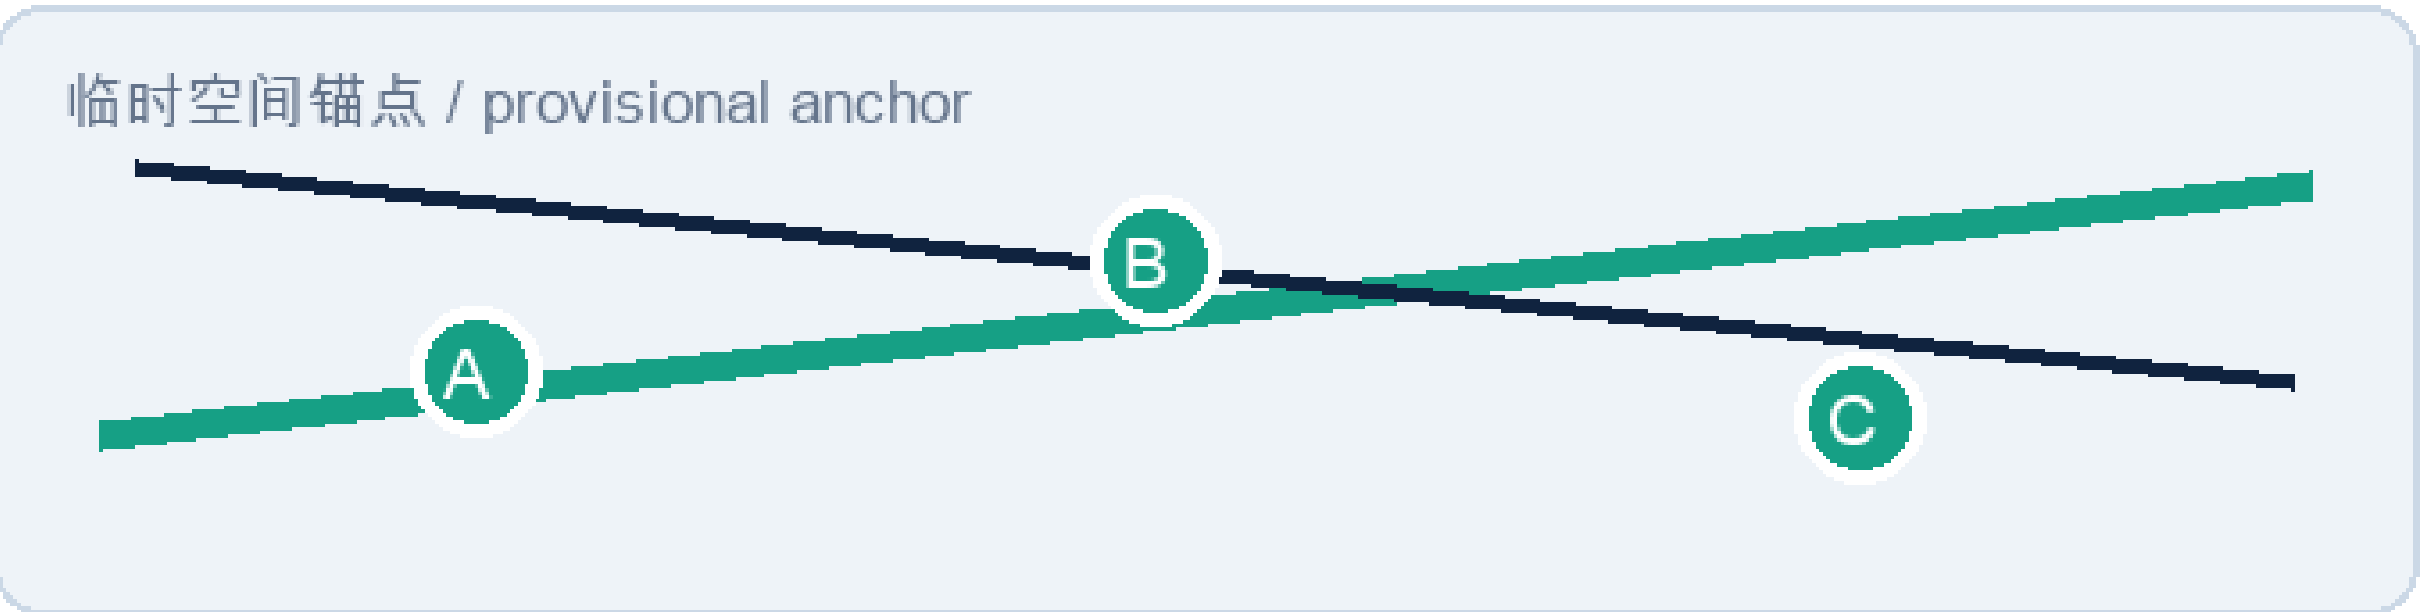

- 1 数据授权
目录—授权—调用—日志—退出
- 2 算电审计
PUE、绿电、热需求先核验
- 3 小团队服务
共享实验、法务和公平申请
- 4 国际客厅
多语、医疗导航、人工解释

空间引用：PROV-KEY-003 · SC-C01 · SC-C04 · SC-D03 · BLDG-C-01 · BLDG-D-01/02

角色类别：数据/能源/OPC/多语服务

临时锚点 / 先回答的问题

到达与人工入口

公共解释与选择

受限机器接口

蓝绿停留与恢复

退出、申诉与回放

北京 AI 原点社区 PROV-KEY-002 · official_boundary=false 普通人怎样先不用 AI 也能办事、学习与退出? GeoJSON 锚点与场景 ID 见同名 JSON 审计。 geometry_role=provisional_constraint	01 · 连续步行 / 人工入口 先看到人工柜台、纸面和电话入口。 人工等效 工作人员 / 纸面 / 电话 机器边界 不要求扫码或情绪识别 停止 / 回退 入口或无障碍不清 → 只补资料	02 · 代际共学 / 社区保留 把保留账本、小商户回迁议事放在可 人工等效 居民代表解释 / 申诉 机器边界 AI 只整理问题，不替人决定 停止 / 回退 无知情基线 → 不发布保留率	03 · 技能再造接力站 登记 → 再培训 → 带薪岗位路径逐段 人工等效 人工职业咨询 / 岗位转介 机器边界 不以培训人次替代就业结果 停止 / 回退 无岗位路径 → 回到 v0.1	04 · 无屏恢复花园 用树荫、声音、静态导视和夜间安心 人工等效 现场求助 / 陪行 机器边界 不采集、不推荐、不强制交互 停止 / 回退 强制采集或安全盲区 → 撤回	05 · 普通服务 / 版本回放 保留纸面凭证、版本差异和异议入口。 人工等效 人工答复 / 删除 机器边界 不留不可撤的数据链 停止 / 回退 无法独立回放 → 不发布
众智园 AI 自主创新加速区 PROV-KEY-001 · official_boundary=false 机器测试怎样在公共空间里被限制、接管并退出? GeoJSON 锚点与场景 ID 见同名 JSON 审计。 geometry_role=provisional_constraint	01 · 人行优先观察边缘 把普通步行、人工求助与测试入口分 人工等效 步行 / 静态提示 / 人工引导 机器边界 先申报时段、权限、退出 停止 / 回退 无安全断面或接管 → 观察门	02 · API 授权解释台 把最小字段、日志、撤销和异议放到 人工等效 工作人员解释用途 机器边界 最小权限、可撤销、可回放 停止 / 回退 越权或无日志 → 冻结调用	03 · 具身测试口袋 只在可关闭的概念单元记录进入、接 人工等效 停机 / 疏散 / 事故复盘 机器边界 一次演示不得扩区 停止 / 回退 事故、保险或回放缺一 → 退回	04 · 小月河翼海绵退避 把行洪、海绵和无屏退避作为机器界 人工等效 避险导视 / 人工巡检 机器边界 不以模拟替代水文审查 停止 / 回退 无蓝线或校准 → 不扩展	05 · 事故复盘 / 版本回退 公开可删减的事件记录，决定修复、撤回或回到 人工等效 独立复核 / 公众异议 机器边界 不可独立回放即停机 停止 / 回退 无法回放 → 不扩区
大钟寺 AI 产业聚集区 PROV-KEY-003 · official_boundary=false 创新怎样变成可理解、可质疑、可复用的日常公共 GeoJSON 锚点与场景 ID 见同名 JSON 审计。 geometry_role=provisional_constraint	01 · 城市问题台 把问题、资料边界和人工解释做成可 人工等效 人工登记 / 纸面目录 机器边界 只交换已授权的最小问题 停止 / 回退 权属或授权不清 → 只公开问题	02 · OPC 公平申请面 把一人公司、小团队的公平申请和冲 人工等效 公开申请 / 人工预约 机器边界 不指定企业或供应商 停止 / 回退 资源分配不透明 → 暂停开放	03 · 版本 / 标准回放台 把通过回放的路权、数据和适老模板 人工等效 人工审阅 / 异议窗口 机器边界 不冒充国家或行业标准 停止 / 回退 不能独立回放 → 不外溢	04 · 多语服务客厅 以多语、医疗导航和知识产权清单支 人工等效 人工翻译 / 线下转介 机器边界 不以品牌替代实际能力 停止 / 回退 服务能力未核验 → 保留普通路径	05 · 发布、撤回与回放 年度体检、变更、撤回和待补资料一起进入 relea 人工等效 责任回复 / 公众复核 机器边界 没有证据不升级版本 停止 / 回退 未回应异议 → 留在上一版

共同空间规则


可读的人行到达 → 公共解释 → 受限接口 → 无屏停留 → 人工退出与回放。官方几何、权属、安全、无障碍、能源、气候与公众基线到位前，所有动作保持概念建议。

概念建议 / 临时约束 · 不产生官方边界、工程断面、容量、许可或运营结果

京张人本城市操作系统 | 空间裁决回执

先保住人的主线，再决定机器如何进入 · HOLD / 概念桌面回放

三种空间组织

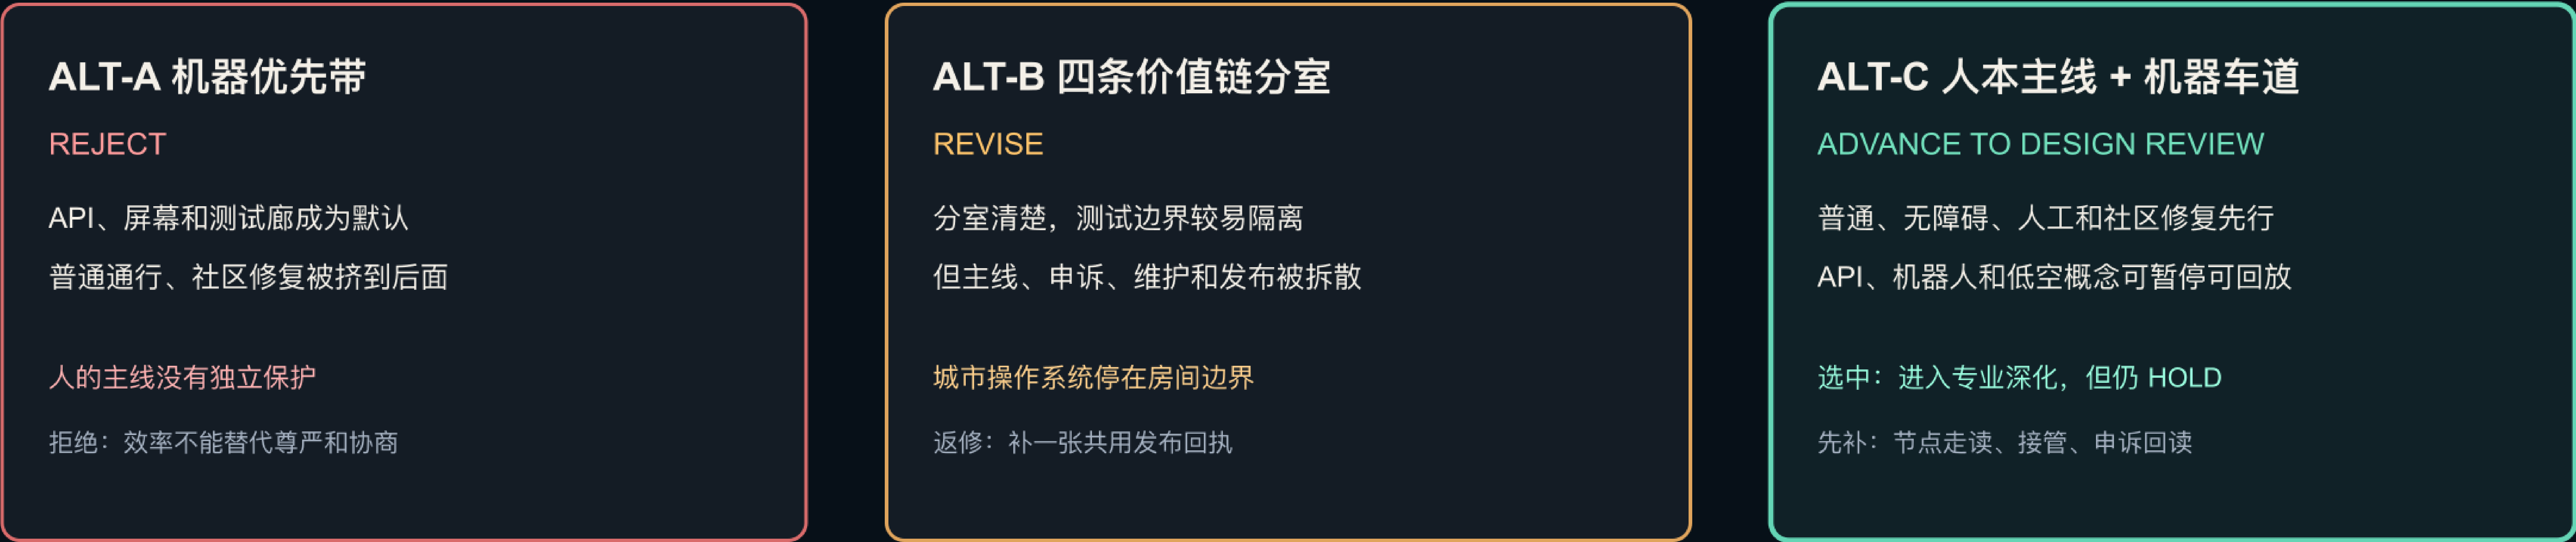

尺度链：从价值链关系落到可读的发布交接



五项公共权利

人的尊严/普通可达 · 非数字等价/无障碍 · 同意暂停申诉退出 · 社区修复保留 · 公共资产/隐私

0 授权 · 0 现场观察 · baseline unknown · not_authorized_not_run · 无现场声明

可选互操作层 | SEB 字段 crosswalk

只回接本包已公开合同字段；不是整包采用、硬门禁、正式评分或现场服务证明

SEB v0.5.0 的五个字段

① AI 关闭后的等价路径

② 人工接管角色

③ 当前闸门

④ 运行方式

⑤ 责任角色

source-of-record：包内台账

HC-T01 · 人工通道与代际共学

人工 / 电话 / 纸本 / 无设备入口 | 公共服务值守角色（待指定）

SC-A03 · PHASE-V01 → SEB G0 · 等价路径逐字来自 human_alternative

HC-T02 · 城市 API 授权解释台

人工复核 / 撤销授权 / 非数字说明 | 数据责任与独立复核角色（待指定）

SC-B01 · PHASE-V02 → SEB G0 · 权限越界或目的漂移时冻结

HC-T03 · 监管沙盒事故复盘台

人工暂停 / 现场处置 / 公开申诉 | 测试责任与事故响应角色（待指定）

SC-C03 · PHASE-V02 → SEB G0 · 无人工停机即不进入测试

HC-T04 · 多语公共服务客厅

人工翻译 / 电话 / 图标 / 纸面表单 | 多语人工服务与内容校对角色（待指定）


SC-D03 · PHASE-V01 → SEB G0 · 双语不一致时停止数字导览

HOLD · contract_check_only · authorization=0 · field_observations=0 · baseline=unknown · performance=null


5 个负例分别拒绝数字依赖、角色缺失、非法闸门、运行方式缺失与来源字段改写；PASS 不等于采用或成效。

一个公共服务节点，三张可被追问的图

ALT-C：普通入口、低位人工台和退出路径先于可撤回 AI 服务岛

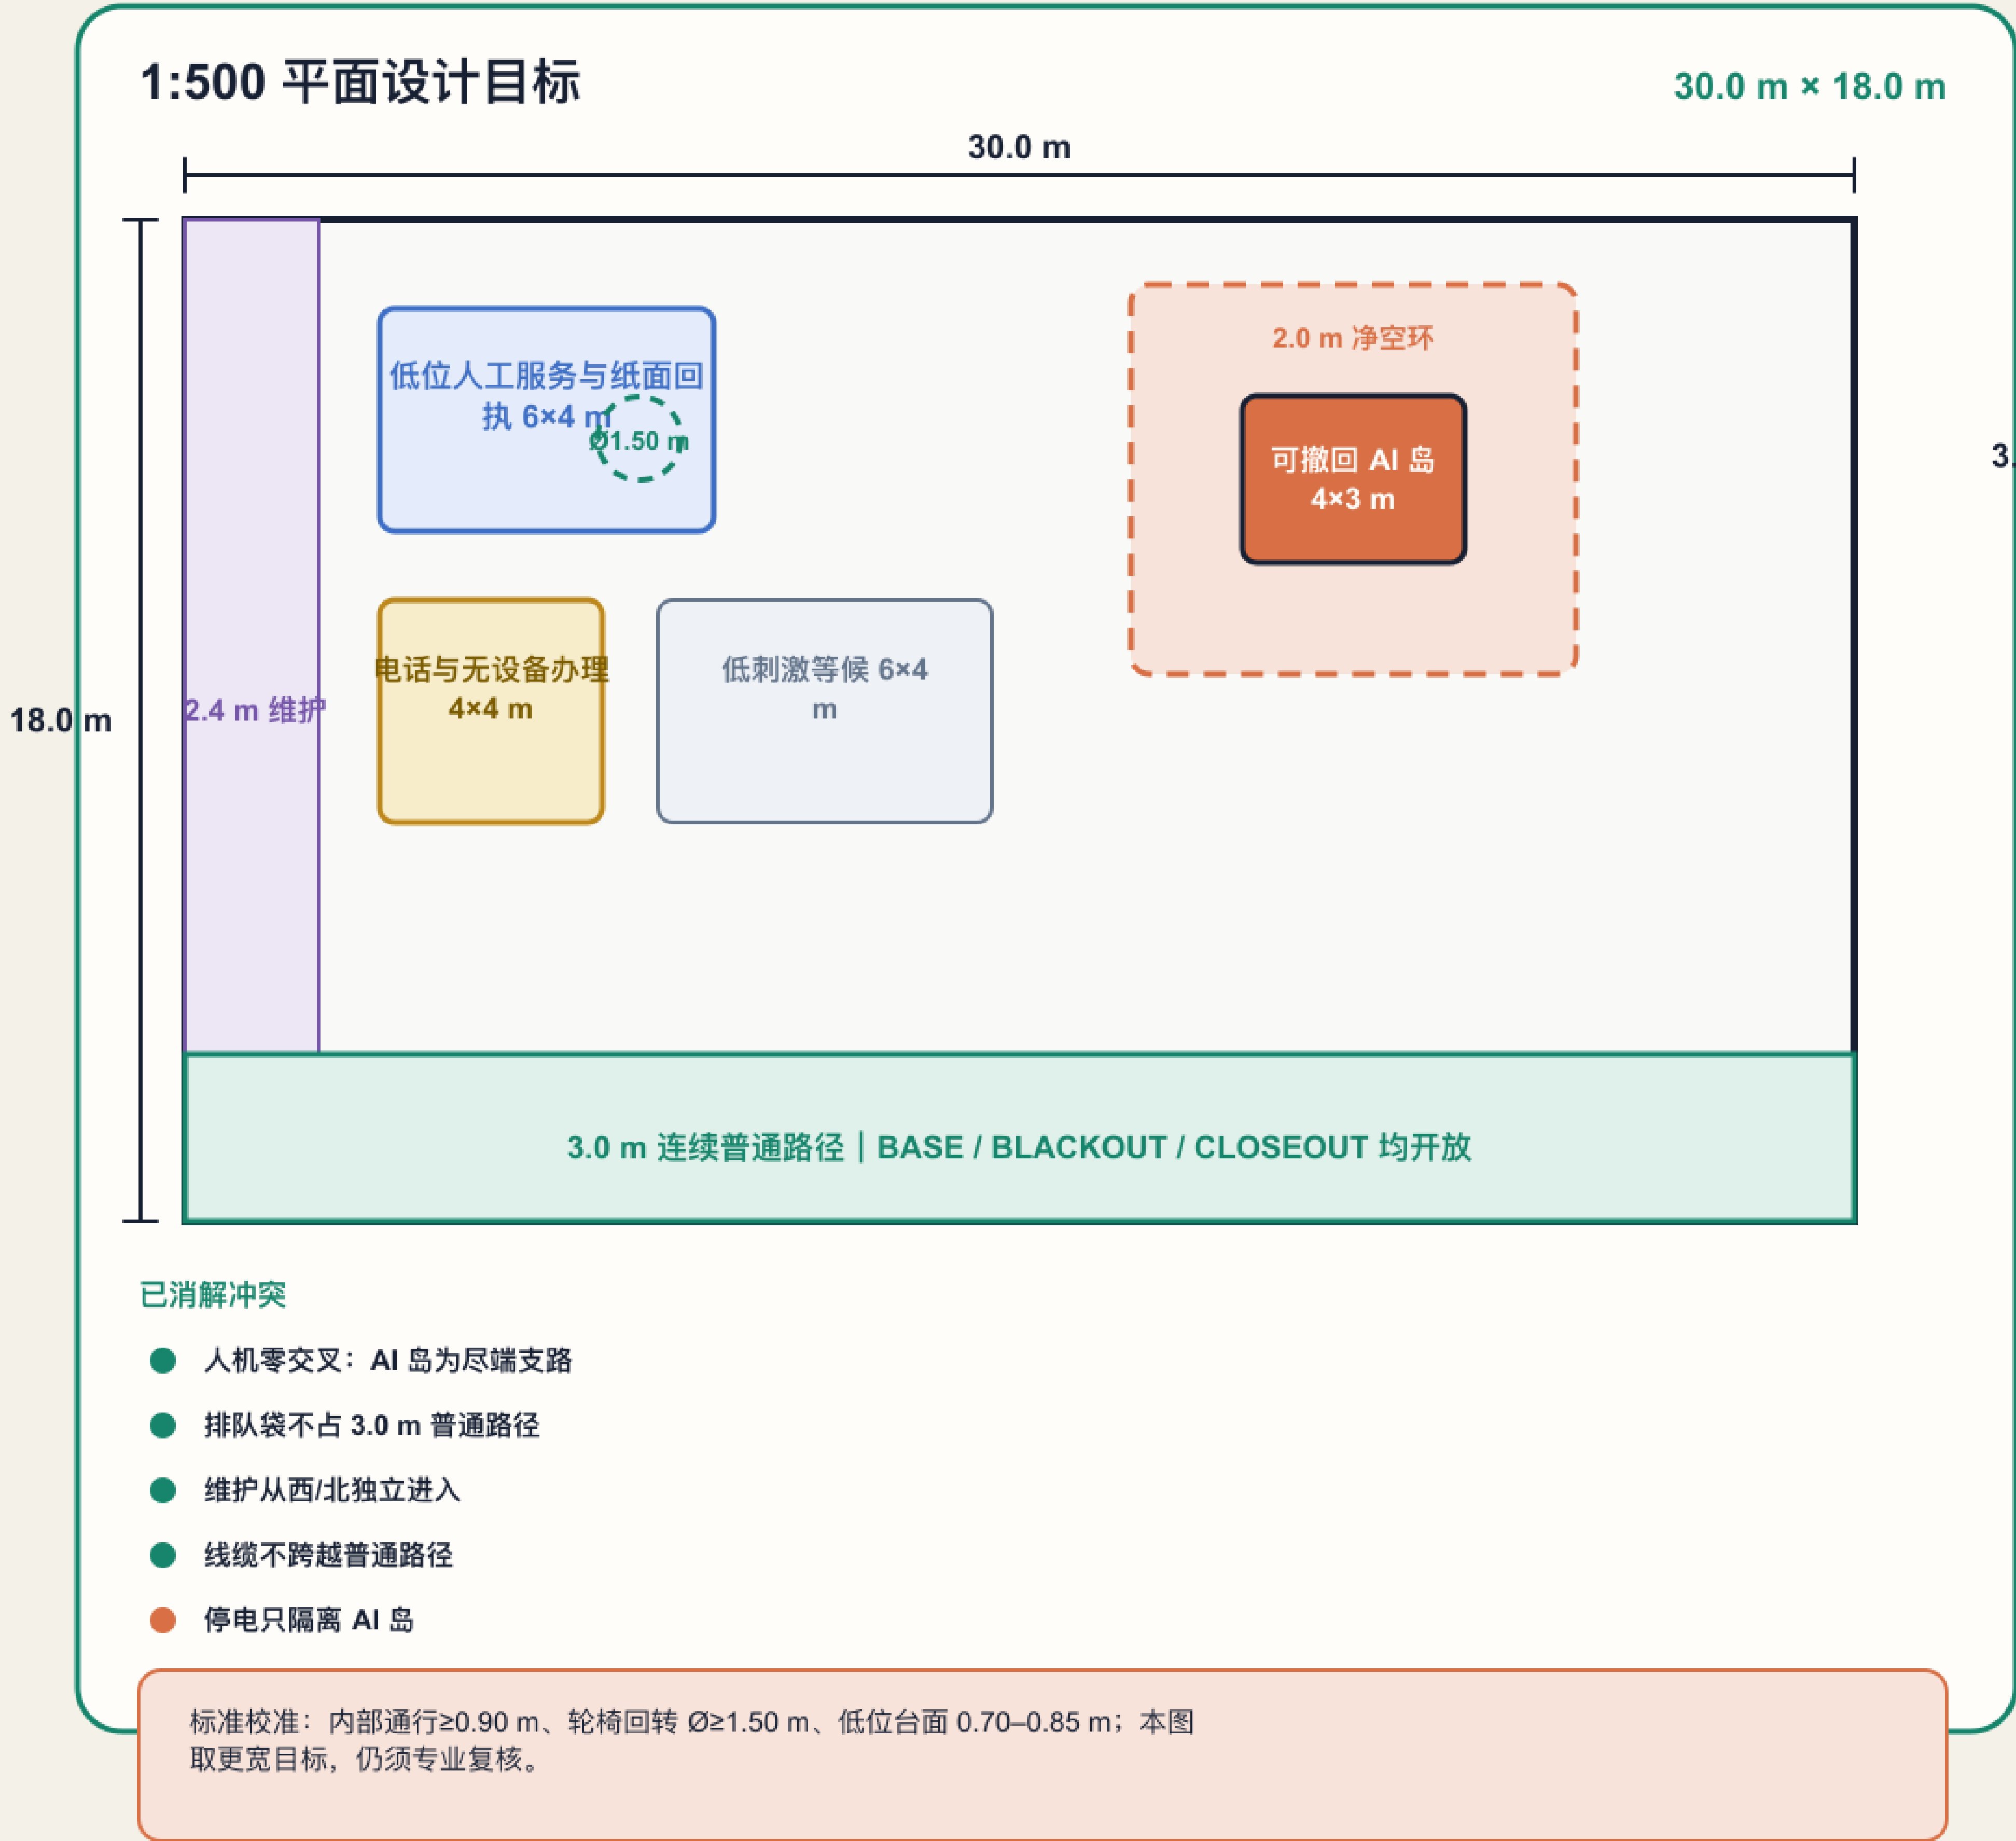

1:100 剖面 | 通行、服务、设备与维护不抢一条线

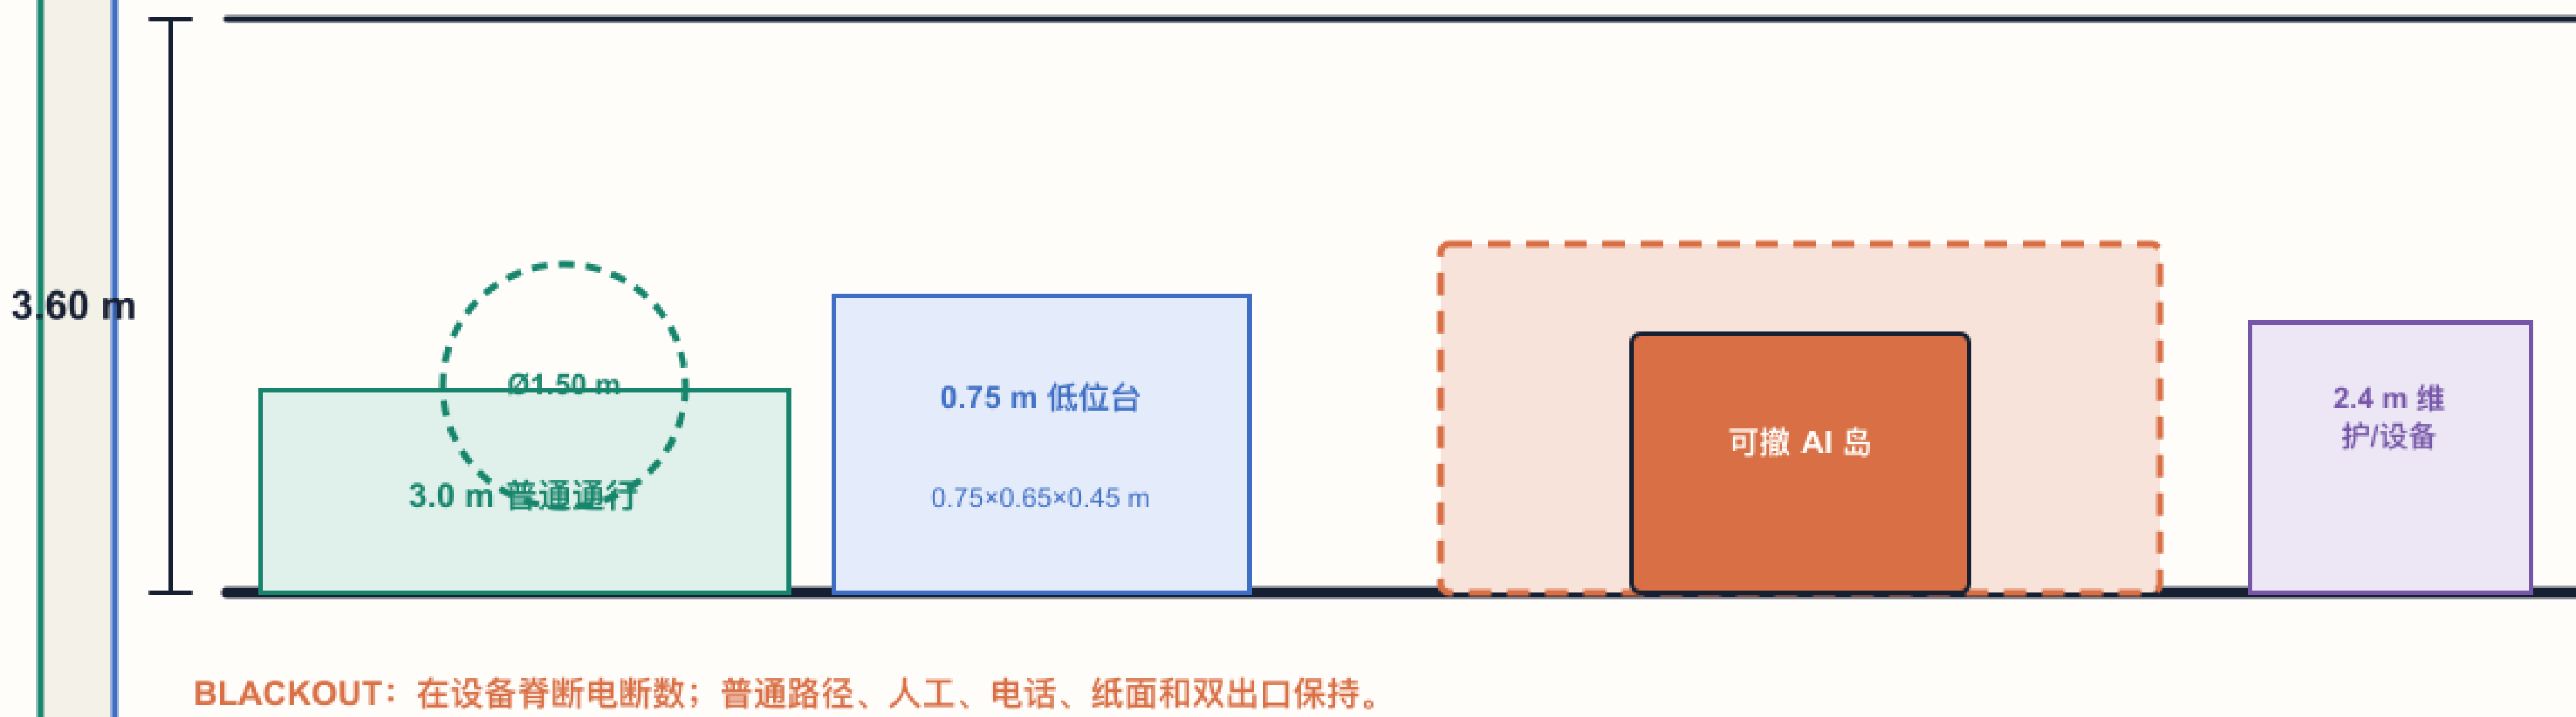

1:50 节点与放大 | 把“可撤回”落到构造动作

低位人工台

台面 0.75 m | 膝部净空 0.75×0.65×0.45 m
轮椅回转 Ø1.50 m；前方不设门槛

人工停用控制

操作中心 0.95 m | 标准校准 0.85–1.10 m
一键隔离 AI 岛，不切断人工/电话

可拆设备接口

模块 1.20×0.60 m | 封闭退避槽 0.30 m
拆除→封口→恢复地面，不留绊倒线缆

门与排队袋


门净宽目标 1.00 m | 排队袋 2.40×4.00 m
门扇、轮椅回转与疏散线不冲突

仍缺：授权测绘、消防/无障碍签字、公众走查、权属与市政核验。
0 authorisations · 0 field observations · release_capacity=null · HOLD

从角色到退役：一份不假装已经落地的交付回执

18 周条件式路径、数量×单价成本、RACI、SLA、保险与双回退

18 周条件式依赖链 | 全部 G0 通过后才起算

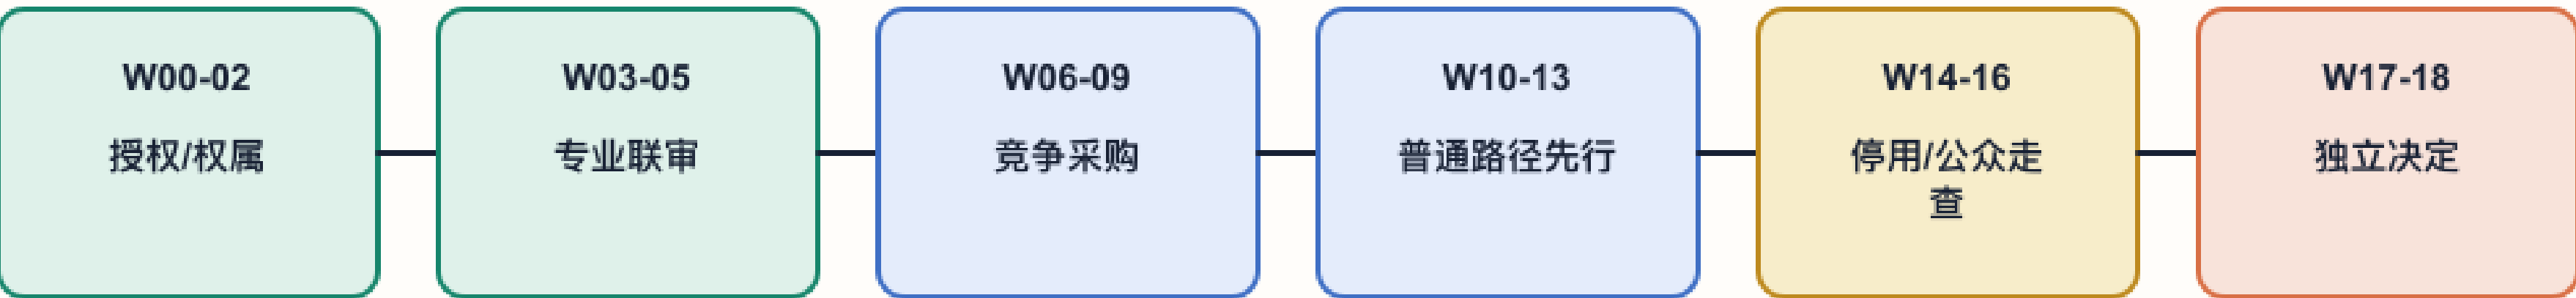

每阶段必须提交可签署的放行证据：任何无障碍、消防、隐私、同意或责任重大失败都退回 HOLD。

采购：两阶段、性能导向、竞争性、公开数量与单价；无指定供应商。

付款节点：普通路径、停用、移交和退役证据通过后。

数量 × 单价概念成本 | 低置信，不是招标价

测绘/设计/专业复核	1 项	10–15 万
普通路径与可逆地面	180 m² × 800–1200	14.4–21.6 万
人工/纸面服务装修	24 m² × 4500–6500	10.8–15.6 万
可撤 AI 岛/离线接口	12 m² × 1.2–1.8 万	14.4–21.6 万
导视/无障碍接口	1 项	8–12 万
测试/培训/恢复	1 项	8–12 万
CAPEX +15% 预备金		75.44–112.47 万元
月 OPEX：320 人时服务 + 维护 + 翻译/无障碍 + 数据/独立审计，再加 10% 预备金		3.278–5.434 万元/月

RACI 资产交接 | 所有机构角色尚未确认

资产	R 负责	A 问责	C 共审
普通路径/地面	现场施工角色	公共资产所有者	无障碍/消防
人工/电话/纸面	公共服务运营角色	服务委托角色	社区/无障碍
可撤回 AI 岛	样机供应角色	试点运营角色	数据/安全
日志/同意/投诉	数据保护角色	服务委托角色	独立复核
退役与恢复	维护/施工角色	公共资产所有者	运营/社区

所有 A 角色须在采购前具名并签字；当前 status=role_unconfirmed。

五条 SLA | 全部是未观察设计目标

- 普通路径 + 人工/电话/纸面服务始终可完成
- 停用触发后 2 分钟内隔离 AI 岛
- 投诉 1 工作日确认、5 工作日给状态
- 开闭场签署路径/电话/纸面/断电/维护检查
- 无障碍/消防/隐私/同意重大失败即归零

退役：断电拆岛、封接口、恢复地面、保留普通服务、通知公众、关闭投诉并归档。

放行仍需：具名所有者、正式几何、专业签字、知情同意公众走查、成本确认、保险和独立决定；当前均未确认。