

京张明带 · 数字山水

人机切换的公共空间基础设施

一个命题 · 五张证明 · 三个可退出试点

图册结构

01 COVER / 02 CONTEXT + DATA GAPS / 03 OVERALL / 04 LAND USE / 05 MOBILITY

06 KEY-AREA INDEX / 07 RESPONSIBILITY-BOUNDARY-EXIT / 08-10 AREA EVIDENCE SHEETS


11 TWELVE-NODE MATRIX + THREE EXAMPLES / 12 METRICS + UNKNOWN CONTROLS

总体设计与三重点区


一条公共空间骨架 · 三处差异化试点 · 十二个可复核服务节点

THE LUCID SHANSHUI


01 开放数据语境 / 临时范围

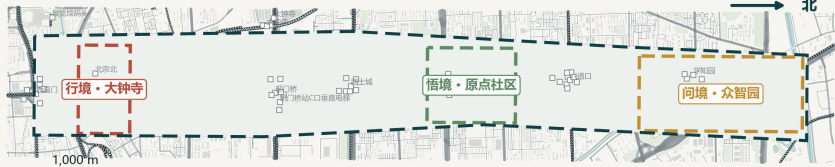

02 空间分配 / 概念体量

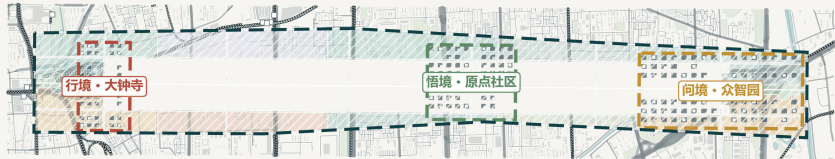

03 地面通行 / 服务网络

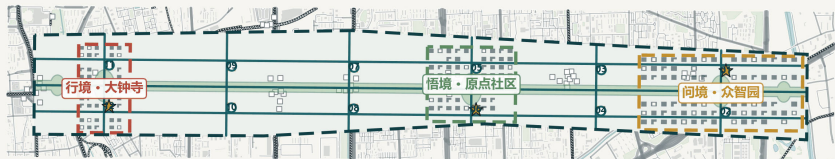

明责 · 明界 · 明退

责

每个服务节点标明责任角色与人工复核人

界

默认地面、非数字可达；AI只在声明范围内试点

退

证据不足或KPI失效时缩减、停止并恢复通行

OSM开放数据语境

仓库 provisional

本提案设计模型

资料缺失/禁作结论

11.41 km² 临时总体范围

03 重点区

12 + 3 服务节点 + 地标

153 概念体量

概念设计 | 边界与重点区为 provisional 粗略几何 | 正式数据发布后须整体复算

方案：提交包 GeoJSON / metrics.json;
现状语境：© OpenStreetMap contributors, ODbL 1.0, 2026-08-21; 非官方红线与工程依据

FIG-01 / SITE OVERVIEW

现状语境、政策依据与资料缺口


把已公开任务依据、临时几何、设计模型与待补专业资料分层表达

THE LUCID SHANSHUI

公开任务依据 可引用名称/层级/公告面积	OSM开放语境 4,940要素 完整性待核	仓库临时几何 1总体 + 3重点区 非法定	本图隐藏方案 不以概念体量冒充现状
--	---	---	---

已有依据 / 可用边界 • 公开公告：项目名称、三级任务范围与公告约面积；不提供可用正式红线。 • 2026-08-12批复新闻：仅证明批复状态；批复成果图文/矢量数据尚未入库。 • OSM开放数据：仅作道路、轨道、建筑、水绿与设施语境；并非测绘或审批底图。 • 经许可任务书：智能体任务、十二场景和交付要求。 • 仓库临时几何：1个总体范围、3个重点区；仅供概念比较与复算。 • 提交设计模型：用地、体量、中心线、绿地、公共空间和分期。

灰底为OSM开放数据语境；虚线为仓库临时范围；本图不显示方案体量、道路或绿地。

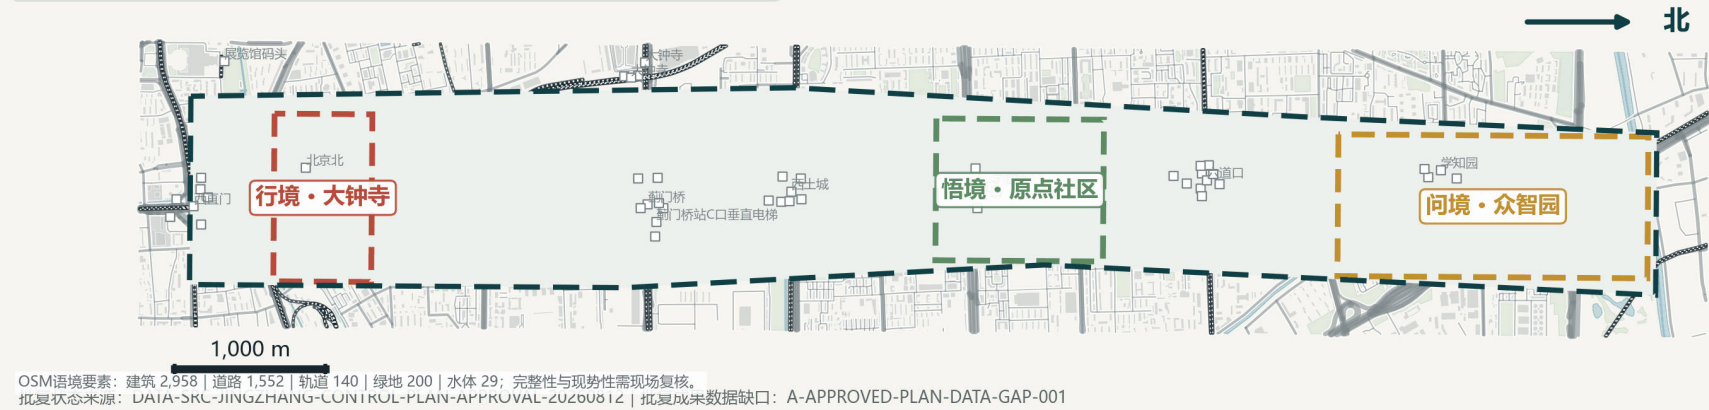

待补资料 / 结论禁区 • 已批规划成果、正式总体/重点区/地块/道路红线与法定控制 • 现状建筑、产权、人口与公共服务容量普查 • 轨道、文保、消防、地灾及其他刚性约束 • 地形标高、水文、排水、地下空间与岩土资料 • 市政管线、能源/算力接口、交通流量与运维能力 • 法定容积率、限高、密度、退线和拆改留结论
--




总体设计与三重点区


一条公共空间骨架 · 三处差异化试点 · 十二个可复核服务节点

THE LUCID SHANSHUI


01 开放数据语境 / 临时范围

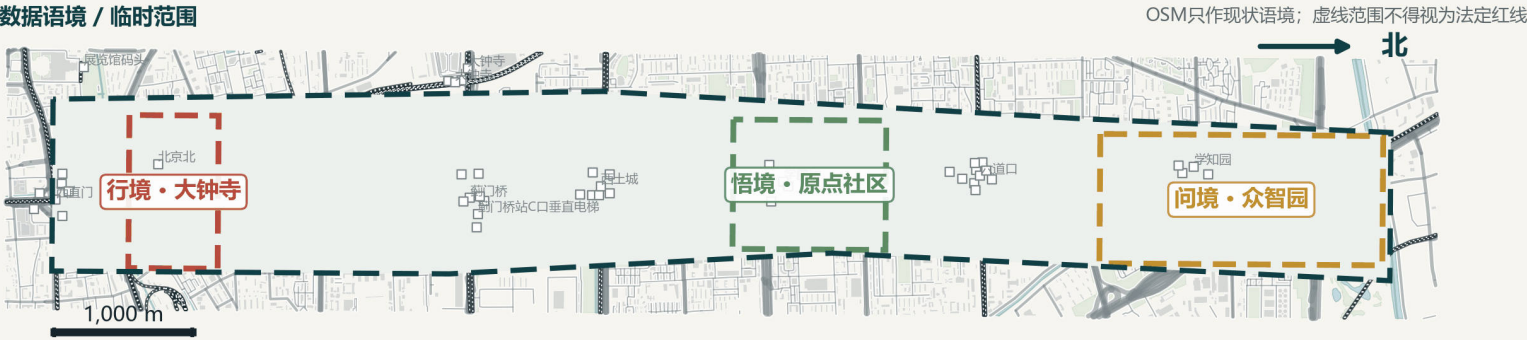

02 空间分配 / 概念体量

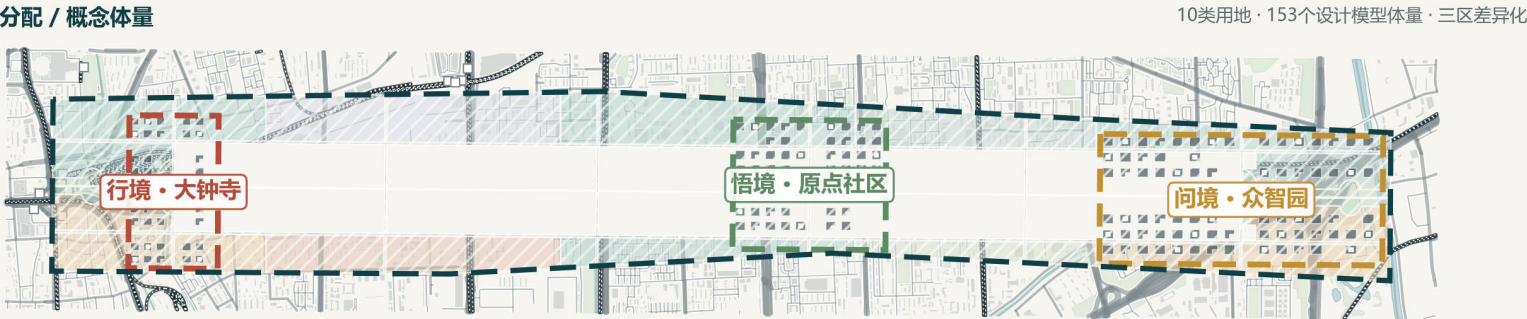

03 地面通行 / 服务网络

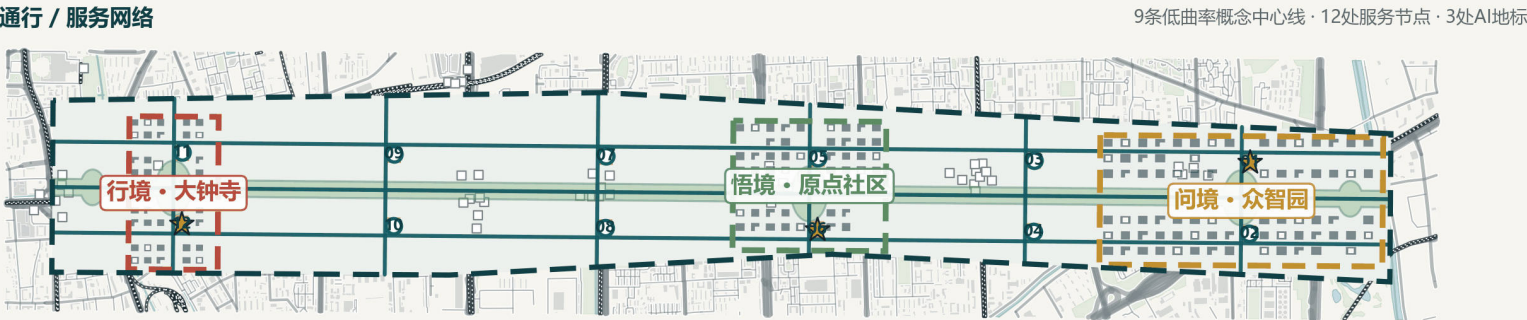

明责 · 明界 · 明退

责
每个服务节点标明责任角色与人工复核人

界
默认地面、非数字可达；AI只在声明范围内试点

退
证据不足或KPI失效时缩减、停止并恢复通行

OSM开放数据语境

仓库 provisional

本提案设计模型

资料缺失/禁作结论

11.41 km² 临时总体范围

03 重点区

12 + 3 服务节点 + 地标


153 概念体量

概念设计 | 边界与重点区为 provisional 粗略几何 | 正式数据发布后须整体复算

用地结构与空间闭合

全部用地单元来自同一场地分割；面积以 EPSG:4548 复算

THE LUCID SHANSHUI

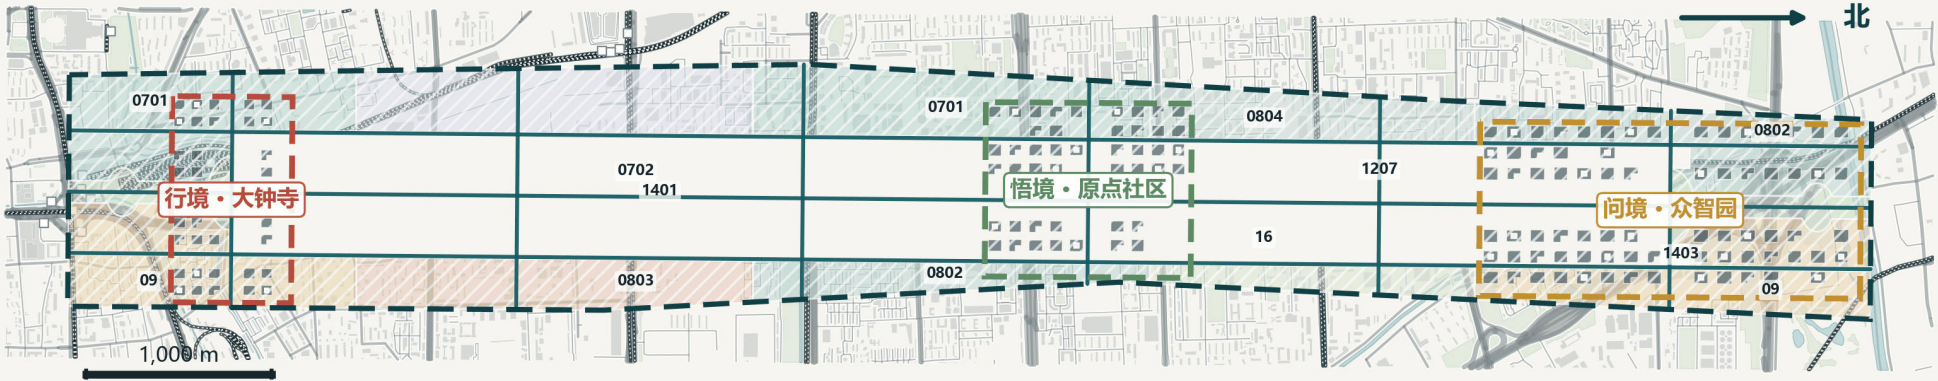

图例		
0701	居住与人才社区	18.1%
09	商业服务业	15.5%
0702	社区服务设施	11.3%
0803	文化展示	9.7%
0802	AI研发与创新	15.1%
0804	教育科研	7.7%
16	弹性留白	6.0%
1207	设计模型道路	4.6%
1401	公园绿地	11.0%
1403	公共广场与驿站	1.0%
100% 场地分区闭合		
容积率上限、建筑限高、退线和法定红线待官方条件补齐。		



设计模型值（非控规指标）

面积 → 代码 → GeoJSON → 指标


本图回答：方案如何分配空间；不回答：法定用地、地块权属、控规强度。

慢行 · 蓝绿 · 公共服务复合系统

从线性口号转为可定位、可计数、可退出的服务网络

THE LUCID SHANSHUI

OSM道路/轨道仅作开放语境；彩色实线路网/绿地/节点为概念设计，虚线范围为仓库临时约束

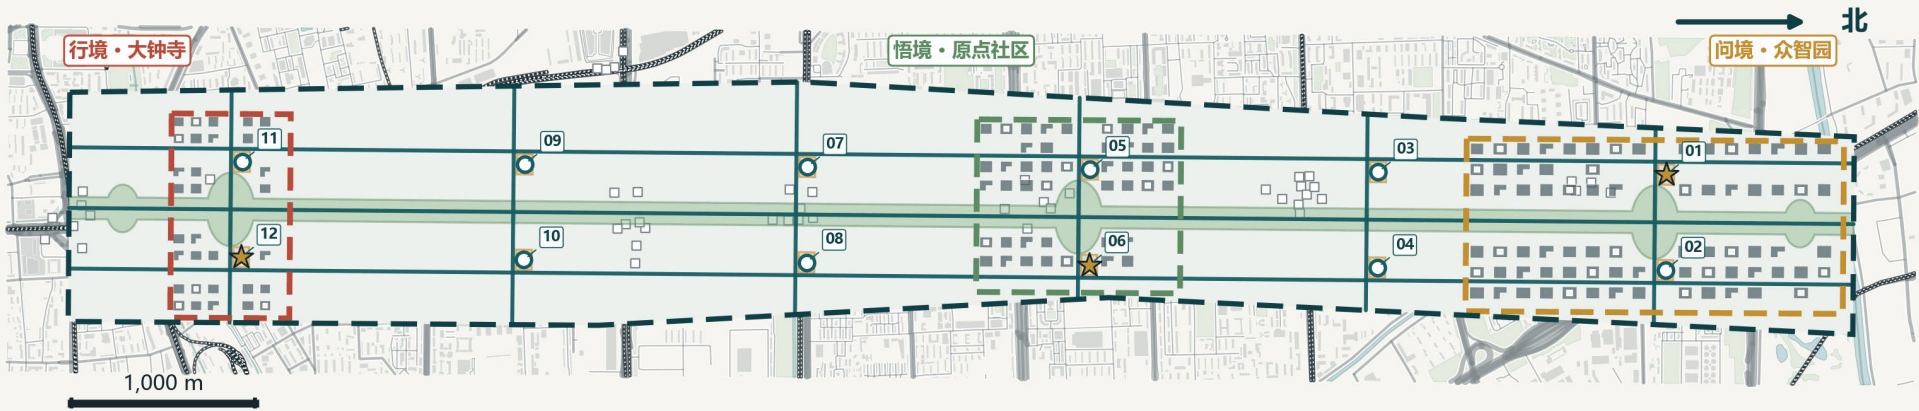

系统图例

- 低曲率概念主轴/直连 09
- 生态意向带 01
- 公共空间面 12
- 服务节点 12
- AI地标 03

默认断面

- 01 地面连续
- 02 无障碍优先
- 03 非数字可达
- 04 人工服务兜底

轨道接驳、交通容量、雨洪、蓝线和工程标高尚无核资料。

非AI基线用户旅程

- 01 看见实体导向
- 02 沿地面连续通行
- 03 人工前台完成服务
- 04 纸面/电话反馈
- 05 安全离场

方案：提交包 GeoJSON / metrics.json;
现状语境：© OpenStreetMap contributors, ODbL 1.0, 2026-08-21; 非官方红线与工程依据


FIG-04 / MOBILITY + BLUE-GREEN

三处重点区概念深化

THE LUCID SHANSHUI

并列对照：各片区按自身范围适配，比例尺见图内标注

01 问境 · 众智园

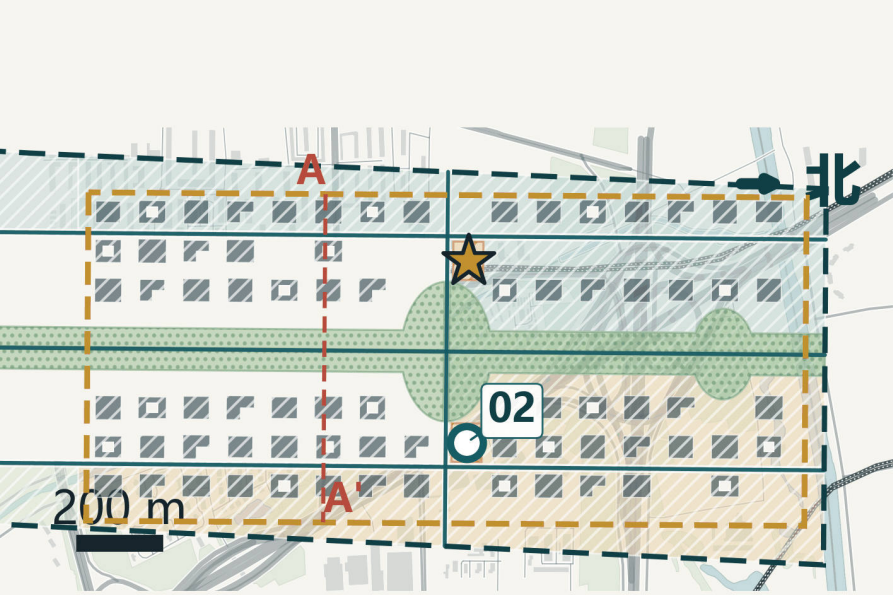


体量 75 · 中心线 4
公共空间 2 · 定位点 2

剖面 → P8/P9/P10

- 01 开放创新界面
- 02 安全评测庭
- 03 共享算力与人工复核

可表达：概念平面 / 体量 / 节点
待补：地块 / 现状 / 标高 / 消防 / 权属

02 悟境 · 原点社区

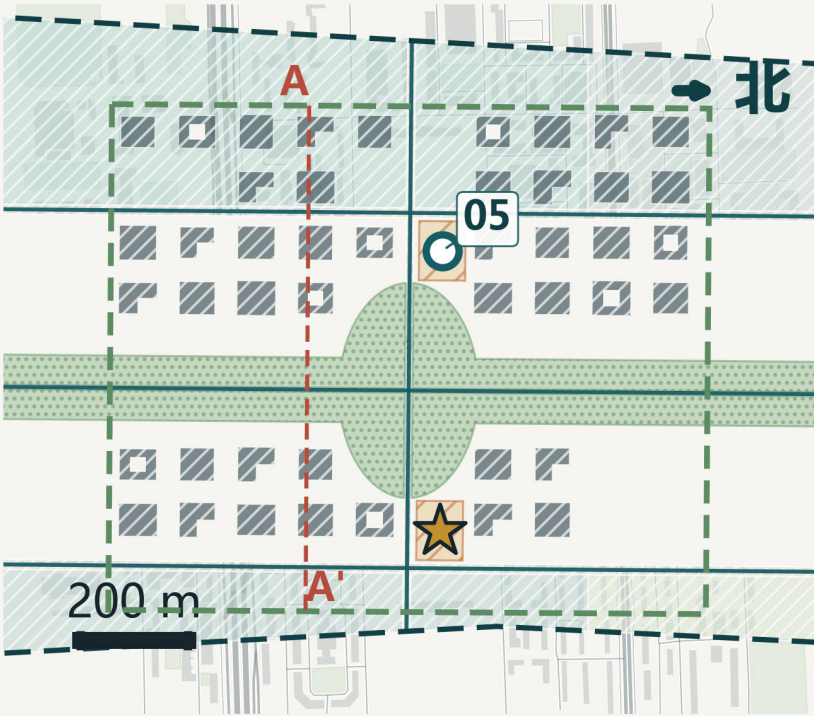


体量 45 · 中心线 4
公共空间 2 · 定位点 2

剖面 → P8/P9/P10

- 01 学习—生活混合
- 02 无屏与适老服务
- 03 社区共治节点

可表达：概念平面 / 体量 / 节点
待补：地块 / 现状 / 标高 / 消防 / 权属

03 行境 · 大钟寺

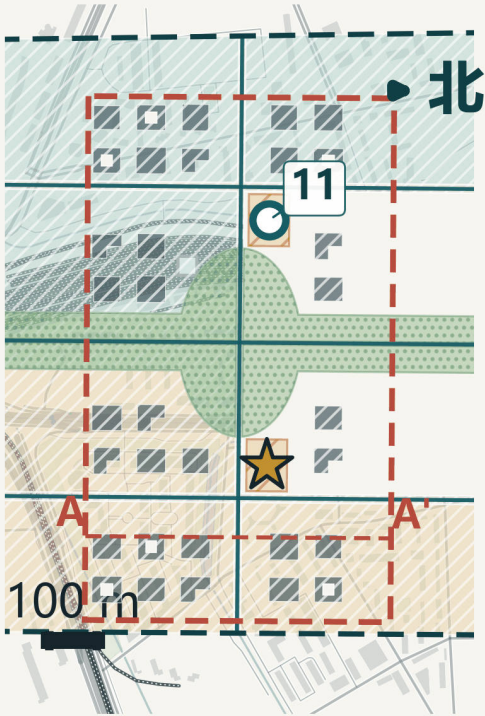

体量 33 · 中心线 4
公共空间 2 · 定位点 2

剖面 → P8/P9/P10

- 01 产业验证与展示
- 02 遗产共生界面
- 03 长期运营场所

可表达：概念平面 / 体量 / 节点
待补：地块 / 现状 / 标高 / 消防 / 权属

图示：斜线=方案用地/体量 | 深青=中心线 | 金色=公共空间/地标 | 灰色=OSM语境 | 红虚线=A—A'

方案：提交包 GeoJSON / metrics.json;
现状语境：© OpenStreetMap contributors, ODbL 1.0, 2026-08-21; 非官方红线与工程依据

FIG-03 / KEY AREAS

明责 · 明界 · 明退

证据升级与实施协议

明责

- 明确公共决策者、服务运营方、数据责任人和人工申诉负责人。
- 每次复核记录责任角色与签字状态。
- 记录字段：决定人 / 运营人 / 复核人 / 申诉人。

- 决定人
- 运营人
- 复核人
- 申诉人

明界

- 标明临时空间边界、服务对象、最小必要数据和有效期。
- 保留非AI基线与全程人工通道。
- 记录字段：地点 / 用户 / 数据 / 时限 / 基线。

- 地点
- 用户
- 数据
- 时限
- 基线

明退

- 预先公布停止阈值、回退方式、数据处置和场地恢复责任。
- 续期、缩减或停止均公开留痕。
- 记录字段：触发 / 处置 / 恢复 / 公示。


- 触发
- 回退
- 数据
- 恢复
- 公示



当前证据	升级触发资料	允许形成的下一结论
公告文字 + 临时范围	正式可用红线/GIS	精确范围、面积与控制对接
参与者设计模型	现状测绘/权属/法定控制	拆改留、容量和工程深化
场景协议草案	非AI基线 + 限时试点记录	续期、缩减或停止

01 问境 · 众智园

平面—切线剖面—指标—证据闸门；现状/工程资料缺口不以渲染补齐

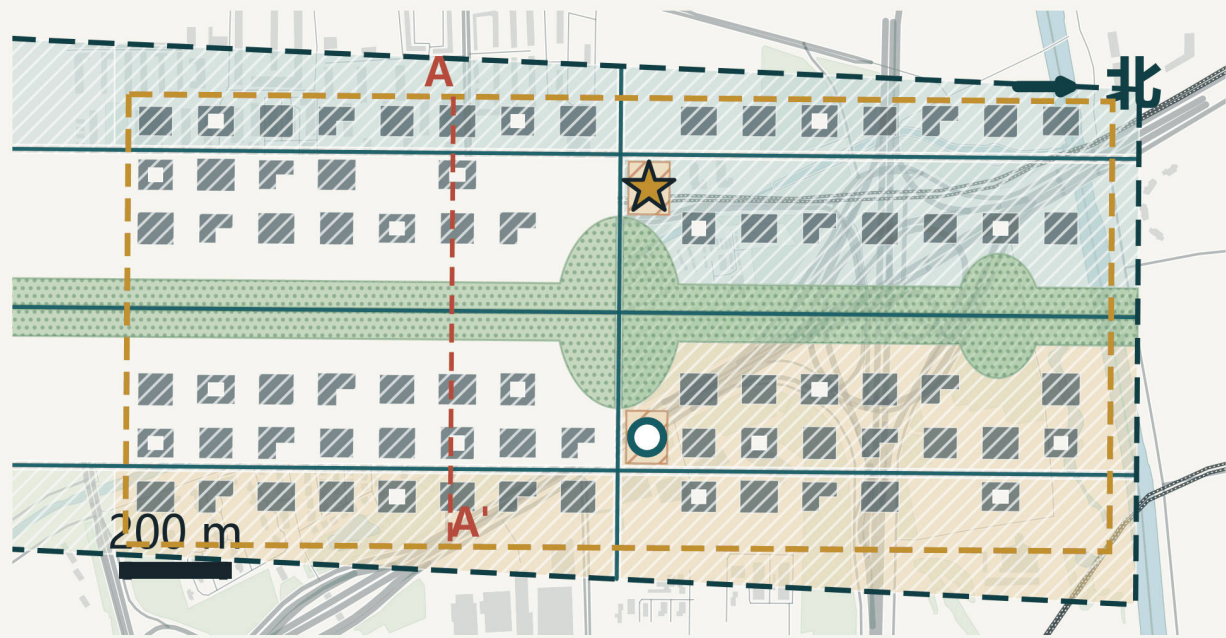

A—A' | 模型关联空间断面

[G] 水平交切/宽度 · [A] 层数×4.2m/净距* · [T] 道路/无障碍/排水 · 平基线≠实测标高

[G] 真切 B0030 3F/12.6m · B0031 4F/16.8m · B0032 4F/16.8m
[G] 真切 B0033 5F/21.0m · B0034 5F/21.0m · B0035 6F/25.2m

[T] 排水意向→绿地；坡度/标高待测



面积	概念体量
1.93 km²	75
模型容积率	模型密度
0.768	17.1%

现状证据/缺口

现状建筑/权属、能源与消防接口待核

试点边界

临时重点区内的可逆开放庭院与评测服务

责任角色

片区运营方 + 安全评测机构 + 数据责任人

触发资料

底图、产权、能源、消防和服务需求共同通过


退出状态

未过闸则退回地面公共空间与人工预约

[T] 18m街道=2.5步+1.5雨树+1.75骑+6.5车+镜像
8m绿道=2.5步+3骑+2.5荫
目标待规范/测绘复核
门槛失败→地面 / 非数字 / 可逆基线

02 悟境·原点社区

平面—切线剖面—指标—证据闸门；现状/工程资料缺口不以渲染补齐

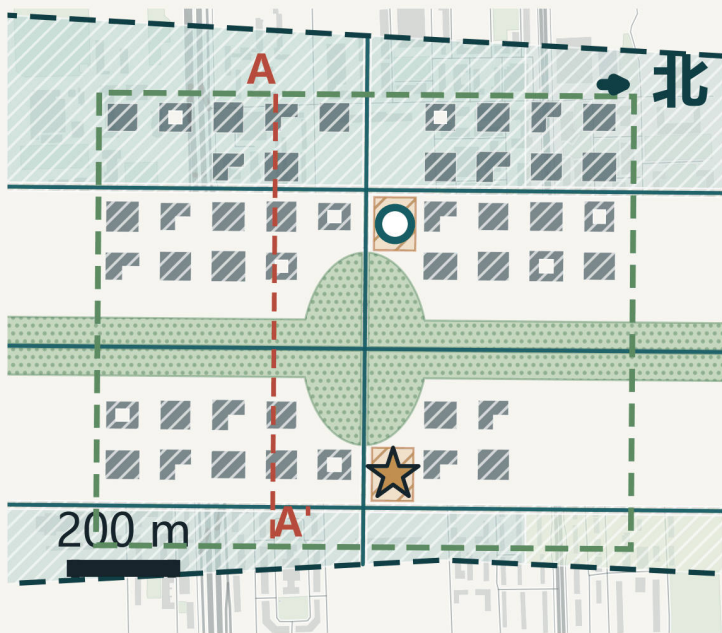


A—A' | 模型关联空间断面

[G] 水平交切/宽度 · [A] 层数×4.2m/净距* · [T] 道路/无障碍/排水 · 平基线≠实测标高

[G] 真切 B0092 7F/29.4m · B0093 4F/16.8m · B0094 5F/21.0m
[G] 真切 B0095 5F/21.0m · B0096 6F/25.2m · B0097 6F/25.2m

[T] 排水意向→绿地；坡度/标高待测

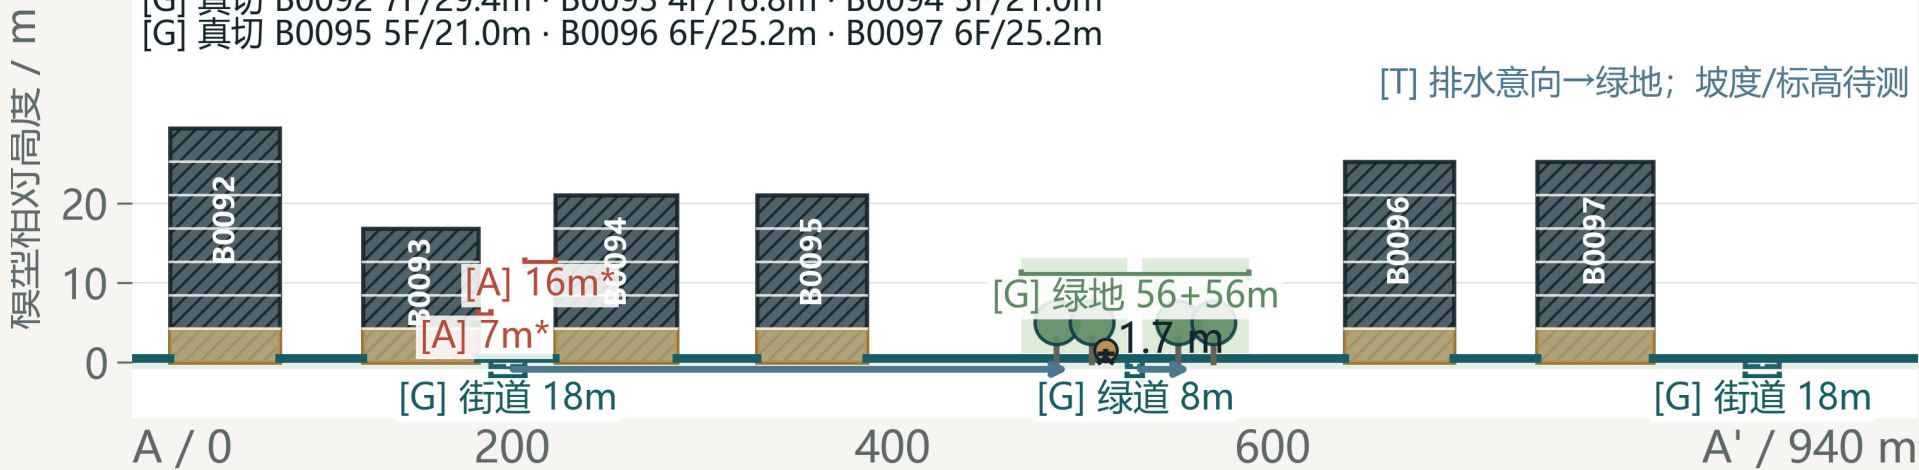

面积	概念体量
1.04 km ²	45
模型容积率	模型密度
0.875	15.9%

现状证据/缺口

人口画像、公共服务容量与无障碍现状待核

试点边界

限时社区服务试点；保留全程非数字通道

责任角色

街道/社区 + 公服机构 + 人工申诉负责人

触发资料

服务容量、可达性、同意与最小数据规则通过


退出状态

复核不达标则缩减功能或停止并公开复盘

[T] 18m街道=2.5步+1.5雨树+1.75骑+6.5车+镜像
8m绿道=2.5步+3骑+2.5荫
目标待规范/测绘复核
门槛失败→地面 / 非数字 / 可逆基线

03 行境 · 大钟寺

平面—切线剖面—指标—证据闸门；现状/工程资料缺口不以渲染补齐

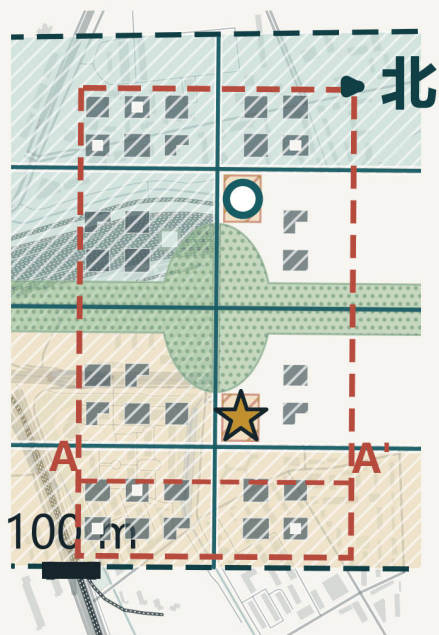


A—A' | 模型关联空间断面

[G] 水平交切/宽度 · [A] 层数×4.2m/净距* · [T] 道路/无障碍/排水 · 平基线≠实测标高

[G] 真切 B0127 6F/25.2m · B0135 7F/29.4m · B0140 6F/25.2m
[G] 真切 B0144 5F/21.0m · B0152 6F/25.2m

[T] 排水未解析：待地形/水文实测

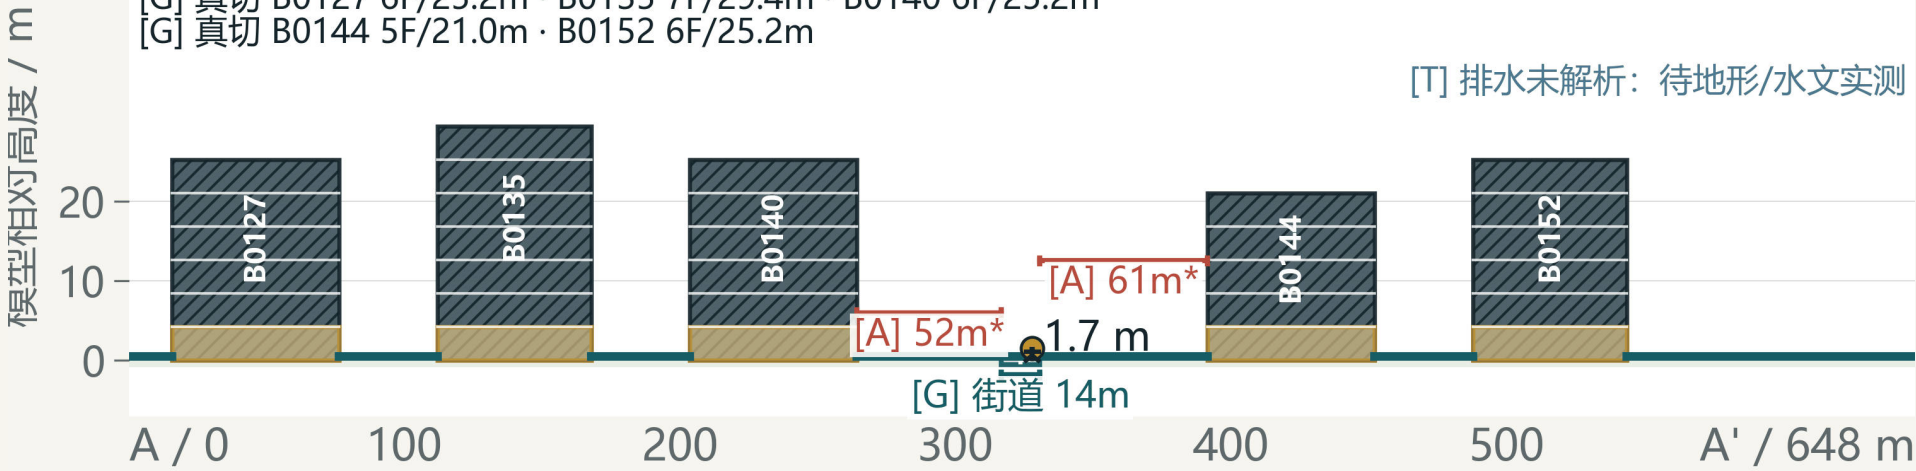

面积	概念体量
0.72 km²	33
模型容积率	模型密度
0.880	13.2%

现状证据/缺口

轨道、文保、产权、交通与长期运维资料待核

试点边界

不触碰遗产/轨道控制的可撤场验证活动

责任角色

属地政府 + 专业主管部门 + 场地运营方

触发资料

轨道文保、疏散、结构、交通和成本门槛通过

退出状态

任一刚性门槛失败即撤场并恢复原公共通行

[T] 14m支路=2.5步+1.5雨树+6共享车行+1.5雨树+2.5步
目标待规范/测绘复核
门槛失败→地面 / 非数字 / 可逆基线

十二个 AI+ 场景协议

12节点可读索引 + 3项代表验证卡；完整字段留在双语正文与HTML


01 明察·公共感知登记 公共设施入口 90日 / 非批准 非AI 纸质台账 + 现场服务台	02 澄心·无屏慢行 连续地面游径 180日 / 非批准 非AI 固定地图 + 触觉标识 + 值守人员	03 问学·触摸模型厅 社区文化设施 一学期 / 非批准 非AI 实物模型 + 人工讲解 + 盲文纸本
04 习静·深阅读室 安静室内公共空间 90日 / 非批准 非AI 纸本目录 + 馆员检索 + 线下预约	05 诚问·算法问诊台 服务窗口附近 30日 / 非批准 非AI 全程人工窗口 + 纸质凭证	06 正验·边缘实验市集 可撤摊试验场 一季市集 / 非批准 非AI 线下服务窗 + 纸质流程 + 实体反馈卡
07 修安·安全演练庭院 隔离测试空间 90日 / 非批准 非AI 人工评测 + 实体隔离 + 立即停止键	08 齐家·适老慢行环 社区地面路径 180日 / 非批准 非AI 志愿者陪行 + 实体导视 + 值守点	09 治业·开放算力日 受控共享设施 180日 / 非批准 非AI 人工审批 + 线下排期 + 人工技术支持
10 践行·静音商业街 站前首层 180日 / 非批准 非AI 现金/实体凭证 + 全程人工服务	11 厚土·首层五件套 沿街首层和站前空间 一年 / 非批准 非AI 明确管理人 + 实体指引 + 替代设施	12 明德·答钟公共事件 文化节点 一年一续 / 非批准 非AI 无声视觉版本 + 现场主持 + 公开听证

06 正验·边缘实验市集 位置/服务可撤摊试验场 测试说明→审查→限时演示→反馈→复盘 非AI基线线下服务窗 + 纸质流程 + 实体反馈卡 证据同意、投诉与撤场记录 / 每月复核 退出数据越界、投诉无法处置或演示超界即停止该摊位/场次 KPI自愿使用情况、撤场执行、反馈闭环	07 修安·安全演练庭院 位置/服务隔离测试空间 公示边界→演练→记问题→人工复核→摘要 非AI基线人工评测 + 实体隔离 + 立即停止键 证据问题台账与停机记录 / 每场结束复核 退出高危未闭环、测试外溢或隔离失效即停机 KPI问题分级、闭环与复发记录	09 治业·开放算力日 位置/服务受控共享设施 申请→用途/资源审核→限时使用→记录→复盘 非AI基线人工审批 + 线下排期 + 人工技术支持 证据预约、兑现、能耗与终止日志 / 每月复核 退出资源未兑现、能耗/安全越界或责任缺位即缩减/停止 KPI资源兑现情况、能耗披露、违规终止记录
---	---	---

指标复算与证据链

THE LUCID SHANSHUI

每个已知数值均回到 GeoJSON；法定控制缺失项继续保持 unknown

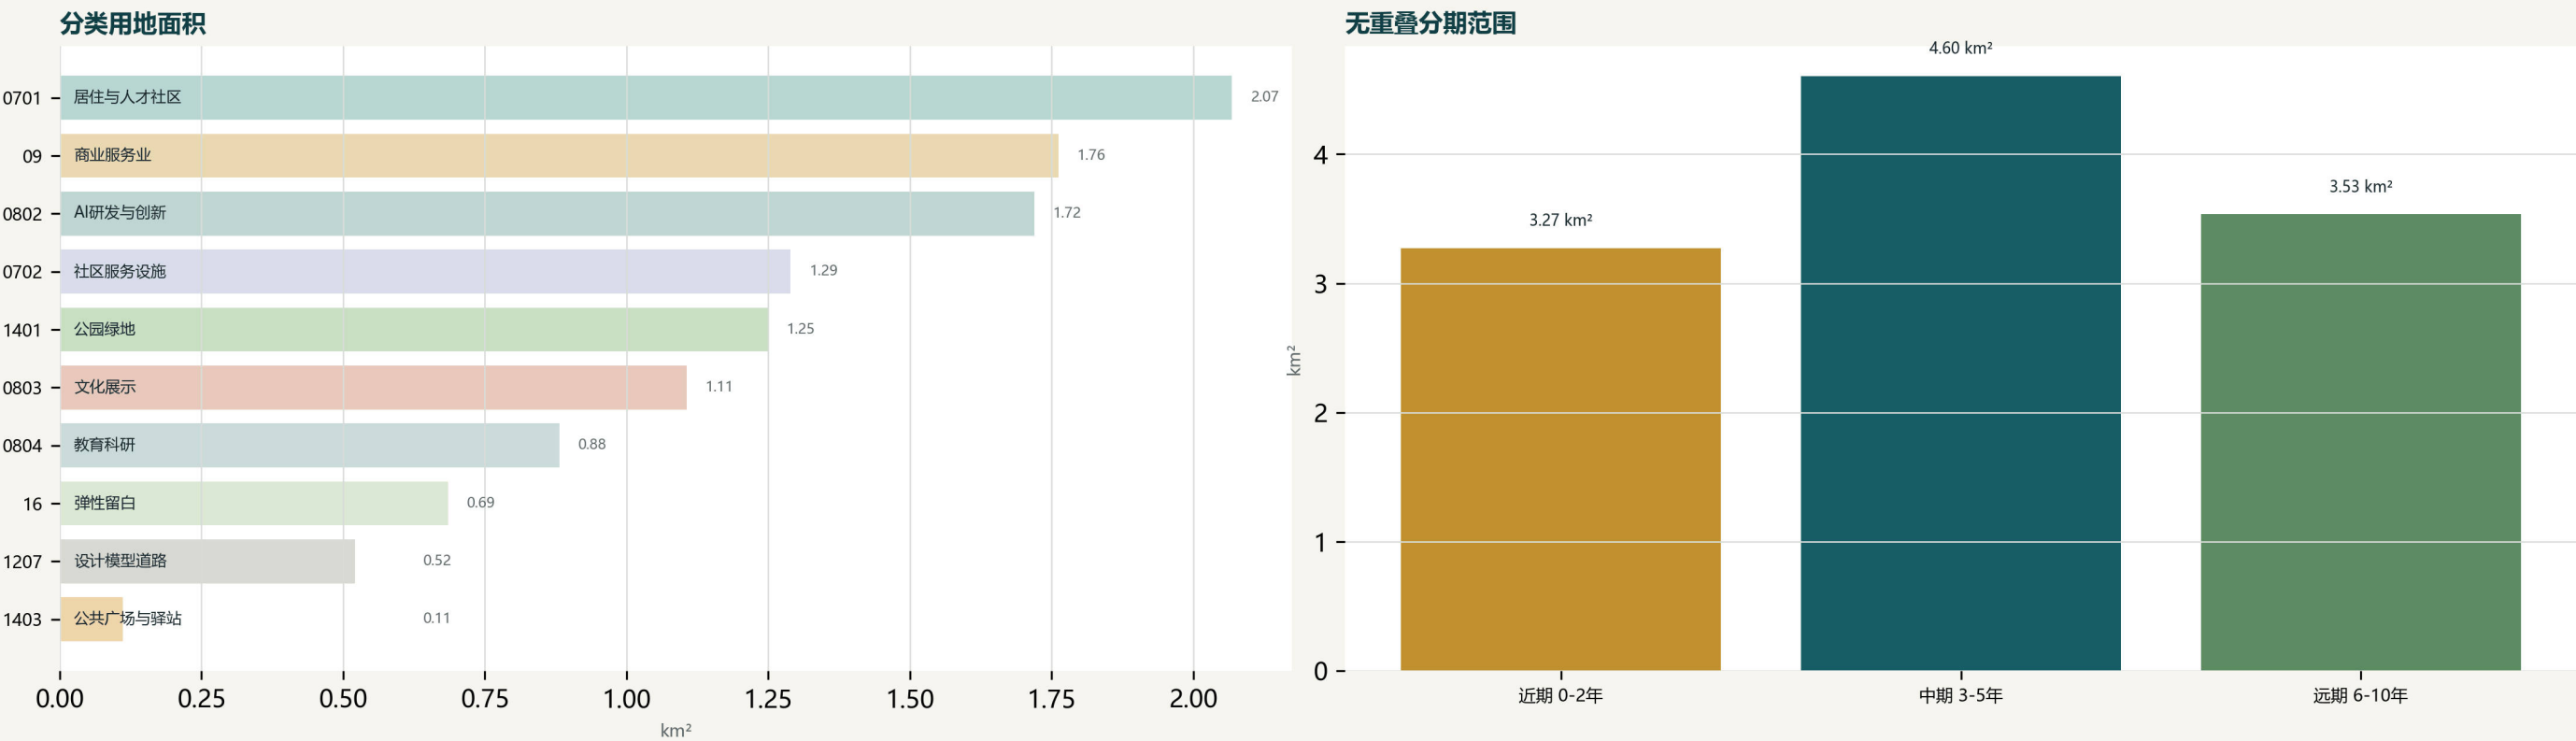

未知项：法定容积率、建筑限高、建筑密度；正式红线、地块、现状建筑/标高/管线到位后整体复算。