


总体设计结构板：一脉三栖两翼五节点

图 01

总体概念与空间结构：一脉三栖两翼五节点

以京张遗址公园为主脉，把 11.4 平方公里组织成人与智能体共同栖息的城市带

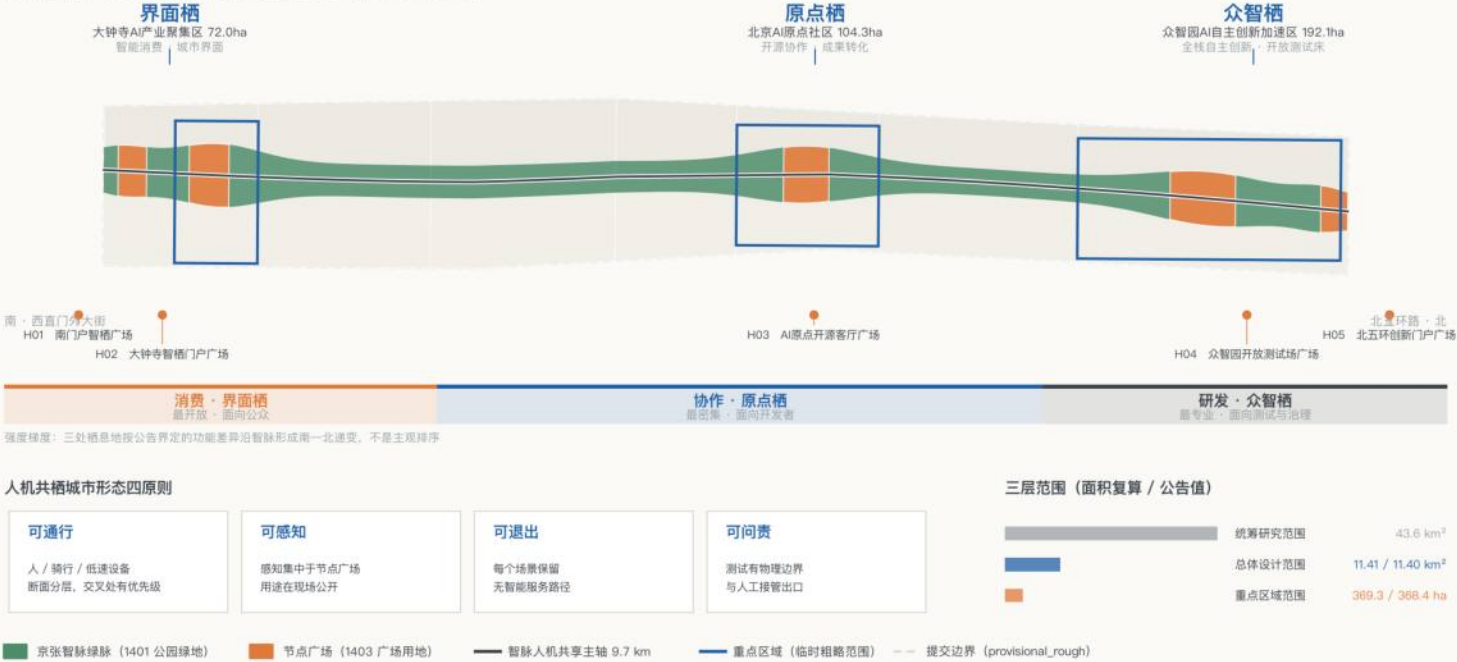

数据来源：本方案 geometry/* .geojson 与 metrics.json，均由组织方提供的 provisional_rough 临时边界派生。临时边界（虚线）不是官方红线，不得作为审批或精确面积依据；官方 polygon 发布后全部图层与比例须整体复算。

总体概念

以京张遗址公园为主脉，把 11.4 平方公里组织成一条人与智能体共同栖息、共同被治理、共同被展示的城市带。

命名体系

主名称 京张智栖带 / Agent Habitat Belt；二级 智脉·栖·翼；三级 H01—H05 节点；四级 SC—XX 场景卡与“栖”字头活动。

视觉方向

“折返的人”：以青龙桥“人”字形展线折返轨迹为图形母题，叠合栖息地等高线；铁轨灰 / 原点蓝 / 栖息绿 / 警示橙四色系统。

强度梯度


南端最开放（消费·界面栖）、中段最协作（协作·原点栖）、北端最专业（研发·众智栖）。梯度来自公告对三处重点区功能的界定。

用地与城市更新板：三层范围传导与七段两翼

图 02

三层范围传导与七段两翼用地结构

统筹研究定策略 → 总体设计定结构 → 重点区域定动作：30 个用地图斑无缝覆盖提交边界

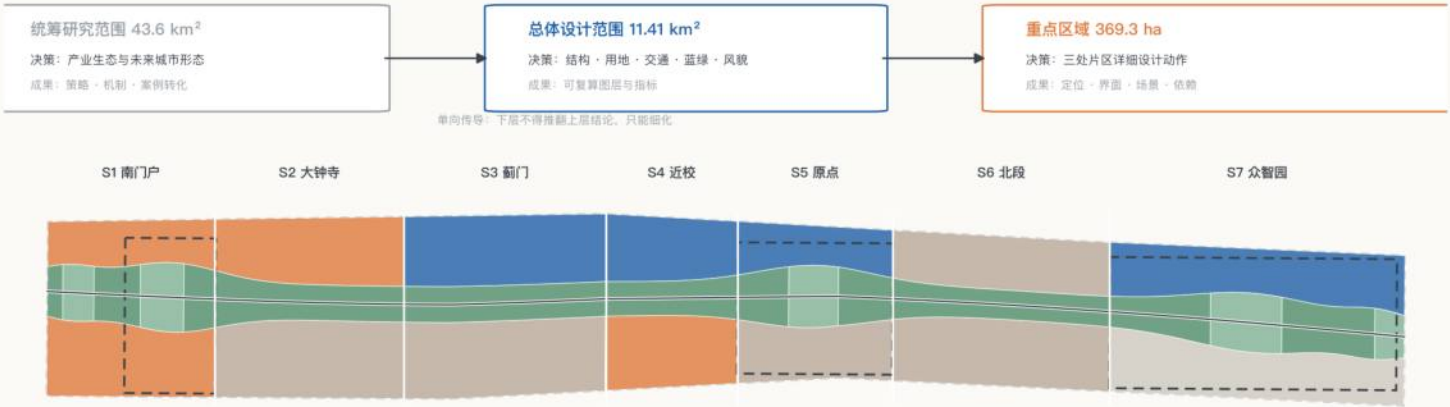

七段功能带：西翼（中关村科技服务翼）/ 东翼（小月河场景赋能翼）与判断依据



数据来源：本方案 geometry/*_geojson 与 metrics.json，均由组织方提供的 provisional_rough 临时边界衍生，临时边界（虚线）不是官方红线，不得作为审批或精确面积依据；官方 polygon 发布后全部图层与比例请整体复算。用地代码取自站点包官方分类子集；两两图斑交集面积为 0，与边界空隙 94.5 m²（容差 1 141 m²）。

级别	更新动作	触发条件
1	留白	功能不确定、技术未成熟
2	界面改造	首层封闭、步行不连续
3	功能置换	结构完好但业态低效
4	结构加固	结构安全不足但有保留价值
5	拆除新建	前四级均不可行

30 个用地图斑无缝覆盖提交边界，两两交集面积为 0，空隙 94.5 m²（容差 1 141 m²）。建议建筑基底 106.6 公顷，占提交边界 9.34%——这不是建筑密度，它只包含方案主动建议动作的基底，不含全部现状建筑。容积率、建筑高度、建筑密度与退线因公开资料包中登记为 missing 而保持 unknown，本方案不以推测值填补。


图 04

交通慢行、低速无人设备路径与蓝绿公共空间复合系统

南北靠连续绿脉贯通，东西靠 8 条缝合通道渗透：人 / 骑行 / 低速设备在断面上分离

京张智梧带 AGENT HABITAT BELT

Clay+HKK · 概念建议 · 非法定规划

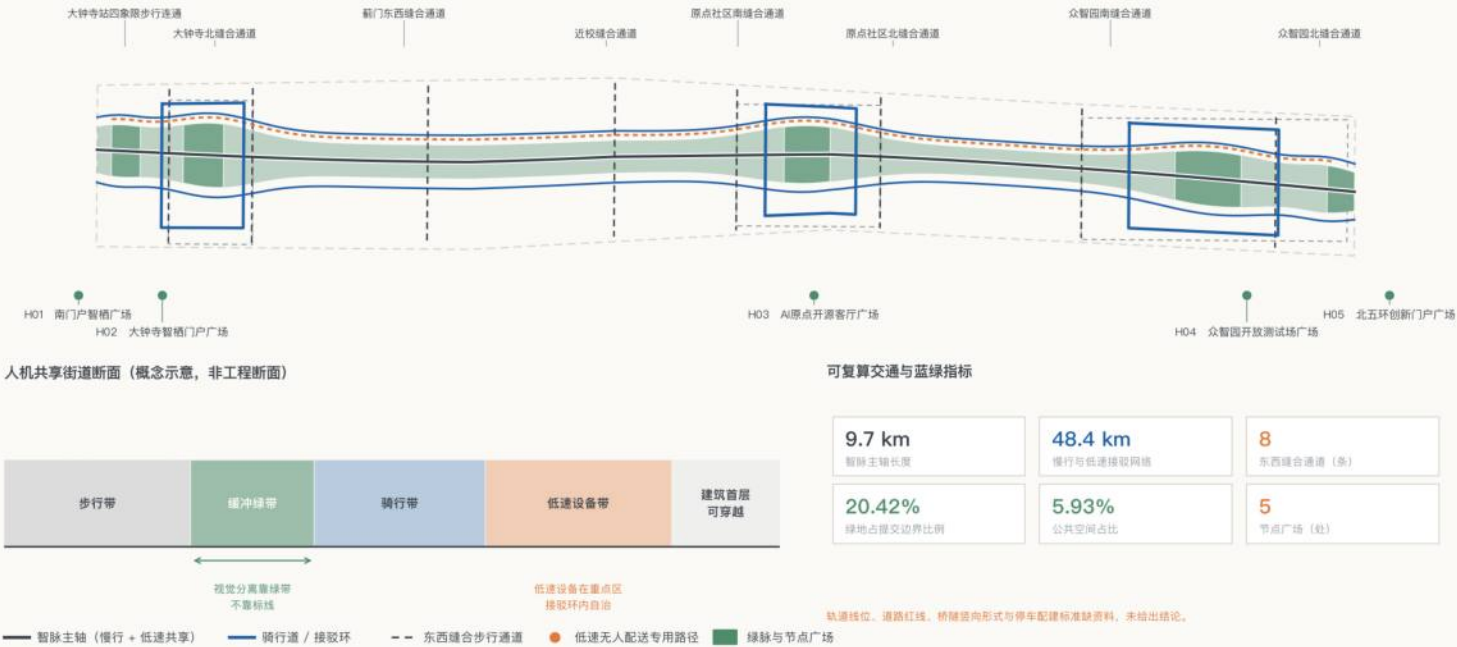

数据来源：本方案 geometry/*geojson 与 metrics.json，均由组织方提供的 provisional_rough 临时边界派生。临时边界（虚线）不是官方红线，不得作为审批或精确面积依据；官方 polygon 发布后全部图层与比例须整体复算。

南北贯通

智脉主轴 9.7 km 连续；慢行与低速接驳网络合计 48.4 km。

东西缝合

8 条缝合通道 + 5 处节点广场；广场设在人已经要横穿的地方，停留才会真实发生。

断面分层

步行带 — 缓冲绿带 — 骑行带 — 低速设备带；靠绿带而非标线实现视觉分离；低速设备在重点区接驳环内自治。

待补条件

轨道线位与站点位置、道路红线与退线、桥隧竖向形式、停车配建标准、市政管线与容量，均缺官方资料，未给结论。

京张遗址公园活力带与蓝绿公共空间板

图 01

总体概念与空间结构：一脉三栖两翼五节点


以京张遗址公园为主体，带 11.4 平方公里组织成人与智能体共同栖居的城市带



图 04

交通慢行、低速无人设备路径与蓝绿公共空间复合系统

南北原绿绿脉贯通，东西原 8 条慢行道路渗透：人 / 慢行 / 低速设备在断面上分离

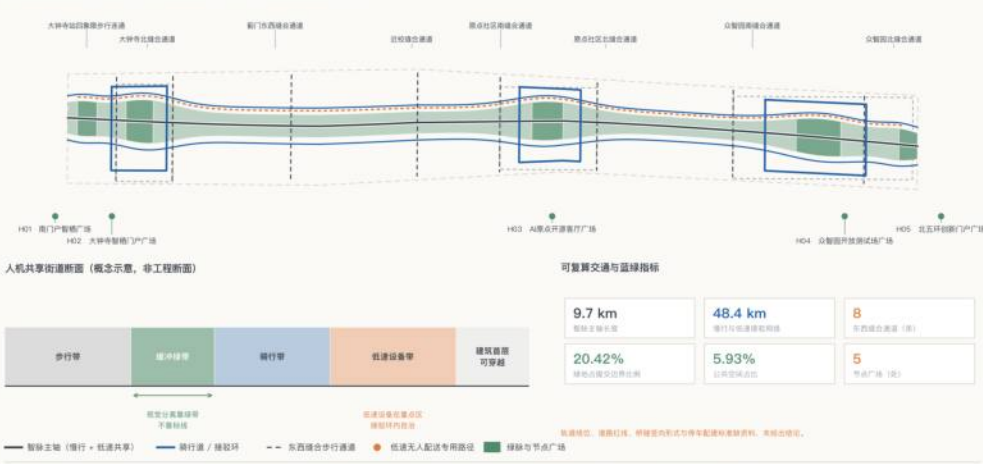

主题绿脉段（自南向北）

使用者结构

南段京张记忆林

消费人流

大钟寺遗产廊段

消费人流 + 访客

蓟门慢行绿脉段

通勤与居民

近校共享草坪段

学生与研究者

原点社区开源花园段

研究者与开发者

北段人机共享林荫段

居民与运维者

众智园测试绿场段

专业测试人员

绿地 233.1 公顷（20.42%），公共空间 67.7 公顷（5.93%），均与用地图层中 1401 / 1403 图斑同源，可直接复算。

公共空间组件库（八类可复制构件，概念建议）：共享感知杆、人机共享路缘、低速设备取件柜、可拆卸测试围界、开源贡献铭牌、无智能服务台、遗产枕木座椅、夜间协作照明单元。组件库的意义在于让这条 9.7 公里的带子在十年内可以逐段建成而不失去整体性。

四处 AI 朝圣地：折返碑（南门户）· 开源贡献墙（原点栖）· 智能体纪念阵列（众智栖）· 人机共栖界碑（北门户）。均为概念建议，选址与建设须由专业团队与主管部门确定。

缺少文物保护范围、建设控制地带、绿线与蓝线的官方矢量数据：本方案提出的“京张遗产绿脉概念控制带”标记为 analysis_helper，不是紫色、绿线或蓝线，不得被解释为任何法定控制线。


三处重点区域详细设计板

图 03

三处栖息地：定位差异、空间抓手与实施依赖

京张智栖带 AGENT HABITAT BELT
Clay-HK · 概念建议 · 非法定规划

界面栖（南）· 原点栖（中）· 众智栖（北）——同一条智脉上的三种开放度

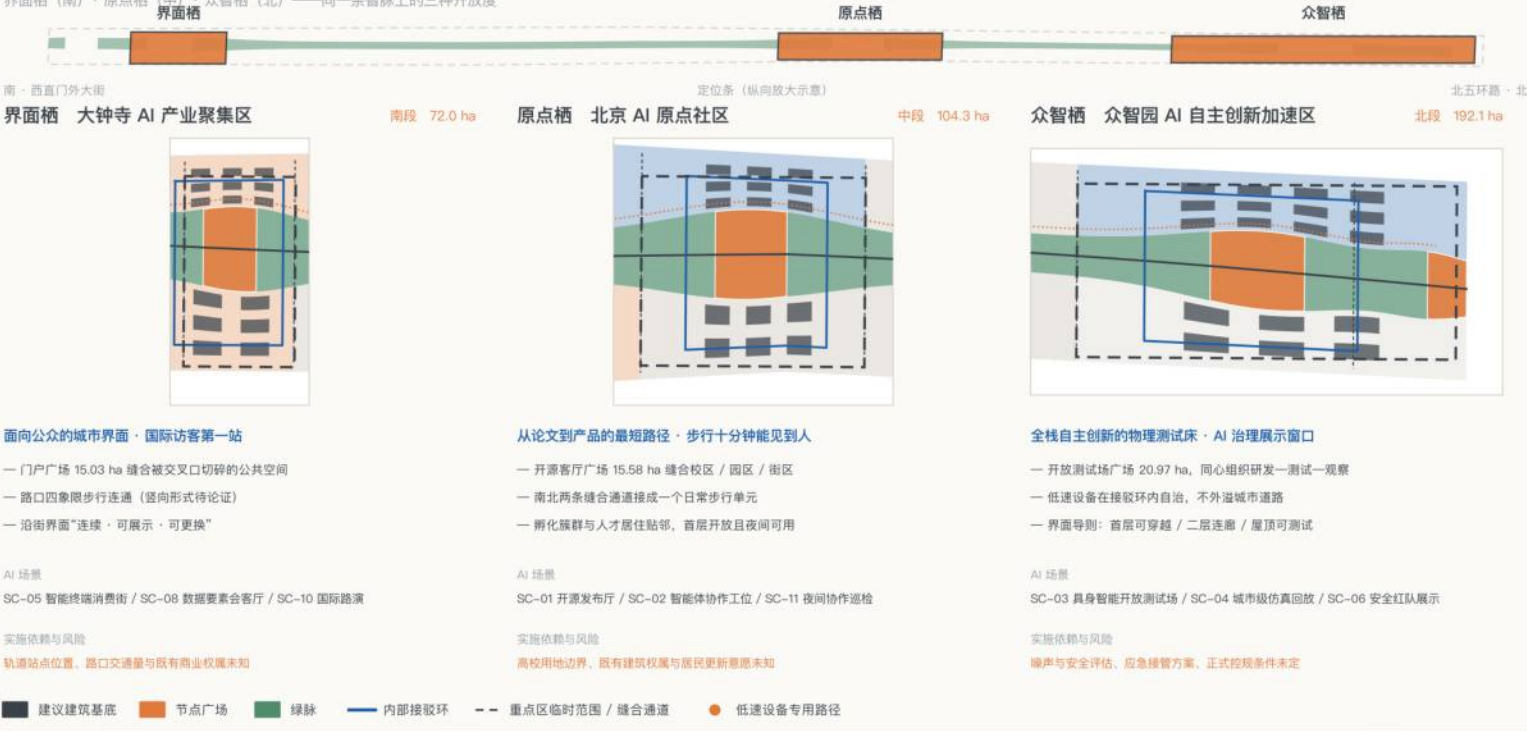

数据来源：本方案 geometry/*_geojson 与 metrics.json，均由组织方提供的 provisional_rough 临时边界派生。临时边界（虚线）不是官方红线，不得作为审批或核算面积依据；官方 polygon 发布后全部图层与比例须整体复算。三处重点区面积为临时几何复算值。官方 polygon 发布后须重算；地块级拆改留结论未给出。

三处重点区共 369.3 公顷（临时几何复算），彼此不重叠且完整落在提交边界内。每处按“定位—空间动作—建筑与界面—交通组织—AI 场景—实施依赖”六项组织。官方 polygon 发布后，重点区面积、内部建筑族群落位、接驳环线形与广场规模均需重算；地块级拆改留结论未给出。

画像	缺的空间
P1 开源开发者	可用到深夜的半公共协作空间
P2 初创团队	可合法出错的物理测试空间
P3 高校师生	校区与园区之间的连续步行
P4 周边居民	不被更新挤走的日常服务
P5 企业访客与国际来宾	可快速理解技术的展示界面
P6 具身智能运维者	设备专用路径与接管点

一级 公众自由进入；二级 需预约登记；三级 需资质、物理围界与现场接管岗。

春 开源栖会 · 夏 共栖开放日 · 秋 智栖节 · 冬
治理工作坊。

运营机制的设计原则是先有可重复的机制，再有活动品牌。场景开放配套“申请—安全评估—试运行—复核—转正或退出”五步流程，其中退出机制是敢于开放测试的前提：任何场景在复核不通过时必须能干净地撤出，空间恢复原状。招引转化四步漏斗：公众体验 → 开发者参与 → 团队落地 → 企业扎根。

以“人”字形展线折返几何为形，碑面刻录京张沿线自主技术的时间线，向公众开放。

逐年记录被采纳的开源贡献与贡献者署名，模块化构造，避免一次建成后无法更新。

记录在真实城市任务中被采用的智能体方案与贡献者标识，是本次开源征集精神的物理延续。

标记全带北端门户，说明这条带子上人与机器的通行规则。本身即一块公开的规则展示牌。

指标复核与合规响应板

图 05

指标复算路径与证据链：从 GeoJSON 到正文结论

21 项 known 指标可由提交几何在 EPSG:4548 下复算；6 项缺官方控制条件的指标保持 unknown

京张智禧带 AGENT HABITAT BELT
Clay-HK · 概念建议 · 非法定规划



第一类：可复算空间指标（占提交边界比例）



数据上圆 30%：绿地与公共空间数据与用地图图 1403 / 1403 图面同圆，可直接复算。

第二类：待确认法定管控指标

容积率 floor_area_ratio	unknown
建筑高度 building_height_m	unknown
建筑密度 official_building_density	unknown
总建筑面积 total_floor_area_sqm	unknown
现状建筑基底 existing_building_footprint	unknown
道路红线退线 road_redline_setback_m	unknown

planning_limits.json 中 status 均为 missing：
以特需指标社会制度色块确定。

自检状态

● BOUNDARY_TRUST	PASS
● KEY_AREAS_TRUST	PASS
● LAND_USE_TOPOLOGY	PASS
● METRIC_RECALC	PASS
● VISUAL_STATIC	PASS
● PROFESSIONAL_EVIDENCE	PASS
● CLAIM_BOUNDARY	PASS
● COPYRIGHT_CLEARANCE	PASS

deterministic / spatial / visual /
professional 四项复核证据。

数据来源：本方案 geometry/*_geojson 与 metrics.json，由团队方提供的 provisional_rough 临时边界清单。临时边界（虚线）不是官方红线，不得作为审批或规划依据。官方 polygon 发布后全部数据与比例调整复算。第三类绩效指标（场景使用状况、活动参与度、转化量）需长期跟踪，本方案不跟踪数据。

任务	标题	方案响应
1.3.1	构建世界级AI创新生态体系	以“三栖两翼一脉”的栖息地生态模型组织基础研究、开源协作、中试验证、企业转化与资本服务，并把每一环节落到具体用地图斑与节点广场。
1.3.2	建设适配AI新质生产力的新型城市形态	提出人机共享街道断面、低速无人设备专用路径与可开放测试的街区界面，形成适配具身智能的城市形态原型。
1.3.3	打造全球AI创新人才向往的高品质城区	以六类用户画像反推居住、协作、健康、文化与夜间生活的空间供给，用连续绿脉与五处节点广场承载日常体验。
1.4.1	统筹研究范围	43.6 平方公里统筹研究范围以 constraints 图层中的临时参照几何表达，只用于产业与协同判断，不作为设计红线。
1.4.2	总体设计范围	11.4 平方公里总体设计范围采用临时边界复算得 11 412 825 平方米，与公告值偏差 0.11%，偏差来源与复算责任已在正文说明。
1.4.3	重点区域范围	三处重点区共 369.3 公顷（临时几何复算），彼此不重叠且完整落在提交边界内。
1.5.1.1	统筹研究范围：AI创新生态体系	从 6 个全球案例提炼可转化机制，映射到众智园全栈自主体系、原点社区开源生态与中关村科技服务翼的要素保障。
1.5.1.2	统筹研究范围：适配人工智能的未来城市形态	提出“人机共栖城市形态四原则”：可通行、可感知、可退出、可问责，并给出对应的街道、界面与留白空间安排。
1.5.2.1	总体设计范围：产业目标与功能布局	七段式功能带把科研、教育、居住、社区服务、文化、健康与留白用地沿智脉两翼组织，形成南消费—中协作—北研发的梯度。
1.5.2.2	总体设计范围：城市更新总体框架	更新框架按“留白优先、界面先行、拆除最后”分级；缺少现状普查数据时只给出分类方法，不给地级拆改留结论。
1.5.2.3	总体设计范围：交通轨道市政配套设施	8 条东西缝合通道、3 处重点区接驳环与 1 条低速无人配送路径构成交通概念框架；红线、线位与管线条件列为待补。
1.5.2.4	总体设计范围：京张遗址公园活力带	9.7 公里京张智脉贯通南北，绿地占比 20.42%，以七段主题绿脉与五处节点广场承载遗产叙事与人机共享活动。
1.5.2.5	总体设计范围：城市风貌	风貌以“铁轨灰—原点蓝—栖息绿”三色系统与低层高密度界面为导向；建筑高度在官方控制条件补齐前保持 unknown。
1.5.3.required	重点区域详细设计必选项	三处重点区分别给出定位、空间动作、建筑与界面策略、交通组织、AI 场景与实施依赖，并逐项标注资料缺口。
1.5.3.1	众智园AI自主创新加速区	北段“自主创新栖”：以众智园开放测试场广场为核心，组织全栈自主研发族群、开放测试实验族群与标准治理展示。
1.5.3.2	北京AI原点社区	中段“开源共栖”：以 AI 原点开源客厅广场缝合校区、园区与街区，组织孵化、发布、人才居住与开源协作。
1.5.3.3	大钟寺AI产业聚集区	南段“智能消费栖”：以大钟寺智禧门户广场与四象限步行连通组织智能终端消费、内容体验与国际路演。
agent.1	一带总体概念与功能统筹方案设计	提出主名称“京张智禧带 / Agent Habitat Belt”、命名体系、Logo 方向与“一脉三栖两翼”总体空间结构及三区两翼协同回路。
agent.2	AI全栈自主创新体系与世界级AI创新生态设计	6 个全球生态案例 + 生态图谱 + 土地/空间/资金/人才/算力/数据/场景七要素保障机制，逐条对应空间载体。
agent.3	AI+场景赋能新范式与智能化AI活力城市设计	13 张 AI 场景卡（含 4 个产业测试验证场景）、6 类用户画像与场景—空间—运营映射表，每张卡附隐私边界与人工复核出口。
agent.4	AI公共空间、智能原生新业态与朝圣地标设计	东西缝合与南北贯通策略 + 4 处 AI 朝圣地标 + 贡献荣誉展示体系 + 公共空间组件库（8 类可复制构件）。
agent.5	百年京张文化、中关村文化与AI新文化融合叙事设计	“自主”一条主线贯通詹天佑自主创新路、中关村自主创新与今日全栈自主 AI，配套导航符号系统与国际传播叙事。
agent.6	一带全球AI创新活动体系与长期运营设计	年度活动日历、开发者社区运营机制、场景开放三级准入、公共体验路线与招引转化四步漏斗，均写为运营机制建议。