


场地总览与证据链

三层范围 / 一带三核 / 分期 / 设计图层

01 OPEN YARD / 百年京张AI公共创新带

场地总览与证据链

一带三核、多点场景、蓝绿慢行复合环 | 三层范围在同一证据链中组织

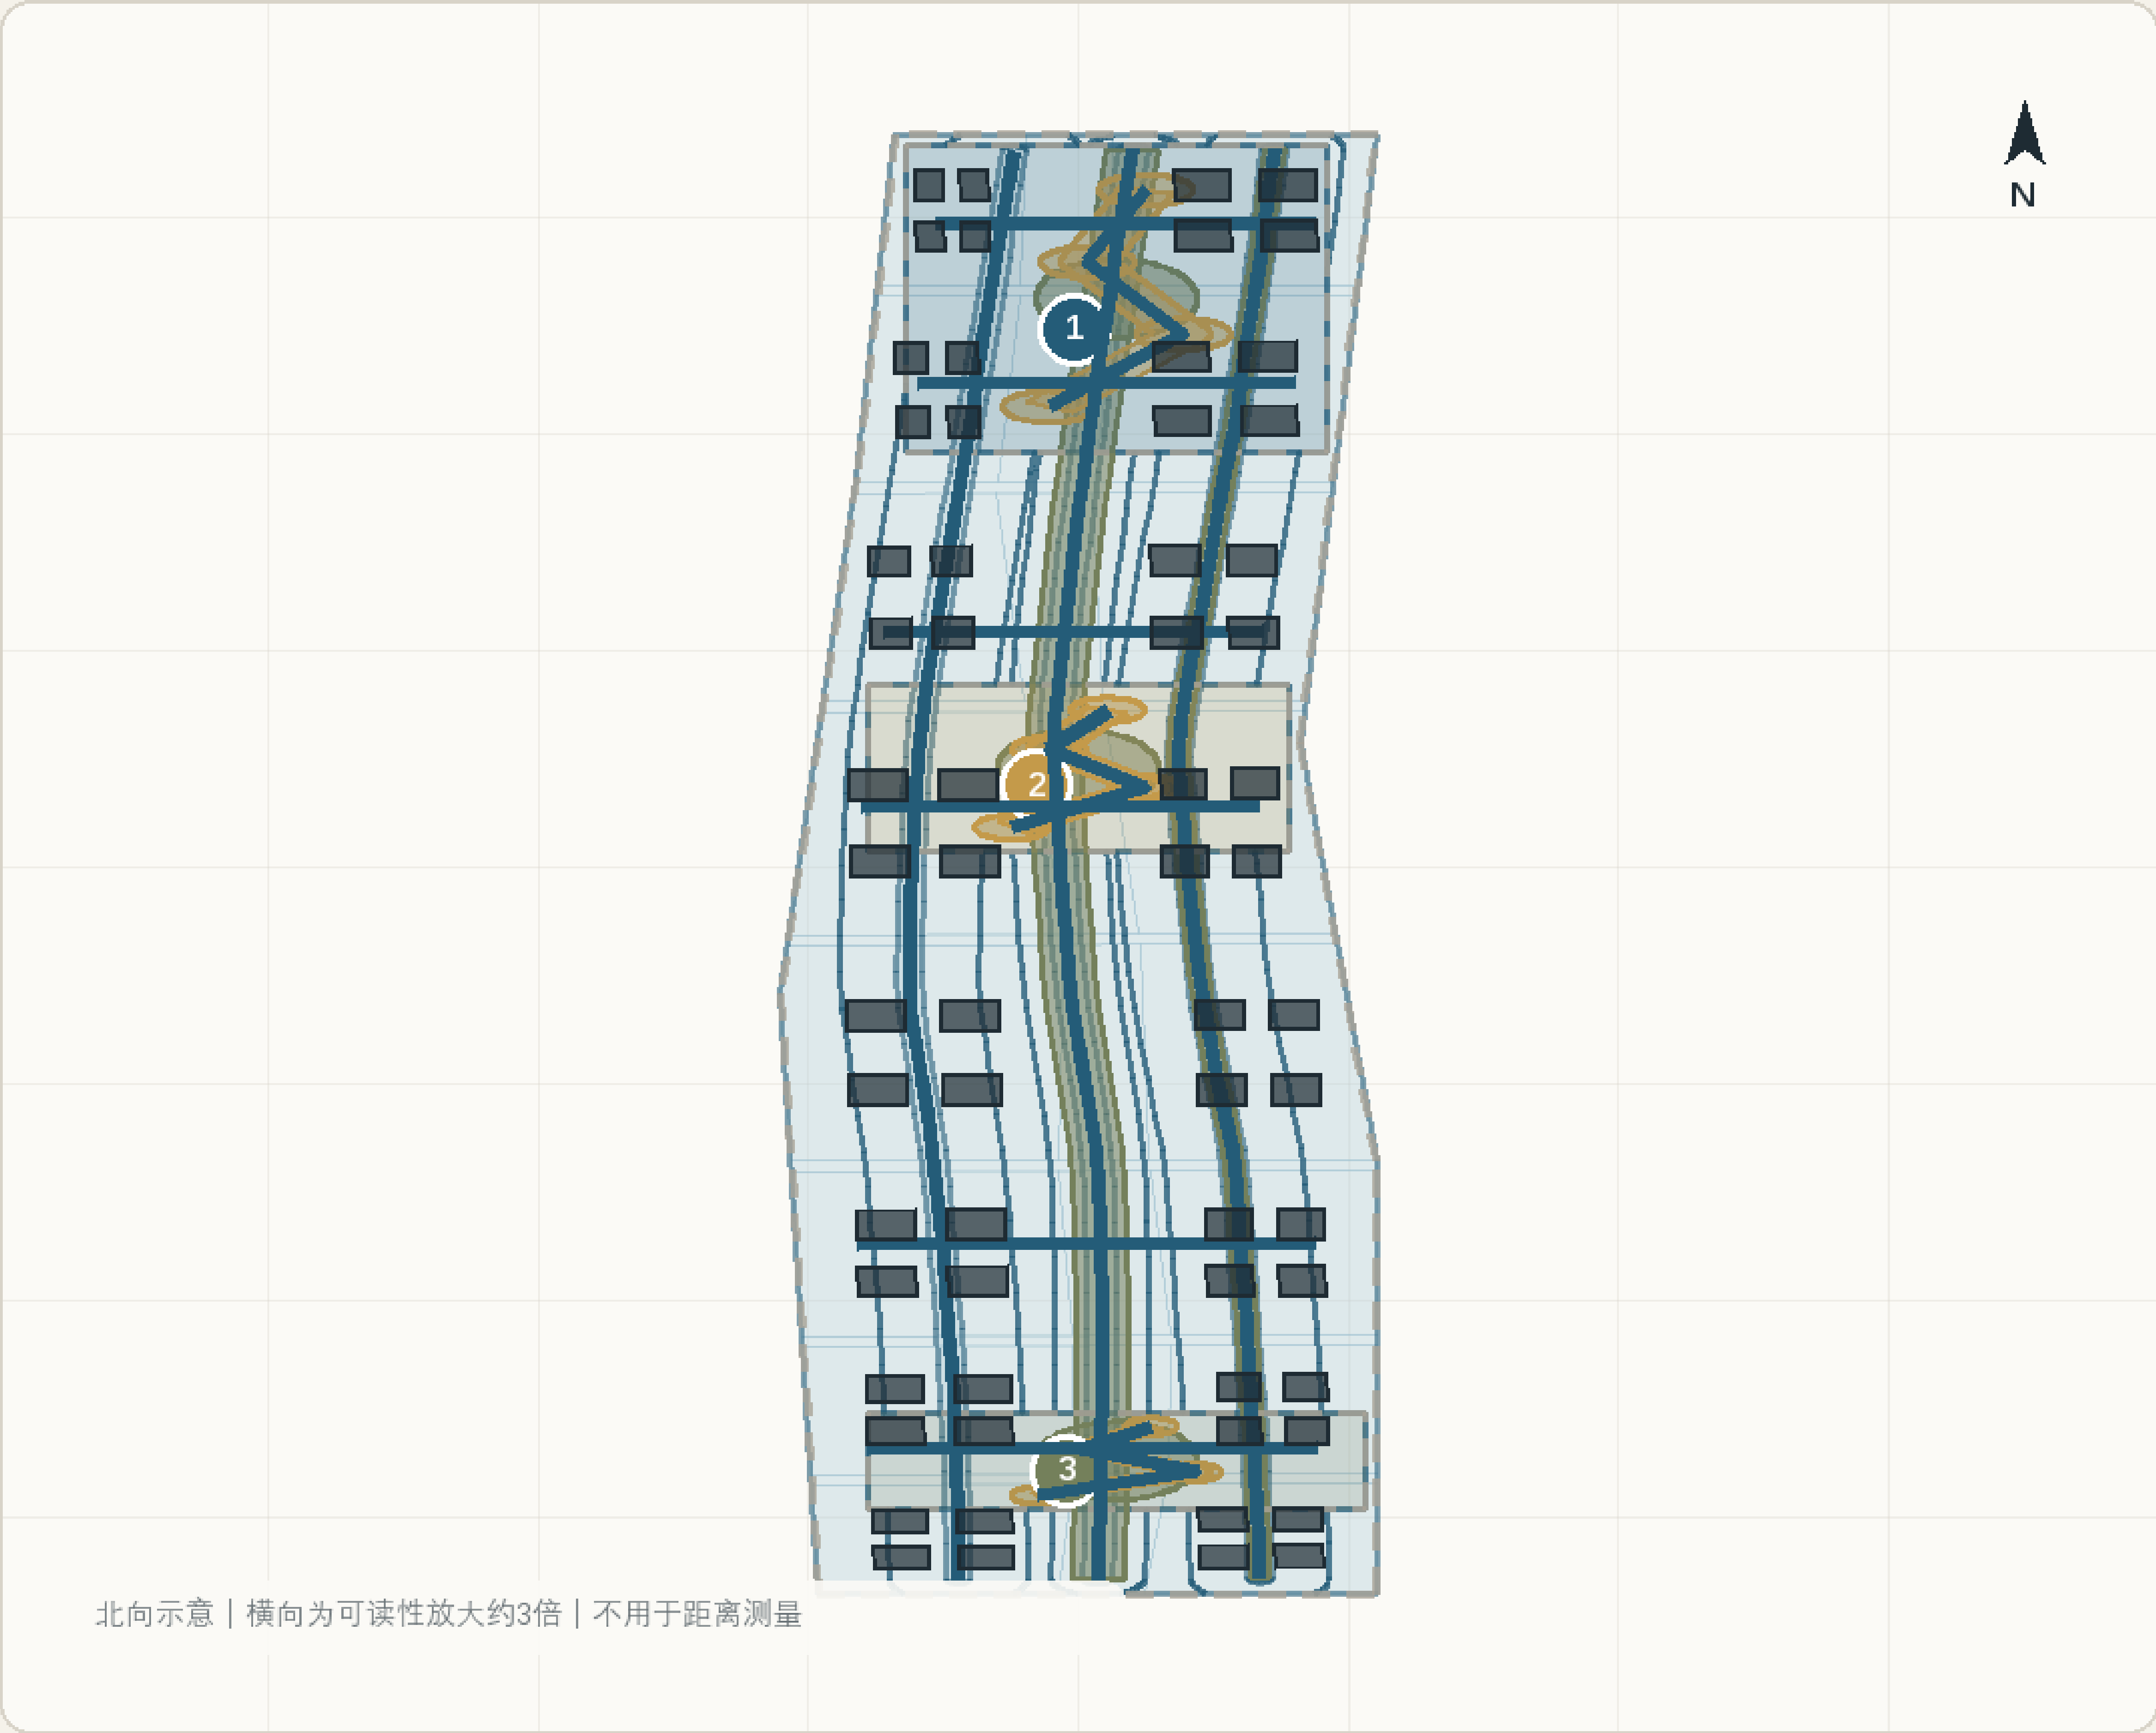

三层范围工作框架

- A 统筹研究范围**
43.6 km² | 产业生态、未来城市与运营网络
- B 总体设计范围**
约11.4 km² | 用地、更新、交通、市政与风貌
- C 重点区域详细设计**
3处 / 368.4 ha | 功能、建筑、交通与公共空间

核心指标快照

11.41 km ²	15.71%	4.20%
总体设计范围	绿地比例	公共空间比例

图例

- 总体设计范围 / 临时边界
- 三处重点片区 / 临时边界
- 一期可讨论范围
- 连续绿地与公共界面
- 慢行与创新服务廊道
- 建筑设计基底

设计注释

三层范围不是三套割裂图纸：战略判断经总体设计落图，再由三处重点区验证空间与运营可实施性。所有面积在正式边界替换后需同步复算。

PROVISIONAL | 总体边界与三处重点片区均为临时粗略范围；不得作为法定红线、审批、测量或精确面积依据。

来源： geometry/*.geojson、metrics.json、proposal.md； 边界来源与用途限制详见 sources.json / assumptions.json。

图示为城市设计提案 / 非测绘图


用地结构与总体空间组织

AI研发 / 公园开敞 / 产业商业 / 社区配套

02 OPEN YARD / 百年京张AI公共创新带

用地结构与总体空间组织

研发转化 - 居住服务 - 文化科研 - 蓝绿交通 | 九类概念用地支撑更新讨论

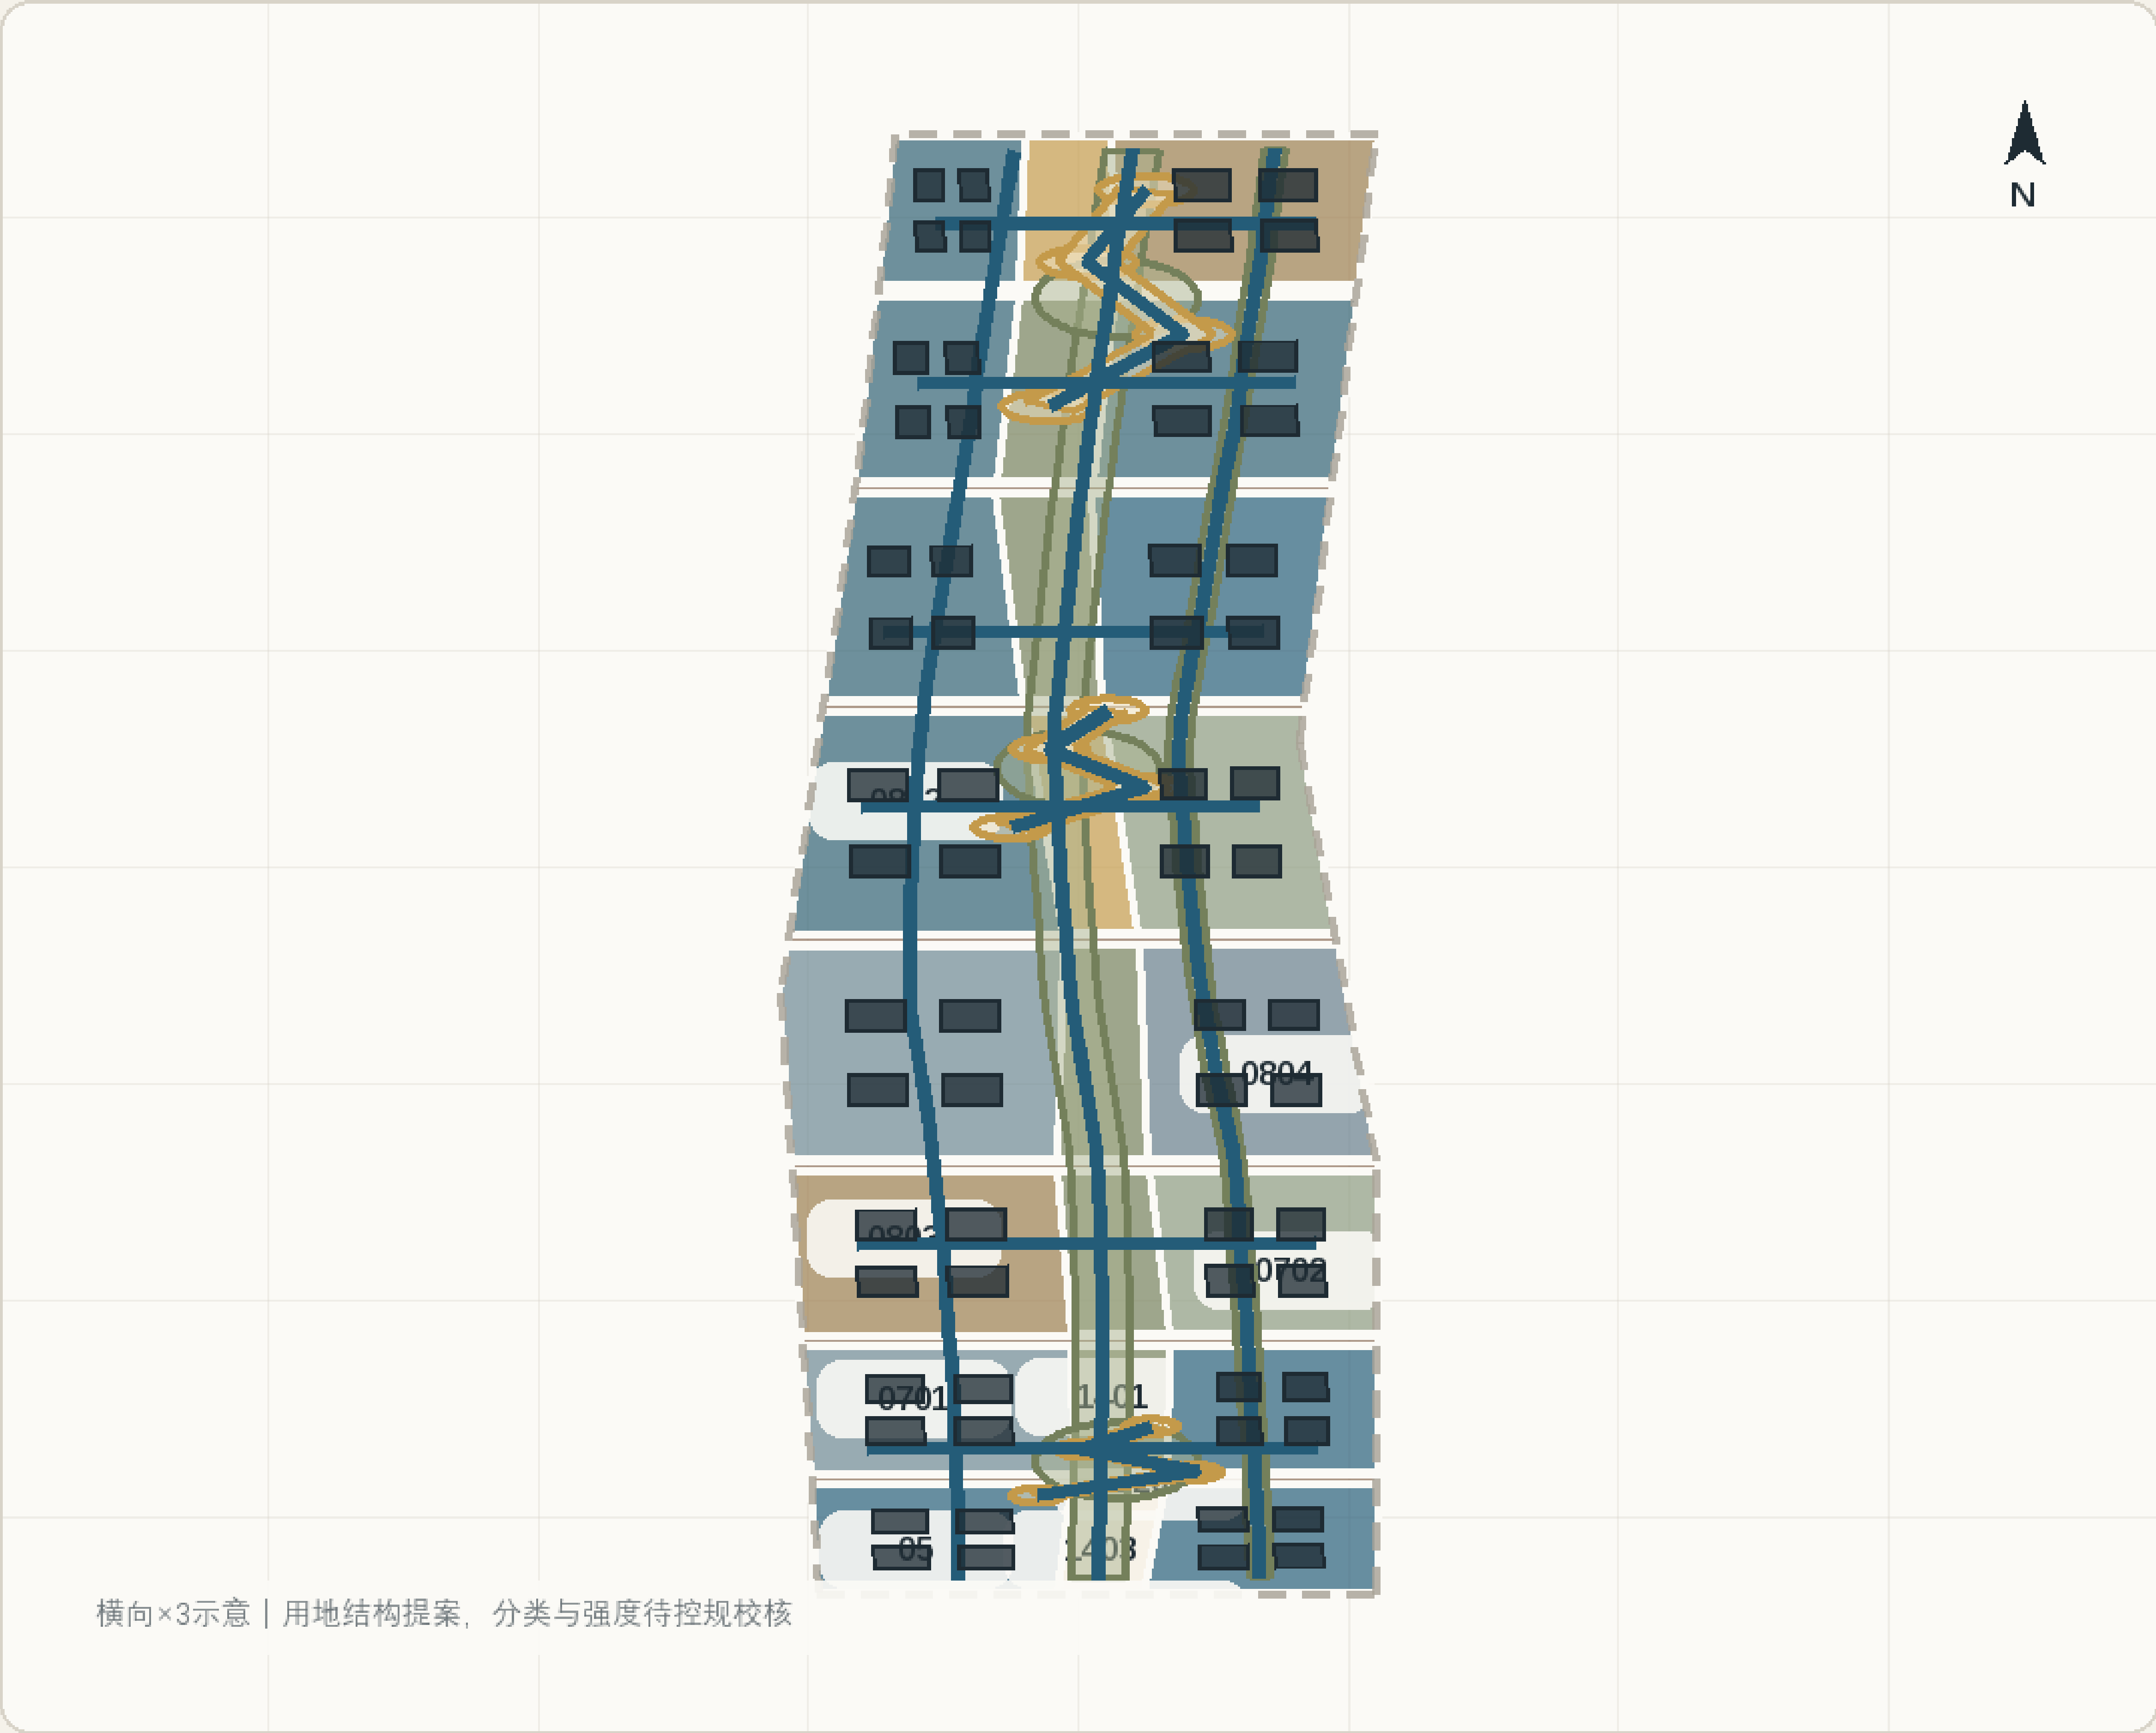

横向×3示意 | 用地结构提案，分类与强度待控规校核

九类概念用地 / 31单元

05	科技商业服务	184.6 ha / 16.2%
0701	人才社区居住	139.9 ha / 12.3%
0702	社区公共服务	117.4 ha / 10.3%
0802	AI研发与转化	269.7 ha / 23.6%
0803	京张文化展示	122.2 ha / 10.7%
0804	教育科研协作	68.4 ha / 6.0%
1207	横向缝合交通	56.5 ha / 4.9%
1401	连续公园绿地	122.2 ha / 10.7%
1403	开源站场广场	60.5 ha / 5.3%

叠加图层

- 绿地系统
- 建筑设计基底
- 公共活动界面
- 临时总体边界
- 慢行创新廊道

设计注释

色块表达“一带三核”的功能连续性，不等同法定用地红线。建筑总规模、容积率、高度、道路红线和退线仍列为待正式控制条件确认。

PROVISIONAL | 总体边界与三处重点片区均为临时粗略范围；不得作为法定红线、审批、测量或精确面积依据。

来源： geometry/*.geojson、metrics.json、proposal.md； 边界来源与用途限制详见 sources.json / assumptions.json。

图示为城市设计提案 / 非测绘图


三处重点区域详细设计

众智园 / 北京AI原点社区 / 大钟寺

03 OPEN YARD / 百年京张AI公共创新带

三处重点区域：定位、动作与场景

众智园 - 北京AI原点社区 - 大钟寺 | 详细设计任务索引与实施依赖

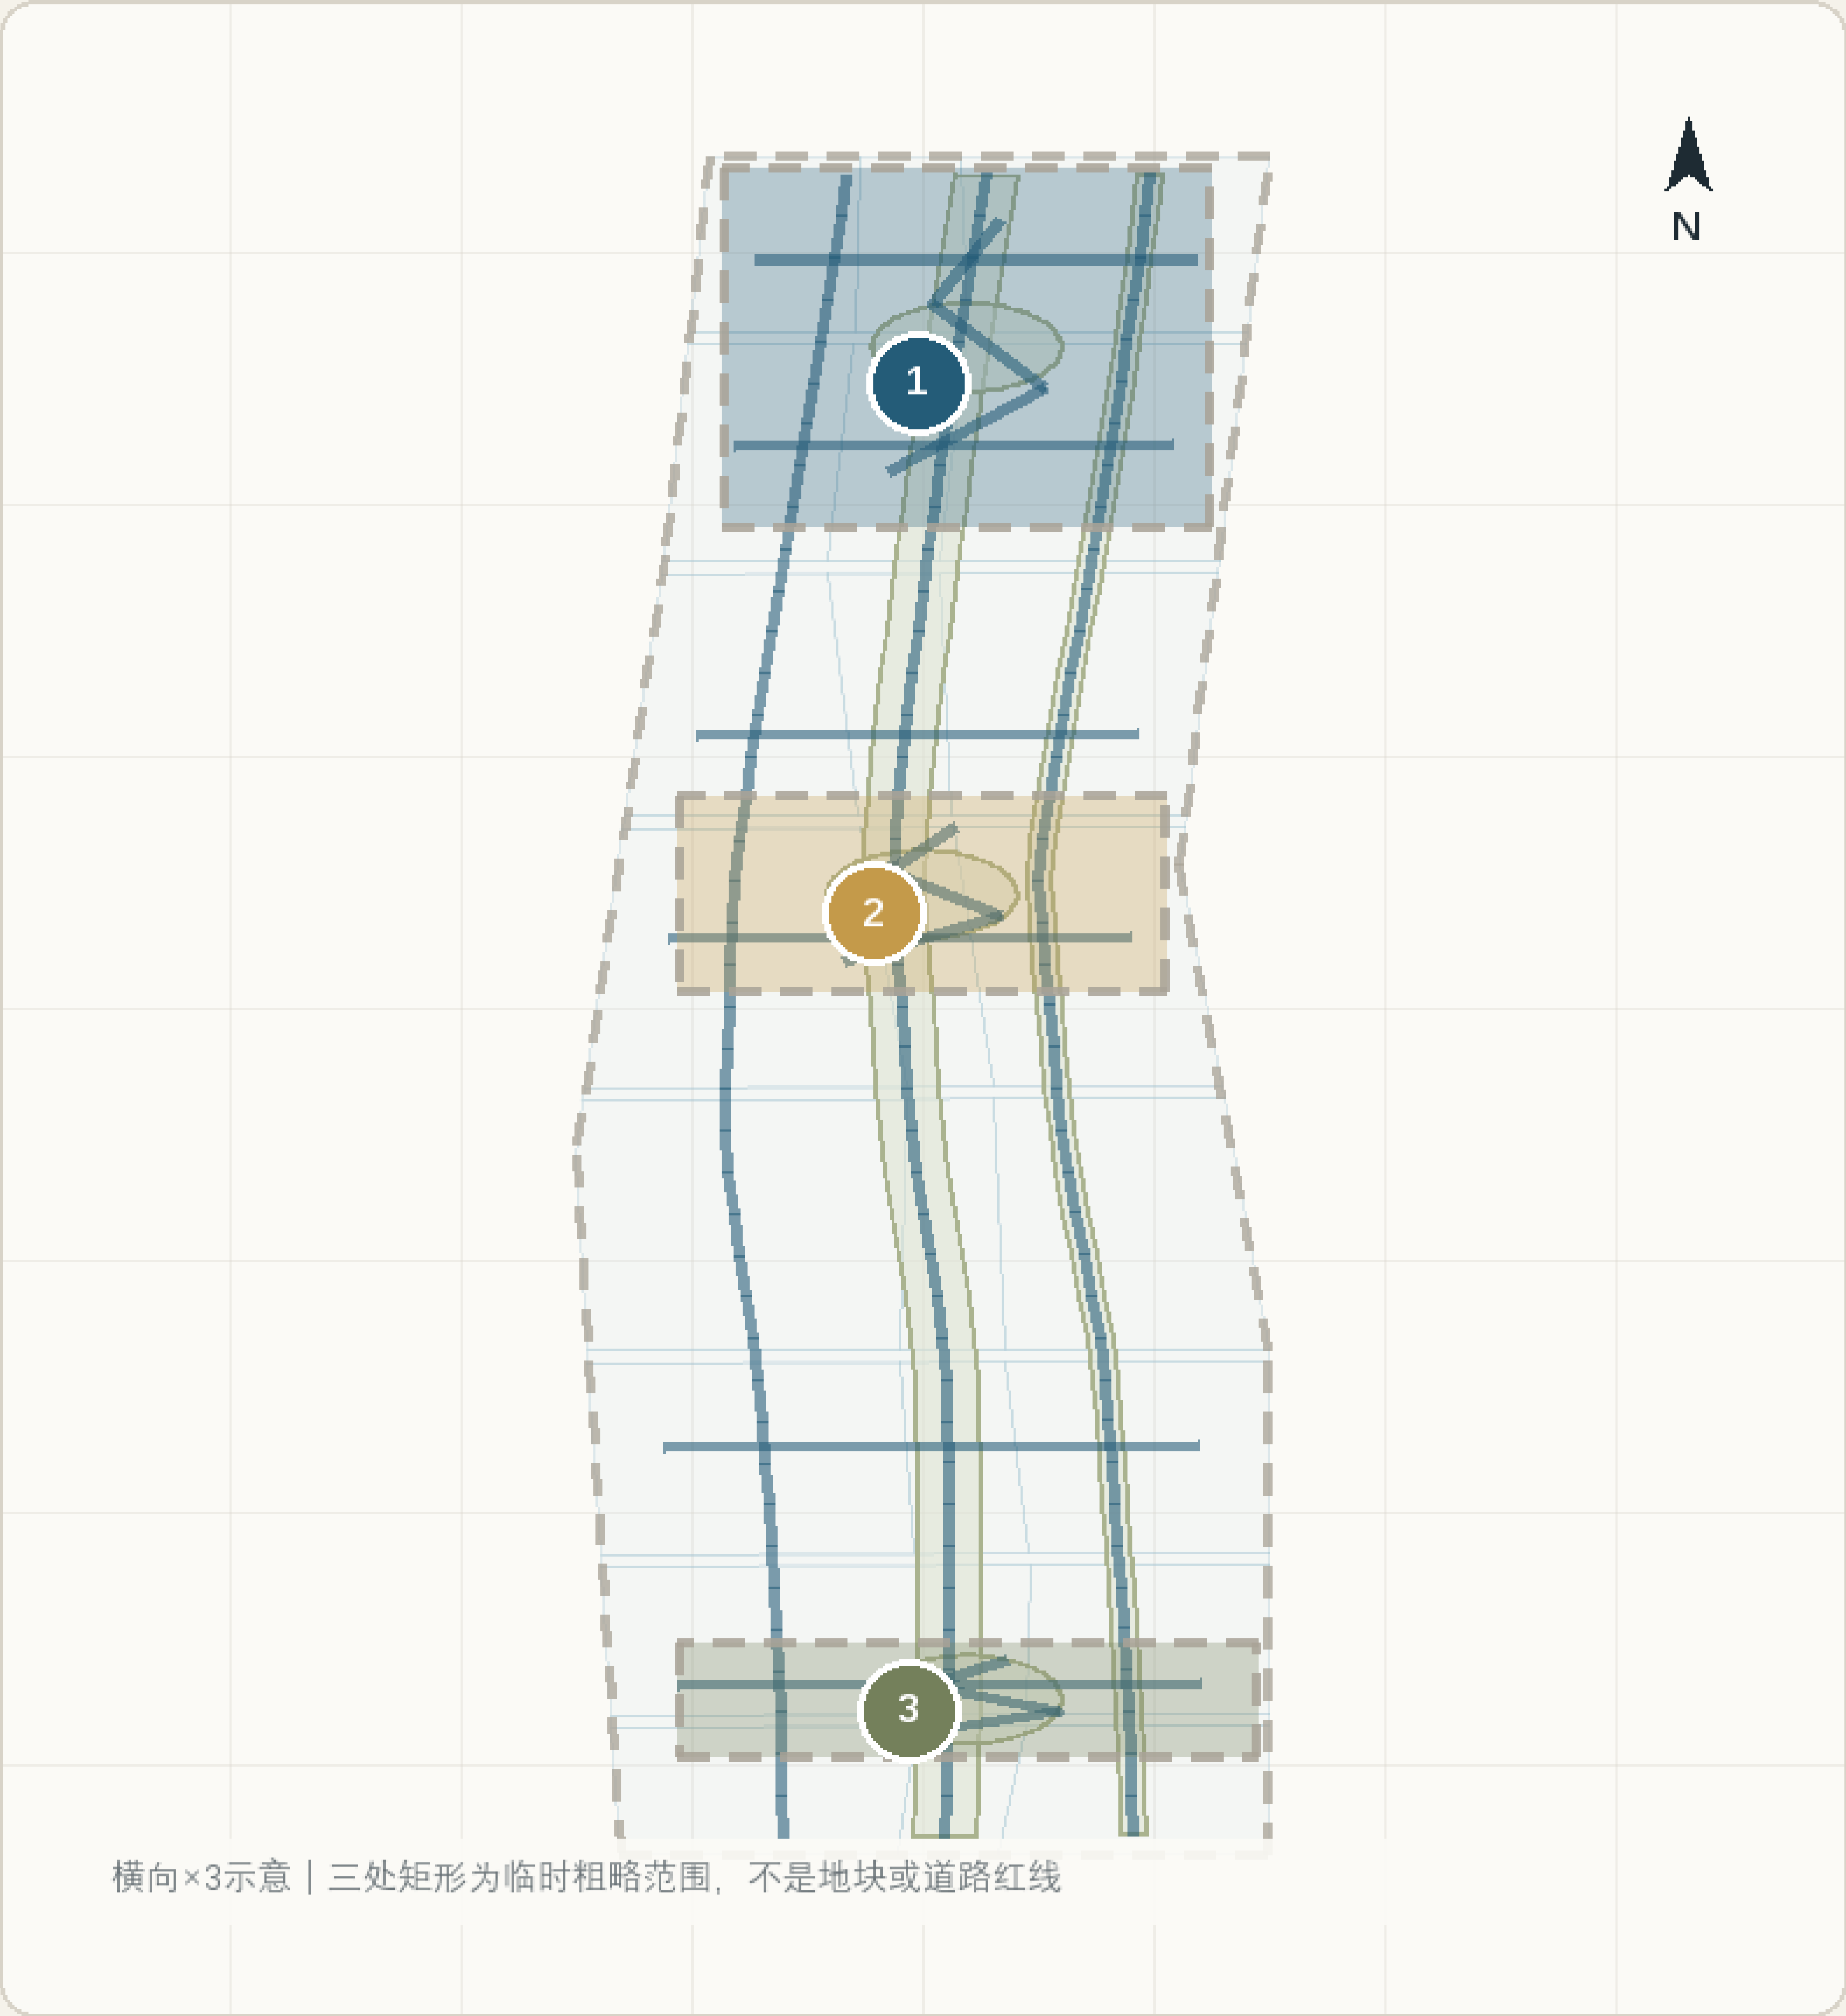

1 众智园AI自主创新加速区

公告约 192.1 ha

花园型全栈自主创新街区

强化清河界面、标准治理展示、低碳创新交往与开放测试。

AI场景：自主模型测试 / 安全治理沙盒 / 低碳算力体验

2 北京AI原点社区

公告约 104.3 ha

近校型成果转化与人才社区

缝合校区、园区、街区慢行，补足发布、居住和开源协作。

AI场景：开源发布 / 成果转化 / 人才服务 / 近校孵化

3 大钟寺AI产业聚集区

公告约 72.0 ha

城市型智能经济与国际交往街区

围绕大钟寺站与四象限步行连通，更新商业和企业公共界面。

AI场景：智能体展示 / 数据要素 / 内容消费 / 国际路演

边界与定位

--- 临时重点片区边界

● 设计定位与场景编号

设计注释

每区均需以功能、建筑、交通、公共空间、AI治理和实施项目共同深化；正式多边形发布后整体重算。

PROVISIONAL | 总体边界与三处重点片区均为临时粗略范围；不得作为法定红线、审批、测量或精确面积依据。

来源： geometry/*.geojson、metrics.json、proposal.md； 边界来源与用途限制详见 sources.json / assumptions.json。

图示为城市设计提案 / 非测绘图


交通慢行与蓝绿公共空间

慢行 / 绿地 / 公共界面 / AI场景锚点

04 OPEN YARD / 百年京张AI公共创新带

交通慢行与蓝绿公共空间复合系统

遗址公园活力带为骨架 | 慢行、绿地、公共界面、轨道接驳与AI场景协同

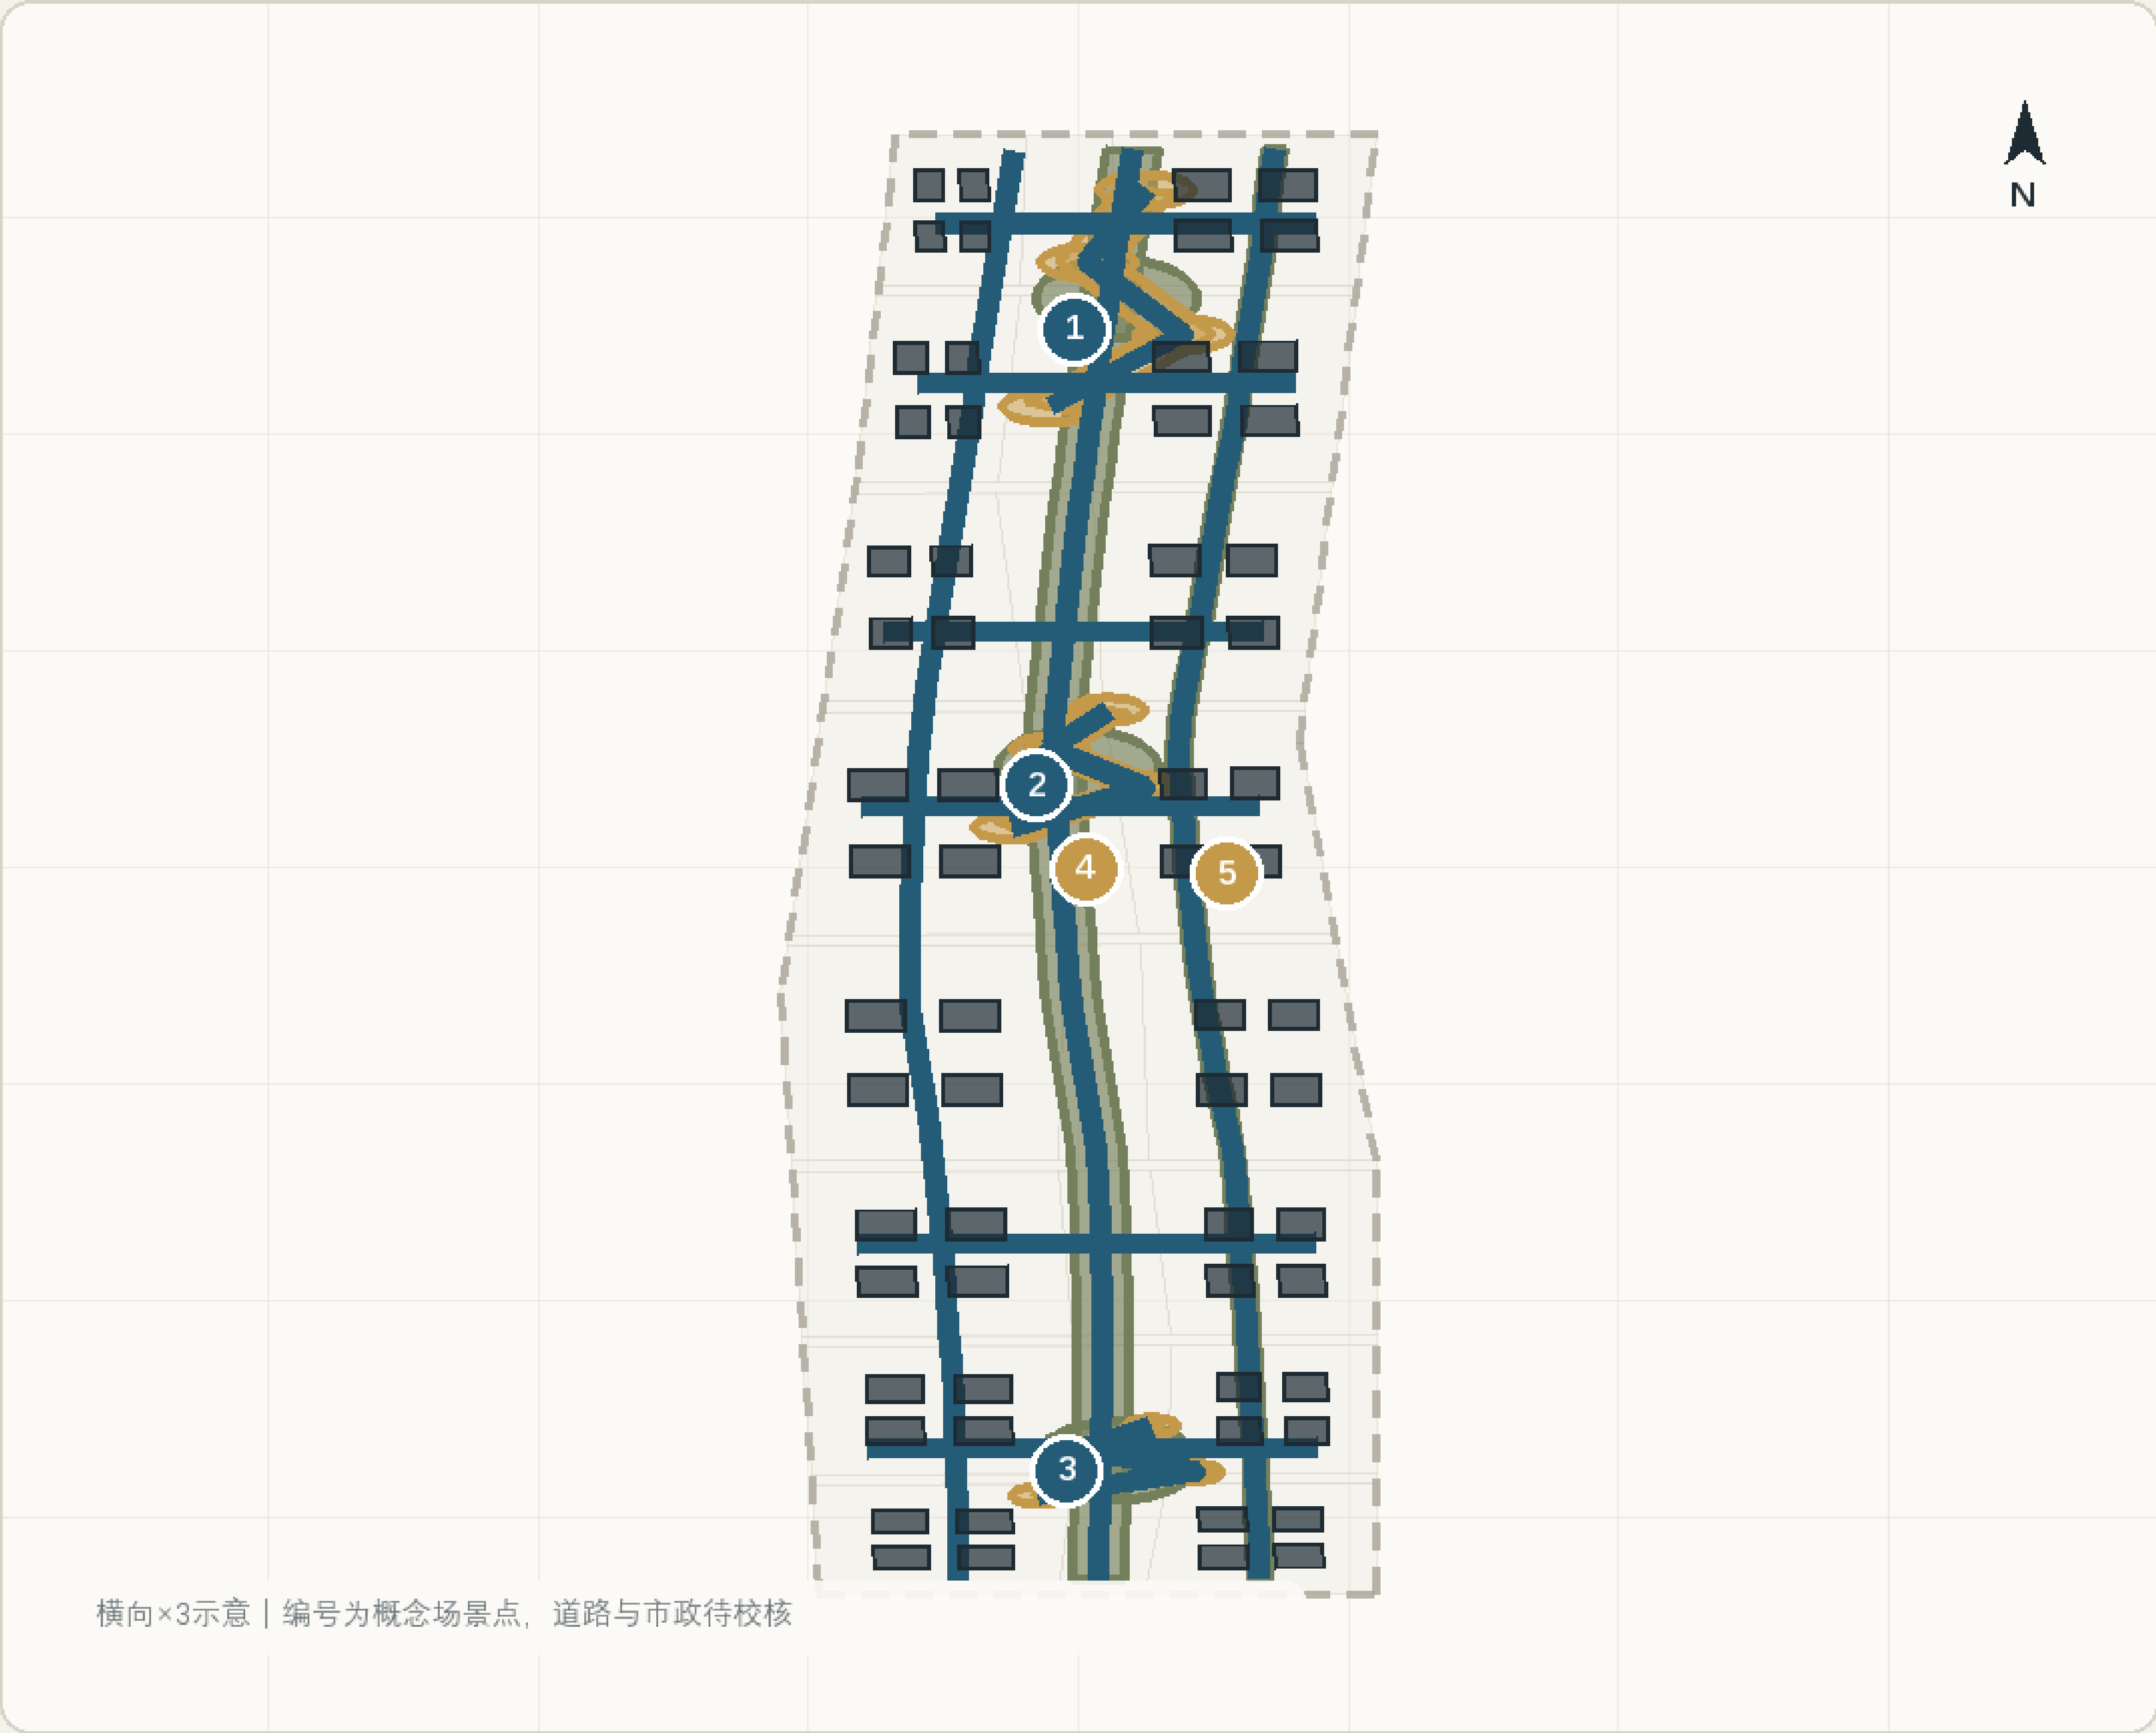

横向×3示意 | 编号为概念场景点，道路与市政待校核

复合系统图例

- 连续公园绿地
- 公共活动界面
- 慢行与创新服务廊道
- 建筑设计基底
- 概念AI场景锚点
- 临时总体边界

场景锚点与空间载体

- 1 清河低碳创新廊
- 2 AI慢行导航
- 3 开源发布厅
- 4 大钟寺国际路演客厅
- 5 AI公共服务与端侧算力节点

空间供给



设计注释

慢行、绿地和公共空间按同一网络校核。感知、导航和运营场景须坚持数据最小化、可解释、人工复核与授权边界。

PROVISIONAL | 总体边界与三处重点片区均为临时粗略范围；不得作为法定红线、审批、测量或精确面积依据。

来源： geometry/*.geojson、metrics.json、proposal.md； 边界来源与用途限制详见 sources.json / assumptions.json。

图示为城市设计提案 / 非测绘图

核心指标与证据复核

数值 / 公式 / 来源文件 / 复算约束

05 OPEN YARD / 百年京张AI公共创新带

核心指标与证据复核

known / unknown 分层表达 | 数值、公式、来源文件与正式深化前置条件同屏

总体设计范围面积

KNOWN

11.413 km²

置信度: medium

复核: area(project(site_boundary, EPSG:4548))

绿地比例

KNOWN

15.71%

置信度: medium

复核: green_space_area_sqm / site_area_sqm

公共空间比例

KNOWN

4.20%

置信度: medium

复核: public_space_area_sqm / site_area_sqm

建筑基底面积

KNOWN

1.264 km²

置信度: medium

复核: area(unary_union(conceptual_building_footprints))

重点区域数量

KNOWN

3 处

置信度: high

复核: count(required_provisional_KEY_AREA_features)

容积率

UNKNOWN

待确认

置信度: unknown

复核: total_floor_area_sqm / official_site_area_sqm

证据路径

指标	状态 / 置信度	来源文件	复算约束
总体设计范围面积	known / medium	geometry/site_boundary.geojson	替换官方边界后重算
绿地比例	known / medium	geometry/green_space.geojson + geometry/site_boundary.geojson	替换官方边界后重算
公共空间比例	known / medium	geometry/public_space.geojson + geometry/site_boundary.geojson	替换官方边界后重算
建筑基底面积	known / medium	geometry/buildings.geojson	替换官方边界后重算
容积率	unknown / unknown	brief/site-package/ranges/planning_limits.json + geometry/constraints.geojson	Approved FAR controls and an official site plan

指标状态图例

- known: 可由当前提交数据复核
- design-derived: 方案图层推导
- unknown: 缺正式控制条件
- provisional: 替换边界后重算

设计注释

面积和比例严格回指 GeoJSON; 容积率不以推测值填充。正式边界、控规、权属与市政条件到位后, 应整体重跑图层、指标、HTML和PDF。

PROVISIONAL | 总体边界与三处重点片区均为临时粗略范围; 不得作为法定红线、审批、测量或精确面积依据。

来源: geometry/*.geojson、metrics.json、proposal.md; 边界来源与用途限制详见 sources.json / assumptions.json。

图示为城市设计提案 / 非测绘图