


京智线 JING · ZHI LINE — 总体概念与设计总览

一条主轴 · 五座车站 · 两翼支撑 · 多次缝合 | 总体设计范围约 11.4 km²

PROVISIONAL 临时边界 · 非官方红线

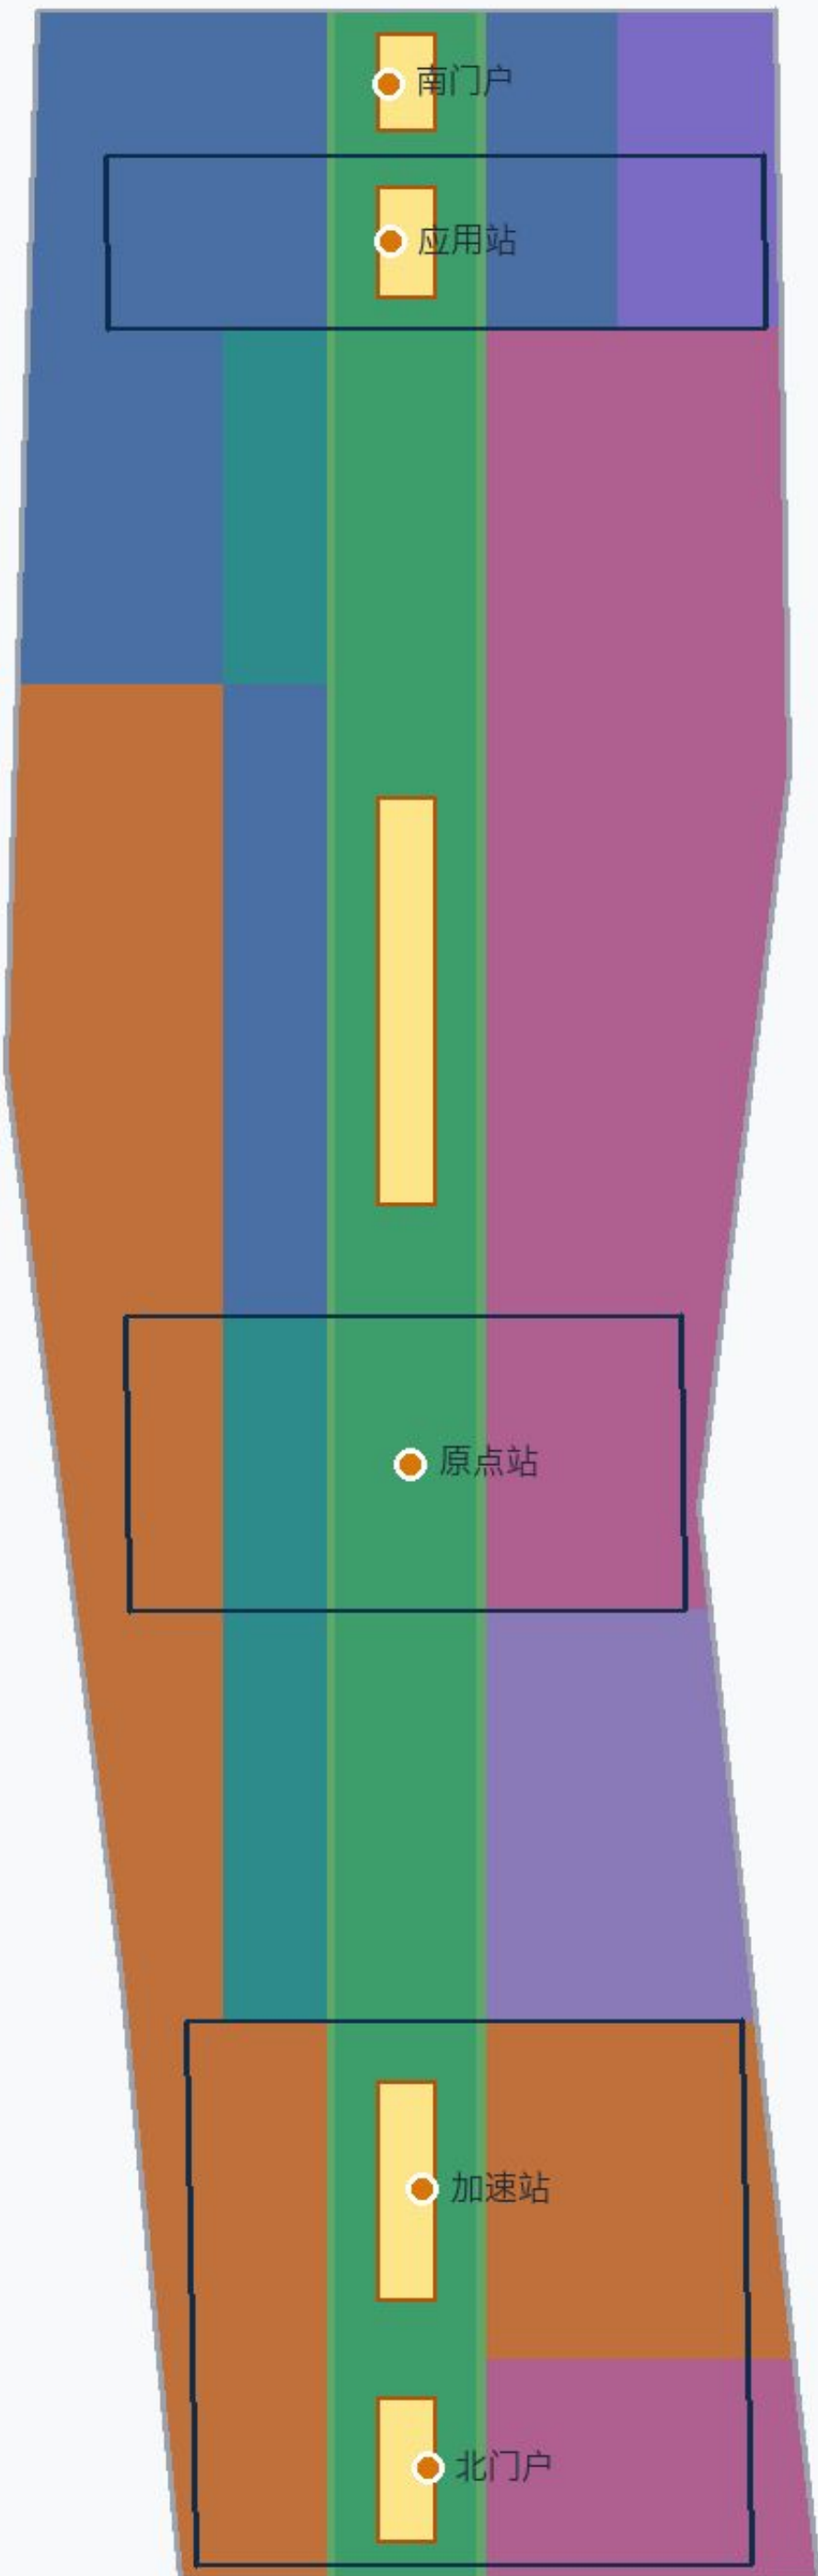

总体设计范围 provisional 边界 (虚线, 非官方红线)

总体概念: 代码 × 铁轨

百年前，詹天佑铺下中国人自主设计的第一条干线铁路——京张铁路；
百年后，我们提议为 AI 时代铺下中国人自主设计的第一条创新带——京智线。


- 文化线 Heri

文化线 Heritage Line
百年京张文化带 · 京张遗址公园活力带
- 生活线 Livi

生活线 Living Line
都市AI生活体验带 · 五座车站与社区
- 创新线 Inno

创新线 Innovation Line
AI融合创新带 · 众智园-原点-大钟寺

三区两翼协同回路 (

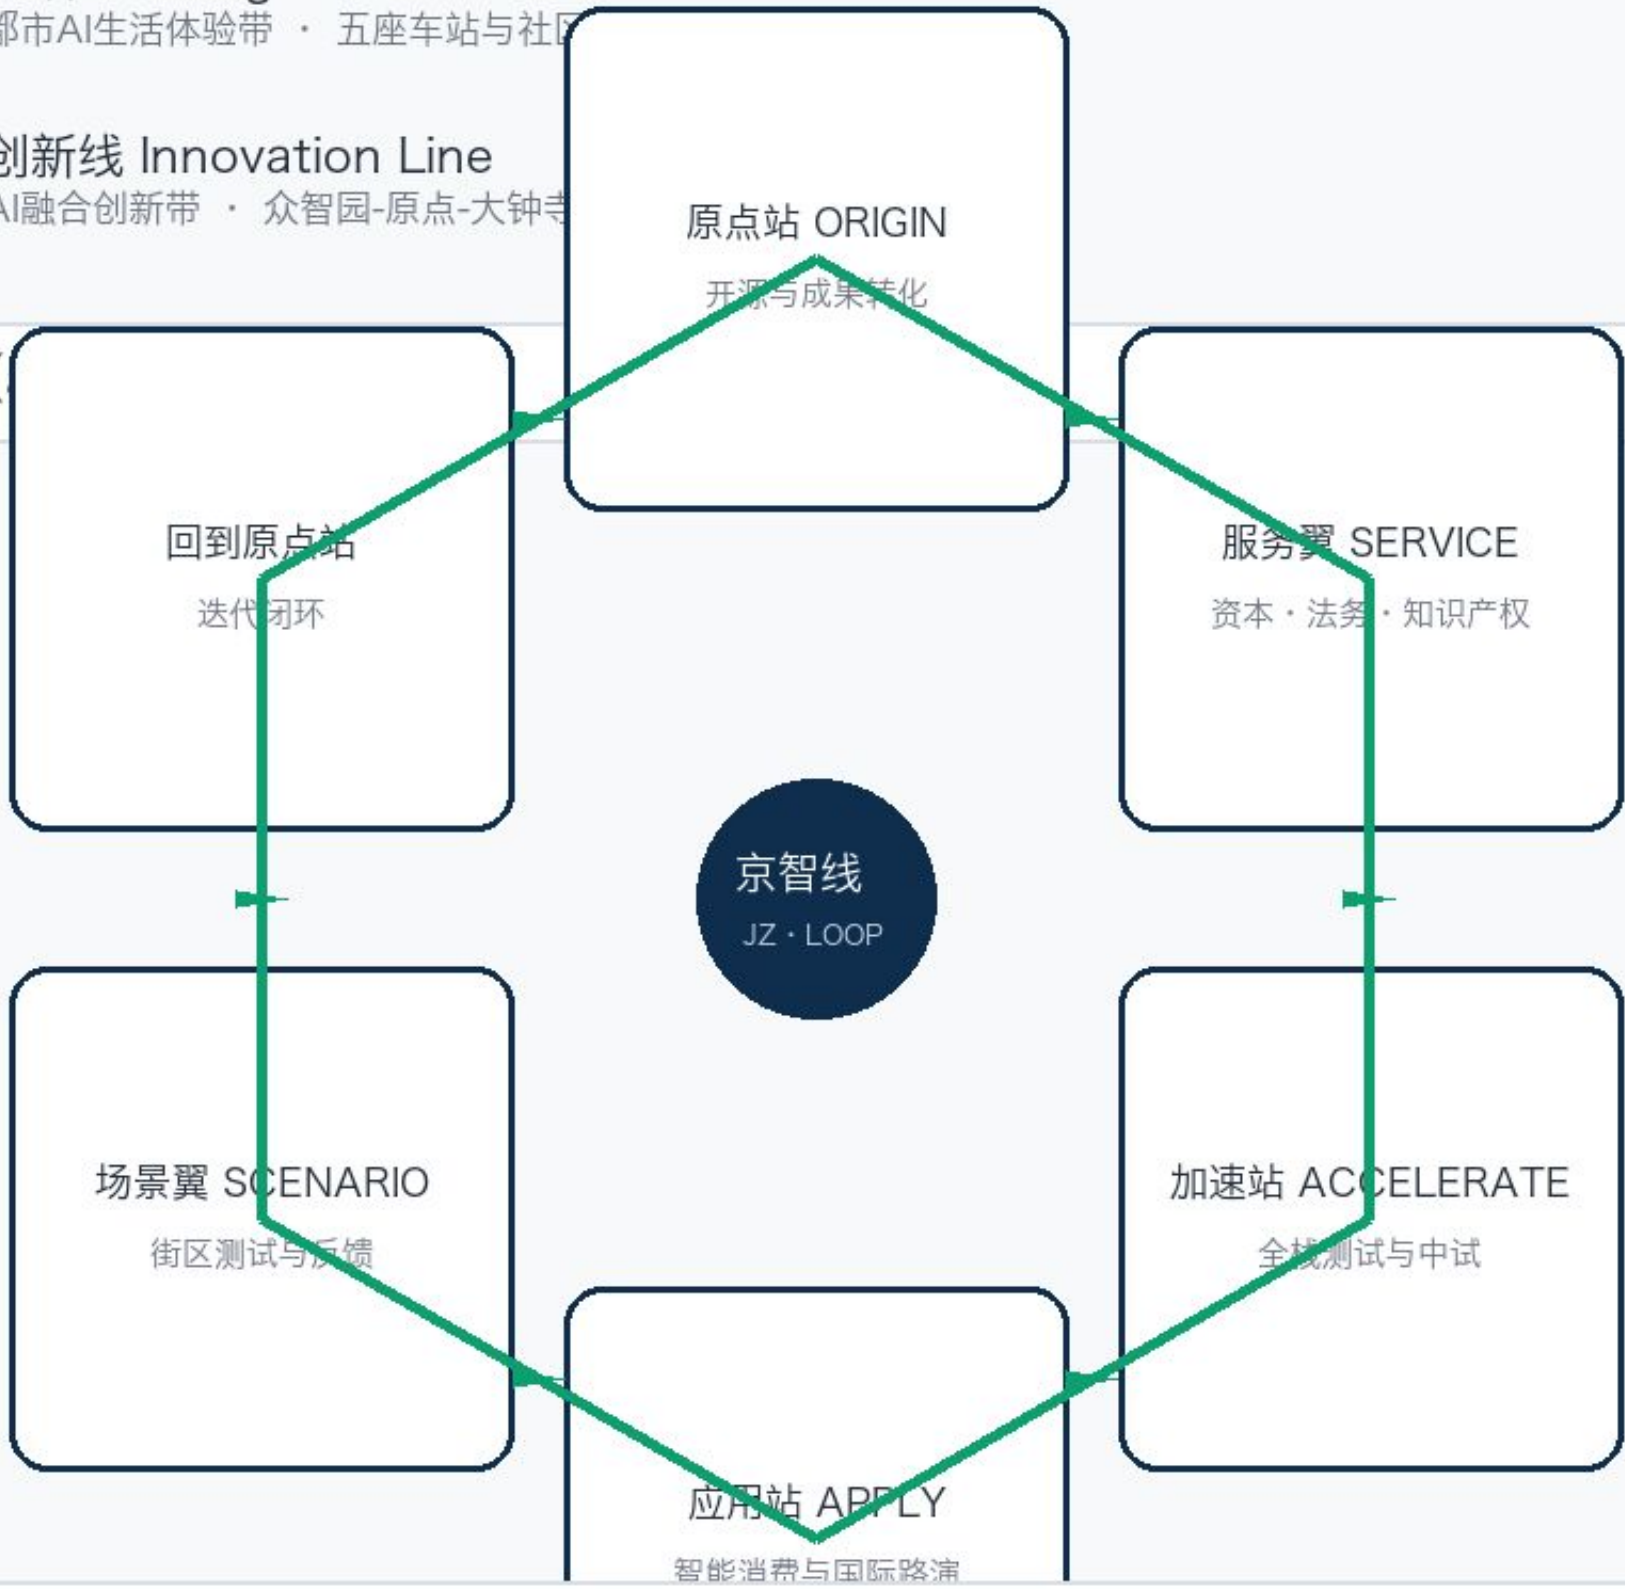

图例

- | | | | |
|--------------|-------------|-----------|-----------|
| 科研用地 0802 | 教育用地 0804 | 商业服务业 05 | 居住用地 0701 |
| 社区服务 0702 | 公园绿地 1401 | 防护绿地 1402 | 广场用地 1403 |
| 留白 · AI测试 16 | 建筑基底 (概念体量) | | |

数据来源: submissions/JackyHanS/jingzhi-line geometry/*.geojson (EPSG:4548 复算) · 边界为 provisional_constraint 临时粗略边界, 官方红线发布后须复算 | 概念建议, 不构成政府审定结论

总体概念: 代码 × 铁轨 —— 百年前中国第一条自主干线铁路, 百年后第一条 AI 创新带


命名: 文化线/生活线/创新线 · 原点站/加速站/应用站 · 服务翼/场景翼 · Logo: 道钉 × 光标

证据: site_boundary.geojson#SITE-001 · land_use 61 地块 · phasing 3 期 · 边界为 provisional 临时粗略边界

京智线 — 用地结构与空间结构

61 个用地地块 · 无缝隙无重叠覆盖提交边界 (EPSG:4548 拓扑校验通过)

PROVISIONAL 临时边界 · 非官方红线

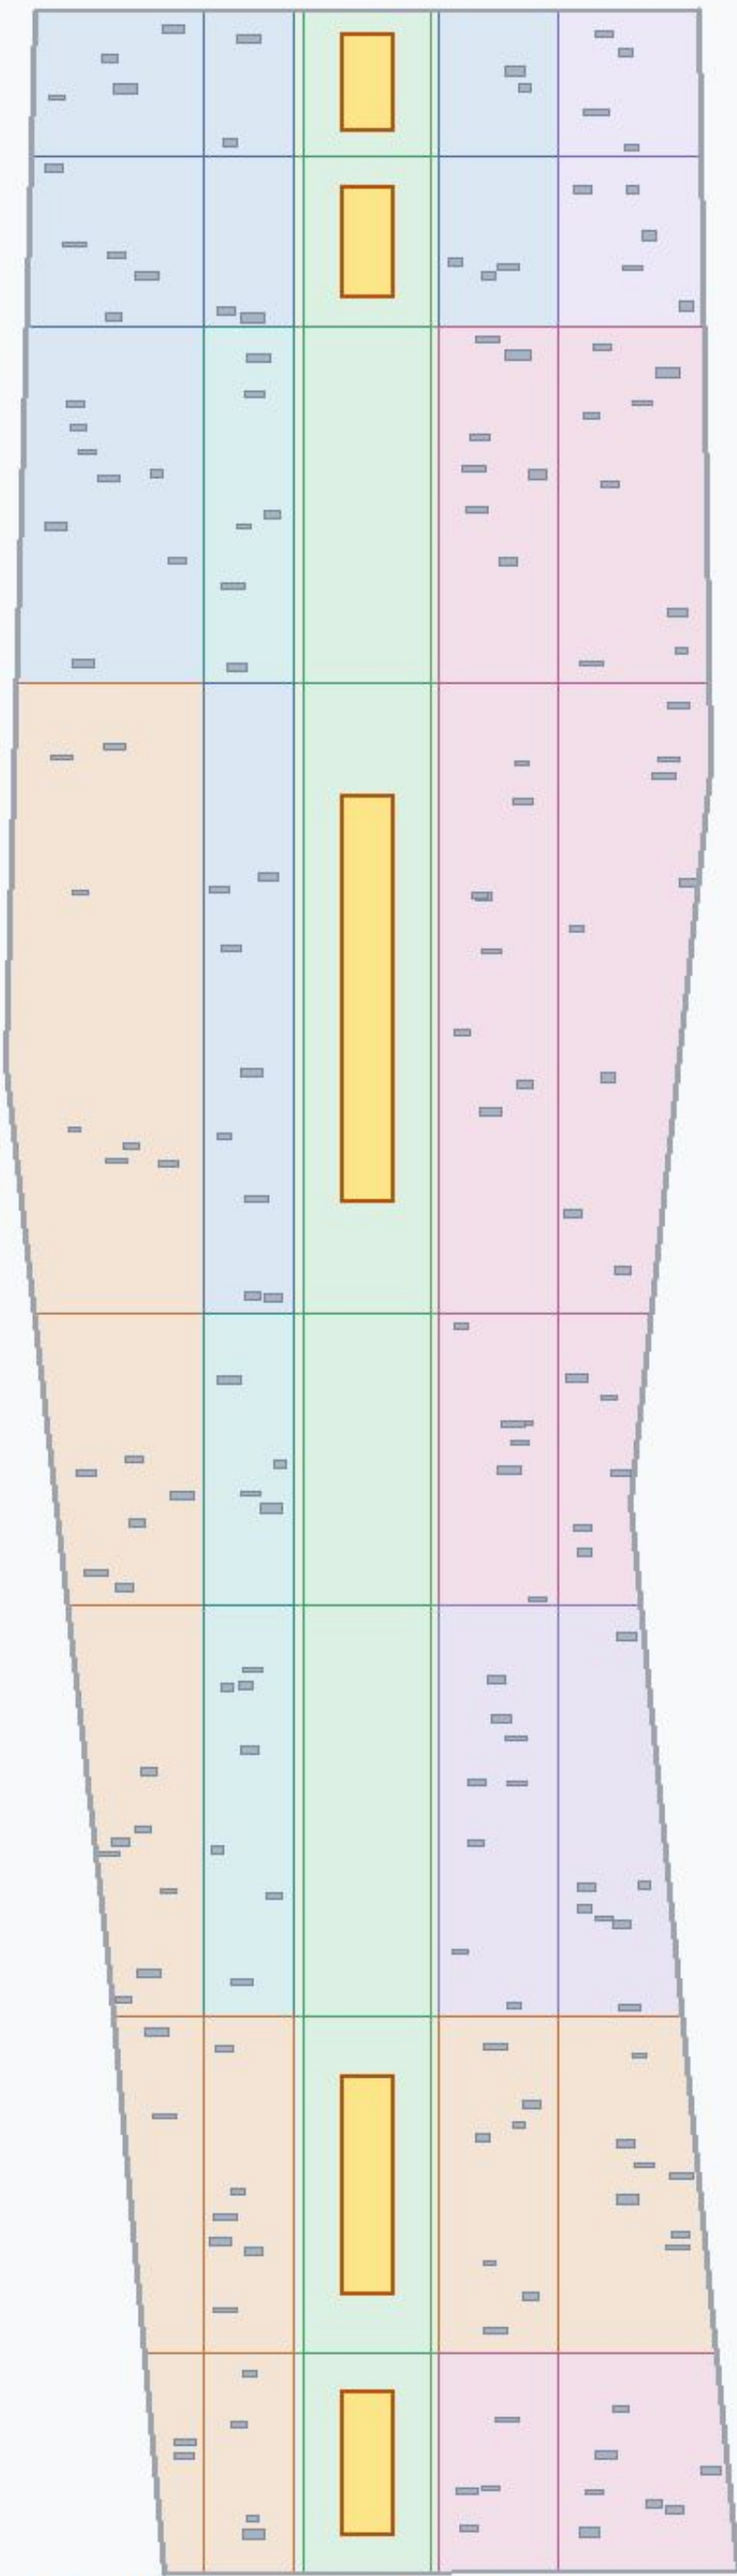

总体设计范围 provisional 边界 (虚线)

用地结构统计 (EPSG:4548 复算)

科研用地 0802	173.5 ha	15.2%	
教育用地 0804	69.1 ha	6.1%	
商业服务业 05	273.1 ha	23.9%	
居住用地 0701	264.8 ha	23.2%	
社区服务 0702	64.8 ha	5.7%	
公园绿地 1401	195.8 ha	17.2%	
防护绿地 1402	31.1 ha	2.7%	
广场用地 1403	36.6 ha	3.2%	
留白 · AI测试 16	32.5 ha	2.9%	

空间结构: 一条主轴 · 五座车站 · 两翼支撑 · 多次缝合

一条主轴 京张遗址公园活力带 (文化线), 南北贯通约 9.7 km

五座车站 北门户/加速站/原点站/应用站/南门户五处广场节点

两翼支撑 西翼中关村科技服务带 + 东翼小月河场景赋能带

多次缝合 9 条东西缝合路 + 16 m 绿楔连接主轴向两翼渗透

拆改留方向 (概念建议, 非地块结论)



比例为依据公开现状认知的方向性划分, 须以权属与控规复核后深化

数据来源: geometry/land_use.geojson (61 地块) + metrics.json | 用地分类依据《用地用海分类指南》| 面积均为 provisional 临时值


拆改留方向: 保留为基 · 改造为主 · 新建为辅 · 留白为试验; 控规指标为待确认条件

分期: P1 近期绿廊贯通/原点/大钟寺 · P2 中期众智园全栈体系 · P3 远期两翼深化

京智线 — 交通慢行与蓝绿公共空间复合系统

文化线绿道主轴 · 9 条东西缝合路 · 大钟寺活力环线 · 10 处 AI 场景节点

PROVISIONAL 临时边界 · 非官方红线

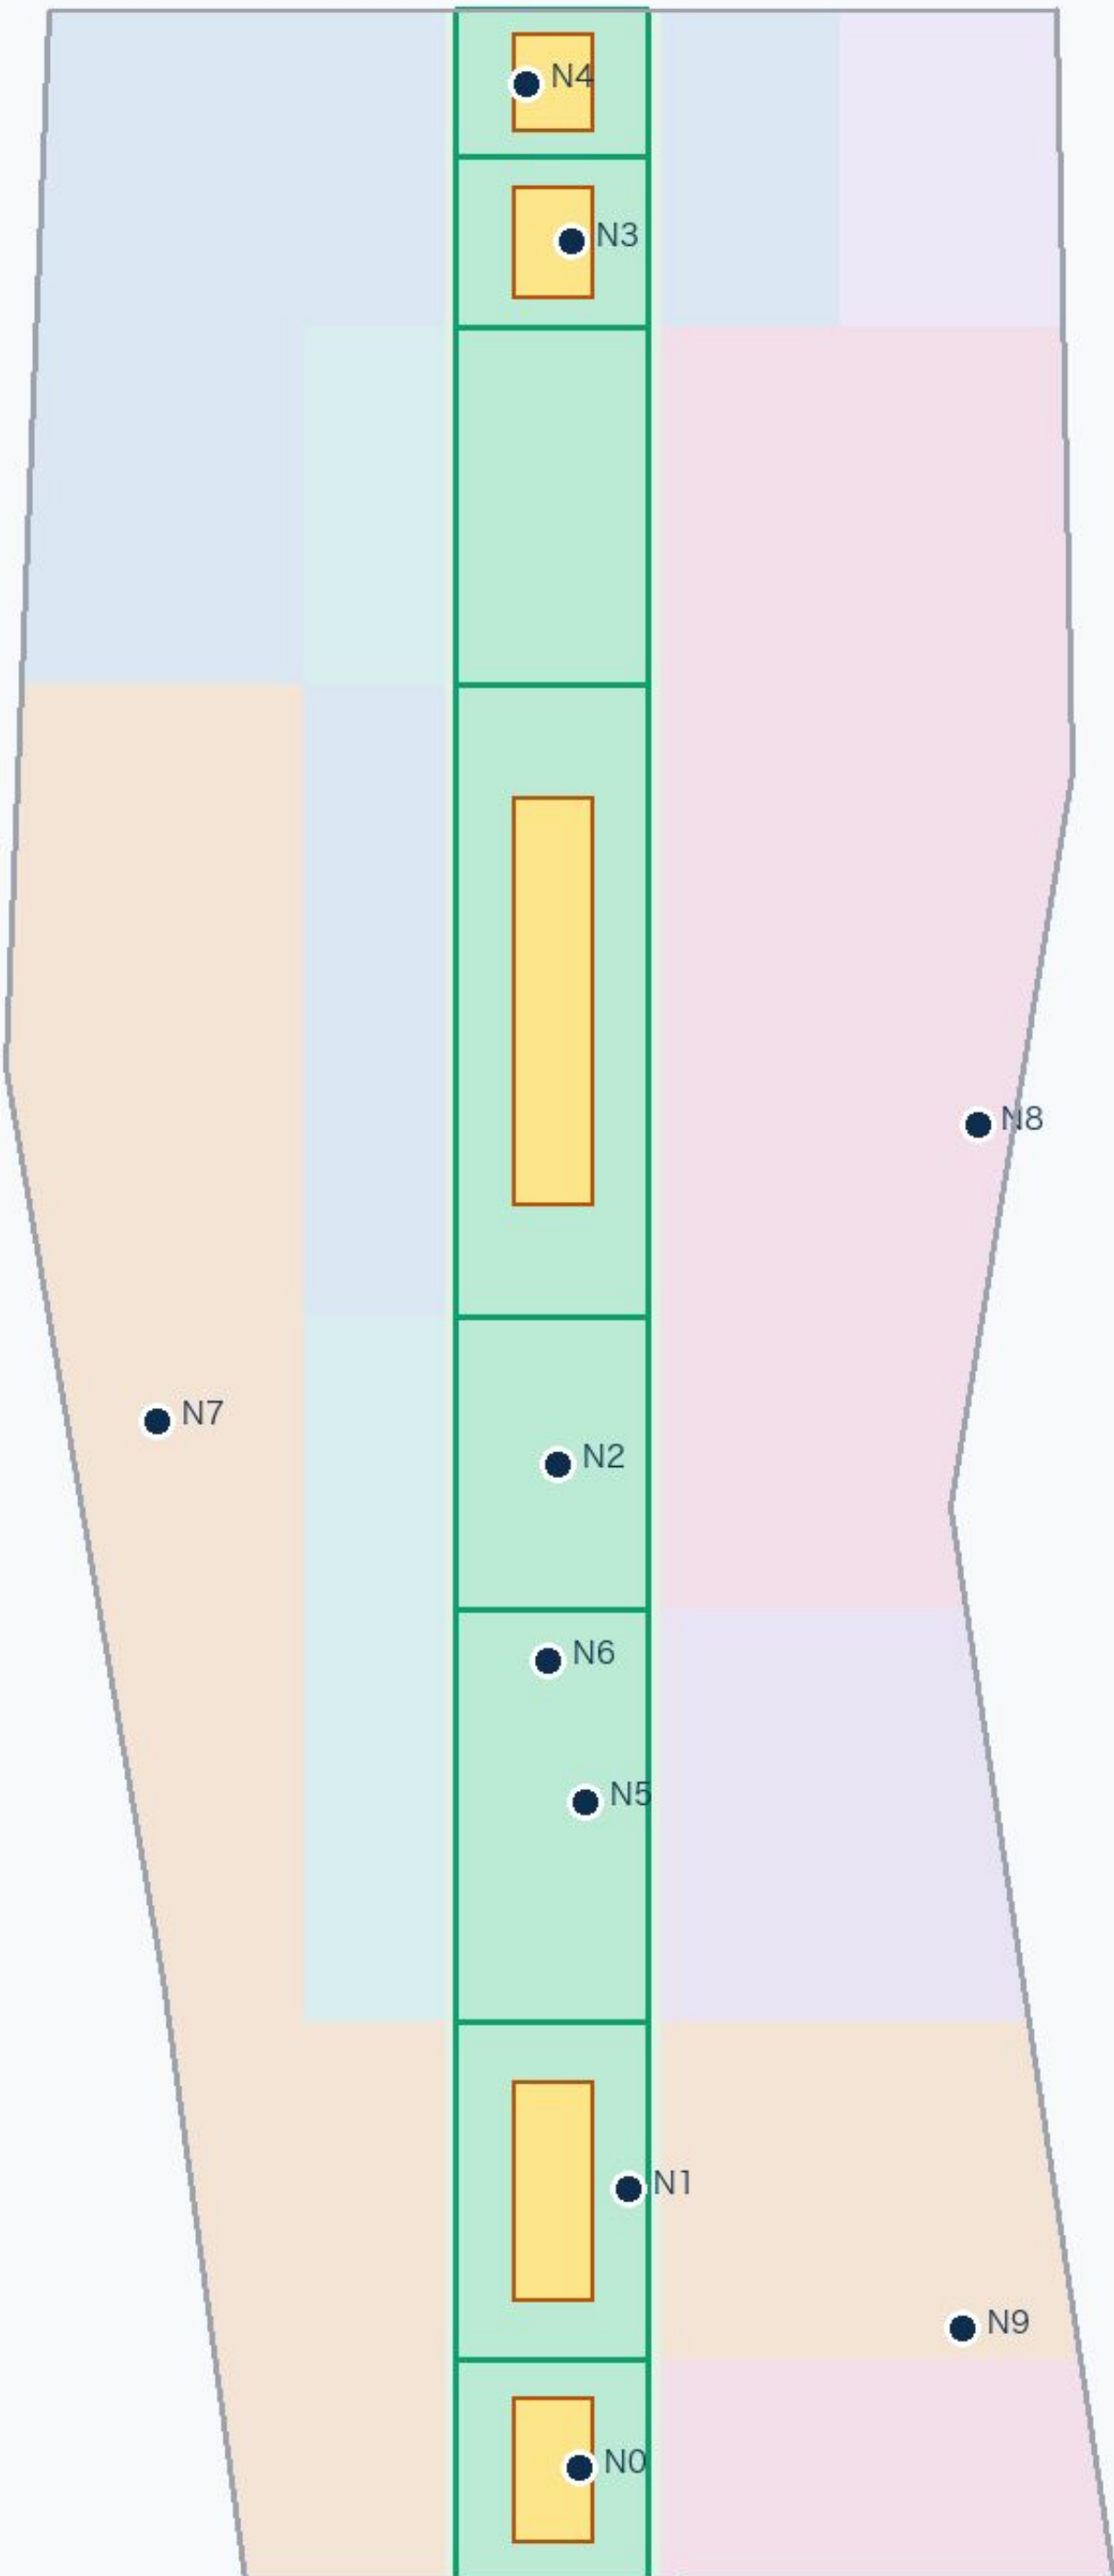

总体设计范围 provisional 边界（虚线）· 文化线绿道为设计主轴

慢行与蓝绿系统

- 文化线绿道（主轴 · greenway）**
南北贯通约 9.7 km, 缝合铁路两侧
- 东西缝合路（secondary/branch）**
9 条连接两翼, 解决断点
- 大钟寺活力环线（loop）**
组织应用站四象限步行
- 绿楔（1402 防护绿地）**
16 m 宽, 主轴向两翼渗透
- 站点广场（1403）**
五处车站节点, 承载 AI 场景与活动

AI 场景节点（N0-N9）

N0 北门户 · AI接入

N2 原点站 · 开源发布厅

N4 南门户 · 国际交往

N6 开源成果展示廊

N8 场景翼 · 机器人配送

N1 加速站 · 算力信号塔

N3 应用站 · 智能生活客厅

N5 COMMIT · 荣誉墙

N7 服务翼 · 资本路演

N9 测试场 · 自主模型

指标

路网总长

20,897.508 m

sum(line_length(road_centerlines))
geometry/roads.geojson

road

绿地率

19.9% ratio

green_space_area_sqm / site_area_sqm
geometry/green_space.geojson

公共空间比例

3.2% ratio

public_space_area_sqm / site_area_sqm
geometry/public_space.geojson


public_sp

数据来源: geometry/roads.geojson / green_space.geojson / public_space.geojson | 路网与节点为概念性设计建议, 道路红线与工程线位须专业复核

京智线 — 三处重点区域详细设计索引

加速站 · 原点站 · 应用站 — 定位 / 空间结构 / 项目抓手 / 风险条件

PROVISIONAL 临时边界 · 非官方红线

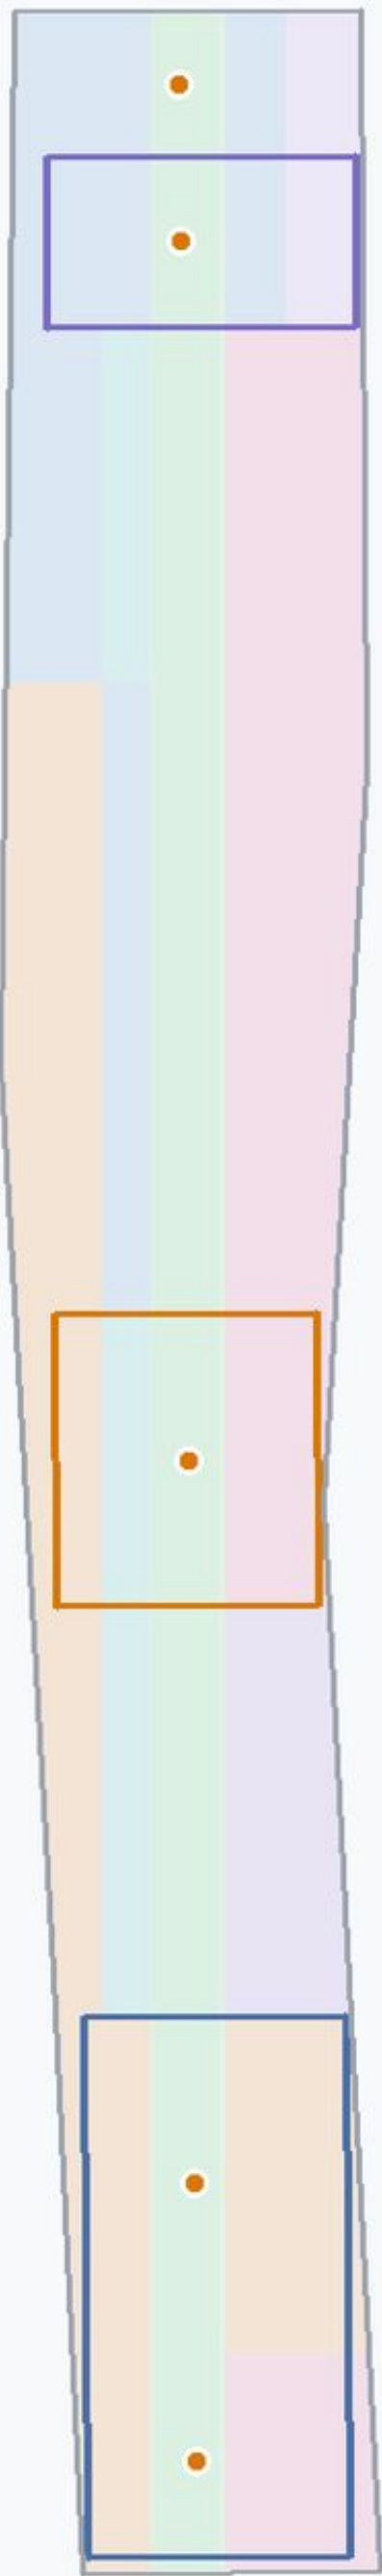

加速站 ACCELERATE

众智园AI自主创新加速区 · 约 192.1 ha

空间结构: 一核两片三环

- 核心: 全栈测试与中试平台
- 西片: 高校科研带衔接
- 东片: 留白用地 · 自主模型测试场/机器人测试走廊

项目抓手: 全栈测试场原型 · 算力信号塔

风险: 测试安全与数据边界须人工复核与审批

原点站 ORIGIN

北京AI原点社区 · 约 104.3 ha

空间结构: 校区-园区-街区三区缝合

- 西侧: 中关村科技服务带（商业服务业）
- 东侧: 近校居住社区与人才公寓
- 中心: 原点站广场 · 清华园遗存叙事

项目抓手: 开源发布厅 · 成果转化街

风险: 校区边界与权属须清权后深化

应用站 APPLY

大钟寺AI产业聚集区 · 约 72.0 ha

空间结构: 一心一环四象限

- 核心: 应用站广场
- 环: 大钟寺活力环线
- 四象限: 智能消费/智能商务/国际路演/内容展示

项目抓手: 轨道站点一体化 · 四象限步行连通

风险: 轨道与市政条件需专业复核

重点区边界为 provisional_constraint（临时粗略），面积以公告值为参考；结论均为概念建议 | 详细证据: geometry/key_areas.geojson

京智线 — 核心指标复算与证据链

全部 known 指标由 geometry 图层经 EPSG:4548 投影复算 · 自检状态与待补资料并列

PROVISIONAL 临时边界 · 非官方红线

总体设计范围 11.412825386 km² geometry/site_boundary.geojson	统筹研究范围 43.609232557999995 km² geometry/provisional_boundaries	重点区域总面积 369.28930049999997 ha geometry/key_areas.geojson
绿地率 19.9 % geometry/green_space/site	公共空间比例 3.2 % geometry/public_space/site	建筑基底总面积 14.7 ha geometry/buildings.geojson
建筑基底数 (概念) 176 栋 geometry/buildings.geojson	路网总长 20.9 km geometry/roads.geojson	用地地块数 61 个 geometry/land_use.geojson
AI测试验证区面积 32.5 ha geometry/ai_test_areas.geojson	分期数量 3 期 geometry/phasing.geojson	重点区数量 3 处 geometry/key_areas.geojson

证据链: GeoJSON → EPSG:4548 复算 → 指标/矩阵 → 图件与展示



数据来源: metrics.json (与 geometry 同源复算, 数值一致) | known 指标全部可复算, unknown 指标为待确认项 | 官方数据发布后须整体复算

任务覆盖: agent.1 命名体系 · agent.2 生态案例(6) · agent.3 场景卡(10, 含3测试) · agent.4 朝圣地标(4) · agent.5 文化叙事 · agent.6 运营体系

合规: compliance_matrix 23 项 · standard_matrix 6 项 · design_depth_matrix 15 项 complete

面积按 EPSG:4548 复算; 指标与 visual/index.html、metrics.json 数值一致; 边界 provisional, 官方数据发布后复算