


空间原型：京张铁路青龙桥“人字形”折返线 → 南北京张绿轴 × 东西小月河蓝绿走廊。

众智站：全栈创新与AI治理（约192.1公顷）
原点站：从0到1的原点生态（约104.3公顷）
钟站：智能原生新业态（约72.0公顷）

两翼：中关村科技服务翼（要素与资本） · 小月河场景赋能翼（场景与活力）

边界状态：PROV-SITE-001 临时粗略边界（非官方红线）；官方红线发布后整体复算。

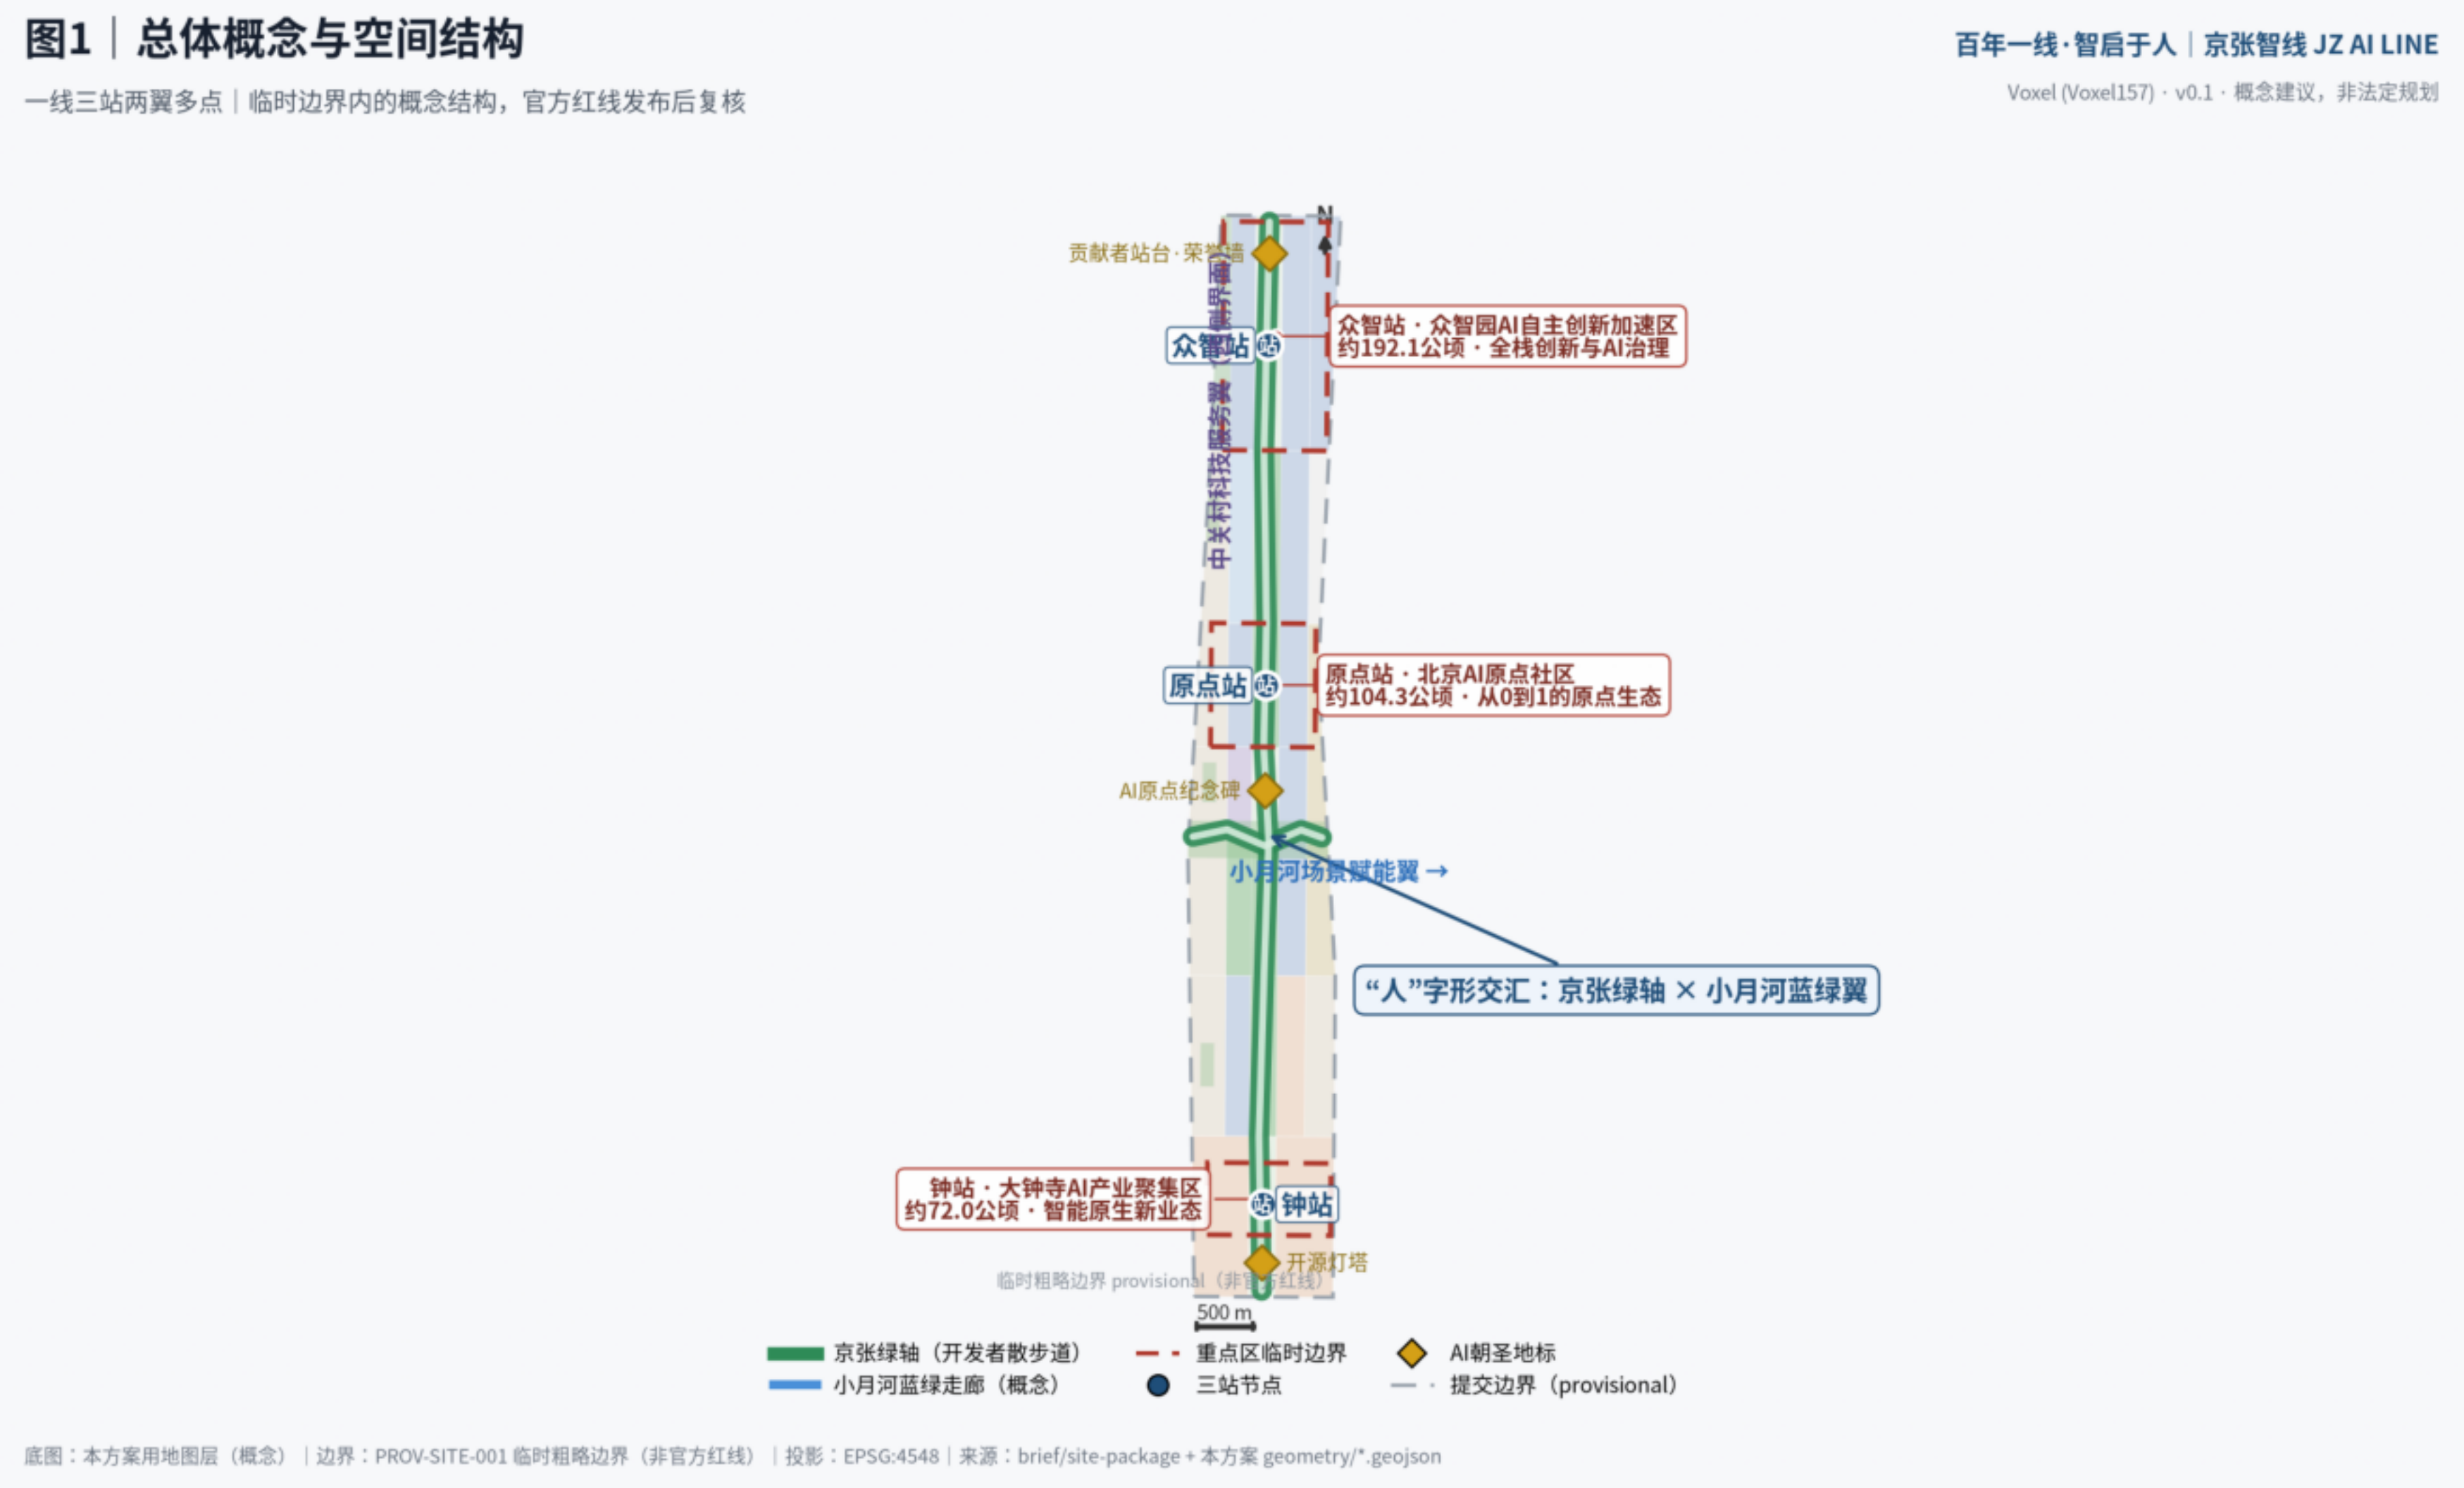


用地构成 (EPSG:4548复算)

- 0802 科研：325.0 公顷 (28.5%)
- 0701 城镇住宅：214.8 公顷 (18.8%)
- 05 商业服务业：184.8 公顷 (16.2%)
- 1401 公园绿地：154.6 公顷 (13.5%)
- 1403 广场：104.9 公顷 (9.2%)
- 0702 社区服务：53.8 公顷 (4.7%)
- 16 留白：50.4 公顷 (4.4%)
- 0804 教育：34.5 公顷 (3.0%)
- 0803 文化：18.5 公顷 (1.6%)

锚点建筑：18处，基底 187 公顷
战略留白：50.4 公顷（触发条件清单管理）

拆改留概念方向：留字当头、改字为主、拆字极慎、建字精准（无现状底数，不落地块）。
容积率/高度/密度：unknown，待控规条件。

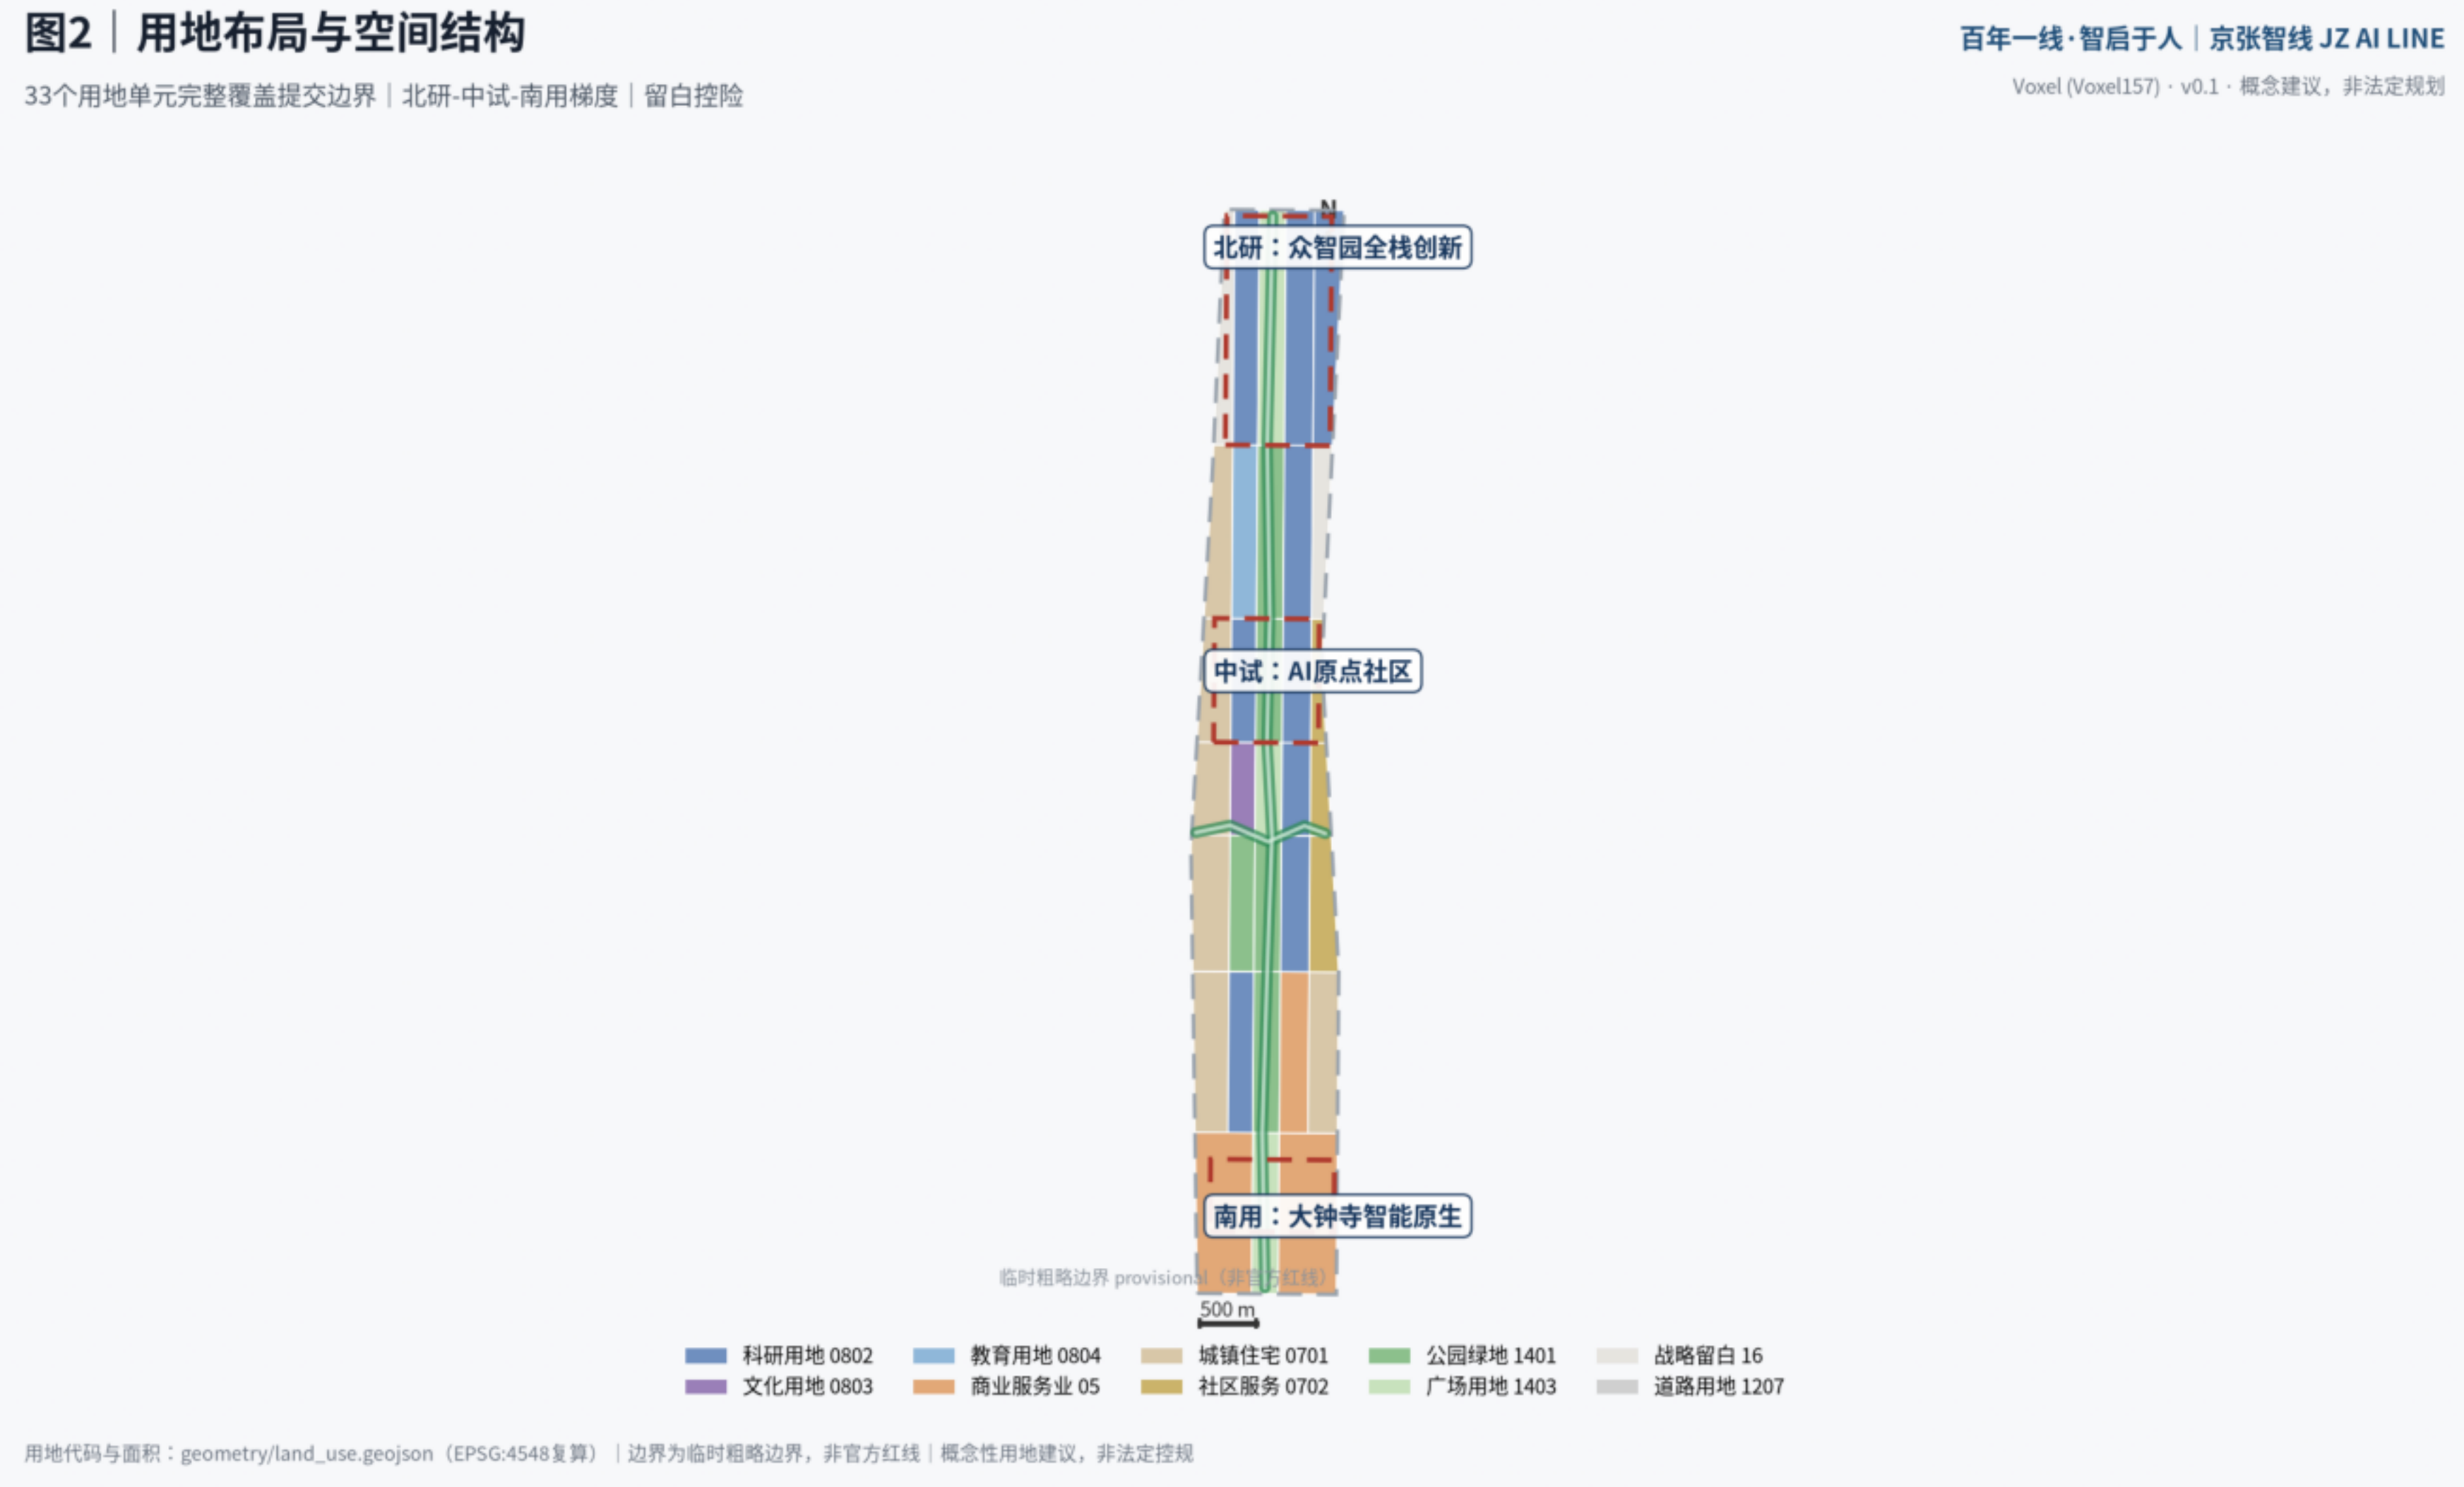

绿道长度：10.8 km（开发者散步道 + 小月河慢行带）
道路面积：58.7 万㎡（占比 5.1%，中心线缓冲近似）
绿地率：20.5% | 公共空间率：12.8%

公共空间节点：原点广场 · 钟鸣广场 · 贡献者广场 · 人字形广场 · 三处站前广场 · 开发者散步道线性空间


轨道：大钟寺既有站接驳枢纽；原点站/众智站为概念接驳节点（线位不作结论）。
小月河线位为公开地名推断的概念蓝线（analysis_helper），以官方蓝线为准。


图4 | 交通慢行与蓝绿公共空间复合系统

一轴两道慢行走廊 + 三站接驳 + 八处公共空间节点 | 线位均为概念建议

百年一线·智启于人 | 京张智线 JZ AI LINE

Voxel (Voxel157) · v0.1 · 概念建议，非法定规划

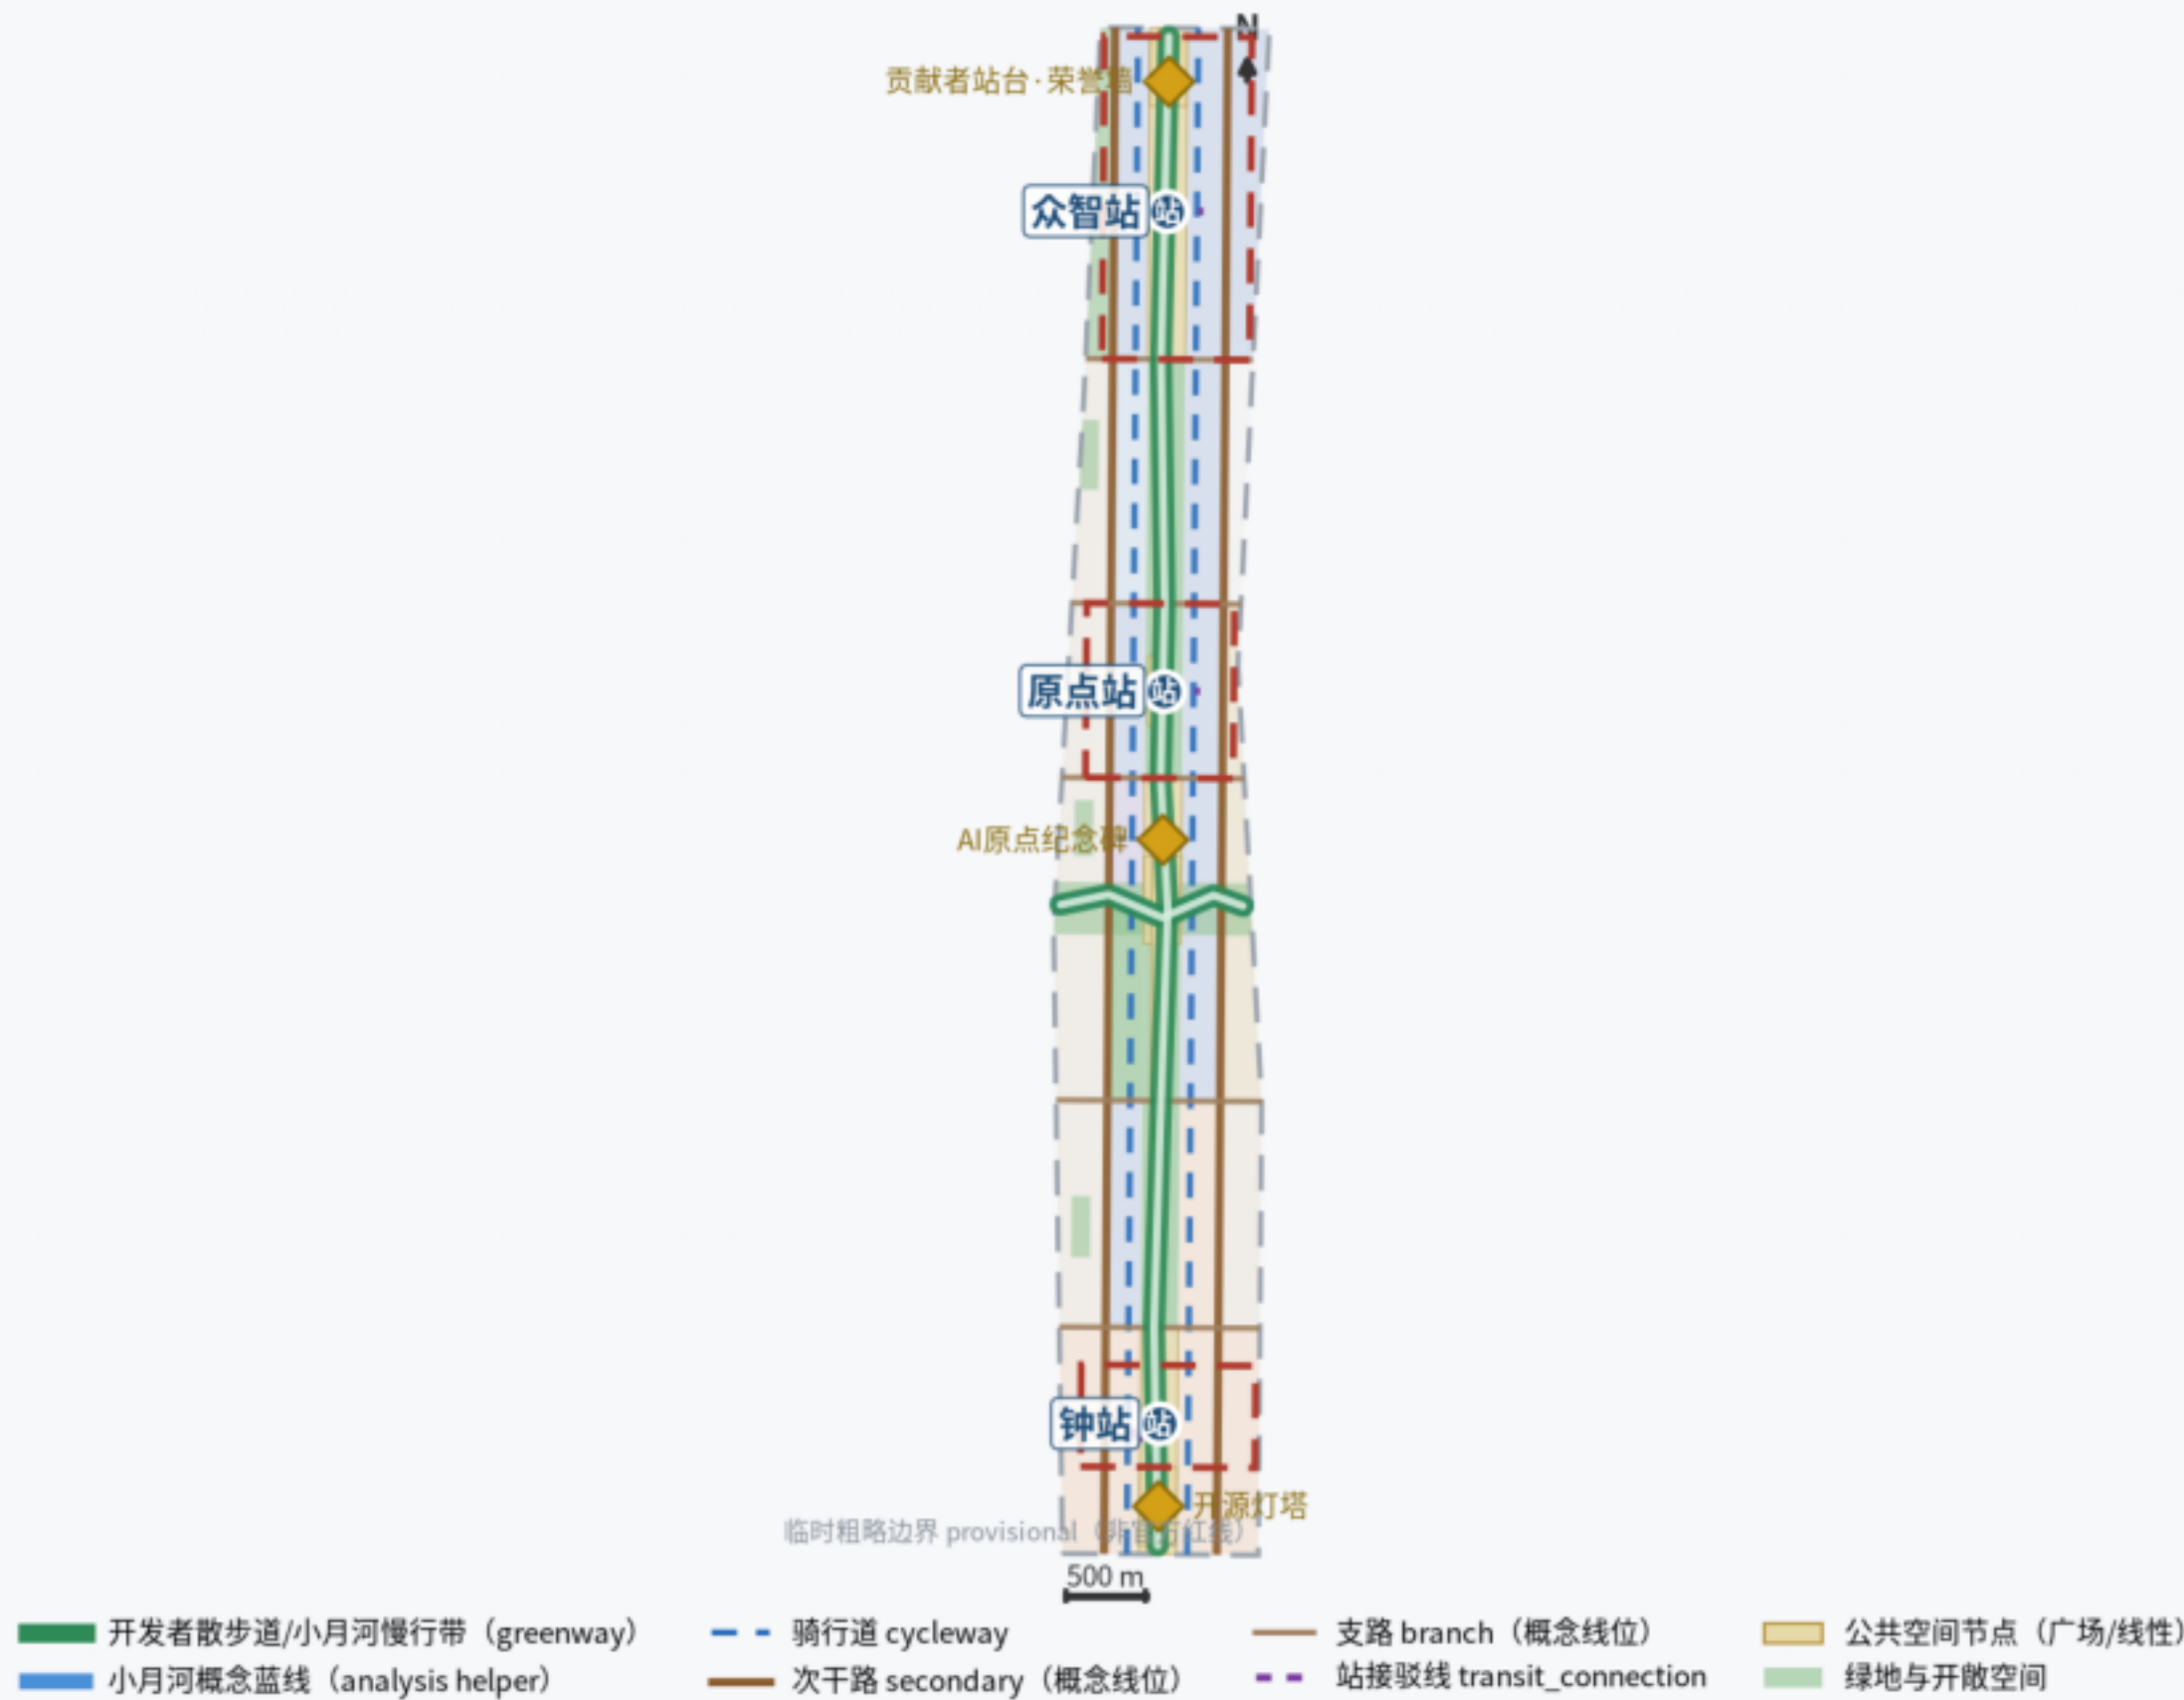

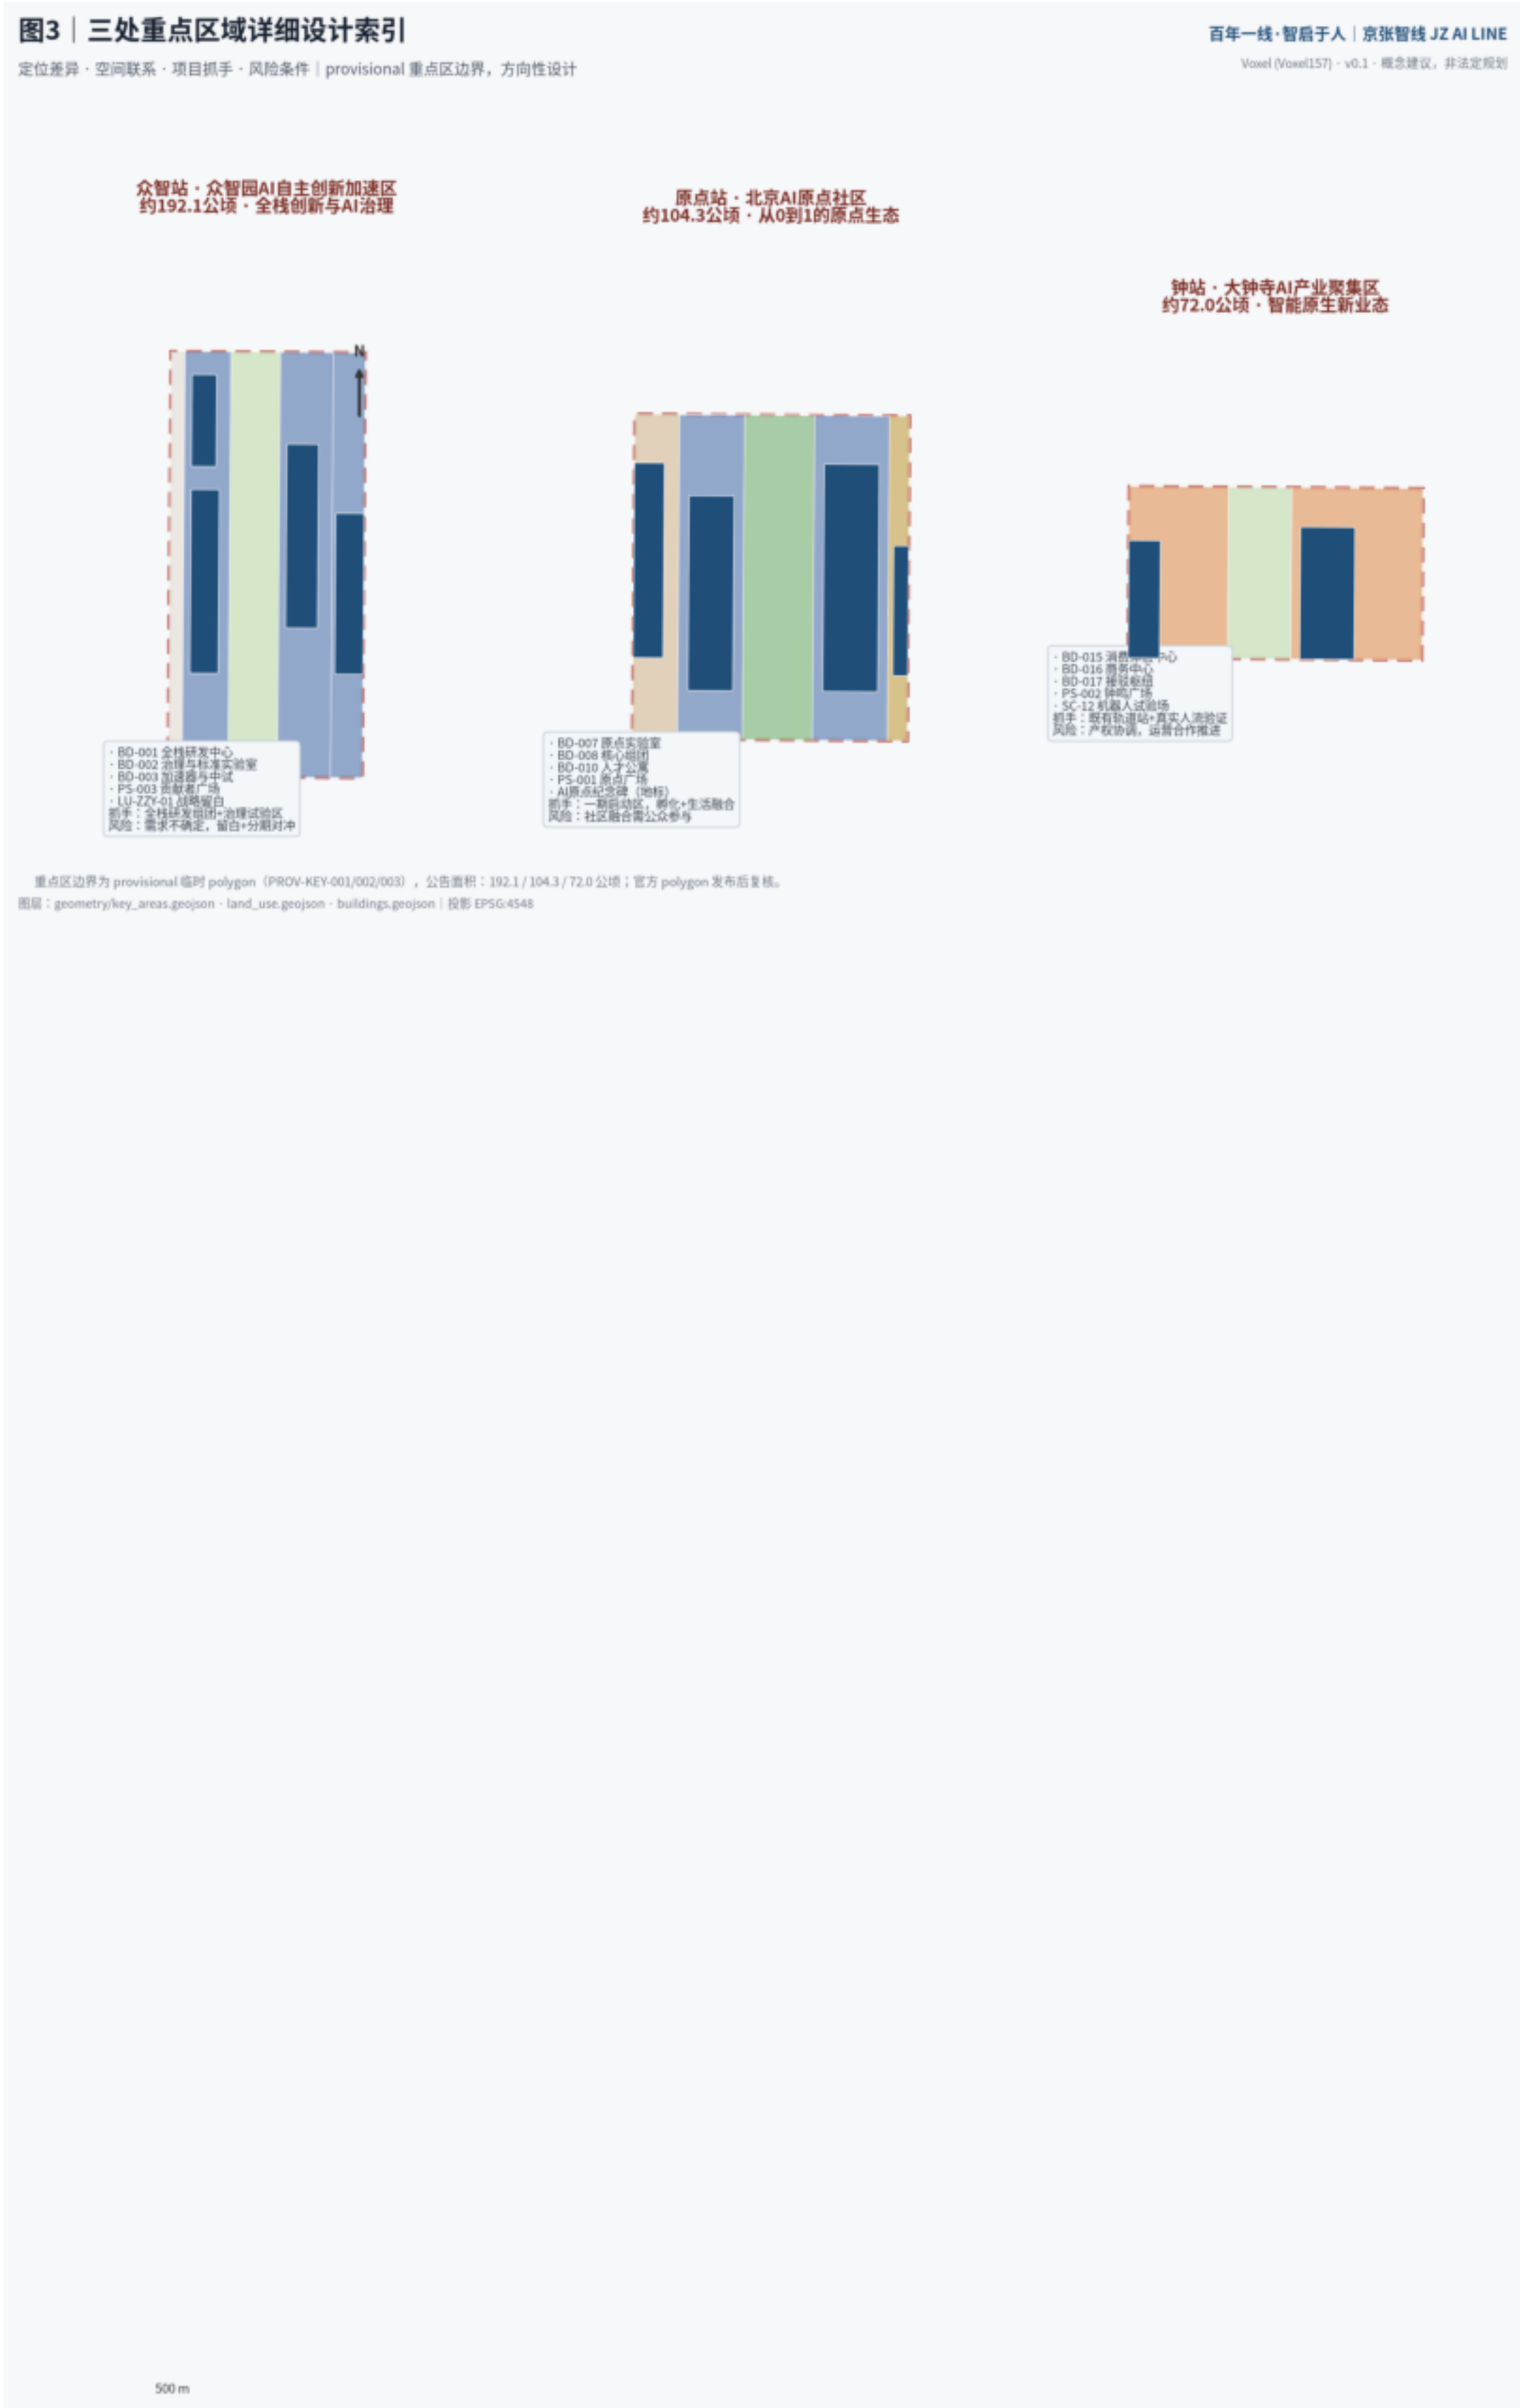

三处重点区 (provisional)
众智园 192.1ha · AI原点社区 104.3ha · 大钟寺 72.0ha

AI场景卡: 12张 (★产业测试验证3张)
全部设置隐私边界与人工复核机制

更新项目: 12项 × 概念分期三期
一期 380 ha · 二期 369 ha · 三期 392 ha

AI朝圣地标: AI原点纪念碑 · 贡献者站台荣誉墙 · 开源灯塔

任务覆盖: 公告17项 + agent 6项 = 23项全覆盖


图5 | 核心指标复算与证据链

EPSG:4548 投影复算 | 公式与来源文件逐项可查 | 控规五要素待确认

百年一线·智启于人 | 京张智线 JZ AI LINE

Voxel (Voxel157) · v0.1 · 概念建议，非法定规划

用地构成 (复算总面积 1141 万㎡, 完整覆盖提交边界)

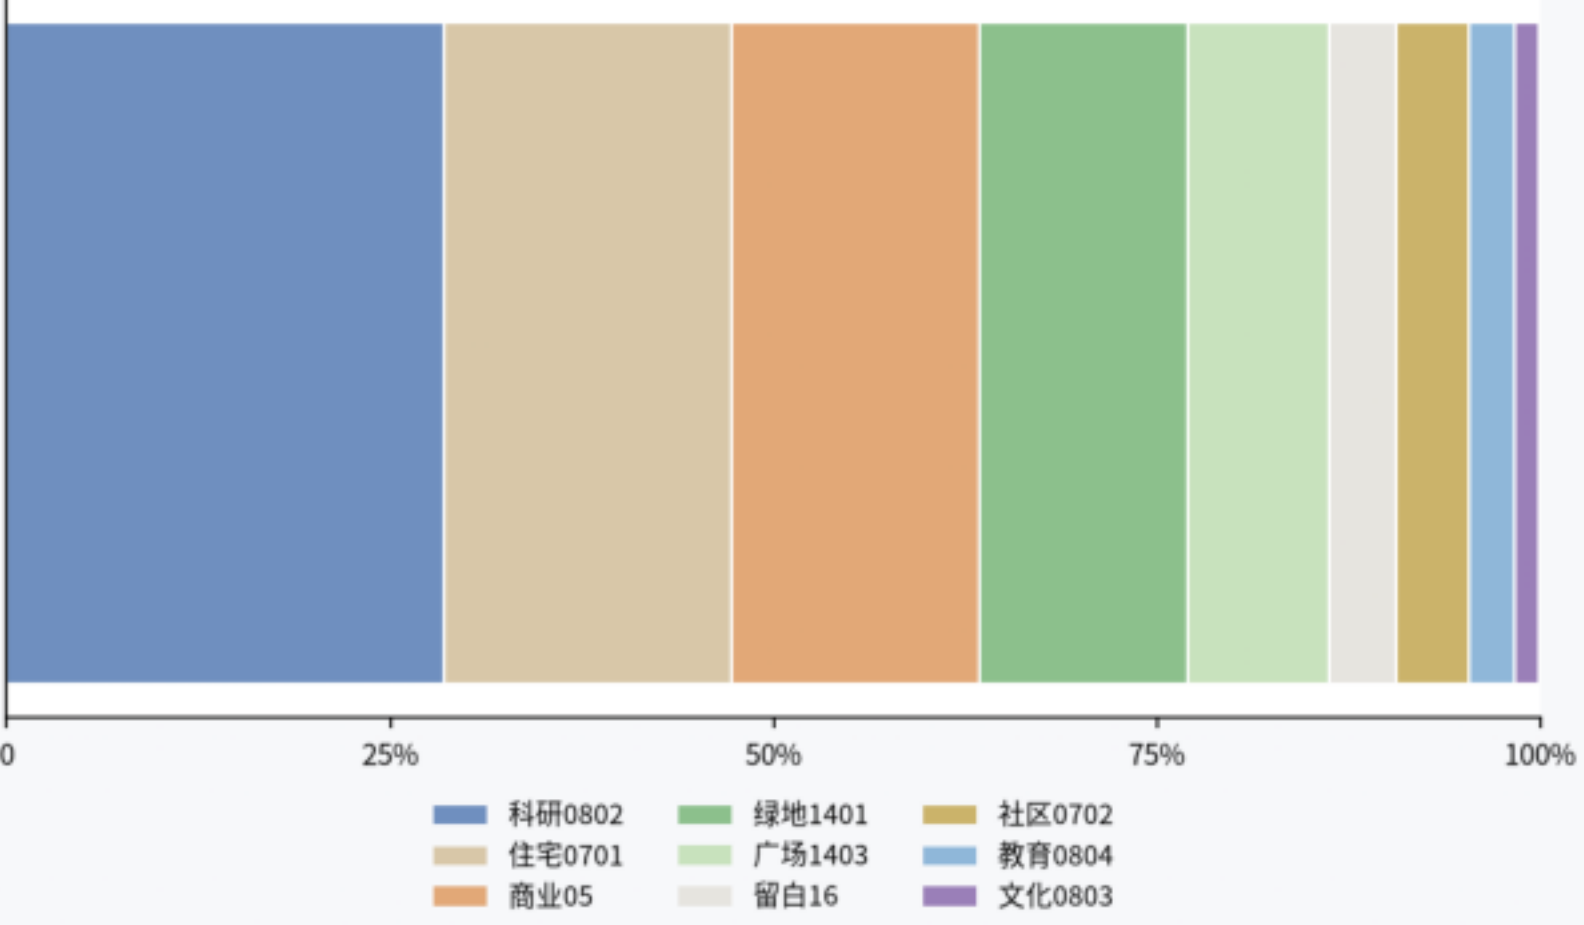

场地面积 1141 万㎡ site_area_sqm · 临时边界复算	绿地率 20.5% green_ratio · 绿地234公顷	公共空间率 12.8% public_space_ratio · 147公顷	锚点建筑密度 16.4% building_density · 18处锚点
道路占比 5.1% road_ratio · 中心线缓冲还原	绿道长度 10.8 km greenway_length_m · 两渠greenway	重点区 3处 · 369公顷 key_area_count · provisional	场景卡/地标 12张 · 3座 scenario_card_count · ai_landmark_count



待确认控规条件 (metrics.json 标记 unknown, 不作编造)

容积率 floor_area_ratio · 建筑高度 building_height_m · 建筑总规模 total_floor_area_sqm —— 官方控规条件发布后, 几何、指标、图纸与HTML整体复算 [metric:floor_area_ratio]

自检状态: BOUNDARY_TRUST / KEY_AREAS_TRUST / LAND_USE_TOPOLOGY / VISUAL_STATIC / PROFESSIONAL_EVIDENCE — 见 self_check.json