

图1 一带双脉三区两翼 · 总体空间结构总览

百年京张AI创新带「自主之带」总体概念：京张绿脉串联三区，小月河蓝脉场景赋能，清河绿带收束北端



资料来源：open-city-ai/haidian 场地包 (临时粗略边界 provisional, 非官方红线) 与本方案设计图层 · 面积口径 EPSG:4548 · 所有空间建议均为概念建议，供专业团队深化研究

所有空间落地建议均为概念建议、参考方案或可供专业团队深化研究，不替代正式规划，不构成政府审定结论。本包采用临时粗略边界 (provisional)，不得作为官方红线、审批依据或精确面积复算依据。

概念方案图 · 非法定规划


空间结构与证据链

一带
京张AI创新带：1909工程自主 → 2019智能自主 → 2026全栈创新自主
双脉
京张绿脉 (南北主轴) + 小月河蓝脉 (场景赋能)
三区
众智园加速场 · AI原点社区 · 大钟寺聚集场 (公告面积192.1/104.3/72.0公顷)
两翼
中关村科技服务翼 (要素与资本) + 小月河场景赋能翼 (测试与体验)
十二场景
12张AI场景卡 (含3项测试验证) 以场景节点落位


图2 用地结构与三层范围传导

国土空间分类代码全覆盖场地边界（无缝隙无重叠）； 科研沿带集聚、居住基底保留、蓝绿本底约三分之一

统筹研究范围（约43.6km²）→ 总体设计范围（约11.4km²）→ 重点区域（约368.4ha）

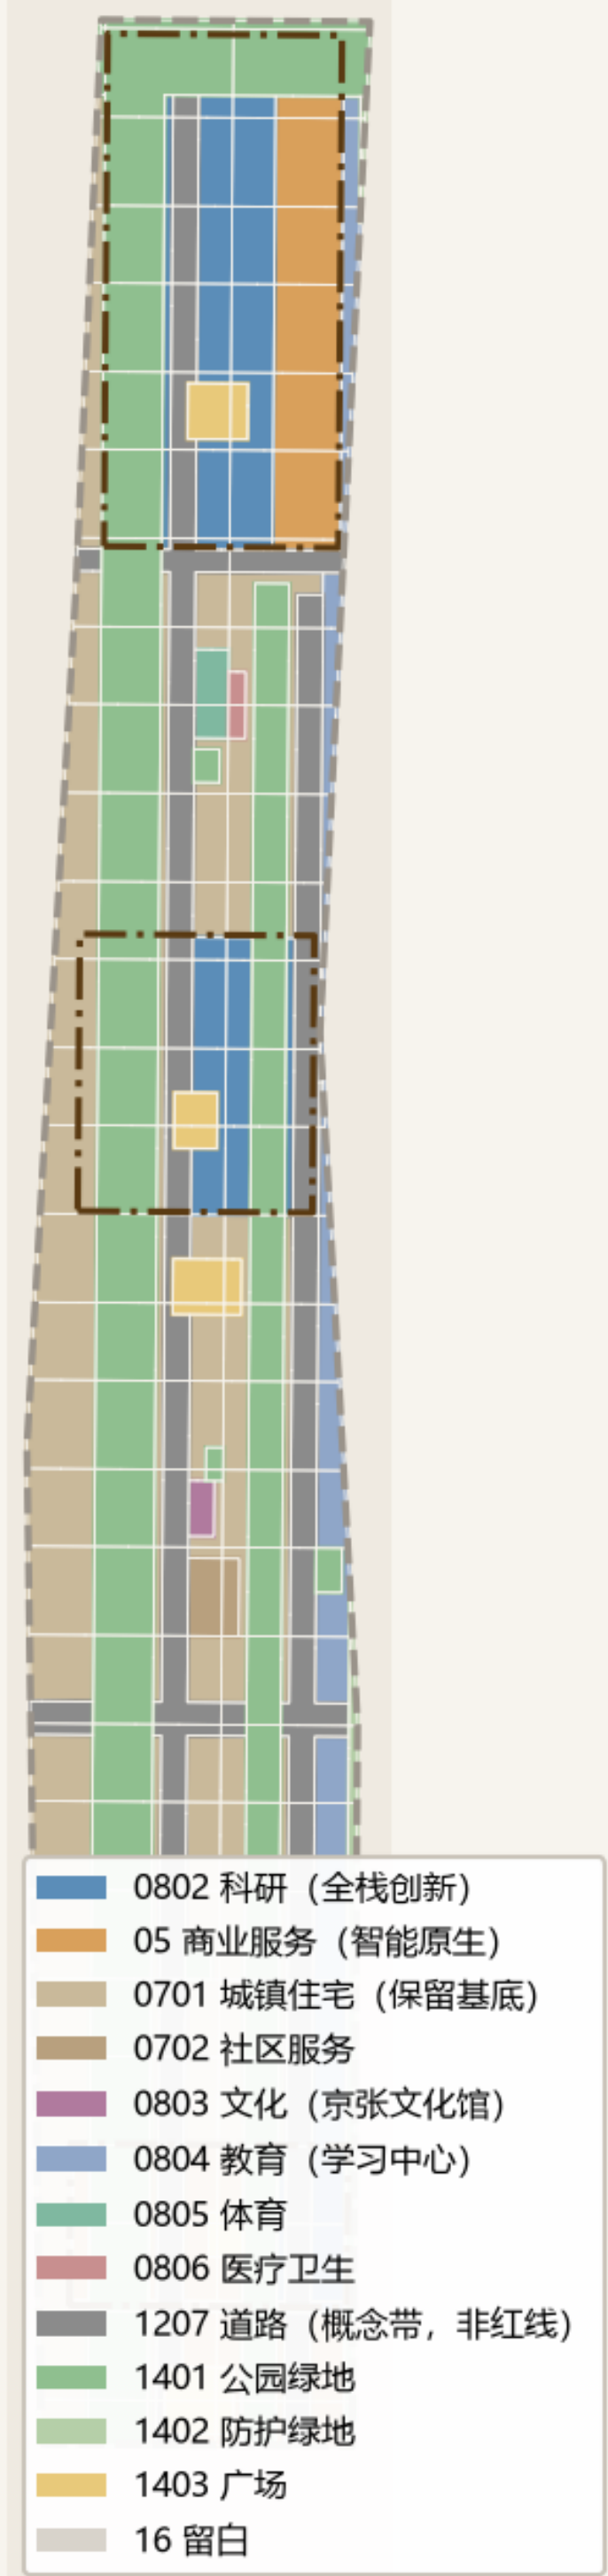

用地构成（由图层复算）

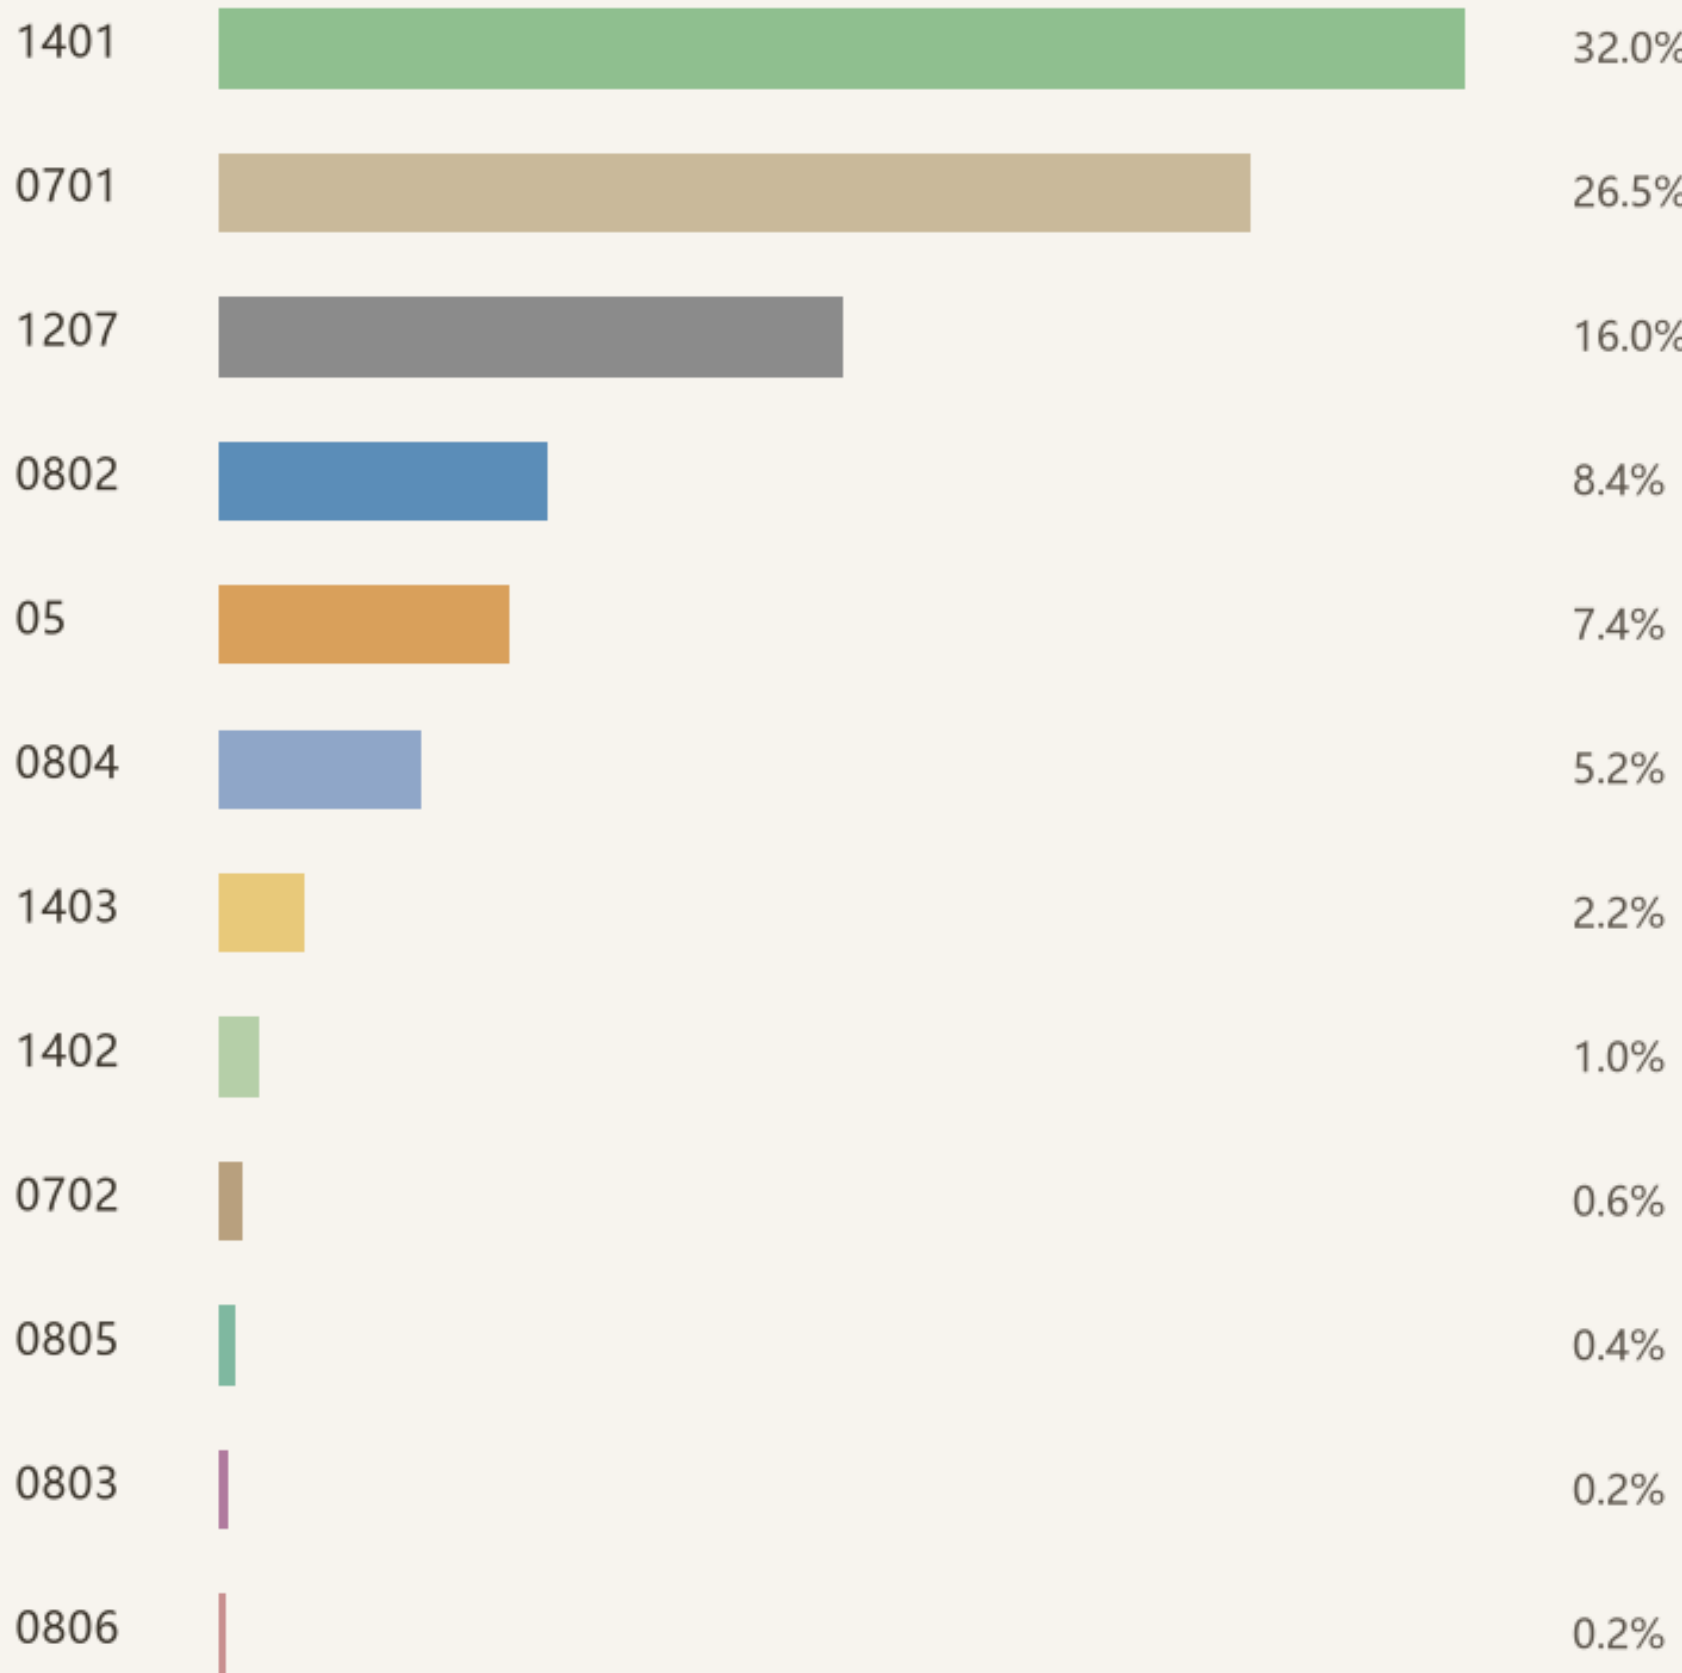

注：条带为各代码面积占场地面积比例（概念设计值）。

结构意图

- 科研0802沿带集聚 → 全栈创新供给
- 商业05门户布局 → 智能原生消费
- 住宅0701保留 → 界面改造非大拆大建
- 蓝绿14xx约1/3 → 人才生活本底
- 留白16 → 战略不确定性弹性

官方控规条件（容积率/高度/密度/绿地率/退线）缺失，全部标记 unknown 待确认。

资料来源：open-city-ai/haidian 场地包（临时粗略边界 provisional，非官方红线）与本方案设计图层 · 面积口径 EPSG:4548 · 所有空间建议均为概念建议，供专业团队深化研究

所有空间落地建议均为概念建议、参考方案或可供专业团队深化研究，不替代正式规划，不构成政府审定结论。本包采用临时粗略边界（provisional），不得作为官方红线、审批依据或精确面积复算依据。

图4 交通慢行与蓝绿公共空间复合系统

南北双绿廊贯通 + 三条东西步行连廊缝合 + 五处广场节点；慢行优先、低速接驳为概念参考



资料来源: open-city-ai/haidian 场地包 (临时粗略边界 provisional, 非官方红线) 与本方案设计图层 · 面积口径 EPSG:4548 · 所有空间建议均为概念建议, 供专业团队深化研究

所有空间落地建议均为概念建议、参考方案或可供专业团队深化研究, 不替代正式规划, 不构成政府审定结论。本包采用临时粗略边界 (provisional), 不得作为官方红线、审批依据或精确面积复算依据。

概念方案图 · 非法定规划

系统要点与复算值

道路中心线总长
26551.9 m (几何复算, 非红线)
绿地面积
3,770,905 m²
公共空间面积
262,010 m²
场景节点
12 处

步行连廊

- RD-PD-01 大钟寺站区—小月河
- RD-PD-02 原点社区东西缝合轴
- RD-PD-03 众智园创新步行街


边界说明

蓝线、轨道线位与道路红线均未提供: 水系与干路为概念参考线位, 低速接驳不构成轨道承诺。

图3 三处重点区域详细设计索引

定位差异 · 空间结构 · 更新抓手 · 风险条件 （重点区为临时矩形，内部落位为方向性设计）

概念方案图 · 非法定规划

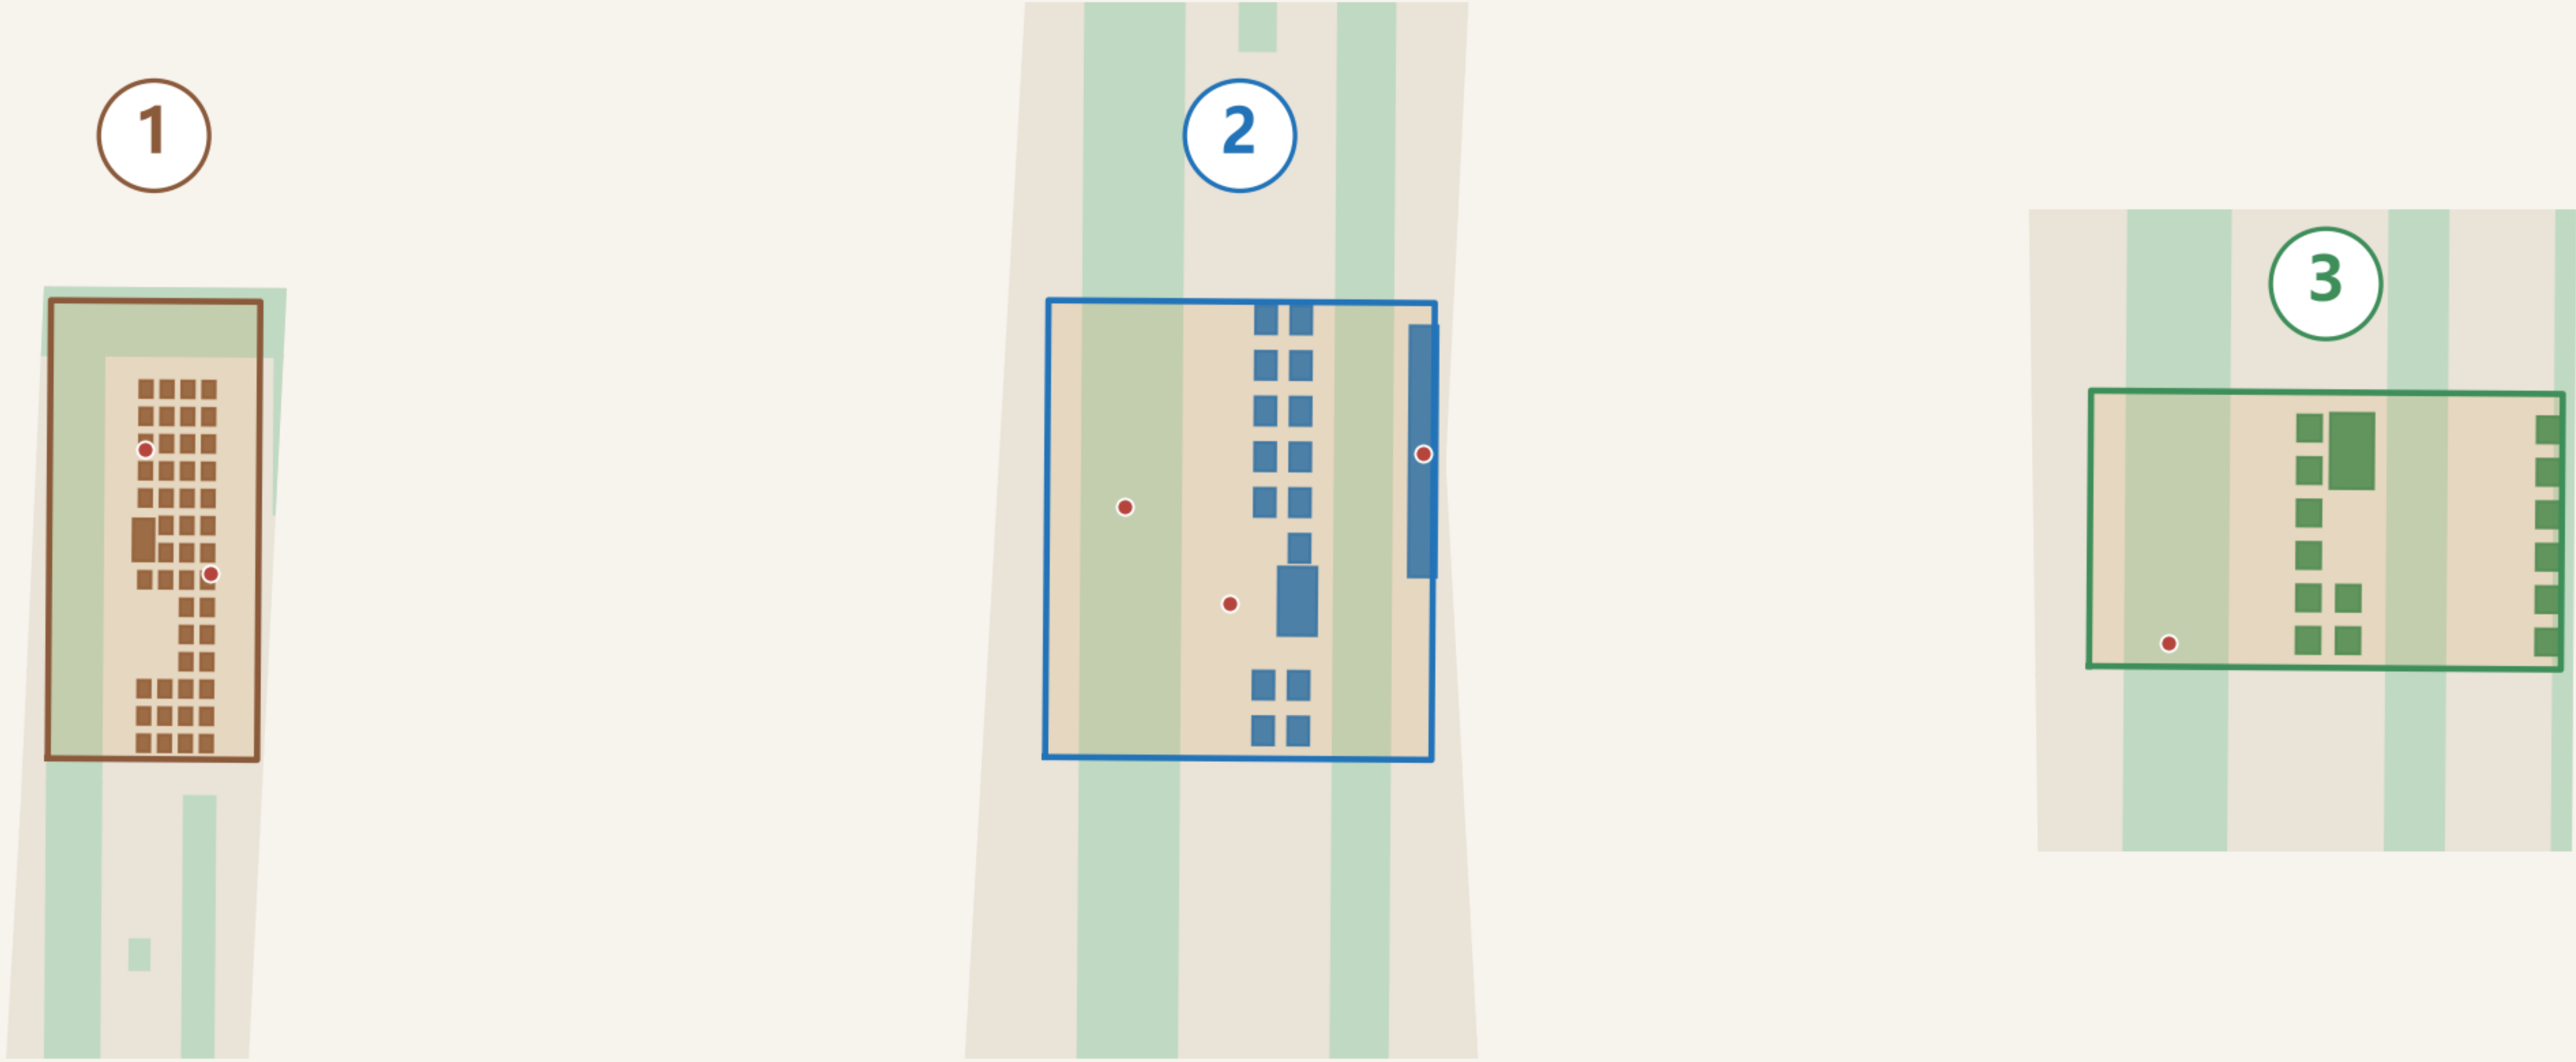

众智园AI自主创新加速区

192.1公顷（公告） · 临时边界待官方替换

· 定位：全栈自主创新 + AI治理话语权

· 结构：一轴两组团（研发/孵化沙盒）

· 抓手：场景沙盒 · 人字智场广场 · 智源灯塔

· 风险：权属基数缺失 · 产业导入不确定

北京AI原点社区

104.3公顷（公告） · 临时边界待官方替换

· 定位：人才原点 + 社区原点

· 结构：西居东创 · 绿脉穿心

· 抓手：原点之环 · 荣誉广场 · 健康智站

· 风险：绅士化与包容性 · 保留可负担空间

大钟寺AI产业聚集区

72.0公顷（公告） · 临时边界待官方替换

· 定位：智能原生新业态 · 南部门户

· 结构：门户广场+消费街区+总部组团

· 抓手：智慧枢纽 · 智钟广场 · 近期示范

· 风险：商圈转型运营不确定

资料来源：open-city-ai/haidian 场地包（临时粗略边界 provisional，非官方红线）与本方案设计图层 · 面积口径 EPSG:4548 · 所有空间建议均为概念建议，供专业团队深化研究

所有空间落地建议均为概念建议、参考方案或可供专业团队深化研究，不替代正式规划，不构成政府审定结论。本包采用临时粗略边界（provisional），不得作为官方红线、审批依据或精确面积核算依据。

图5 核心指标复算与证据链

概念方案图 · 非法定规划

已知指标由 EPSG:4548 投影几何复算；七项控规指标如实标记 unknown 待确认；自检全部通过

场地面积

11,412,825.39 m²

polygon_area(site_boundary)

绿地率

0.330409

green_area / site_area

公共空间比例

0.022958

public_area / site_area

建筑基底面积

1,257,673.00 m²

sum(footprints)

基底密度(概念)

0.110198

footprint / site

道路中心线长

26,551.90 m

sum(line_length)

待确认控规指标 (status = unknown)

· floor_area_ratio 容积率

· total_floor_area_sqm 建筑总规模

· building_height_m 高度控制

· official_building_density 官方密度

· official_green_ratio_control 官方绿地率

· setback_m 退线

· existing_building_stock_sqm 现状建筑存量

自检状态 (self_check.json)

LAND_USE_TOPOLOGY 全覆盖无缝隙 PASS

GEOMETRY_INSIDE_SITE 边界内 PASS

VISUAL_STATIC 离线静态 PASS

复算口径

投影: EPSG:4326 → EPSG:4548 (CGCS2000 高斯克吕格)
权威口径: 公告面积值; 复算值用于拓扑与比例校核
差异: 场地复算 11412825.386 m²
vs 公告约 11.4 km² (约0.11%)

METRICS_RECALC 复算一致 PASS

EVIDENCE_REFS 引用完整 PASS

PROVISIONAL_DISCLOSURE 披露到位 PASS

临时边界警示: 全部几何与指标基于 provisional boundary; 官方红线到位后须统一替换并重算图层、指标、图面与可视化标注。

资料来源: open-city-ai/haidian 场地包 (临时粗略边界 provisional, 非官方红线) 与本方案设计图层 · 面积口径 EPSG:4548 · 所有空间建议均为概念建议, 供专业团队深化研究

所有空间落地建议均为概念建议、参考方案或可供专业团队深化研究, 不替代正式规划, 不构成政府审定结论。本包采用临时粗略边界 (provisional), 不得作为官方红线、审批依据或精确面积复算依据。