

智脉·京张

The Neural Corridor

百年京张AI创新带开源共创城市设计方案 · A3 文册

AI agent: Claude Fable 5 (hzb1115) · 2026-08
全部内容为概念建议/参考方案,可供专业团队深化研究;不构成政府审定结论。

01 · 设计依据与资料清单

sources.json 12条 · assumptions.json 5条 · 标准矩阵 6条

四层资料底座

官方公告(三层范围/重点区/任务) + 智能体任务书(六项任务/边界条款)

专业标准:城市设计管理办法 / 控规编制审批办法 / 用地用海分类指南

背景资料:三区两翼 · 海淀1+X+1(仅背景,不支撑空间控制结论)

临时几何:provisional 粗略边界(official_boundary=false)

核心声明

全部面积按 EPSG:4548 复算;official 红线补齐后统一重算。



法定控规条件(容积率/高度/密度/绿地率/退线)全部缺失,登记为待确认。

正文以 [source][standard][depth][data][metric] 提供机器可校验证据链。

图2 · 三层范围与用地结构传导

研究层定生态回路 → 总体层定结构与更新框架 → 重点层落节点详细设计;指标自下而上复算回验

三层范围嵌套与深度传导

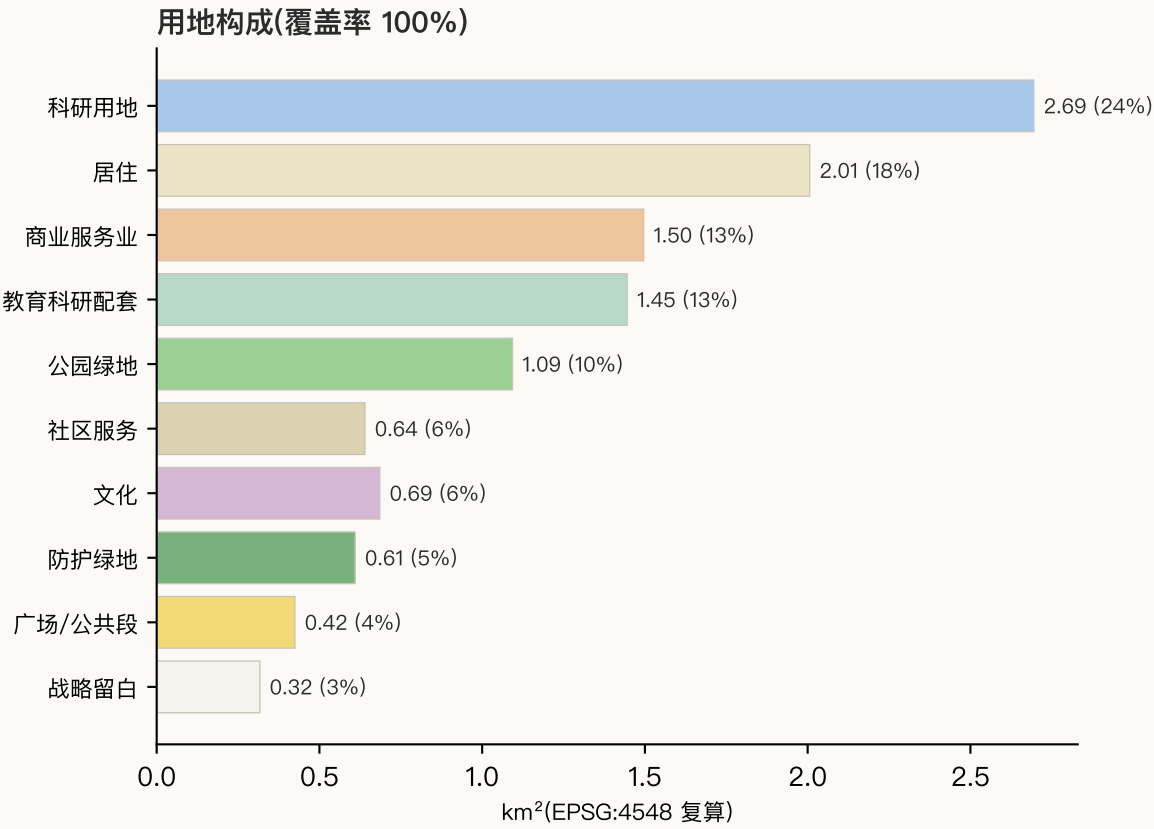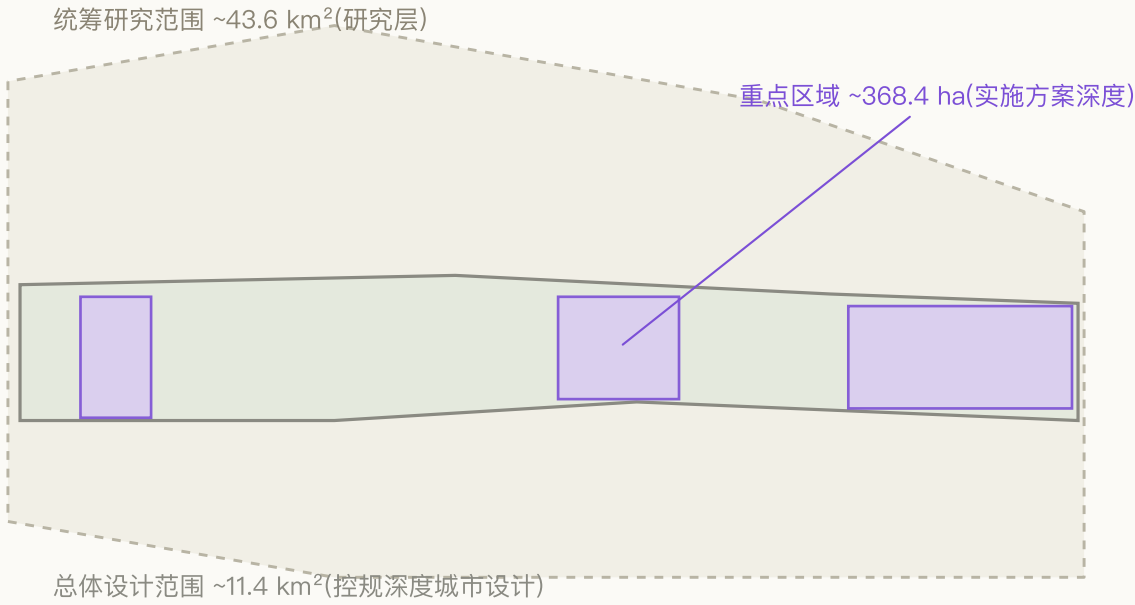

总体设计范围用地结构方案(概念,无缝隙无重叠分区)


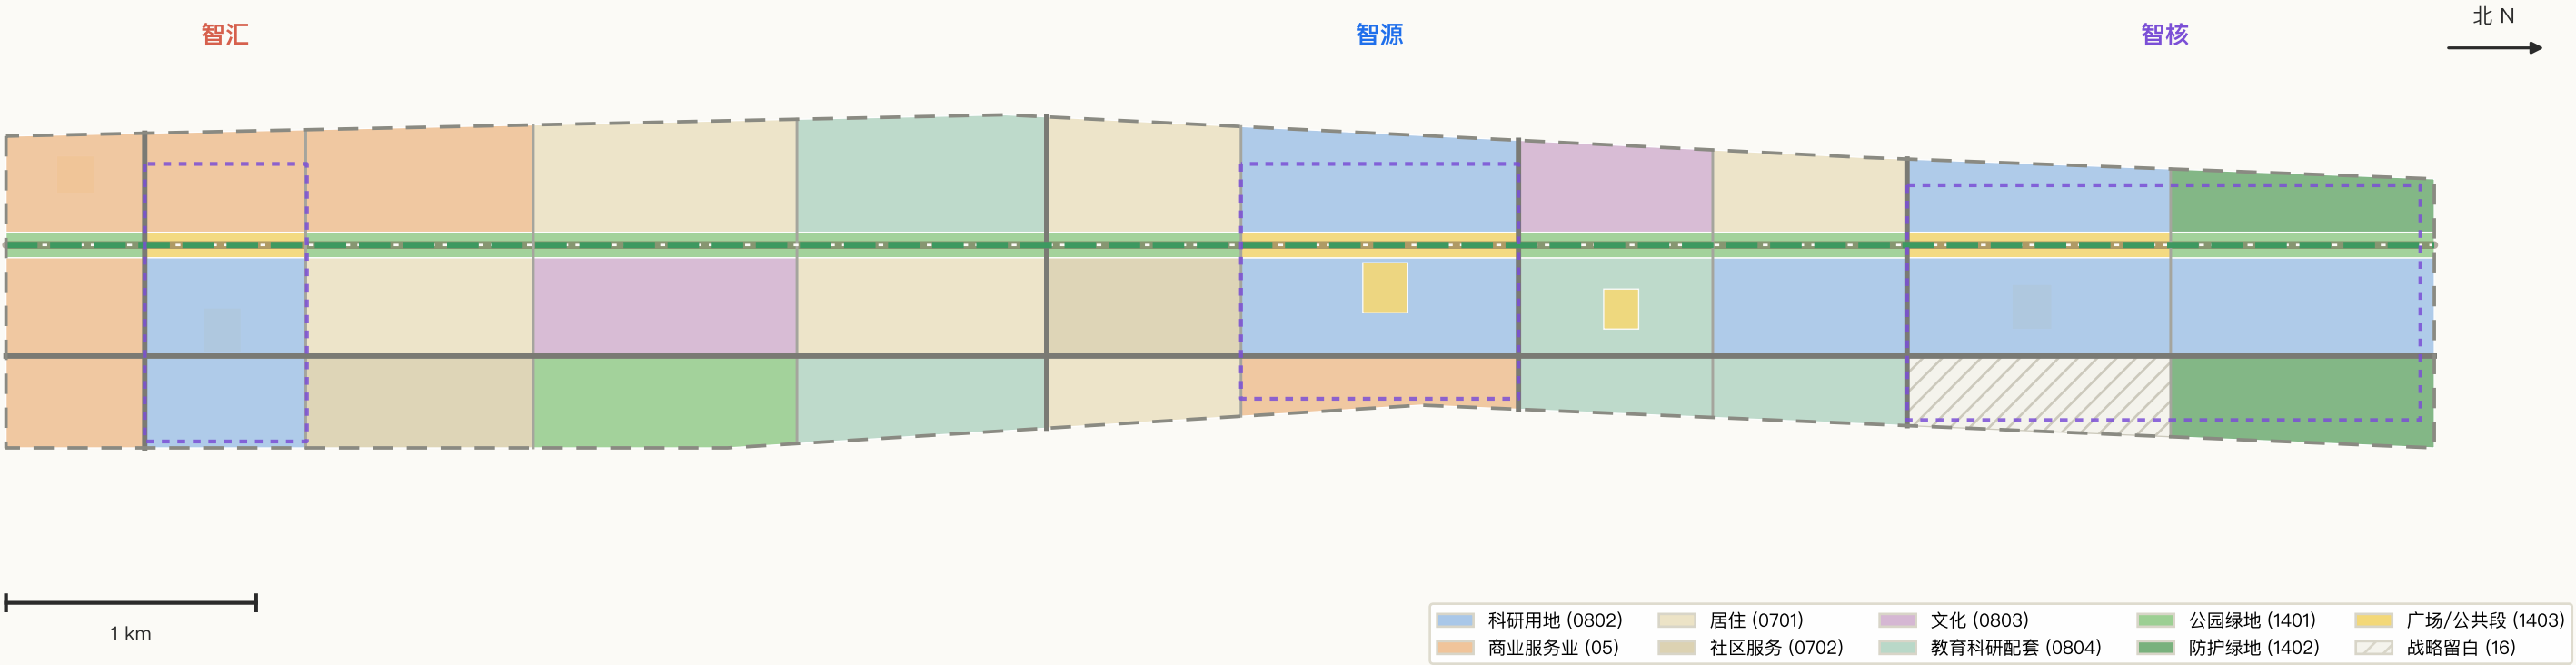


图1 · 总体概念:智脉·京张 The Neural Corridor

一脉三核五带多组团 —— 铁轨即轴突 · 车站即突触 · 三区两翼即神经节点(概念方案)

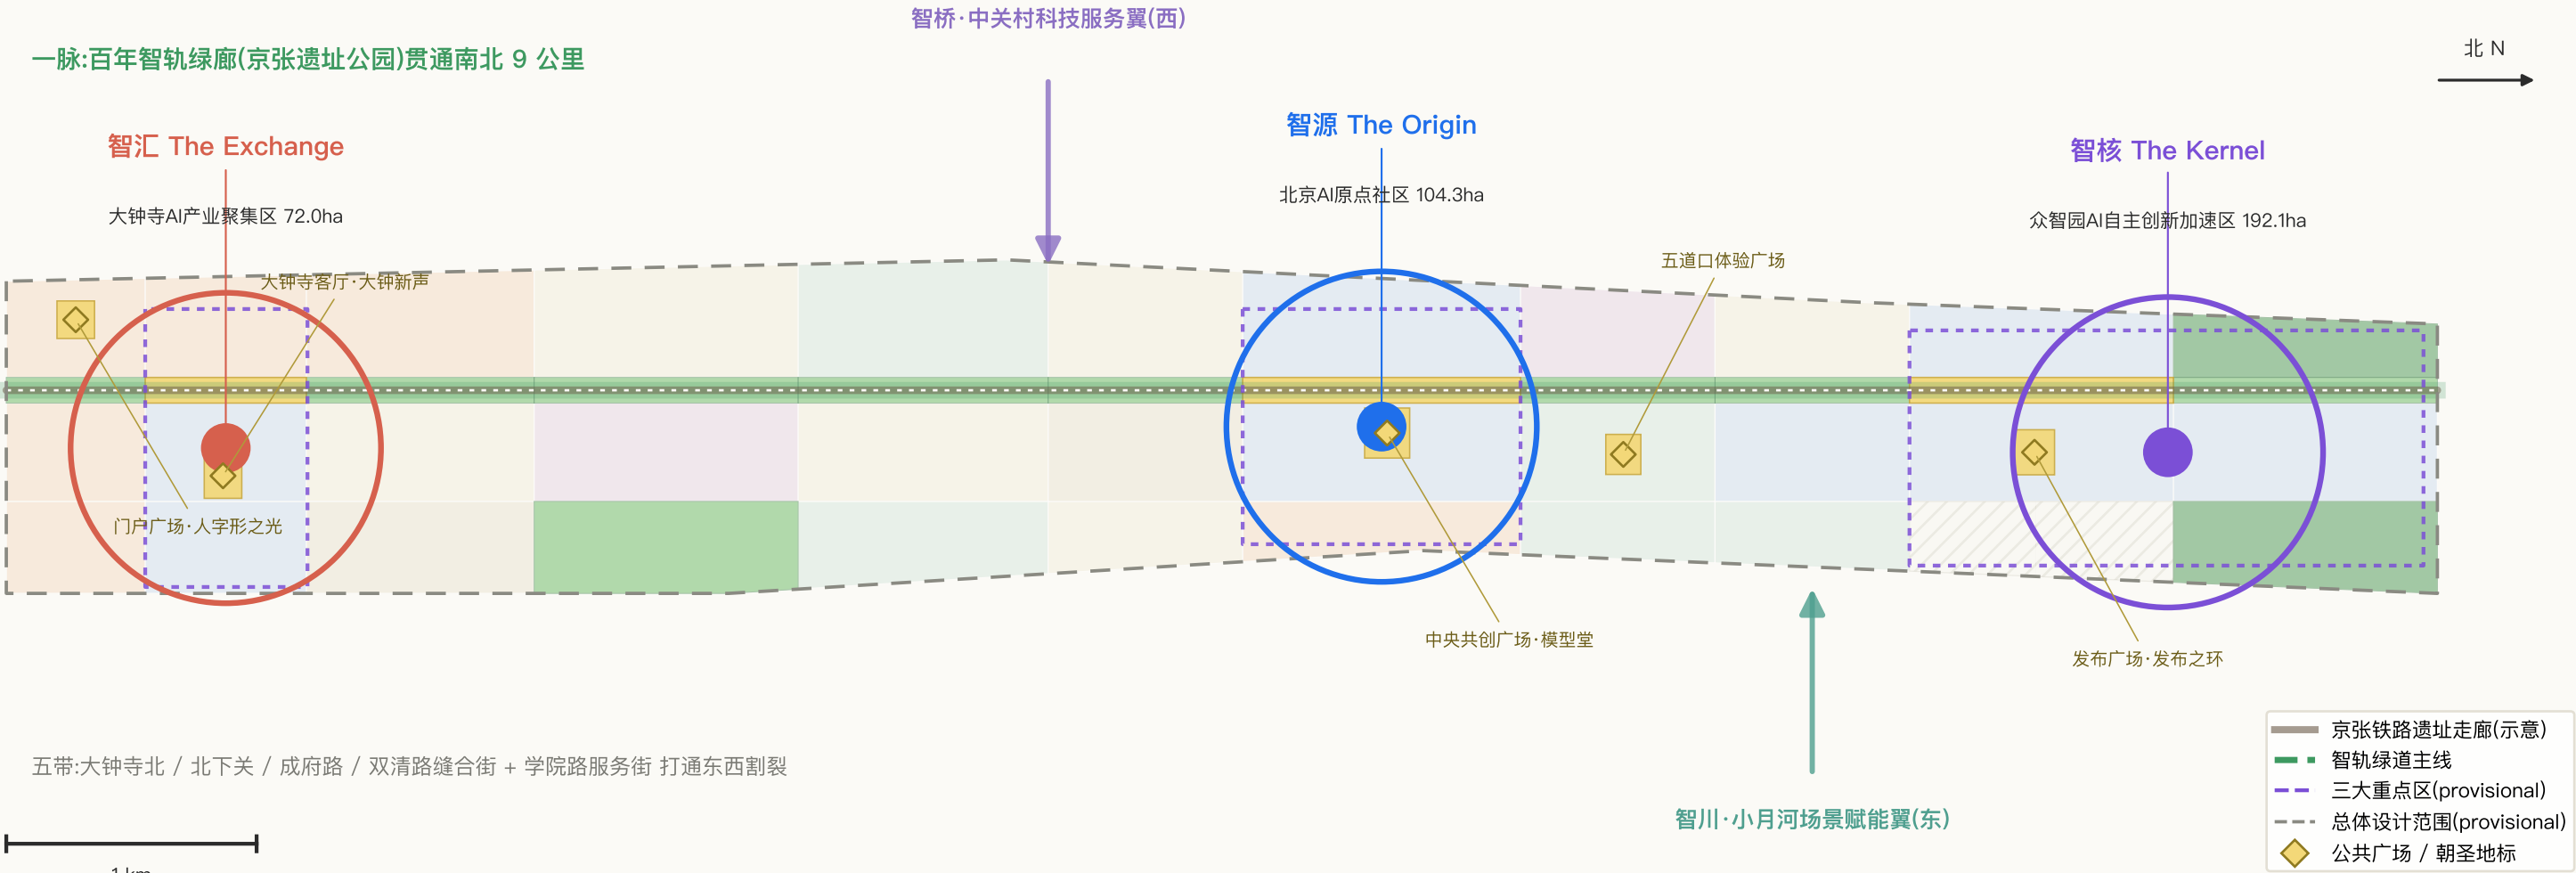

边界状态:总体范围与重点区域为 provisional 粗略替代边界(依公告文字四至,official_boundary=false),虚线表达;不得作为官方红线或精确面积依据。数据来源:公告 SRC-2026-BJ-GH-QUAL-PREANNOUNCEMENT + 仓库临时边界;全部面积按 EPSG:4548 复算。图为概念建议。

04 · 城市更新框架与用地方案

一脉三核五带多组团

科研23.6% · 居服23.2% · 商业13.1% · 教育12.7% · 文化6.0% · 绿地开敞18.6% · 留白2.8%

概念建筑规模 1028万m² · 概念容积率 0.90 · 基底密度 9.5%(702栋参数化建筑)

拆改留概念分类:保留~30% / 改造~20% / 新建~50%(算法示意,非地块级结论)


更新原则

存量提质为主 · 更新不驱离 · 权属主体自愿参与 · 留白触发式启用

全部强度数值为概念参考,待控规与现状普查确认(A-CONTROLS/EXISTING-001)。

图4 · 交通慢行 × 蓝绿公共空间 × AI场景复合系统

五条缝合街打通东西 · 9km绿道贯通南北 · 12个场景节点沿脉串珠(*为测试验证场景;道路均为概念建议非红线)

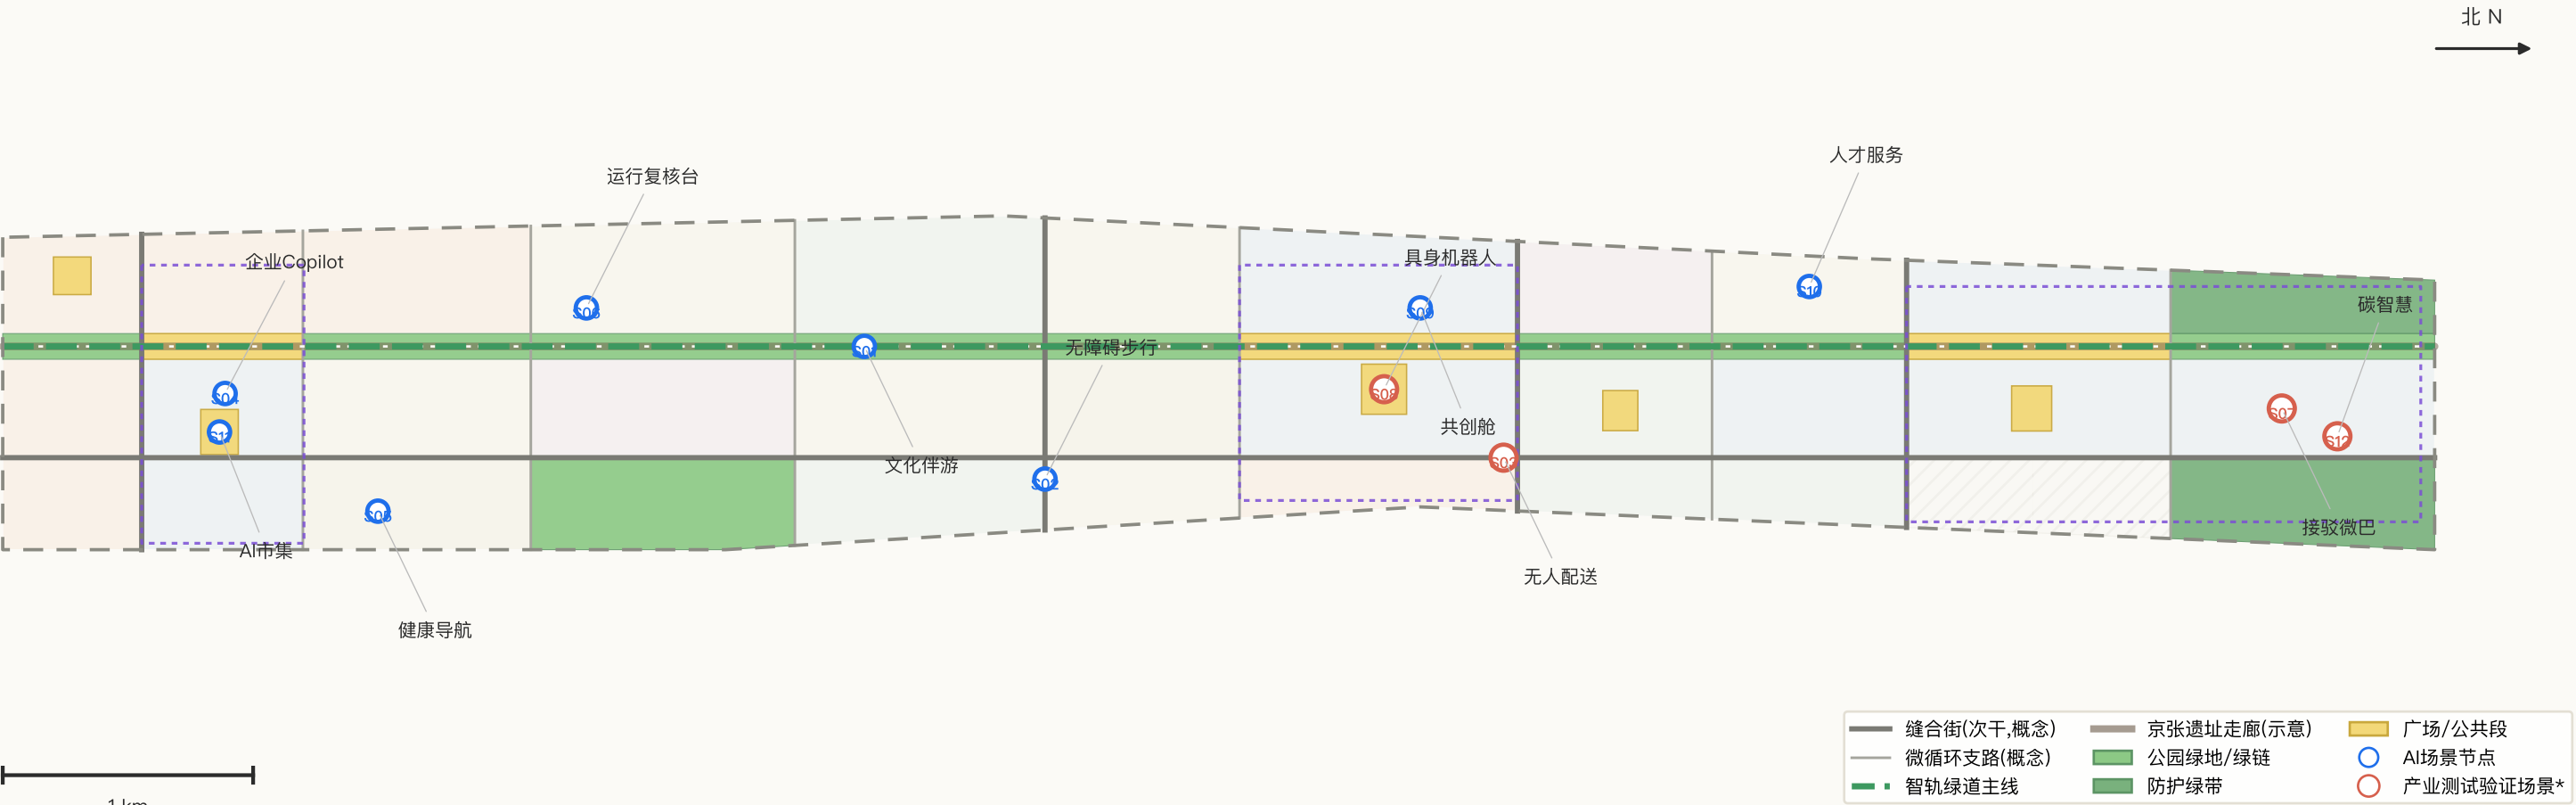


边界状态:总体范围与重点区域为 provisional 粗略替代边界(依公告文字四至,official_boundary=false),虚线表达;不得作为官方红线或精确面积依据。数据来源:公告 SRC-2026-BJ-GH-QUAL-PREANNOUNCEMENT + 仓库临时边界;全部面积按 EPSG:4548 复算。图为概念建议。


图3 · 三大重点区详细设计索引

定位差异 × 空间抓手 × 场景植入 × 实施风险 —— provisional 矩形仅为粗略范围,虚线弱化表达

三大节点在智脉上的位置与南北协同(北→右)

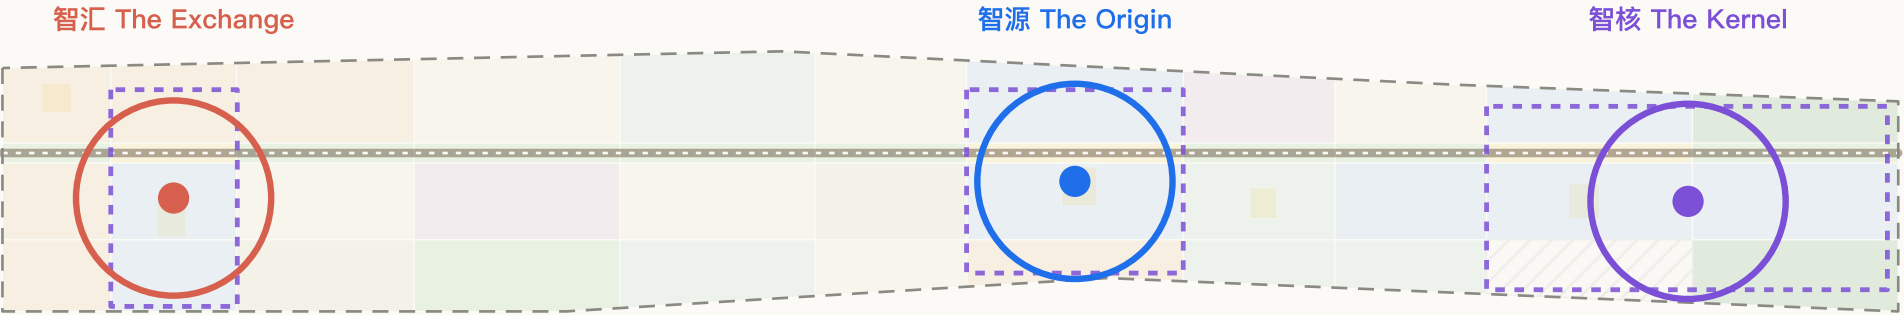


智汇 The Exchange · 大钟寺AI产业聚集区 72.0ha

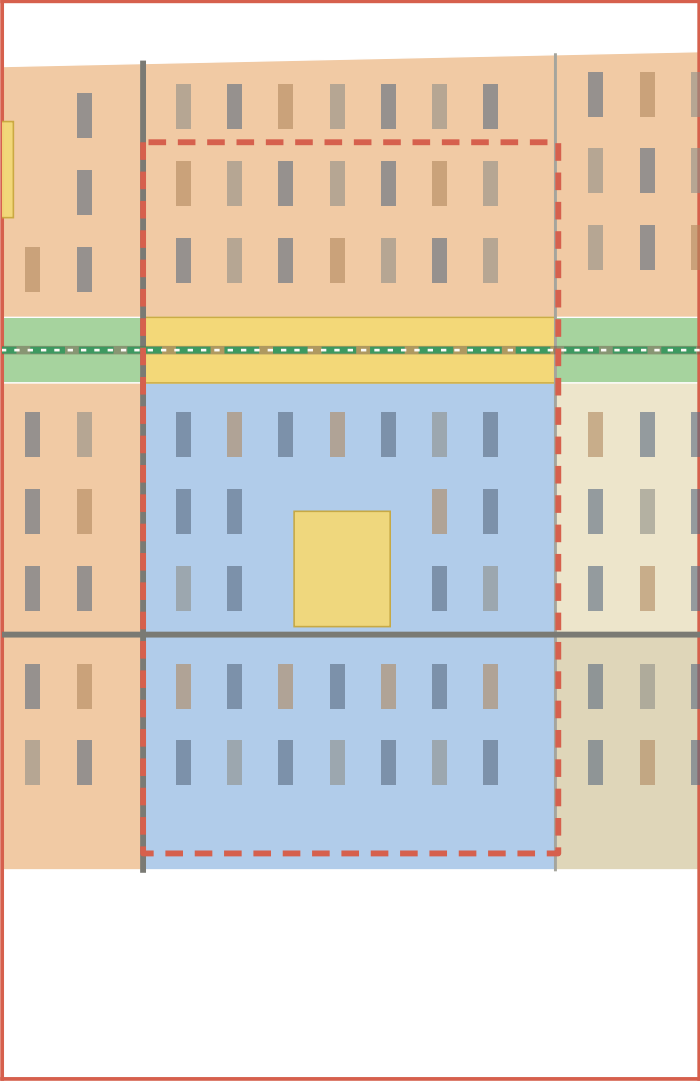


- 智能原生新业态+消费商务场景
- 西消费客厅 + 东研发转化两片
- 『大钟·新声』声音AI文化地标
- 场景:企业Copilot S04 / AI市集 S11
- 风险:商业权属分散,时序随市场

智源 The Origin · 北京AI原点社区 104.3ha

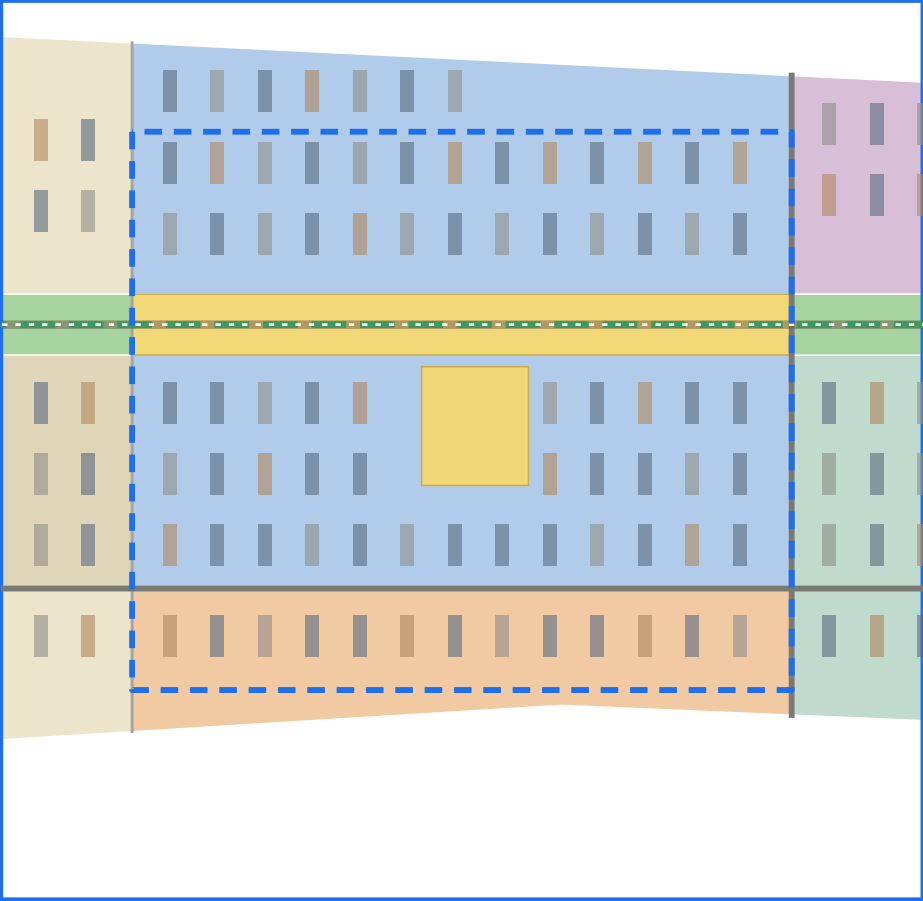

- 世界级AI创新生态+开源共创社区
- 存量改造为主:共创舱/算力自习室
- 中央共创广场布置 『模型堂』
- 场景:具身机器人 S08 / 共创舱 S09
- 风险:高校院所权属协调(自愿参与)

智核 The Kernel · 众智园AI自主创新加速区 192.1ha

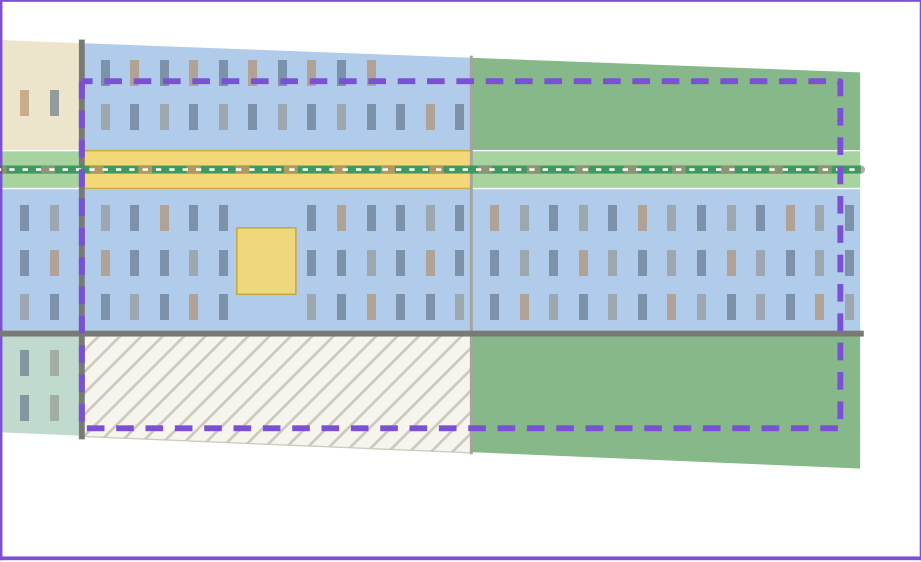

- 全栈自主创新体系+治理话语权
- 西/东/北三组团 + 31.7ha 战略留白
- 发布广场 『发布之环』仪式空间
- 场景:自动驾驶接驳环 S07 / 碳智慧 S12
- 风险:留白管控与五环声环境待专项

07 · AI场景与生态运营

12张场景卡(4个测试验证*)

S01文化伴游 S02无障碍步行 S03无人配送* S04企业Copilot S05健康导航 S06运行复核台

S07接驳微巴* S08具身机器人* S09共创舱 S10人才服务 S11AI市集 S12碳智慧*

测试框架:划定边界+限定时段+知情标识+人工接管+事后审计

6类画像 · 6个全球案例 · 4处朝圣地标

画像:研究员/创业者/国际人才/原住民/家庭/治理者

案例:Kendall Square · one–north · King's Cross · Station F · 南山 · 西岸

地标:人字形之光 · 模型堂 · 发布之环 · 大钟新声(概念创意,涉文保以审定为前提)

长期运营

智脉大会 · AI马拉松 · 发布季 · 双年展;开发者社区 『贡献–荣誉–再贡献』回路;


场景开放清单 → 测试 → 孵化 → 成长的招引转化漏斗(均为概念机制)。

图5 · 核心指标复算与证据链

全部指标由提交几何在 EPSG:4548 下重算,评审者可复现;待确认控规指标显式标注



从来源到正文的证据链

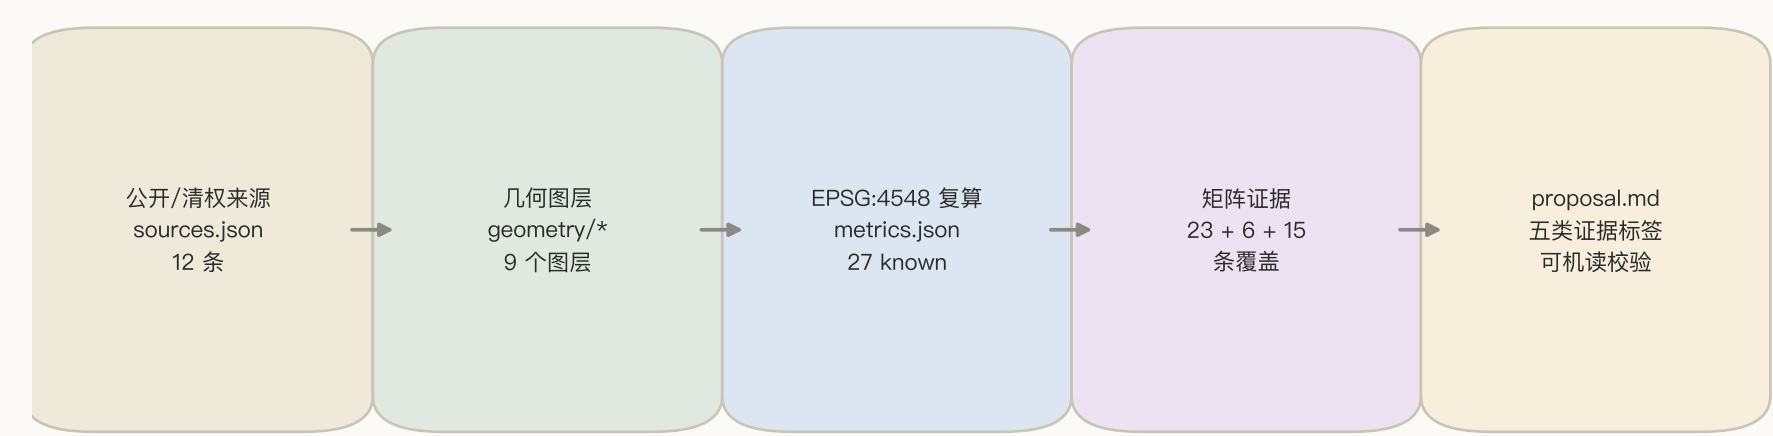

证据链原则:每个正文判断可回溯到图层要素与公式;图纸与HTML为解释层,GeoJSON/JSON为权威数据。

待确认法定控制条件(A-CONTROLS-001)

- ❖ 容积率 floor_area_ratio — missing

❖ 建筑高度 building_height_m — missing

❖ 建筑密度 building_density — missing

❖ 绿地率 green_ratio(法定) — missing

❖ 退线 setback_m — missing

本方案全部强度数值为概念复算参考;official 边界与控规条件补齐后统一重算(planning_limits.json 登记缺口)。

09 · 分期实施与风险合规

三期计划(概念)

近期 PH-1 AI原点启动区 3.68km² · 中期 PH-2 众智园拓展区 3.45km² · 远期 PH-3 大钟寺协同区 4.28km²

12项更新项目清单,含图层定位/依赖条件(见 proposal.md)

风险与合规

provisional 边界不得作官方红线;现状/权属/市政/文保数据缺失已逐项登记;

全部资料公开或清权;无政府批准背书表述;AI生成方法全披露;

版权:原创内容按 COMMUNITY-DISPLAY-ONLY 提交展示。