


一带三核、两翼串联、三类基准互相校验。

01 / OVERVIEW - 三类基准、三核与公共验证主线

京张智证公地总览

JZ BENCHMARK / v0.1

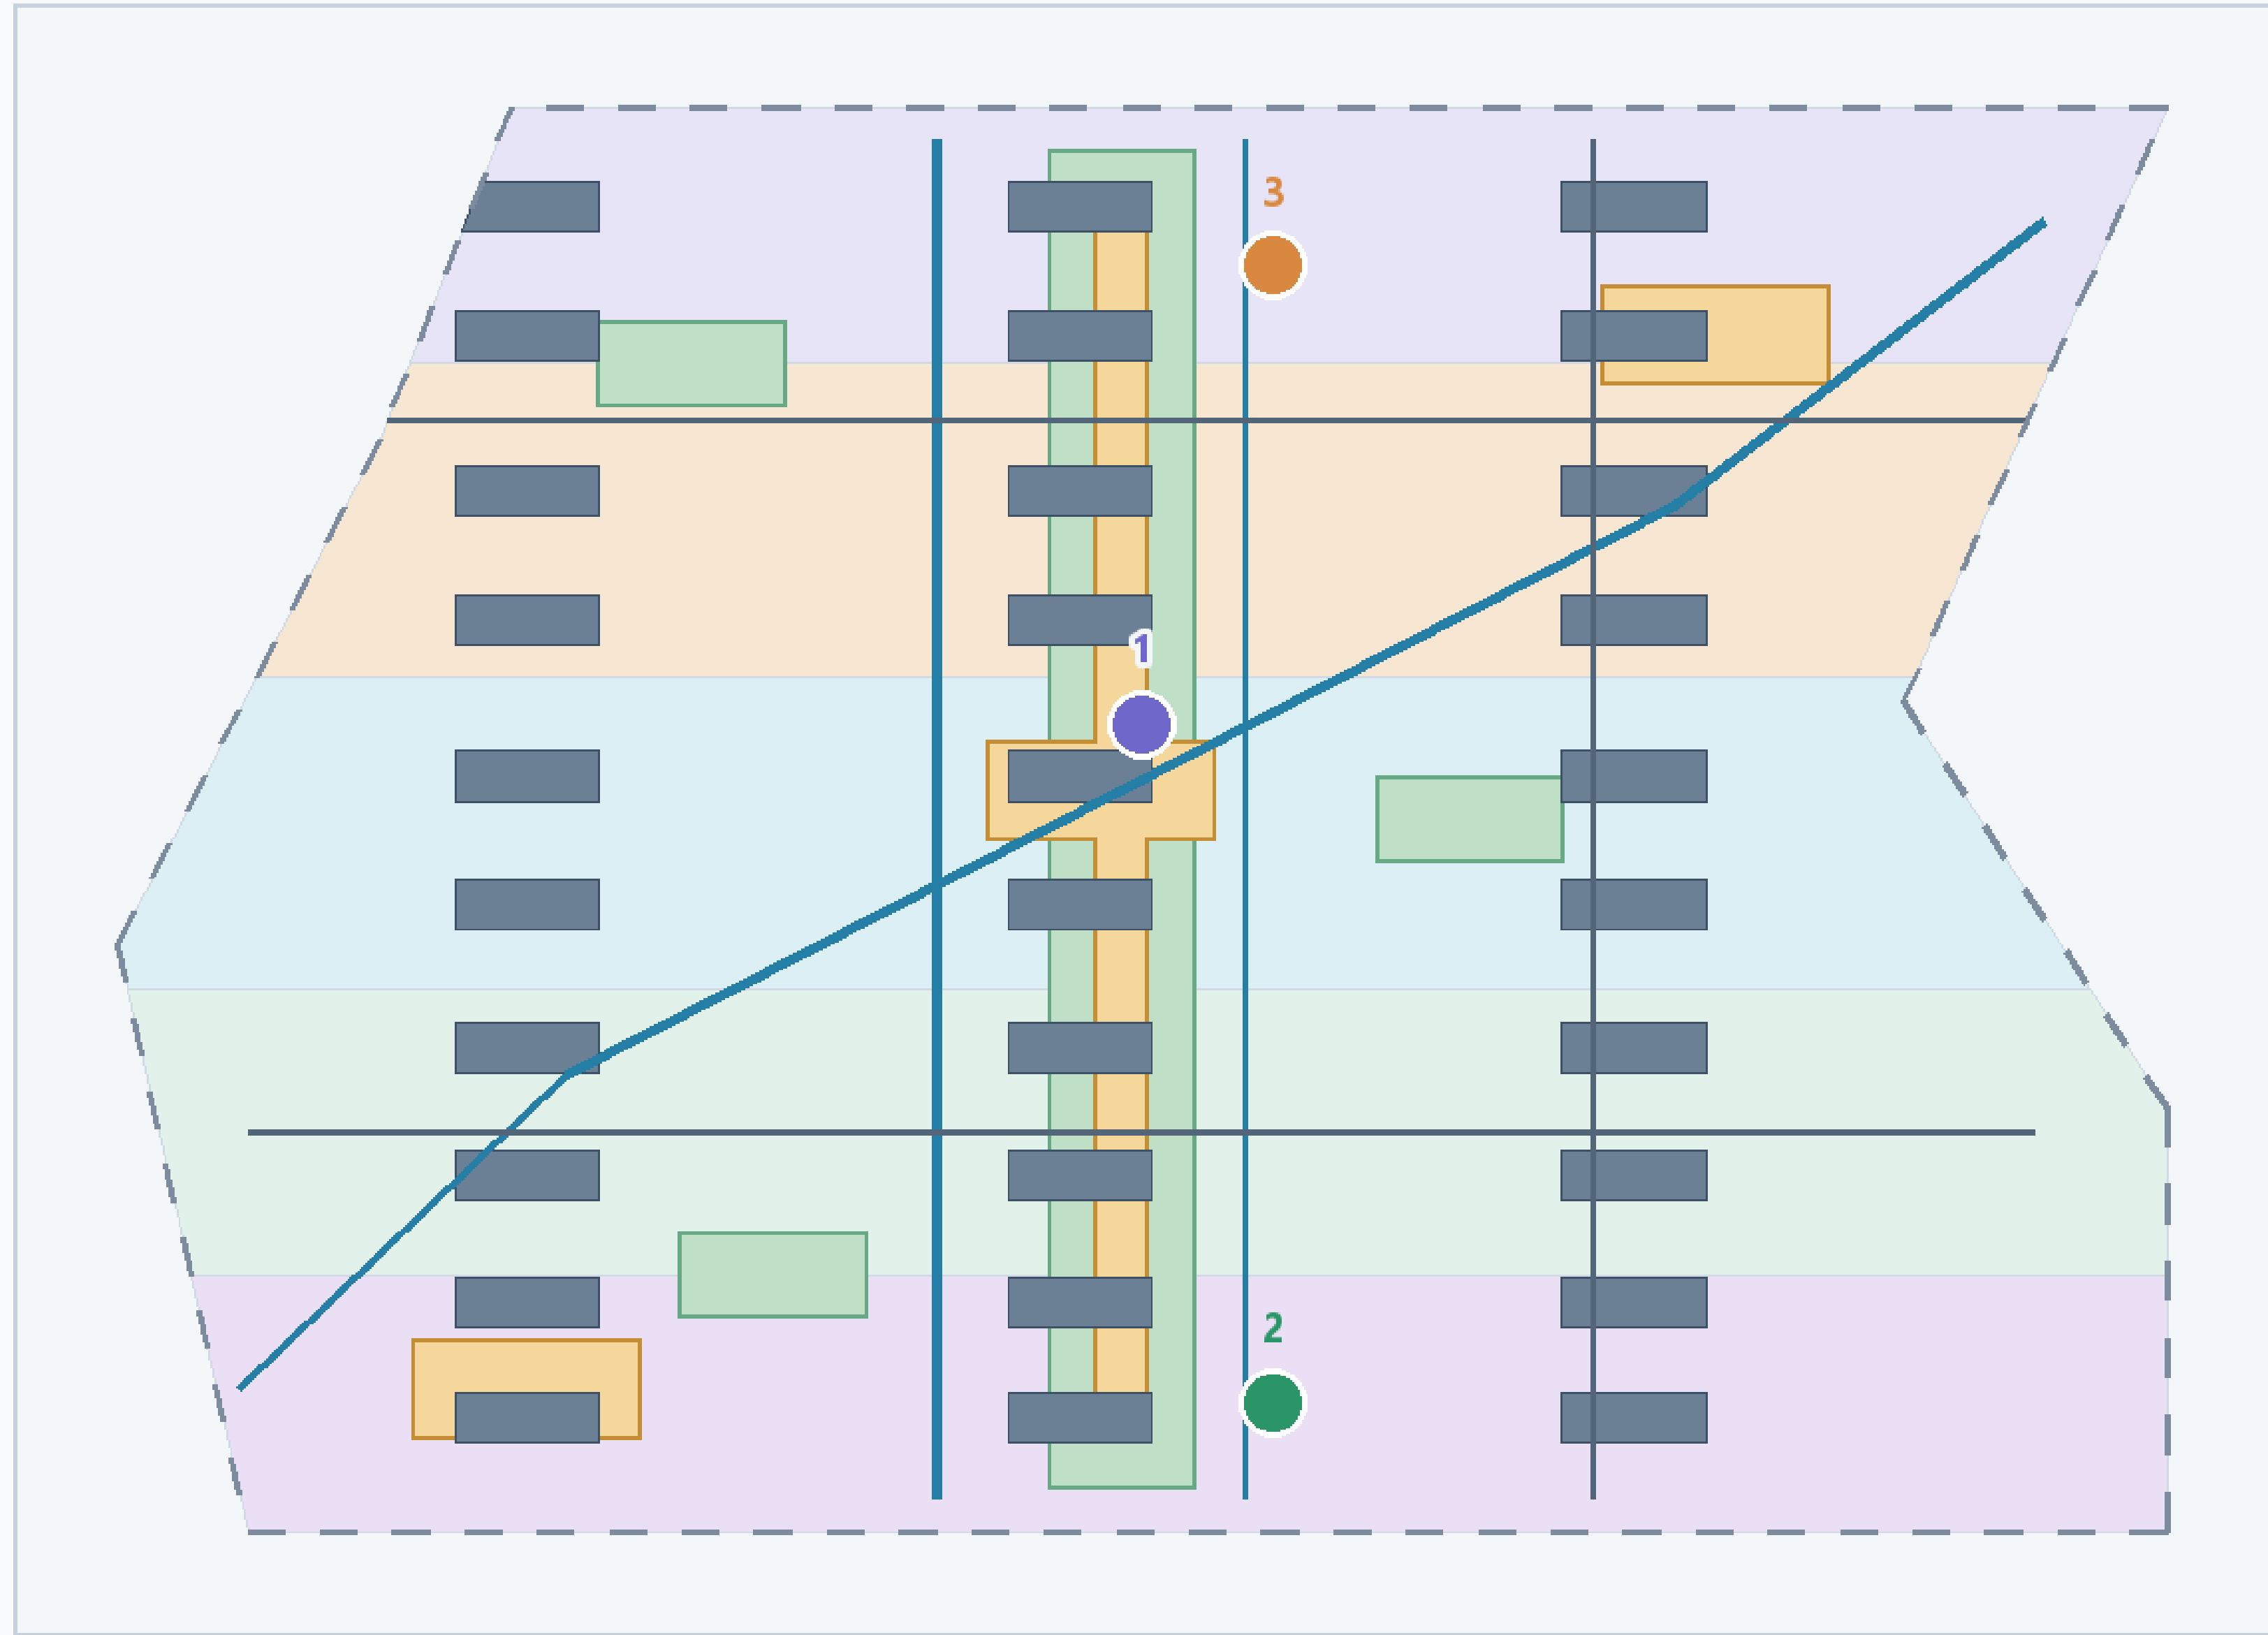

方案主线

研发基准 - 安全、标准、开源协作

公共基准 - 京张记忆、居民服务、慢行公地

应用基准 - 产业展示、城市服务、国际交流

三处重点区

- 众智园 / 研发基准核
- AI原点 / 公共基准核
- 大钟寺 / 应用基准核

同源图面：site_boundary / land_use / buildings / roads / green_space / public_space / metrics；边界虚线为 provisional。

PROVISIONAL INTAKE

三层范围

统筹研究范围 43.6 km²，总体设计范围 11.41 km²；三类重点区约 368.4 ha。

证据主线

GeoJSON 固定空间关系，metrics.json 算量比例，相关任务和专业深度输出正文与图档。


概念建议 / provisional geometry / 供专业团队深化研究

五类用地共边覆盖临时 site boundary，更新逻辑从保留与可逆改造开始。

02 / STRUCTURE - 共边分区、蓝绿公地与三层范围

空间结构与用地分区

JZ BENCHMARK / v0.1

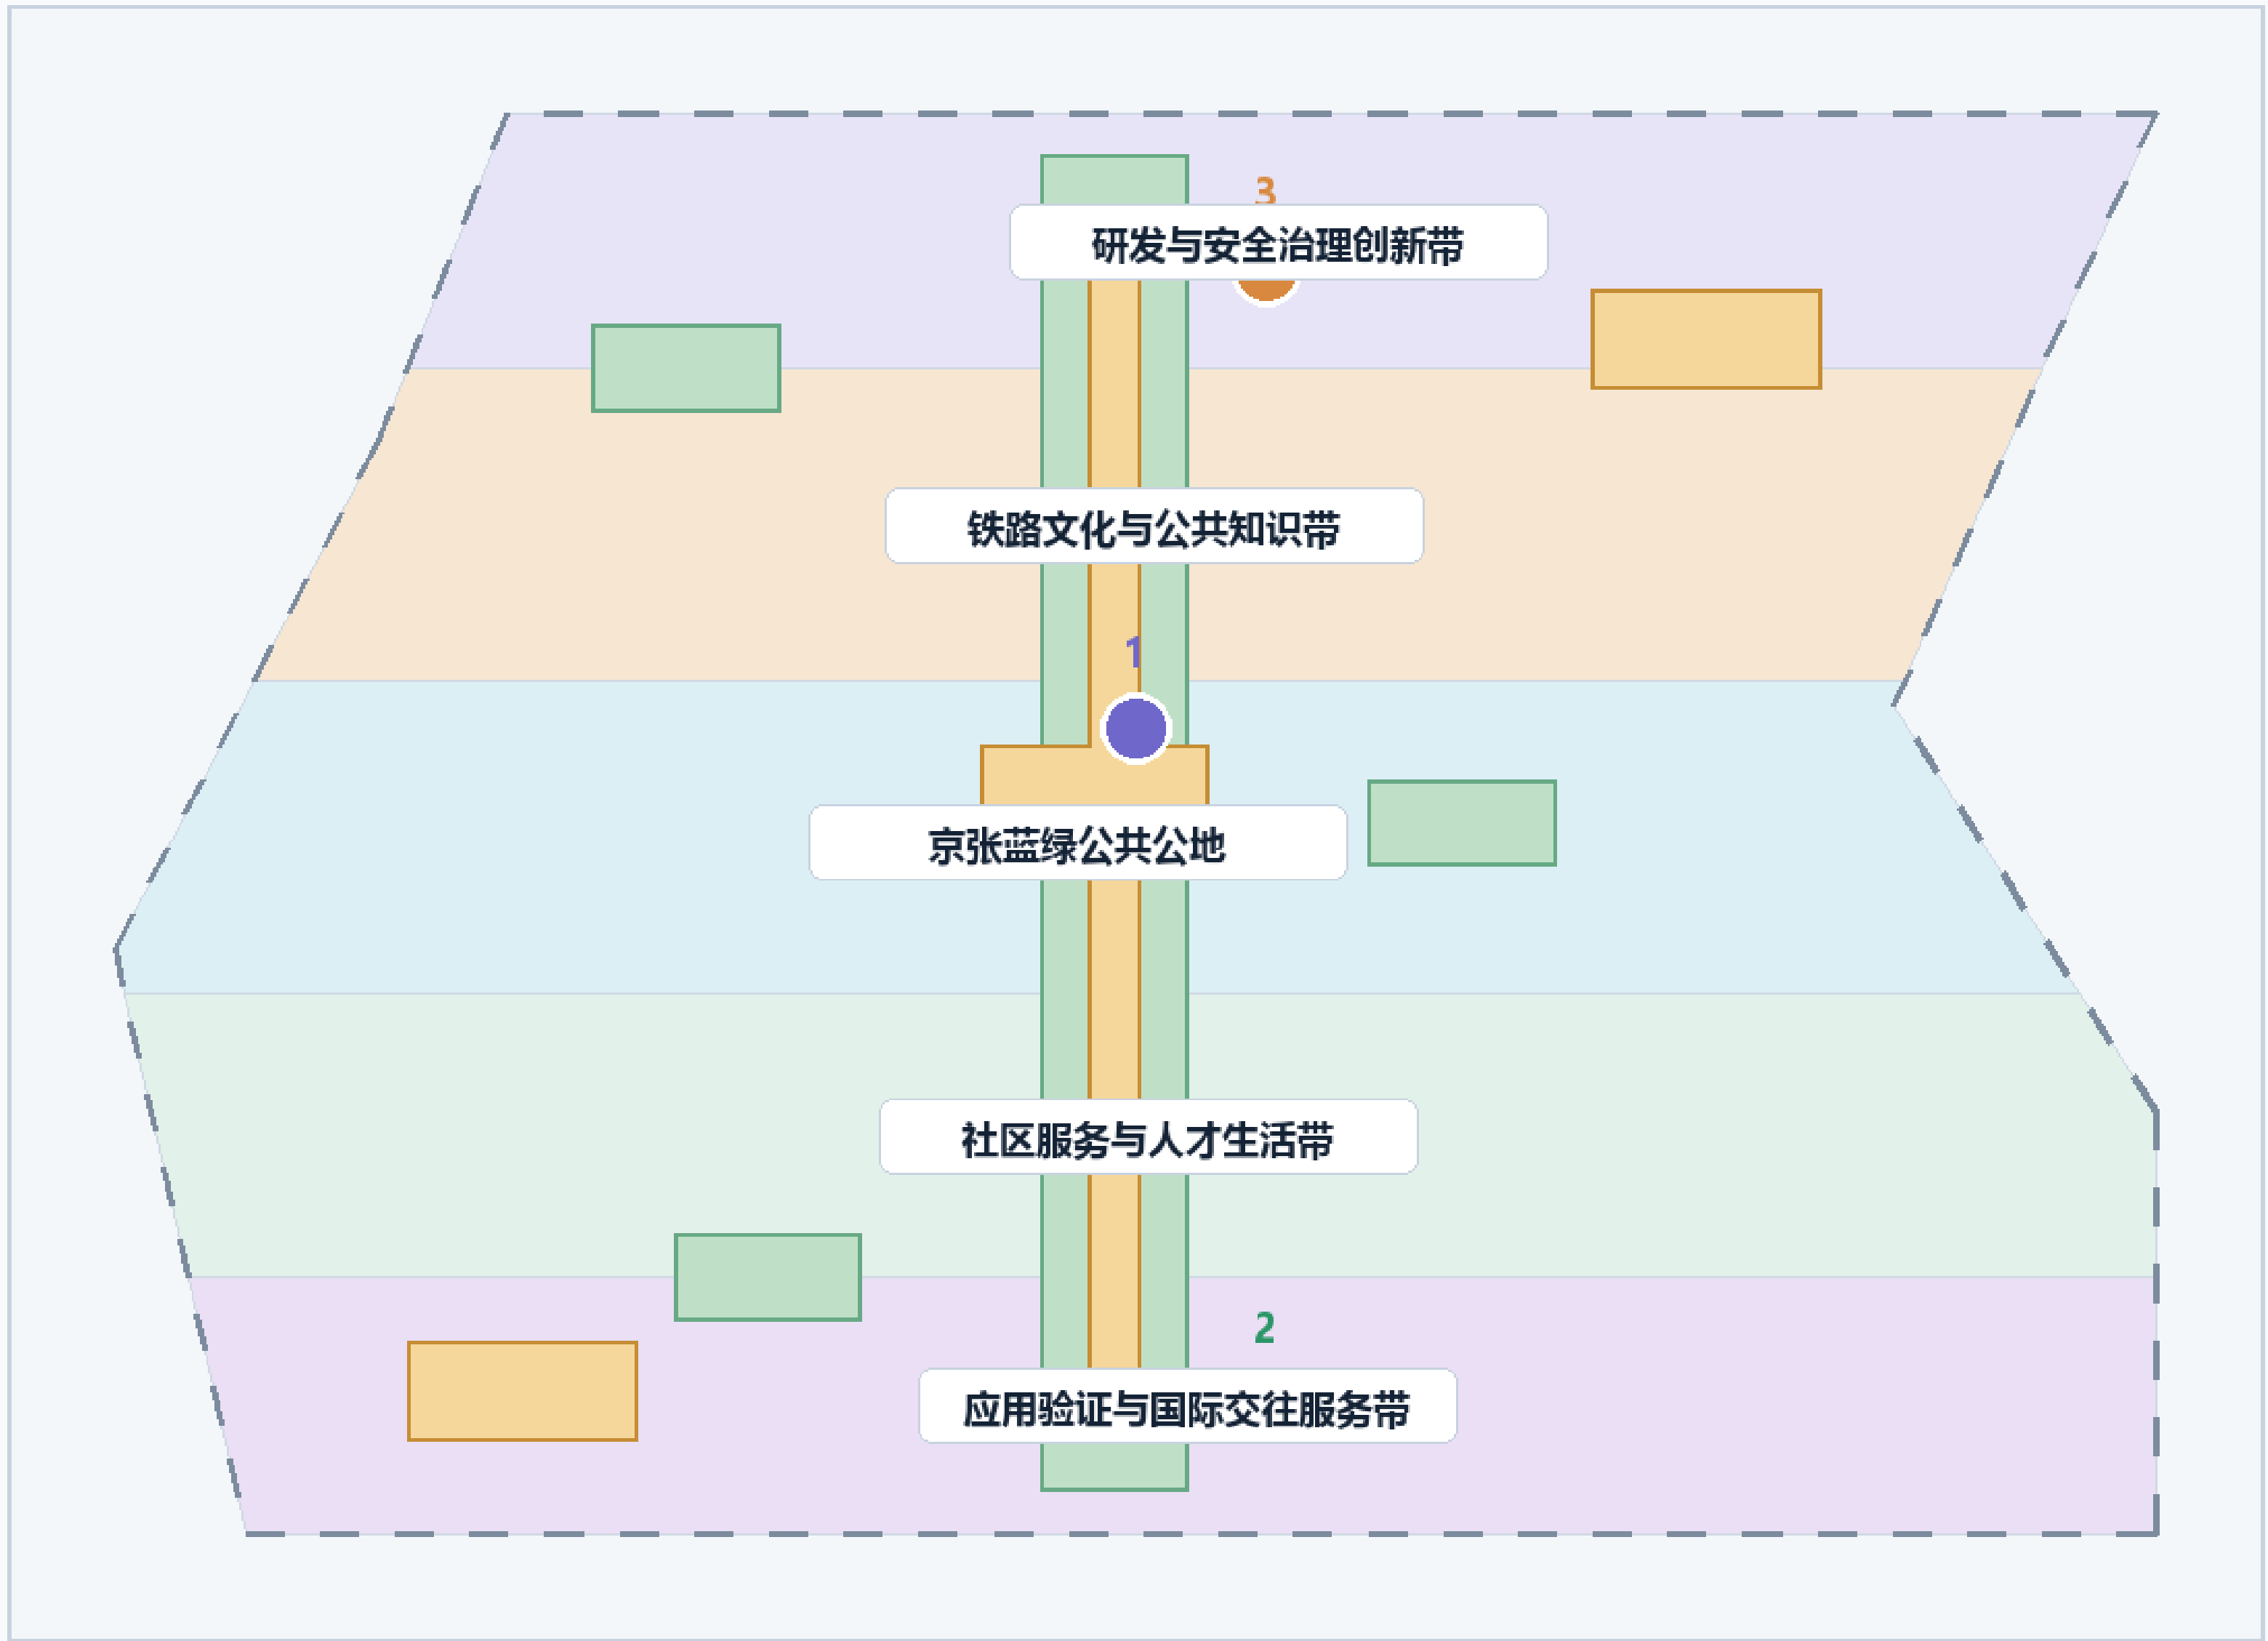

空间递进

统筹研究
43.6 km²
产业、文化、人才和区域协同

总体设计
11.4 km²
城市更新、交通、市政、风貌

重点区域
368.4 ha
三核详细设计与场景验证

五类用地共边切分
每个分区从同一 provisional site 派生，避免重叠和缺口；官方 polygon 到位后整体替换与复算。

用地代码遵循项目枚举与 MNR 分类逻辑；彩色面为设计建议，非控规批准用地。

PROVISIONAL INTAKE

用地分区
研发与安全治理、社区与人才生活、京张蓝绿公地、铁路文化与公共知识、应用验证与国际交往服务。

建筑与更新
30 个概念建筑基底；六类可更新项目包；FAR、高度、总楼面积和拆建留伟正式图和确认。


概念建议 / provisional geometry / 供专业团队深化研究

慢行先行，公共空间可达，AI 场景以授权和人工复核进入城市日常。

04 / MOBILITY + BLUE-GREEN - 慢行先行、公共可达

交通、蓝绿与AI场景节点

JZ BENCHMARK / v0.1

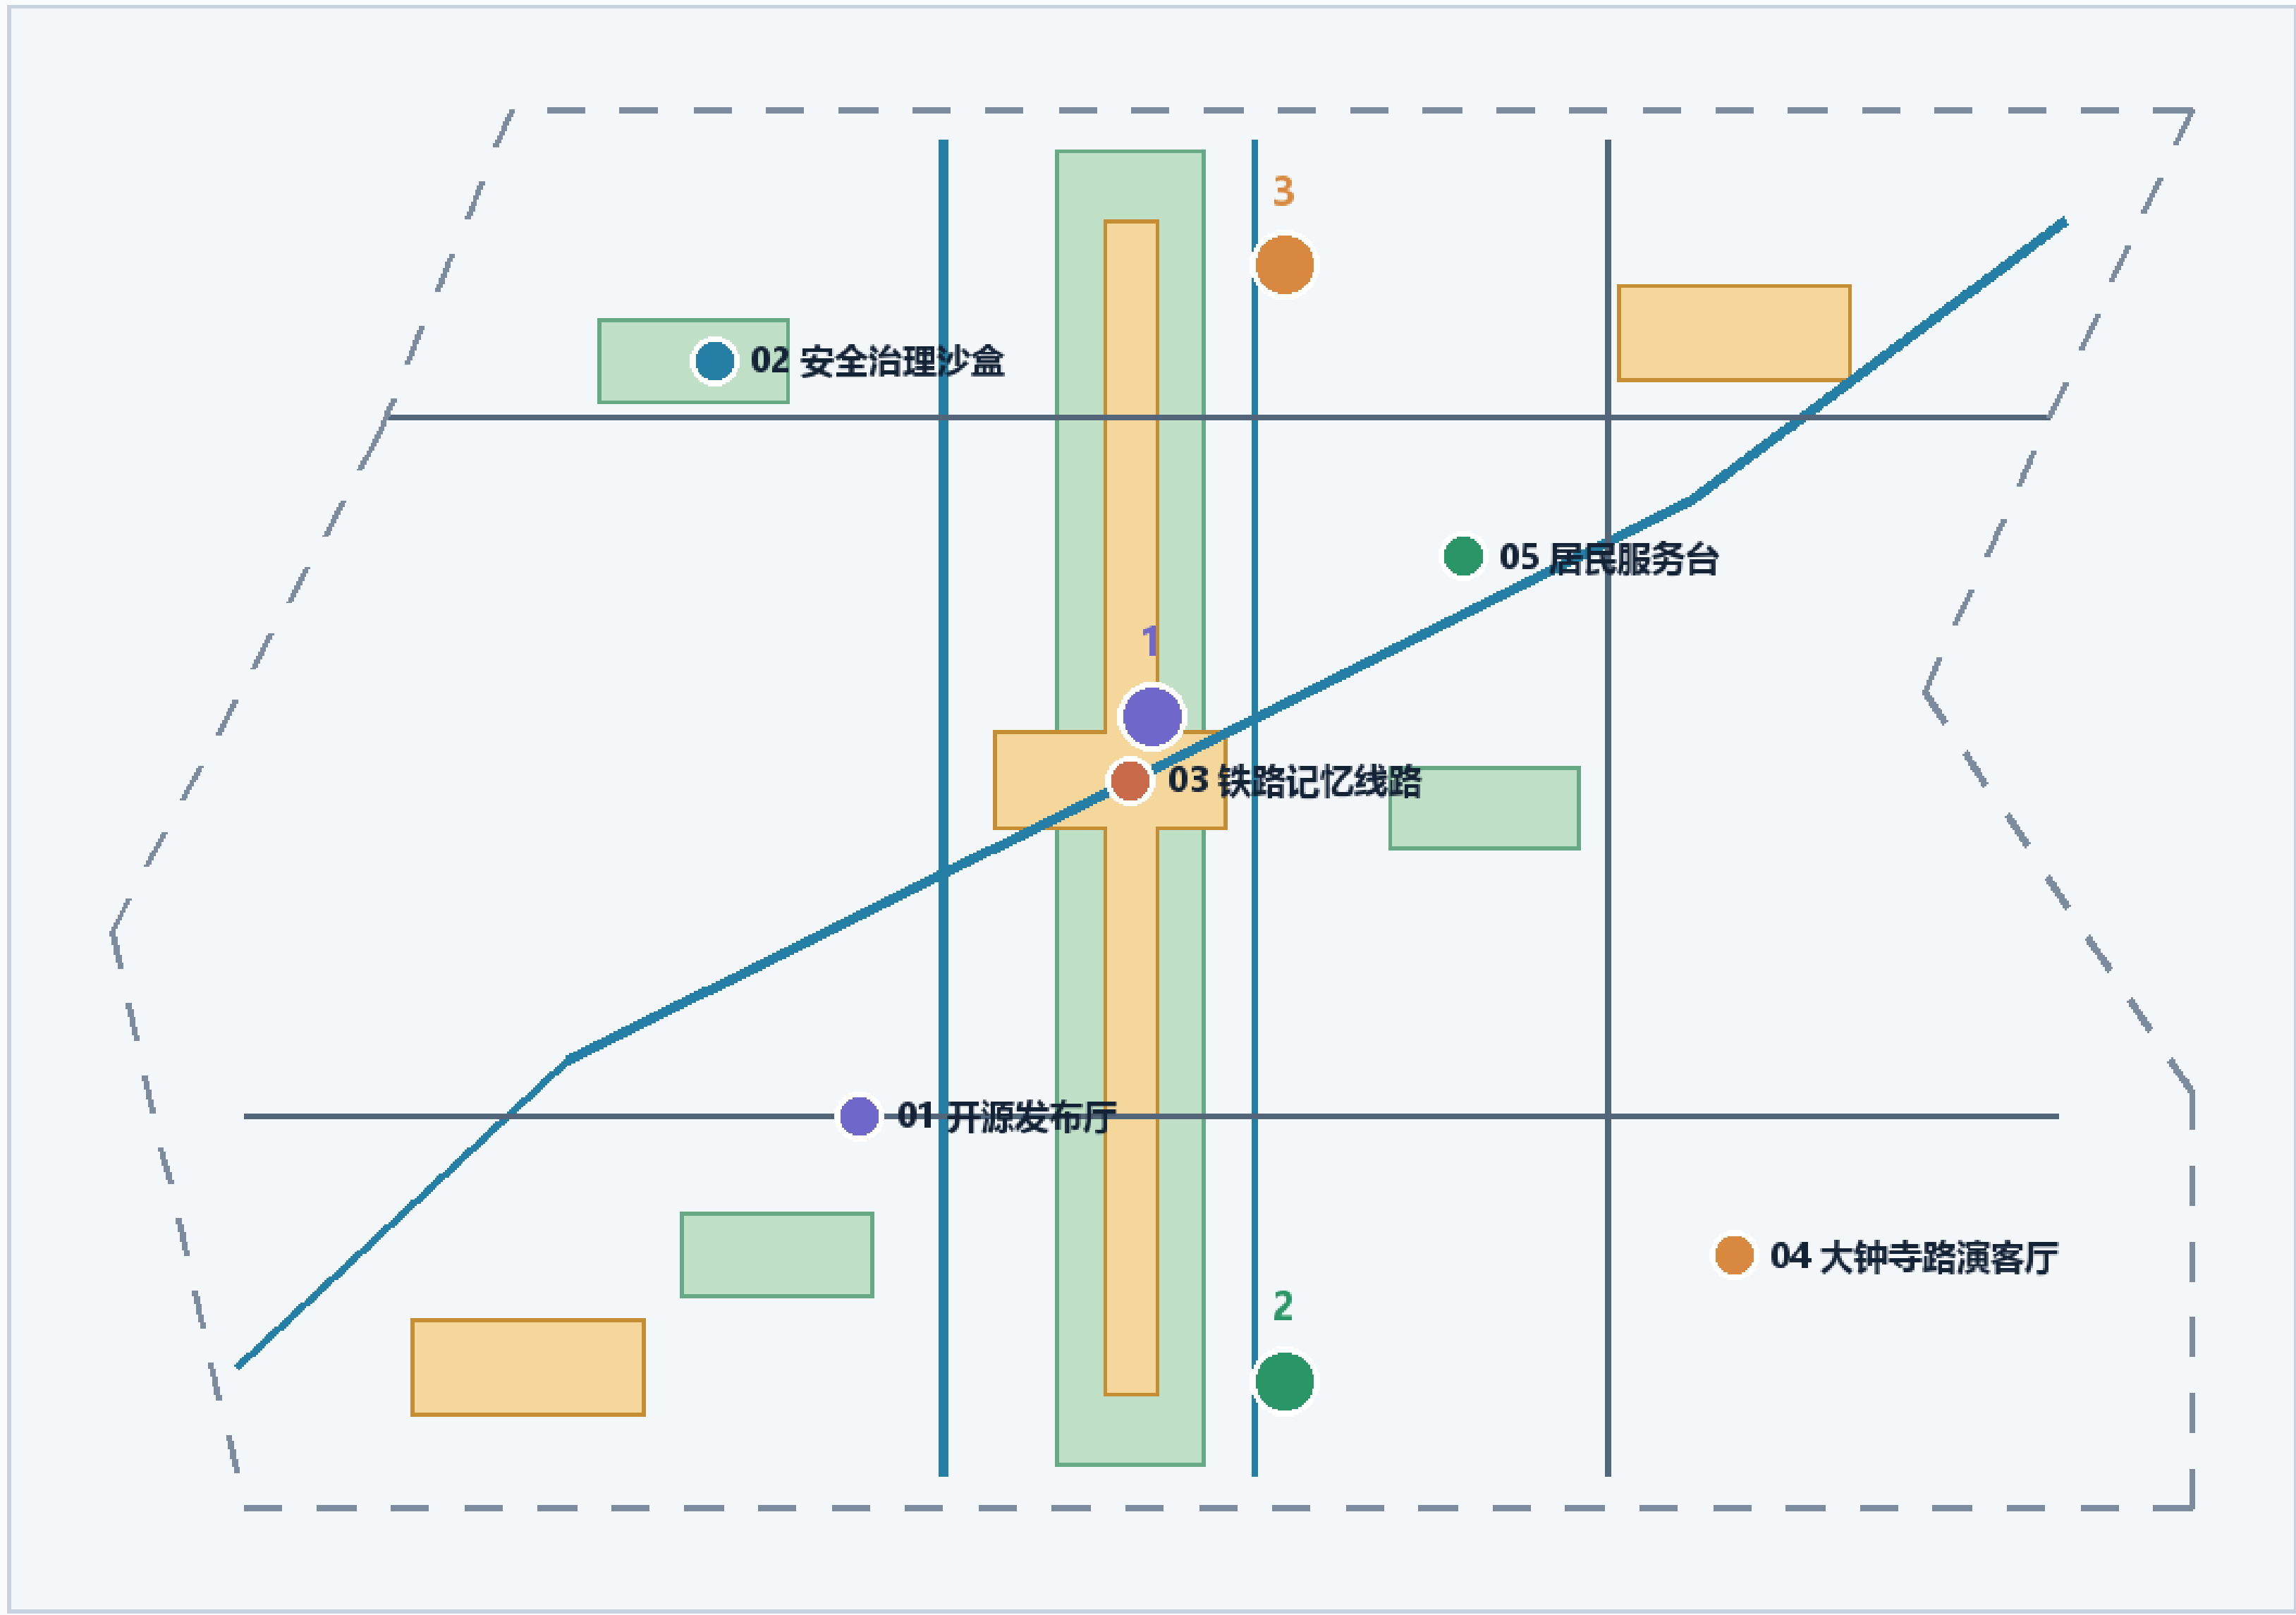

四层关系

- 站点接驳**
轨道接口与步行安全
- 慢行主环**
绿道、骑行、无障碍
- 公共验证**
场景预约与人工复核
- 社区服务**
不参与试验也能使用

概念边界

道路为中心线建议，不是红线；蓝绿面为公共空间概念网络。

交通与蓝绿图由 roads / green_space / public_space 同源派生；不包含远程底图。

PROVISIONAL INTAKE

交通慢行

六条概念中心线约 38.10 km，包含主环、铁路记忆线、小月河慢行线和三桥接驳线。

蓝绿公共空间

中央蓝绿公共空间串联公共空间、验证庭院和线性公共验证台，居民不参与试验也可正常使用。


概念建议 / provisional geometry / 供专业团队深化研究

三核承担不同基准，不做同质化科技园。

03 / KEY AREAS - 三核定位与公共接口

三处重点区：不同角色、同一证据链

JZ BENCHMARK / v0.1

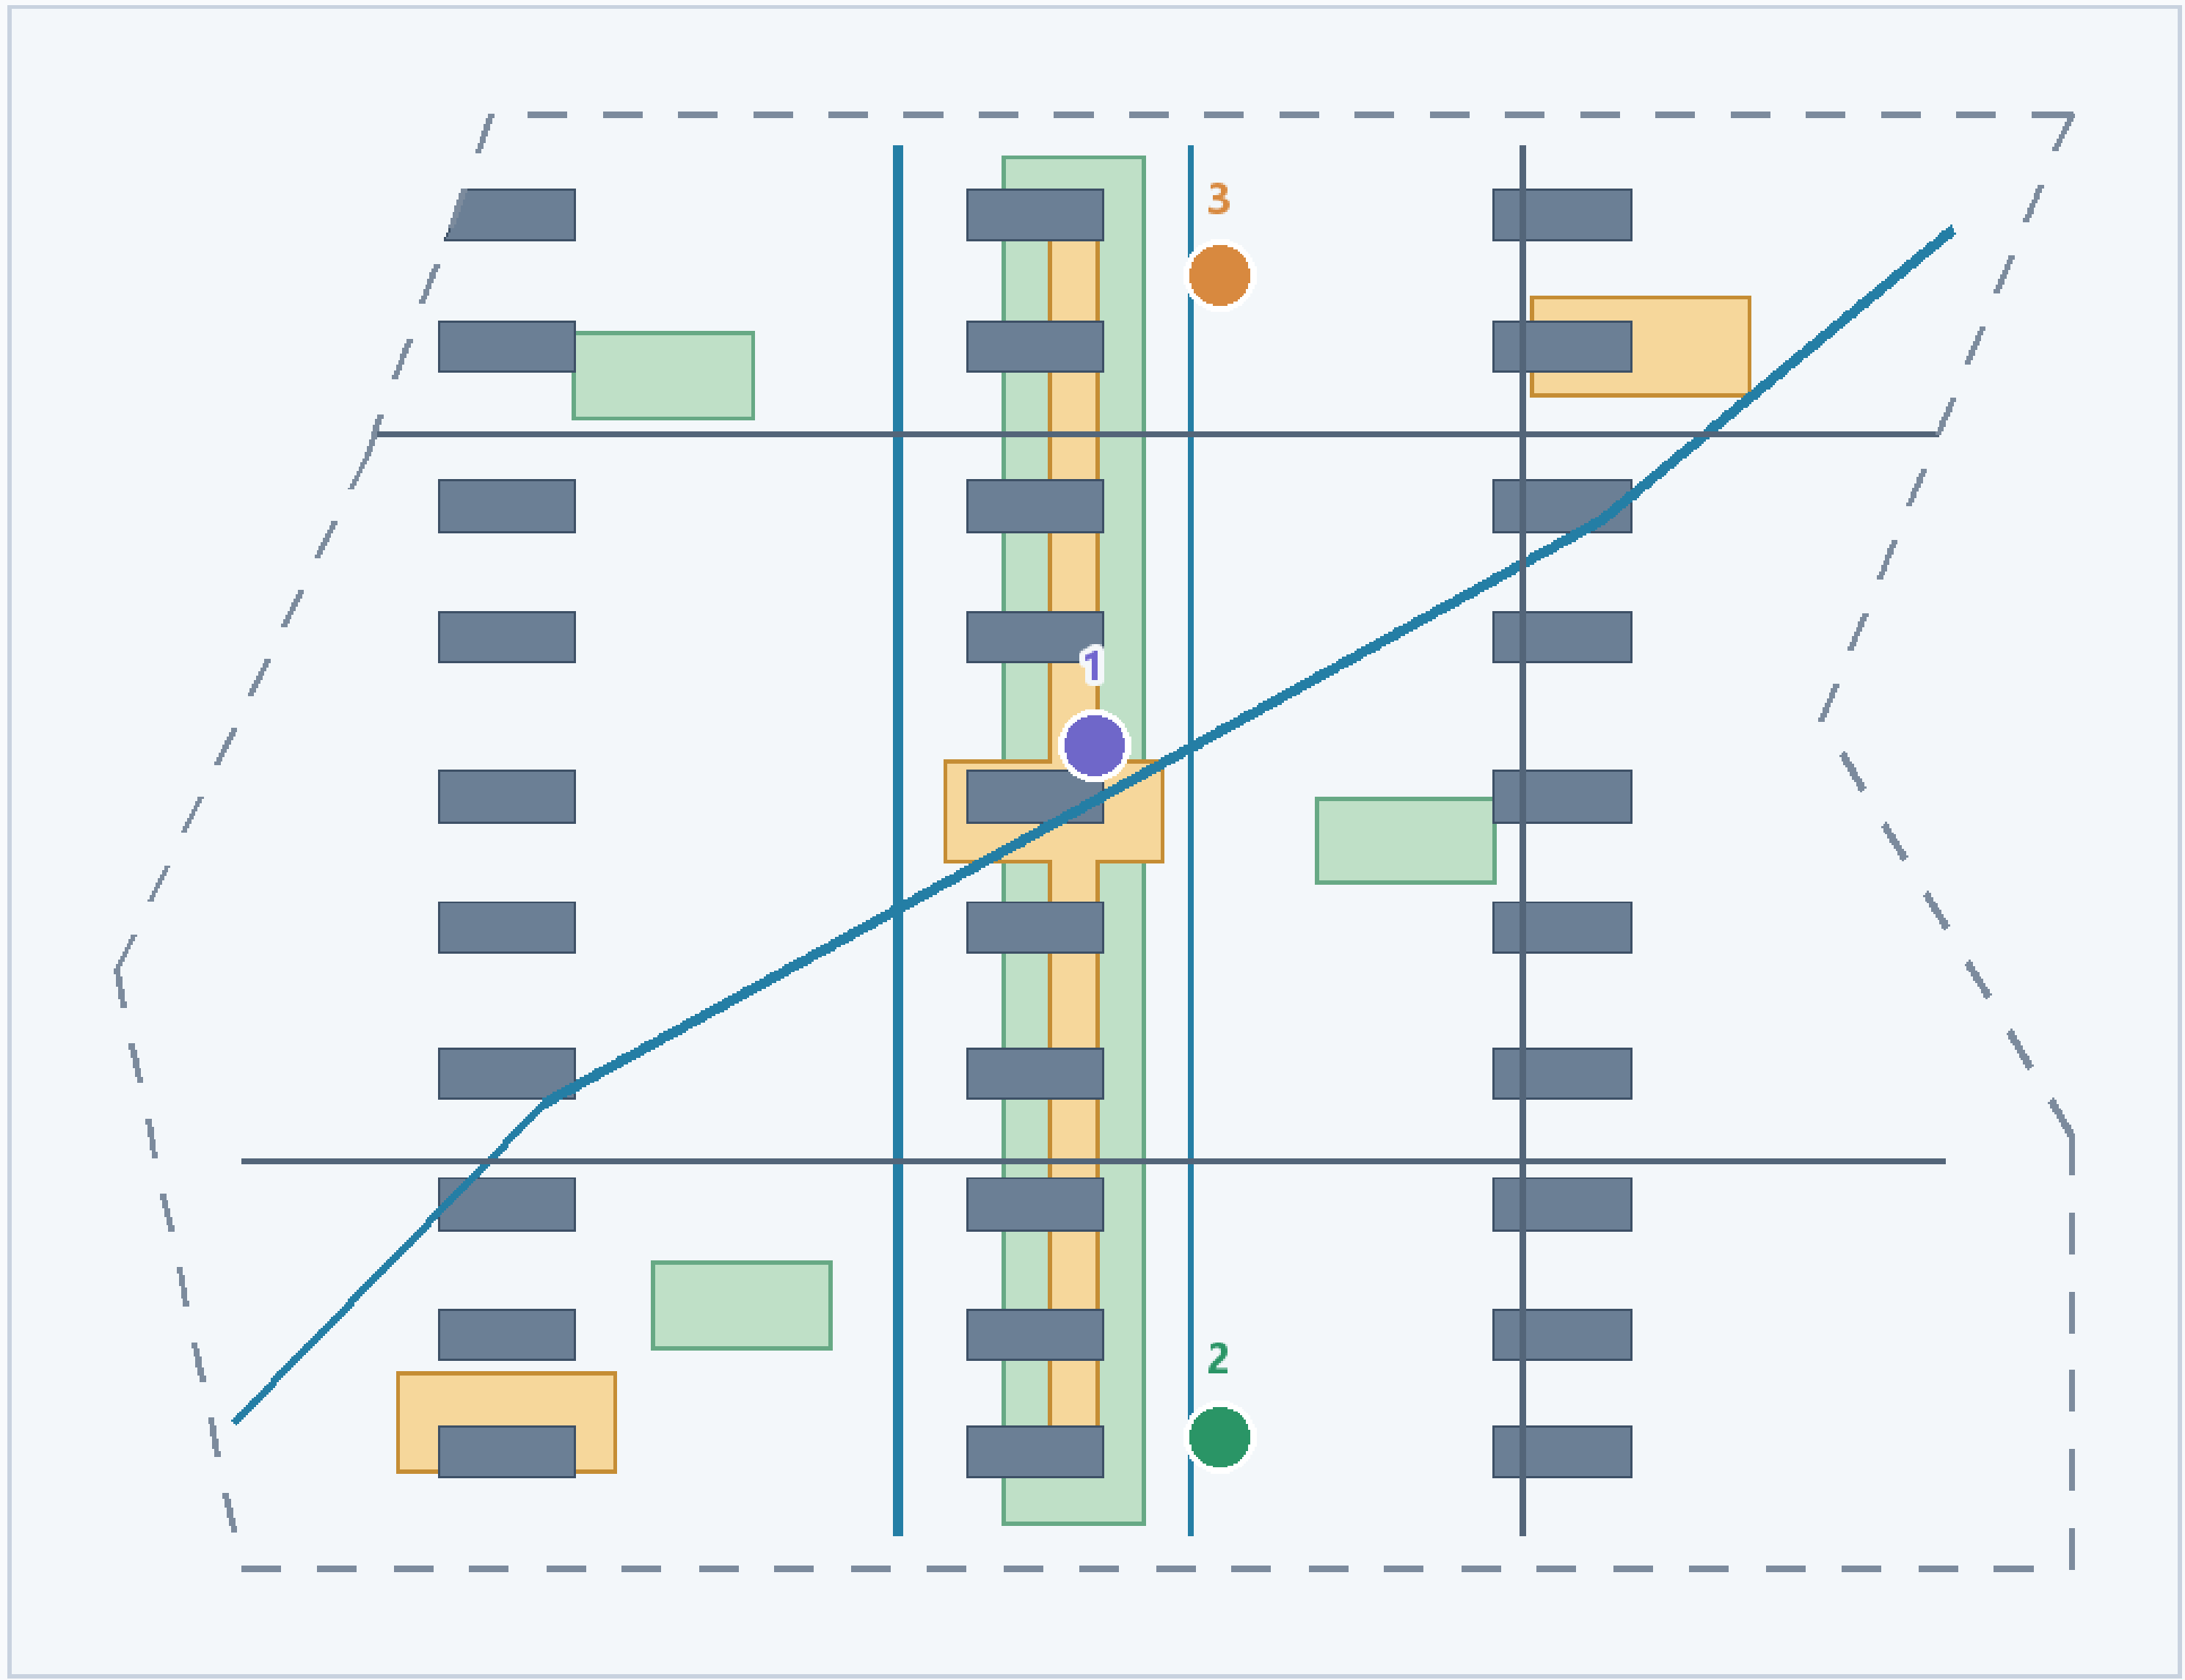

三核动作

1 众智园

研发基准核

安全治理、标准共创、低碳创新廊

2 AI原点社区

公共基准核

开源发布、成果转化、人才生活

3 大钟寺

应用基准核

国际路演、智能终端、站点步行

共同约束

三处 polygon 均为 provisional；权属、文保、控规、交通和工程条件须由专业团队补齐。

重点区编号对应 key_areas.geojson；色彩只表达角色差异，不表达审批等级。

PROVISIONAL INTAKE

01 / 众智园

研发基准核：安全治理实验室、标准共创工坊、低碳创新廊和验证庭院。

02-03 / AI 原点与大钟寺

公共基准核：知识共享和人才生活；应用基准核：国际路演、智能终端和站点步行。


概念建议 / provisional geometry / 供专业团队深化研究

十张场景卡把知识生产、产业验证、城市服务和文化体验连成公共路线。

04 / MOBILITY + BLUE-GREEN - 慢行先行、公共可达

交通、蓝绿与AI场景节点

JZ BENCHLINE / v0.1

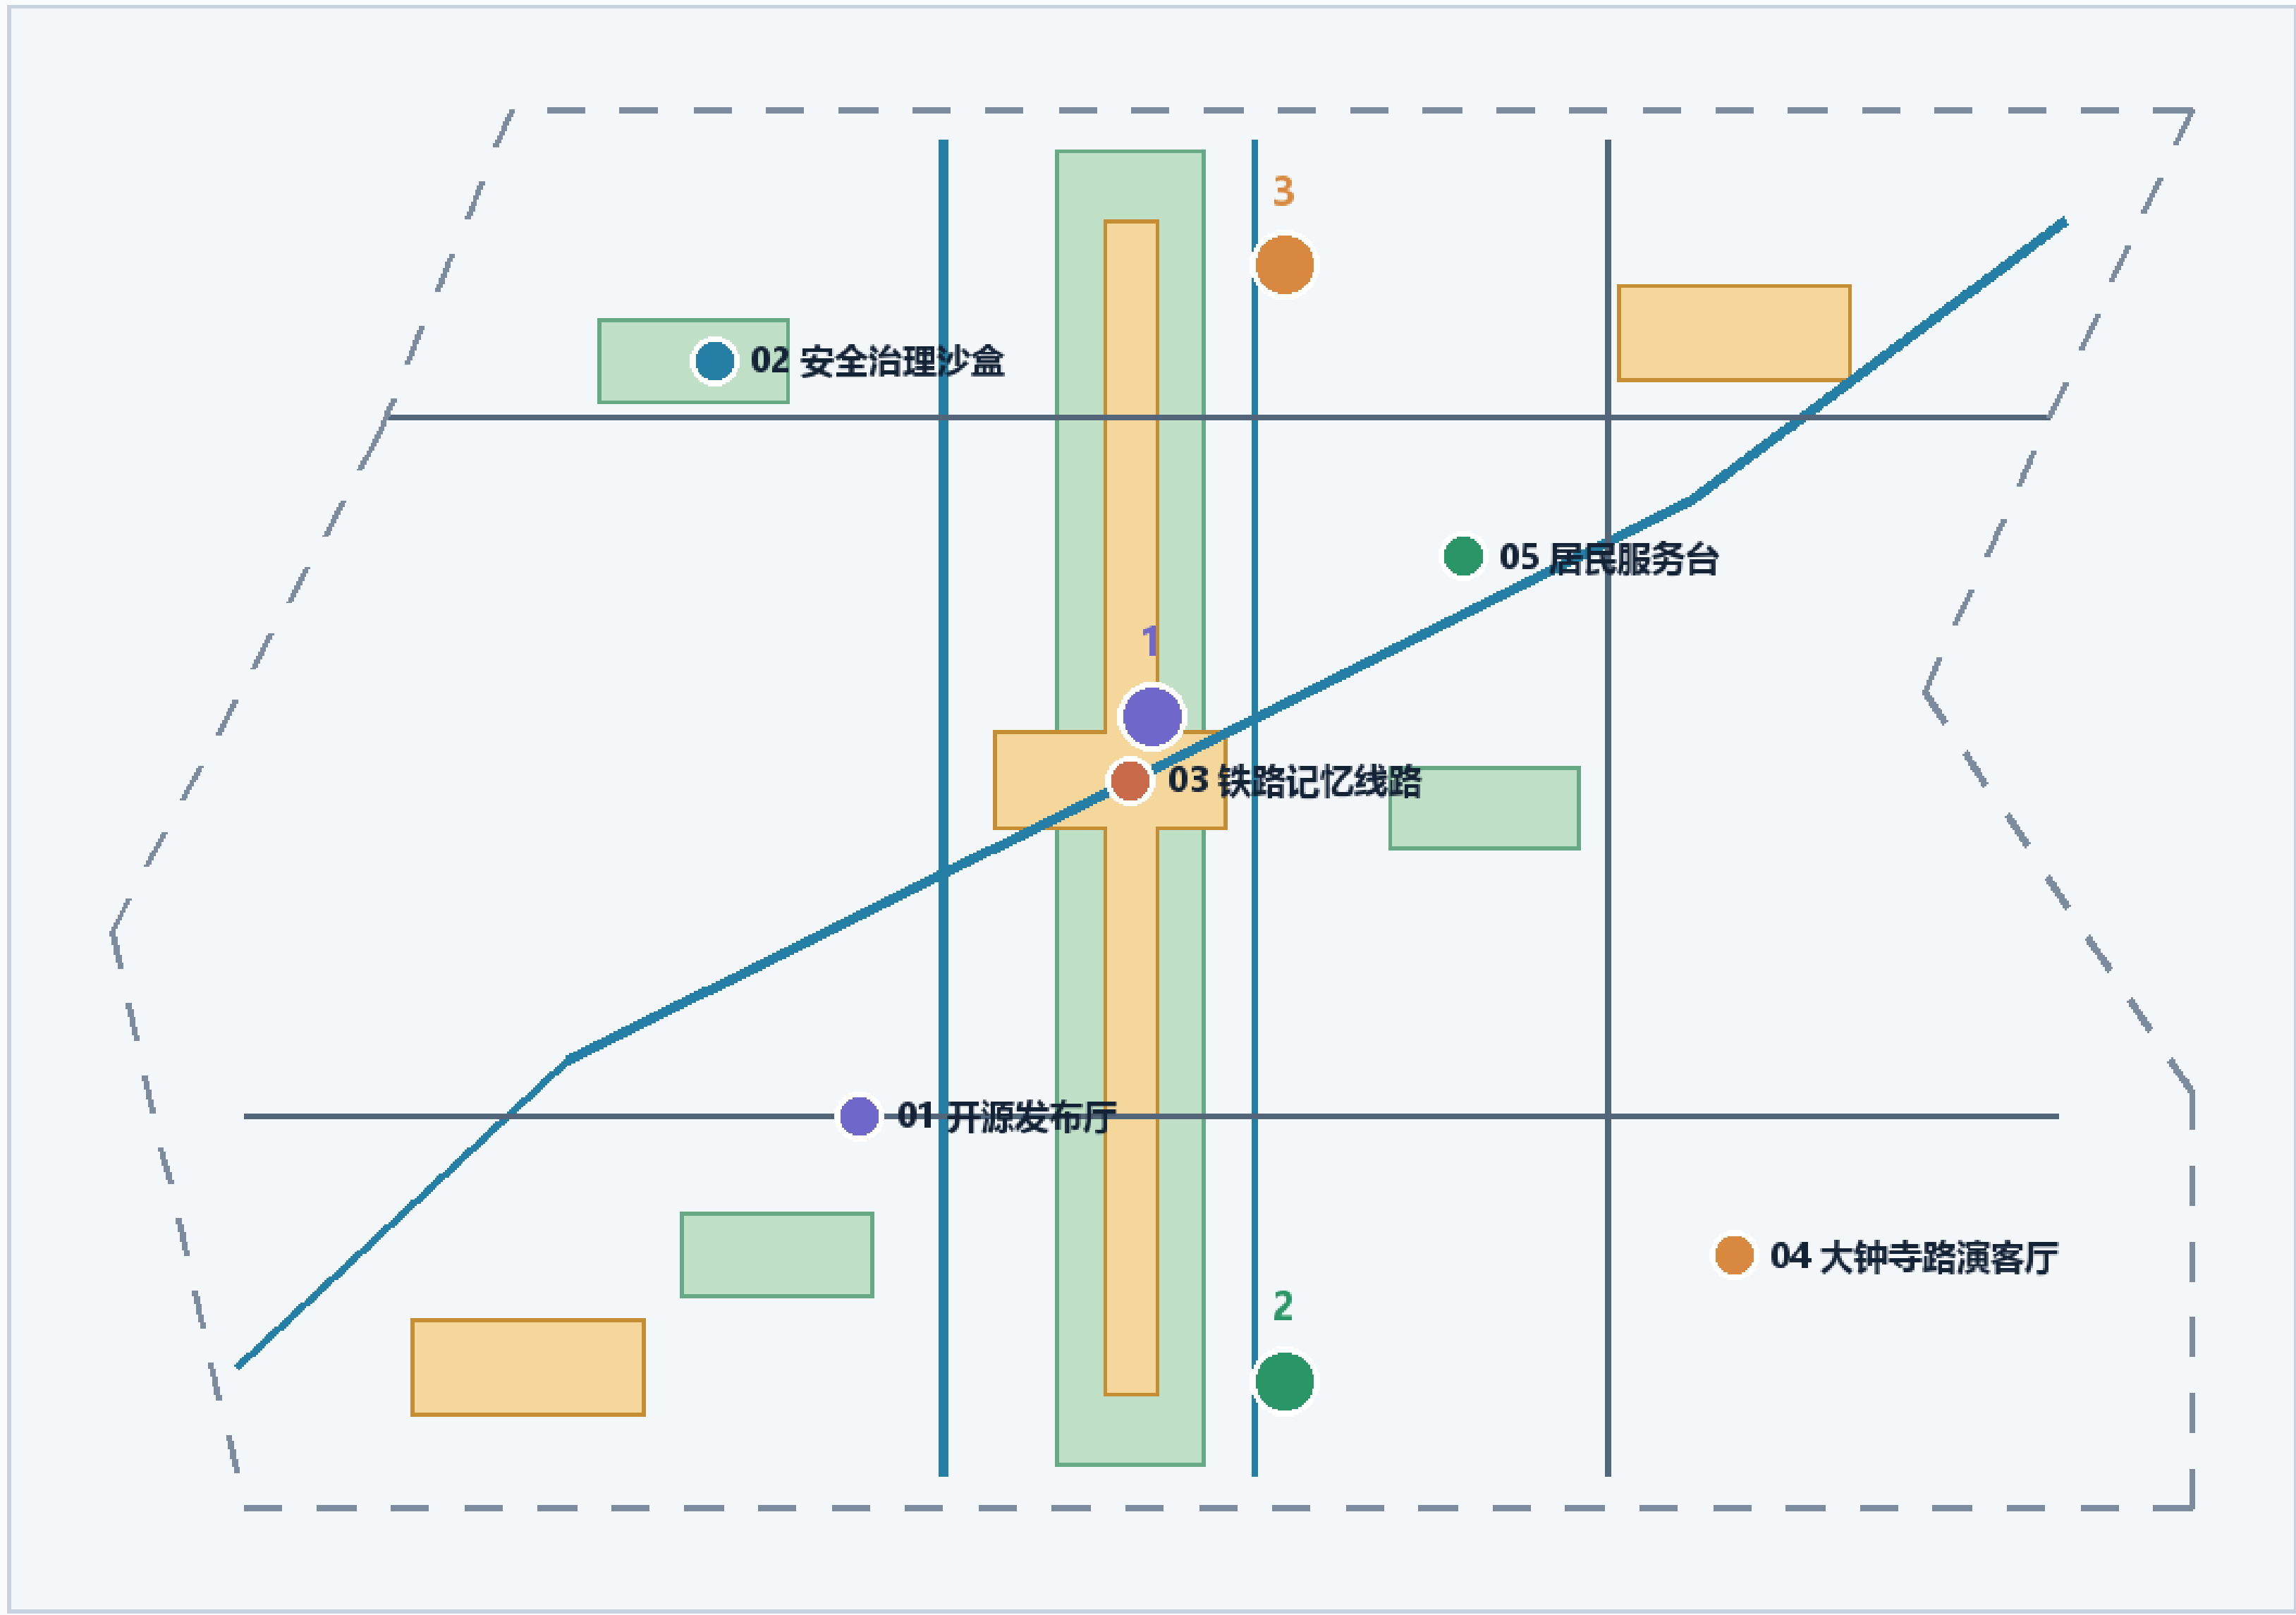

四层关系

- 站点接驳**
轨道接口与步行安全
- 慢行主环**
绿道、骑行、无障碍
- 公共验证**
场景预约与人工复核
- 社区服务**
不参与试验也能使用

概念边界

道路为中心线建议，不是红线；蓝绿面为公共空间概念网络。

交通与蓝绿图由 roads / green_space / public_space 同源派生；不包含远程底图。

PROVISIONAL INTAKE

用户与场景

五类用户画像、十张场景卡、三类产业测试场景；数据最小化、主动授权、人工复核和可撤回前置条件。

长期运营


春季开发预览、夏季公共开放日、秋季论坛、冬季公开评估为概念节点，需由运营团队深化。

概念建议 / provisional geometry / 供专业团队深化研究

每个空间判断都留有回程证据；未知项保持 unknown。

指标证据与复算关系

EPSG:4548 复算指标

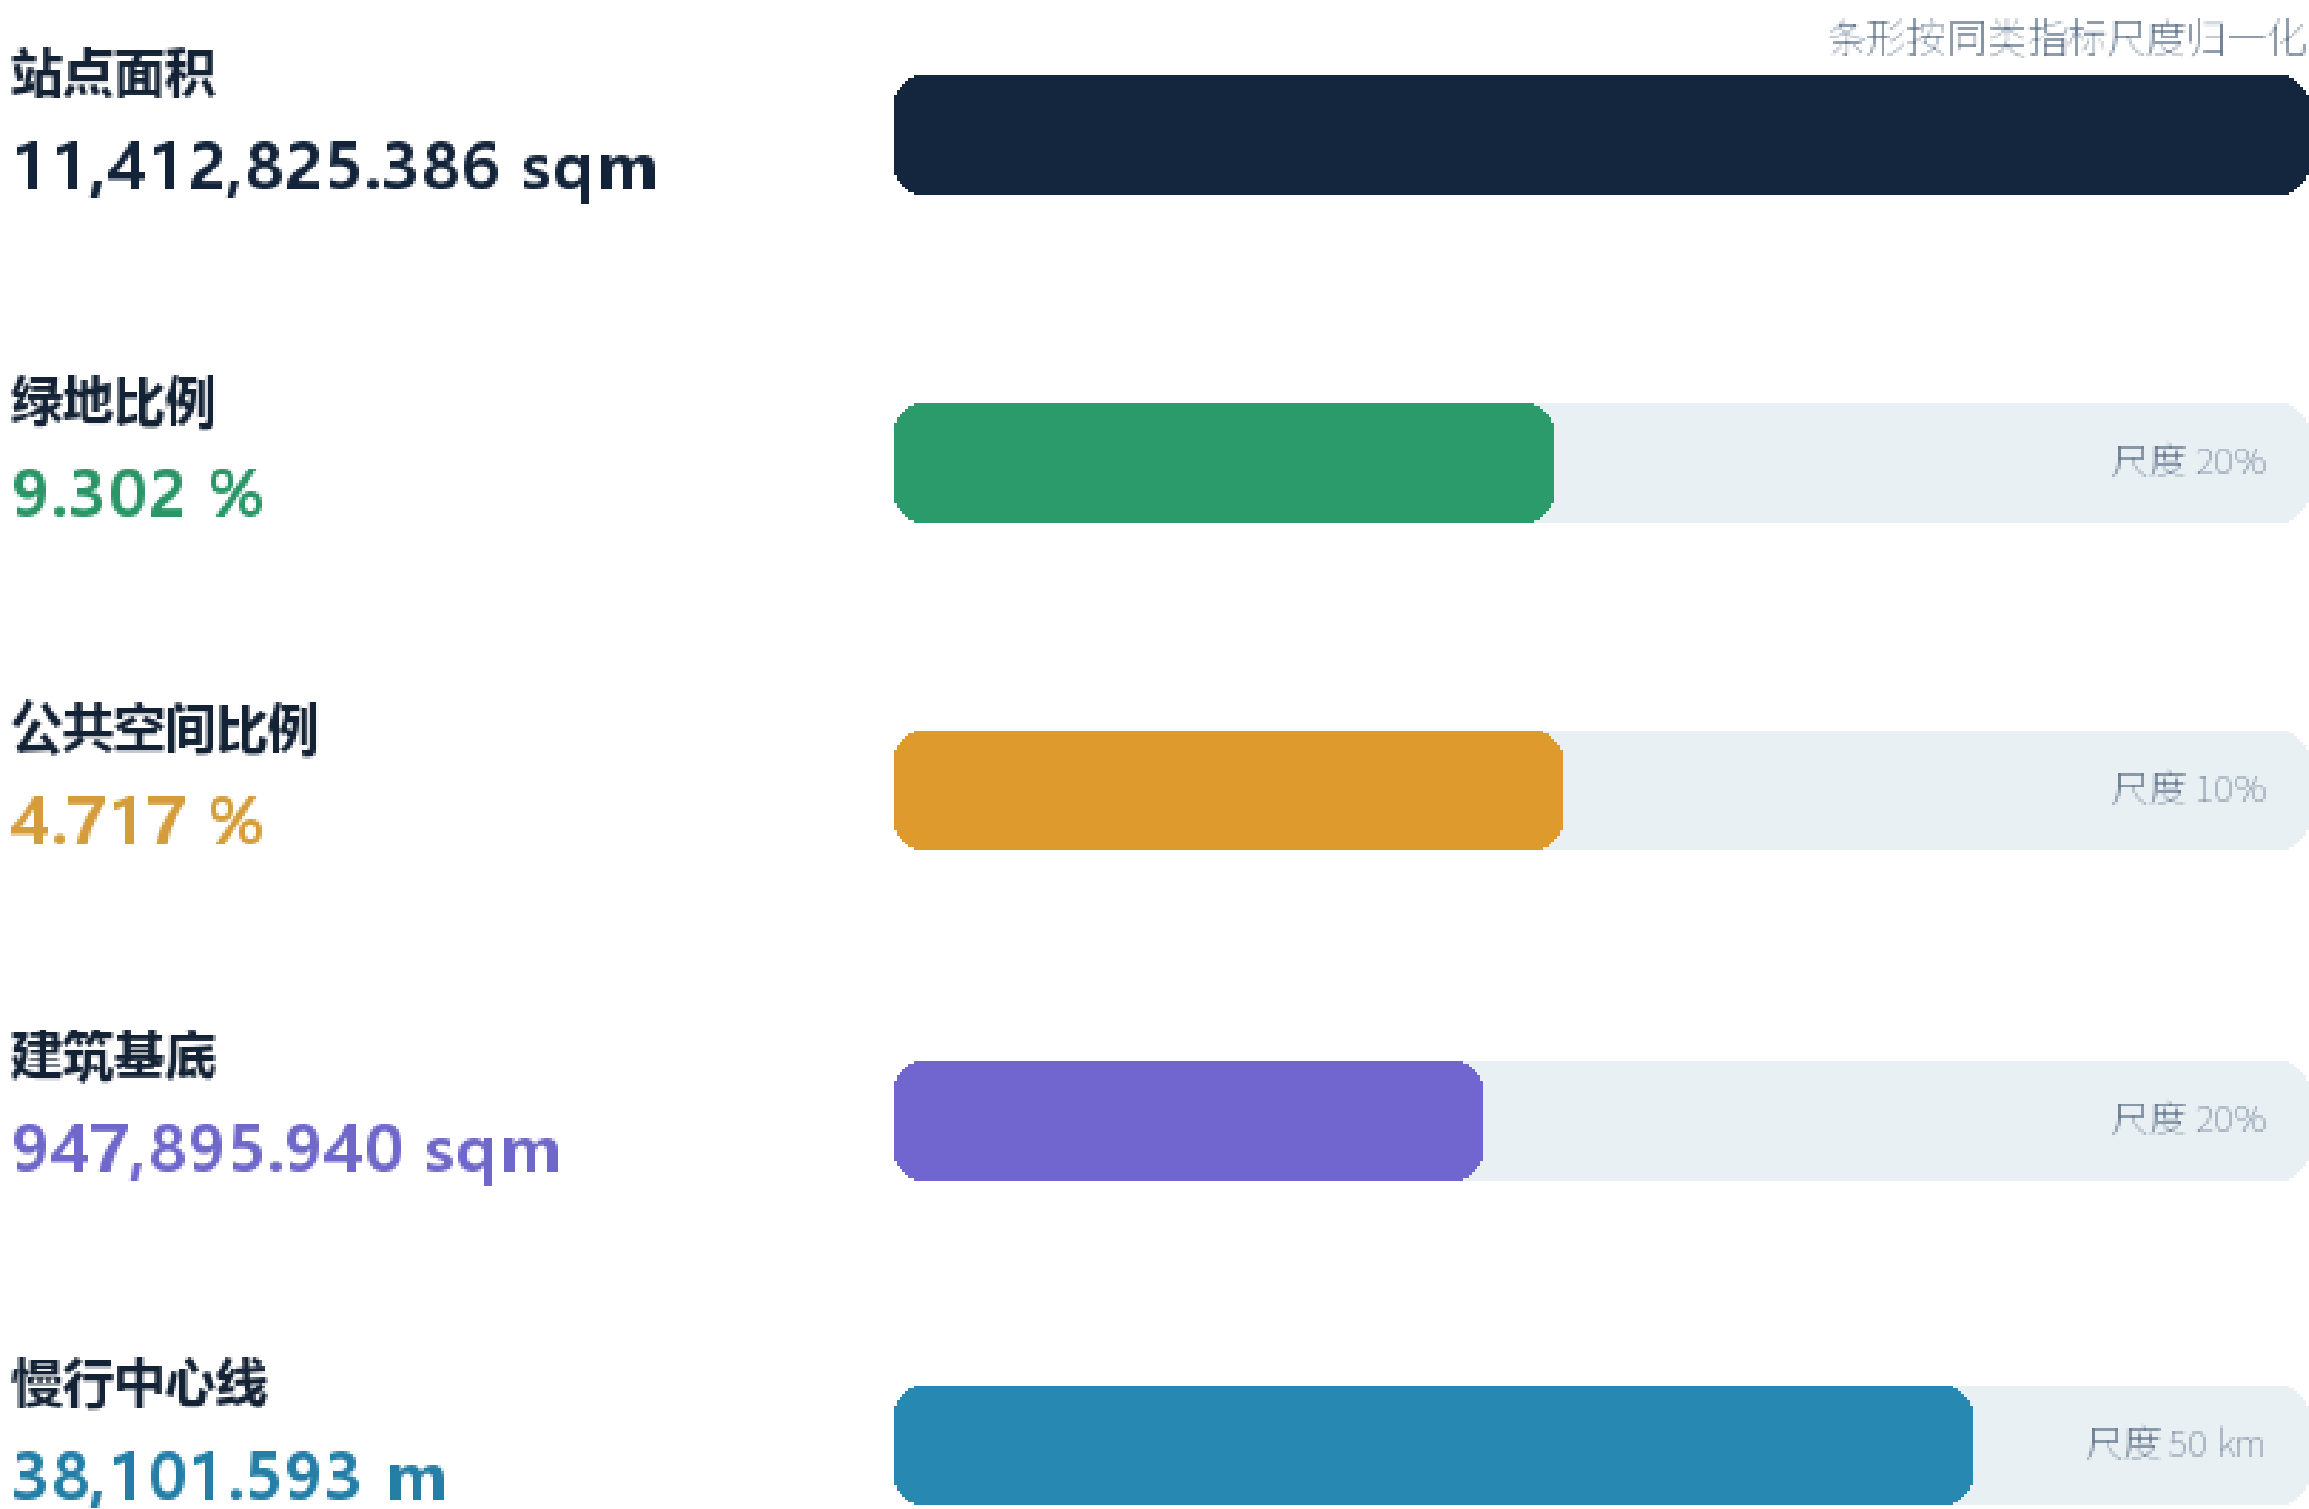

证据链

- 01 GeoJSON
边界、用地、建筑、道路、蓝绿、分期
- 02 metrics.json
面积、比例、长度与未知项
- 03 矩阵
任务、标准、深度与自检引用
- 04 图纸与HTML
给人类评审的解释层

FAR: unknown / 待正式控规与官方总楼面资料

条形采用同类语义尺度：绿地/建筑 20%，公共空间 10%，慢行 50 km；不是目标值。

PROVISIONAL INTAKE

核心指标

site_area_sqm 11,412,825.386; green_ratio 0.093021; public_space_ratio 0.047169; road_centerline_length_m 38,101.593.

合规状态

23 / 23 mandatory task mapped; 5 项专业标准 addressed.. 1 项 data gap; 15 / 15 design depth complete. provisional 警告不等同于官方批准。

概念建议 / provisional geometry / 供专业团队深化研究