



天枢智带 · 百年京张AI创新带 — 总体结构与用地

总体概念结构图 · 一廊三区两翼多节点

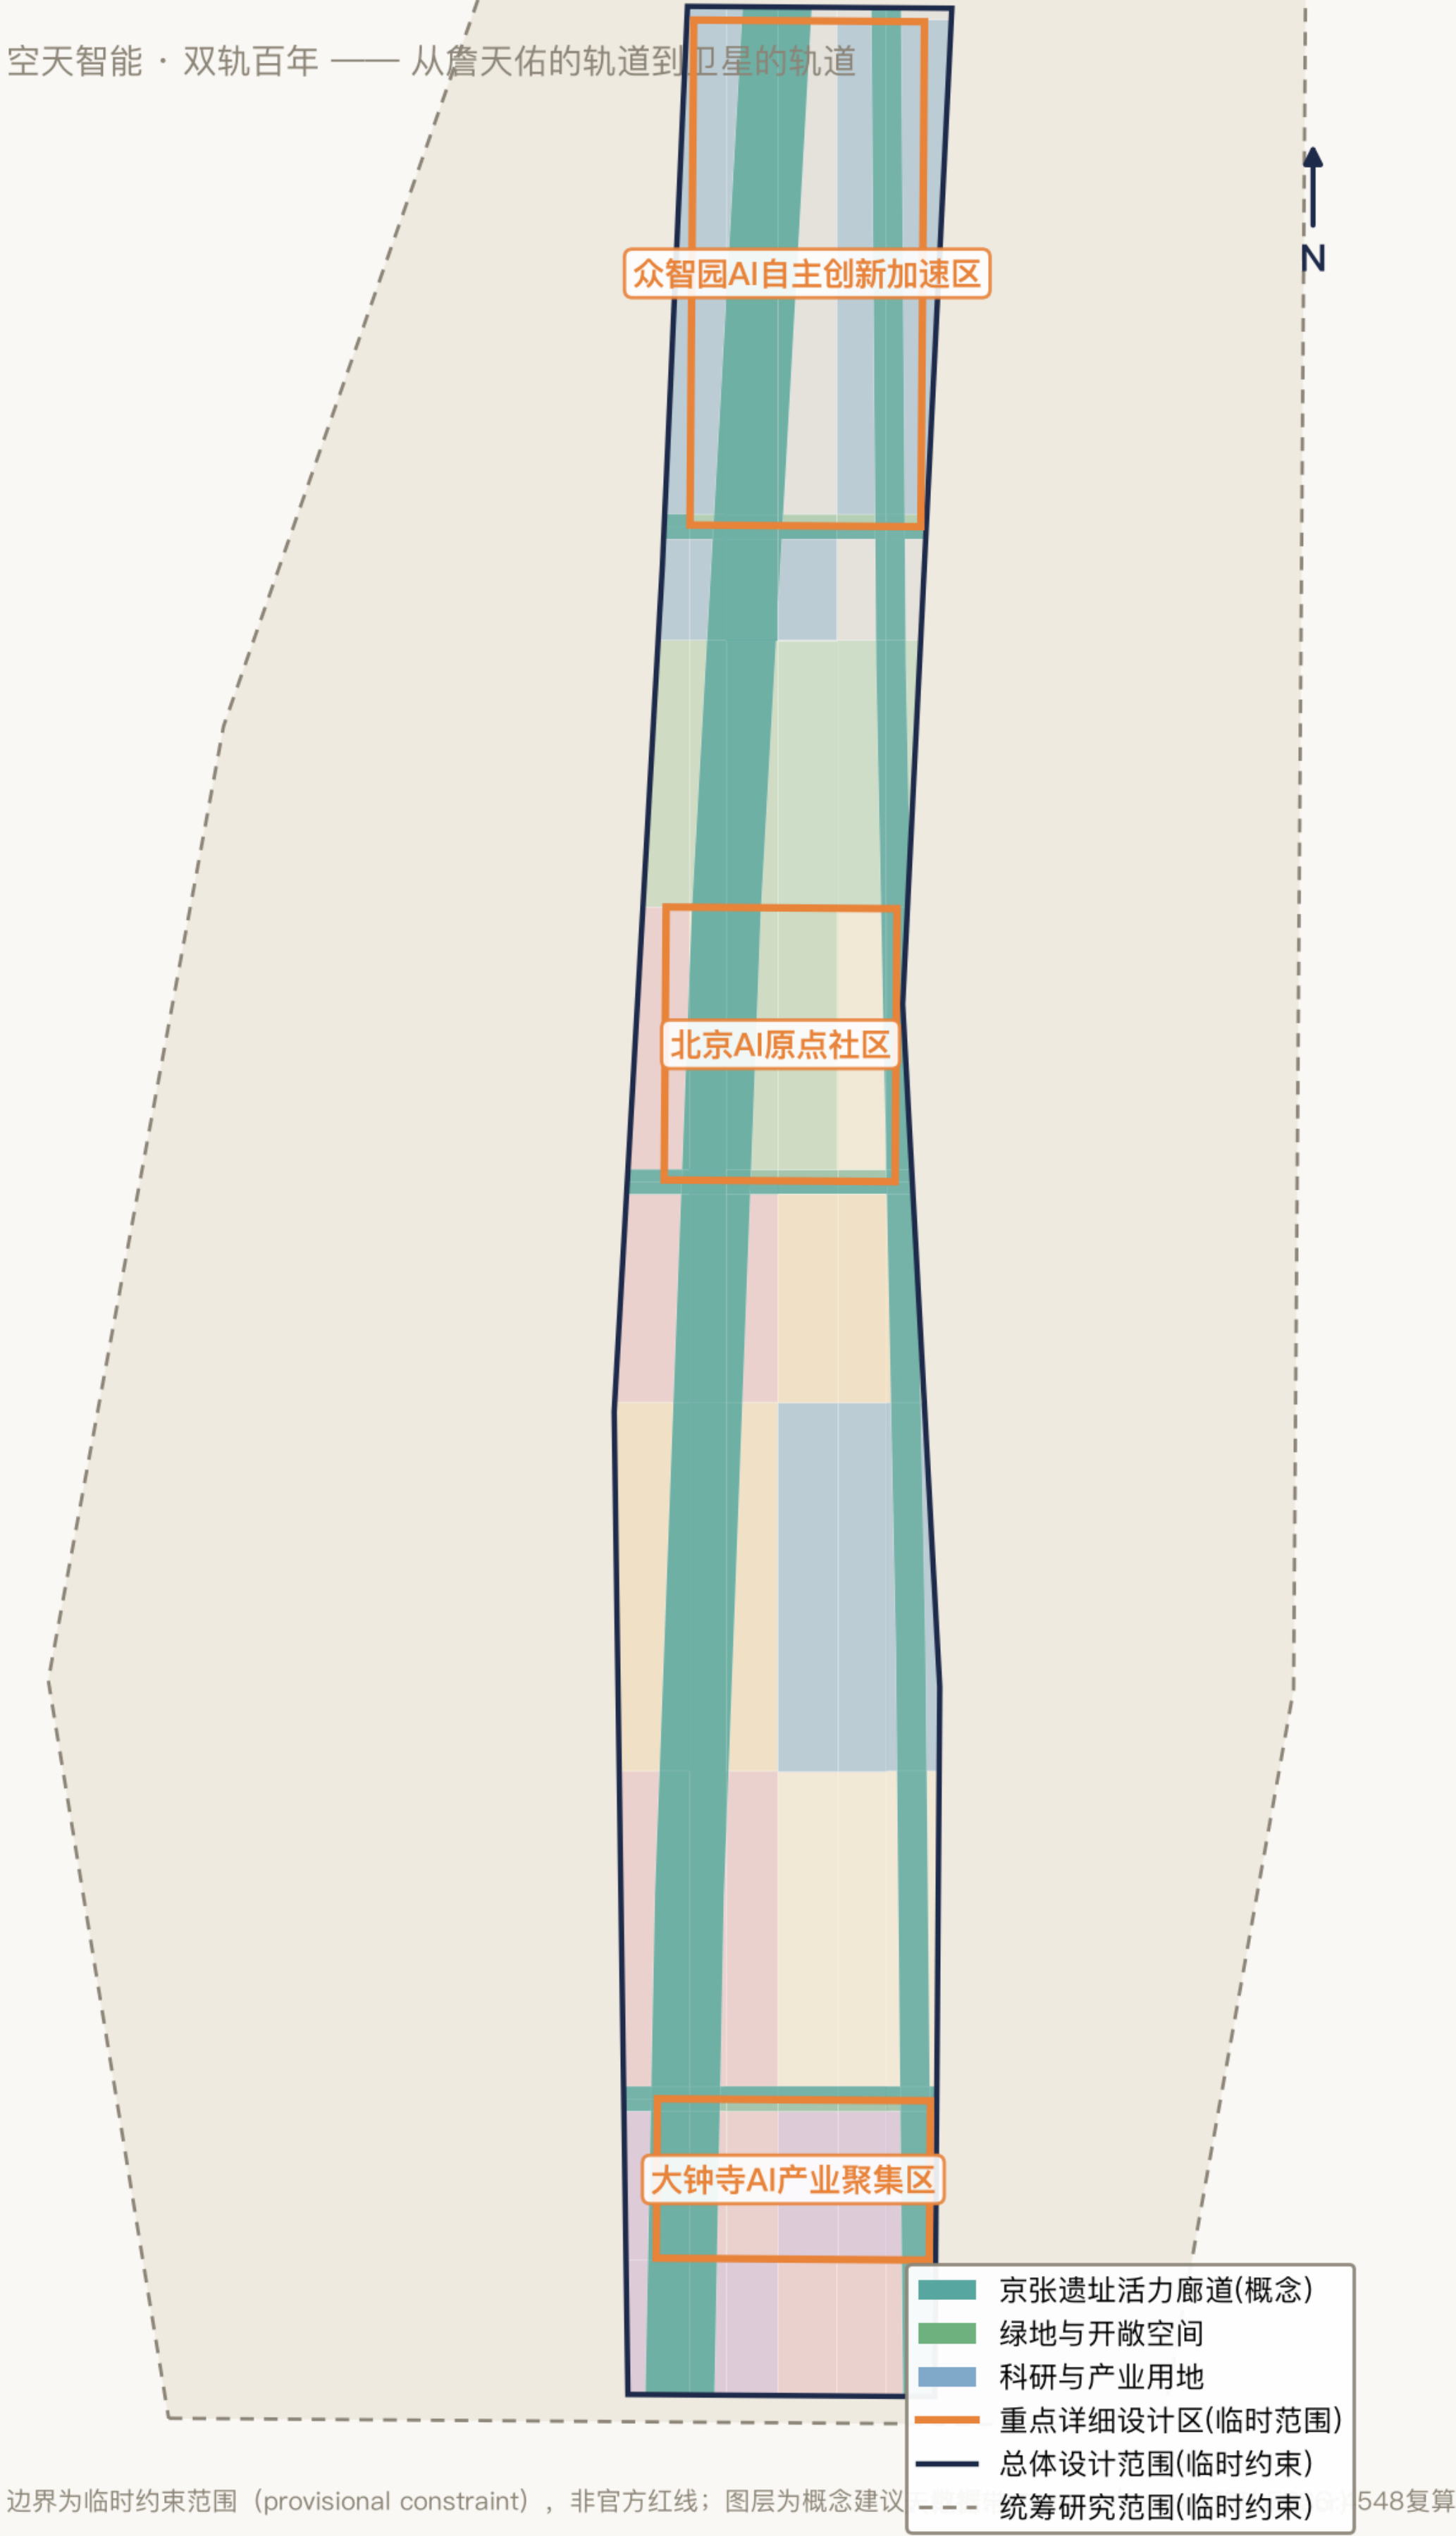

用地结构与空间传导图

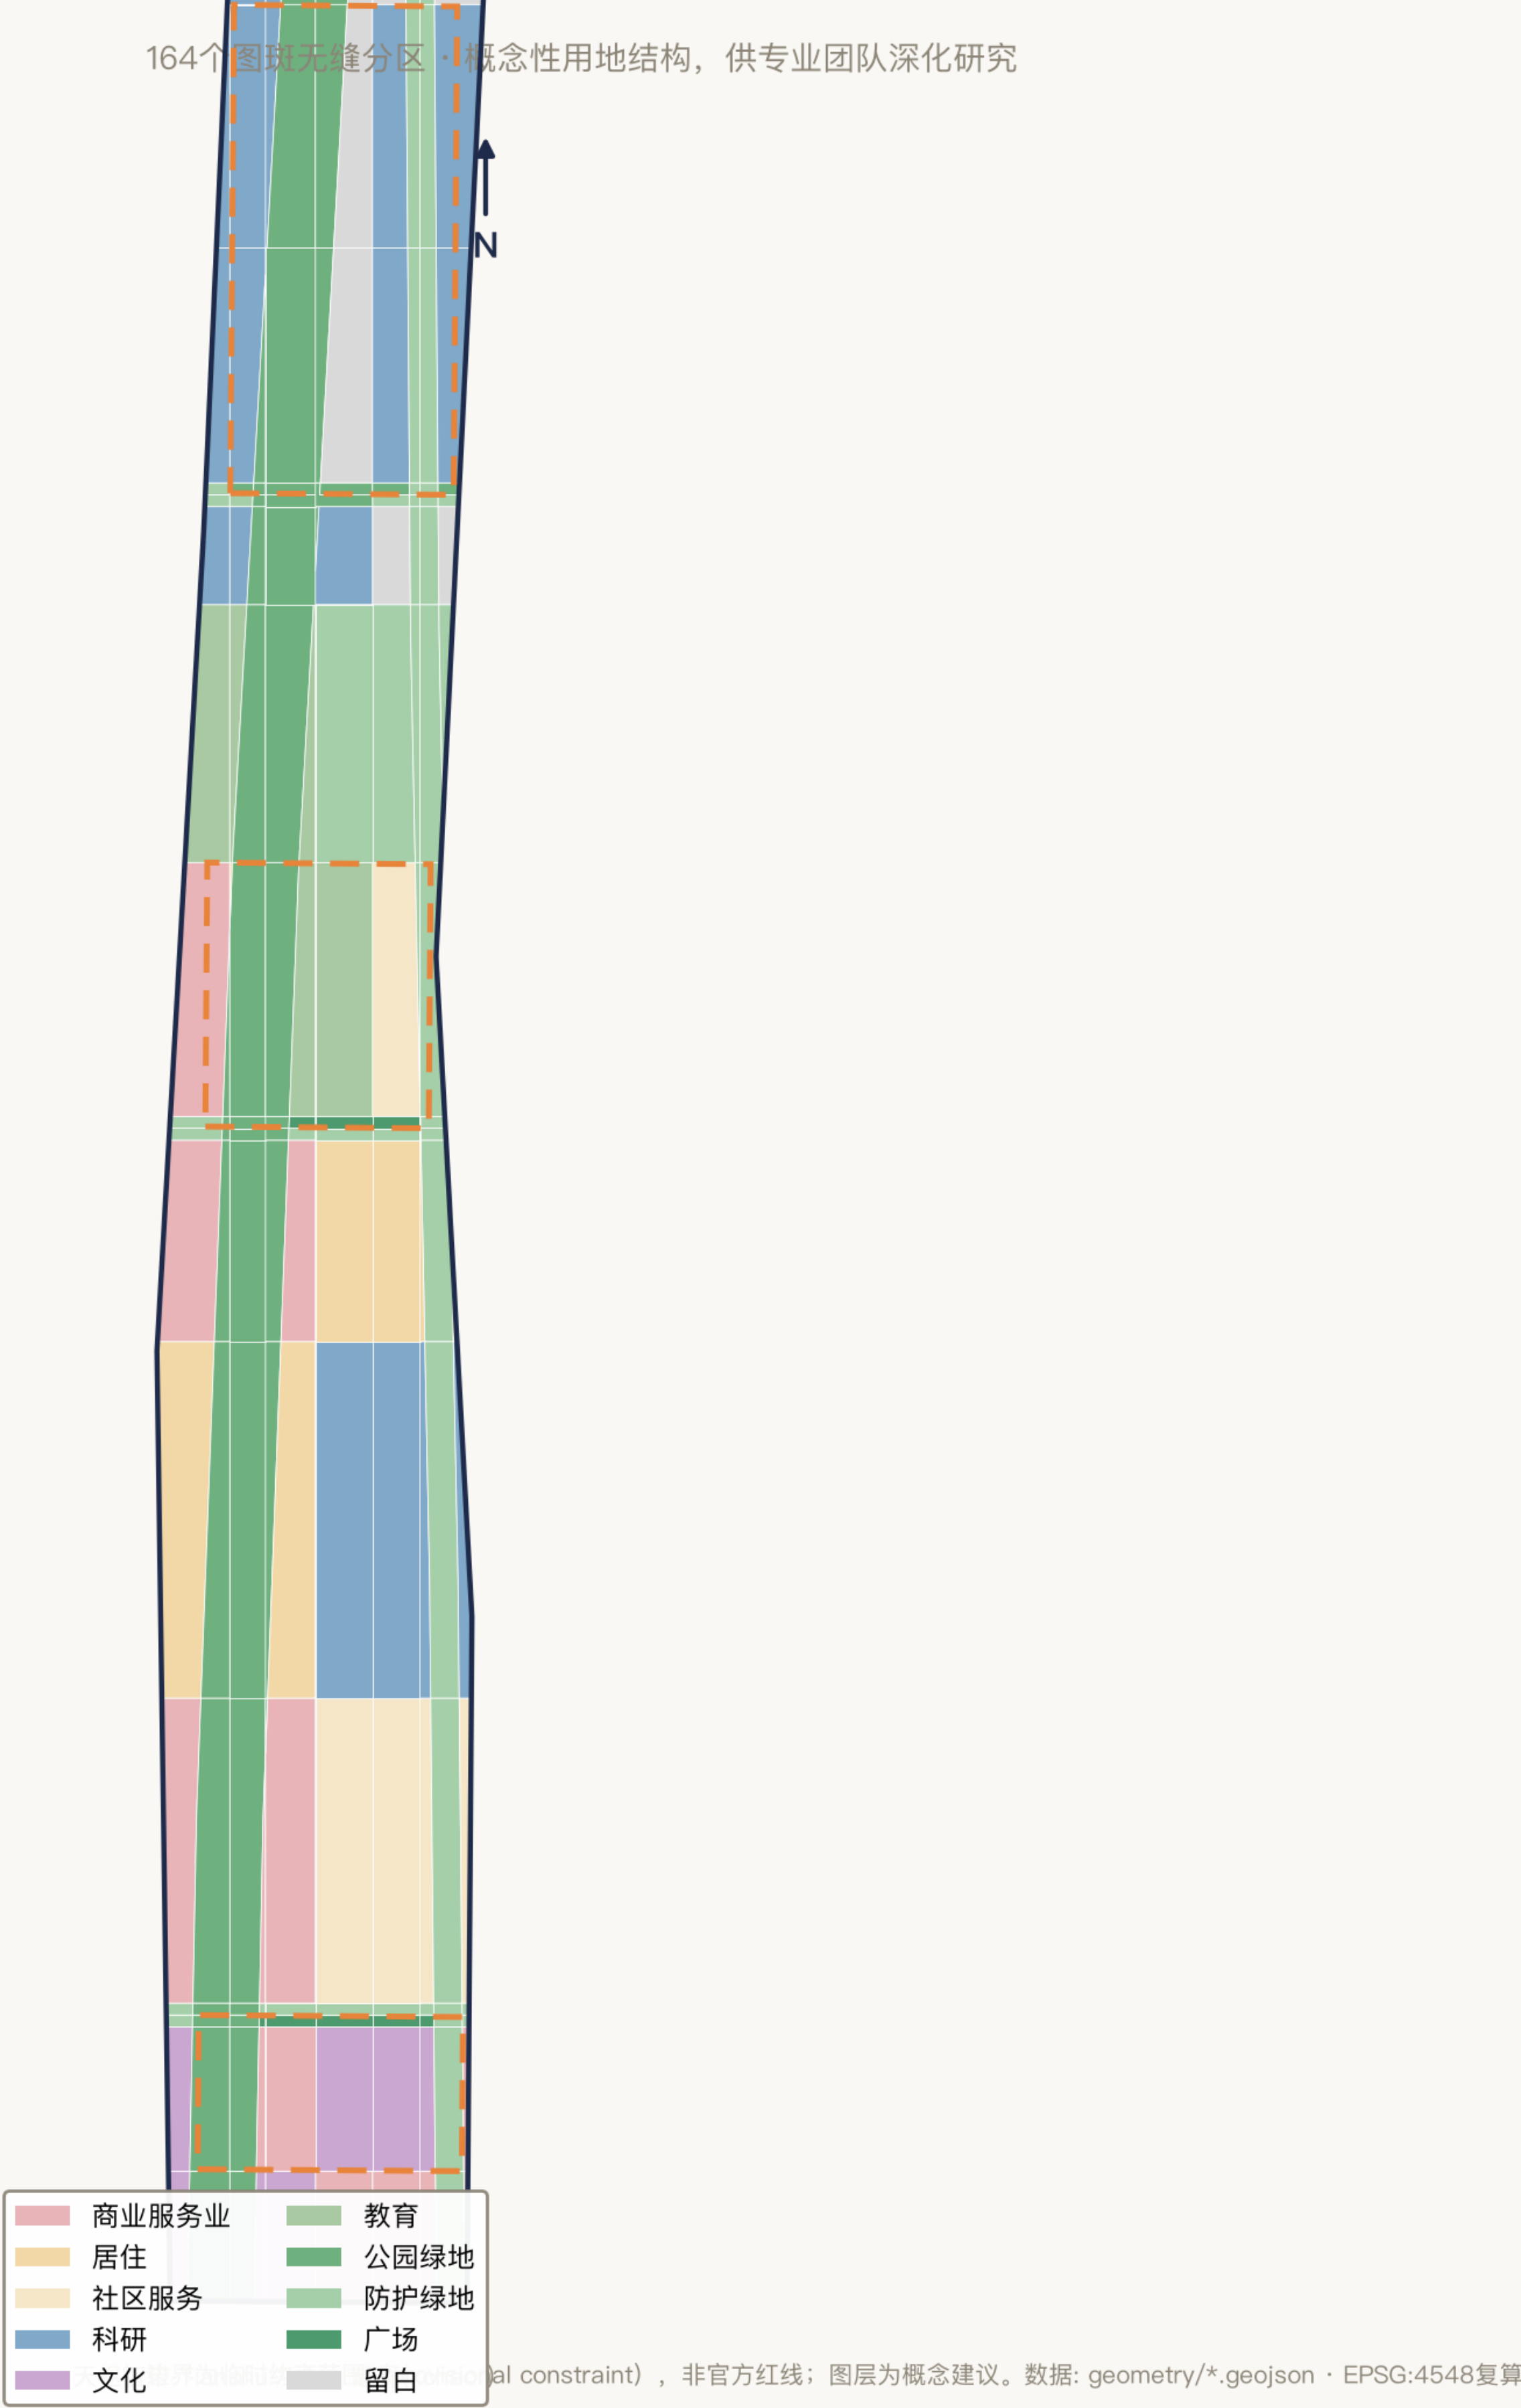


天枢智带 · 百年京张AI创新带 — 重点区与交通蓝绿


三处重点区域详细设计索引

定位差异 · 空间联系 · 概念项目抓手（临时范围，方向性设计）


众智园AI自主创新加速区

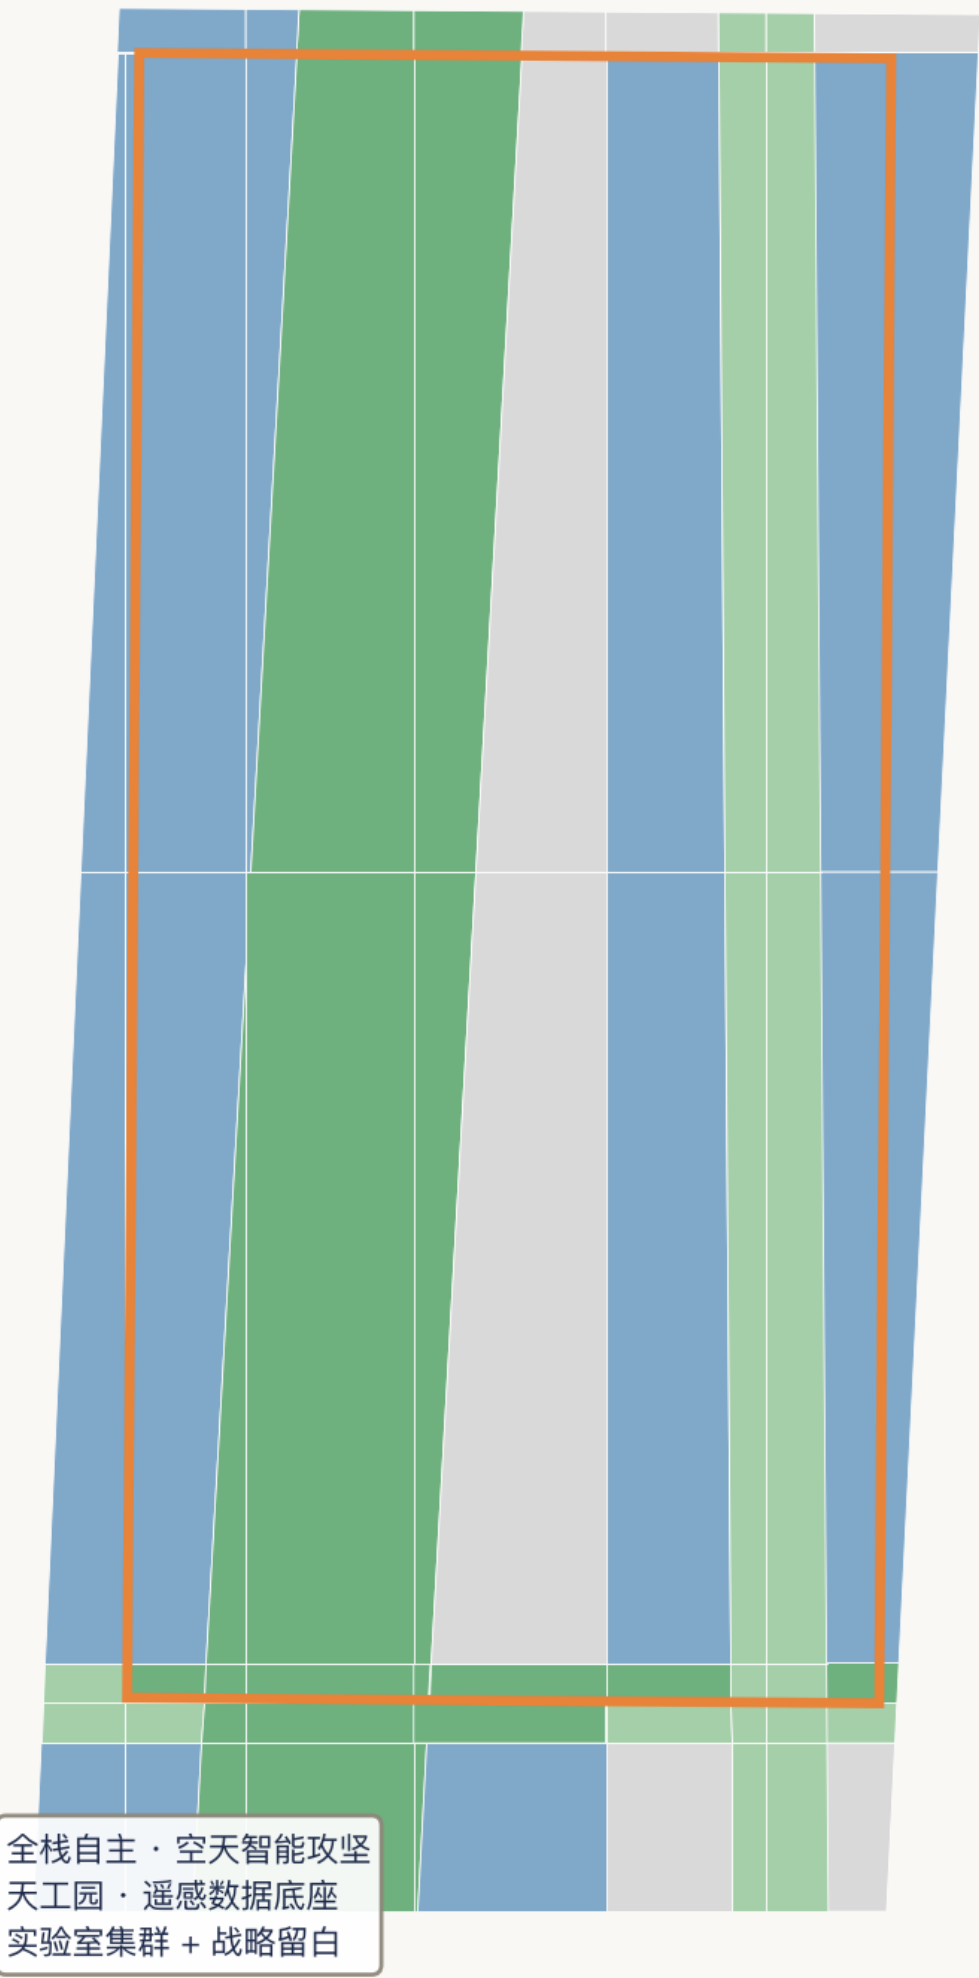

北京AI原点社区

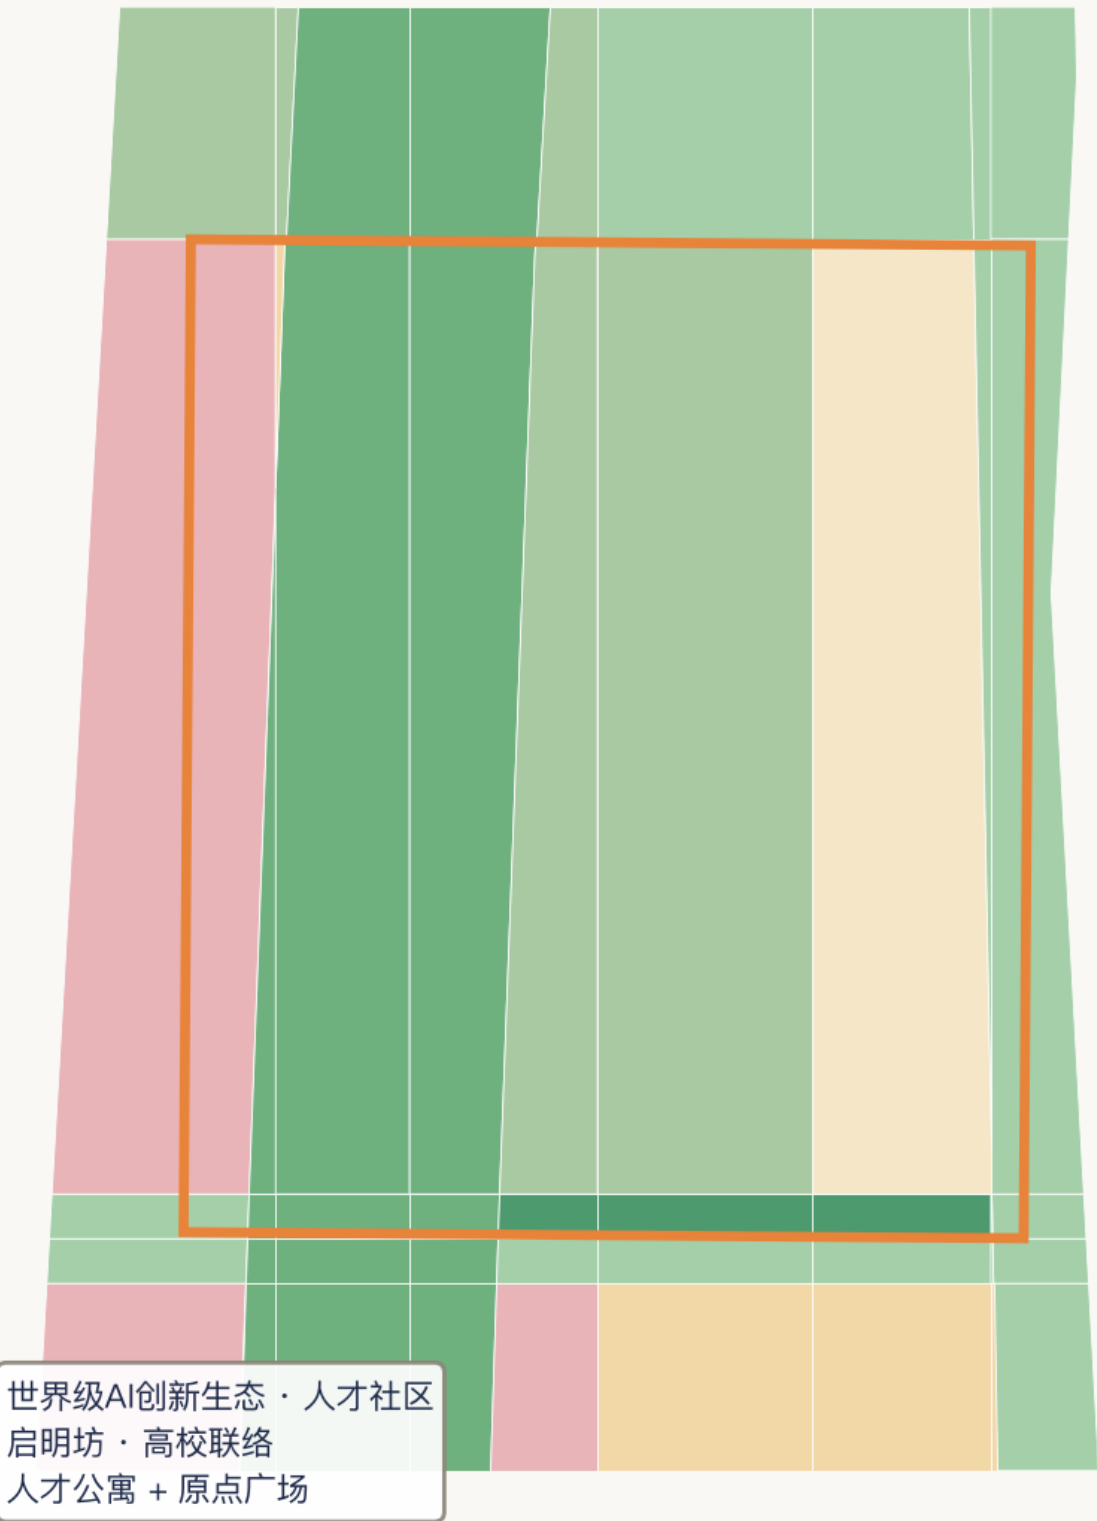


大钟寺AI产业聚集区

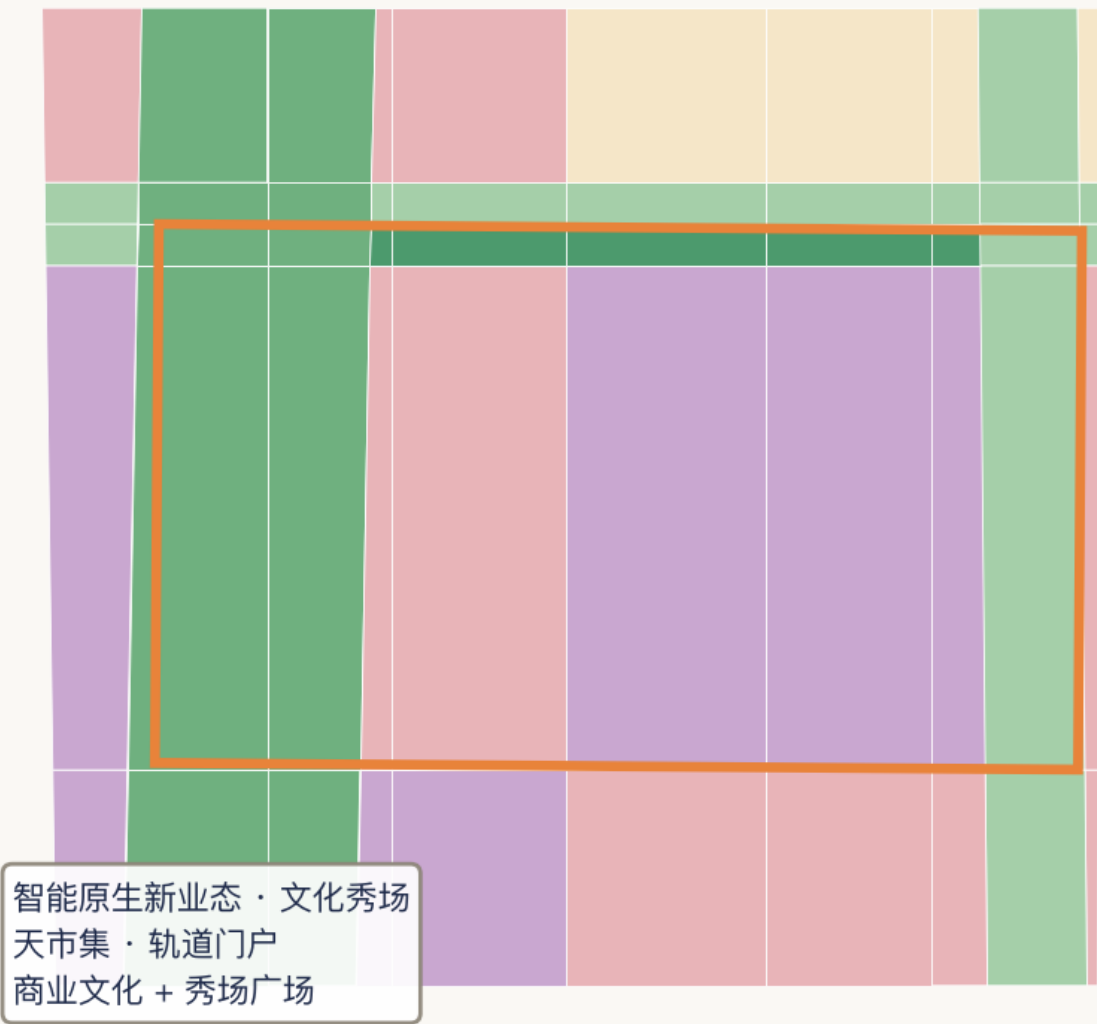

交通慢行与蓝绿公共空间复合系统


京张遗产廊道(开发者散步道) · 小月河滨水绿道 · 三条轨道接驳慢行道（概念线位）

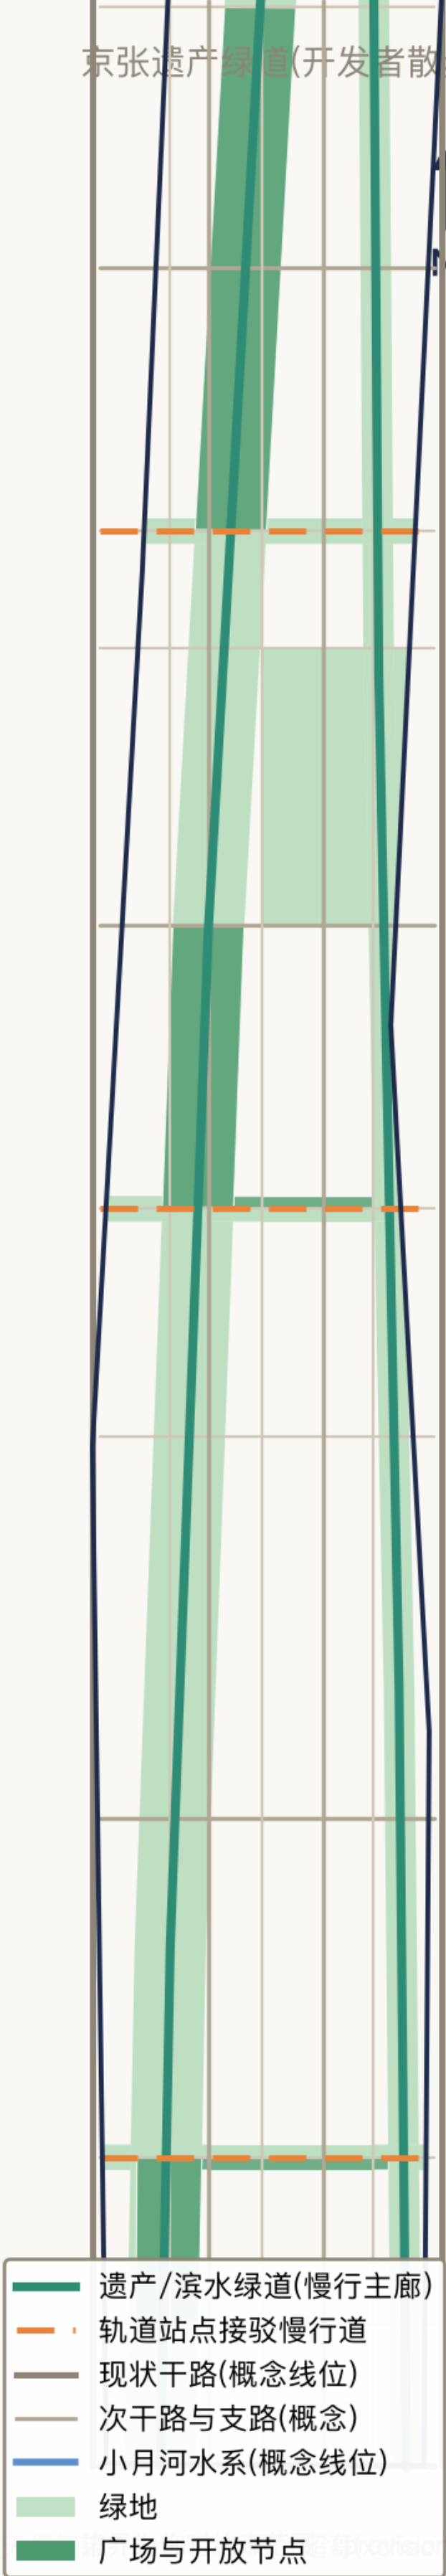

三个重点区均为临时约束范围（provisional constraint），公告面积约192.1/104.3/72.0公顷；详细设计为方向性概念建议。

核心指标复算与证据链

全部指标由 geometry/*.geojson 在 EPSG:4548 下复算 · 未知指标如实标注

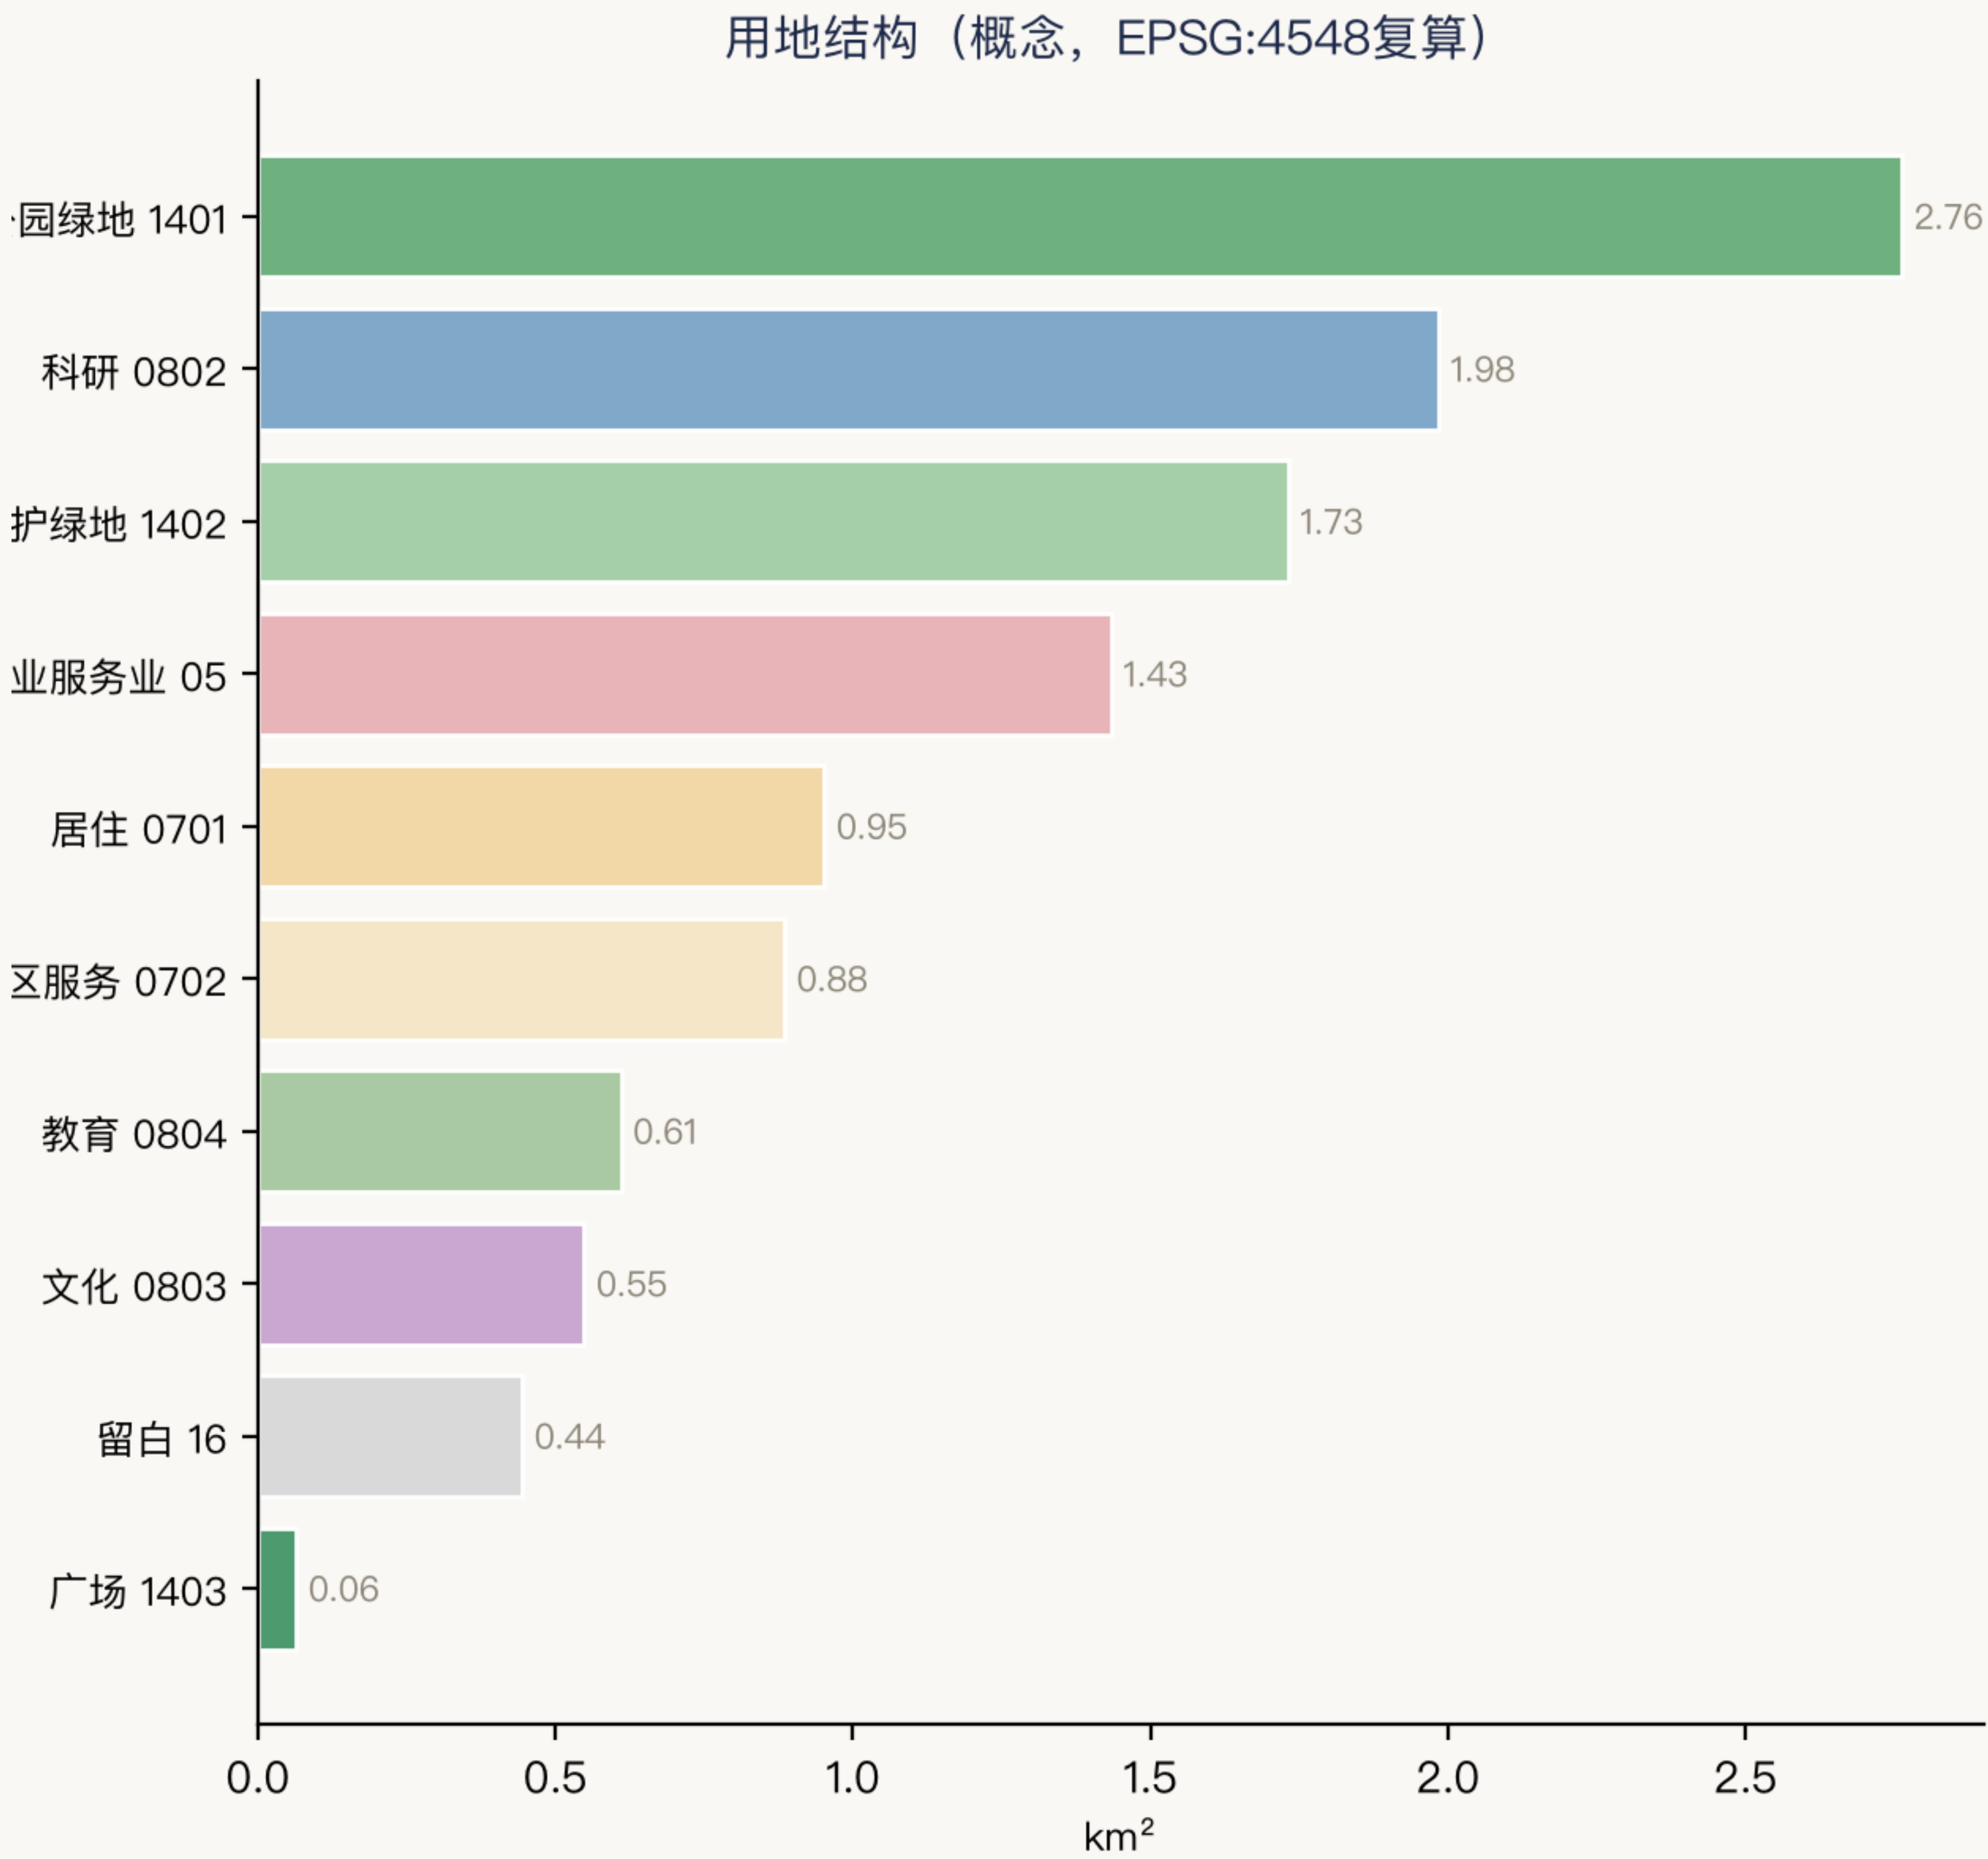

11.41 km²

总体设计范围面积

39.4%

绿地率(概念)

9.8%

公共空间比例

11.5%

建筑基底密度(概念)

3

重点详细设计区

106.9 km

道路中心线总长

待正式数据补齐 (unknown) :
容积率(floor_area_ratio) · 总建筑面积(total_floor_area_sqm) · 道路用地率(road_area_ratio)

复算前提: 获批控规条件 + 官方边界 polygon 发布后统一复算

证据链: GeoJSON图层 → EPSG:4548面积复算 → metrics.json → 本图; 图件为解释层, 权威数据以JSON/GeoJSON为准。