总图与总体概念 · 一轨三站两翼

总体概念图 · 一轨三站两翼

京张1435轨距带 · GAUGE 1435 —— 从标准轨距到 AI 标准接口

GAUGE 1435
轨距带

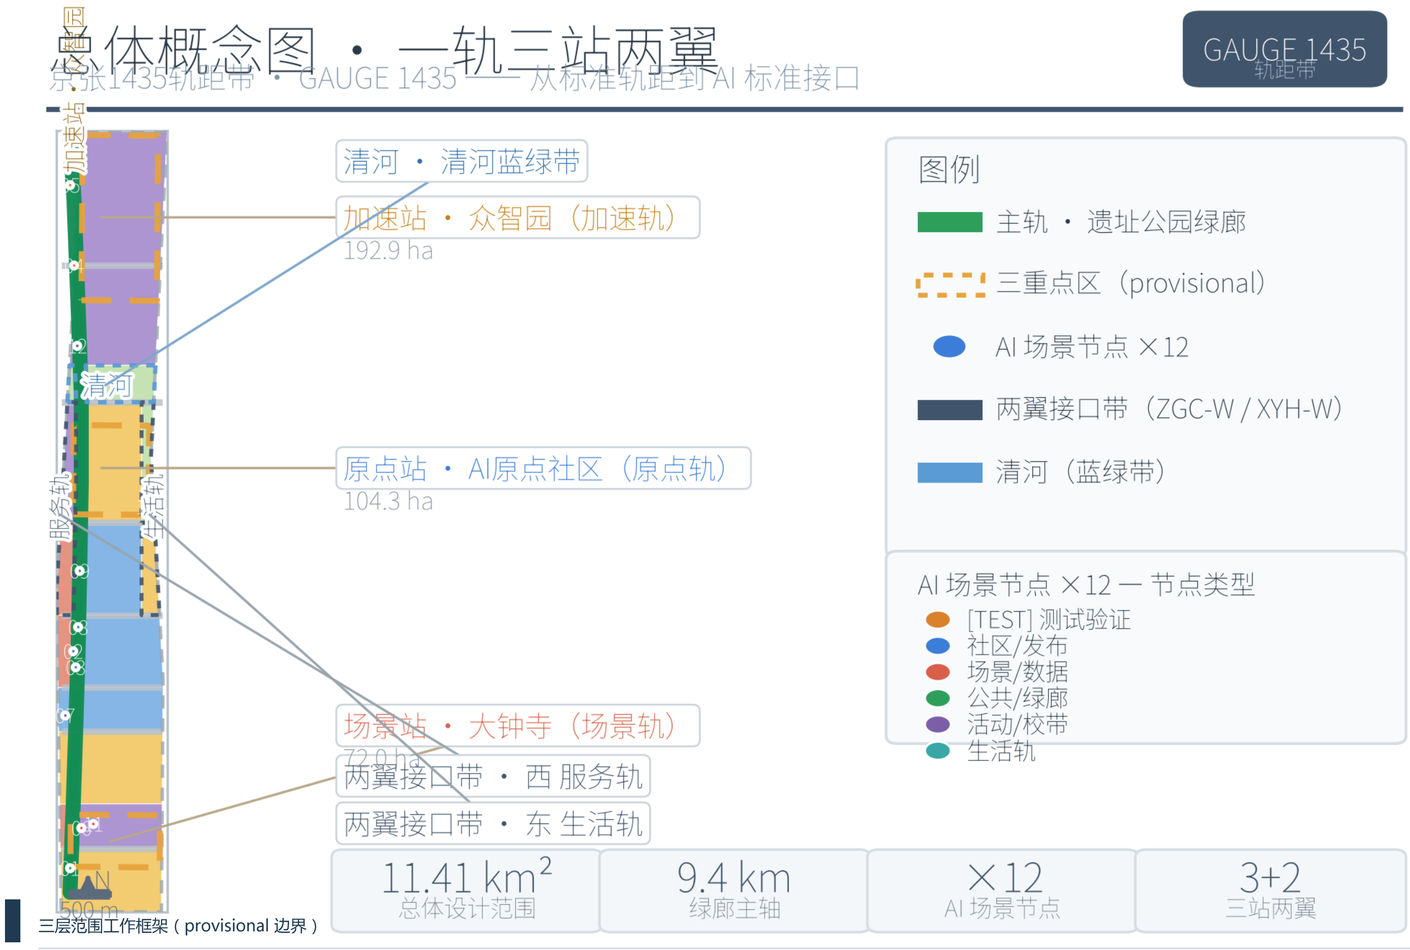

11.41 km² 总体设计范围	43.61 km² 统筹研究范围
368.4 ha 三区合计（重点区域）	9.4 km 绿廊主轴
27.9 km 概念道路网	164.9 ha 绿地面积
14.5% 绿地率	12 AI 场景节点

三层范围工作框架（provisional 边界）

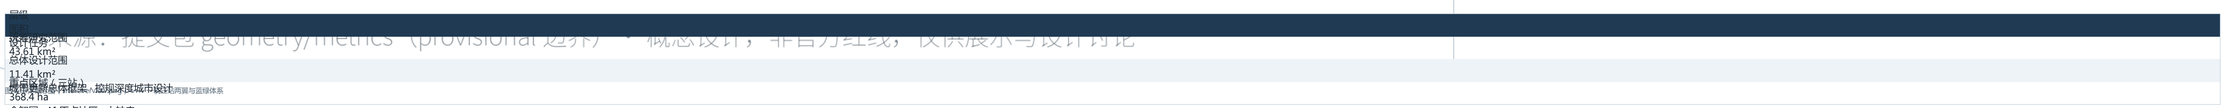

三区概览（重点区域 · 加速站 / 原点站 / 场景站）

众智园 · 加速站

面积：192.1 ha（provisional）
花园型全钱自主创新加速区（测试轨）；SN-004 测试场 · SN-005 沙盒 · SN-012 活动周

AI 原点社区 · 原点站

面积：104.3 ha（provisional）
近校型成果转化与开源人才社区（原点轨）；SN-002 轨距原点碑 · SN-003 发车站台 · SN-008 人才市集

大钟寺 · 场景站

面积：72.0 ha（provisional）
智能原生新业态与数据要素场景场（场景轨）；SN-006 体验街 · SN-011 会客厅 · SN-001 基准道

概念定位：标准即轨道、开源即路基、人才即列车；一轨三站两翼 · 五轨策略 · 12 张 AI 场景卡。所有面积基于 provisional 边界在 EPSG:4548 下复算，官方红线发布后需整包重算。

来源：提交包 geometry/metrics（provisional 边界）；概念设计，非官方红线，仅供展示与设计讨论。

三区详细设计（定位 / 空间 / 建筑 / 场景 / 风险）

三重点区索引图 · 加速站 / 原点站 / 场景站

京张1435轨距带 · GAUGE 1435 —— 从标准轨距到 AI 标准接口

GAUGE 1435 轨距带

总体范围上下文

① 加速站 · 众智园

192.9 ha · 1,929,202 m²（provisional）

AI 全栈自主创新加速区 · 加速轨

产业园块化布局 · 临清河界面 · 绿廊北段穿区

代表场景：SN-004 测试场 [TEST] · SN-005 沙盒 [TEST] · SN-012 活动周

清河蓝线/防洪与控规强度待确认

② 原点站 · AI原点社区

104.3 ha · 1,043,23… m²（provisional）

成果转化 · 开源人才社区 · 原点轨

校区-园区-街区慢行缝合 · PLZ-02 · 13号线接驳

代表场景：SN-002 原点碑 · SN-003 发布台 · SN-008 人才市集

校区边界/权属与文保要求待确认

③ 场景站 · 大钟寺

72.0 ha · 720,0… m²（provisional）

智能原生新业态 · 数据要素场景场 · 场景轨

四象限步行连通 · PLZ-01 · 商业核心+产业环

代表场景：SN-006 体验街 · SN-011 会客厅 · SN-001 基准道

轨道一体化/更新权属/风貌待确认

图例

用地分类　概念建筑

绿廊主轴　广场节点

场景节点

500 m

来源：提交包 geometry/metrics（provisional 边界） · 概念设计，非官方红线，仅供展示与设计讨论

① 众智园 · 加速站（192.1 ha）
定位：花园型全栈自主创新加速区——模型训练、评测、标准制定、安全治理的「测试轨」。
空间动作：临清河界面打开（QH 蓝绿带）、产业园区块化布局（ZZY 0802）、绿廊北段穿区。
建筑形态：中高层研发楼组团 + 实验厂房（concept massing，高度 12–60 m 概念示意）。
交通：北五环入口组织、绿廊绿道贯通、横向联络路接驳。
AI 场景：SN-004 加速轨测试场 · SN-005 安全治理沙盒 · SN-012 全球 AI 活动周北端节点。
实施风险：清河蓝线与防洪条件待确认、控规强度未定、权属未明。

② AI 原点社区 · 原点站（104.3 ha）
定位：近校型成果转化与开源人才社区——「从代码到产品」的原点。
空间动作：校区-园区-街区慢行缝合（ORIGIN-RD 0802 + ORIGIN-COM 05 + EDU-ORIGIN 0804）、成果发布与人才服务空间、原点站广场（PLZ-02）。
建筑形态：中低层街区式混合（办公 + 人才公寓 + 商业），首层开放。
交通：地铁 13 号线（概念示意线 RAIL-001）站点接驳、绿道慢行。
AI 场景：SN-002 轨距原点碑 · SN-003 发车站台 · SN-008 换轨人才市集。
实施风险：校区边界与权属待确认、文保（清华园站旧址相关）要求待官方图层。

③ 大钟寺 · 场景站（72.0 ha）
定位：智能原生新业态与数据要素的城市级场景场——「AI 被看见、被消费、被讨论」的地方。
空间动作：大钟寺站四象限步行连通（PLZ-01 站前广场）、商业核心（DZS-COM 05）+ 产业环（DZS-IND 0802）、绿廊南段穿区。
建筑形态：中高层商业综合体 + 智能终端旗舰店街区。
AI 场景：SN-006 智能终端体验街 · SN-011 数据要素会客厅 · SN-001 1435 无障碍慢行基准道南端。
实施风险：轨道站点一体化条件、商业更新权属、文保与风貌控制待确认。

图 2 三处重点区域索引与设计任务图（key-areas.png）

实施分期（概念）与运营

阶段	内容
近期 Near (0–2 yr)	PHASE-001
中期 Mid (2–5 yr)	PHASE-002
远期 Far (5–10 yr)	PHASE-003

PHASE-001 4,980,003 m² (479.8 ha)
PHASE-002 4,943,737.5 m² (494.4 ha)
PHASE-003 …
运营点：…
中段居住与两翼接口。留白
年度活动：春「接轨周」· 夏「发车季」· 秋「轨距大会 · 全球 AI 活动周」· 冬「让轨节」。
品牌 IP：GAUGE 1435 视觉系统 + 轨枕刻度带 + 信号色（绿 / 琥珀 / 白）。
开发者社区：开源发布站台 · 贡献者荣誉墙 · PR/Issue 文化。
场景开放运营：测试场与沙盒预约制 · 人工复核 · 数据最小化。
转化路径：活动 → 社区 → 孵化 → 加速 → 场景 → 全球发布。

交通慢行与蓝绿空间 · 用地结构

交通慢行与蓝绿网络图

京张1435轨距带 · GAUGE 1435 —— 从标准轨距到 AI 标准接口

GAUGE 1435 轨距带

北五环路（概念示意）

京张高铁走廊（概念示意）

学院路/西土城路（概念示意）

清河

绿廊绿道

绿地地铁13号线（概念示意）

N

500 m

图例

绿廊绿道（绿廊主轴 9.4 km）
设计道路网（9 条 · 27.9 km）
地铁13号线（概念示意）
京张高铁走廊（概念示意）
北五环路（概念示意） / 学院路/西土城路（概念示意）
广场节点（3 组）
清河（蓝绿空间）
小月河（生活轨蓝绿带）
AI 场景节点 ×12

27.9 km	9.4 km	165 万 m²	4.3 万 m²	9 条
慢行/道路网络	绿廊主轴	绿地	广场占比	道路

站点接驳与分期

- 原点站：地铁13号线接驳，绿道直达站前广场（PLZ-02）
- 场景站：大钟寺站四象限步行连通（PLZ-01）
- 加速站：北五环入口 + 绿廊北段，横向联络路接驳

分期（概念）

PH-1 · 209 ha	PH-2 · 480 ha	PH-3 · 494 ha
0-2年	2-5年	5-10年

来源：提交包 geometry/metrics（provisional 边界） · 概念设计，非官方红线，仅供展示与设计讨论

用地结构图 · 七大功能分区

京张1435轨距带 · GAUGE 1435 —— 从标准轨距到 AI 标准接口

GAUGE 1435 轨距带

ZZY

QH

ZGC-W

XYH-W

SPINE

ORIGIN

DZS-I

N

500 m

图例 — 用地分类

商业（05） 453,060 m² · 3.97%
居住（0701） 3,211,295 m² · 28.14%
科研/产业（0802） 3,725,088 m² · 32.64%
教育（0804） 2,331,086 m² · 20.42%
公园绿地（1401） 1,011,754 m² · 8.86%
防护绿地（1402） 637,543 m² · 5.59%
广场（1403） 43,000 m² · 0.38%

面积占比

产业相关（0802 科研 + 05 商业）≈ 36.6%

结构要点

- 科研/产业 0802 为最大类别（32.6%），沿绿廊成带
- 居住 0701 与教育 0804 分段织入中南部
- 绿廊（1401）+ 防护（1402）+ 广场（1403）构成蓝绿骨架
- 西服务轨（ZGC-W）与东生活轨（XYH-W）两翼呼应

功能带名称

ZZY	众智园 AI 加速区	QH	清河蓝绿带
ORIGIN	原点社区商业/教育	DZS-C/I	大钟寺核心 / 产业环
ZGC-W	服务轨接口带（西）	XYH-W	生活轨接口带（东）
EDU-C/N	高校园区 / 教育带	SPINE	遗址公园绿廊
RES-S/M/N	南 / 中 / 北居住区		

来源：提交包 geometry/metrics（provisional 边界） · 概念设计，非官方红线，仅供展示与设计讨论

图 4 交通慢行与蓝绿公共空间复合系统图（mobility-bluegreen.png）

图 3 用地结构图（land-use-structure.png）

来源：提交包 geometry/metrics（provisional 边界）；概念设计，非官方红线，仅供展示与设计讨论。