


百年京张 AI 创新带 · 空间结构板

三层范围 — 用地结构 — 重点区 — 交通与蓝绿 | 全部几何为临时约束 (provisional)，非官方红线；权威数据以 metrics.json 为准

资料证据链与提交包关系图

百年京张AI创新带 · 总体设计范围 (临时边界)

FIG-01 / 05

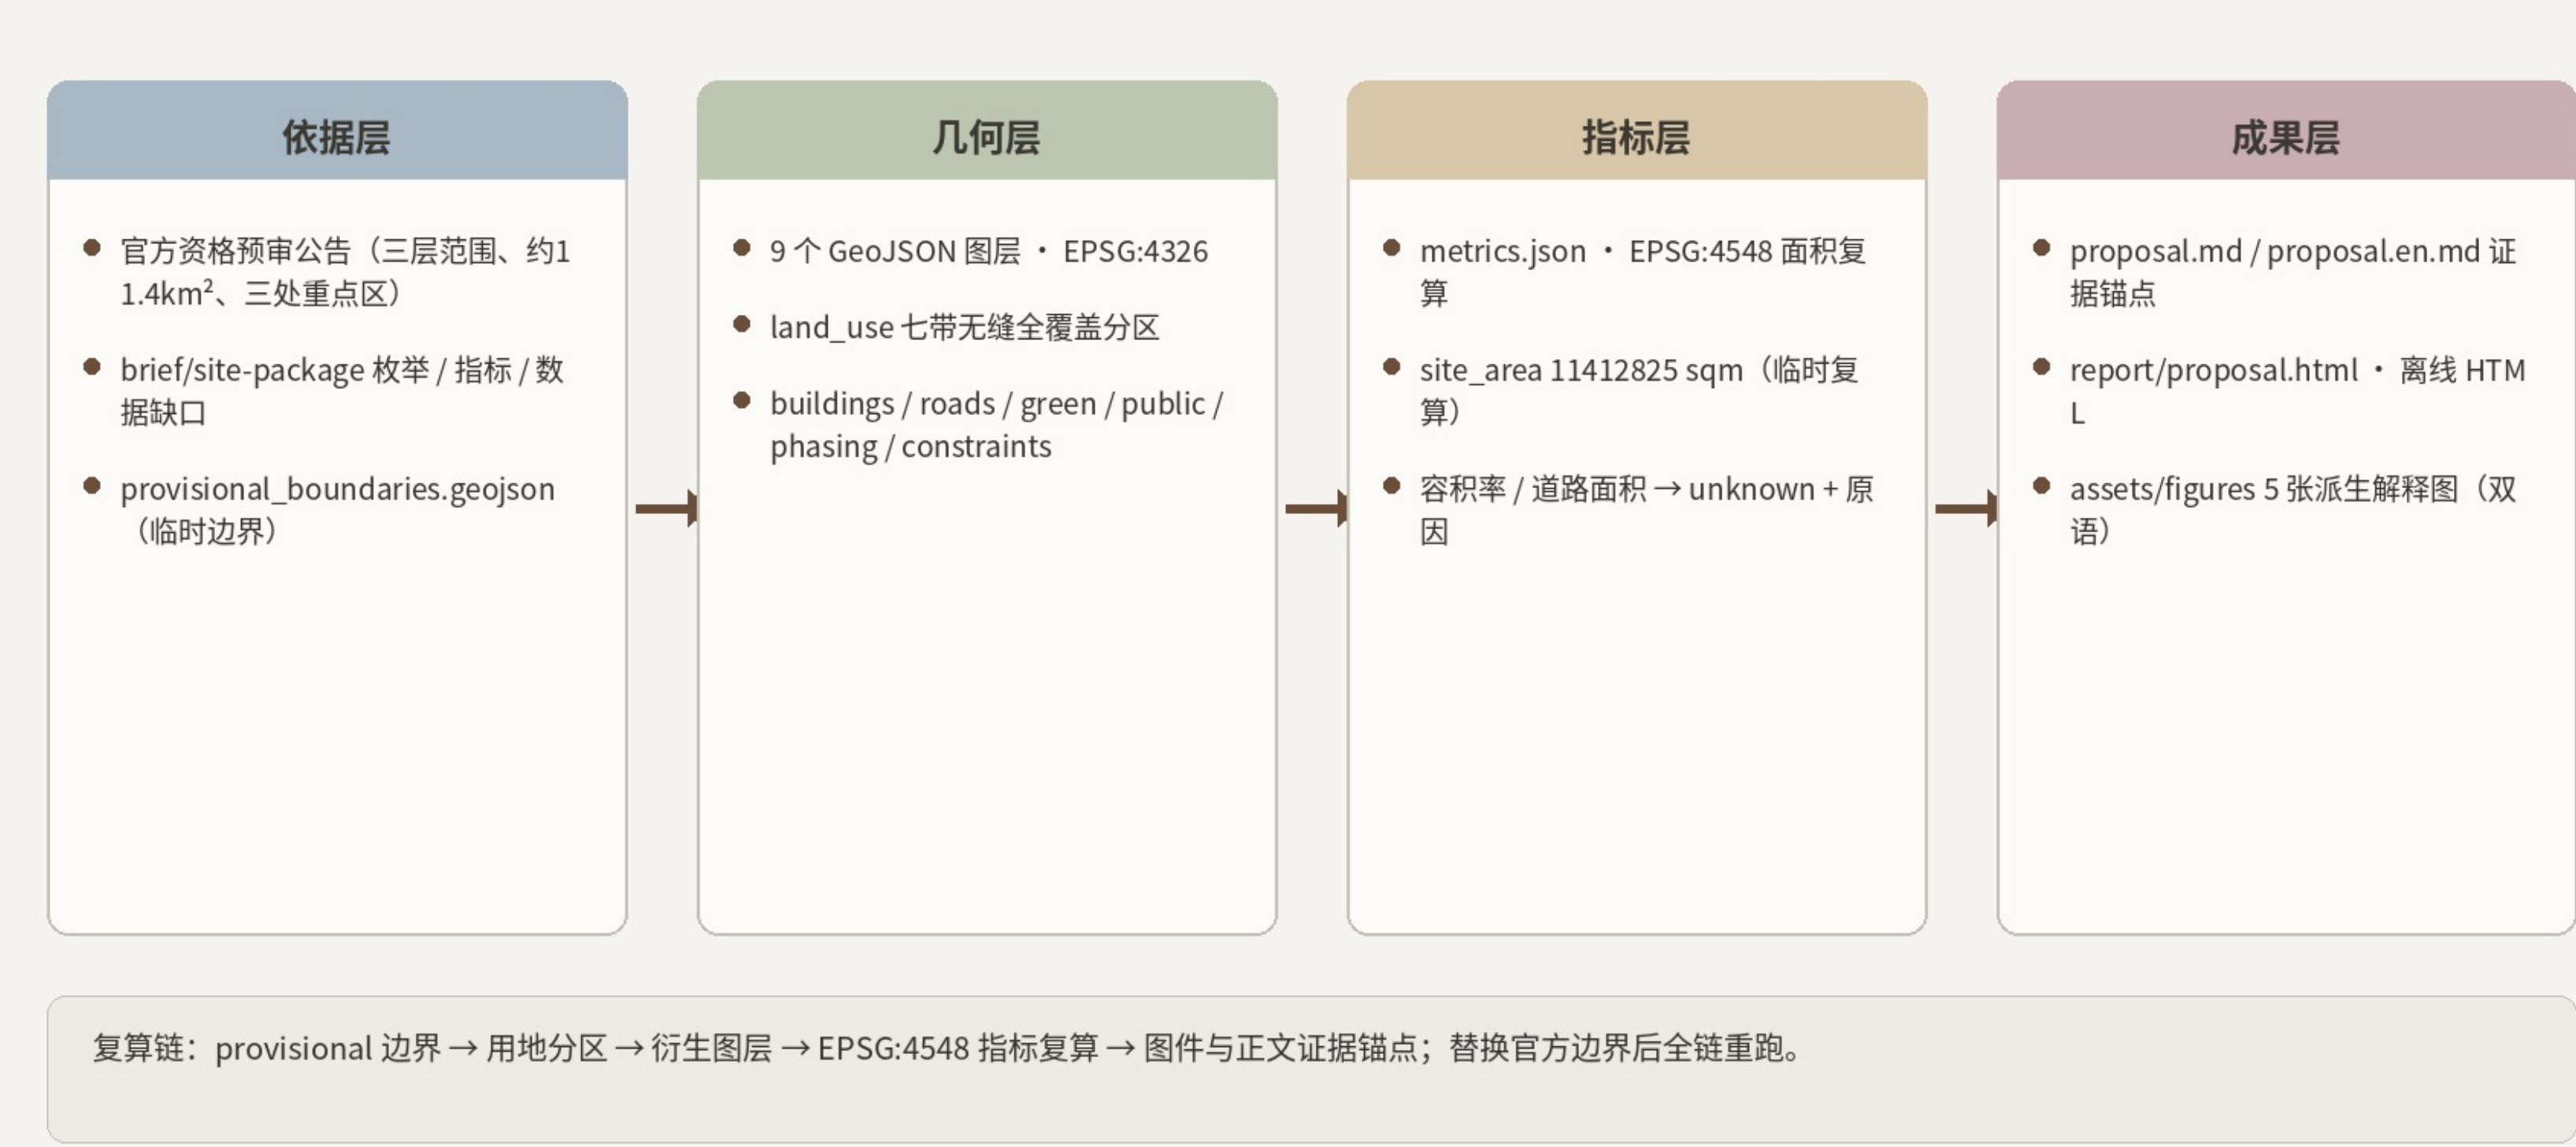

临时约束 provisional constraint: 本图所有边界均为临时粗略范围, 非官方红线, 面积待官方数据复算。

来源: brief/site-package/geometry/provisional_boundaries.geojson; geometry/*.geojson; metrics.json

① 三层范围总览 (site-overview)

统筹研究范围 43.6 km² · 总体设计范围 11,412,825.386 sqm (provisional 复算, confidence medium) · 重点区域 3 处 (公告口径约 192.1 / 104.3 / 72.0 ha, 官方 polygon 缺失)

三处重点详细设计区索引与设计任务图

众智园 AI 加速区 · 北京 AI 原社区 · 大钟寺 AI 产业聚集区 (临时范围)

FIG-03 / 05



③ 三处重点区域 (key-areas)

众智园 (北·策源, 约 192.1 ha) / 北京 AI 原社区 (中·孵化, 约 104.3 ha) / 大钟寺 (南·产业化, 约 72.0 ha) ; 官方 polygon 缺失, 详细设计结论为方向性设计

结构框架
"一轴一环三核多接口": 京张绿廊为轴、慢行环串联、三重点区为核、轨道站点与东西缝合通道为接口。南北创新链"策源→孵化→产业化", 东西服务链"资本与 IP ↔ 场景与数据" (概念建议)。

用地结构 (provisional 复算)		
0702 社区服务设施	3,006,997.433 sqm	26.35%
0802 科研	2,477,312.922 sqm	21.71%
0803 文化	1,738,608.869 sqm	15.23%
05 商业服务业	1,517,250.379 sqm	13.29%
0804 教育	1,486,567.535 sqm	13.03%
16 留白	1,186,083.435 sqm	10.39%


蓝绿与公共 (provisional 复算)	
绿地面积 / 绿地率	1,290,877.036 sqm / 0.113108
公共空间 / 占比	84,399.550 sqm / 0.007395
建筑密度	0.017822 (设计几何密度, 非法定指标)
容积率	unknown (法定指标与官方边界缺失)
道路用地面积	unknown (仅概念道路中心线)

边界纪律
全部图层基于临时粗略边界派生 (official_boundary=false) ; 官方 polygon 发布后整体替换并同公式复算全部派生图层与指标 (A-BOUNDARY-PROV-002 / A-AREA-RECALC-014)。本板全部内容为概念建议, 不构成官方规划文件或实施承诺。

三层范围与用地功能结构图

一带七段: 南北向功能带无缝全覆盖分区 · 临时边界派生

FIG-02 / 05

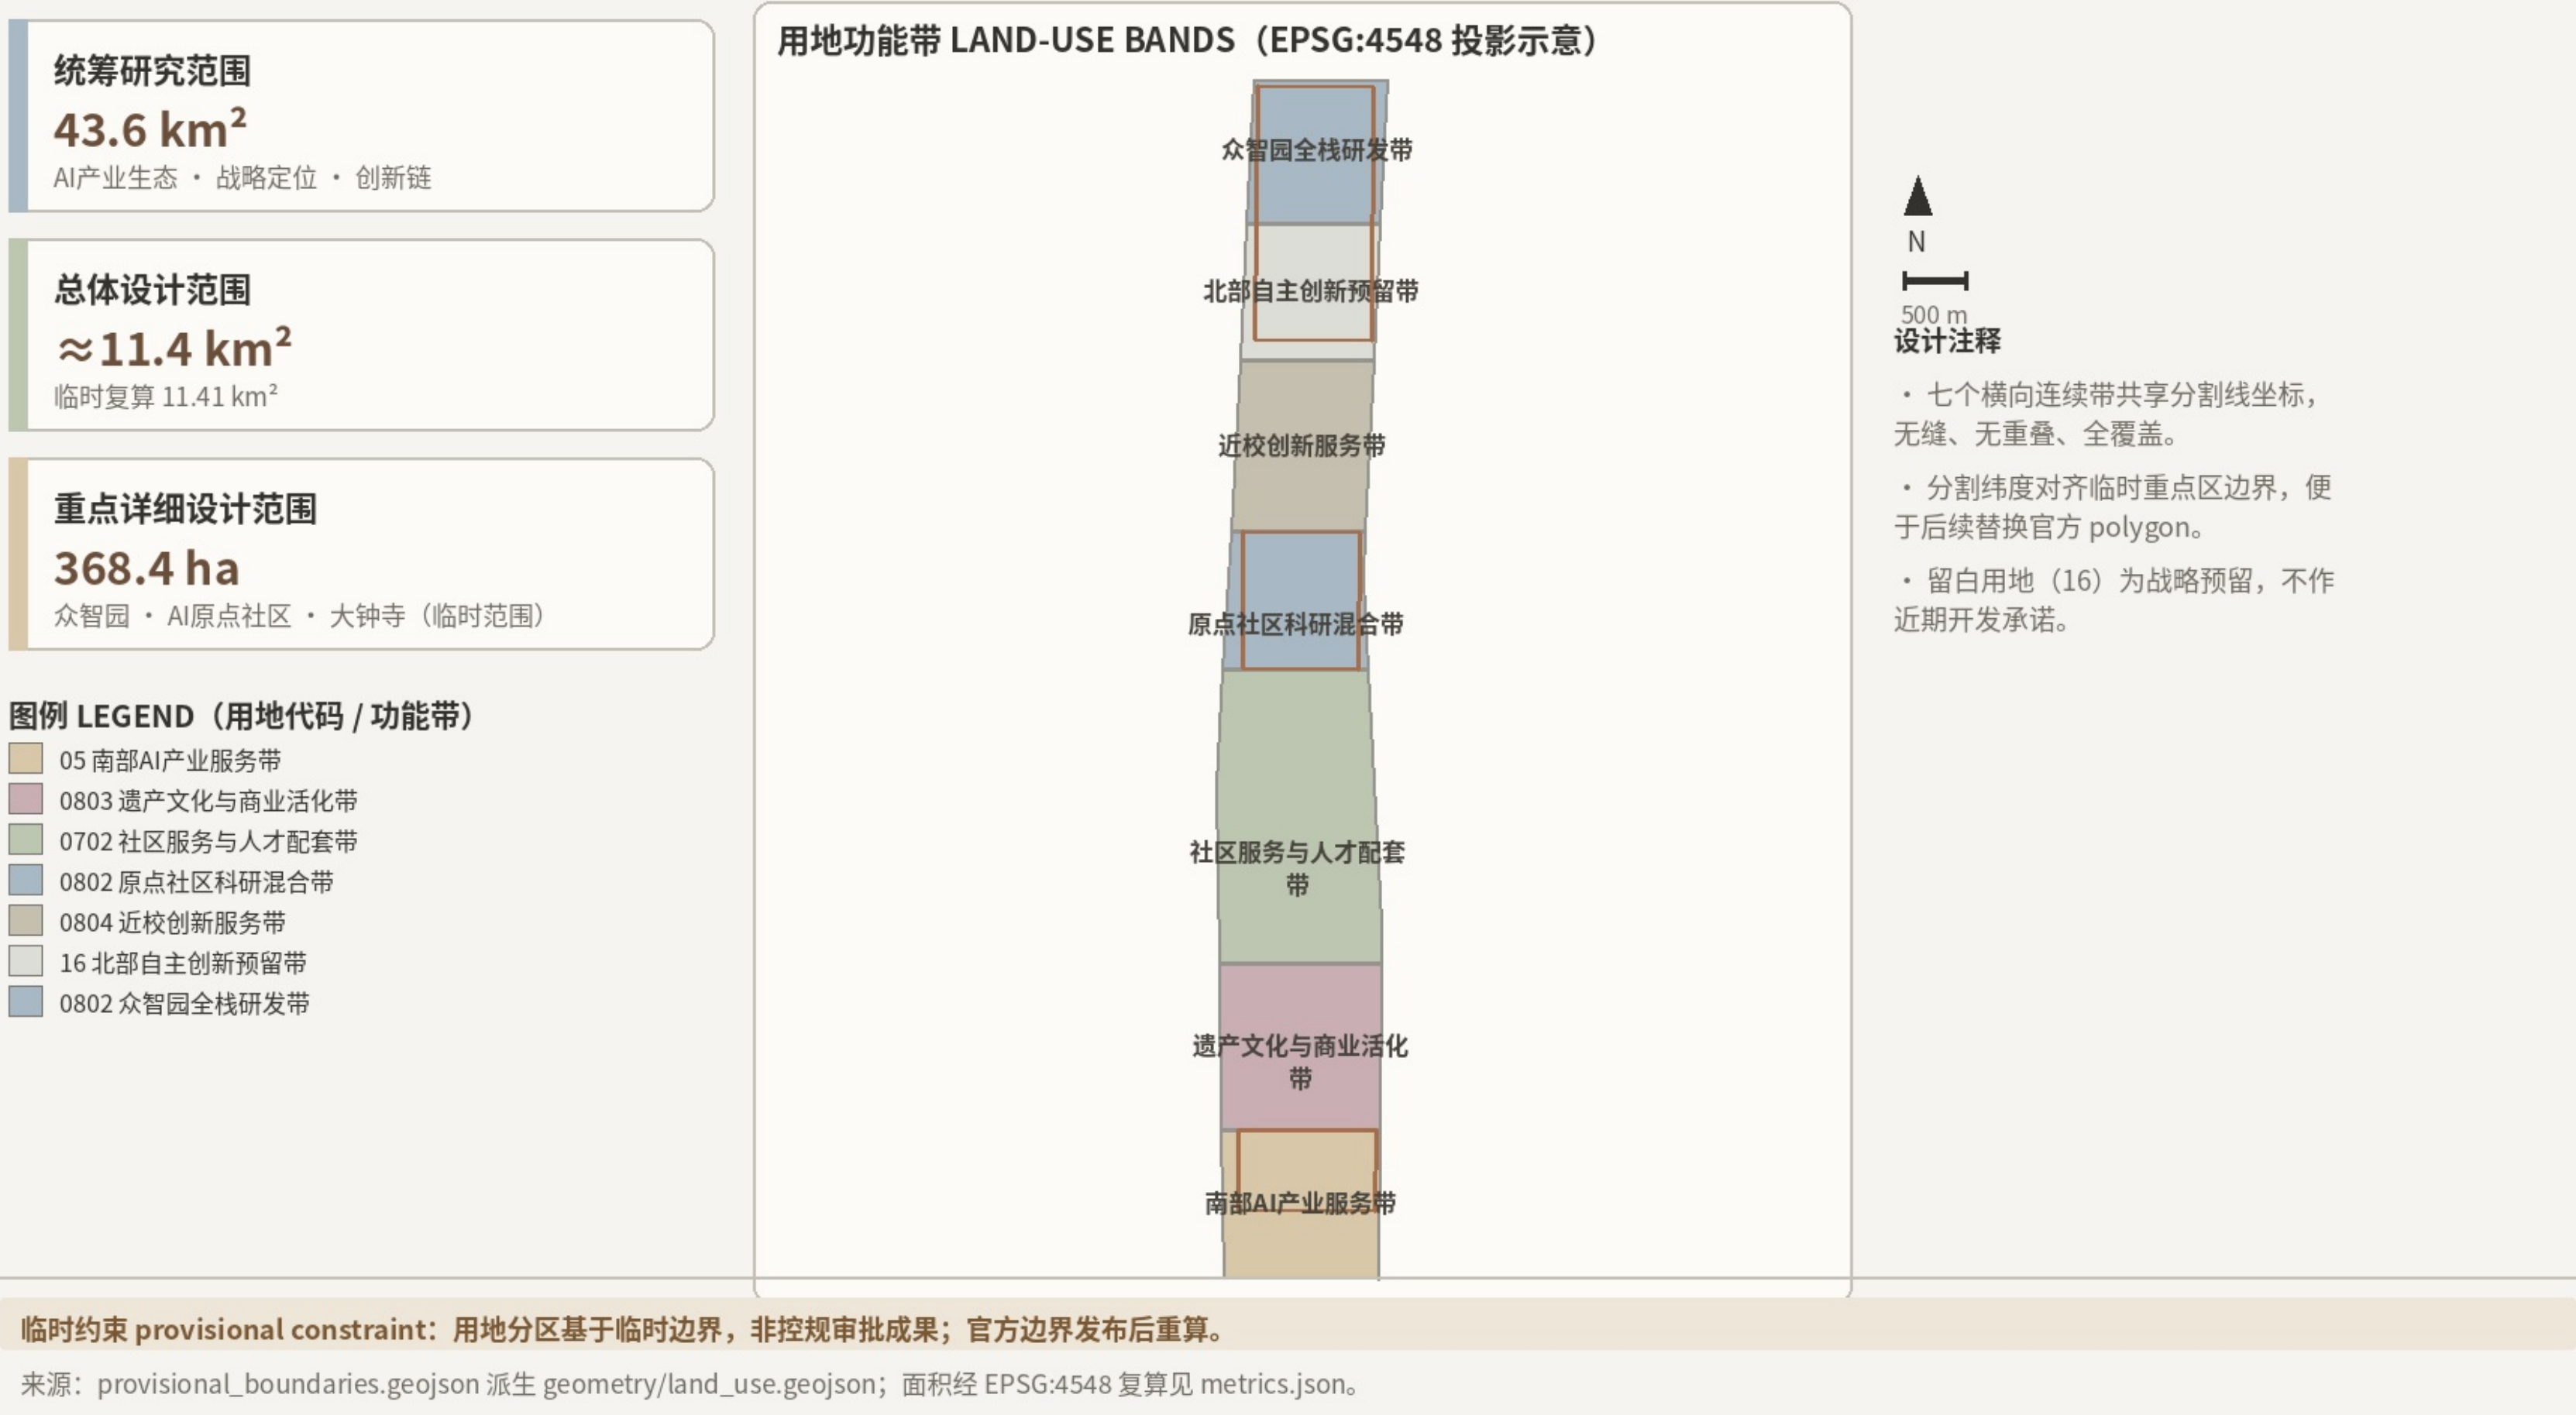

② 用地结构主叙事 (land-use-structure)

七大功能带 · 六个用地代码 · 覆盖率 100% / 重叠 0 / 缝隙 0 的零和封闭系统; 0702 社区服务设施 26.35% 居首, 16 留白 10.39% 高于任何单一产业带

交通慢行与蓝绿公共空间复合系统图

绿色慢行主轴 · 东西缝合 · 轨道接驳 · 微循环 · 遗址绿廊 · 社区公园 · 公共节点

FIG-04 / 05



④ 交通与蓝绿结构 (mobility-bluegreen)

交通按"已兑现/在建预期/待定/概念建议"四档引用, 不跨档引用; 9 km 京张遗址绿廊为叙事主轴; 道路用地面积 unknown (仅概念中心线)

百年京张 AI 创新带 · 场景与实施板

12 张分级场景卡 × 三期概念实施 × 可复核指标 | 全部场景、项目、分期与运营为概念建议，未获监管许可、不构成实施承诺

