


双轨共生带：百年京张AI创新带城市设计

双轨共生带（TRSB）· Hyp6666

基于公开或清权资料；临时边界（provisional），官方红线待发布。本方案为概念研究包，非审定控规成果。

双轨共生带 · 总体概念 / Twin-Rail Symbiosis Belt — Overview

铁轨文脉带 × 光轨创新带 × 三处重点区 · 用地与空间结构 (provisional)

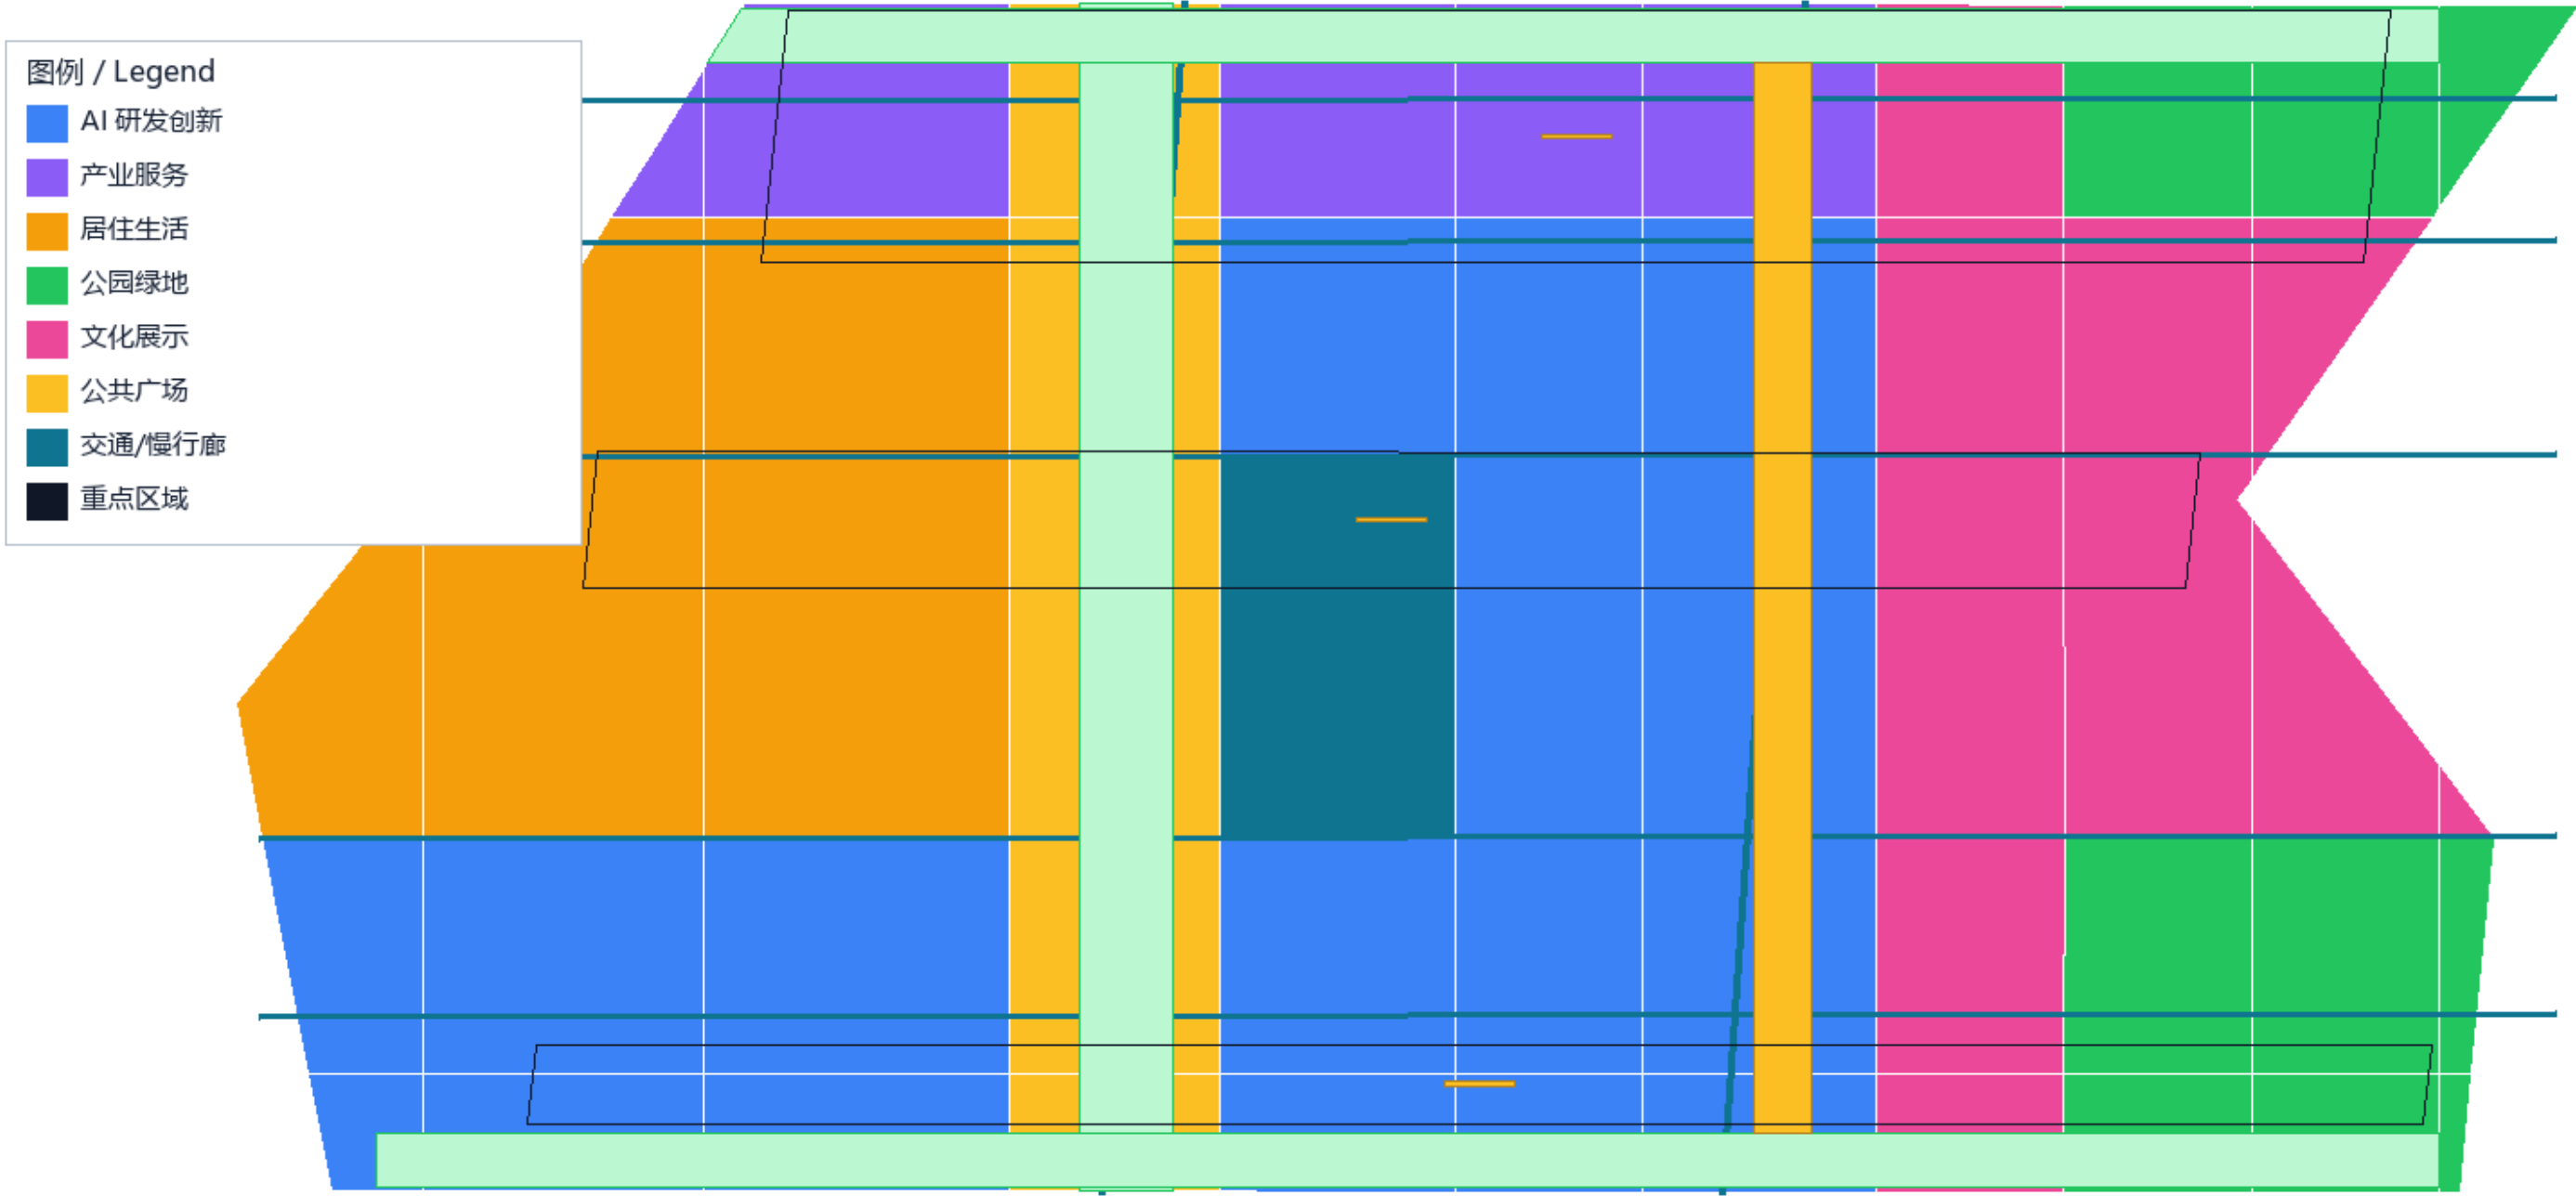

图面由 geometry/*.geojson 与 metrics.json 派生；官方精确红线未发布，全部结论待复算。

图 0-1 双轨共生带总体概念：铁轨文脉带（历史）× 光轨创新带（AI）× 枕木廊道（慢行/蓝绿）

1. 总体概念与三层范围 / Overall Concept & Three-Level Scope

以京张铁路百年双轨为空间原型：铁轨承载历史文脉（京张文化带），光轨承载AI产业创新（AI融合创新带），枕木即东西向慢行与蓝绿廊道（都市AI生活体验带）。三区两翼协同：众智园（加速轨）、AI原点社区（原点轨）、大钟寺（应用轨）。

范围	面积	任务
统筹研究范围	43.6 km²	产业生态、未来城市形态、命名logo
总体设计范围	11.4 km²	控规深度更新、交通市政、风貌
重点区域范围	368.4 ha	三处重点区精细化设计

双轨五链·用地结构 / Land-Use Structure under Twin-Rail Five-Chain


AI研发·文化·居住·商务·蓝绿·广场 全分区 (provisional)

图例 / Legend

铁轨文脉带

光轨创新带


枕木廊道

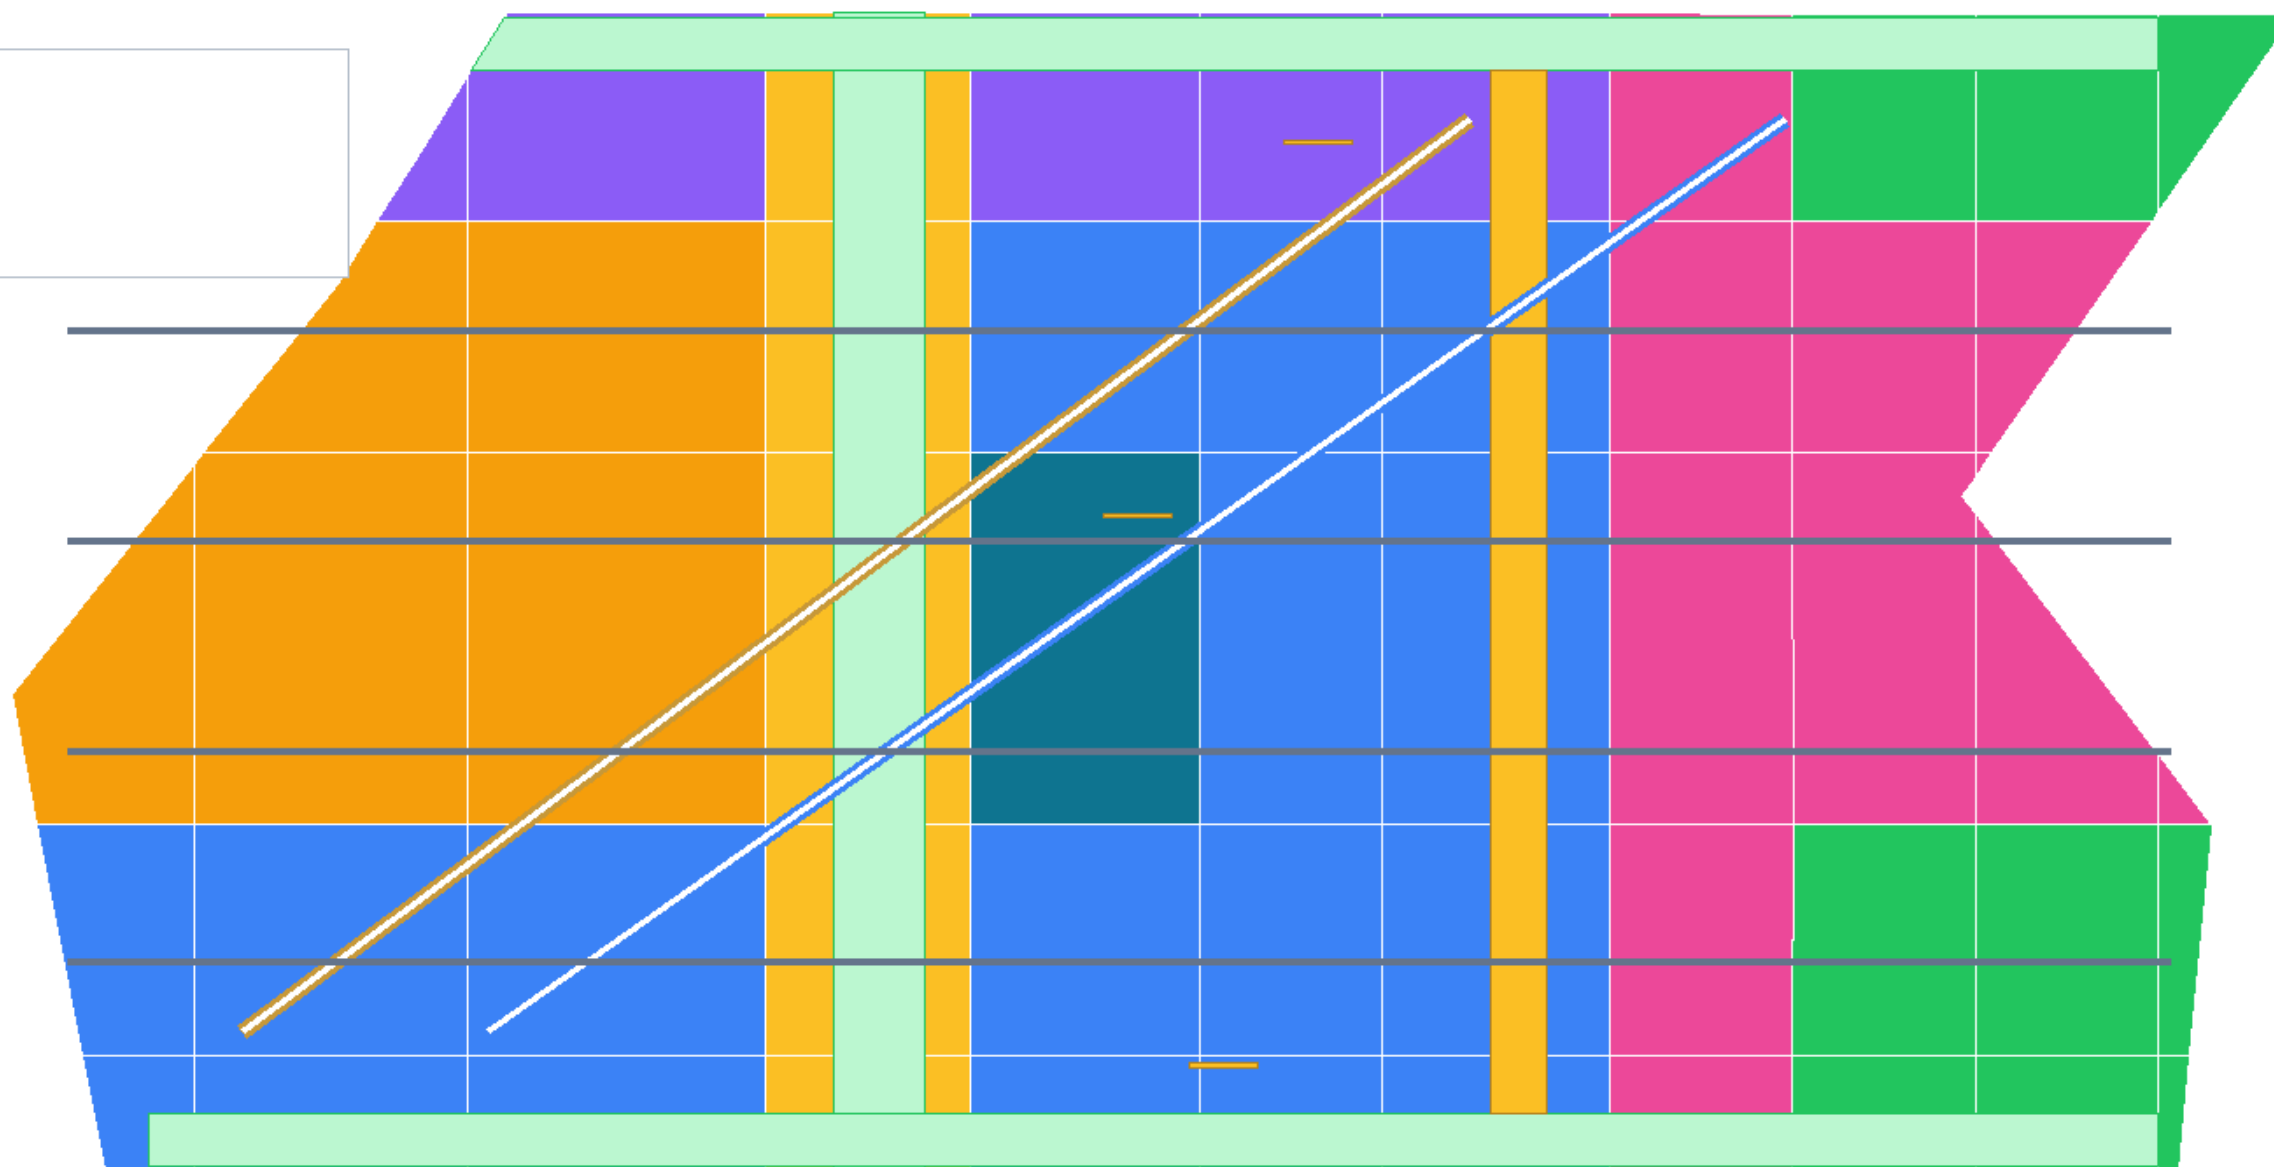

双轨平行共生，枕木即东西向慢行与蓝绿廊道；比例由 metrics.json 复算。

图 1-1 双轨五链用地结构：AI研发·文化·居住·商务·蓝绿·广场

2. 三处重点区域 / Three Key Areas

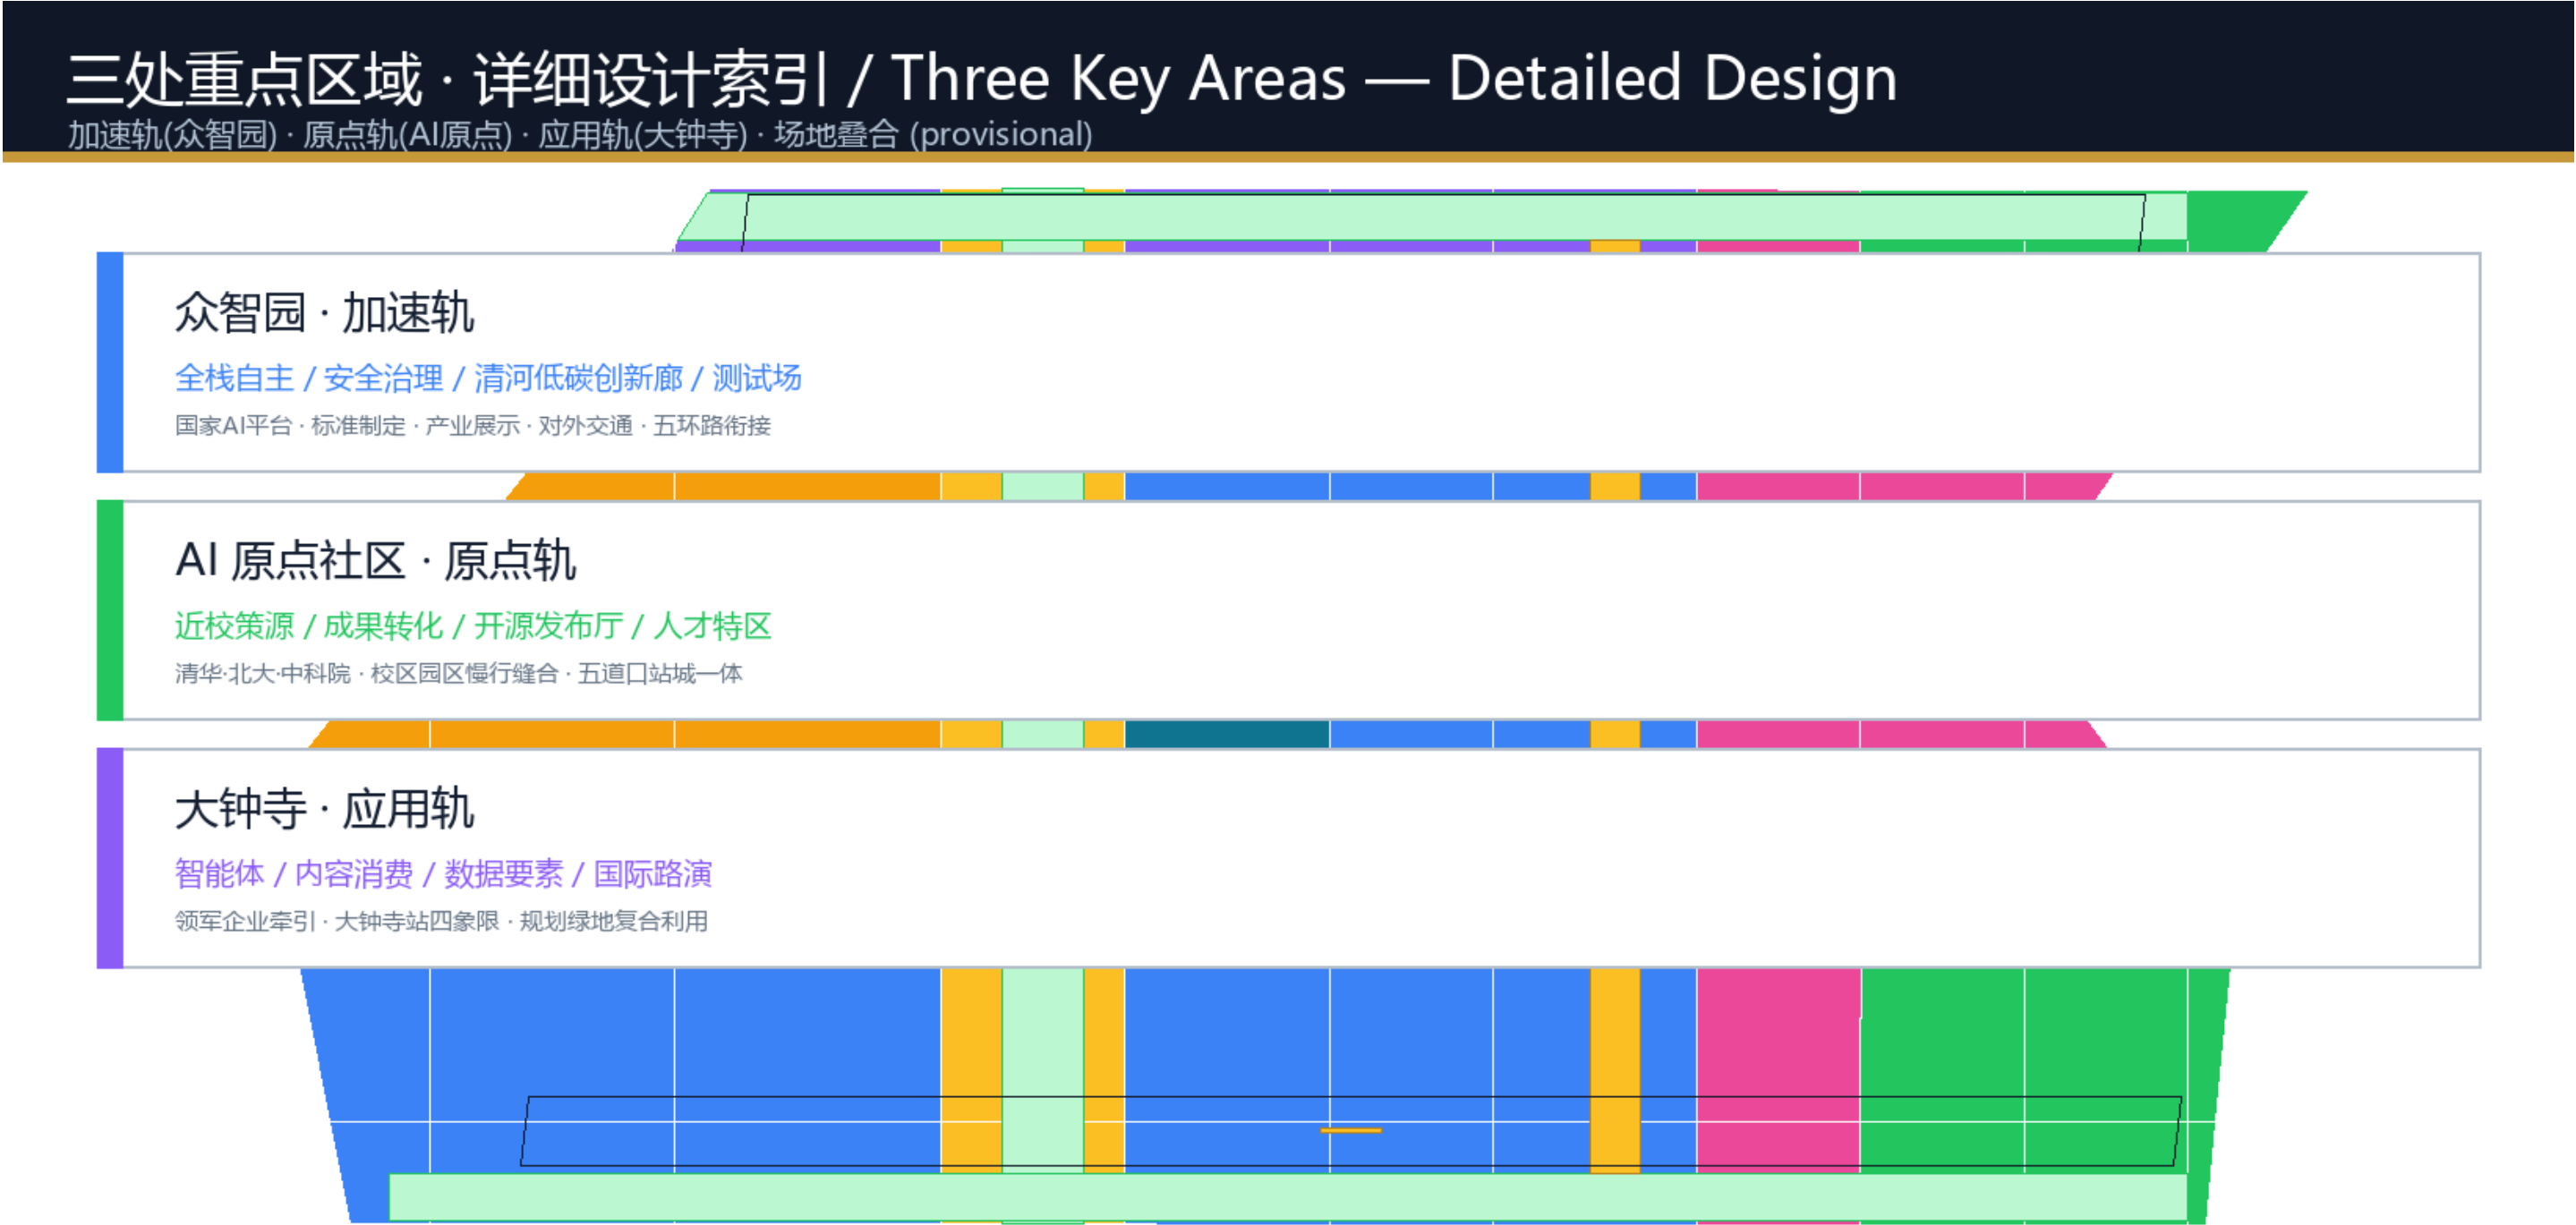

三处重点区均达概念研究深度；面积偏差 <0.5%，待官方 polygon 复算。


图 2-1 三处重点区 (provisional) 设计索引：加速轨(众智园) · 原点轨(AI原点) · 应用轨(大钟寺)

众智园：花园型全栈自主创新街区，承担全栈自主与AI治理话语权；清河低碳创新廊、安全治理沙盒。AI原点社区：近校成果转化与人才社区，校区园区慢行缝合、开源发布厅、五道口站城一体。大钟寺：城市型智能经济街区，大钟寺站四象限连通、数据要素会客厅、国际路演。

3. 交通慢行 × 蓝绿公共空间 / Mobility × Blue-Green

交通慢行 × 蓝绿公共空间 / Mobility × Blue-Green Network

交通廊 · 慢行 · 蓝绿带 · 换乘广场 · 遗址公园 (provisional)

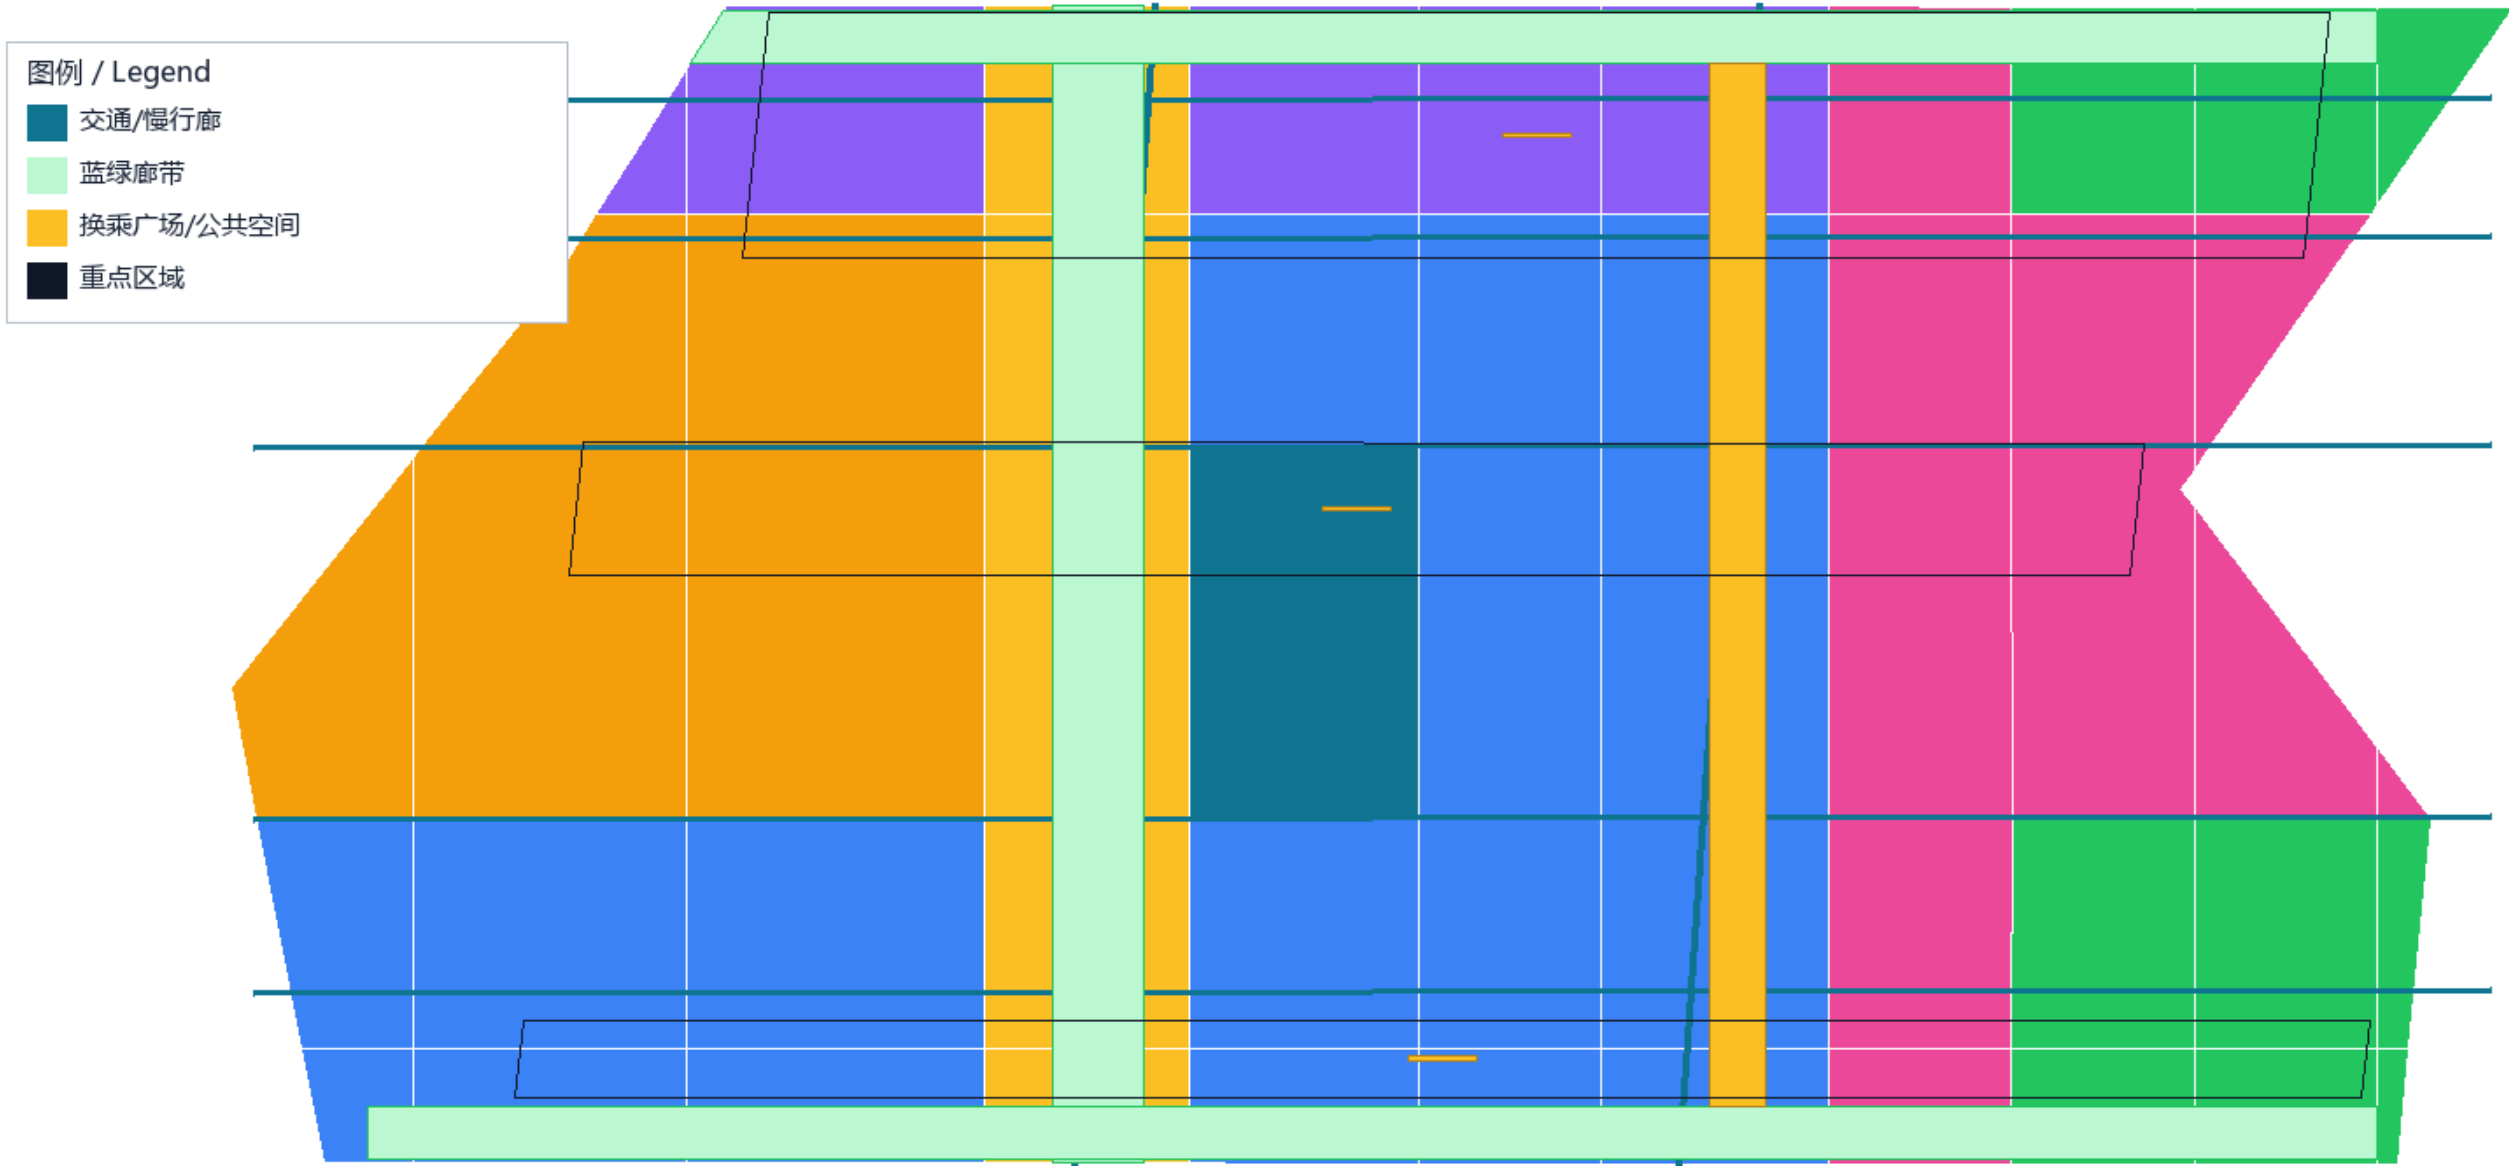

站城一体、慢行断点缝合与蓝绿连通共同支撑双轨共生；道路与蓝线均待专业深化。

图 3-1 双轨复合走廊 + 枕木联络 + 换乘广场 + 清河/小月河蓝绿带

交通围绕双轨+枕木组织：两条南北向复合走廊为主轴，五条东西向联络路为枕木，连接高校、园区、社区与轨道站点（五道口、清华东路西口、大钟寺）。市政探索分布式能源、端侧算力与传统设施融合。道路红线、轨道线位待专业深化。

4. 核心指标 / Core Metrics

核心指标复算 · 证据链 / Metrics Recalculation & Evidence Chain

面积 · 绿地 · 公共空间 · 建筑 · 用地结构 · 待确认指标 (provisional)

总体设计范围面积 1141.3 ha	绿地比例 12.75%	公共空间比例 2.57%
建筑基底面积 44.39 万 m²	道路中心线总长 26.2 km	重点区域数量 3 处

未知/待确认指标：容积率、建筑高度、建筑密度、退线 —— 待官方控规条件补齐后复算

证据链：geometry/*.geojson → metrics.json → figures → report/proposal.html → visual/index.html

图 4-1 核心指标复算与证据链：面积 · 绿地 · 公共空间 · 建筑 · 待确认指标

指标 / Metric	数值 / Value
site_area_sqm	11412825.386
green_ratio	0.12747

public_space_ratio	0.02573
building_footprint_area_sqm	443875.173
road_length_m	26236.172
floor_area_ratio	待官方条件 / pending

5. 任务覆盖与合规 / Task Coverage & Compliance

合规矩阵覆盖公告 1.3/1.4/1.5 与 agent.1-agent.6；标准矩阵覆盖城市设计管理办法、控规办法、用地分类指南；深度矩阵全部核心项 complete。所有空间落地建议均为概念建议，不构成政府承诺。

声明：本方案不声称官方批准、审定控规、最终权属或保证实施；官方边界、控规、权属、市政与工程条件待补后复算。