

总体概念与空间结构

设计定位与命名体系

三大定位：百年京张文化带、都市AI生活体验带、AI融合创新带；五大功能：AI全栈自主创新体系、世界级AI创新生态、AI+场景赋能新范式、智能化AI活力城市、AI治理全球话语权。

- 主名「京张经纬带」Jing-Zhang Warp-Weft Belt：经线=时间纵深与自主工程精神，纬线=创新织补与开放协作
- 织梭标志：双平行线=钢轨轨距；60°人字折角=青龙桥人字线；纬线+节点圆点=缝合与网络
- 三区两翼命名：织源（众智园AI自主创新加速区）· 织心（北京AI原点社区）· 织声（大钟寺AI产业集聚区）· 织金（中关村科技服务翼）· 织绿（小月河场景赋能翼）

空间结构

- 一带三核：京张遗址公园绿廊为南北脊柱（记忆/原点/未来三段）
- 三缝合带：S1知识缝合（五道口-学院路-中关村）· S2科技缝合（清华园车站）· S3产业缝合（大钟寺-中关村南大街）
- 两翼两河：织金/织绿两翼 + 清河/小月河两条水绿副线

三层范围

43.6km²


统筹研究范围

11.4km²

总体设计范围

368.4ha

重点区域合计

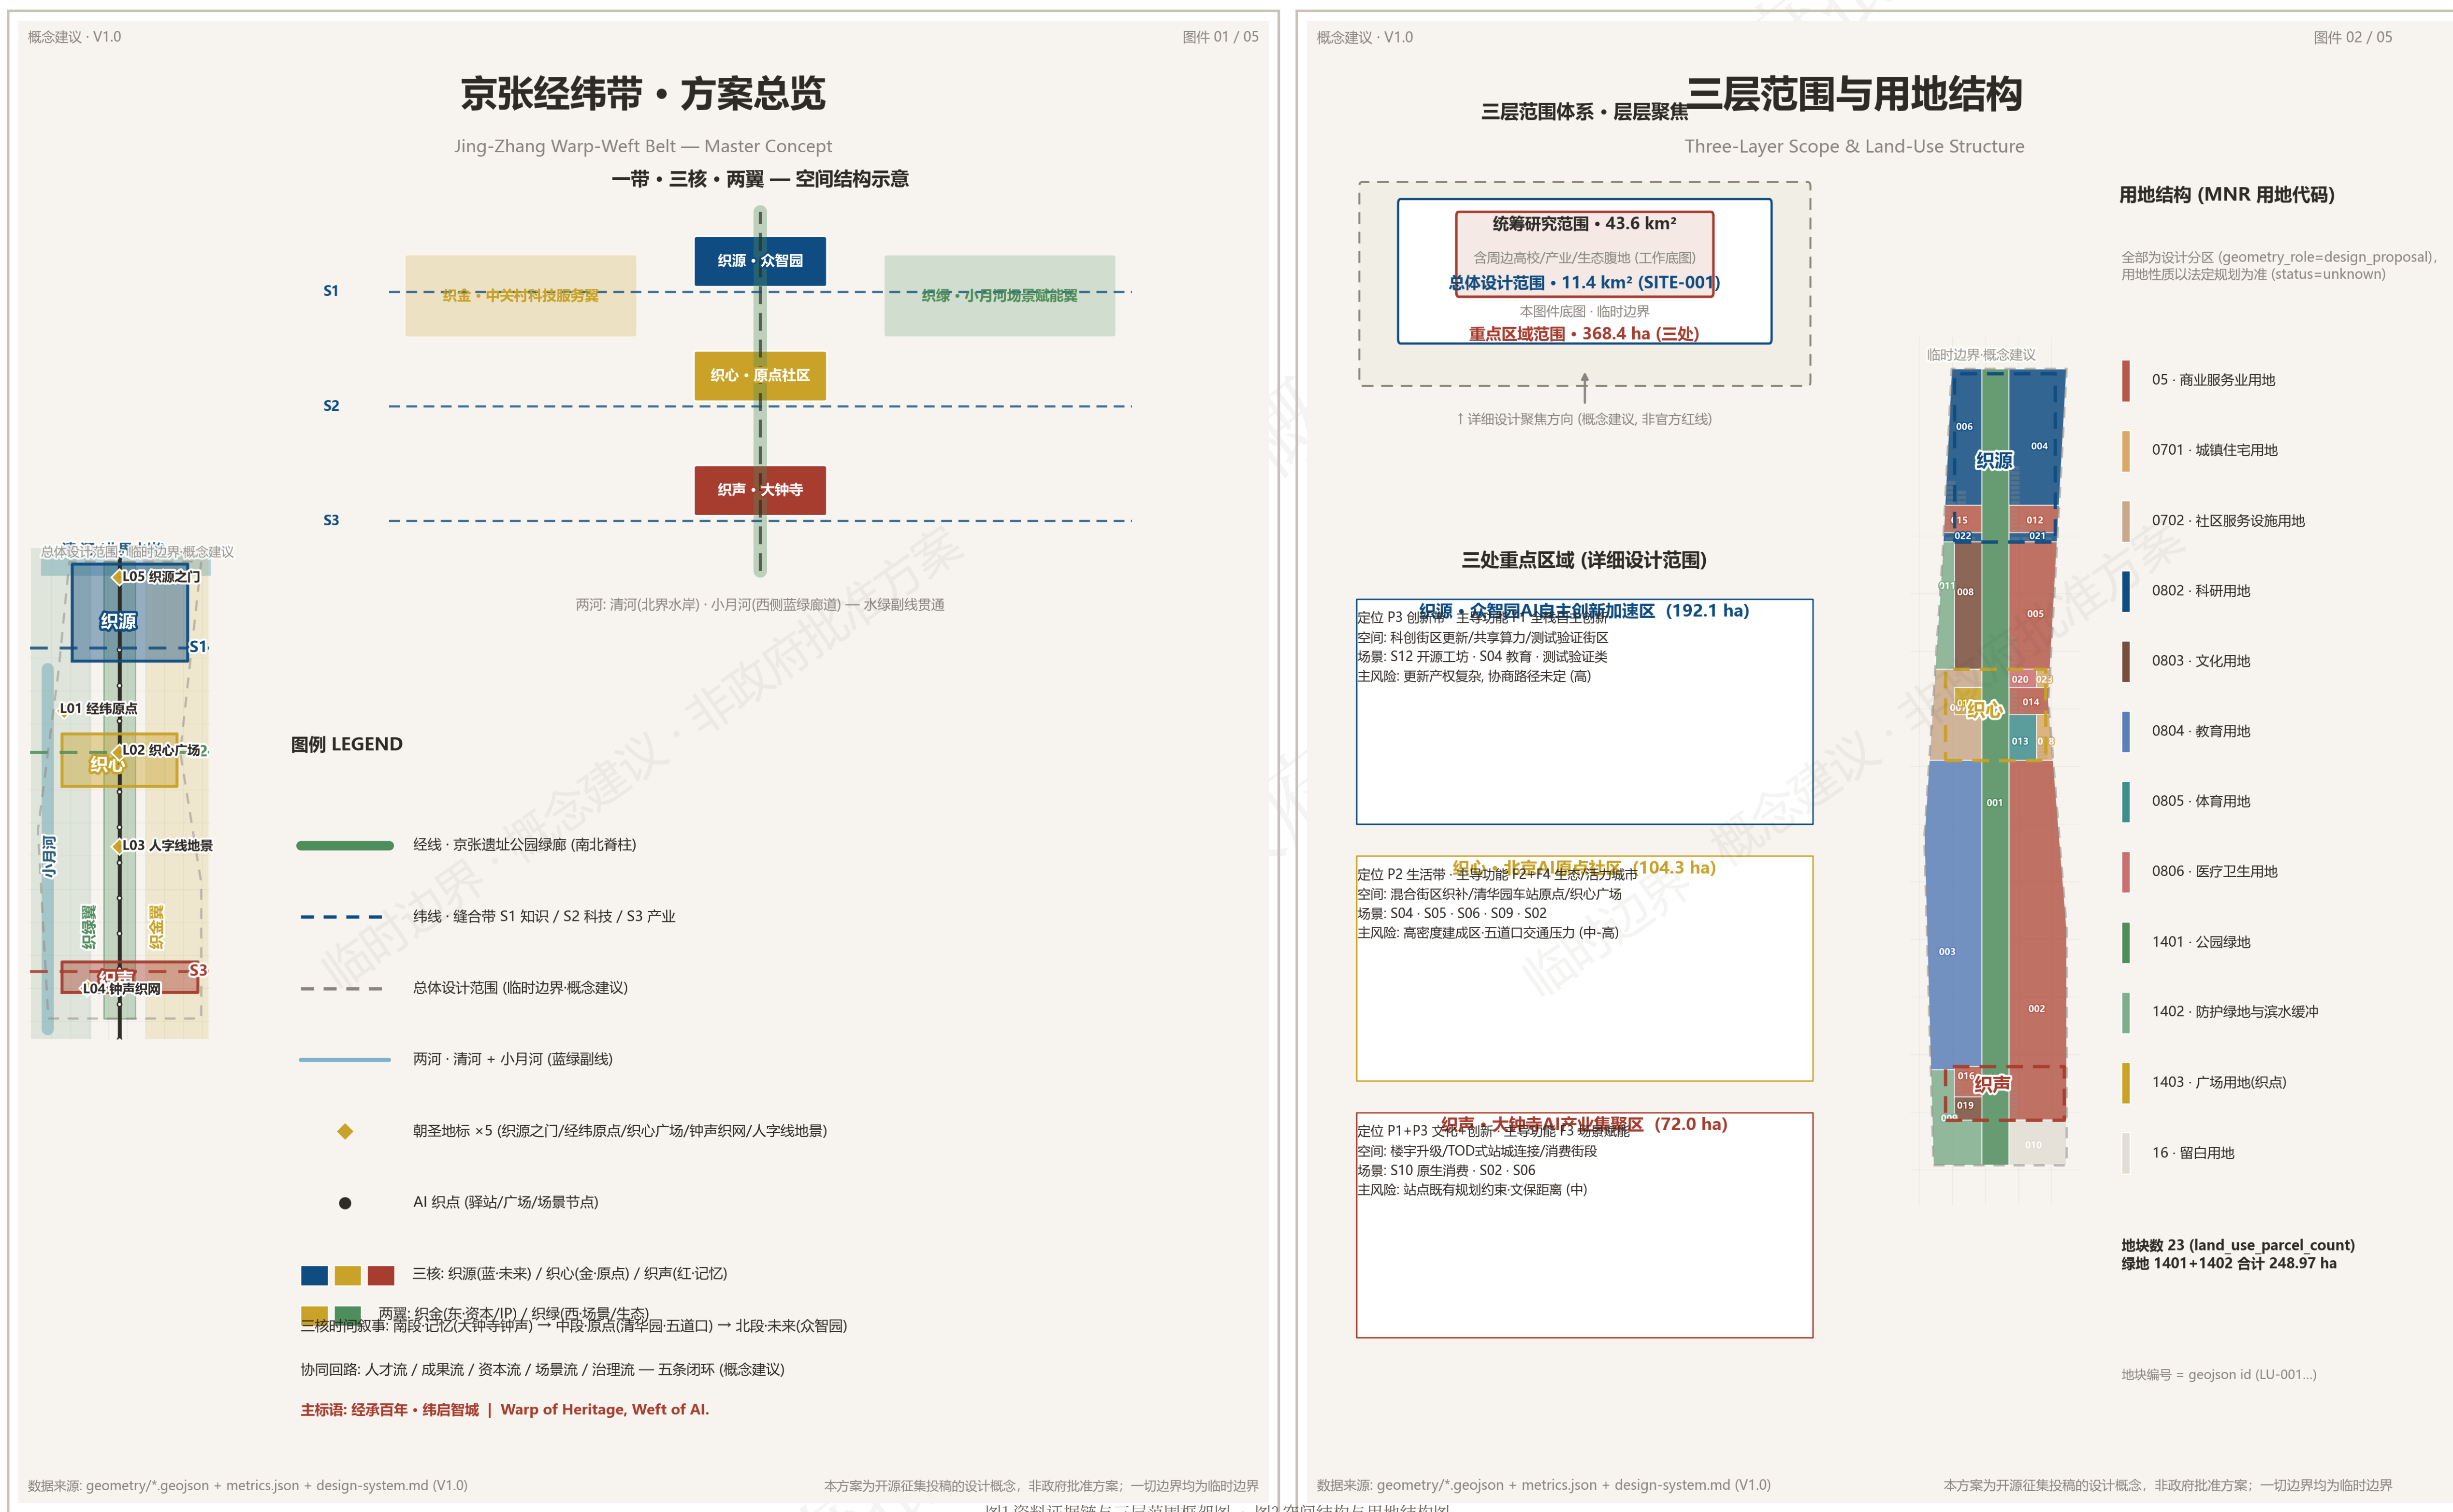

临时边界 · 概念建议 — 本图边界为公开资料推算的临时多边形 (PROV-SITE-001 / PROV-KEY-001/002/003)，非官方红线，正式图件发布后需复算全部边界与指标

用地与更新

用地结构（23 个用地图斑）

23

用地图斑

336.7万m²

商业服务业

144.9万m²

科研

191.5万m²

教育

· 绿地与开敞空间约 248.97 万m²；留白用地约 29.9 万m²，为未来功能调整预留弹性

· 城镇住宅约 10.4 万m² + 社区服务设施约 43.0 万m²，支撑人才安居与公共服务一体化

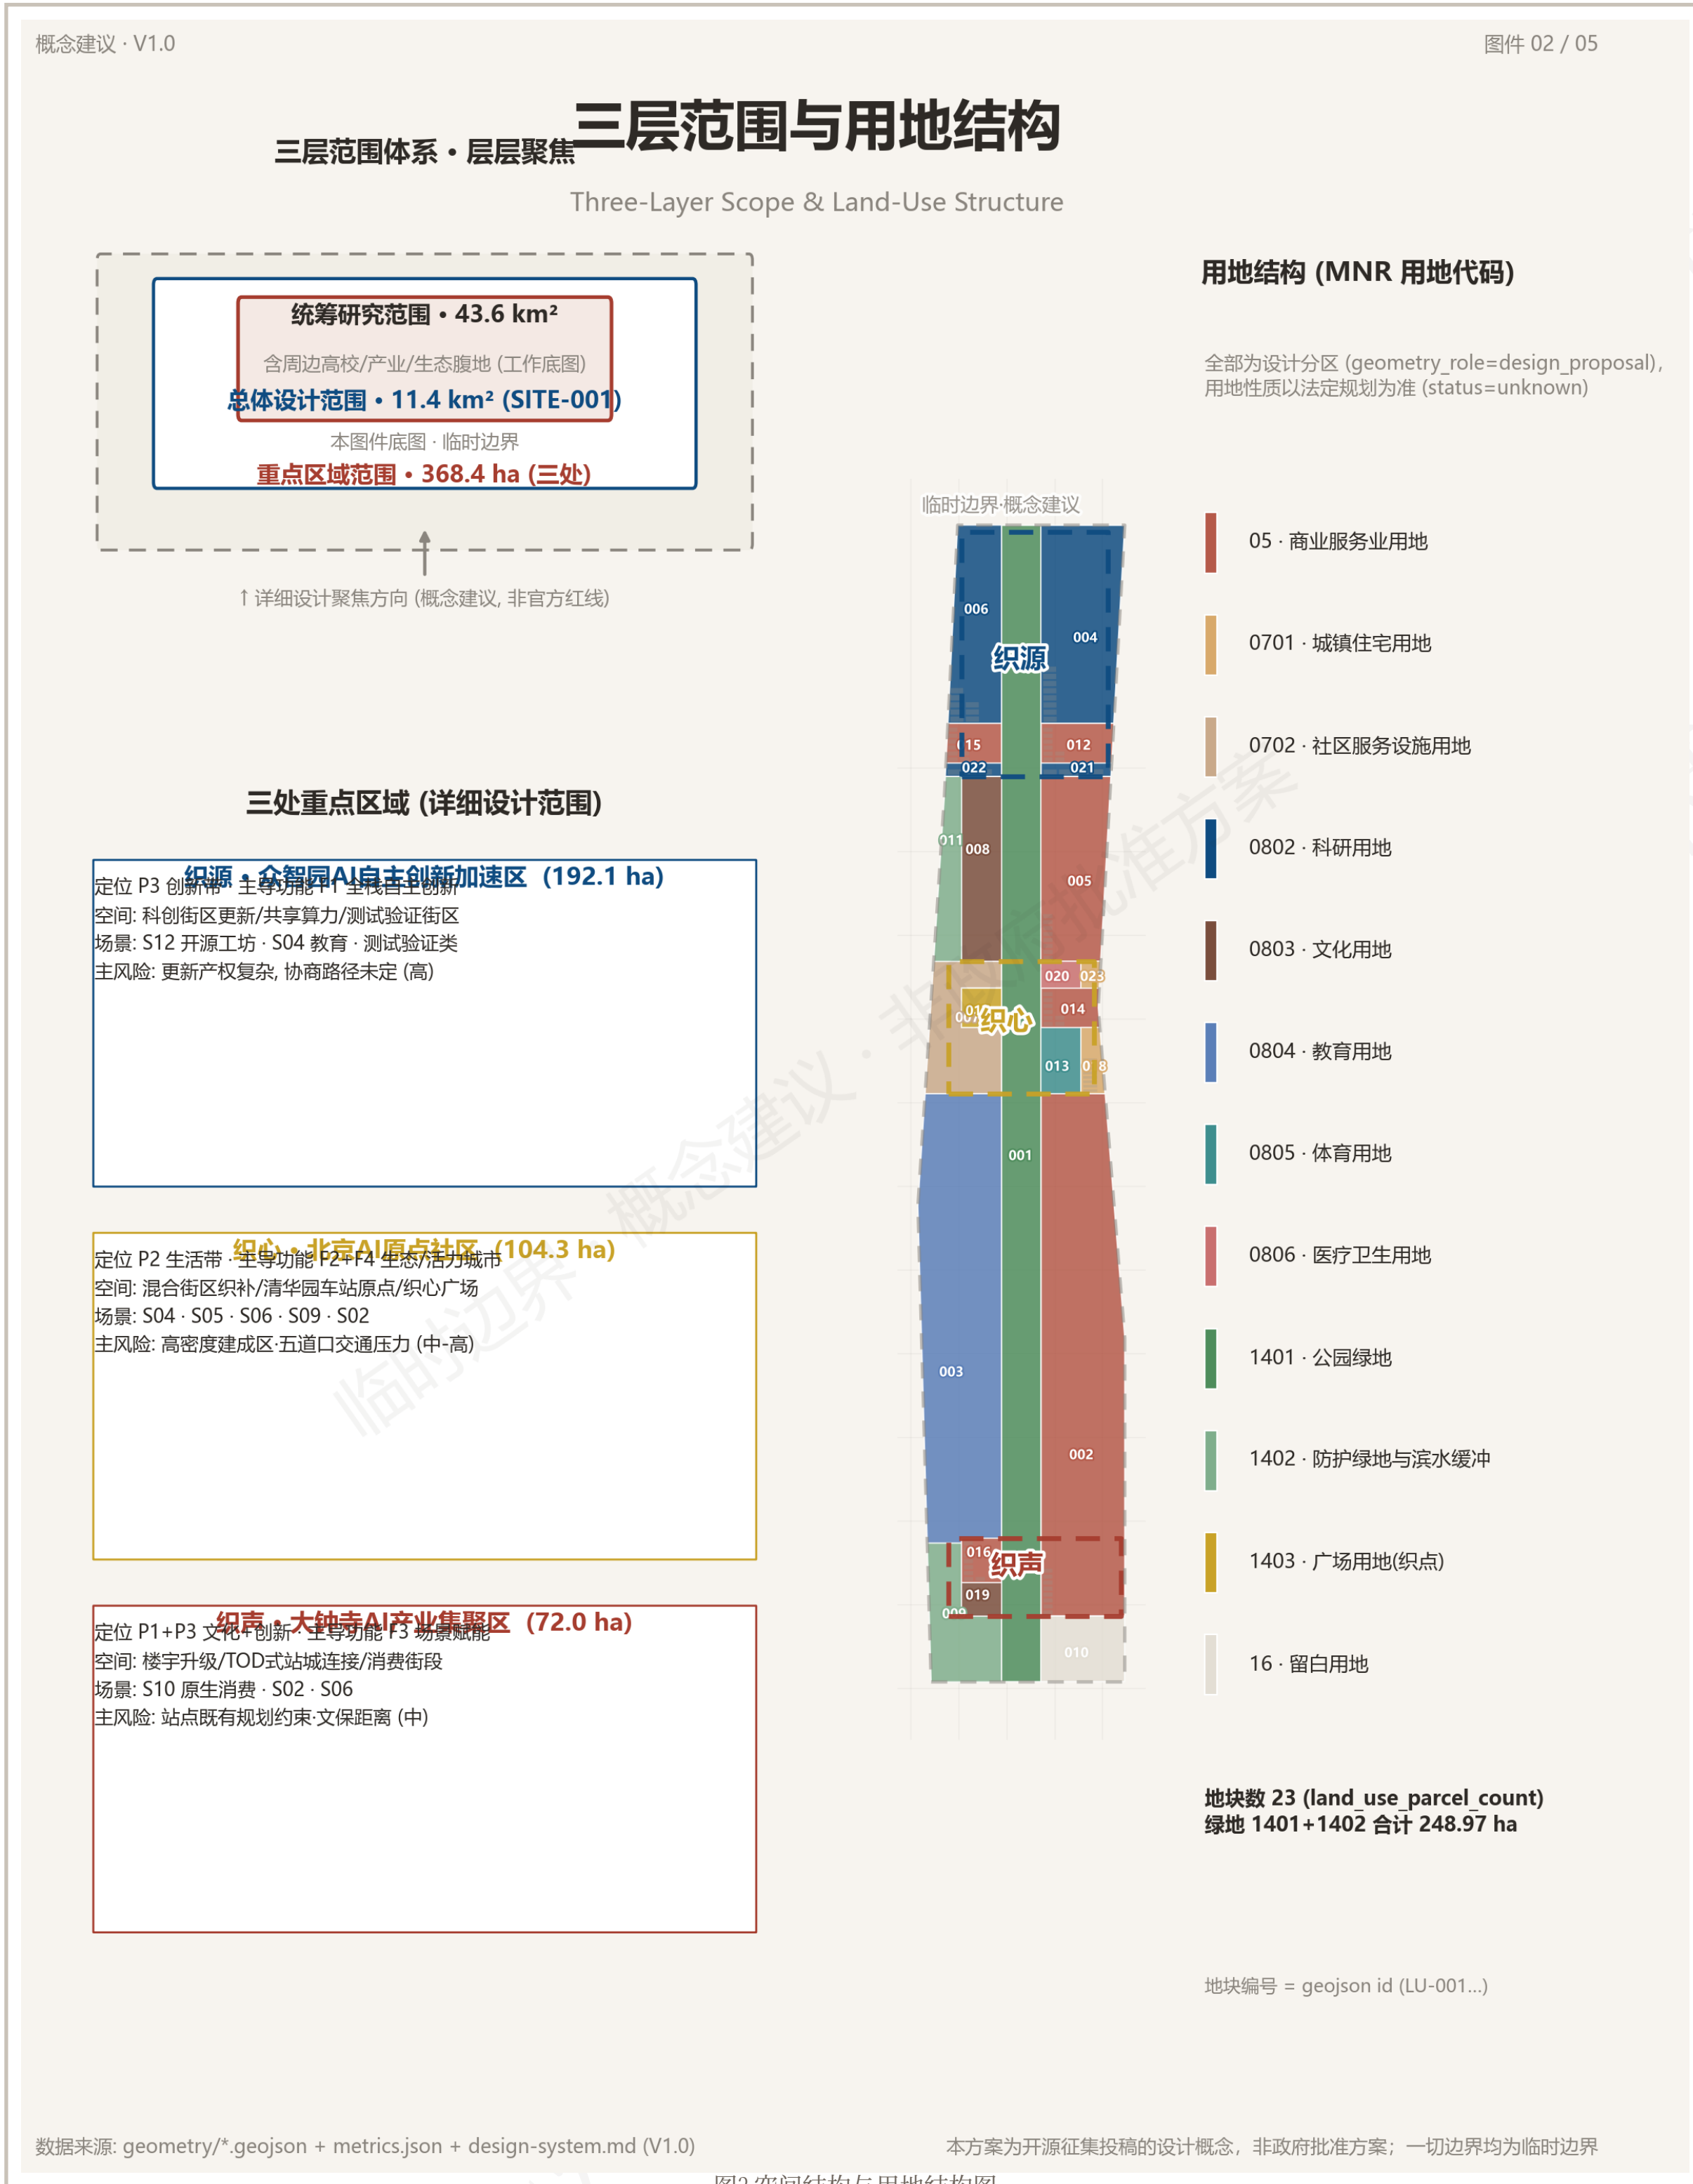


图2-空间结构与用地结构图

建筑与管控指标

79 栋概念体量、基底总面积复算约 20.5 万m²；容积率、建筑高度、密度与退线在缺少官方控规前统一 status=unknown，待控规发布后按复算公式与官方面积重算。

拆改留与分期

- 保留：遗址绿廊、清华园车站旧址、大钟寺博物馆片区
- 改造：缝合带楼宇底商与产业楼宇功能升级
- 新建：织源测试验证街区、织心混合街区织补；不给出任何拆除搬迁结论
- 近期0-3年 约626.4万m²（场景快闪·慢行贯通）| 中期3-5年 约289.0万m²（示范织点·织心广场）| 远期5-10年 约225.9万m²（全带成网）

临时边界 · 概念建议 —— 本图边界为公开资料推算的临时多边形 (PROV-SITE-001 / PROV-KEY-001/002/003)，非官方红线，正式图件发布后需复算全部边界与指标

交通市政与蓝绿

交通与慢行

34.1km

道路中心线总长

9.3km

经线主脊慢行道

2条

滨水绿道（清河/小月河）

- 三条缝合带以次干路织补东西向连接（S1知识/S2科技/S3产业）
- 织心广场人行横穿承接地铁五道口站接驳；大钟寺站前人行道组织站城一体步行界面
- 站点周边地下地面连接、慢行断点织补与桥下空间利用均为概念建议

市政与新型基础设施

- 智慧灯杆、智慧座椅、信息亭、AI导览屏与无人配送柜构成智能基础组件
- 雨水花园与生态植草沟落实海绵要求；织点标准含活动电源预留与聚合脱敏数据展示
- 端侧算力+公共感知：织源共享算力工坊预留算力接口，织绿翼生态传感与小月河水环境监测并网联动

蓝绿空间

248.97万m²

绿地面积

21.8%

全带绿地率


8处

织点广场

0.6%

公共空间率

公共空间约 6.8 万m²，织点广场价值在连通性而非面积规模；织点标准：无障碍通行、公共座椅、饮水、信息亭、应急呼叫人工优先、活动电源、聚合脱敏数据展示、生态友好夜间照明。

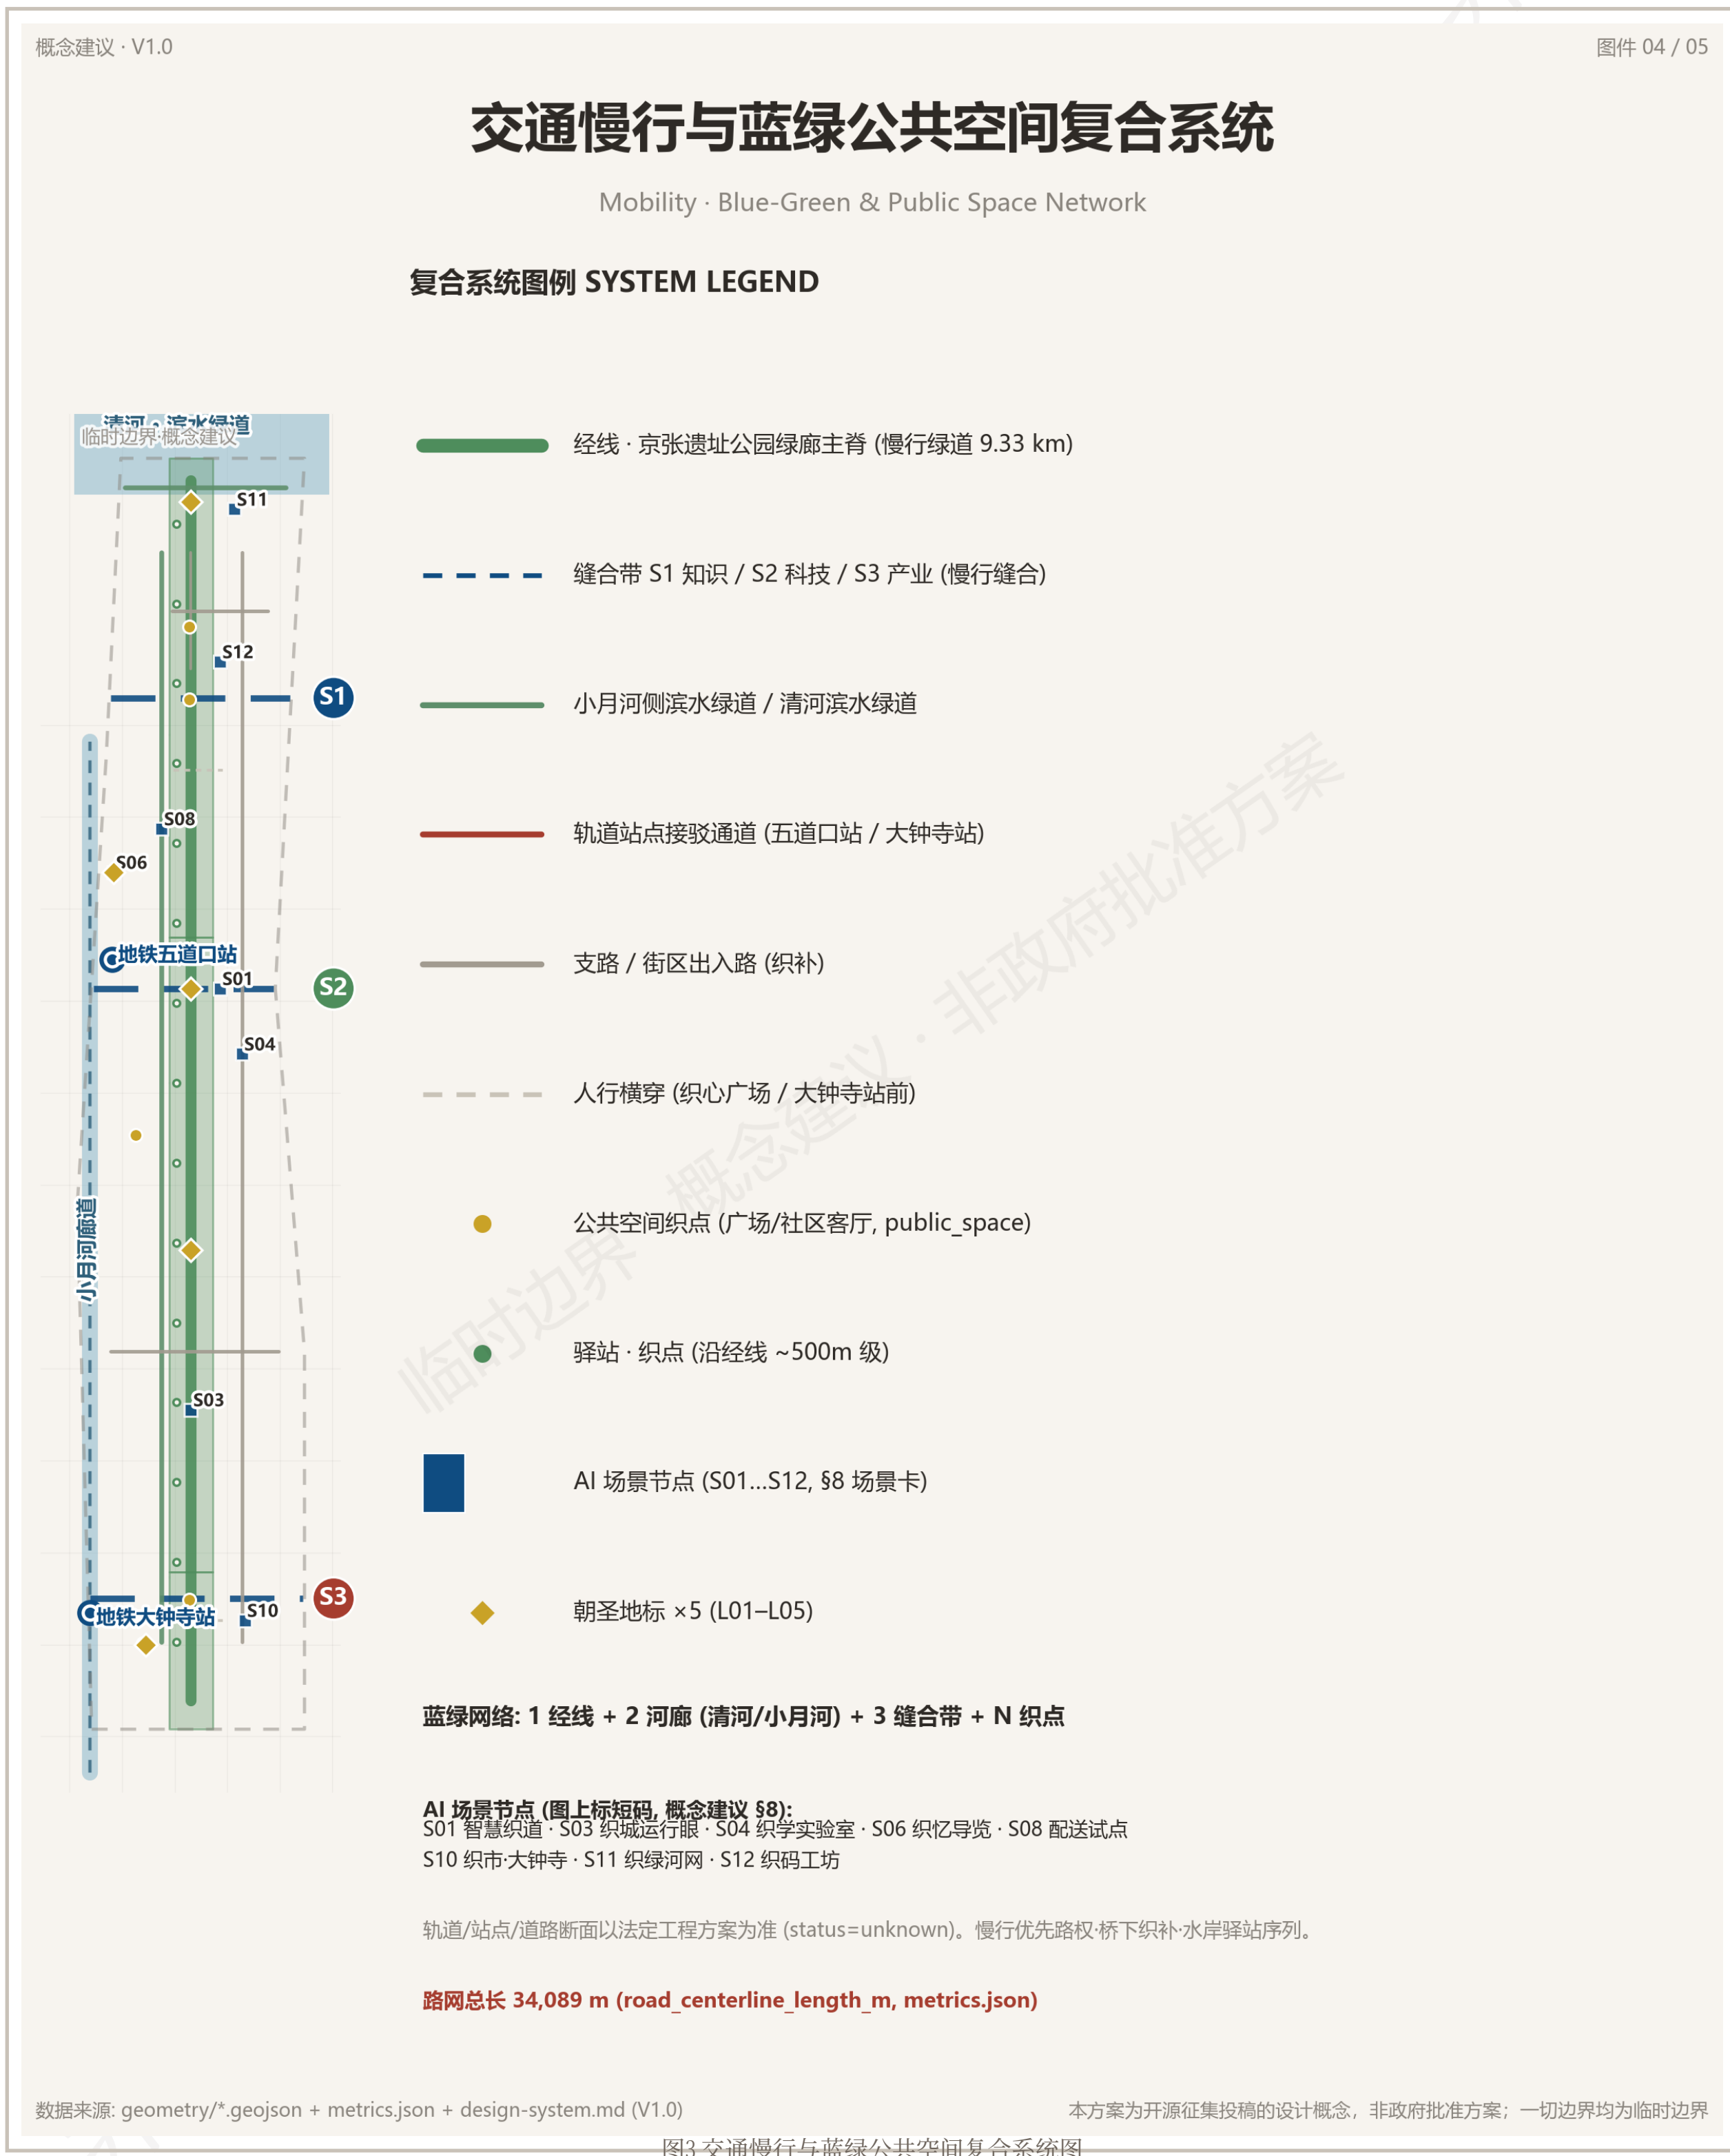

临时边界 · 概念建议 —— 本图边界为公开资料推算的临时多边形（PROV-SITE-001 / PROV-KEY-001/002/003），非官方红线，正式图件发布后需复算全部边界与指标

三区重点区域详设

织源 · 众智园AI自主创新加速区（约192.1公顷）

- 定位：AI全栈自主创新加速区，承担源头创新、中试熟化与测试验证
- 织源广场为核心，科研与孵化楼宇为主体，预留共享算力工坊与测试验证街区
- 风险：现状建成区权属复杂、更新单元划分与交通承载力待确认（高风险）

织心 · 北京AI原点社区（约104.3公顷）

- 定位：世界级AI创新生态的人才、社区与文化原点引擎
- 清华园车站旧址原点广场组织混合街区织补，配置人才公寓与社区服务设施
- 地铁五道口站接驳枢纽；风险：高密度建成区、交通压力与历史建筑保护平衡，文保以文物部门公布为准

织声 · 大钟寺AI产业集聚区（约72.0公顷）

3

重点区域

368.4ha

合计范围

- 定位：AI产业集聚与AI原生消费场景高地
- 大钟寺站前人行通道组织站点衔接；钟声织网文化节点与消费街段联动
- 风险：站点周边既有规划约束与古钟博物馆保护距离

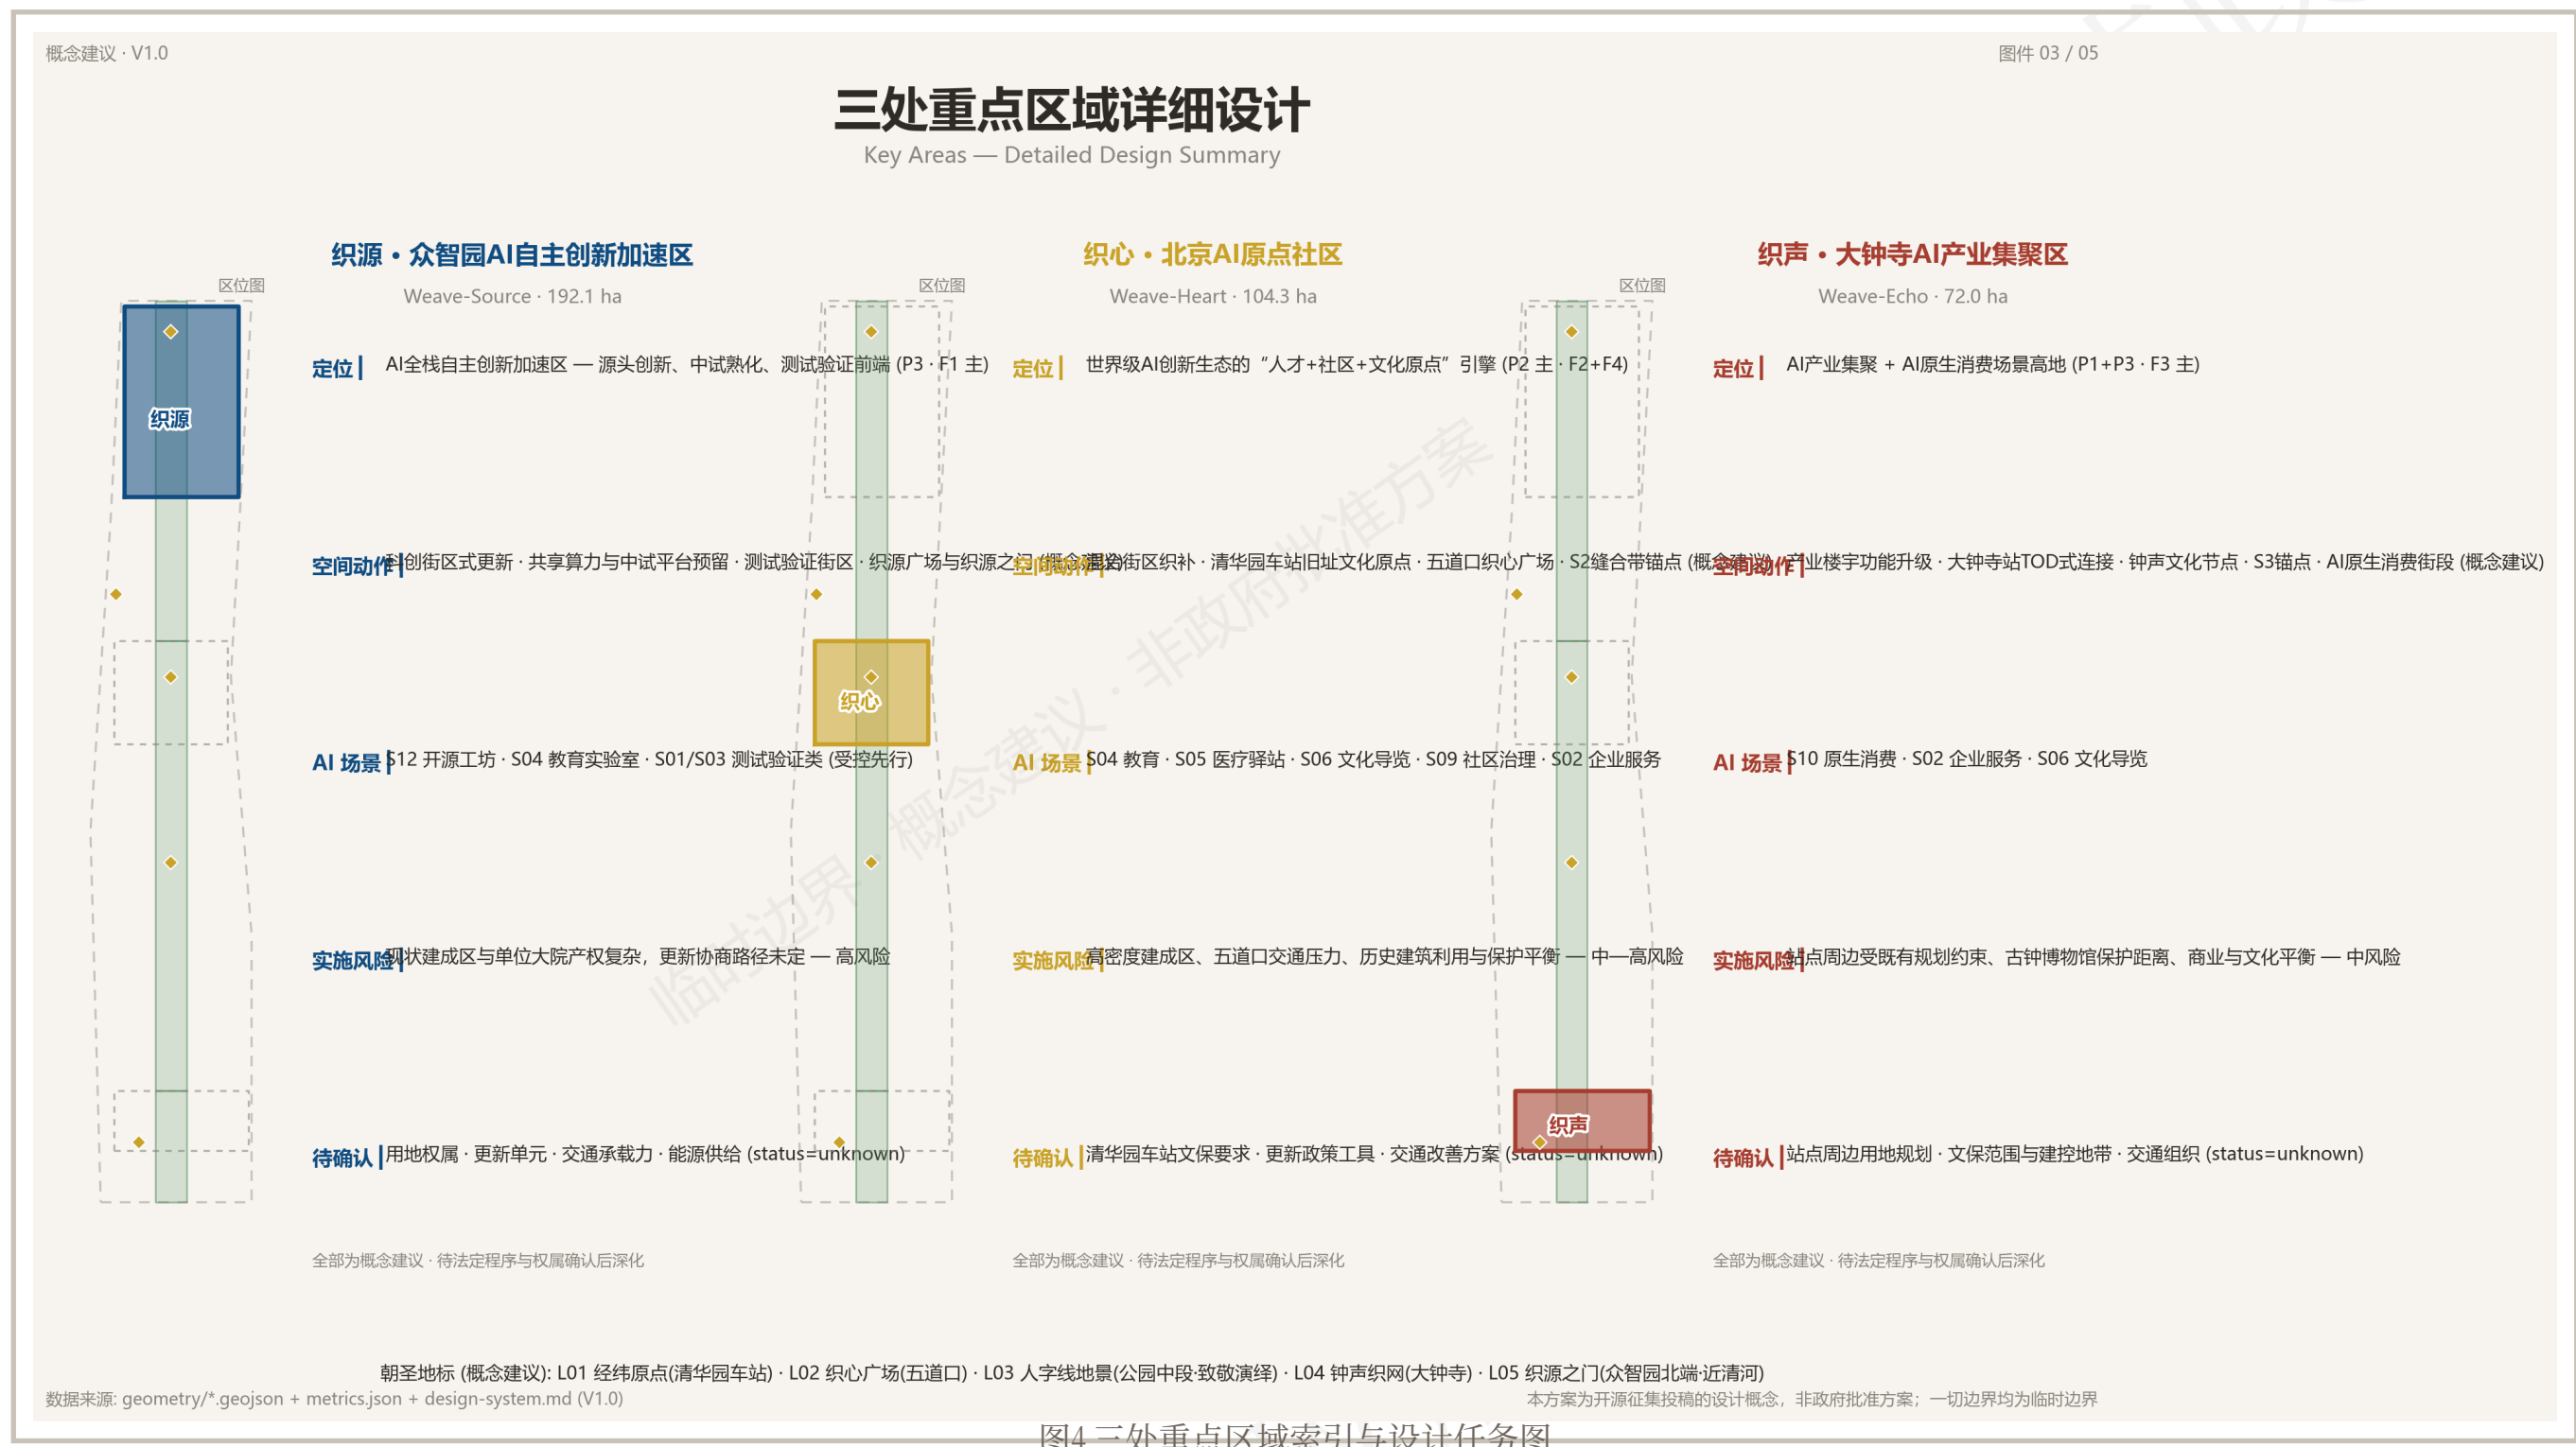


图4 三处重点区域索引与设计任务图

临时边界 · 概念建议 —— 本图边界为公开资料推算的临时多边形（PROV-SITE-001 / PROV-KEY-001/002/003），非官方红线，正式图件发布后需复算全部边界与指标

AI场景与指标合规

场景体系（场景前置规划）

12 场景卡	4 测试验证	3 公共服务	3 文化消费	2 产业服务
-----------	-----------	-----------	-----------	-----------

- 测试验证类（受控街区先行 · 人工复核）：S01智慧织道 / S03织城运行眼 / S05织康驿站 / S08织递配送试点
- 公共服务类：S04织学开放实验室 / S09织邻议事 / S11织绿河网；文化消费类：S06织忆导览 / S07织光自演 / S10织市大钟寺
- 产业服务类：S02织务数字员工 / S12织码工坊
- 六画像：织码人/织梦者/织航者/织居人/织学者/织龄人；四项硬性：数据最小化/来源可追溯/可解释/人工复核兜底

指标复核（metrics.json 溯源）

1141.3万m ² 全带面积	21.8% 绿地率	0.6% 公共空间率	34.1km 道路中心线	23 图斑	3 分期
-------------------------------	--------------	---------------	-----------------	----------	---------

统一口径复算、公式可复核：场地=site_boundary多边形面积；绿地率=绿地并集/场地；公共空间率=广场并集/场地；道路=中心线长度之和；图斑/分期/重点区按数量计数。容积率与高度 status=unknown, 不参与复算结论。

合规与对外口径

- 三矩阵（compliance / standard / design_depth）与正文互为印证；正文可读解释，矩阵机器复核
- 对外口径：开源征集投稿的设计概念，非政府批准方案
- 未使用未授权字体、商标与图片；织梭为原创几何抽象；文化史实仅用公开锚点



图5 核心指标复算与证据链图