



JINGZHANG RISING 京张向上

A Century of Self-Reliance, Rising in the Shape of 人

A0 Exhibition Boards

Open call for the Centennial Jing-Zhang AI Innovation Belt · package cf3901646

A conceptual recommendation for an open call. Not a statutory plan, approval basis or government decision.

The site extent and key areas use the organiser's provisional rough surrogate boundary.

All metrics are recomputed from the package geometry layers in EPSG:4548 and must be rebuilt once official data is published.



Fig.01 Overall Structure: One Spine, Three Terraces, Two Wings

JINGZHANG RISING 京张向上 · A Century of Self-Reliance, Rising in the Shape of 人 — The heritage park spine links three key areas and two wings · conceptual proposal

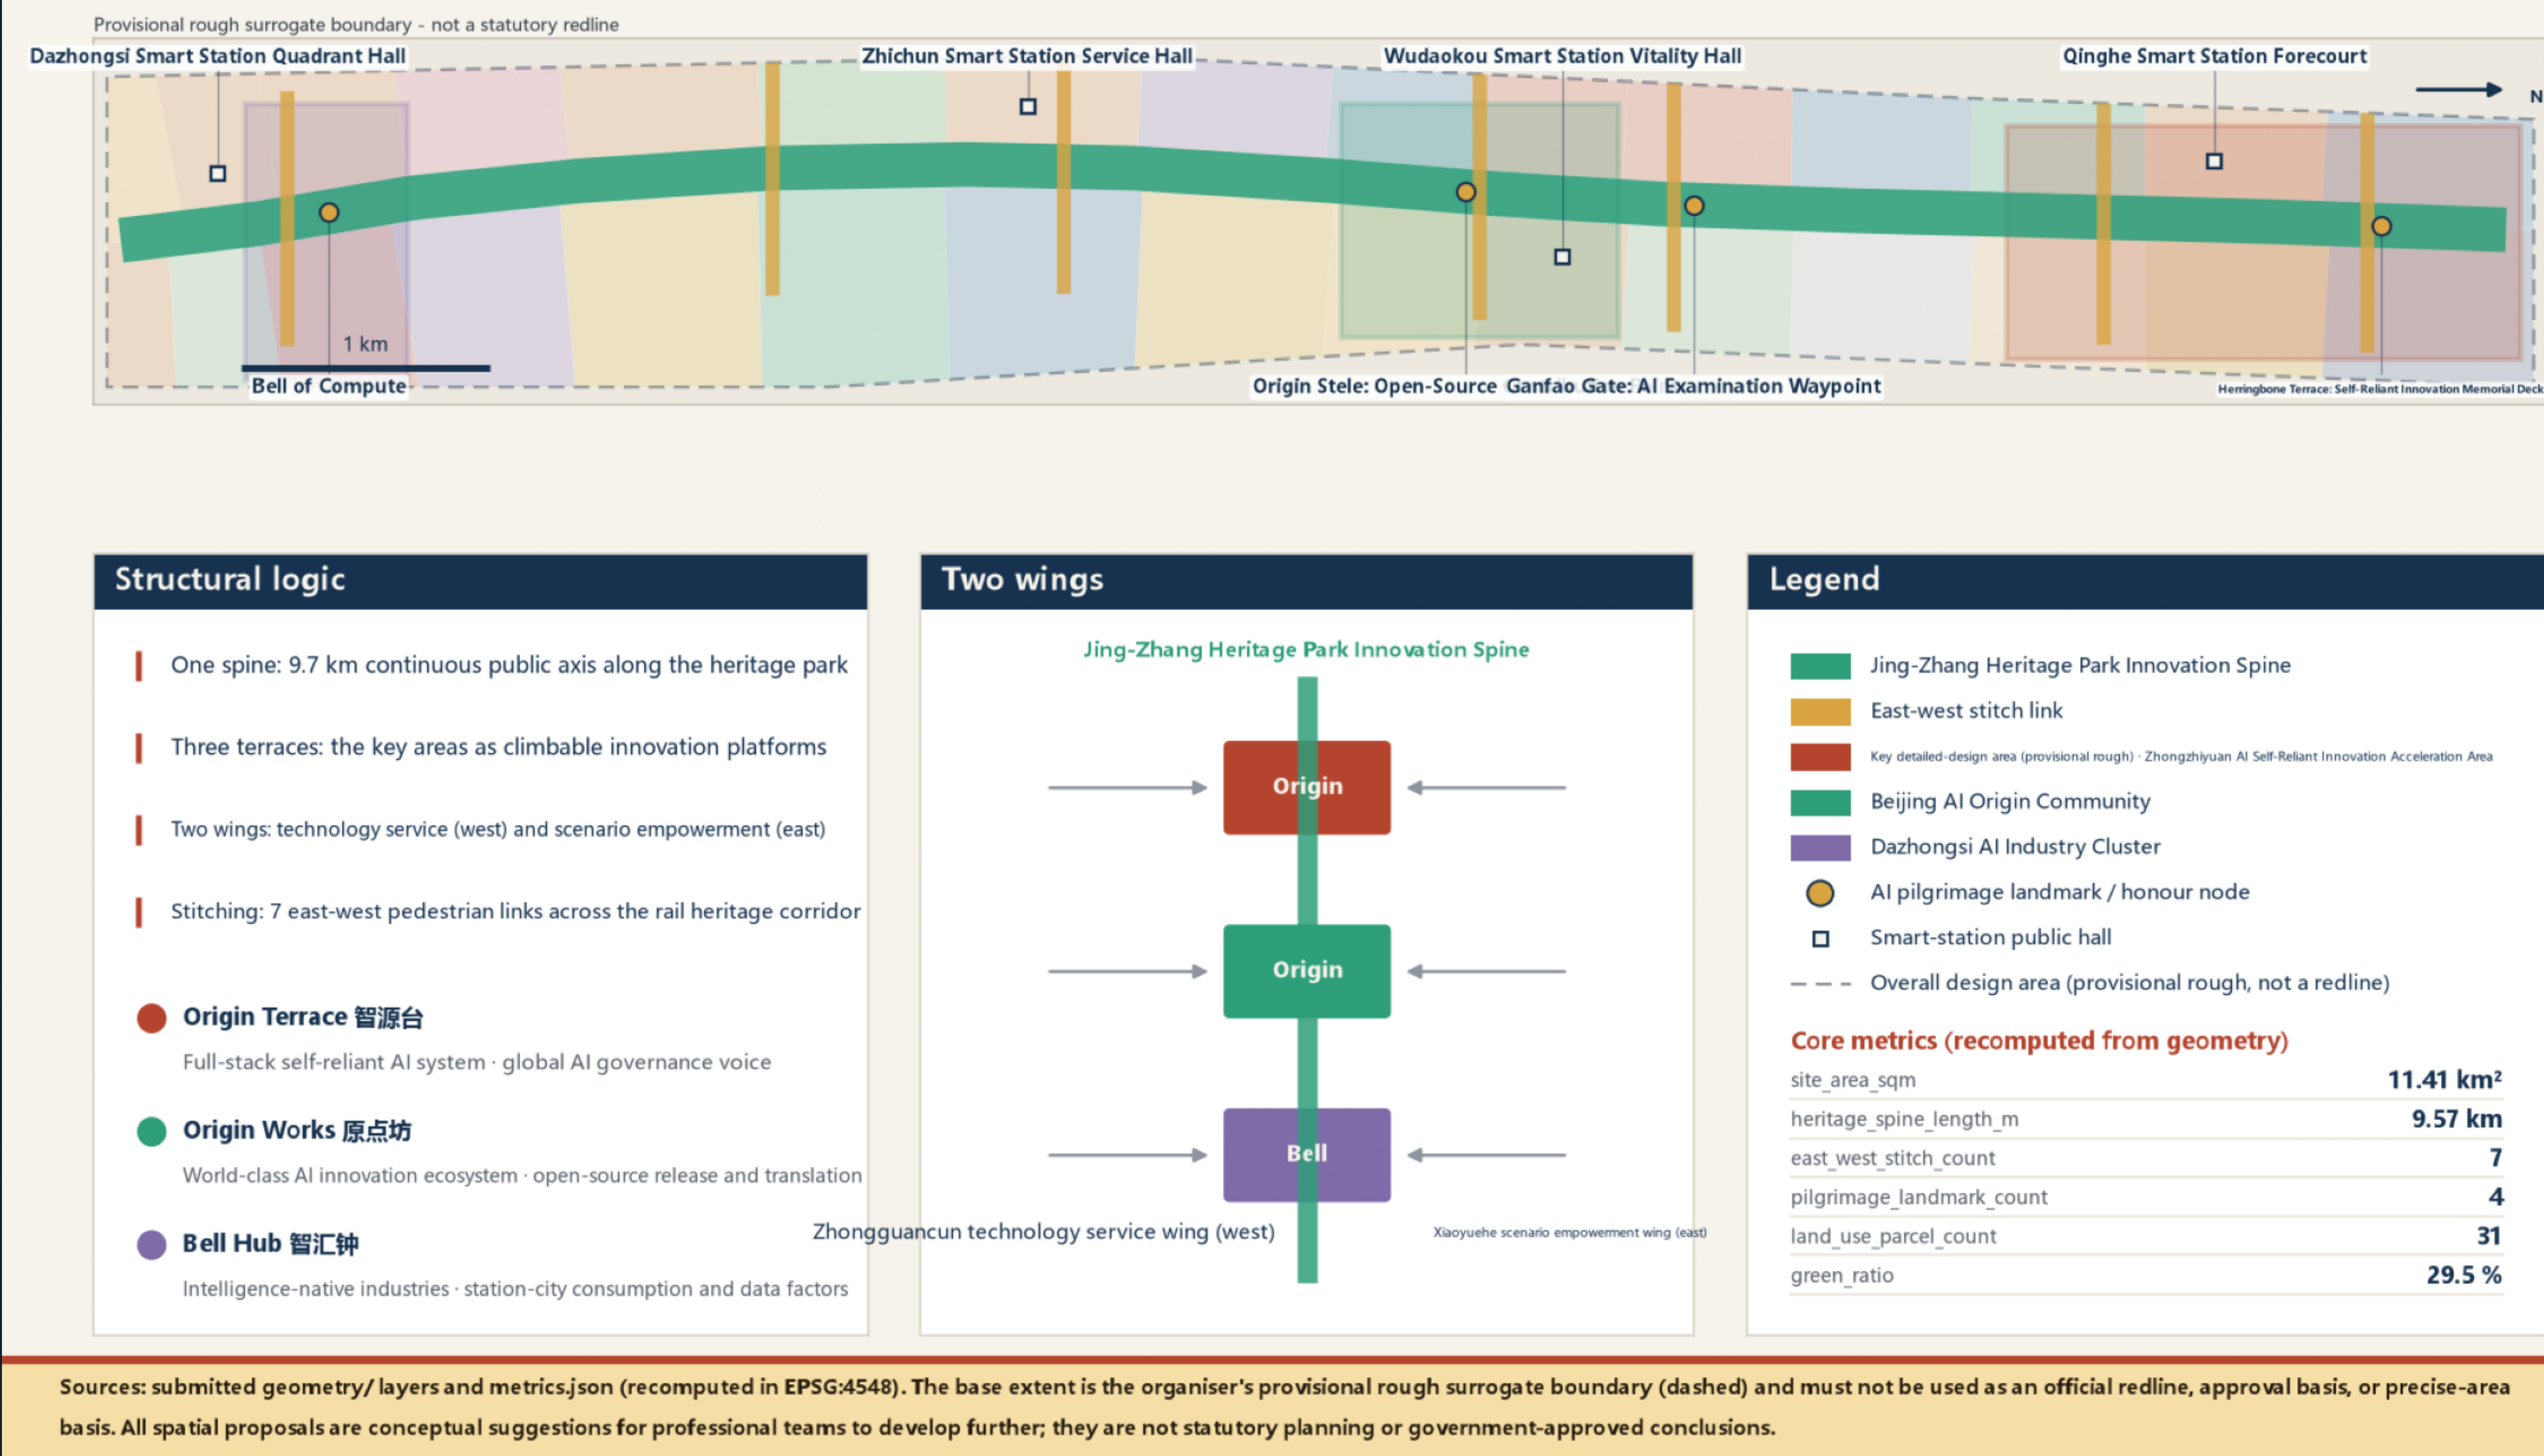


Fig.02 Land-Use Structure and Anchor Catchment Partition

JINGZHANG RISING 京张向上 — Smart-station and innovation-anchor catchments fully partition the design area · no gaps, no overlaps

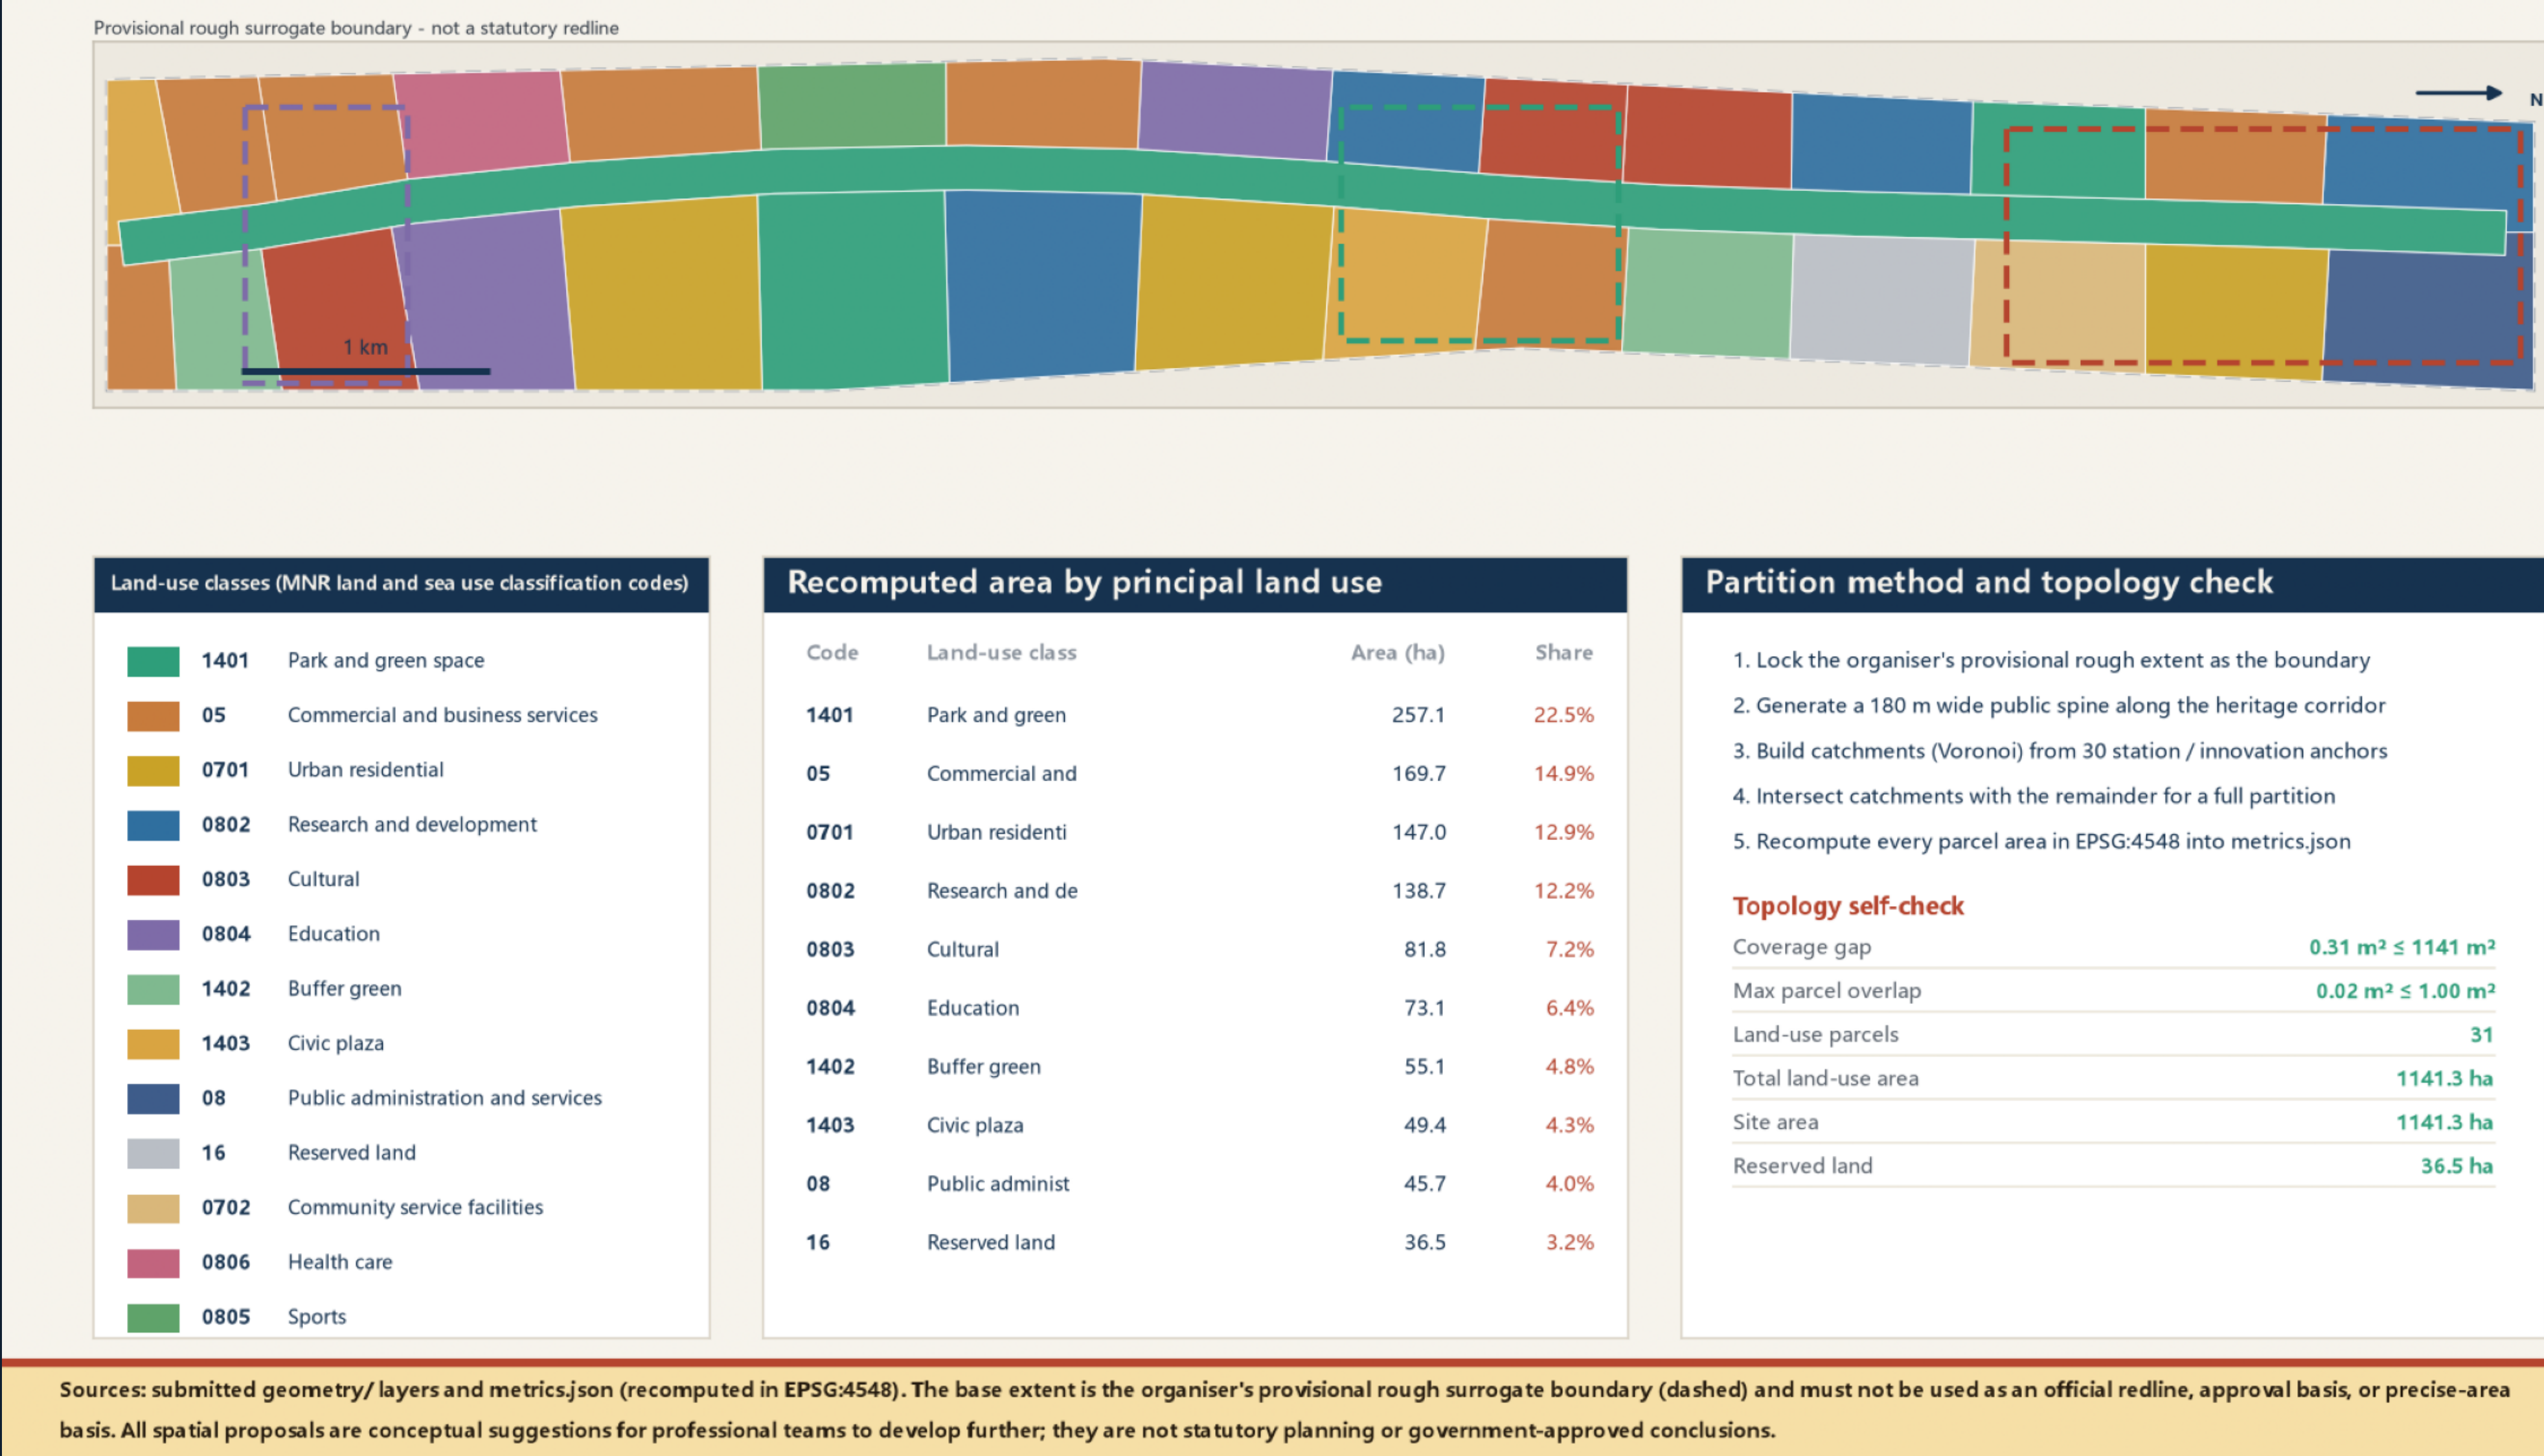


Fig.03 Detailed Design Index of the Three Key Areas

JINGZHANG RISING 京张向上 — Zhongzhiyuan · AI Origin Community · Dazhongsi: role, spatial moves and renewal logic

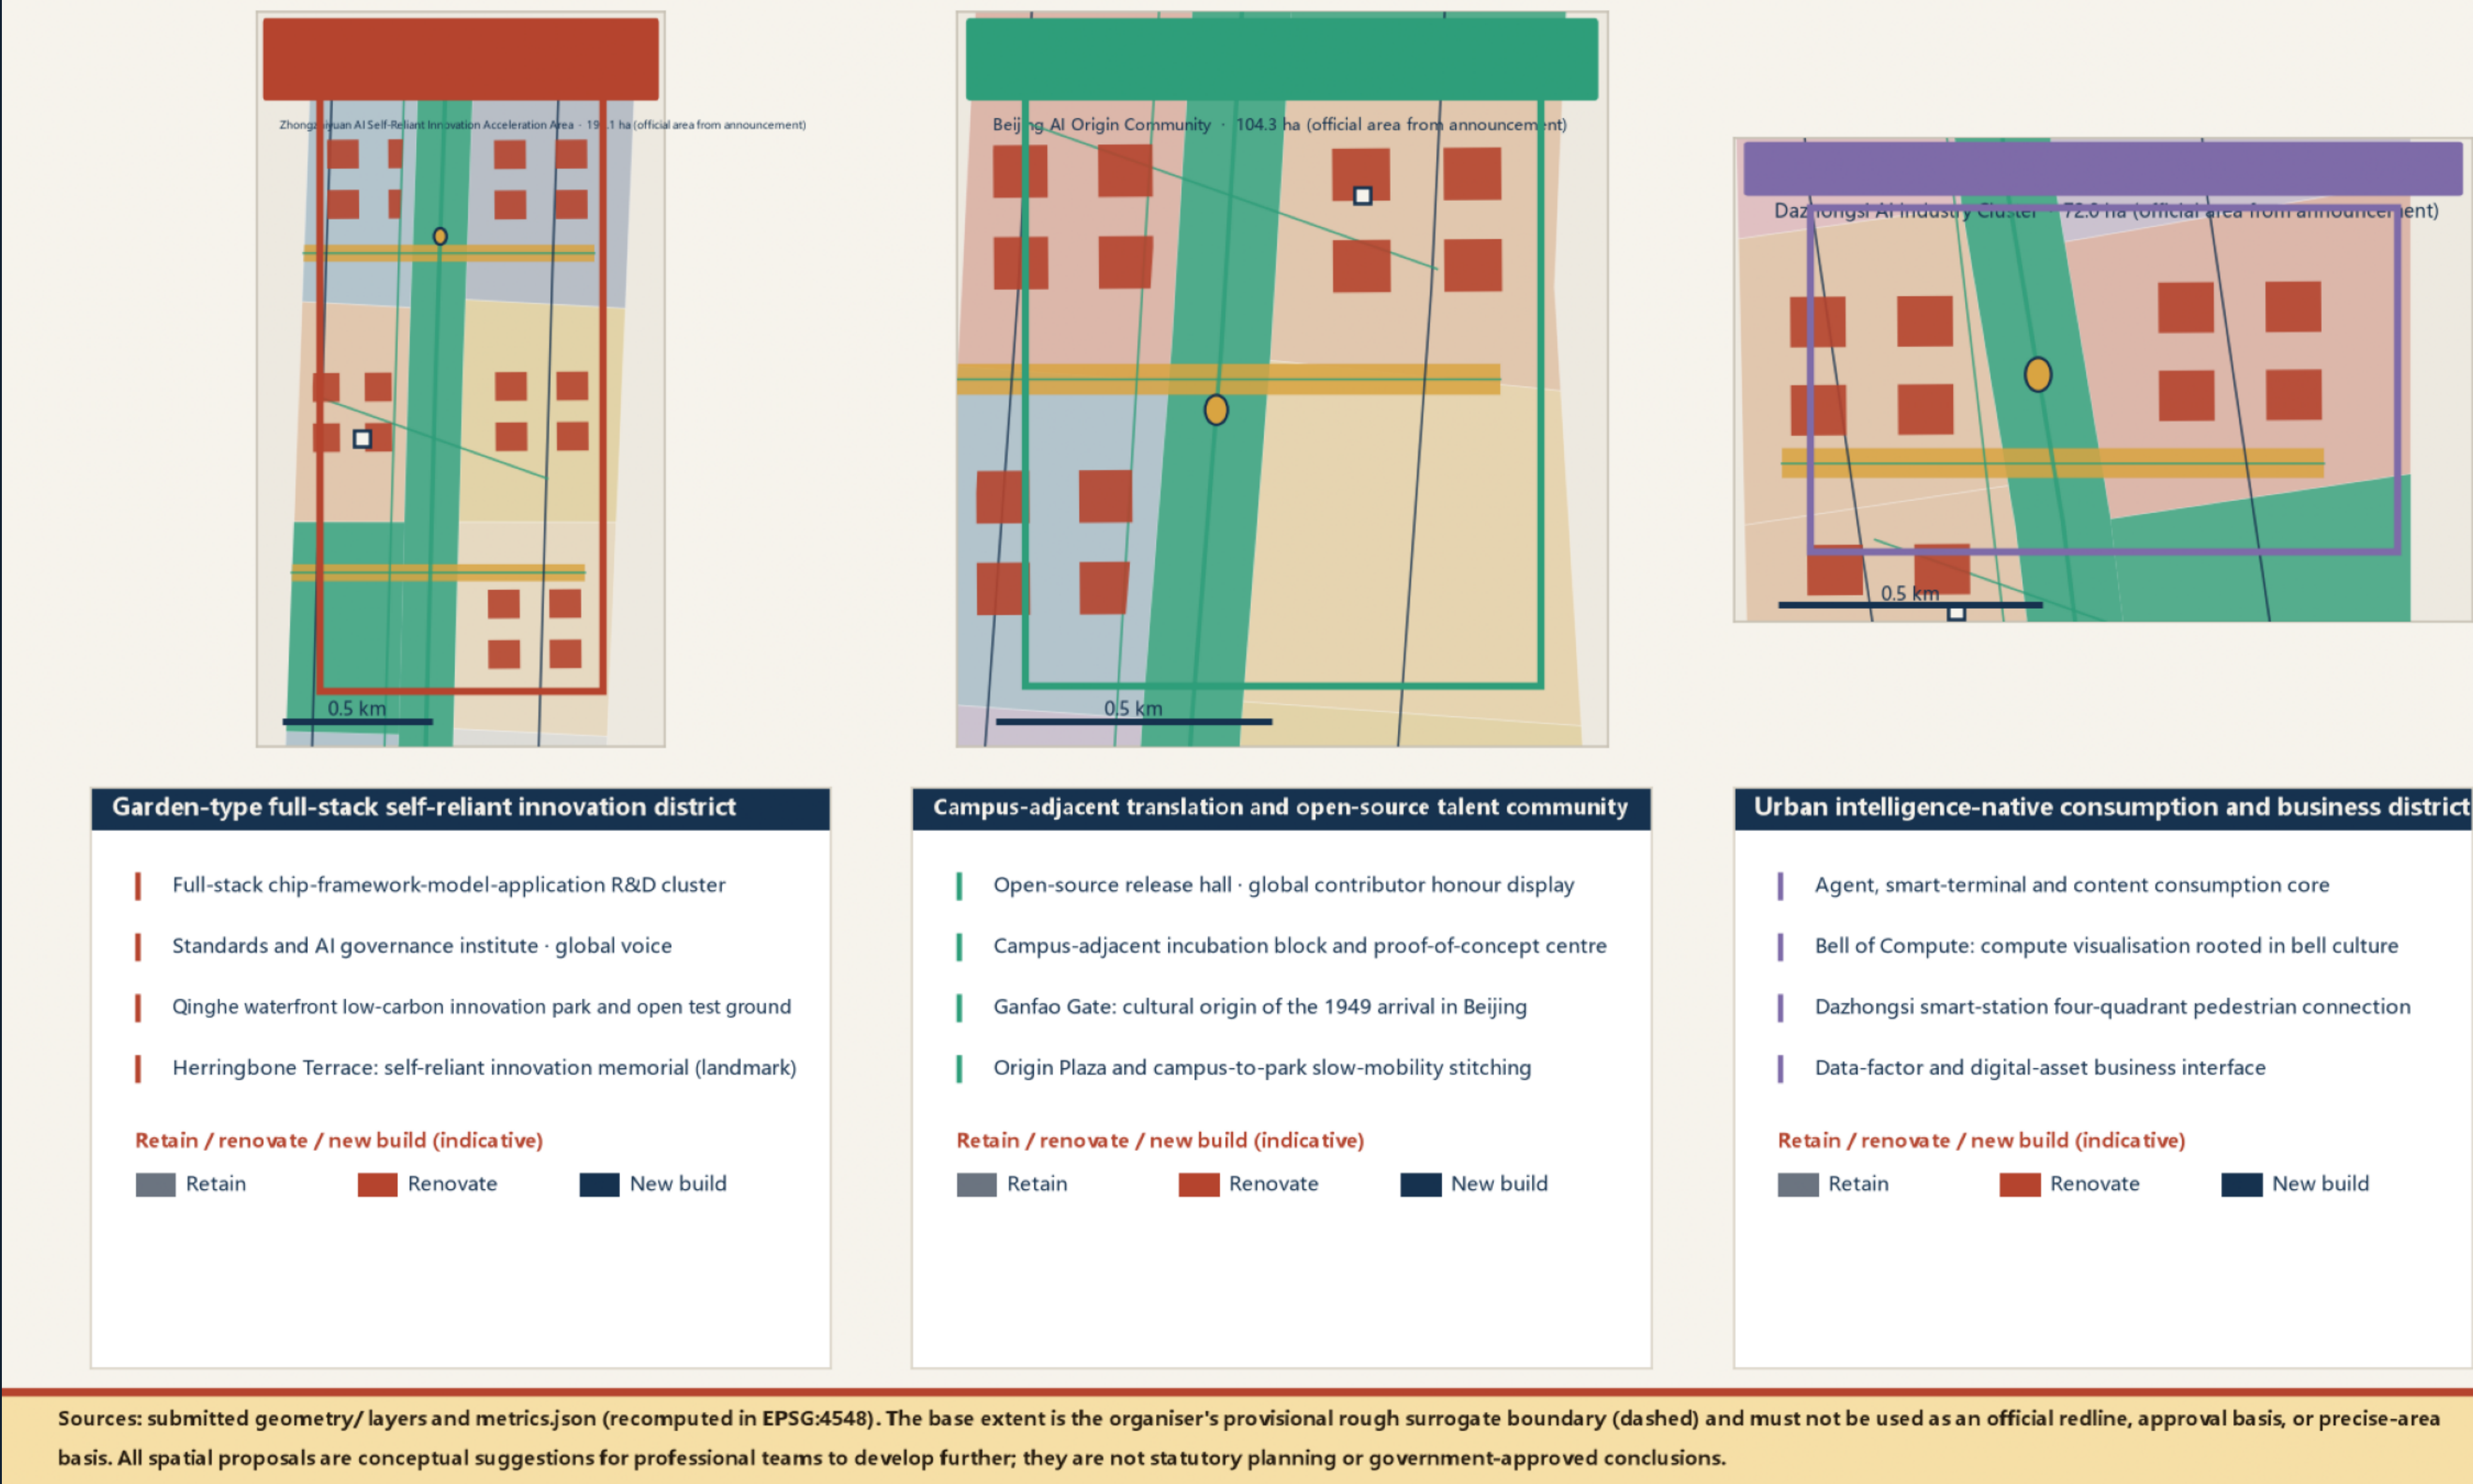


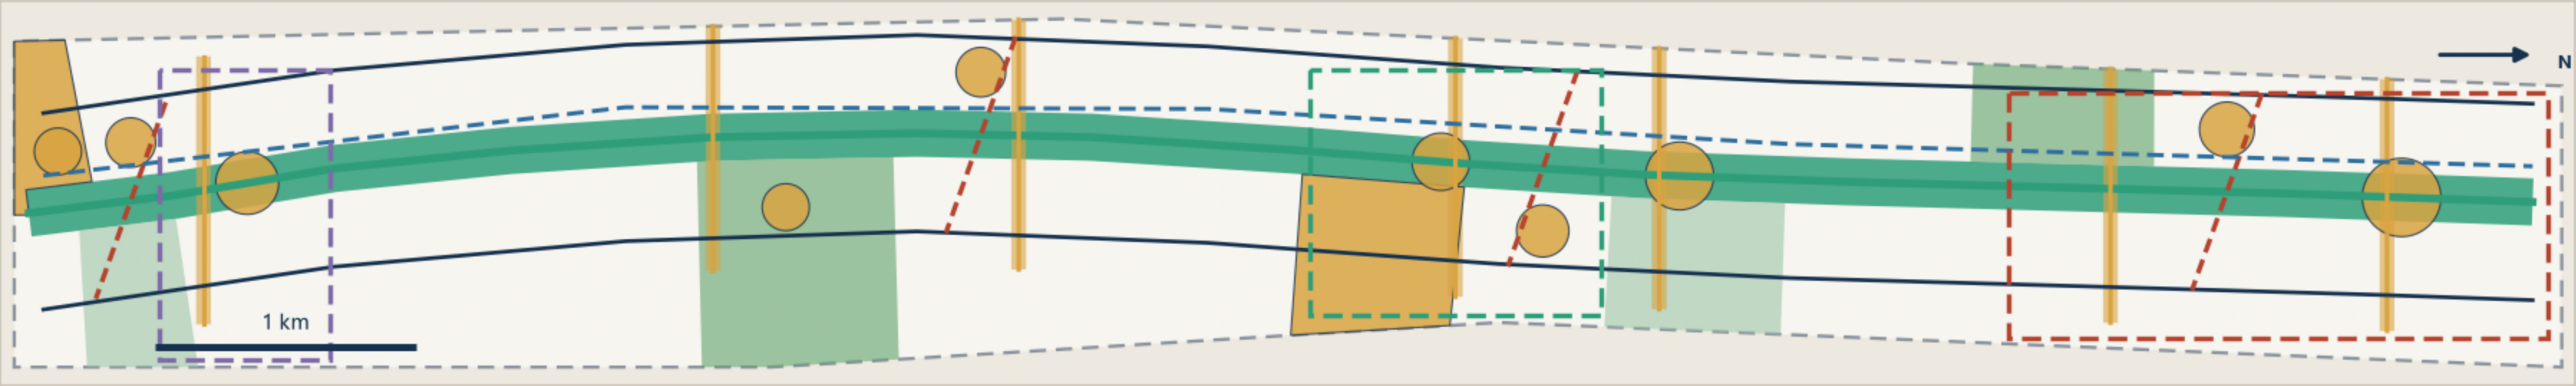


Fig.04 Mobility and Blue-Green Public Space System

JINGZHANG RISING 京张向上 — Continuous greenway spine + seven east-west stitch links + smart-station interchange



Provisional rough surrogate boundary - not a statutory redline



Legend	
	Principal greenway (slow-mobility spine)
	Commuter cycleway
	Secondary street / micro-circulation
	East-west stitch link
	Smart-station connector
	Green and open space
	Public space node


Mobility and blue-green metrics	
slow_mobility_network_length_m	25.93 km
road_centrelines_length_m	48.16 km
green_space_area_sqm	336.6 ha
green_ratio	29.49 %
public_space_area_sqm	84.7 ha
public_space_ratio	7.42 %
east_west_stitch_count	7
ai_public_space_node_count	10

Mobility and infrastructure strategy	
North-south continuity	A 9.7 km continuous greenway removes breaks and unifies levels and wayfinding
East-west stitching	Seven pedestrian links cross the rail corridor to join campuses, parks and communities
Station-city integration	Four station connectors organise cycle interchange, quadrant walking and forecourts
Green mobility	Commuter cycleway separated from the leisure greenway to reduce conflicts
Utilities and new infrastructure	Edge-compute waypoints, distributed energy and charging co-located with public nodes
Accessibility	Continuous barrier-free and age-friendly design along the whole belt

Sources: submitted geometry/ layers and metrics.json (recomputed in EPSG:4548). The base extent is the organiser's provisional rough surrogate boundary (dashed) and must not be used as an official redline, approval basis, or precise-area basis. All spatial proposals are conceptual suggestions for professional teams to develop further; they are not statutory planning or government-approved conclusions.

Fig.05 Recomputed Metrics and Evidence Chain

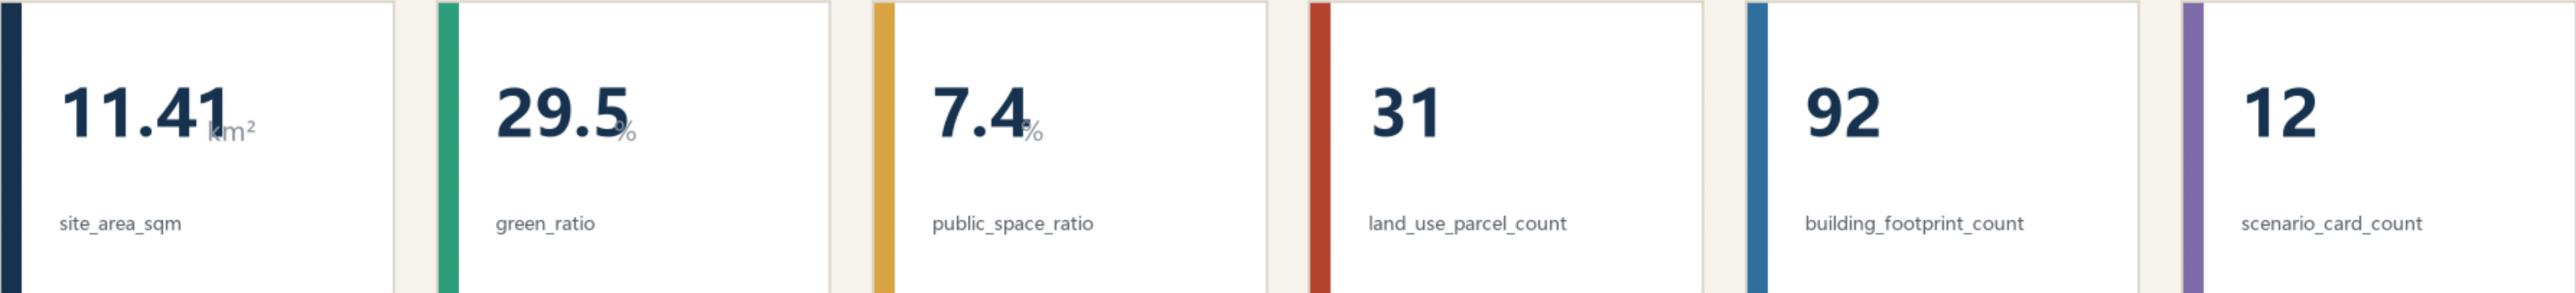JINGZHANG RISING 京张向上 — Core metrics, task coverage and self-check state all recomputed from structured files



Recomputation chain (geometry → metric → text)	
geometry/site_boundary.geojson → site_area_sqm	1141.3 ha
geometry/land_use.geojson → land_use_total_area_sqm	1141.3 ha
geometry/green_space.geojson → green_space_area_sqm	336.6 ha
geometry/public_space.geojson → public_space_area_sqm	84.7 ha
geometry/buildings.geojson → building_footprint_area_sqm	83.2 ha
geometry/roads.geojson → road_centrelines_length_m	48.16 km
geometry/phasing.geojson → phase_one_area_sqm	514.9 ha
geometry/key_areas.geojson → key_area_total_area_sqm	369.3 ha
geometry/constraints.geojson → constraint_feature_count	4

Task coverage	
Announcement tasks 1.3 / 1.4 / 1.5	17 of 17 covered
Agent taskbook agent.1-agent.6	6 of 6 covered
Mandatory professional standards	6 of 6 answered
Formal design-depth items	15 of 15 complete
AI scenario cards	12 (required ≥10)
Industry test scenarios	4 (required ≥3)
User personas	6 (required ≥5)
Pilgrimage landmarks and honour nodes	4 (required ≥3)
Global AI ecosystem cases	8 (required 5-8)

Self-check state	
Deterministic validation	PASS
Spatial review	PASS
Visual packaging check	PASS
Professional evidence review	PASS
Pending official data	
floor_area_ratio	Pending official data
building_height_control_m	Pending official data
total_floor_area_sqm	Pending official data
Once official boundaries and regulatory conditions are published, geometry, metrics, figures and all four self-check gates must be regenerated before revision.	

Sources: submitted geometry/ layers and metrics.json (recomputed in EPSG:4548). The base extent is the organiser's provisional rough surrogate boundary (dashed) and must not be used as an official redline, approval basis, or precise-area basis. All spatial proposals are conceptual suggestions for professional teams to develop further; they are not statutory planning or government-approved conclusions.