



京张向上 JINGZHANG RISING

百年自主 · 人字向上

A0 展板 · Exhibition Boards

百年京张AI创新带城市设计开源征集 · 提交包 cf3901646

本文册为面向开源征集的概念建议，不构成法定规划、审批依据或政府决策。


范围与重点区采用组织方发布的临时粗略替代边界（provisional），

全部指标由提交包 geometry/ 图层在 EPSG:4548 下复算，官方边界发布后须整体重算。




图01 总体空间结构：一脉三台两翼

京张向上 JINGZHANG RISING · 百年自主·人字向上 — 京张遗址公园主脉串联三处重点区与两翼·概念建议

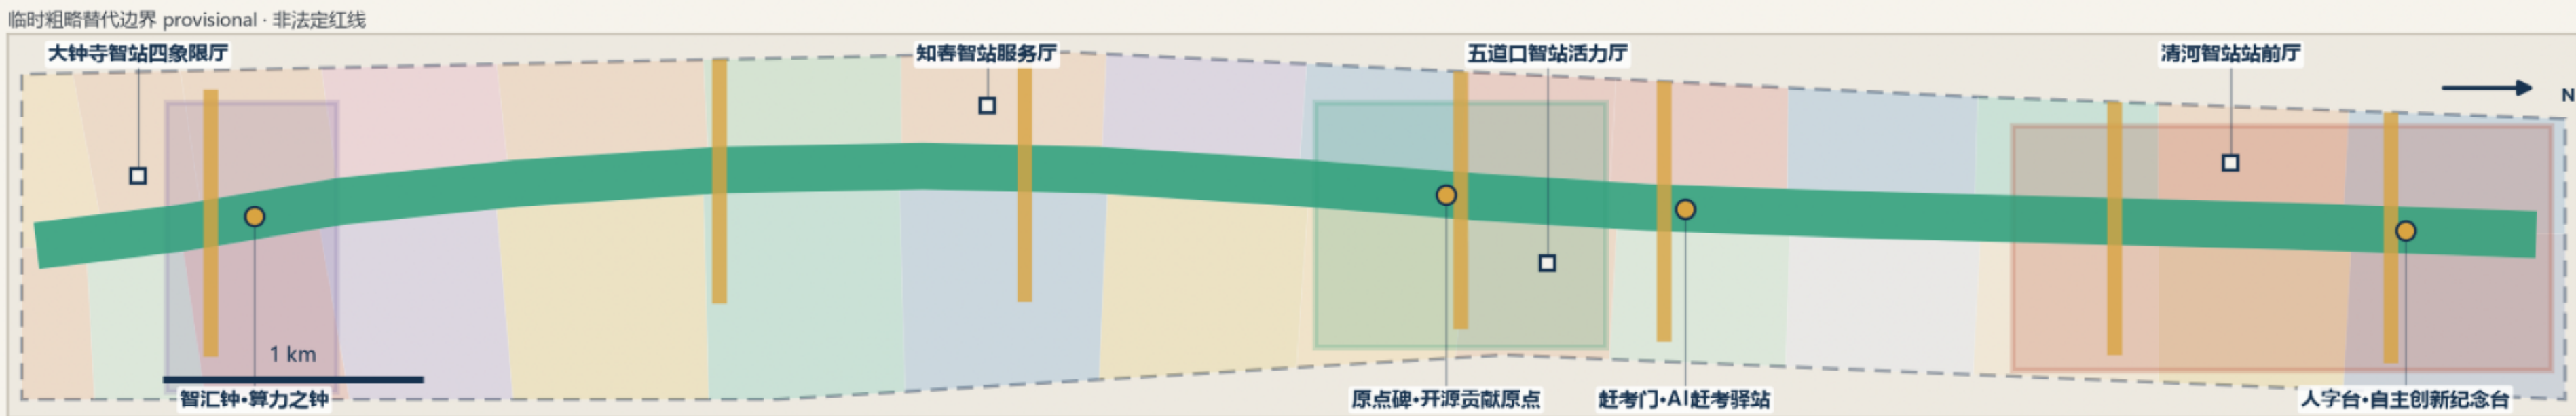

结构逻辑	
一脉	京张遗址公园南北贯通，9.7公里连续公共主轴
三台	三处重点区域作为可攀登的创新平台
两翼	西侧科技服务、东侧场景赋能双向赋能
双缝	7条东西缝合步行链跨越铁路遗址廊道
智源台 Origin Terrace	
AI全栈自主创新体系·AI治理全球话语权	
原点坊 Origin Works	
世界级AI创新生态·开源发布与成果转化	
智汇钟 Bell Hub	
智能原生新业态·站城一体消费与数据要素	

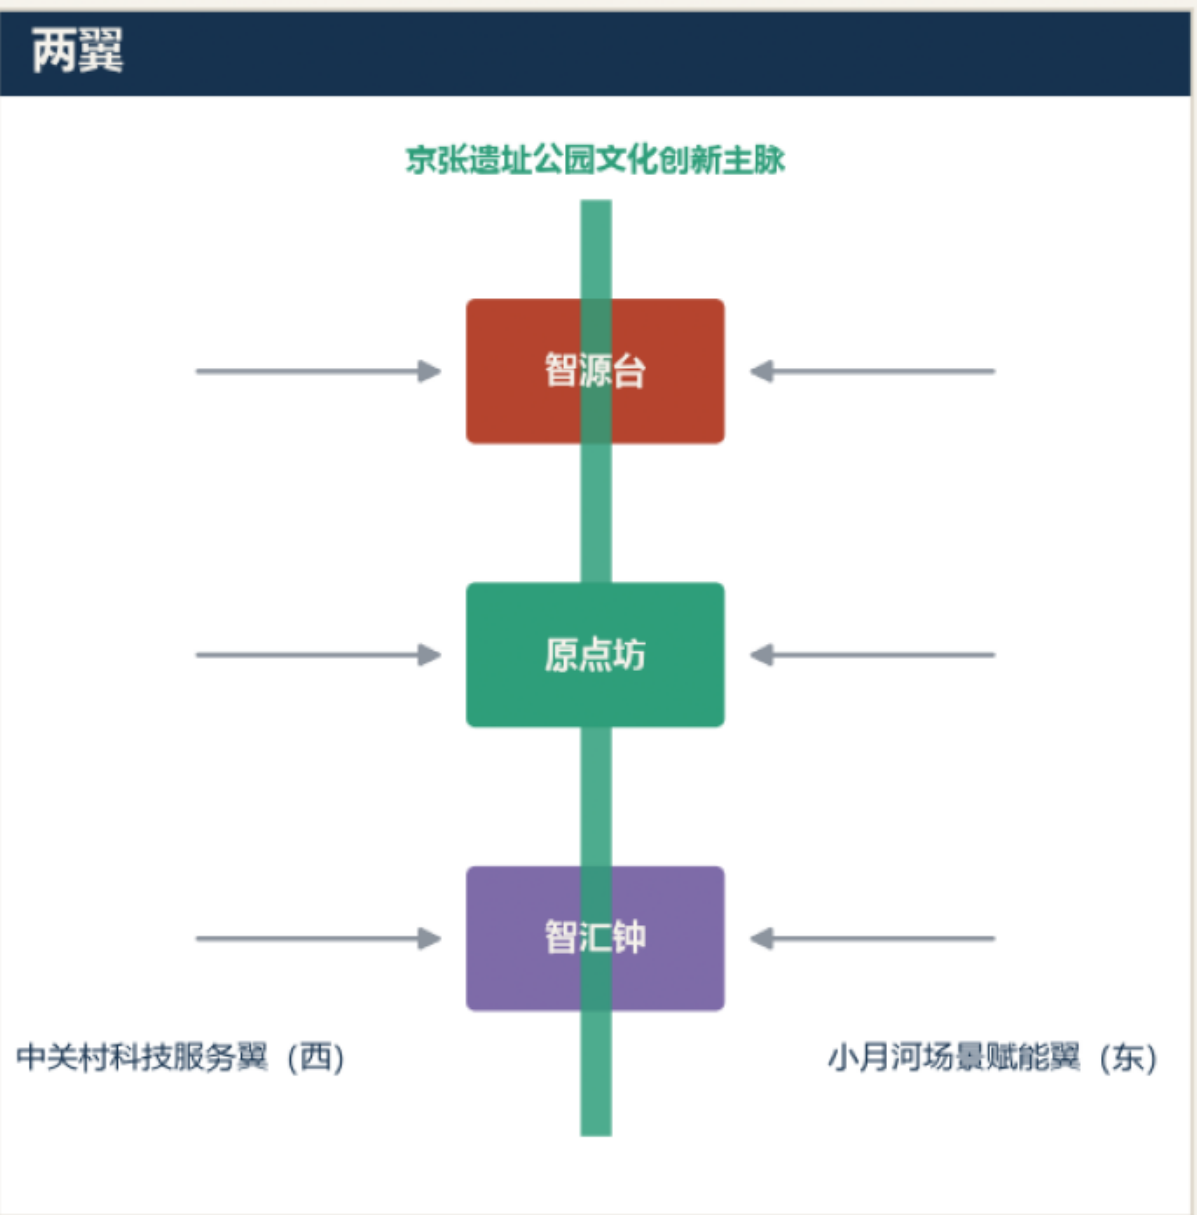

图例	
■	京张遗址公园文化创新主脉
■	东西缝合绿链
■	重点详细设计区域（临时粗略）·众智园AI自主创新加速区
■	北京AI原点社区
■	大钟寺AI产业聚集区
●	AI朝圣地标 / 荣誉节点
□	智站公共厅
---	总体设计范围（临时粗略·非红线）
核心指标（由几何复算）	
site_area_sqm	11.41 km²
heritage_spine_length_m	9.57 km
east_west_stitch_count	7
pilgrimage_landmark_count	4
land_use_parcel_count	31
green_ratio	29.5 %

数据来源：提交包 geometry/ 图层与 metrics.json（EPSG:4548 复算）；范围虚图为用户发布的临时粗略替代边界（provisional，虚线），不得作为正式红线、审批依据或精确面积依据。所有空间落地内容均为概念建议，可供专业团队深化研究，不构成法定规划或政府审定结论。

图02 用地结构与锚点服务域划分

京张向上 JINGZHANG RISING — 以智站与创新锚点服务域完整划分总体设计范围·无缝隙、无重叠



用地分类（国土空间用地海分类指南代码）	
■	1401 公园绿地
■	05 商业服务业用地
■	0701 城镇住宅用地
■	0802 科研用地
■	0803 文化用地
■	0804 教育用地
■	1402 防护绿地
■	1403 广场用地
■	08 公共管理与公共服务用地
■	16 留白用地
■	0702 城镇社区服务设施用地
■	0806 医疗卫生用地
■	0805 体育用地


主要用地面积复算			
代码	用地名称	面积(公顷)	占比
1401	公园绿地	257.1	22.5%
05	商业服务业用地	169.7	14.9%
0701	城镇住宅用地	147.0	12.9%
0802	科研用地	138.7	12.2%
0803	文化用地	81.8	7.2%
0804	教育用地	73.1	6.4%
1402	防护绿地	55.1	4.8%
1403	广场用地	49.4	4.3%
08	公共管理与公共服务用地	45.7	4.0%
16	留白用地	36.5	3.2%

划分方法与拓补校验	
1. 锁定组织方临时粗略边界作为提交范围	
2. 沿京张铁路遗址廊道生成 180 米宽公共主脉	
3. 以 30 个智站与创新锚点生成服务域（Voronoi）划分	
4. 服务域与剩余范围求交，得到完整用地分区	
5. 在 EPSG:4548 下复算每个地块面积并写入 metrics	
拓补自检结果	
用地面积缺口	0.31 m² ≤ 1141 m²
地块间最大重叠	0.02 m² ≤ 1.00 m²
用地地块数	31
用地总面积	1141.3 ha
范围面积	1141.3 ha
留白用地	36.5 ha


数据来源：提交包 geometry/ 图层与 metrics.json（EPSG:4548 复算）；范围虚图为用户发布的临时粗略替代边界（provisional，虚线），不得作为正式红线、审批依据或精确面积依据。所有空间落地内容均为概念建议，可供专业团队深化研究，不构成法定规划或政府审定结论。

图03 三处重点区域详细设计索引


京张向上 JINGZHANG RISING — 众智园·AI原点社区·大钟寺：定位、空间动作与更新逻辑

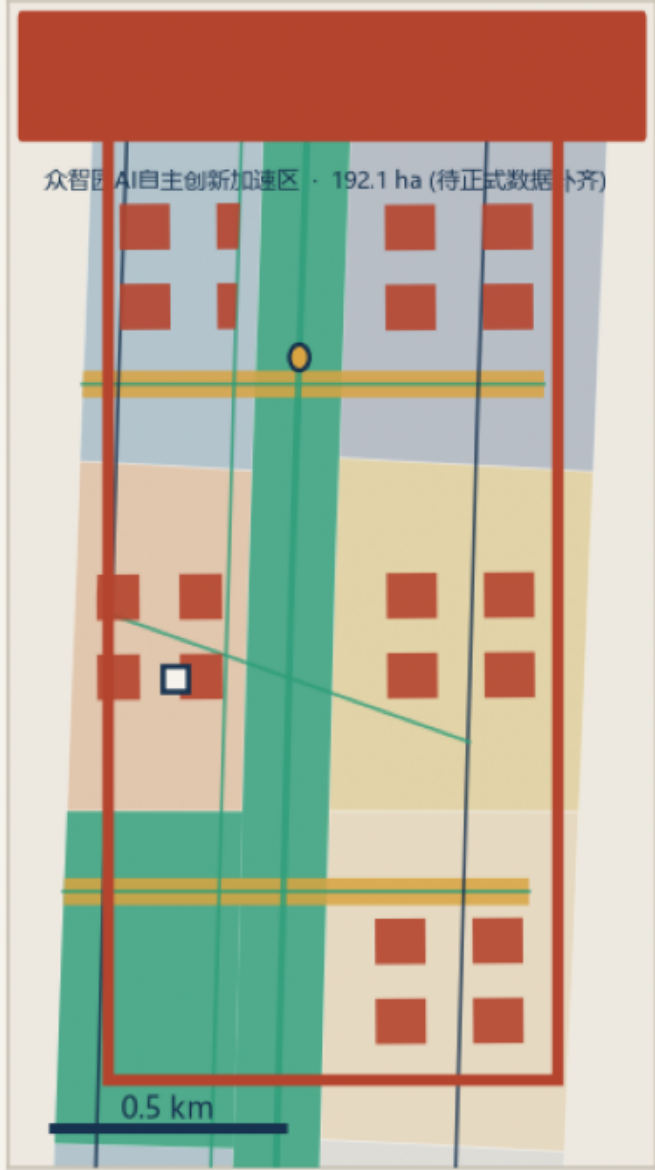

花园型全栈自主创新新街区	
自主芯片—框架—模型—应用全栈研发集群	
标准制定与安全治理院·AI治理话语权	
清河流域低碳创新廊与开放测试场	
人字台：自主创新纪念台（朝圣地标）	
拆改留逻辑（示章）	
■	保留
■	改造
■	新建

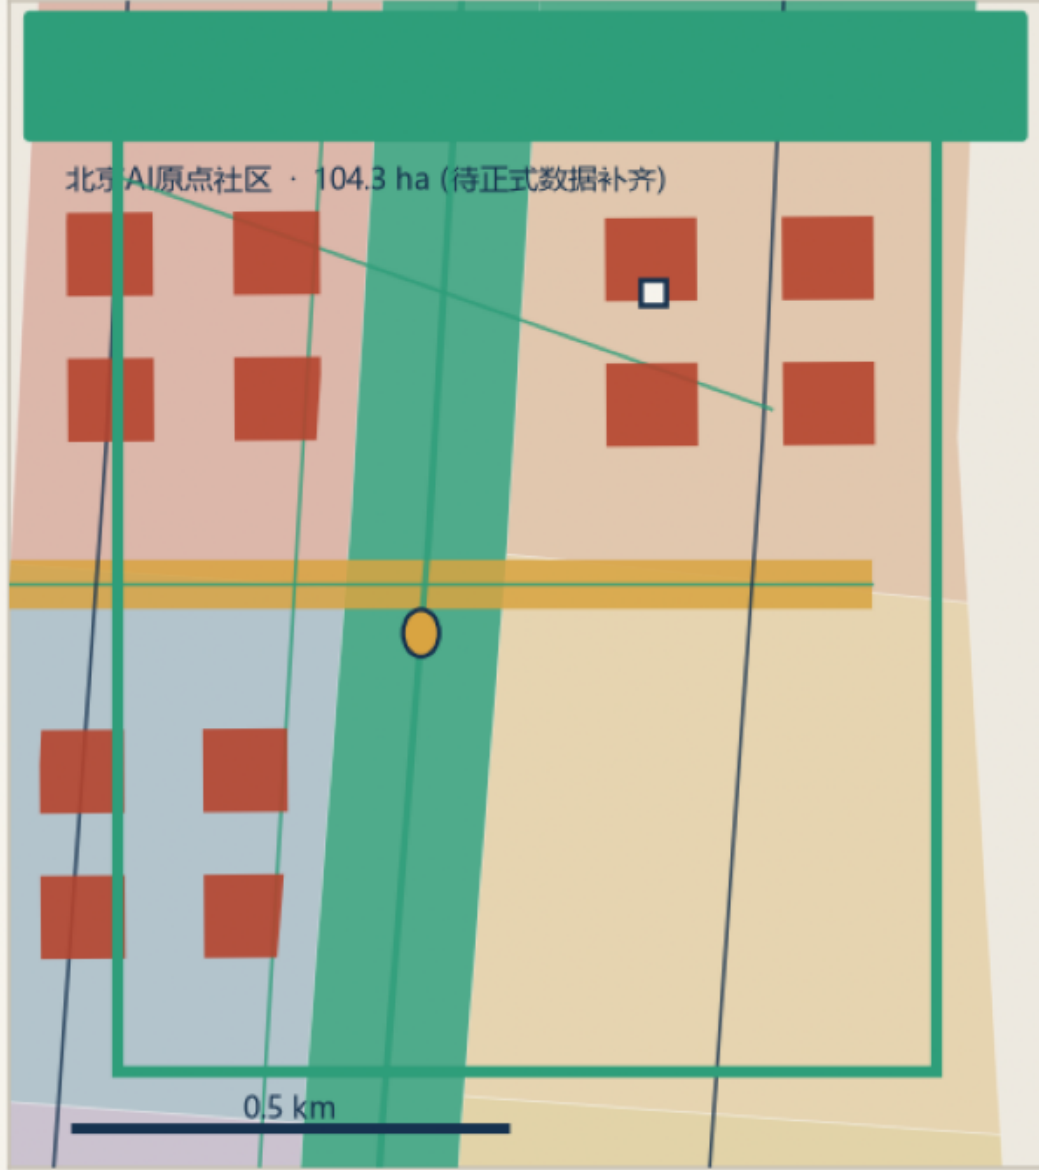

近校型成果转化与开源人才社区	
开源发布厅·全球贡献者荣誉展示	
近校孵化街区与概念验证中心	
赶考门：1949年进京赶考首站文化原点	
原点广场与校区—园区慢行缝合	
拆改留逻辑（示章）	
■	保留
■	改造
■	新建

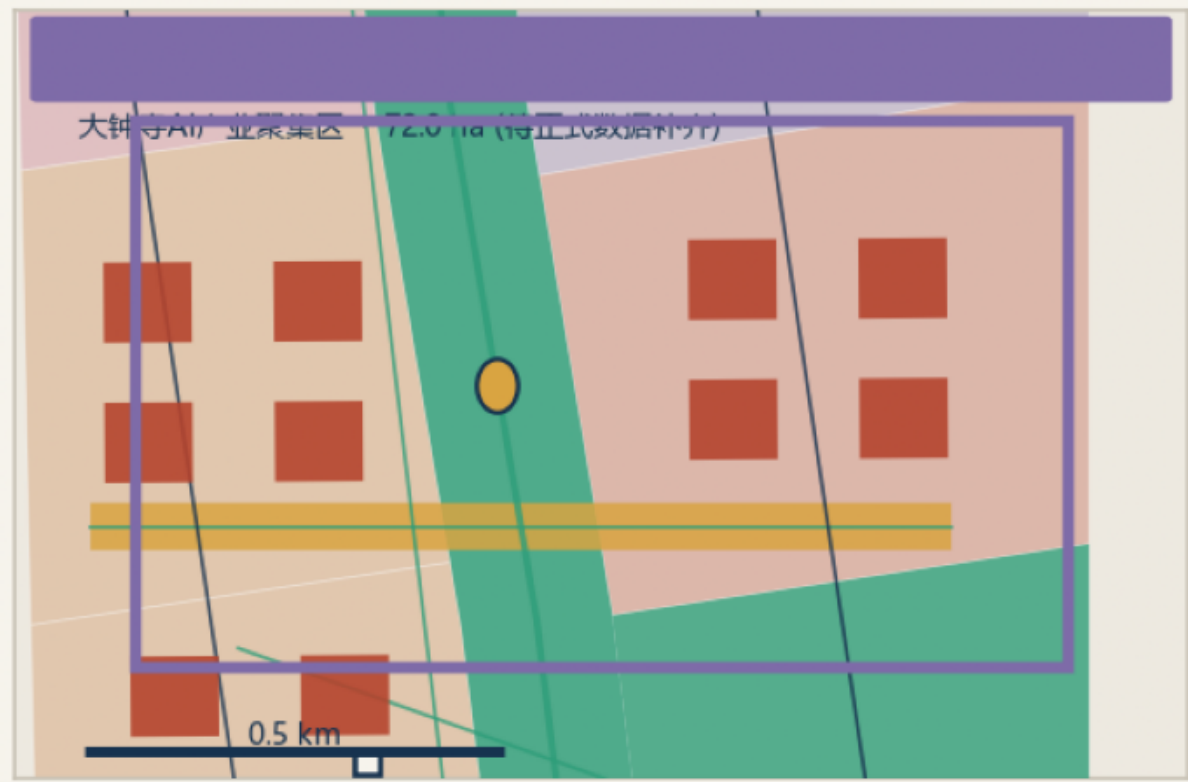

城市型智能原生消费与商务街区	
智能体、智能终端与内容消费核	
算力之钟：古钟文化的算力可视化地标	
大钟寺智站四象限步行连通	
数据要素与数字资产商务界面	
拆改留逻辑（示章）	
■	保留
■	改造
■	新建


数据来源：提交包 geometry/ 图层与 metrics.json（EPSG:4548 复算）；临时粗略边界，概念建议，不构成法定规划或审批依据。



图04 交通慢行与蓝绿公共空间系统

京张向上 JINGZHANG RISING — 南北贯通主绿道 + 东西缝合步行链 + 智站一体化接驳

临时粗略替代边界 provisional · 非法定红线

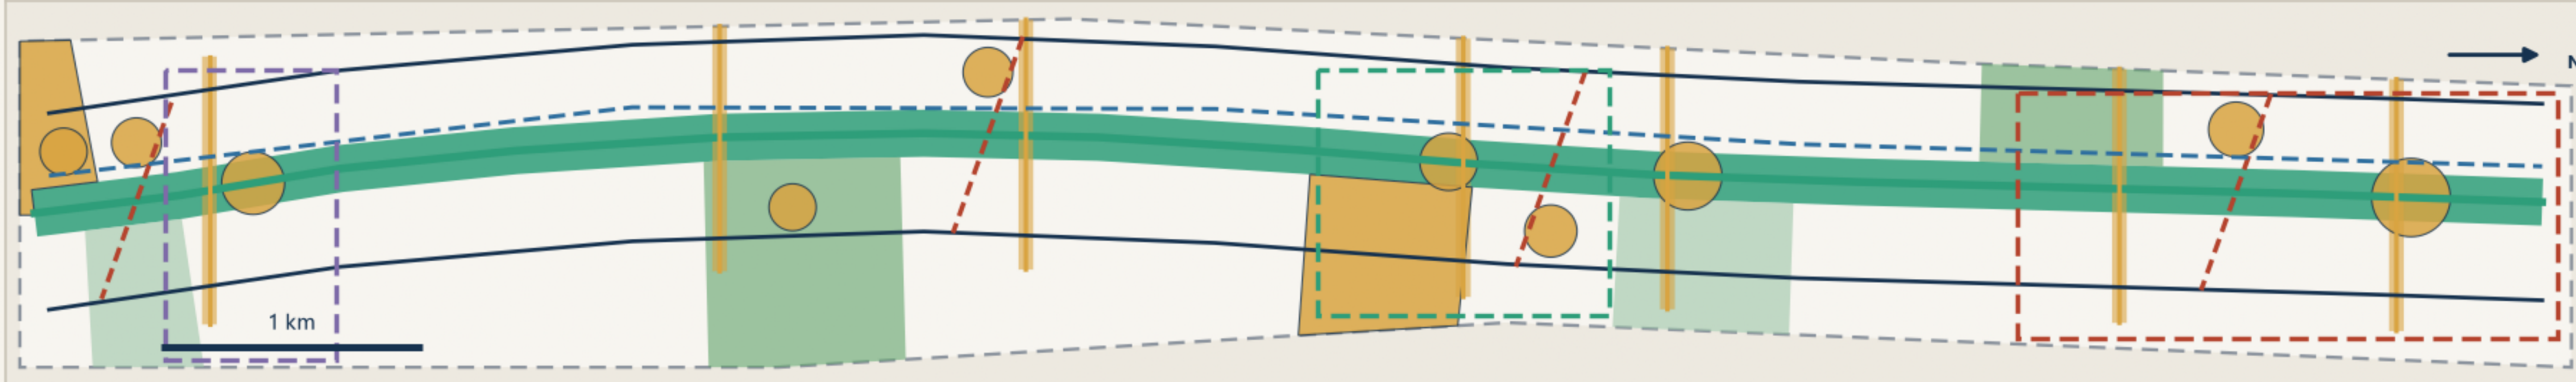

图例	慢行与蓝绿指标	交通与设施策略
主绿道（慢行主轴） 通勤自行车道 次干路 / 微循环 东西缝合绿链 智站接驳线 绿地与开敞空间 公共空间节点	slow_mobility_network_length_m 25.93 km road_centreline_length_m 48.16 km green_space_area_sqm 336.6 ha green_ratio 29.49 % public_space_area_sqm 84.7 ha public_space_ratio 7.42 % east_west_stitch_count 7 ai_public_space_node_count 10	南北贯通 以 9.7 公里连续主绿道贯通遗址公园，取消断点、统一标高与导视 东西缝合 7 条缝合步行链跨越铁路廊道，连接校区、园区与社区 站城一体 4 处智站接驳线组织非机动车换乘、四象限步行与站前公共厅 绿色出行 通勤自行车道与休闲绿道分离，减少人车与快慢冲突 市政与新基建 端侧算力驿站、分布式能源与充电设施结合公共节点布局 无障碍 全线连续无障碍与适老化设计，落实无障碍环境建设法要求

数据来源：提交包 geometry/ 图层与 metrics.json（EPSG:4548 复算）；范围底图为组织方发布的临时粗略替代边界（provisional，虚线），不得作为正式红线、审批依据或精确面积依据。所有空间落地内容均为概念建议，可供专业团队深化研究，不构成法定规划或政府审定结论。

图05 指标复算与证据链

京张向上 JINGZHANG RISING — 核心指标、任务覆盖与自检状态均由结构化文件复算

11.41 km² site_area_sqm	29.5 % green_ratio	7.4 % public_space_ratio	31 land_use_parcel_count	92 building_footprint_count	12 scenario_card_count
---	---	---	--	---	--

指标复算链（几何 → 指标 → 正文）	任务覆盖	自检状态
geometry/site_boundary.geojson → site_area_sqm 1141.3 ha geometry/land_use.geojson → land_use_total_area_sqm 1141.3 ha geometry/green_space.geojson → green_space_area_sqm 336.6 ha geometry/public_space.geojson → public_space_area_sqm 84.7 ha geometry/buildings.geojson → building_footprint_area_sqm 83.2 ha geometry/roads.geojson → road_centreline_length_m 48.16 km geometry/phasing.geojson → phase_one_area_sqm 514.9 ha geometry/key_areas.geojson → key_area_total_area_sqm 369.3 ha geometry/constraints.geojson → constraint_feature_count 4	公告任务 1.3 / 1.4 / 1.5 17 项全部覆盖 智能体任务书 agent.1-agent.6 6 项全部覆盖 强制专业标准 6 项全部响应 正式设计深度项 15 项全部 complete AI 场景卡 12 张（要求 ≥10） 产业测试验证场景 4 个（要求 ≥3） 用户画像 6 类（要求 ≥5） AI朝圣地标与荣誉节点 4 处（要求 ≥3） 全球AI生态案例 8 个（要求 5-8）	确定性校验 Deterministic PASS 空间审查 Spatial PASS 视觉打包 Visual packaging PASS 专业证据 Professional evidence PASS 待正式数据补齐 floor_area_ratio 待正式数据补齐 building_height_control_m 待正式数据补齐 total_floor_area_sqm 待正式数据补齐 正式边界与控规条件发布后，必须重新运行几何生成、指标复算、附件渲染与四门自检，再提交修订版本。

数据来源：提交包 geometry/ 图层与 metrics.json（EPSG:4548 复算）；范围底图为组织方发布的临时粗略替代边界（provisional，虚线），不得作为正式红线、审批依据或精确面积依据。所有空间落地内容均为概念建议，可供专业团队深化研究，不构成法定规划或政府审定结论。