


自主智能带 · Autonomous Intelligence Belt (AIB)

资料证据链与提交包关系图 / Evidence chain & submission package

1909 自主建造 → 2026 自主智能

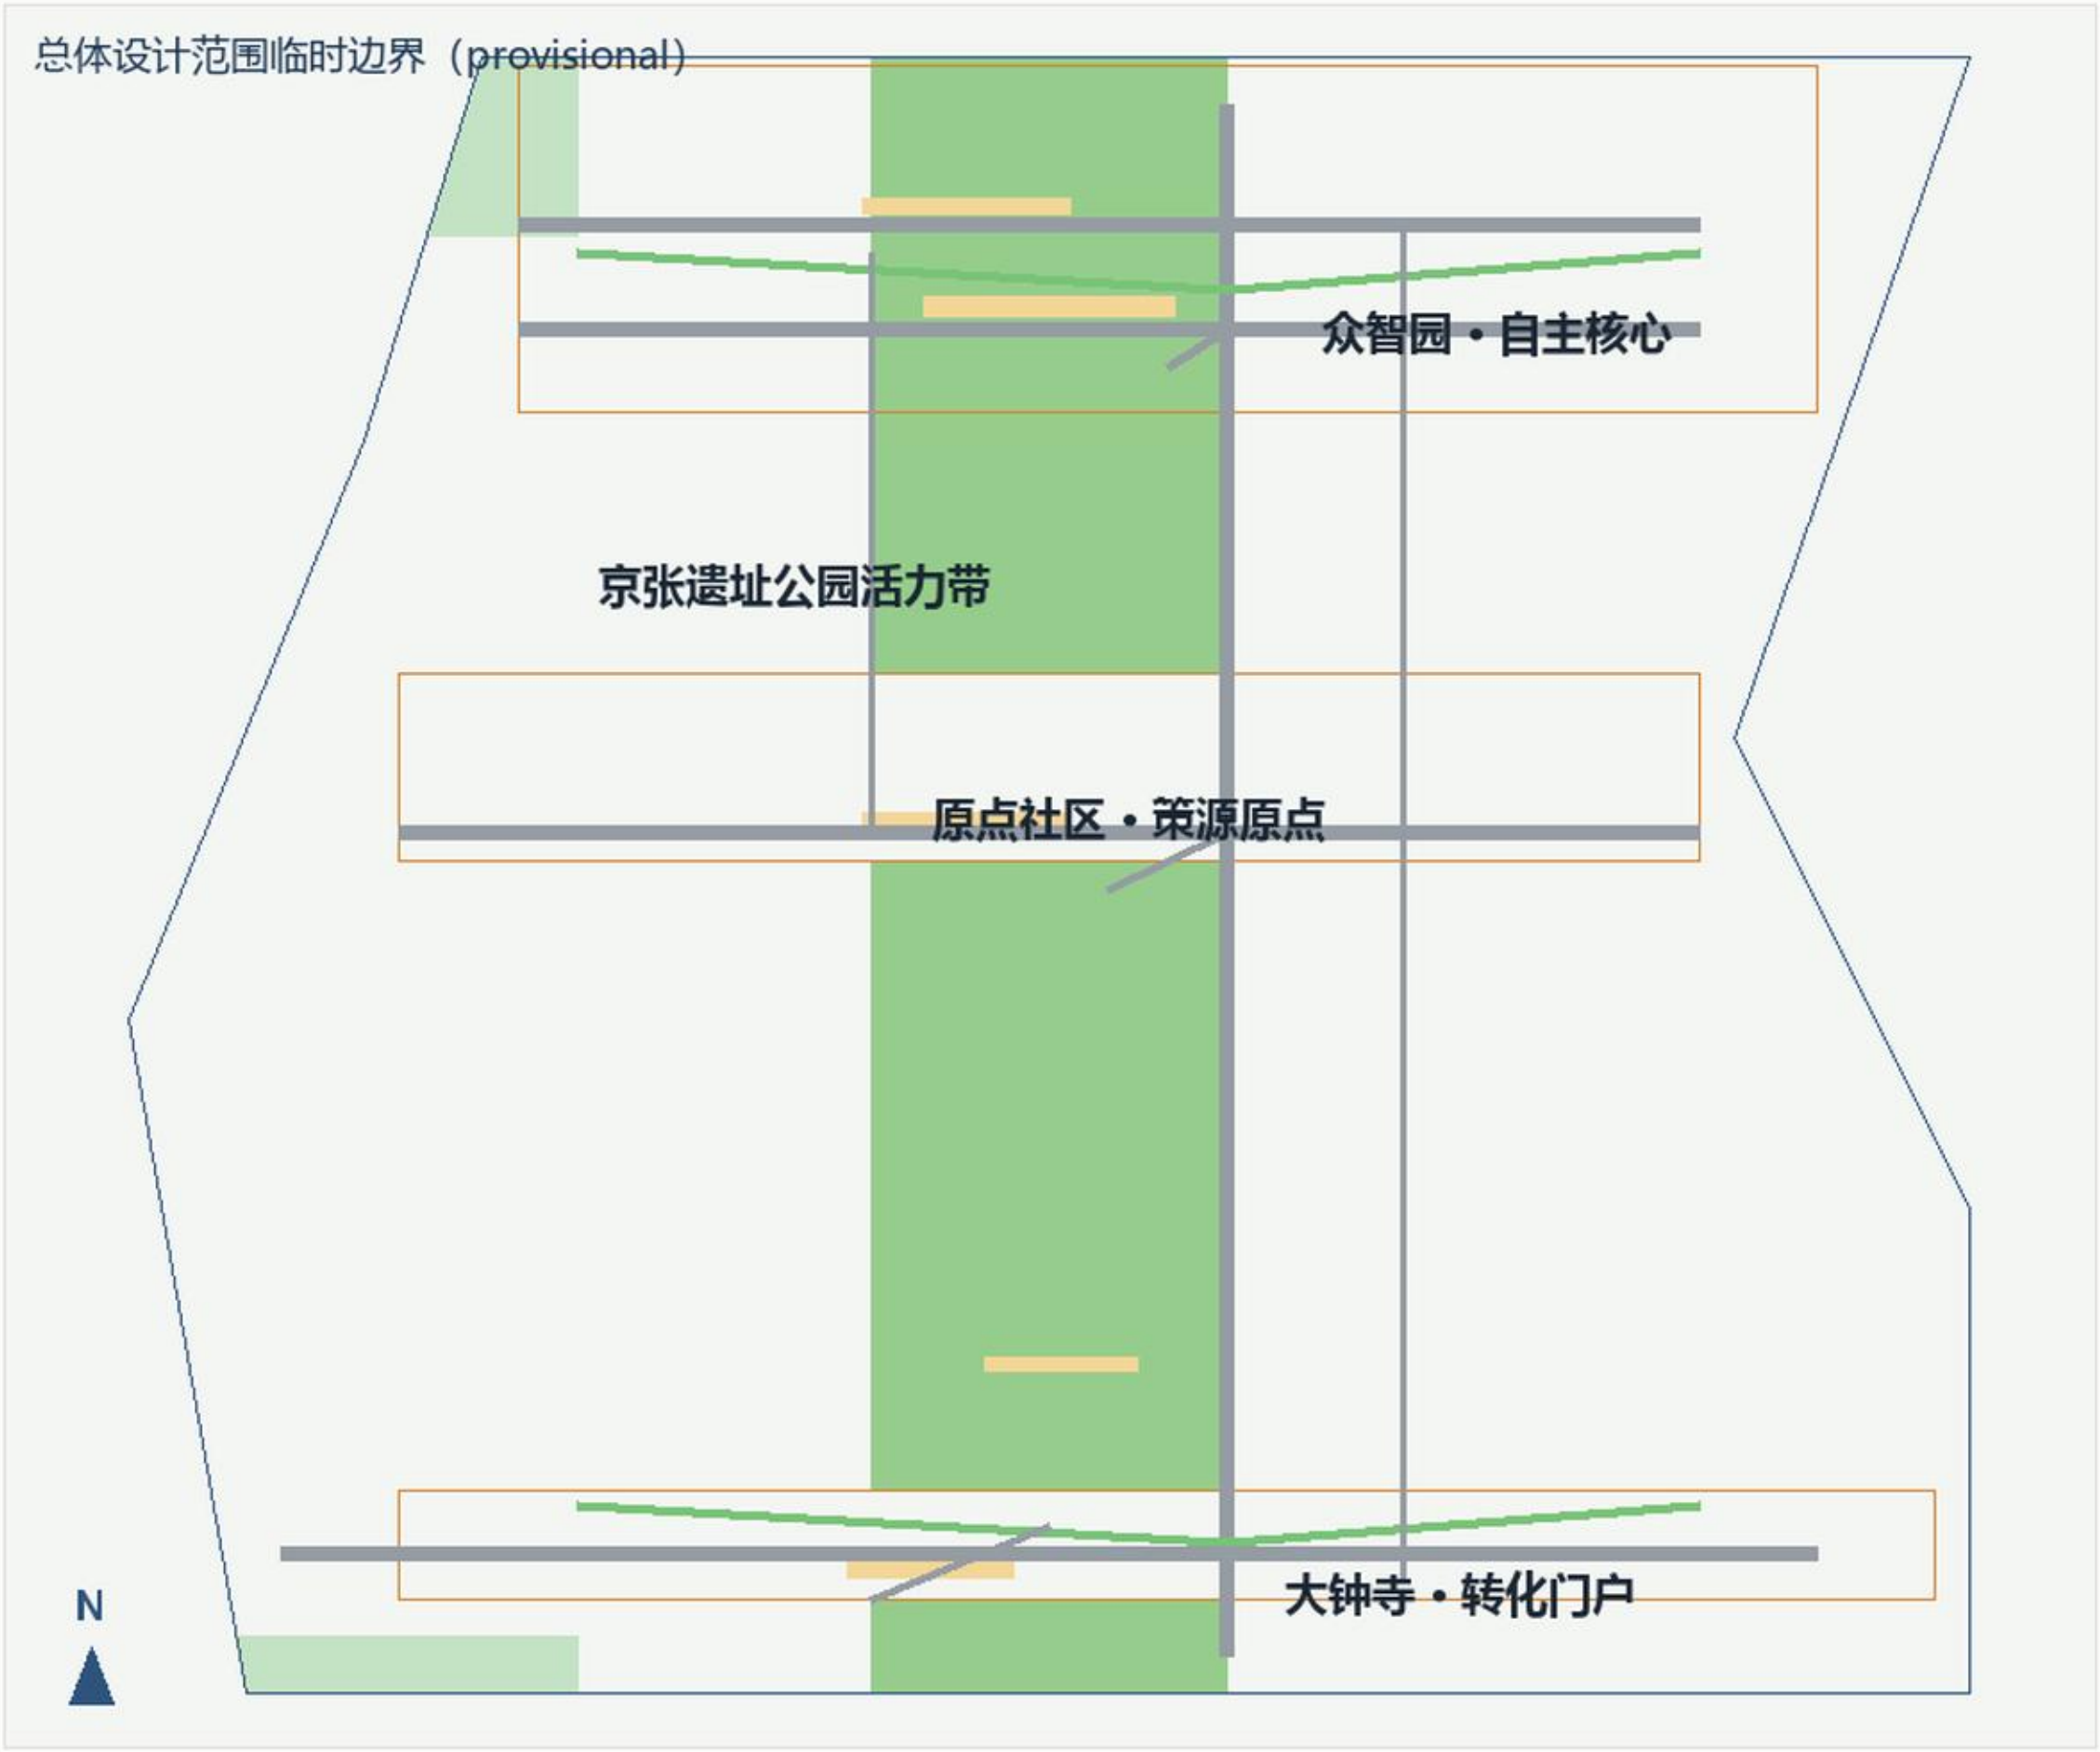

1 来源 Sources

官方公告 / 任务书 / 场地包 / 来源登记

2 几何 Geometry

9 个 GeoJSON 图层 (EPSG:4326)

3 指标 Metrics

EPSG:4548 复算 → metrics.json

4 矩阵 Matrices

合规/标准/深度/来源 4 矩阵

5 提案 Proposal

双语 proposal.md + proposal.en.md

Provisional boundary · concept design · EPSG:4548 recalculation

五大功能 · 三区两翼

- AI全栈自主创新体系：众智园·自主核心（算力/数据/模型/标准）
- 世界级AI创新生态：原点社区·策源原点（人才/开源/创业）
- AI+场景赋能新范式：小月河场景赋能翼（场景开放）
- 智能化AI活力城市：大钟寺·转化门户（智能原生新业态）
- AI治理全球话语权：中关村科技服务翼（资本/IP/要素配置）

文化叙事

- 第一幕 1909 自主建造：詹天佑、人字形展线
- 第二幕 中关村自主创新：从电子信息到互联网
- 第三幕 2026 自主智能：AI 全栈回路贯穿一带
- 「人字形」为母题的识别系统：一级一带总识 / 二级三核色带 / 三级场景节点

图1 资料证据链与提交包关系

三层范围


- 统筹研究 43.6 km² · 总体设计 11.4 km² · 重点区 368.4 ha
- 核心→策源→转化→反馈 的自主回路逐级落实

命名与Logo

- AIB / 自智带；A = Autonomy + AI
- 人字形铁轨 + 电路回路 → 字母 A；京张钢蓝 + 智能青绿

三层范围与空间工作框架

一带三核两翼 · 京张遗址公园活力带为脊柱 / Land-use structure (design proposal)

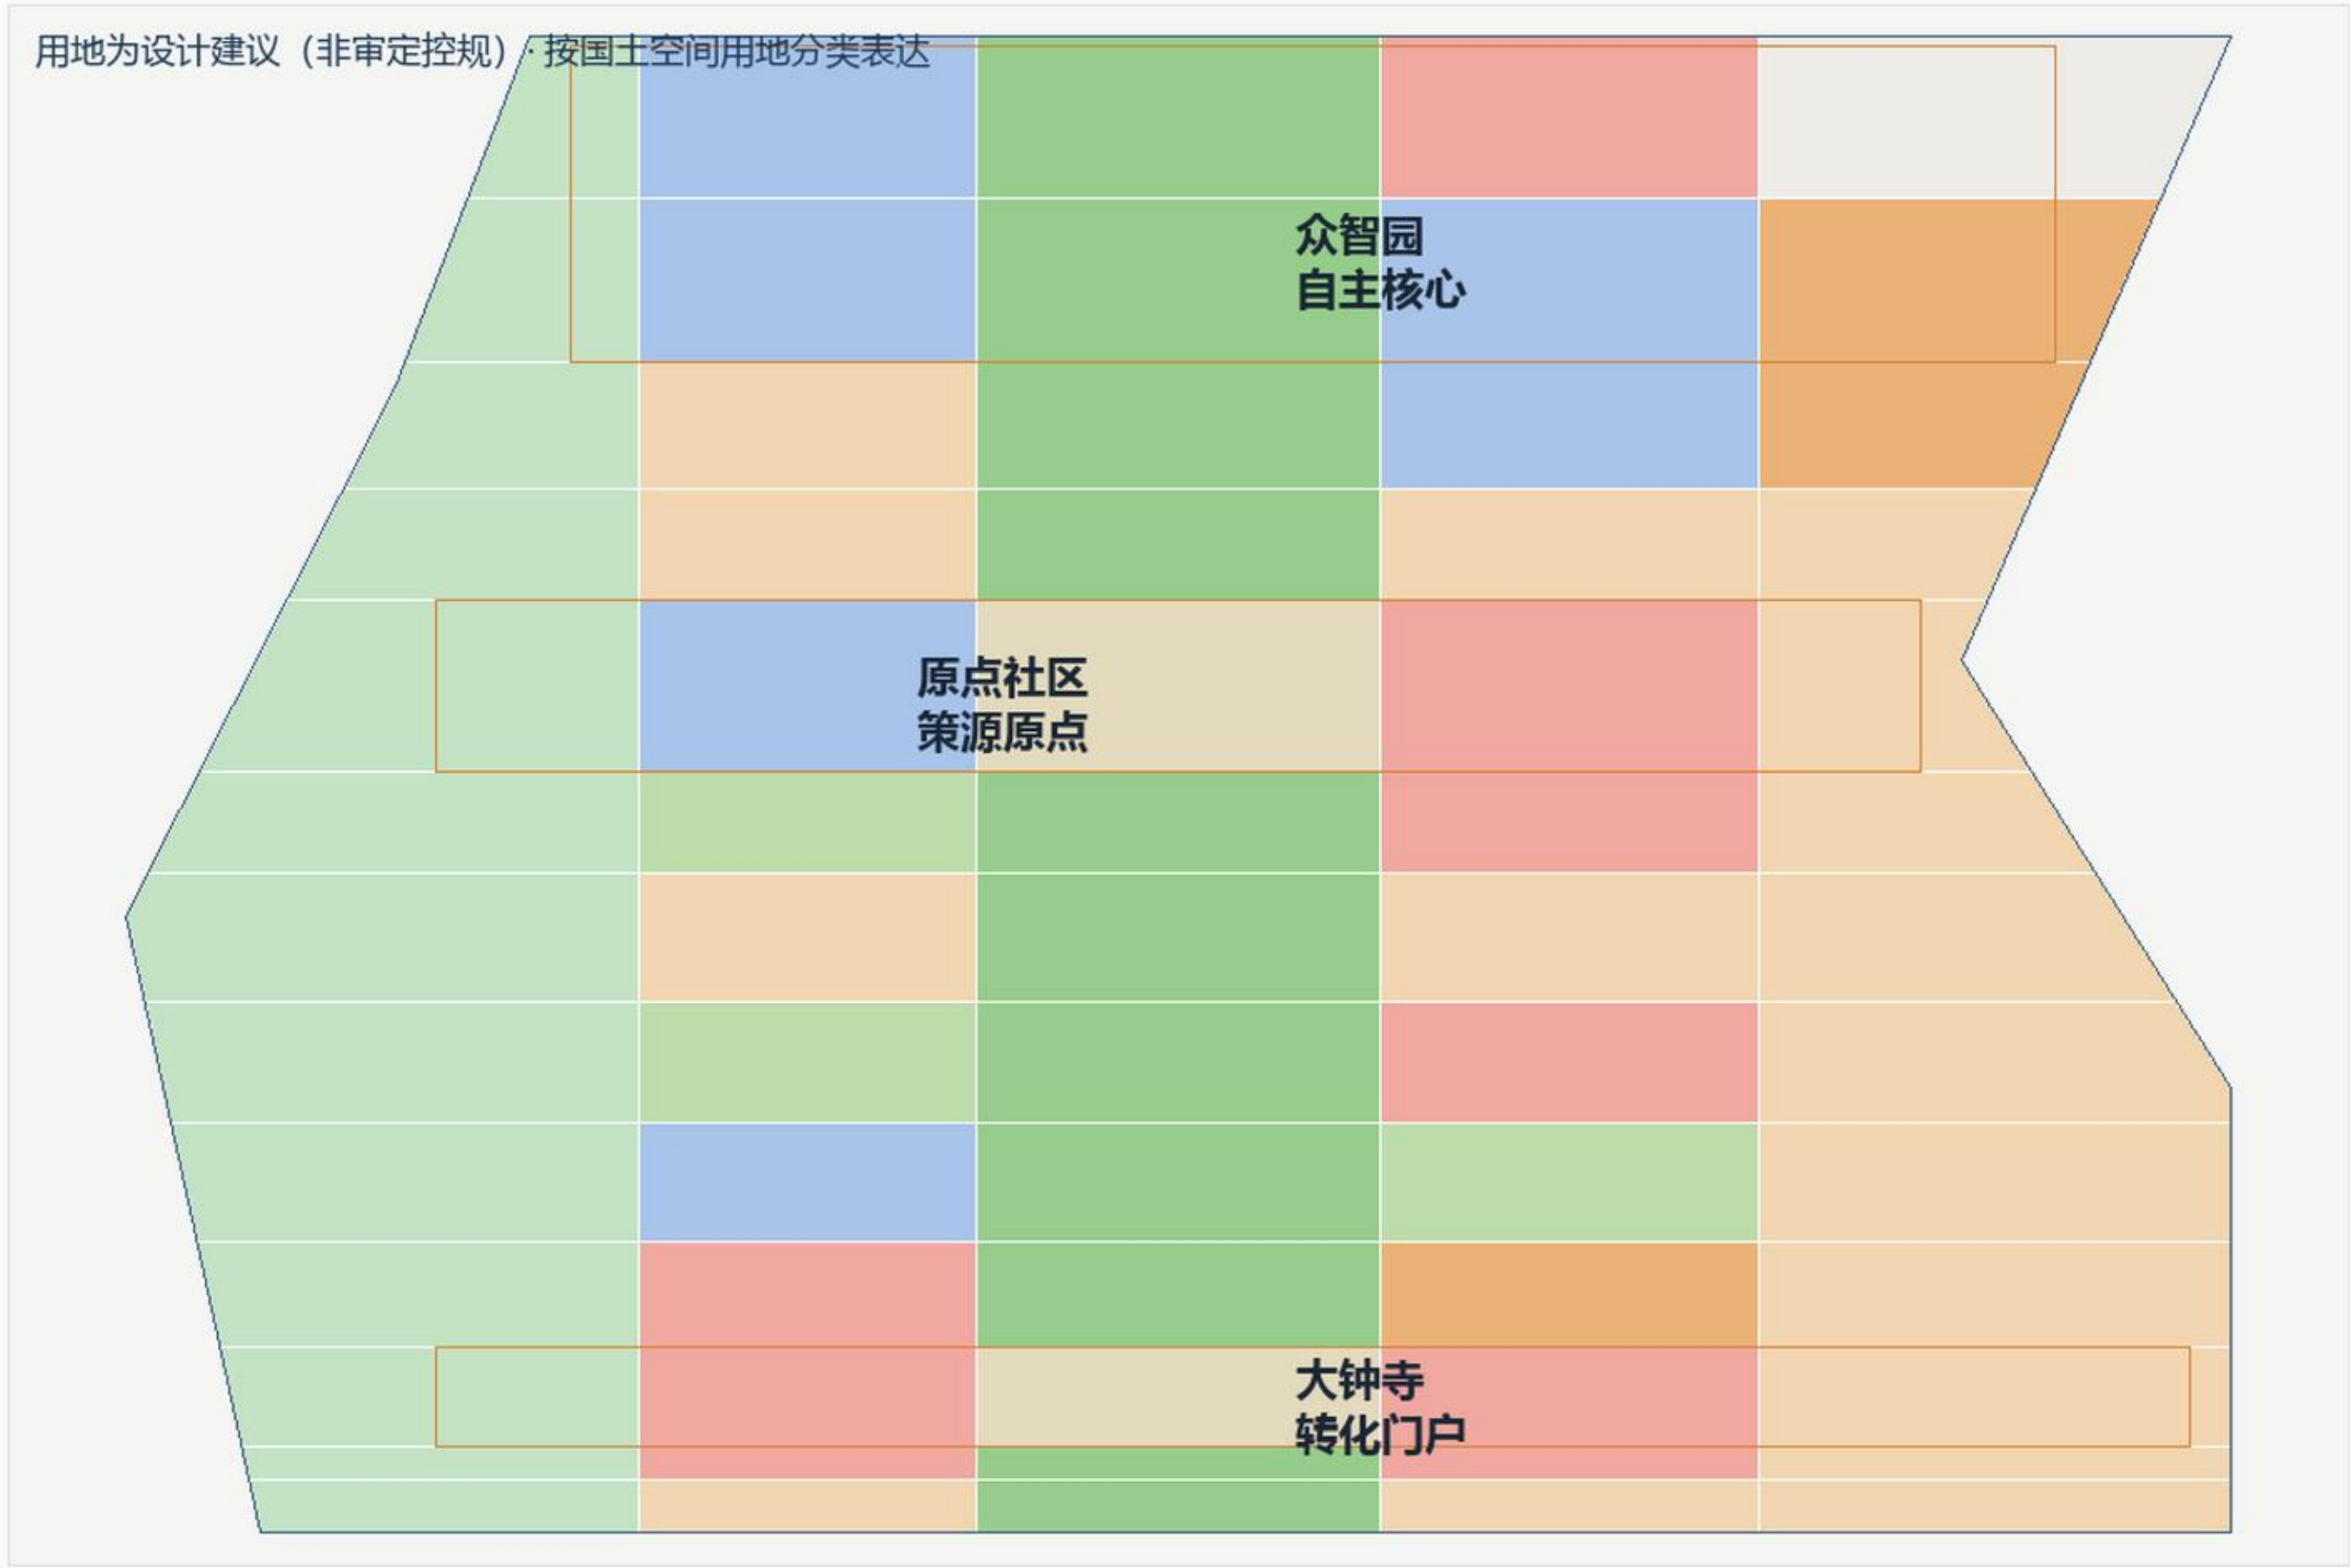

三层范围 → 三级落实

同一套「自主回路」逐级递进

统筹研究范围 · 43.6 km²

AI 产业生态、未来城市形态、区域协同
自主核心—策源原点—转化门户—两翼赋能

总体设计范围 · 11.4 km²

城市更新、用地、交通市政、风貌
控规深度的城市设计

重点区域范围 · 368.4 ha

三处片区规划综合实施方案深度
众智园 / 原点社区 / 大钟寺

用地图例（国土空间分类代码）

0701 城镇住宅	0702 社区服务
0802 科研	0803 文化
0804 教育	05 商业服务业
1401 公园绿地	1402 防护绿地
1403 广场	16 留白

注：用地/比例可由 GeoJSON 在 EPSG:4548 复算

Land-use parcels are design proposals; official regulatory plan pending

图2 三层范围与用地结构

总体策略

· 城市更新「先盘点、再开放、后建造」三阶段；拆改留以设计载体与待复核对象表达


· 用地结构：脊柱两侧科研/教育/商业/居住，三核周边广场与服务设施，绿地承担雨洪+慢行+创新交往

· 交通骨架：京张大道脊柱廊道+人字形双环绿道；轨道站点一体化；4处慢行断点优先缝合

· 开发强度：容积率/高度/密度/退线在无官方控规下统一标注 unknown 并给出补数路径

交通慢行与蓝绿公共空间复合系统

人字形双环+脊柱绿道·轨道站点一体化·慢行断点缝合

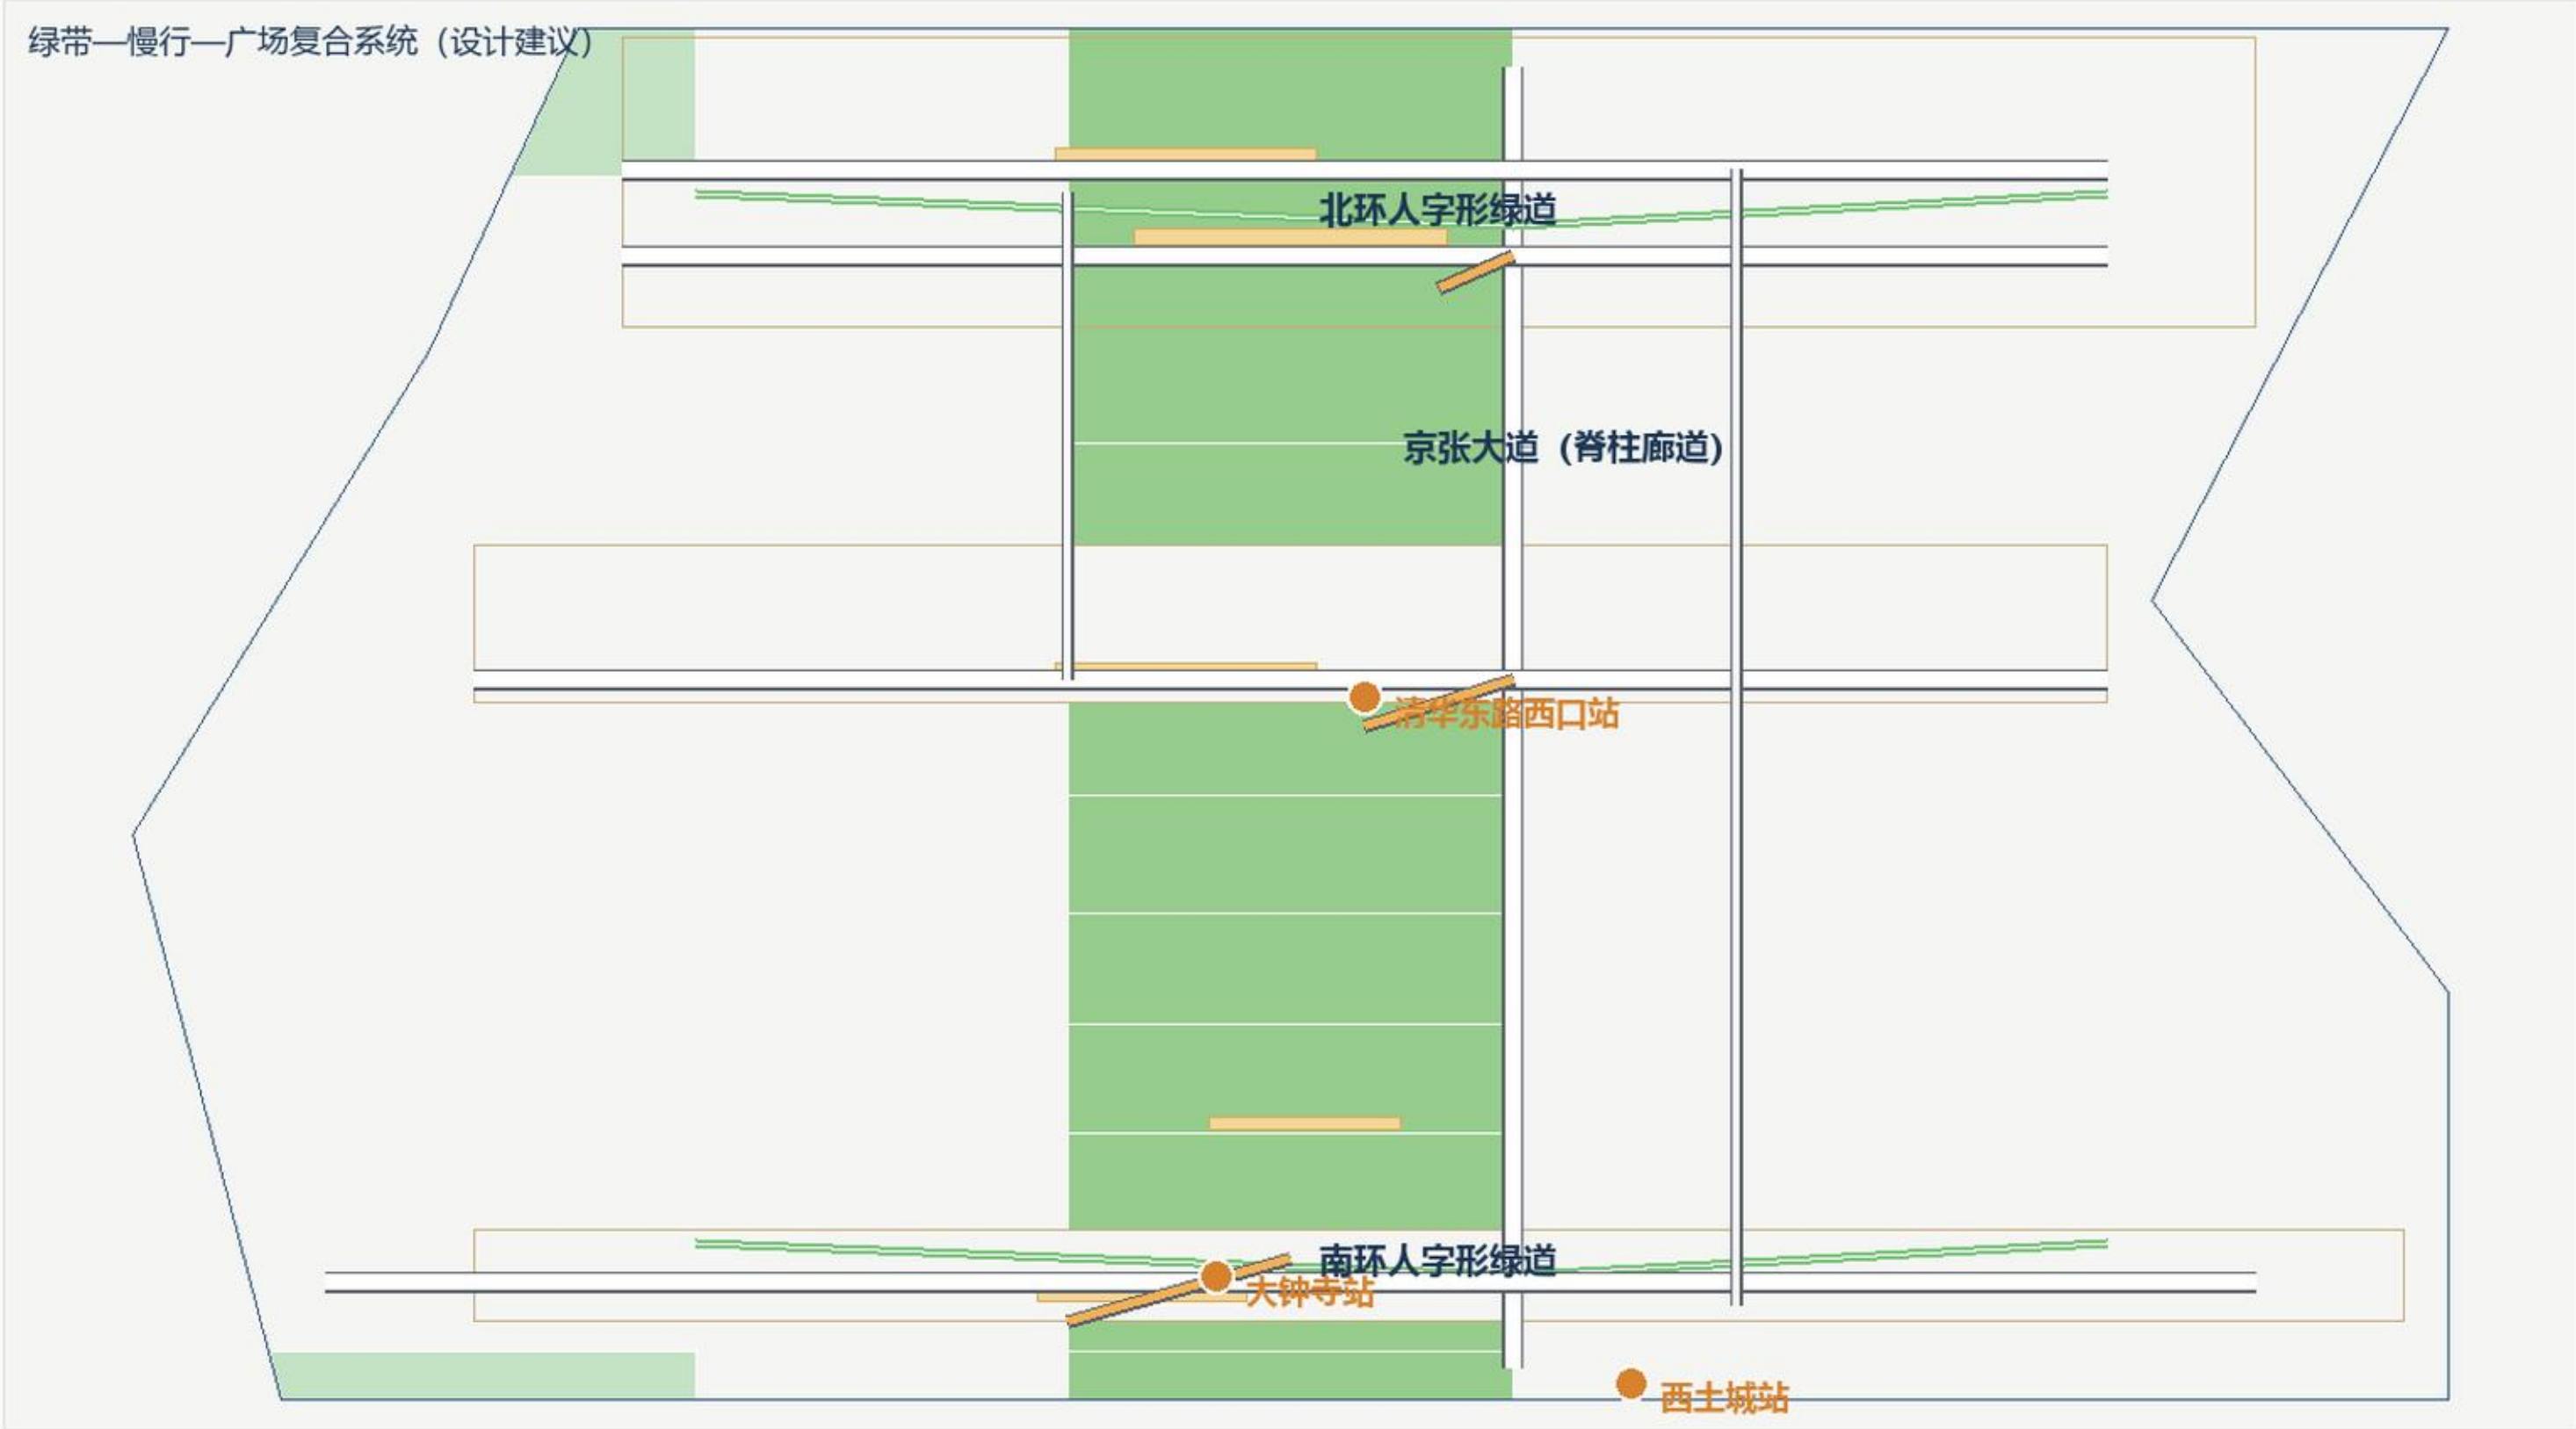

Road redlines and transit interfaces pending official engineering review

图4 交通—蓝绿—公共空间复合系统

复合系统要点

- 人字形双环：北环缝合众智园—清河—五环
- 南环缝合大钟寺—西土城—西直门
- 脊柱绿道 = 雨洪 + 慢行 + 创新交往
- 慢行断点（4处）为优先缝合工程
- 非机动车停放服务轨道接驳与共享出行
- 公共空间「先日常、后活动」时间规则

图例

- 次干廊道（京张大道）
- 人字形绿道
- 支路 / 地块出入
- 轨道站点接驳
- 公园绿地
- 广场节点

重点区域 · AI 场景与朝圣地标

三处片区详细设计 · 13 张场景卡 · 4 处概念地标

三处重点区域 · 详细设计

对应自主回路的三级能力，均达规划综合实施方案城市设计深度

众智园 · 自主核心

Autonomy Core · 约 192.1 公顷

全栈自主创新与测试验证「核心级」园区

一心两轴三组团 · 研发/测试/绿色交往

自主大模型开放评测场 · 端侧AI与具身智能测试街 · 安全治理沙盒

风险：算力、土地、市政条件待确认

原点社区 · 策源原点

Origin · 约 104.3 公顷

近校策源、人才与开源生态「原点级」社区

原点广场 + 成果转化街 + 人才服务带

开源协作发布厅 · 成果转化驿站 · 人才特区会客厅

风险：校区边界、权属、首层业态待确认

大钟寺 · 转化门户

Confluence · 约 72.0 公顷

智能原生新业态、内容消费与国际交往「门户级」城区

站前广场四象限步行连通 · 站城一体

数据要素合规验证沙盒 · 国际路演客厅 · 智能体新业态展示街

风险：站点改造、市政时序依赖正式条件

自主回路 · Autonomy Loop



Key-area polygons are provisional; conclusions are directional

图3 三处重点区域与自主回路

朝圣地标（概念地标，未获批准建设）

· LB-01 自主原点碑（清华园火车站遗址）· LB-02 人字形智能回环广场（众智园）

· LB-03 自主智能之光（大钟寺站南）· LB-04 开发者贡献之墙（原点社区）

· AI 场景：13 卡（4 产业测试）· 6 画像 · 更新项目 6 项 · 分期 3 段

· 实施风险均待正式条件；六项门禁通过后提交

核心指标复算与证据链

每个 known 指标均可由提交几何在 EPSG:4548 复算 / Metric recomputation & evidence

指标 metric	含义	复算值	说明	来源文件	置信度
site_area_sqm	总体设计范围面积	11,412,825.4 m²	≈ 11.41 km²	site_boundary.geojson	high
green_space_area_sqm	绿色空间面积	2,212,765.7 m²		green_space.geojson	medium
green_ratio	绿地比例	19.39 %		green_space / site	medium
public_space_area_sqm	公共空间面积	69,608.0 m²	广场节点口径	public_space.geojson	medium
public_space_ratio	公共空间比例	0.61 %	线性空间未另计	public_space / site	medium
building_footprint_area_sqm	建筑基底面积	101,324.4 m²	设计载体口径	buildings.geojson	medium
key_area_area_total_sqm	重点区面积合计	3,692,893.0 m²	与公告 368.4ha 差 <3%	key_areas.geojson	medium

待确认管控指标（unknown）

容积率 / 建筑高度 / 建筑密度 / 退线 / 道路红线 / 总建筑面积 —— 缺官方控规，统一标注 unknown 并给出补数路径

复算链路

GeoJSON (EPSG:4326)

↓

shapely.transform → CGCS20

↓

polygon_area / union_area

↓

metrics.json 指标

↓

正文 + HTML 联动

六项门禁

模型再验证 / 数据再验证 / 指标再验证

All areas recomputed from submitted geometry in EPSG:4548

图5 核心指标复算与证据链