


造物绿脊：把 AI 设备全生命周期写进城市

临时范围 + OSM 现状背景 + 同源设计网络；不替代法定红线

空间总图 / SPATIAL SYNTHESIS

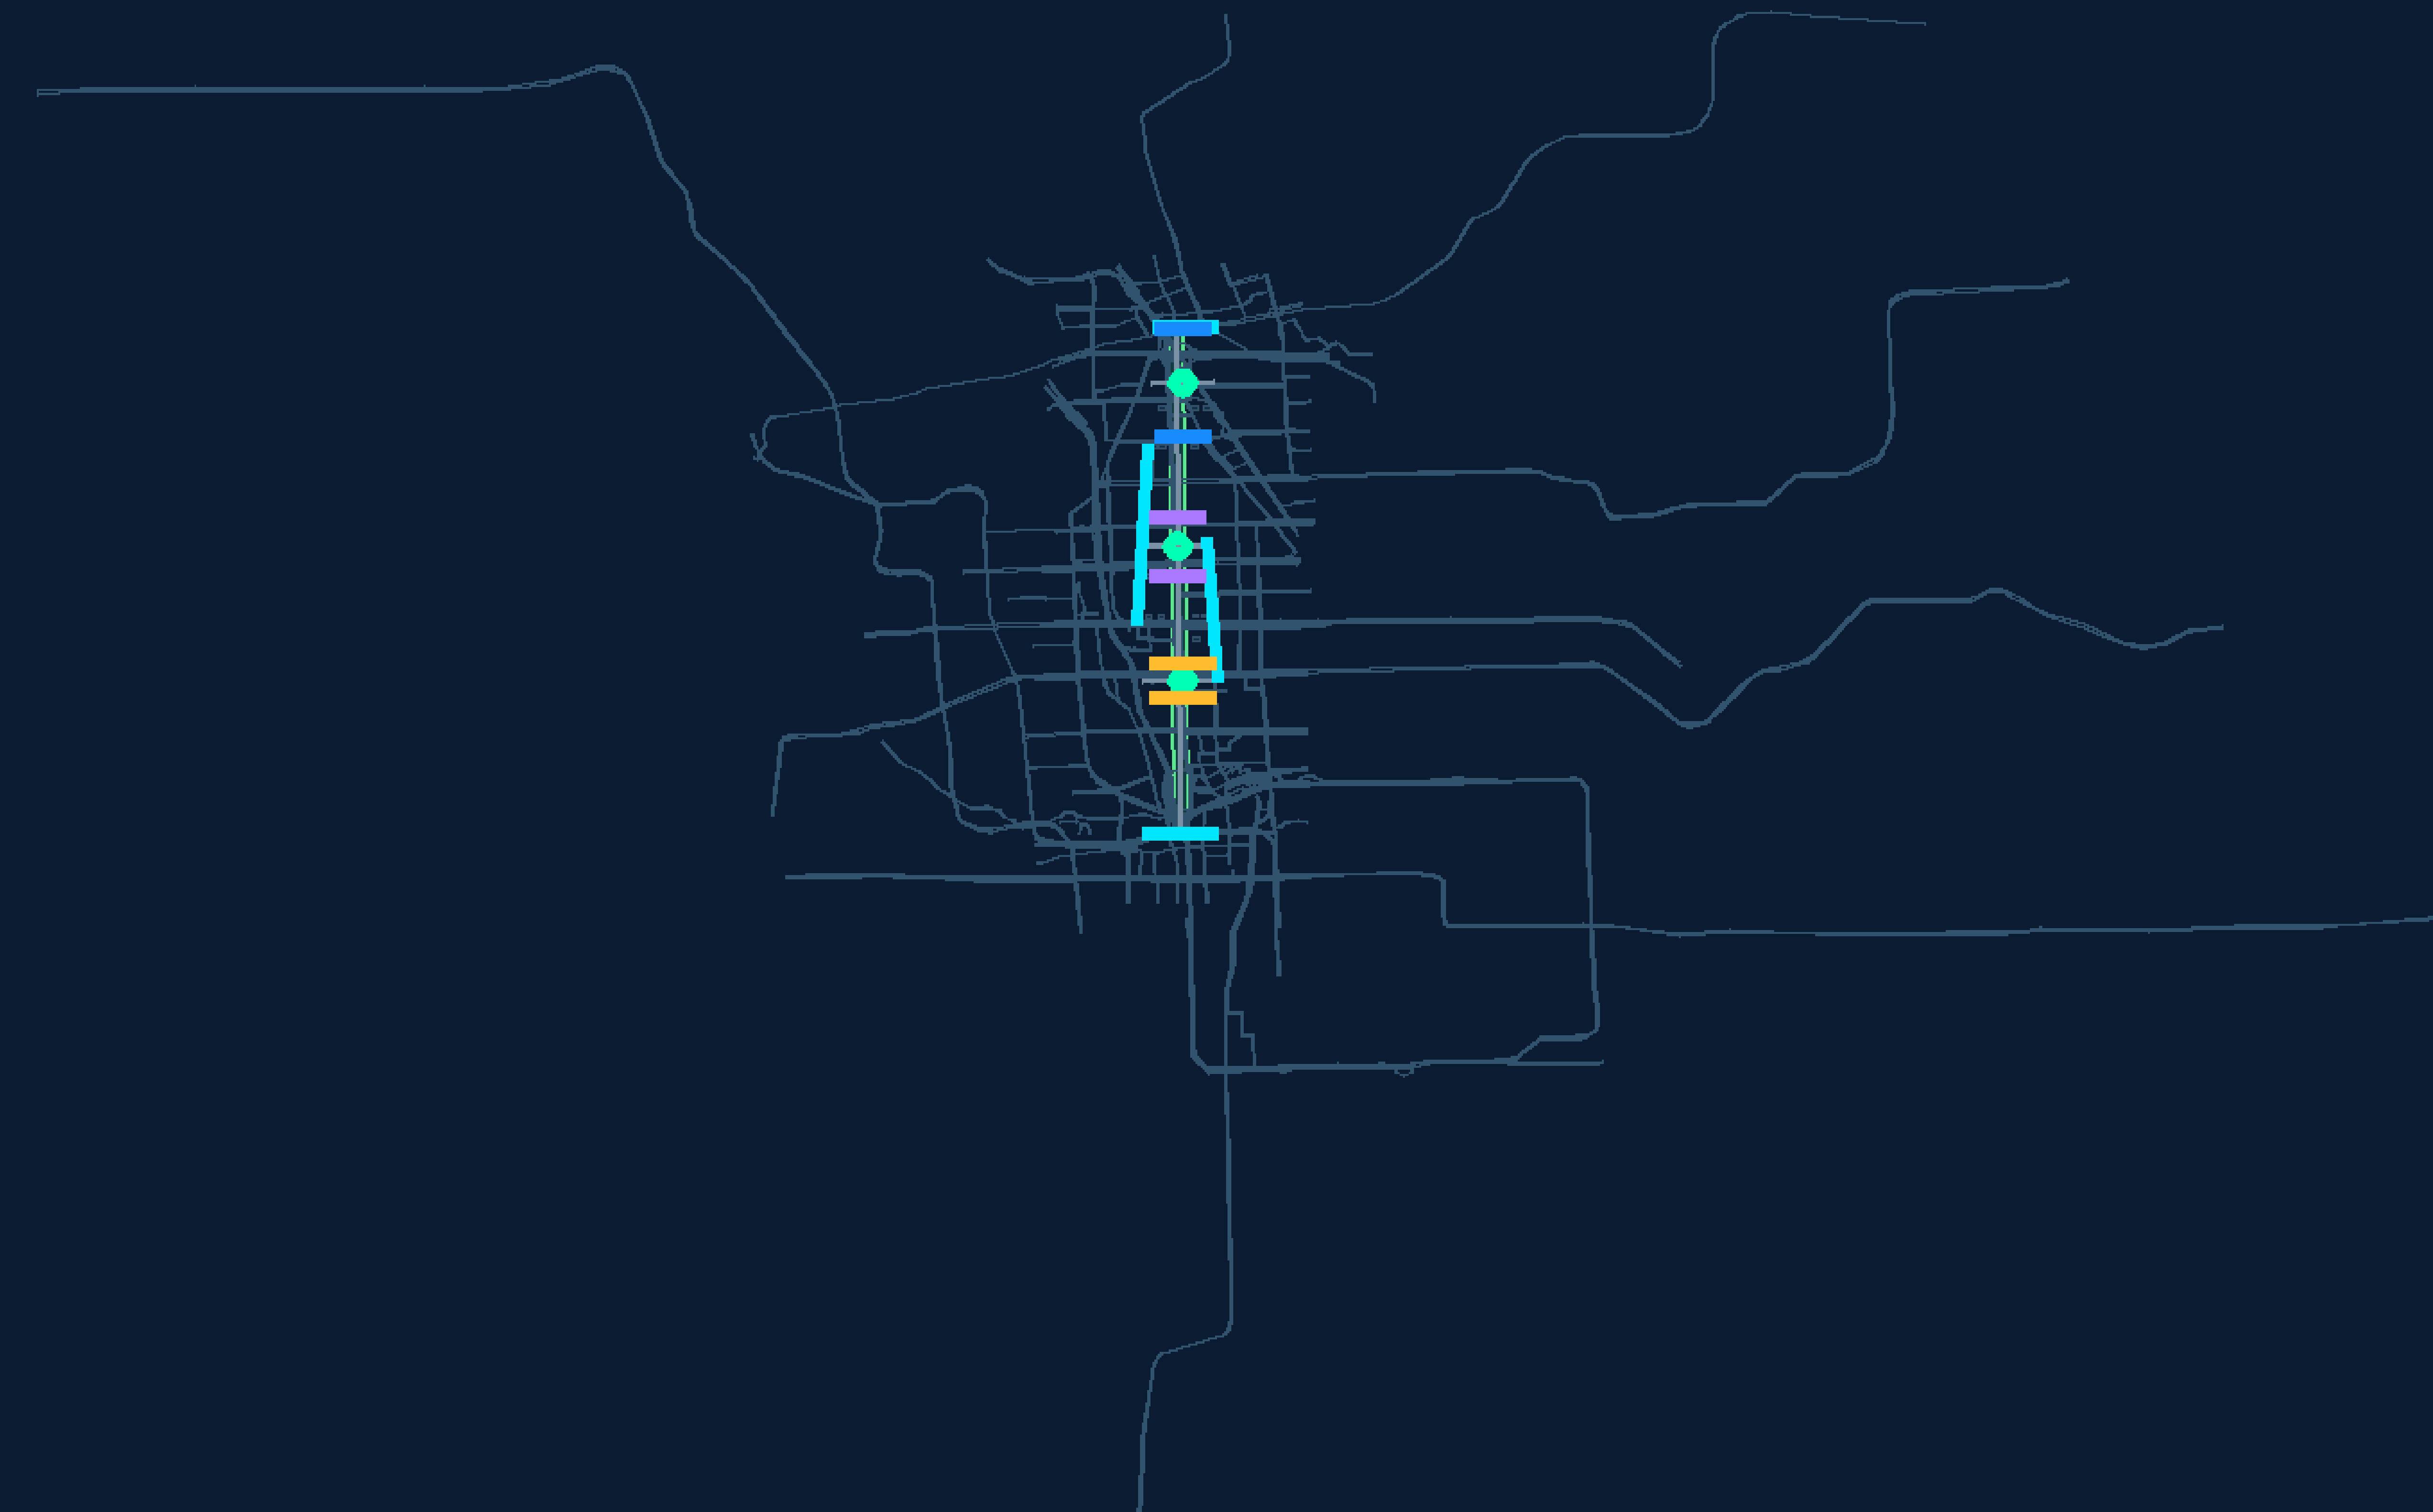

- 临时总体范围
- 公共造物绿脊
- 三处重点区域

一脊·三院·两翼

一条公共绿脊连接学习、试制、展示、维修与回收；三座造物院提供差异化平台；东西两翼把高校、园区、社区和市场接入同一服务协议。

三层范围 / 3 SCALES

11.43 km²

总体设计范围

重点设计区域

12

AI+ 场景卡


证据边界 / EVIDENCE

OSM 仅作道路、轨道、水系、公园、站点与高校的现状背景。总体边界和三处重点区域仍为临时约束，待官方图形发布后重算。

共享边界的用地拼图

概念性功能分区，完整覆盖且无缝无重叠；不替代法定用地

六类城市生产功能

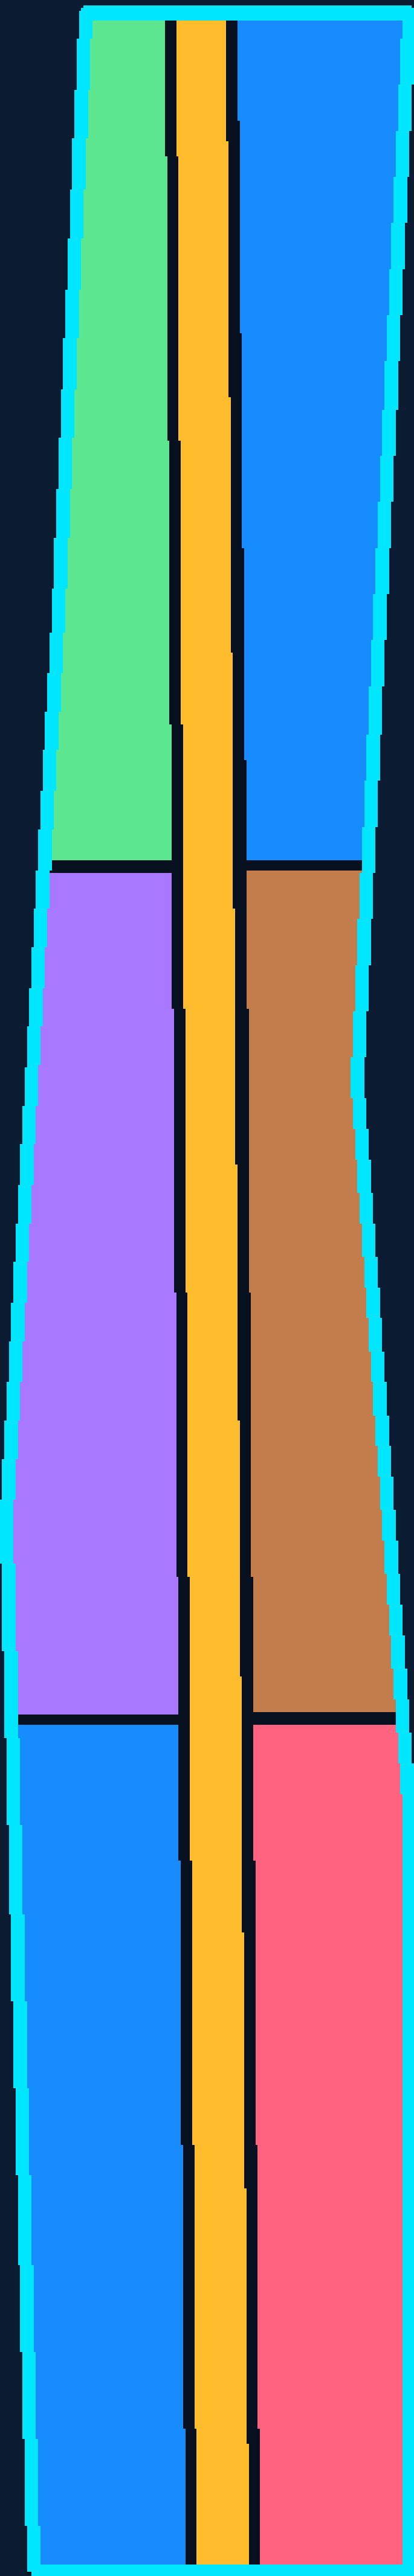

功能面积 / PROGRAMME

铁路文化展示与再制造	178.1 ha
造物绿脊与开放公园	200.3 ha
维修市场与产业服务	169.8 ha
开放教育与技能认证	171.4 ha
混合居住与生活服务	142.0 ha
AI研发与受控测试	116.7 ha


设计逻辑 / DESIGN LOGIC

- 01 共享边界**
相邻地块复用同一坐标链
- 02 绿脊优先**
公共空间先行，再嵌入生产单元
- 03 可逆更新**
以修缮、适配和轻量增量为主
- 04 动态复算**
官方边界到位后自动重算指标

三座造物院：测试、共造、维修

面积拟合临时范围叠加 OSM 背景；待官方 polygon 发布后重算

众智园 · 受控试造

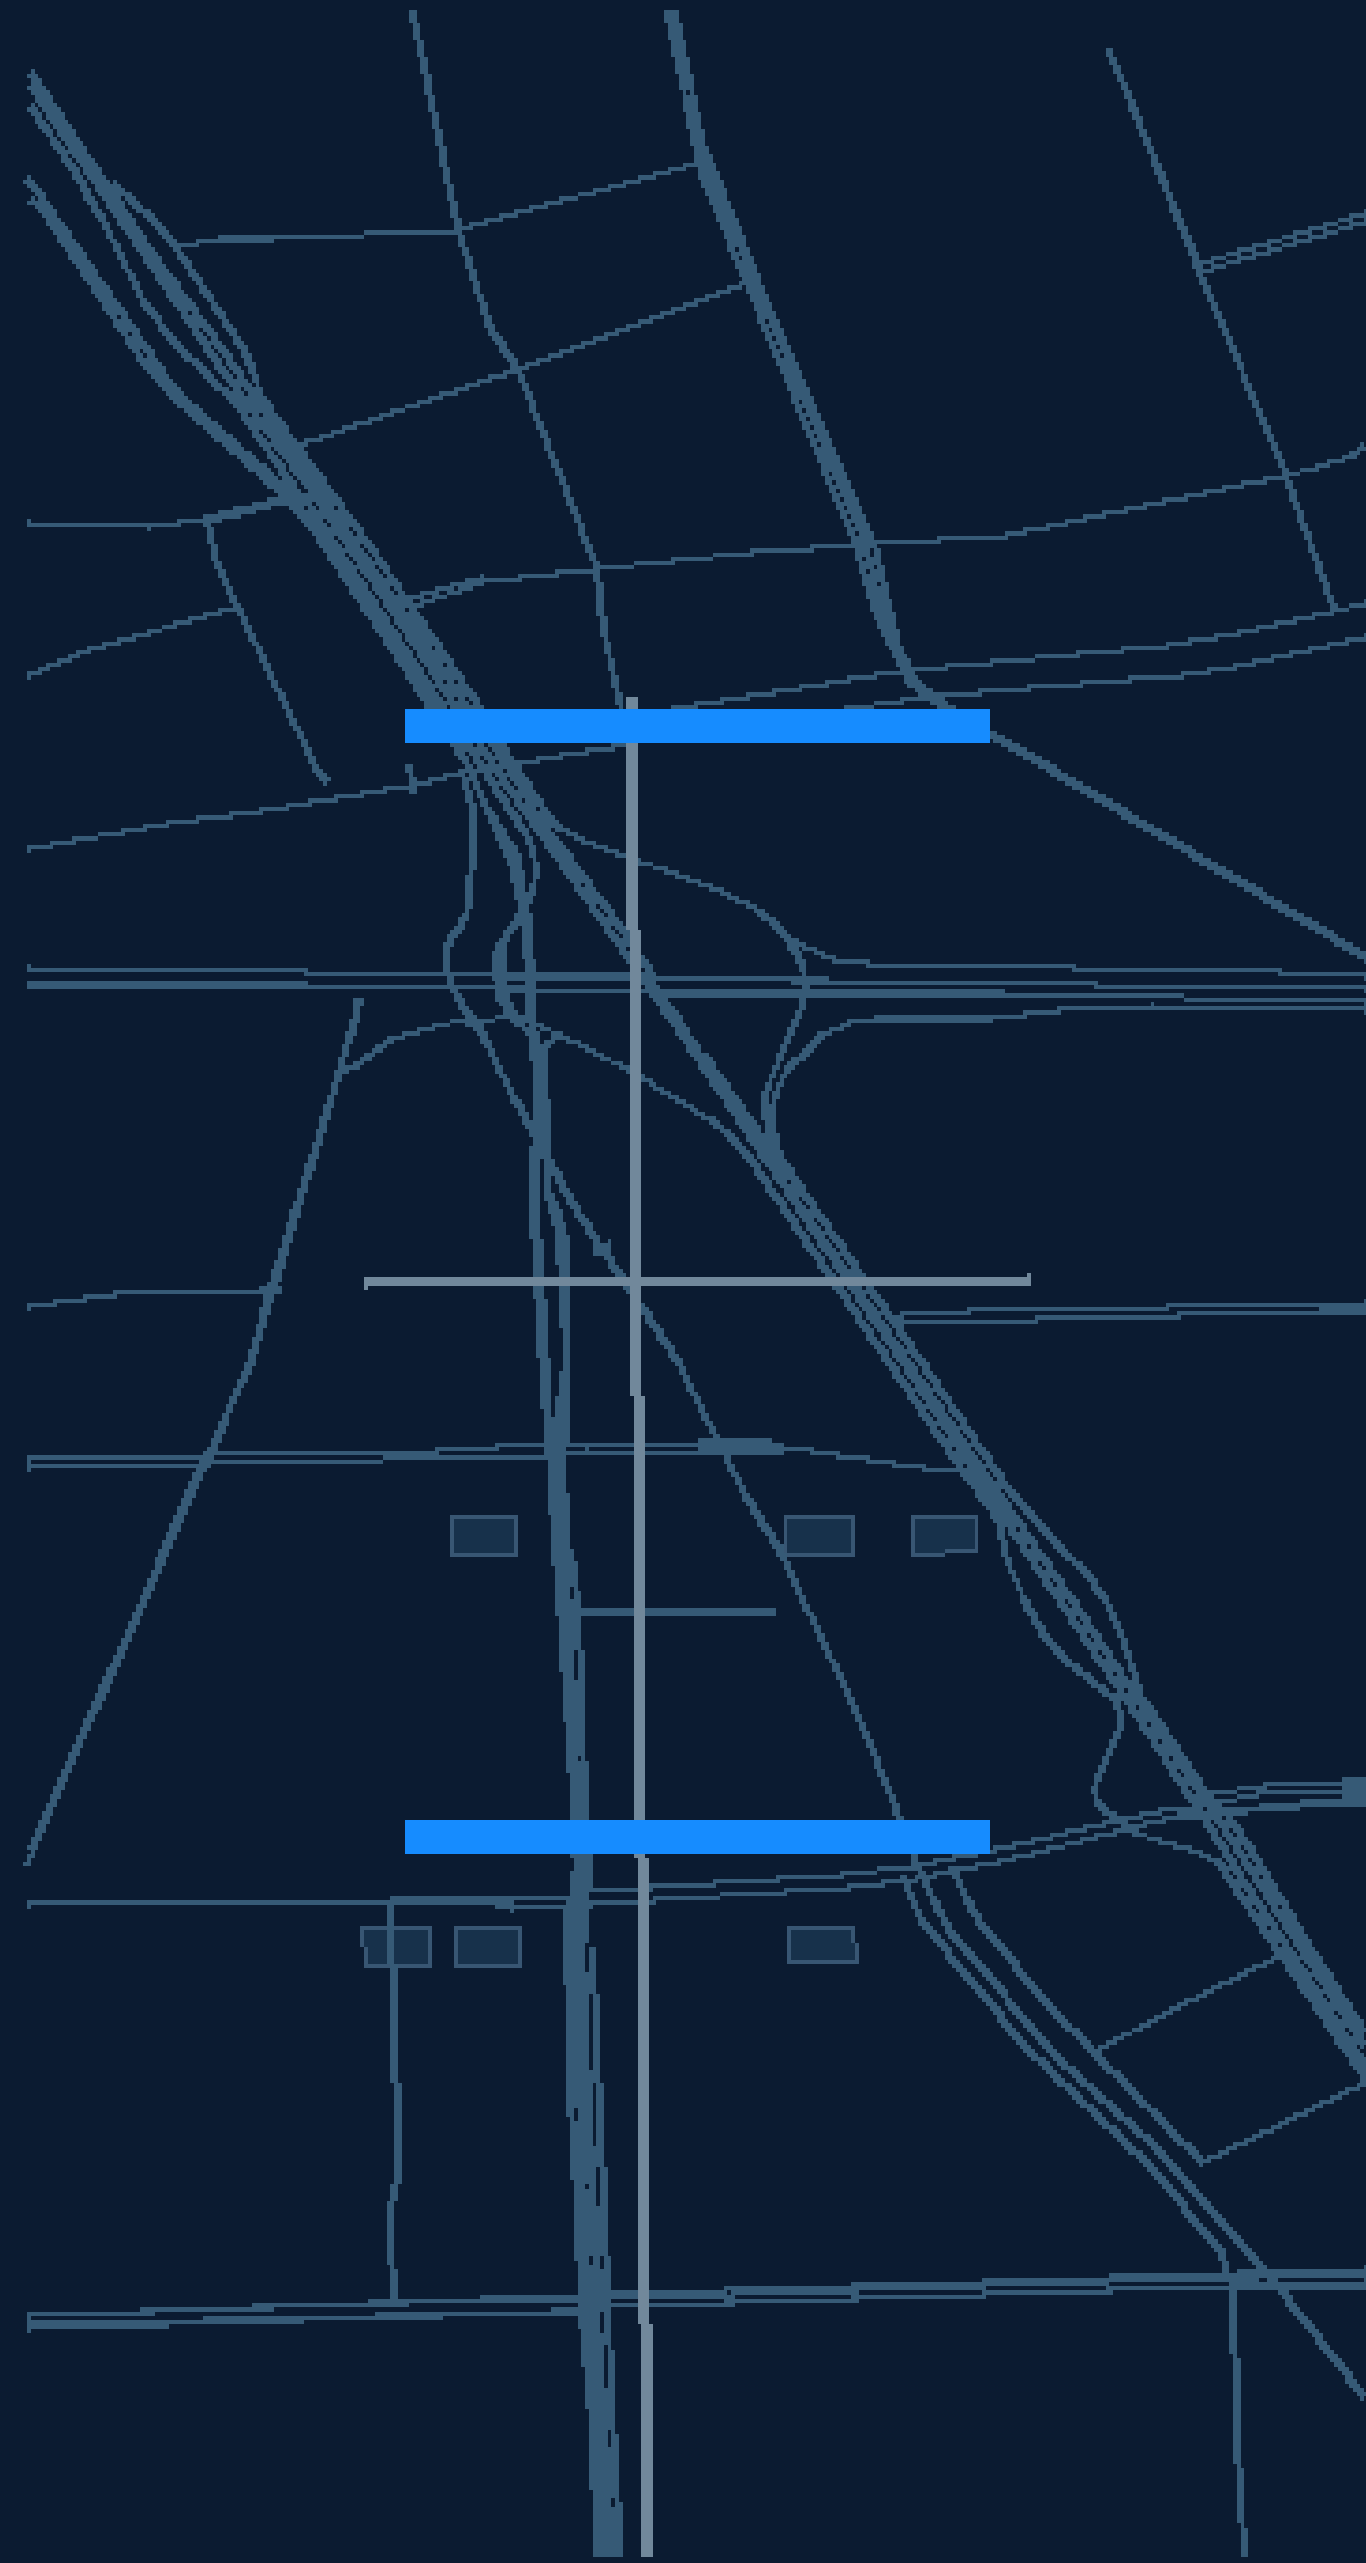

192.1 ha

PROVISIONAL CONSTRAINT

小批测试 / 合规沙盒 / 夜间物流

证据门：可维护 · 可追溯 · 可撤回

AI 原点 · 开放共造




104.3 ha

PROVISIONAL CONSTRAINT

公共算力 / 技能认证 / 开源工坊

证据门：可维护 · 可追溯 · 可撤回

大钟寺 · 日常维修

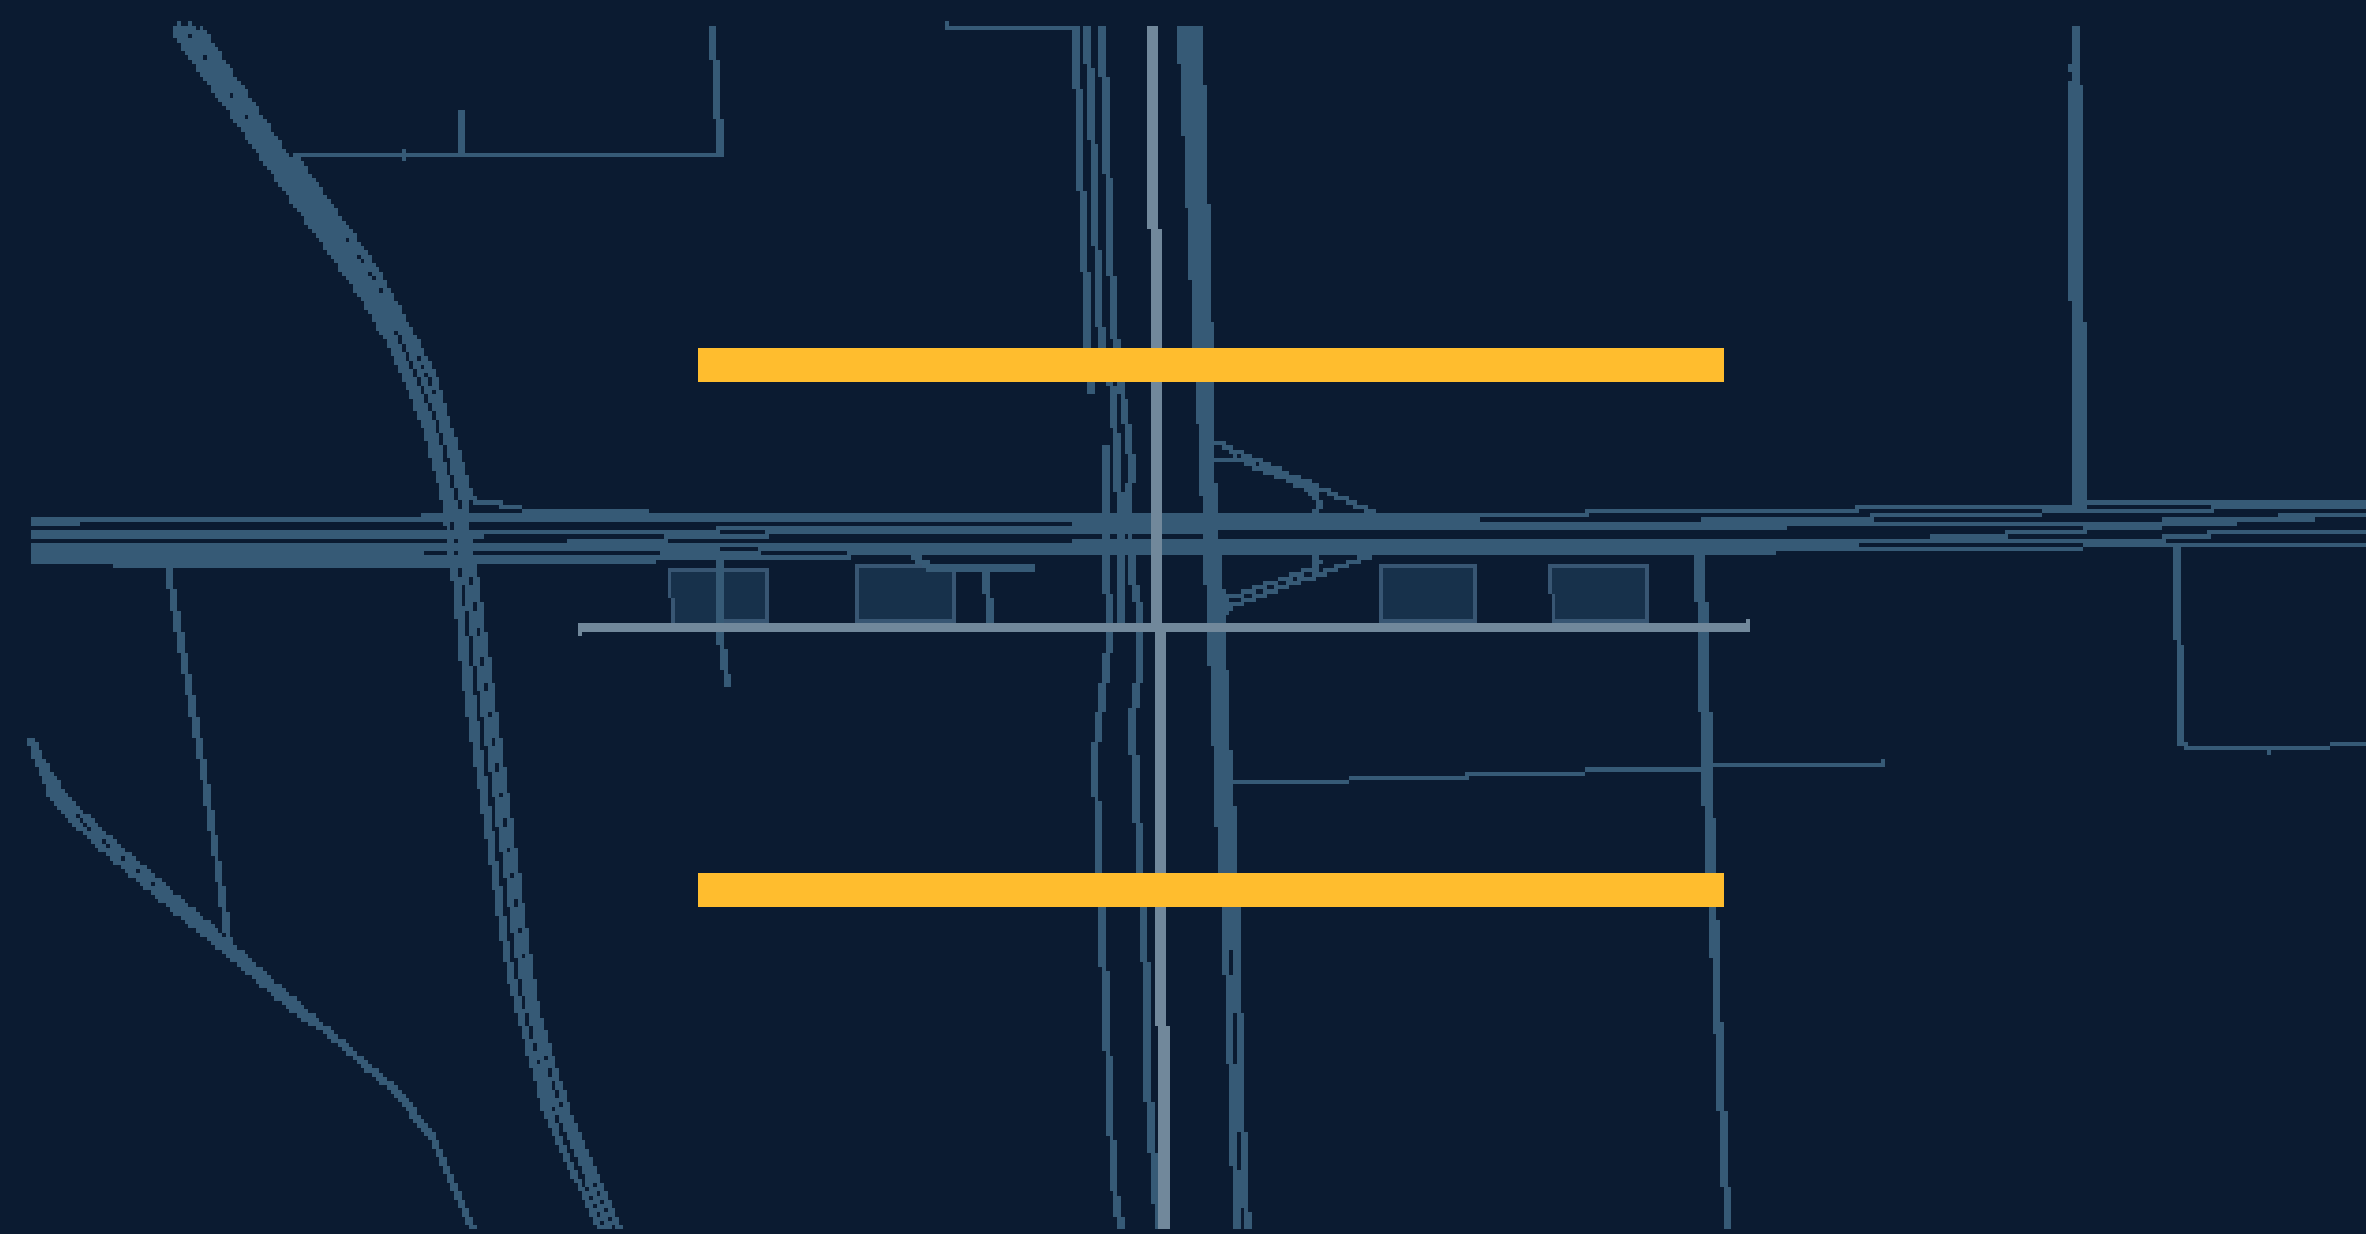

72.0 ha

PROVISIONAL CONSTRAINT


维修市集 / 零件银行 / 回收再造

证据门：可维护 · 可追溯 · 可撤回

三网叠合：到达、生态、照护

轨道站点—慢行绿脊—15 分钟公共服务同图校核

复合网络图 / COMPOSITE NETWORK

 

- 公共造物绿脊
- 蓝绿开敞空间
- 轨道/道路背景

网络角色 / ROLES

到达网

站点—园区—社区最后一公里

生态网

清河—绿地—口袋公园连续降温

照护网

设备医生、零件银行、无障碍工位

分期动作 / PHASING

1

2026—28

先开工位与维修节点

2

2029—32

连成慢行与数据基础设施

3

2033+

按绩效扩容并保留撤回权

指标不是口号：每个数字都能回到空间与来源

同一数据源驱动 GeoJSON、指标、矩阵、图件与离线可视化

核心指标 / CORE METRICS

11.43 km² 临时总体范围

17.55% 概念绿地率

1.98% 公共造物空间率

18 标准矩阵单元

12 AI+ 场景卡

4 产业测试场景

证据流水线 / AUDIT PIPELINE

01

锁定空间

02

投影复算

03

矩阵校核

04

图件同源

05

双语交付

GeoJSON → EPSG:4548 → metrics.json → compliance / standard / depth matrices → figures / PDF / offline HTML

自检状态 / SELF-CHECK

确定性校验

PASS

空间校验

PASS

视觉包装

PASS

专业证据

PASS

待更新：官方总体边界与三处重点区域 polygon。临时约束不进入最终面积评分。