

原点服务台 ORIGIN SERVICE DESK

AI原点社区近校创新服务网络城市设计


百年京张AI创新带城市设计开源征集 · 概念建议 · provisional 边界 · EPSG:4548 复算

原点服务台·近校创新服务网络总体概念



百年京张AI创新带城市设计开源征集·原点服务台 ORIGIN SERVICE DESK (概念建议)
基于 provisional 临时粗略边界, 非官方红线; 官方几何到位后整包复算。
一轴 (原点服务街)·三台 (策源/成长/发布)·服务窗口网络·遗址公园活力带


用地结构：一轴三台的服务型用地组织

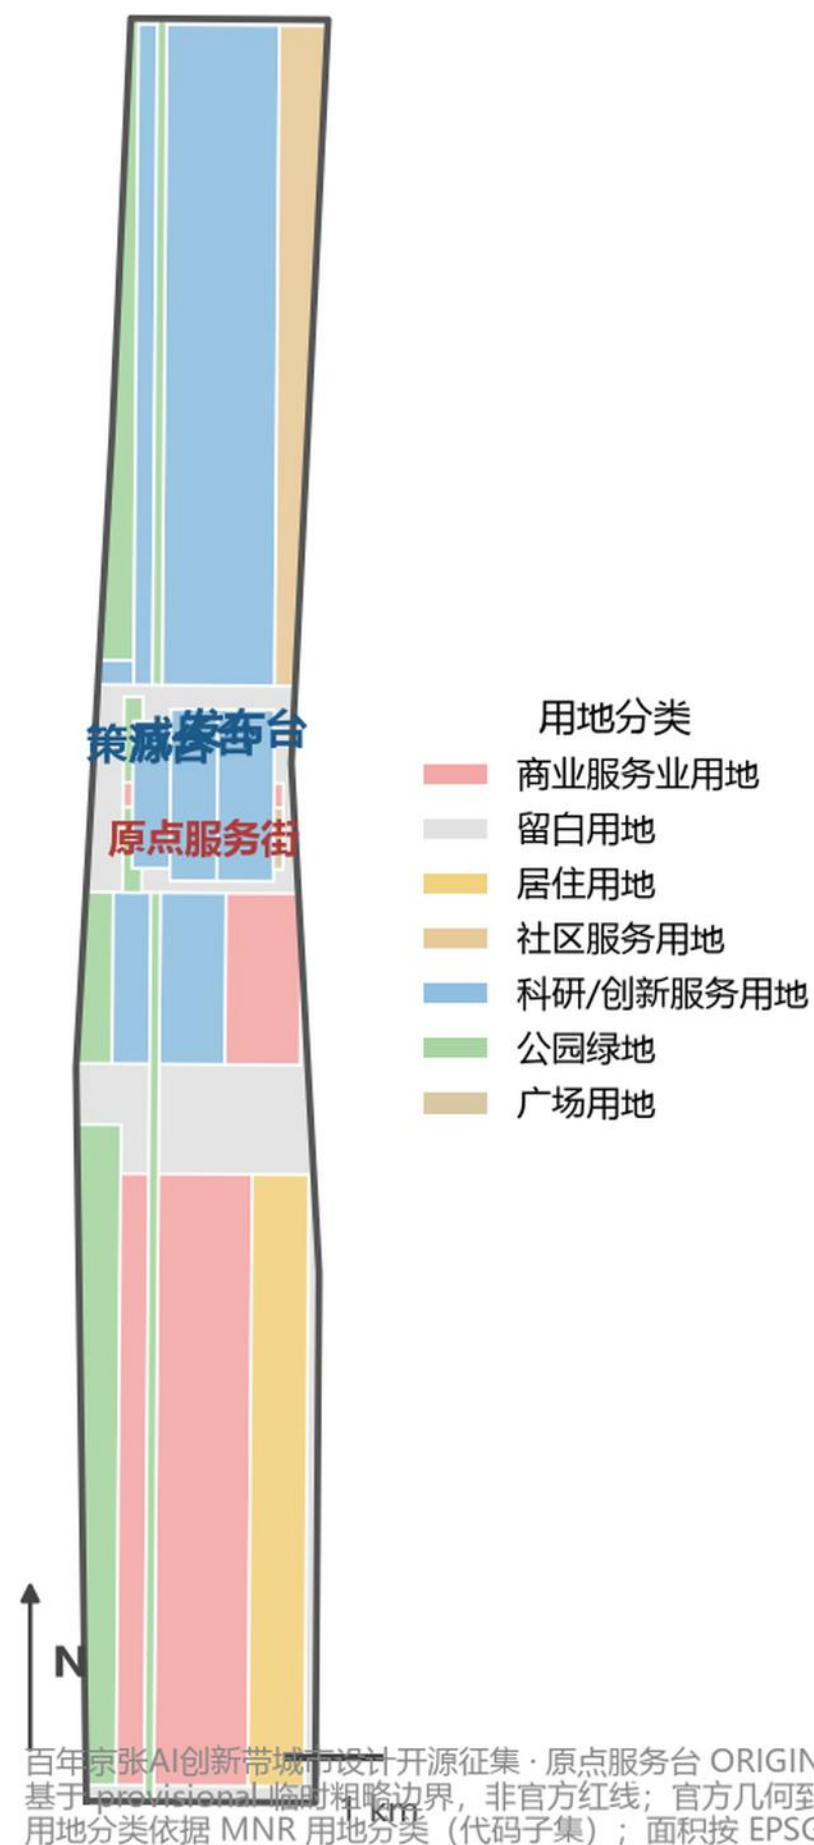

三处重点区域索引




北京AI原点社区·一轴三台详图

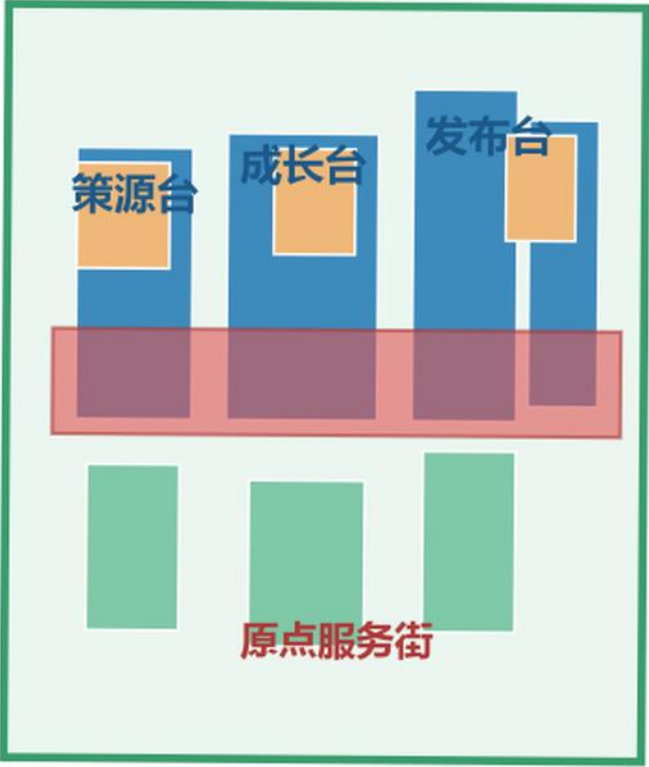


百年京张AI创新带城市设计开源征集·原点服务台 ORIGIN SERVICE DESK (概念建议)
基于 provisional 临时粗略边界，非官方红线；官方几何到位后整包复算。
建筑为概念示意基底，非现状测绘，不代表拆改留结论

交通慢行与蓝绿公共空间复合系统

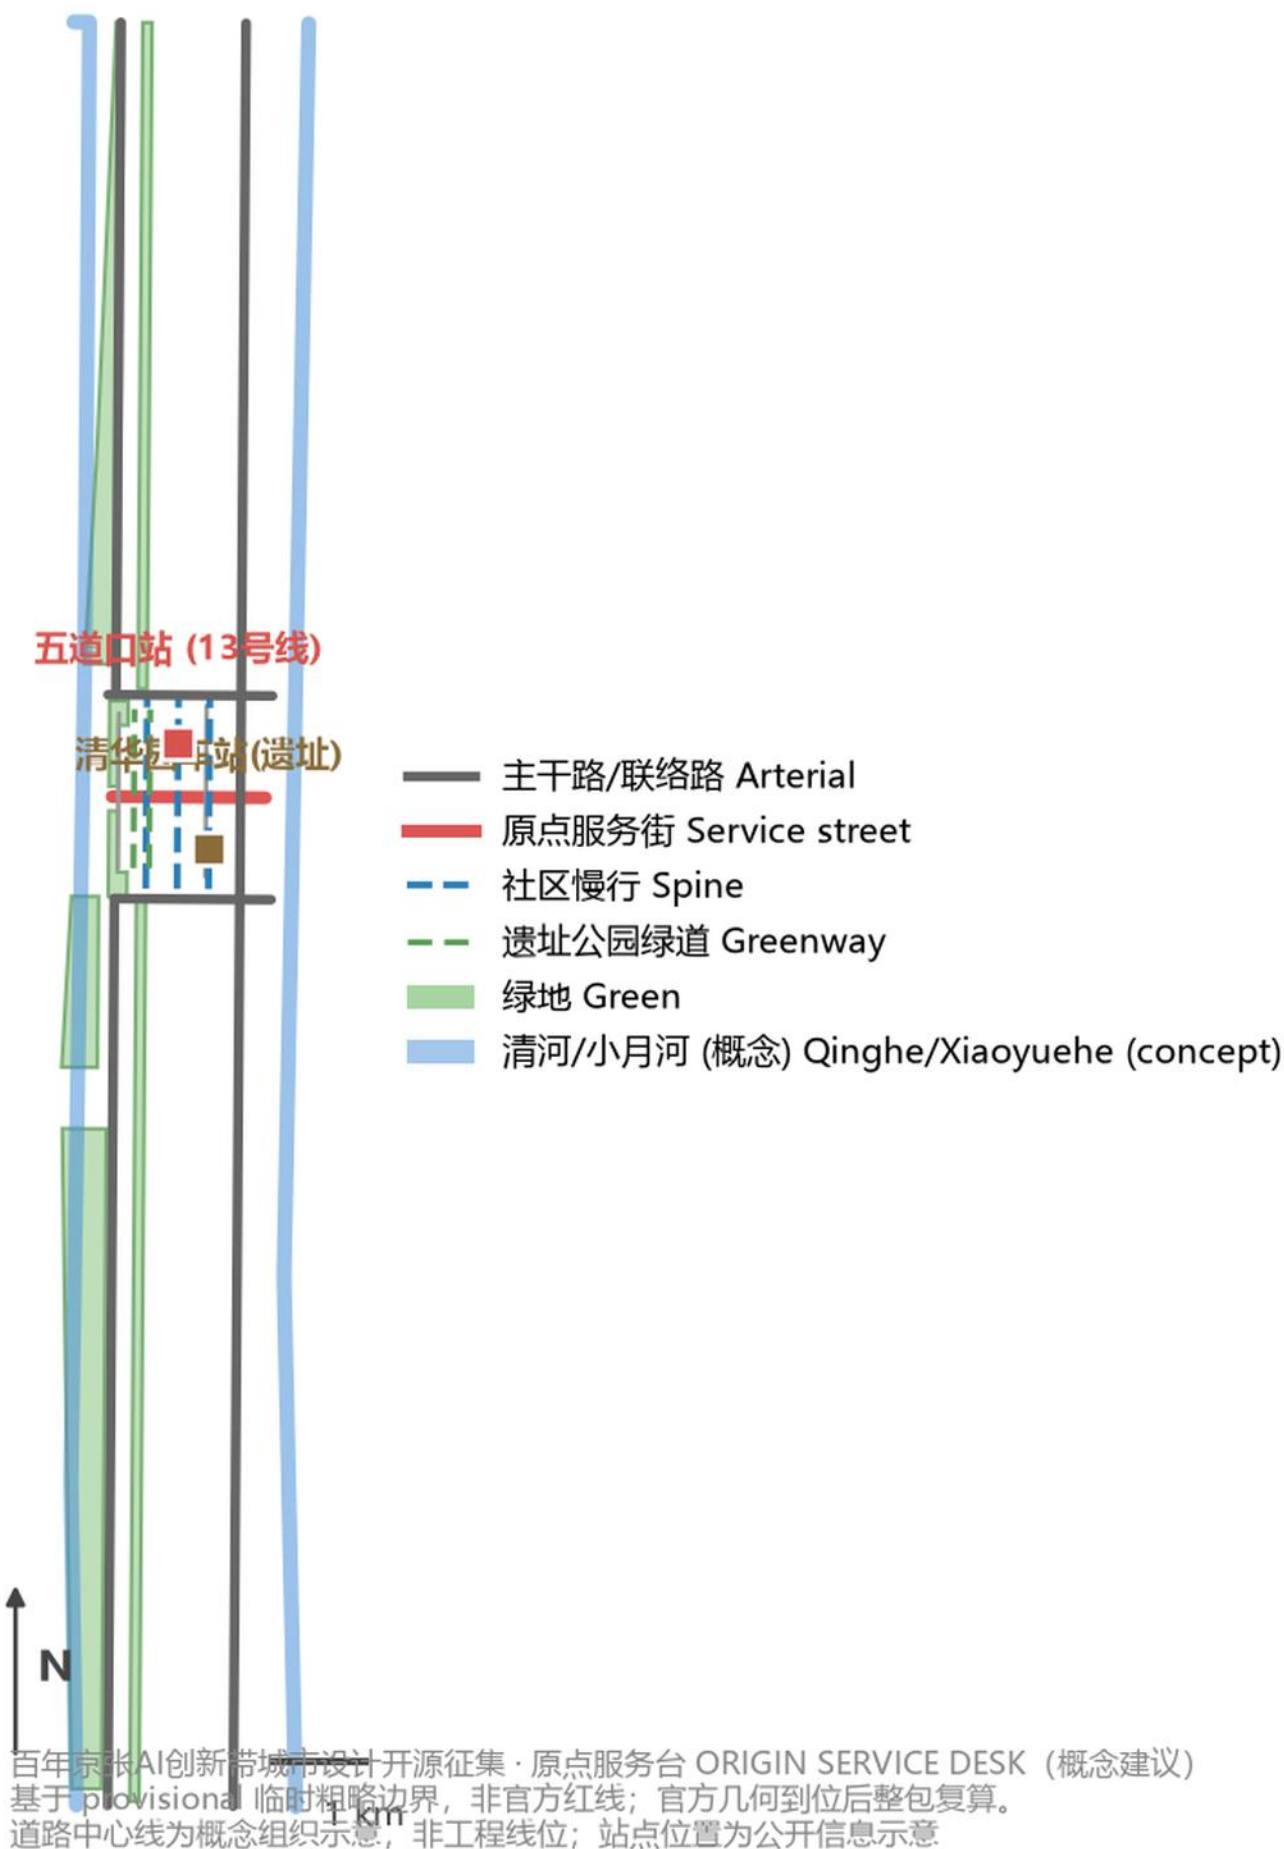


核心指标复算与证据链


面积复算 (km²)

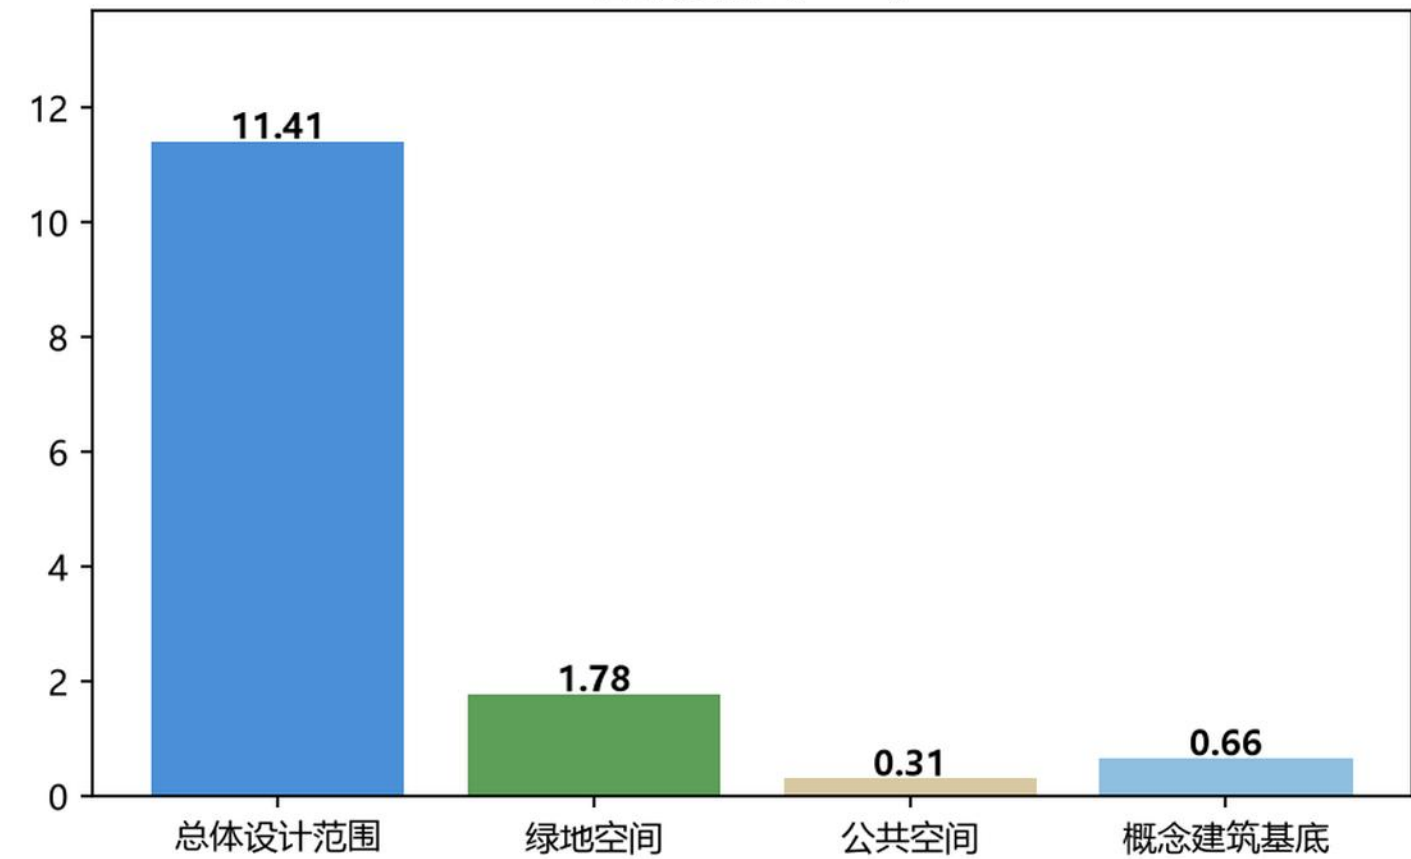

15.6% 占比 (% , EPSG:4548 复算)

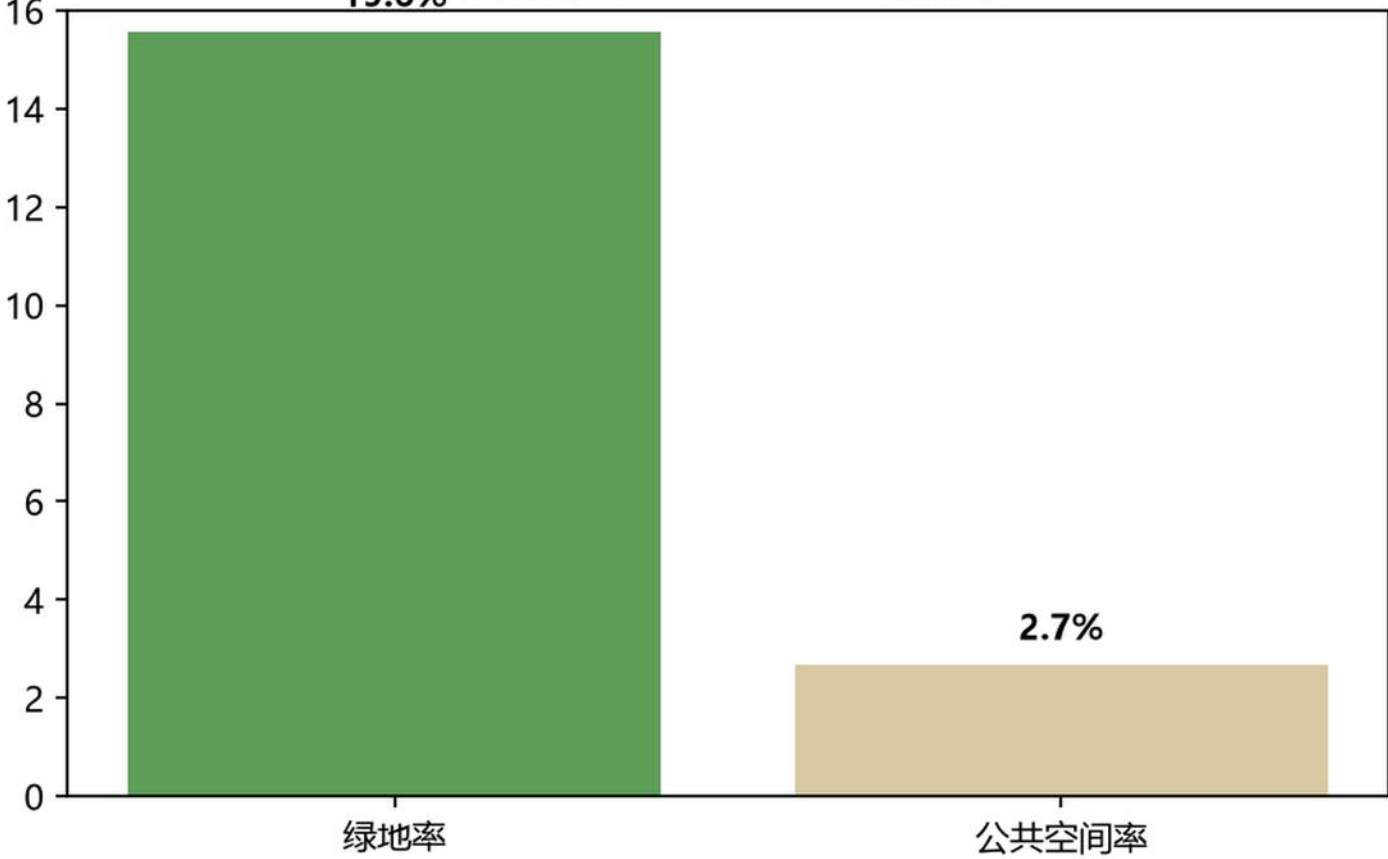

三处重点区面积 (ha, provisional)

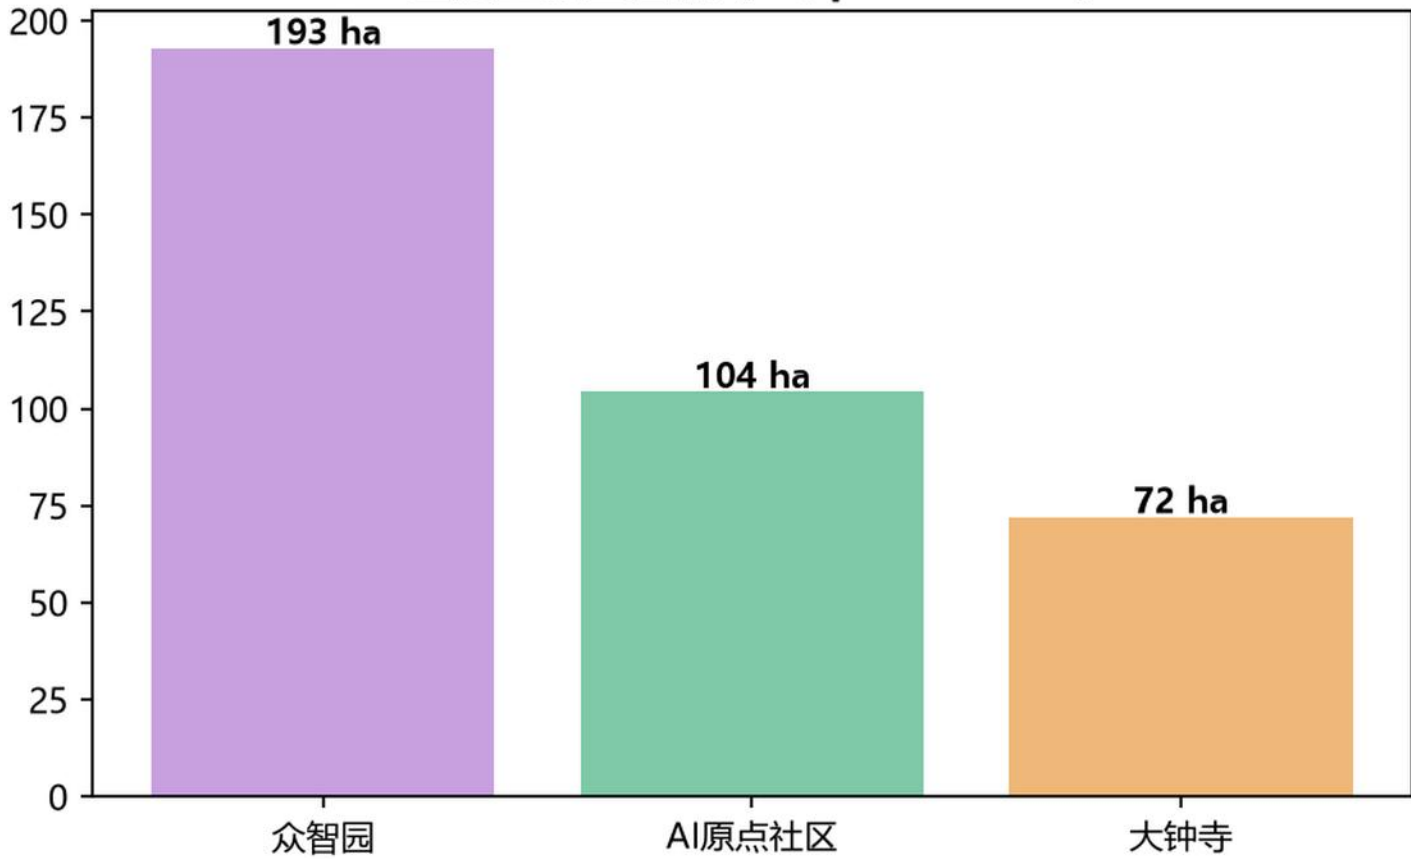

复算说明

计算坐标系: EPSG:4548 (CGCS2000 / 3°GK CM 117E)

交换格式: GeoJSON, EPSG:4326

总体设计范围: 11.4128 km² (公告约 11.4 km²)

绿地率: 15.58% (概念设计值)

公共空间率: 2.69% (概念设计值)

百年京张AI创新带城市设计开源征集: 原点服务台 ORIGIN SERVICE DESK (概念建议)
边界状态: provisional 临时粗略边界, 非官方红线; 官方几何到位后整套复算。
所有指标可由提交 GeoJSON 在 EPSG:4548 下复算; 控规类指标待官方数据