


Two-board · Jingzhang The Gauge Line · Three vertical belts · West · Heritage Belt · Center · AI Life Belt · East · AI Innovation Belt · Residential spine · Blue-green network

图01 资料证据链与三带总览

Fig.01 Evidence Chain & Three-Belt Overview

三带范围由用地地块跨度派生；建筑基底为设计提案体量 / Belts derived from parcel spans

京张尺规线 / Jingzhang The Gauge Line
双轨度量 · Dual Gauge, not Slogan

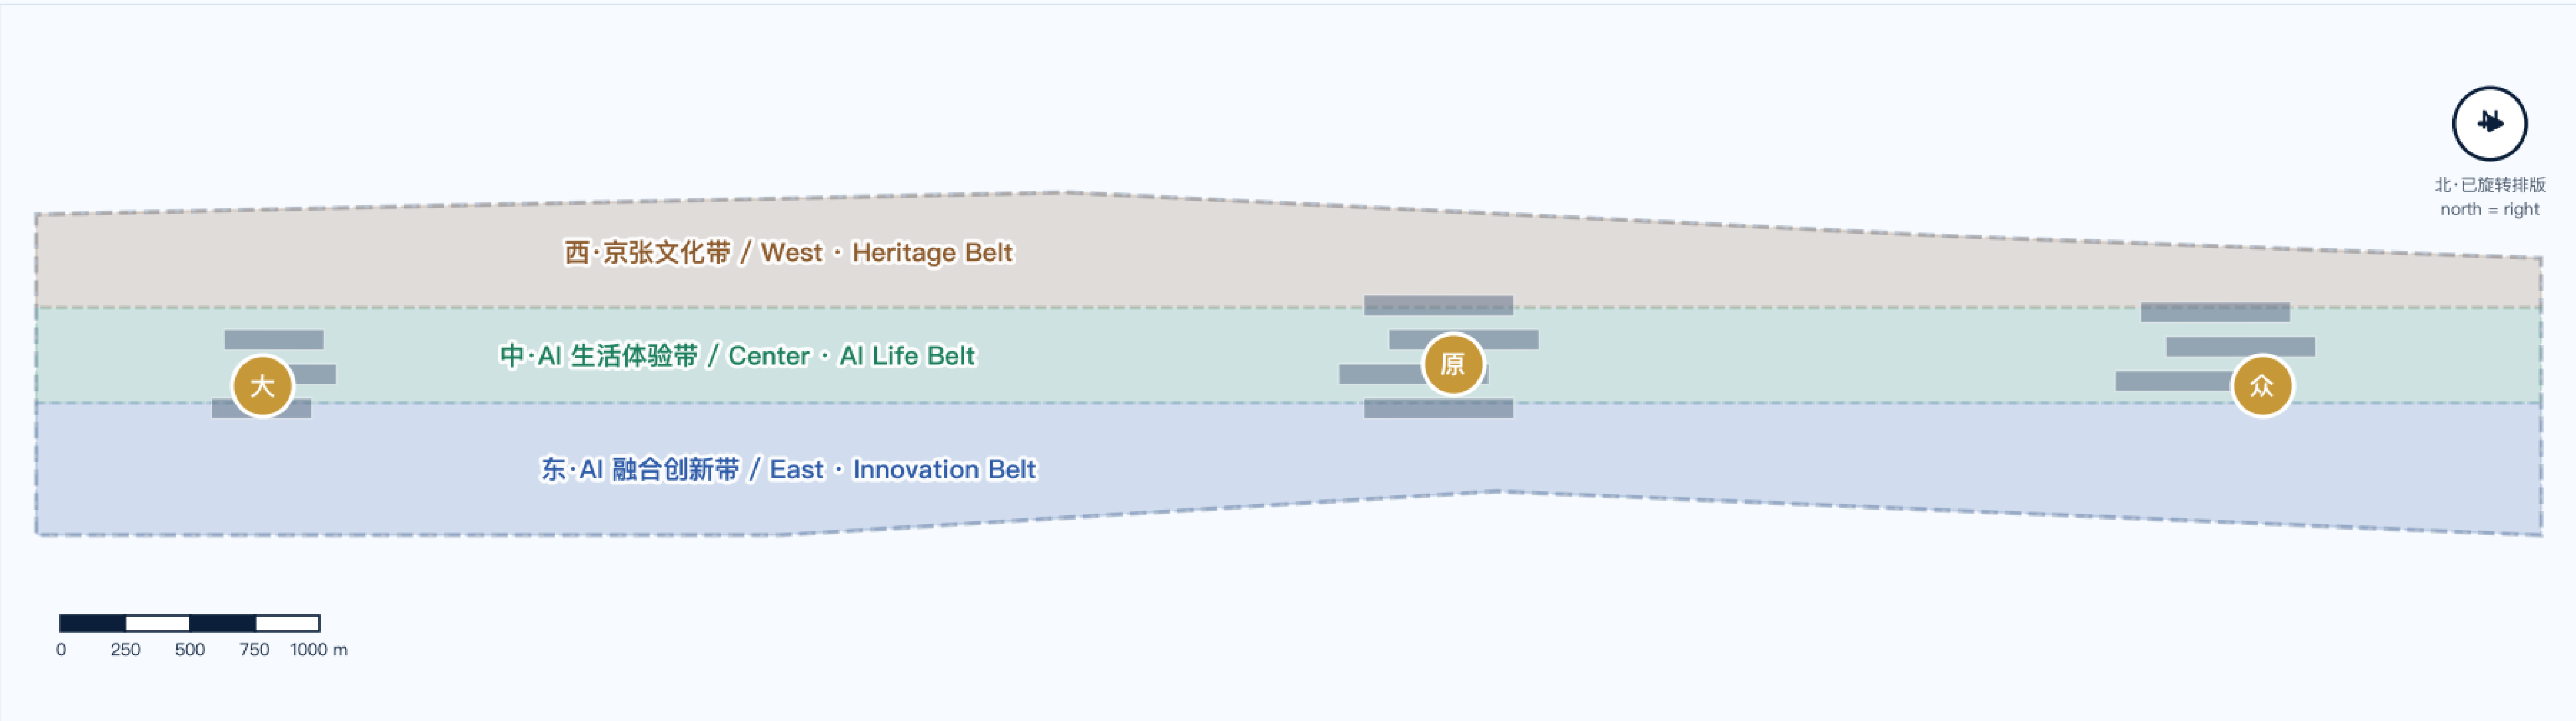

Provisional boundary · 临时粗略边界，仅用于设计讨论与自检，非官方红线 / Not an official redline | 米制投影·等比·已旋转排版 / Projected (m), equal aspect, rotated for layout | Source: provisional_boundaries.geojson (EPSG:4548)




Fig.01 Overview: three belts + key areas + evidence chain
Spatial spine: a human-scale pedestrian spine threads the Jingzhang heritage-park green axis; east-west stitching secondary roads reconnect the fabric severed by the railway. Three key areas — Zhongzhiyuan (autonomous innovation), AI Origin Community (open-source conversion), Dazhongsi (intelligent economy) — land along the axis.

图02 总体设计范围用地结构

Fig.02 Land-Use Structure of Overall Design Area

用地全覆盖、无重叠；代码依《国土空间调查、规划、用途管制分类》；面积占比按米制投影复算

京张尺规线 / Jingzhang The Gauge Line
双轨度量 · Dual Gauge, not Slogan

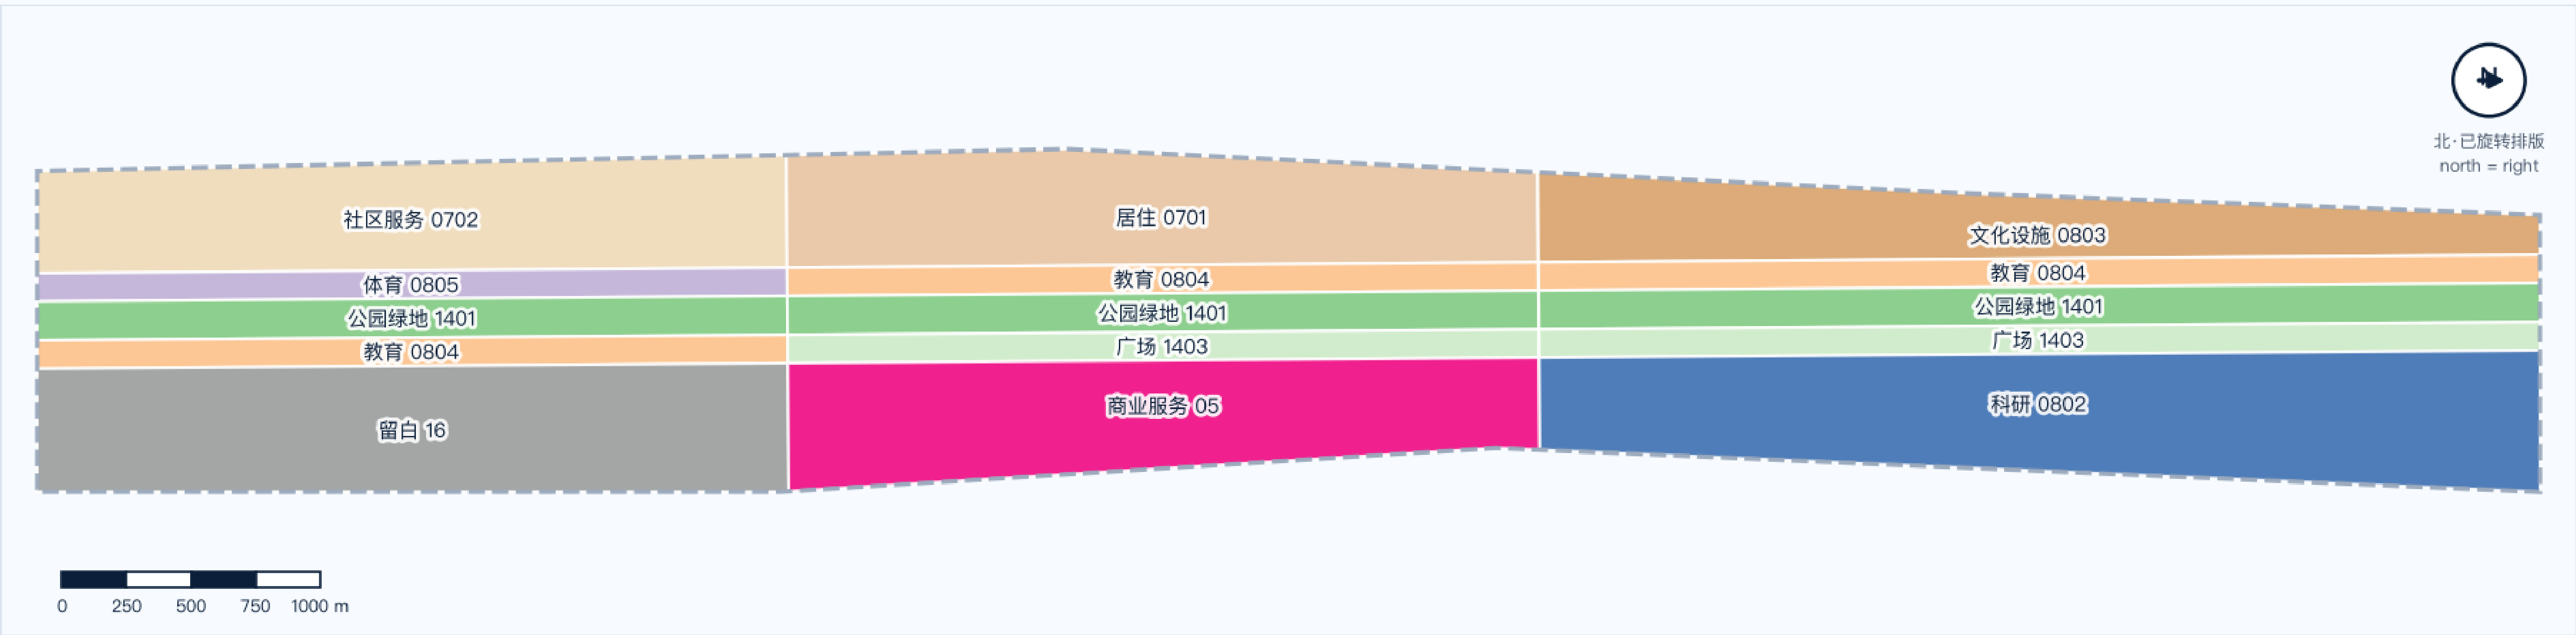

Provisional boundary · 临时粗略边界，仅用于设计讨论与自检，非官方红线 / Not an official redline | 米制投影·等比·已旋转排版 / Projected (m), equal aspect, rotated for layout | Source: provisional_boundaries.geojson (EPSG:4548)

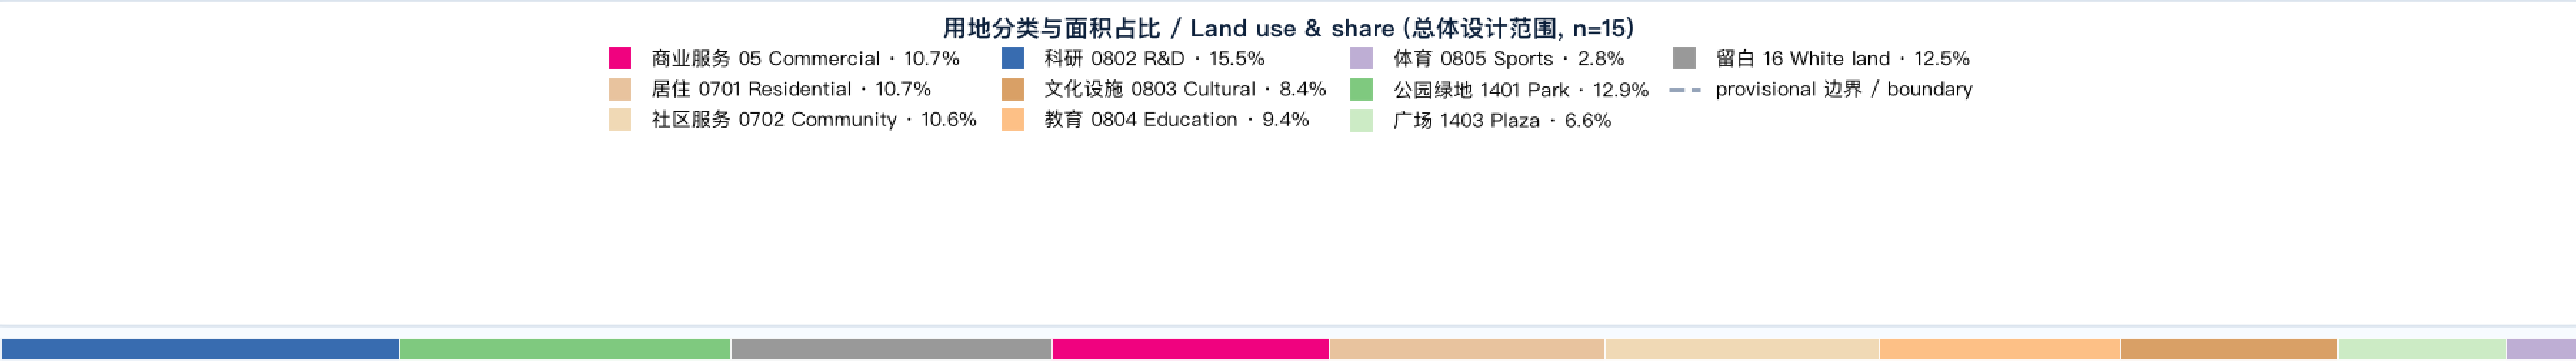


Fig.02 Land-use structure of overall design area


Three key areas & composite systems

图03 三处重点区域索引与设计任务

Fig.03 Three Key Areas Index & Design Tasks

编号对应信息栏卡片 / Numbered chips match the cards below · 每区：定位+结构+更新+慢行+空间+AI+风险

京张尺规线 / Jingzhang The Gauge Line
双轨度量 · Dual Gauge, not Slogan

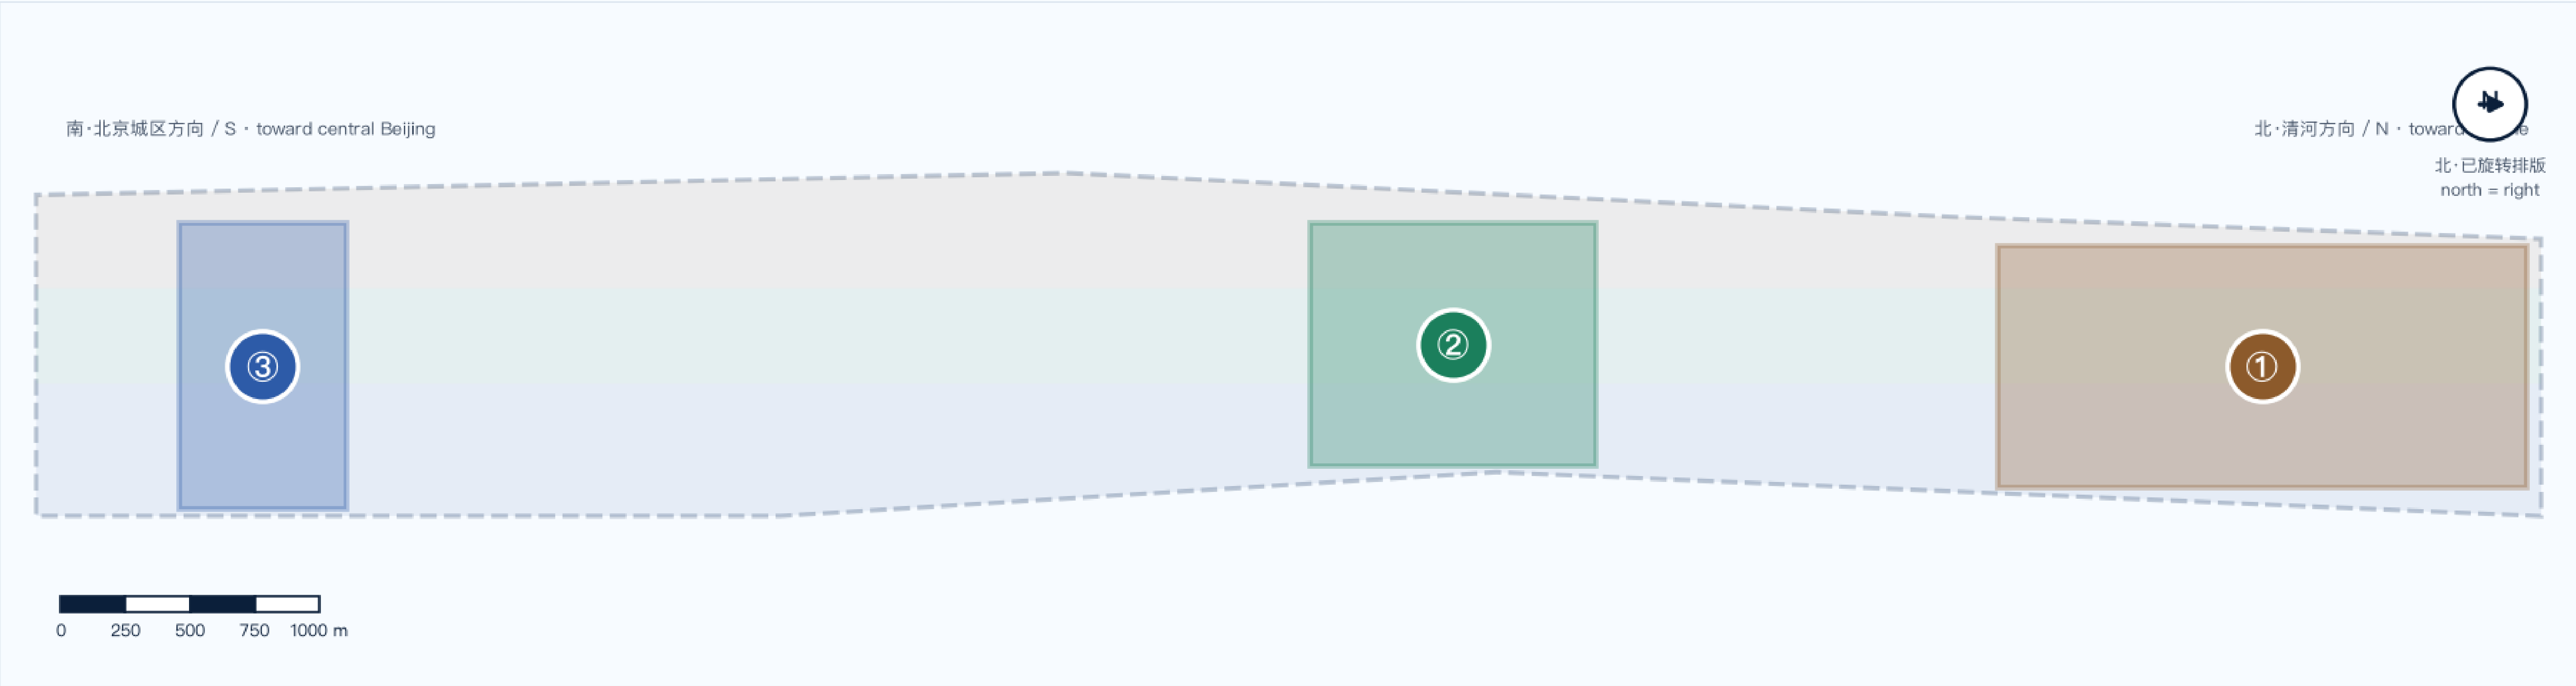

Provisional boundary · 临时粗略边界，仅用于设计讨论与自检，非官方红线 / Not an official redline | 米制投影·等比·已旋转排版 / Projected (m), equal aspect, rotated for layout | Source: provisional_boundaries.geojson (EPSG:4548)

① 众智园 AI 自主创新加速区 Zhongzhiyuan Acceleration Area	② 北京 AI 原点社区 Beijing AI Origin Community	③ 大钟寺 AI 产业聚集区 Dazhongsi Industry Cluster
定位 / Positioning 花园型全栈自主创新街区 设计动作 / Design moves · 自主模型测试 · 标准制定 · 安全治理展示 · 低碳算力体验 深度任务：空间结构+建筑更新+交通慢行+公共空间+AI场景+实施风险	定位 / Positioning 近校型成果转化与人才社区 设计动作 / Design moves · 开源协作 · 成果发布 · 人才特区 · 近校孵化 深度任务：空间结构+建筑更新+交通慢行+公共空间+AI场景+实施风险	定位 / Positioning 城市型智能经济街区 设计动作 / Design moves · 领军企业 · 智能体新业态 · 数据要素 · 四象限连通 深度任务：空间结构+建筑更新+交通慢行+公共空间+AI场景+实施风险


Fig.03 Three key areas index & design tasks

图04 交通慢行与蓝绿公共空间复合系统

Fig.04 Mobility & Blue-Green Public Space System

人本尺度步行主轴 + 东西缝合 + 蓝绿网络 + 现状轨道站点：水系/蓝线为现状约束（OSM）

京张尺规线 / Jingzhang The Gauge Line
双轨度量 · Dual Gauge, not Slogan

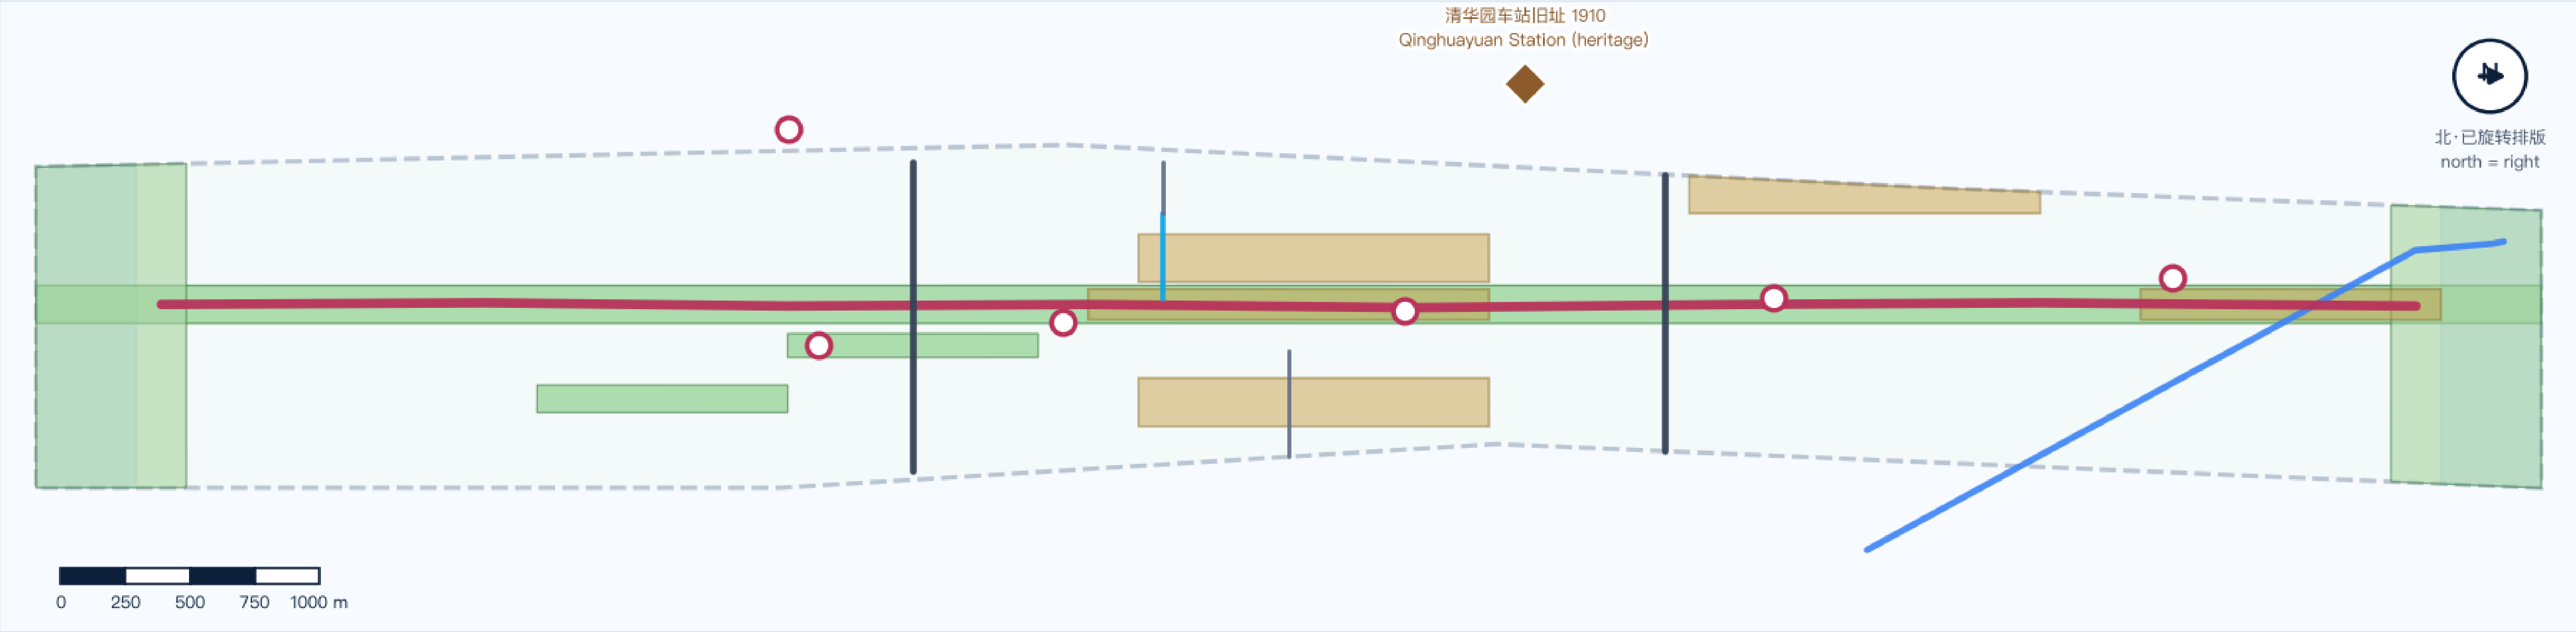

Provisional boundary · 临时粗略边界，仅用于设计讨论与自检，非官方红线 / Not an official redline | 米制投影·等比·已旋转排版 / Projected (m), equal aspect, rotated for layout | Source: provisional_boundaries.geojson (EPSG:4548)

图例 / Legend					
— 现状水系 / Waterway (OSM)	— 缝合次干路 / Stitching road	— 校园道路 / Campus lanes	■ 防护绿地 / Buffer green (1402)		
■ 蓝线管控 (方向性) / Blue-line	— 支路 / Branch	○ 地铁站 (场地周边) / Metro station (n=6)	■ 公共空间·地标前场 / Public space		
— 步行主轴 / Pedestrian spine	— 自行车道 / Cycleway	■ 公园绿地 / Park (1401)	◆ 文保点 / Heritage site		

Fig.04 Mobility & blue-green public space system

图05 核心指标复算与证据链

Fig.05 Metrics Recalculation & Evidence

空间指标由提交几何米制复算；管控指标（FAR/高度）因官方控规缺失标 unknown——承认不知道，比编造假数字更接近真实工程



Fig.05 Metrics recalculation & evidence

AI scenario cards (12, incl. 3 test/validation) — sense-decide-act loops with human review

01 开源发布厅 Open-source release hall	02 安全治理沙盒 Safety-governance sandbox ●测试/test	03 端侧算力驿站 Edge-compute relay ●测试/test	04 自主模型测试场 Autonomous-model testbed ●测试/test
05 AI 慢行导航 AI slow-mobility nav	06 国际路演客厅 Intl. roadshow living room	07 清河低碳创新廊 Qinghe low-carbon corridor	08 近校成果转化街 Near-campus conversion st.
09 数据要素会客厅 Data-factor reception	10 AI 生活服务样板街 AI life-service street	11 京张记忆线路 Jingzhang memory route	12 全球 AI 活动周路线 Global AI Week route

Governance: four agent roles (perception / service / governance / operations) × data boundaries × human review points — data minimization, human-in-the-loop, explainable logging, no substitution for statutory process; agents recommend, never decide. Compliance: no official approval, approved regulatory plan, final ownership or guaranteed implementation is claimed; spatial conclusions under the provisional boundary are directional designs.