

A3 Booklet · Centennial Jingzhang AI Innovation Belt Open Call · Motif: Dual Gauge, not Slogan

Not another software belt, but a real spatial belt that can be measured, walked into and implemented — translating AI from slogans into land-use ratios, street cross-sections, public-space scales and building-renewal actions. Three vertical belts carry the three lines: Heritage (west) / Life (center) / Innovation (east).

图01 资料证据链与三带总览

Fig.01 Evidence Chain & Three-Belt Overview

三带范围由用地地块跨度派生；建筑基底为设计提案体量 / Belts derived from parcel spans

京张尺规线 / Jingzhang The Gauge Line

双轨度量 · Dual Gauge, not Slogan

西·京张文化带 / West · Heritage Belt

中·AI 生活体验带 / Center · AI Life Belt

东·AI 融合创新带 / East · Innovation Belt

大 (Key area: 大=大钟寺)

原 (Key area: 原=AI原点社区)

众 (Key area: 众=众智园)

0 250 500 750 1000 m

北·已旋转排版
north = right

Provisional boundary · 临时粗略边界，仅用于设计讨论与自检，非官方红线 / Not an official redline | 米制投影·等比·已旋转排版 / Projected (m), equal aspect, rotated for layout | Source: provisional_boundaries.geojson (EPSG:4548)

图例 / Legend

西·京张文化带 / West · Heritage Belt

中·AI 生活体验带 / Center · AI Life Belt

东·AI 融合创新带 / East · Innovation Belt

建筑基底 (提案) / Buildings

重点区: 众=众智园 原=AI原点社区 大=大钟寺 / Key areas

provisional 边界 / boundary

证据层级 / Evidence layers

① 公告 + Agent 任务书
Brief & agent taskbook

② provisional 边界 + 三重点区
Provisional boundary + key areas

③ 用地·建筑·道路·绿地·公共空间
Land use · buildings · roads · green

④ metrics 指标复算 (EPSG:4548)
Metrics recomputed in meters

⑤ 合规·标准·深度矩阵 + 自检
Metrics + self-check gates

每一层结论可回溯至提交包内文件 · Every conclusion traces to a file in this package

Fig.01 Evidence chain & three-belt overview

图02 总体设计范围用地结构

Fig.02 Land-Use Structure of Overall Design Area

用地全覆盖、无重叠；代码依《国土空间调查、规划、用途管制分类》；面积占比按米制投影复算

京张尺规线 / Jingzhang The Gauge Line

双轨度量 · Dual Gauge, not Slogan

社区服务 0702

居住 0701

文化设施 0803

体育 0805

教育 0804

公园绿地 1401

广场 1403

留白 16

商业服务 05

科研 0802

0 250 500 750 1000 m

北·已旋转排版
north = right

Provisional boundary · 临时粗略边界，仅用于设计讨论与自检，非官方红线 / Not an official redline | 米制投影·等比·已旋转排版 / Projected (m), equal aspect, rotated for layout | Source: provisional_boundaries.geojson (EPSG:4548)

用地分类与面积占比 / Land use & share (总体设计范围, n=15)

商业服务 05 Commercial · 10.7%

科研 0802 R&D · 15.5%

体育 0805 Sports · 2.8%

留白 16 White land · 12.5%

居住 0701 Residential · 10.7%

文化设施 0803 Cultural · 8.4%

公园绿地 1401 Park · 12.9%

广场 1403 Plaza · 6.6%

社区服务 0702 Community · 10.6%

教育 0804 Education · 9.4%

provisional 边界 / boundary

Fig.02 Three-level scope & land-use structure


Provisional boundary · 临时粗略边界, 非官方红线 · Recalculate when official geometry supplied · Source: provisional_boundaries.geojson (EPSG:4548)

图03 三处重点区域索引与设计任务

Fig.03 Three Key Areas Index & Design Tasks

编号对应信息栏卡片 / Numbered chips match the cards below · 每区：定位+结构+更新+慢行+空间+AI+风险

京张尺规线 / Jingzhang The Gauge Line
双轨度量 · Dual Gauge, not Slogan

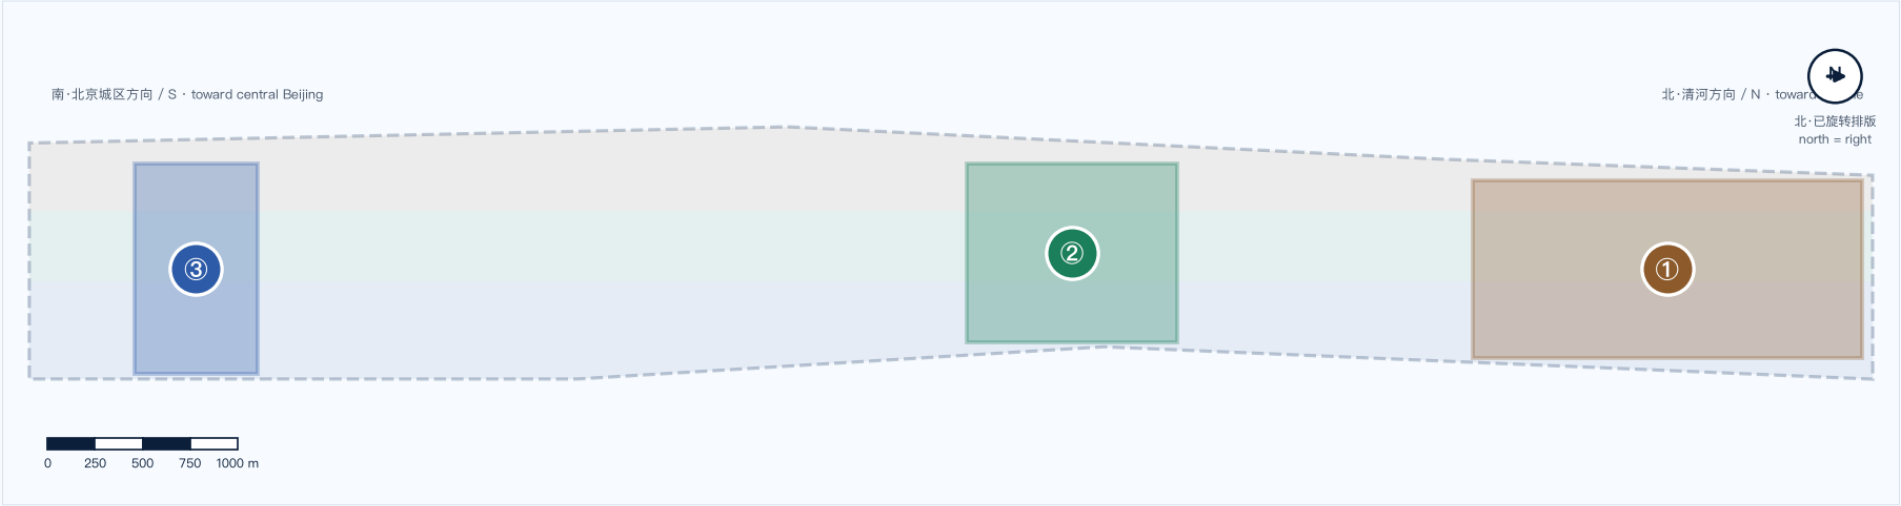

Provisional boundary · 临时粗略边界，仅用于设计讨论与自检，非官方红线 / Not an official redline | 米制投影·等比·已旋转排版 / Projected (m), equal aspect, rotated for layout | Source: provisional_boundaries.geojson (EPSG:4548)

① 众智园 AI 自主创新加速区 Zhongzhiyuan Acceleration Area	② 北京 AI 原点社区 Beijing AI Origin Community	③ 大钟寺 AI 产业聚集区 Dazhongsi Industry Cluster
定位 / Positioning 花园型全栈自主创新街区 设计动作 / Design moves · 自主模型测试 · 标准制定 · 安全治理展示 · 低碳算力体验 深度任务：空间结构+建筑更新+交通慢行+公共空间+AI场景+实施风险	定位 / Positioning 近校型成果转化与人才社区 设计动作 / Design moves · 开源协作 · 成果发布 · 人才特区 · 近校孵化 深度任务：空间结构+建筑更新+交通慢行+公共空间+AI场景+实施风险	定位 / Positioning 城市型智能经济街区 设计动作 / Design moves · 领军企业 · 智能体新业态 · 数据要素 · 四象限连通 深度任务：空间结构+建筑更新+交通慢行+公共空间+AI场景+实施风险


Fig.03 Three key areas index

图04 交通慢行与蓝绿公共空间复合系统

Fig.04 Mobility & Blue-Green Public Space System

人本尺度步行主轴 + 东西缝合 + 蓝绿网络 + 现状轨道站点；水系/蓝线为现状约束（OSM）

京张尺规线 / Jingzhang The Gauge Line
双轨度量 · Dual Gauge, not Slogan

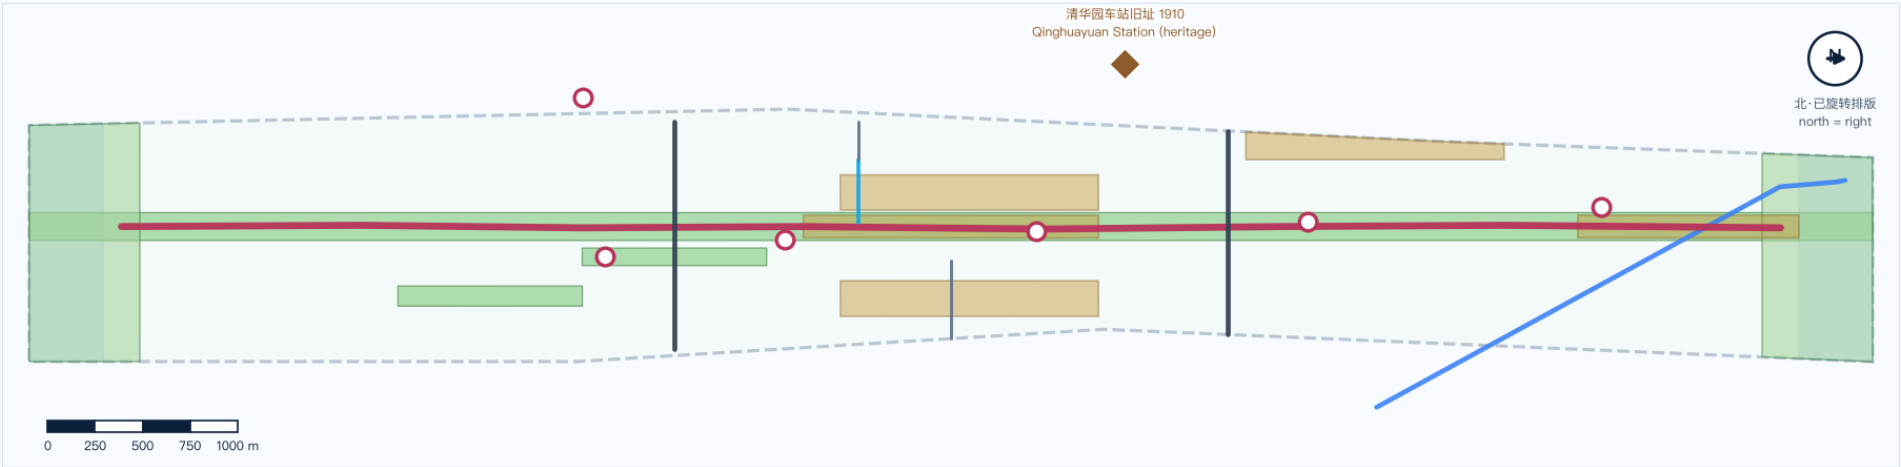

Provisional boundary · 临时粗略边界，仅用于设计讨论与自检，非官方红线 / Not an official redline | 米制投影·等比·已旋转排版 / Projected (m), equal aspect, rotated for layout | Source: provisional_boundaries.geojson (EPSG:4548)

图例 / Legend			
— 现状水系 / Waterway (OSM)	— 缝合次干路 / Stitching road	— 校园道路 / Campus lanes	■ 防护绿地 / Buffer green (1402)
■ 蓝线管控 (方向性) / Blue-line	— 支路 / Branch	○ 地铁站 (场地周边) / Metro station (n=6)	■ 公共空间·地标前场 / Public space
— 步行主轴 / Pedestrian spine	— 自行车道 / Cycleway	■ 公园绿地 / Park (1401)	◆ 文保点 / Heritage site

Fig.04 Mobility & blue-green public space

图05 核心指标复算与证据链

Fig.05 Metrics Recalculation & Evidence

空间指标由提交几何米制复算；管控指标（FAR/高度）因官方控规缺失标 unknown——承认不知道，比编造假数字更接近真实工程

京张尺规线 / Jingzhang The Gauge Line



Fig.05 Metrics recomputation & evidence

3. Core metrics (recomputed, EPSG:4548)

Metric / 指标	Value / 值	Unit	Source / 来源
site_area / 总体范围面积	11,411,445	sqm	site_boundary.geojson
green_ratio / 绿地率	24.6	%	green_space.geojson
public_space_ratio / 公共空间率	8.7	%	public_space.geojson
building_footprint / 建筑基底	419,486	sqm	buildings.geojson
slow_mobility_length / 慢行总长	11,963	m	roads.geojson
land_use_parcelscount / 用地地块	15	count	land_use.geojson
key_area_count / 重点区	3	count	key_areas.geojson
FAR / 容积率	unknown	—	planning_limits.json (missing)
height / 建筑高度	unknown	—	planning_limits.json (missing)