

京张尺规线 / Jingzhang The Gauge Line

A3 图册 · 百年京张AI创新带城市设计开源征集 · 母题：双轨度量（Dual Gauge, not Slogan）

一、方案主旨


不写又一条软件带，做一条可被丈量、可被走入、能落地的真实空间带——把 AI 从概念口号翻译成用地比例、街道断面、公共空间尺度和建筑更新动作。三纵带结构承载三条主线：京张文化带（西）/ AI 生活体验带（中）/ AI 融合创新带（东）。

二、核心图纸

图01 资料证据链与三带总览

Fig.01 Evidence Chain & Three-Belt Overview

三带范围由用地地块跨度派生；建筑基底为设计提案体量 / Belts derived from parcel spans

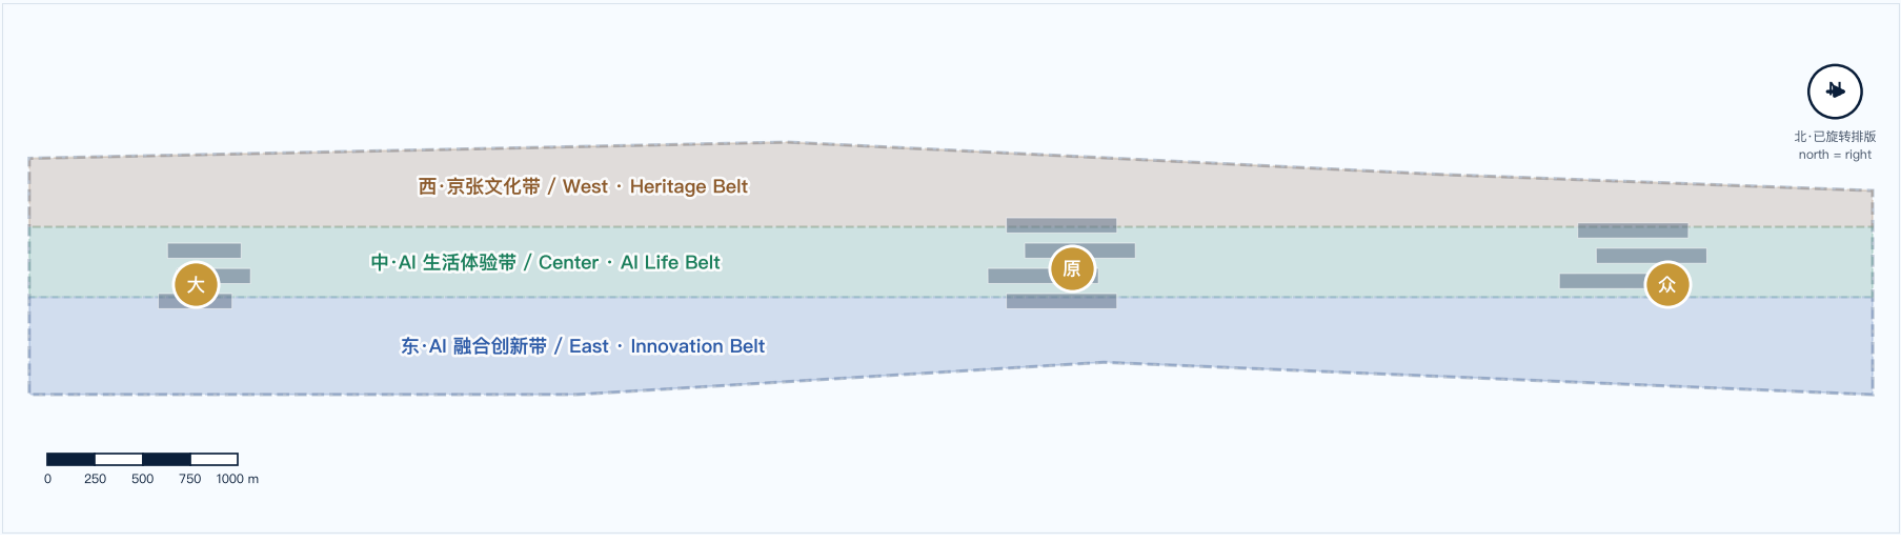

Provisional boundary · 临时粗略边界，仅用于设计讨论与自检，非官方红线 / Not an official redline | 米制投影·等比·已旋转排版 / Projected (m), equal aspect, rotated for layout | Source: provisional_boundaries.geojson (EPSG:4548)

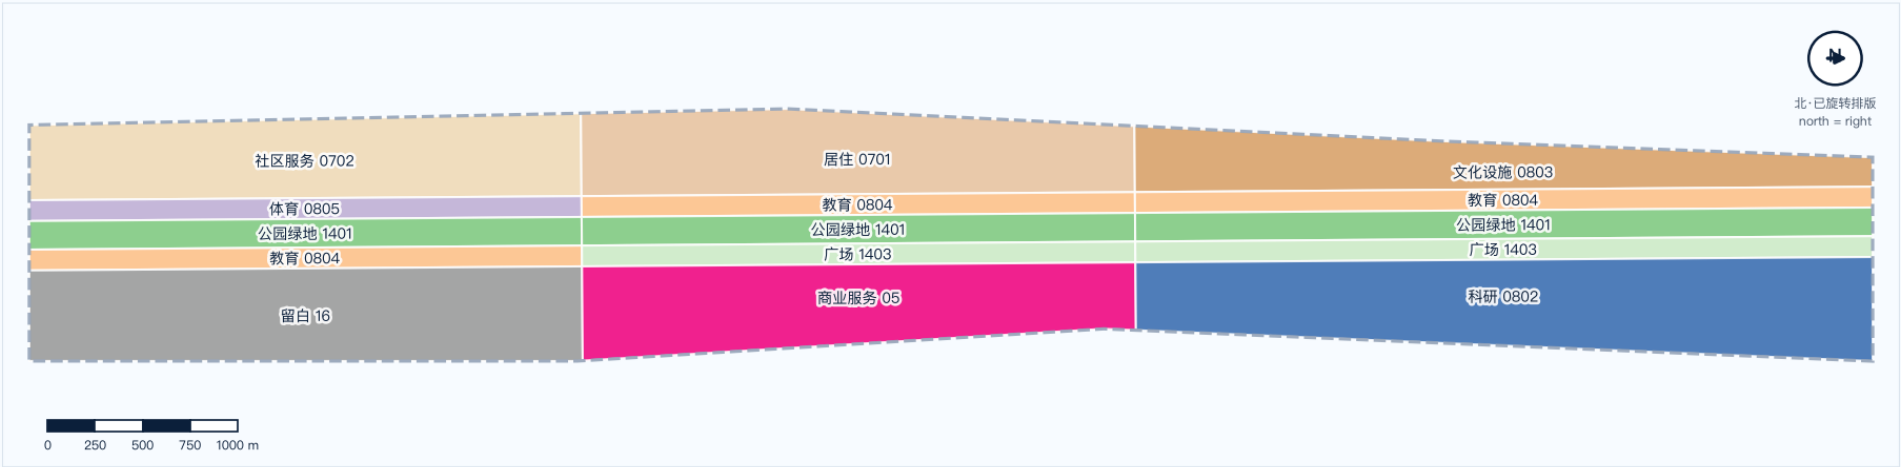


图01 资料证据链与三带总览

图02 总体设计范围用地结构

Fig.02 Land-Use Structure of Overall Design Area

用地全覆盖、无重叠；代码依《国土空间调查、规划、用途管制分类》；面积占比按米制投影复算



Provisional boundary · 临时粗略边界，仅用于设计讨论与自检，非官方红线 / Not an official redline | 米制投影·等比·已旋转排版 / Projected (m), equal aspect, rotated for layout | Source: provisional_boundaries.geojson (EPSG:4548)

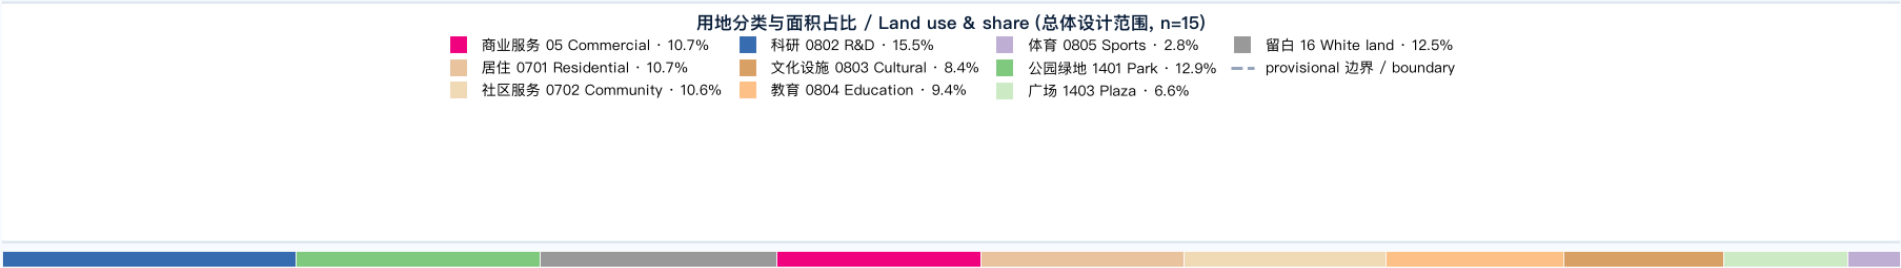



图02 三层范围与用地结构

图03 三处重点区域索引与设计任务

Fig.03 Three Key Areas Index & Design Tasks

编号对应信息栏卡片 / Numbered chips match the cards below · 每区：定位+结构+更新+慢行+空间+AI+风险

京张尺规线 / Jingzhang The Gauge Line
双轨度量 · Dual Gauge, not Slogan

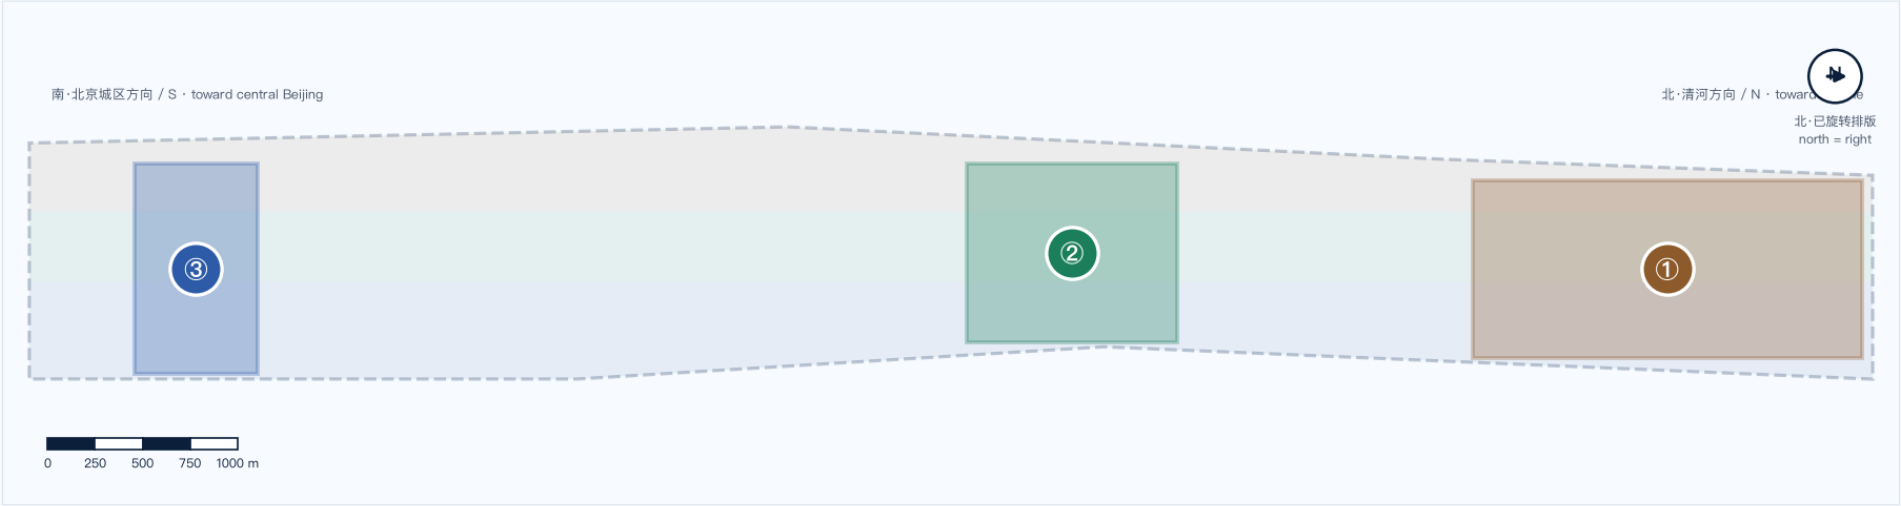

Provisional boundary · 临时粗略边界，仅用于设计讨论与自检，非官方红线 / Not an official redline | 米制投影·等比·已旋转排版 / Projected (m), equal aspect, rotated for layout | Source: provisional_boundaries.geojson (EPSG:4548)

① 众智园 AI 自主创新加速区 Zhongzhiyuan Acceleration Area	② 北京 AI 原点社区 Beijing AI Origin Community	③ 大钟寺 AI 产业聚集区 Dazhongsi Industry Cluster
定位 / Positioning 花园型全栈自主创新街区 设计动作 / Design moves · 自主模型测试 · 标准制定 · 安全治理展示 · 低碳算力体验 深度任务：空间结构+建筑更新+交通慢行+公共空间+AI场景+实施风险	定位 / Positioning 近校型成果转化与人才社区 设计动作 / Design moves · 开源协作 · 成果发布 · 人才特区 · 近校孵化 深度任务：空间结构+建筑更新+交通慢行+公共空间+AI场景+实施风险	定位 / Positioning 城市型智能经济街区 设计动作 / Design moves · 领军企业 · 智能体新业态 · 数据要素 · 四象限连通 深度任务：空间结构+建筑更新+交通慢行+公共空间+AI场景+实施风险


图03 三处重点区域索引

图04 交通慢行与蓝绿公共空间复合系统

Fig.04 Mobility & Blue-Green Public Space System

人本尺度步行主轴 + 东西缝合 + 蓝绿网络 + 现状轨道站点；水系/蓝线为现状约束（OSM）

京张尺规线 / Jingzhang The Gauge Line
双轨度量 · Dual Gauge, not Slogan

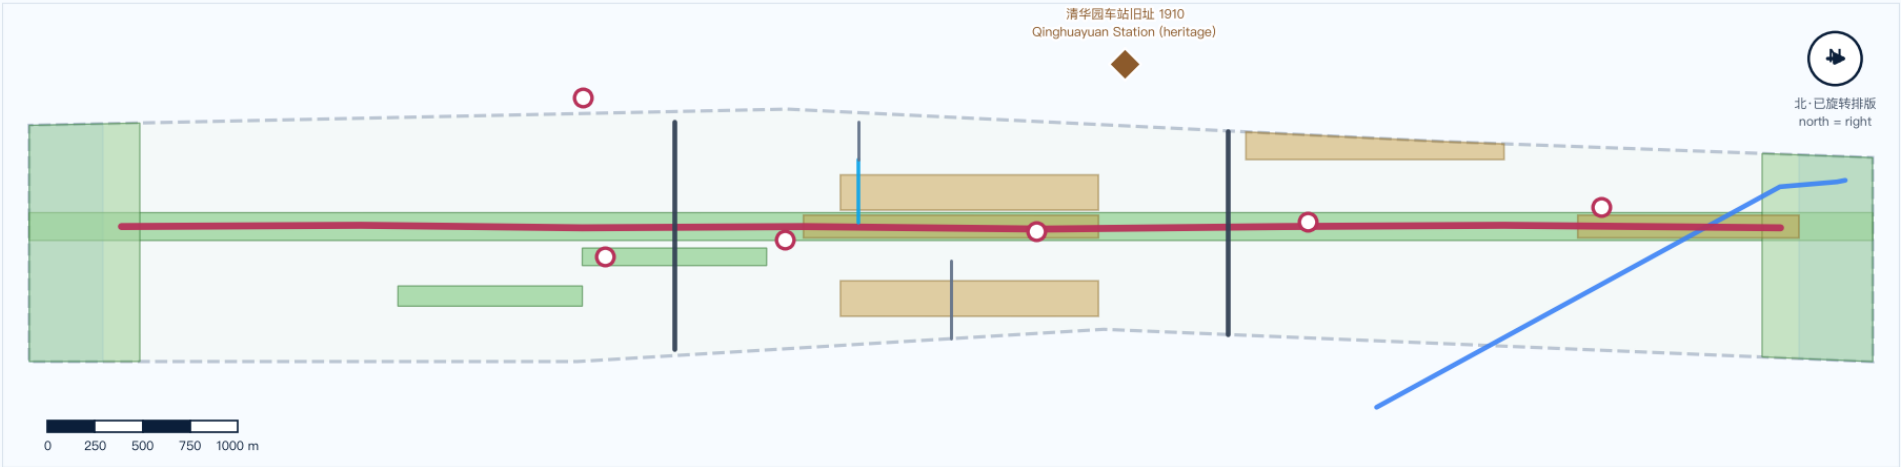

Provisional boundary · 临时粗略边界，仅用于设计讨论与自检，非官方红线 / Not an official redline | 米制投影·等比·已旋转排版 / Projected (m), equal aspect, rotated for layout | Source: provisional_boundaries.geojson (EPSG:4548)

现状水系 / Waterway (OSM) 蓝线管控 (方向性) / Blue-line 步行主轴 / Pedestrian spine	缝合次干路 / Stitching road 支路 / Branch 自行车道 / Cycleway	图例 / Legend 校园道路 / Campus lanes 地铁站 (场地周边) / Metro station (n=6) 公园绿地 / Park (1401)	防护绿地 / Buffer green (1402) 公共空间·地标前场 / Public space 文保点 / Heritage site
--	--	---	---

图04 交通慢行与蓝绿公共空间

图05 核心指标复算与证据链

Fig.05 Metrics Recalculation & Evidence

空间指标由提交几何米制复算；管控指标（FAR/高度）因官方控规缺失标 unknown——承认不知道，比编造假数字更接近真实工程

京张尺规线 / Jingzhang The Gauge Line



图05 核心指标复算与证据链

三、核心指标（EPSG:4548 复算）

Metric / 指标	Value / 值	Unit	Source / 来源
site_area / 总体范围面积	11,411,445	sqm	site_boundary.geojson
green_ratio / 绿地率	24.6	%	green_space.geojson
public_space_ratio / 公共空间率	8.7	%	public_space.geojson
building_footprint / 建筑基底	419,486	sqm	buildings.geojson
slow_mobility_length / 慢行总长	11,963	m	roads.geojson
land_use_parcel / 用地地块	15	count	land_use.geojson
key_area_count / 重点区	3	count	key_areas.geojson
FAR / 容积率	unknown	—	planning_limits.json (missing)
height / 建筑高度	unknown	—	planning_limits.json (missing)