

# 总体城市设计：全线定位 + 三重点区放大


同一真实底图承载两种都能成立的状态；AI只占可关闭口袋

全线定位



概念设计 · 临时边界 · 非官方红线

01 众智园实验门廊

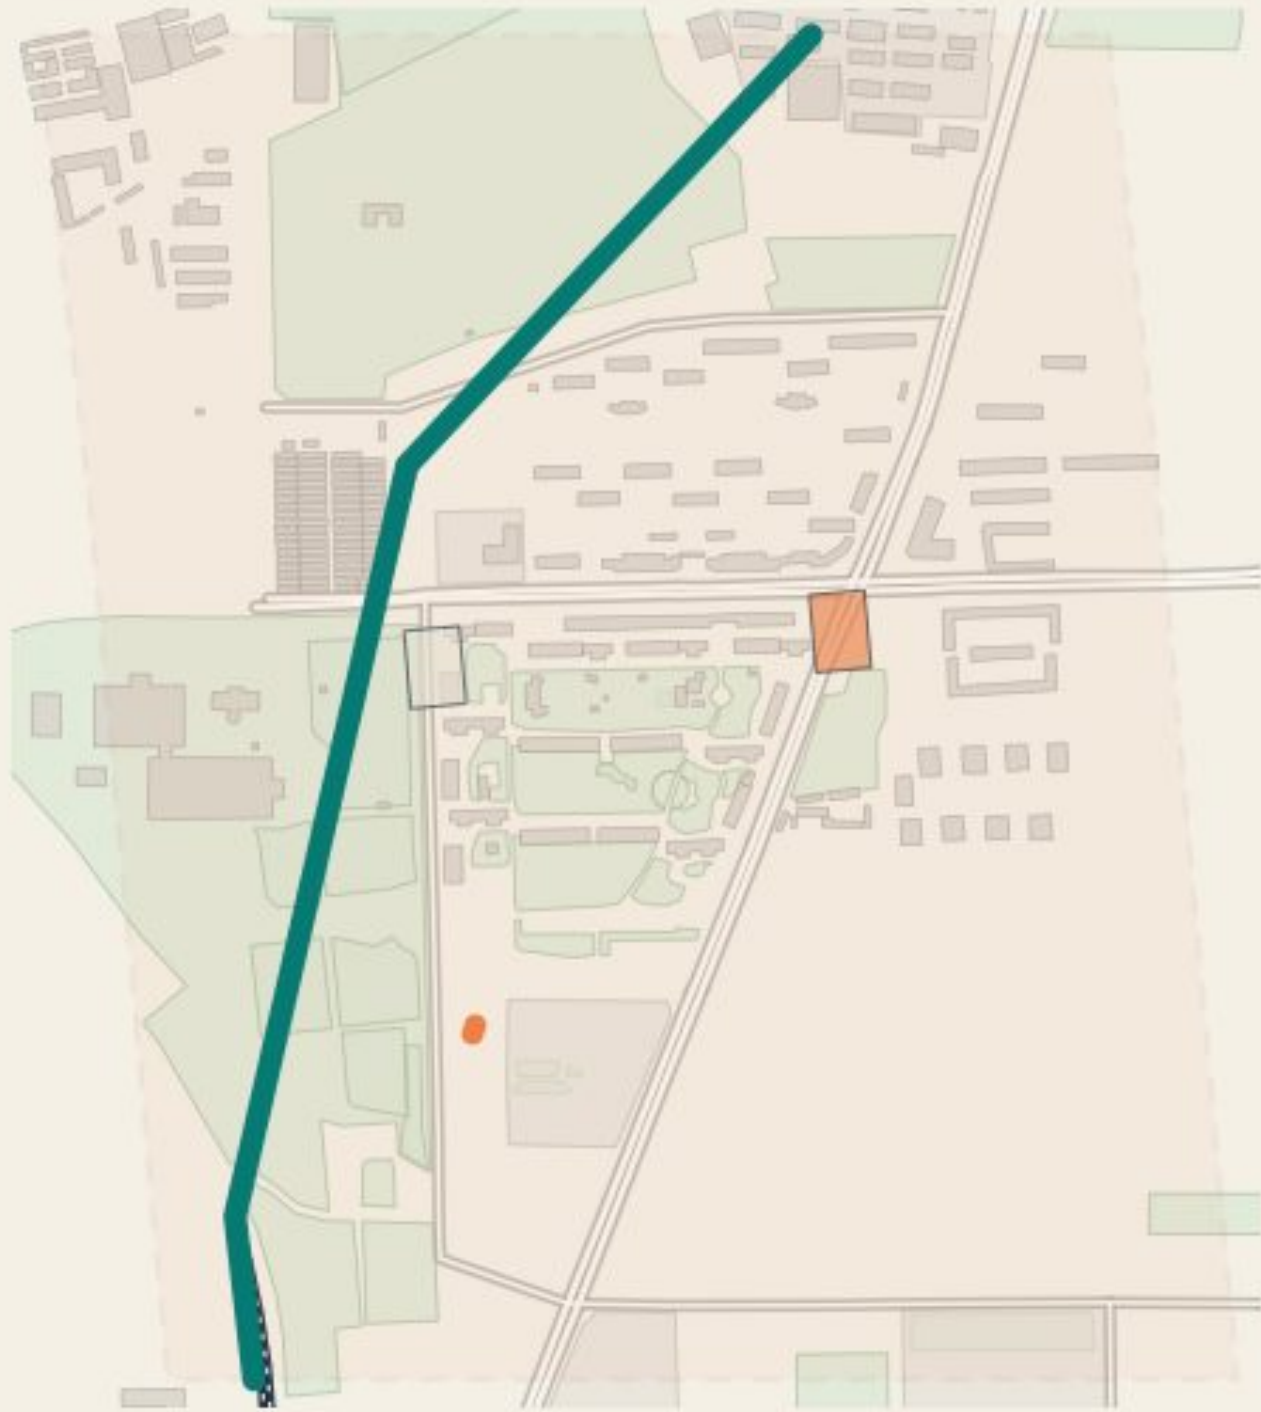

五环南侧的发控测试、清河生态与二期接口

AI ON 公共底层 + 可关闭插件口袋

AI OFF 同一主路 + 人工台 + 静态导视 + 普通用途恢复

轨道安全界面与真实道路接口两态不变；红虚线仍是临时概念范围。

02 AI 原点学习门廊



五道口—清华东路西口：真实站点、城市道路与一期公园

03 大钟寺生活门廊



大钟寺站四条限：轨道换乘、商业首层与社区步行



JING-ZHANG COMMON VERANDA · CONCEPTUAL URBAN DESIGN





# 三个重点区：同一真实底图上的开启 / 关闭双态总平

关闭AI不是清空设计：公众主路、普通用途、静态导视和人工服务必须继续成立

## 01 众智园实验门廊




AI ON 发控测试口袋开启

AI OFF 测试口袋退回普通庭院；公众线不变

五环南侧的发控测试、清河生态与二期接口

每区只画一张真实底图，ON/OFF共享道路、轨道、建筑与公众主路；状态带只改变可关闭插件与恢复用途。  
概念设计 · 临时边界 · 非官方红线

## 02 AI 原点学习门廊

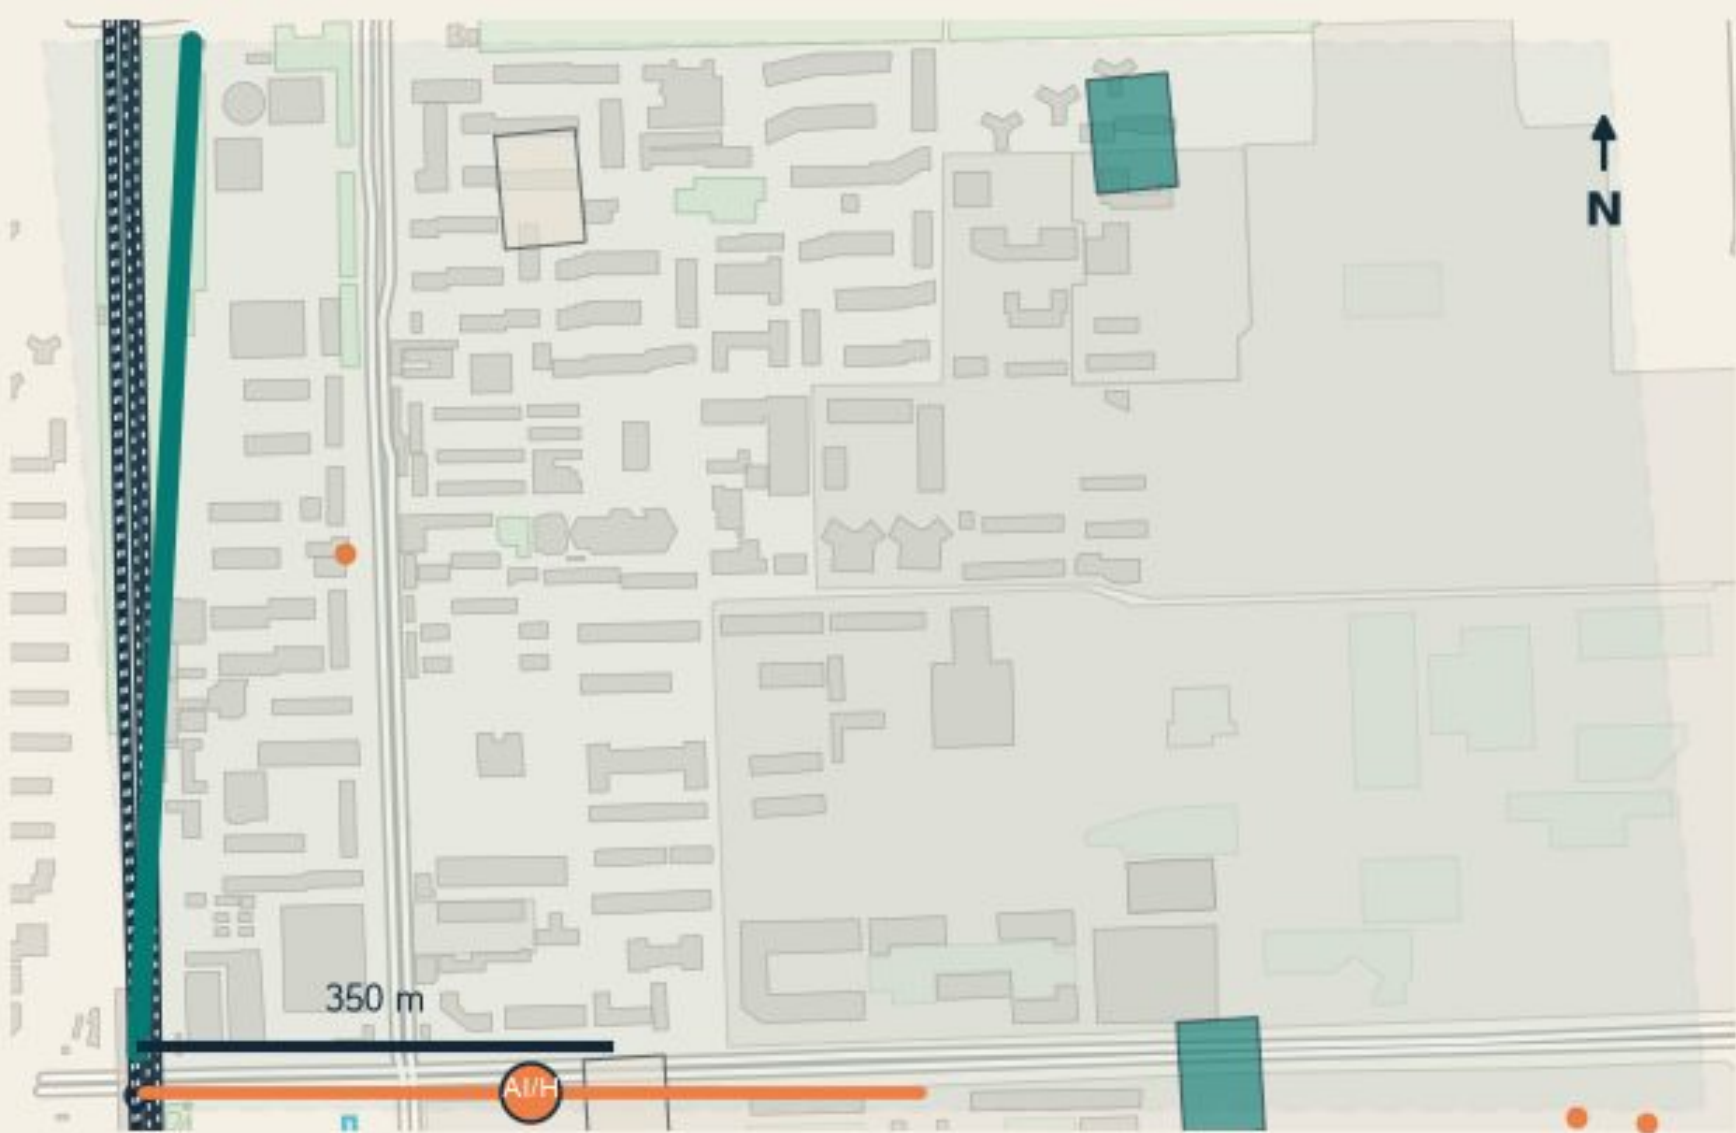

AI ON 来源解释与学习插件开启

AI OFF 纸质来源台与人工课堂继续

五道口—清华东路西口：真实站点、城市道路与一期公园

## 03 大钟寺生活门廊



AI ON 导航、协寻与遗失物插件开启

AI OFF 人工台、饮水、休息与换乘继续

大钟寺站四象限：轨道换乘、商业首层与社区步行

JING-ZHANG COMMON VERANDA · CONCEPTUAL URBAN DESIGN

## 证据分级与边界替换：真实背景不冒充官方红线

四条提示只有一个根源：官方精确polygon尚未公开；数据缺口不间断内容评分

|                                                                |                                                       |                                                            |                                                       |
|----------------------------------------------------------------|-------------------------------------------------------|------------------------------------------------------------|-------------------------------------------------------|
| 01 官方已知<br>文字信息中的面积<br>40.6 km² / 11.4 km² / 368.4 ha<br>可正式引用 | 02 公开真实背景<br>建筑与地铁路口非公开建筑<br>一期已建 / 已建 / 二期拟建<br>用于定位 | 03 概念设计<br>六环与五环之间<br>12.1 km² / 2.1 km² / 6.5 ha<br>可正式引用 | 04 待正式补充<br>官方polygon与实地不符<br>官方数据 / 实地数据不符<br>不可正式引用 |
|----------------------------------------------------------------|-------------------------------------------------------|------------------------------------------------------------|-------------------------------------------------------|

官方边界到位后的确定性替换链



11.41 km²

临时信息量

192.1 / 104.3 / 72.0 ha

信息量与官方官方数据

4 → 1

官方数据与官方数据

0

官方数据与官方数据


说明：根据polygon数据，提供真实数据，只靠数据，提供，但所有数据与官方文件才能满足。  
概念设计 · 临时边界 · 非官方红线

JING-ZHANG COMMON VERANDA · CONCEPTUAL URBAN DESIGN




午饭走进公园：全线与清华东路西口的双尺度校验

500-600米是一期真实城市门周边的目标服务半径，不是已测步行路线

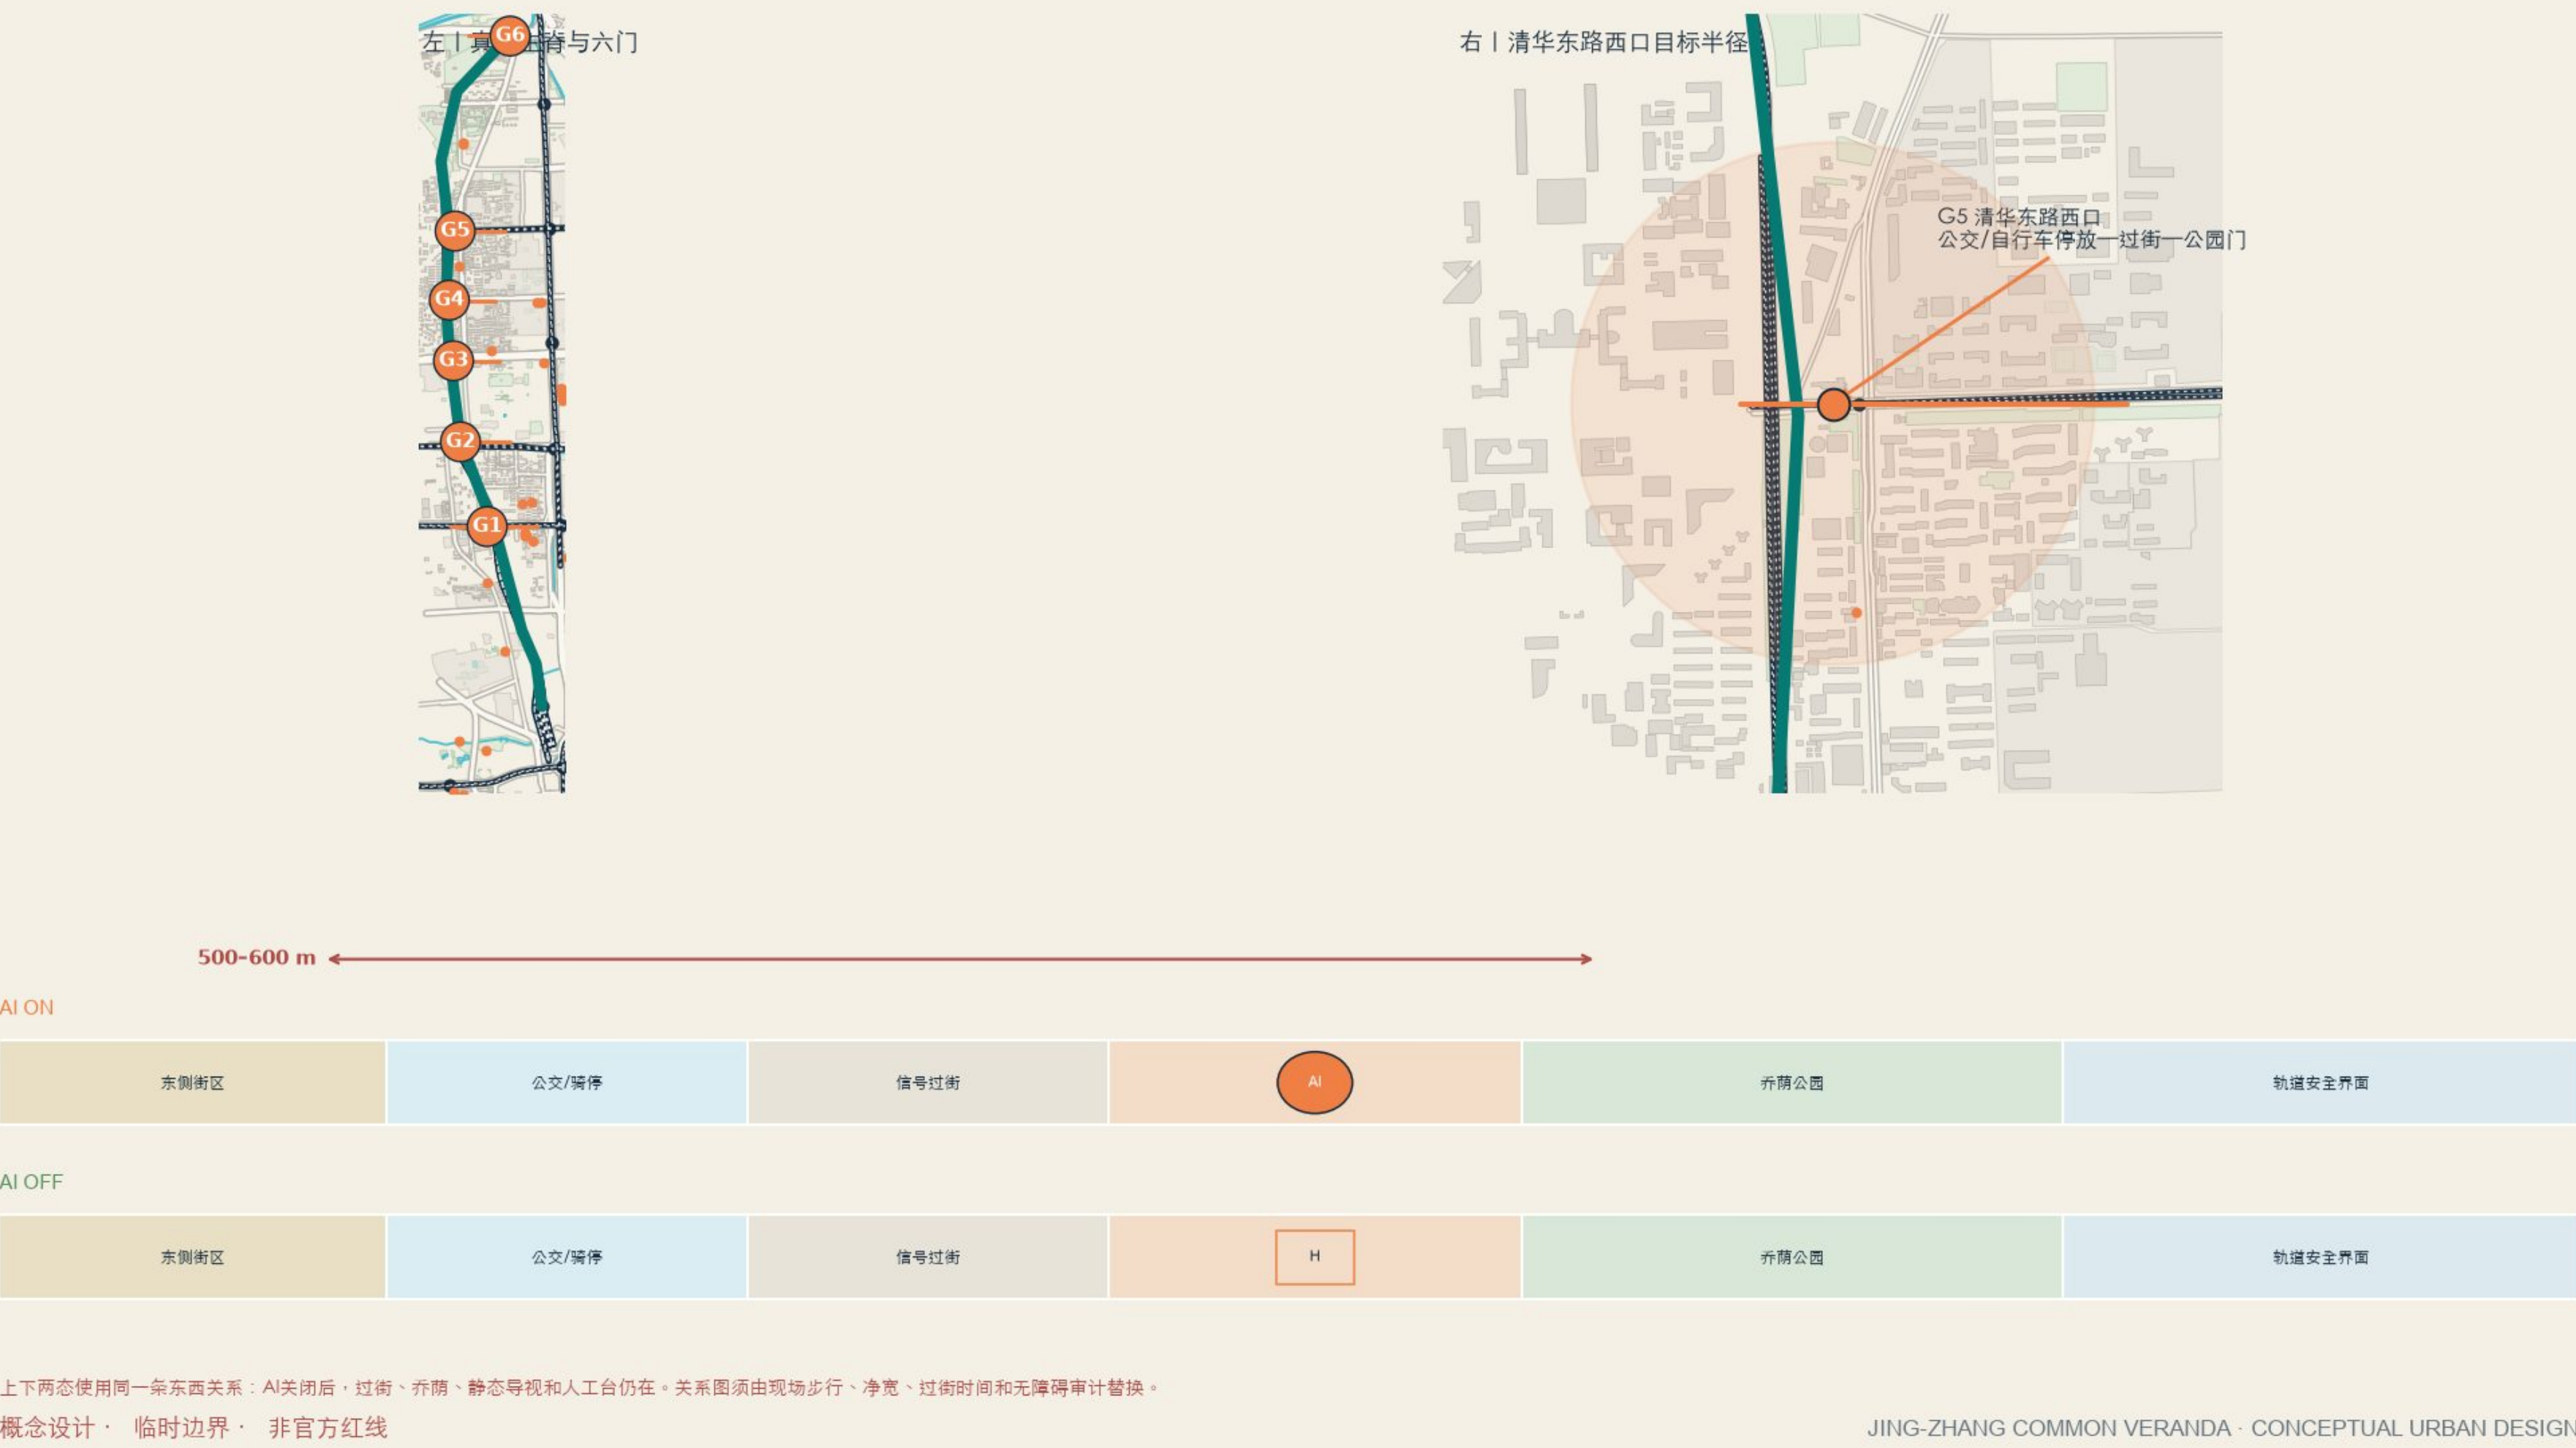


AI 原点学习门廊

五道口—清华东路西口：真实站点、城市道路与一期公园

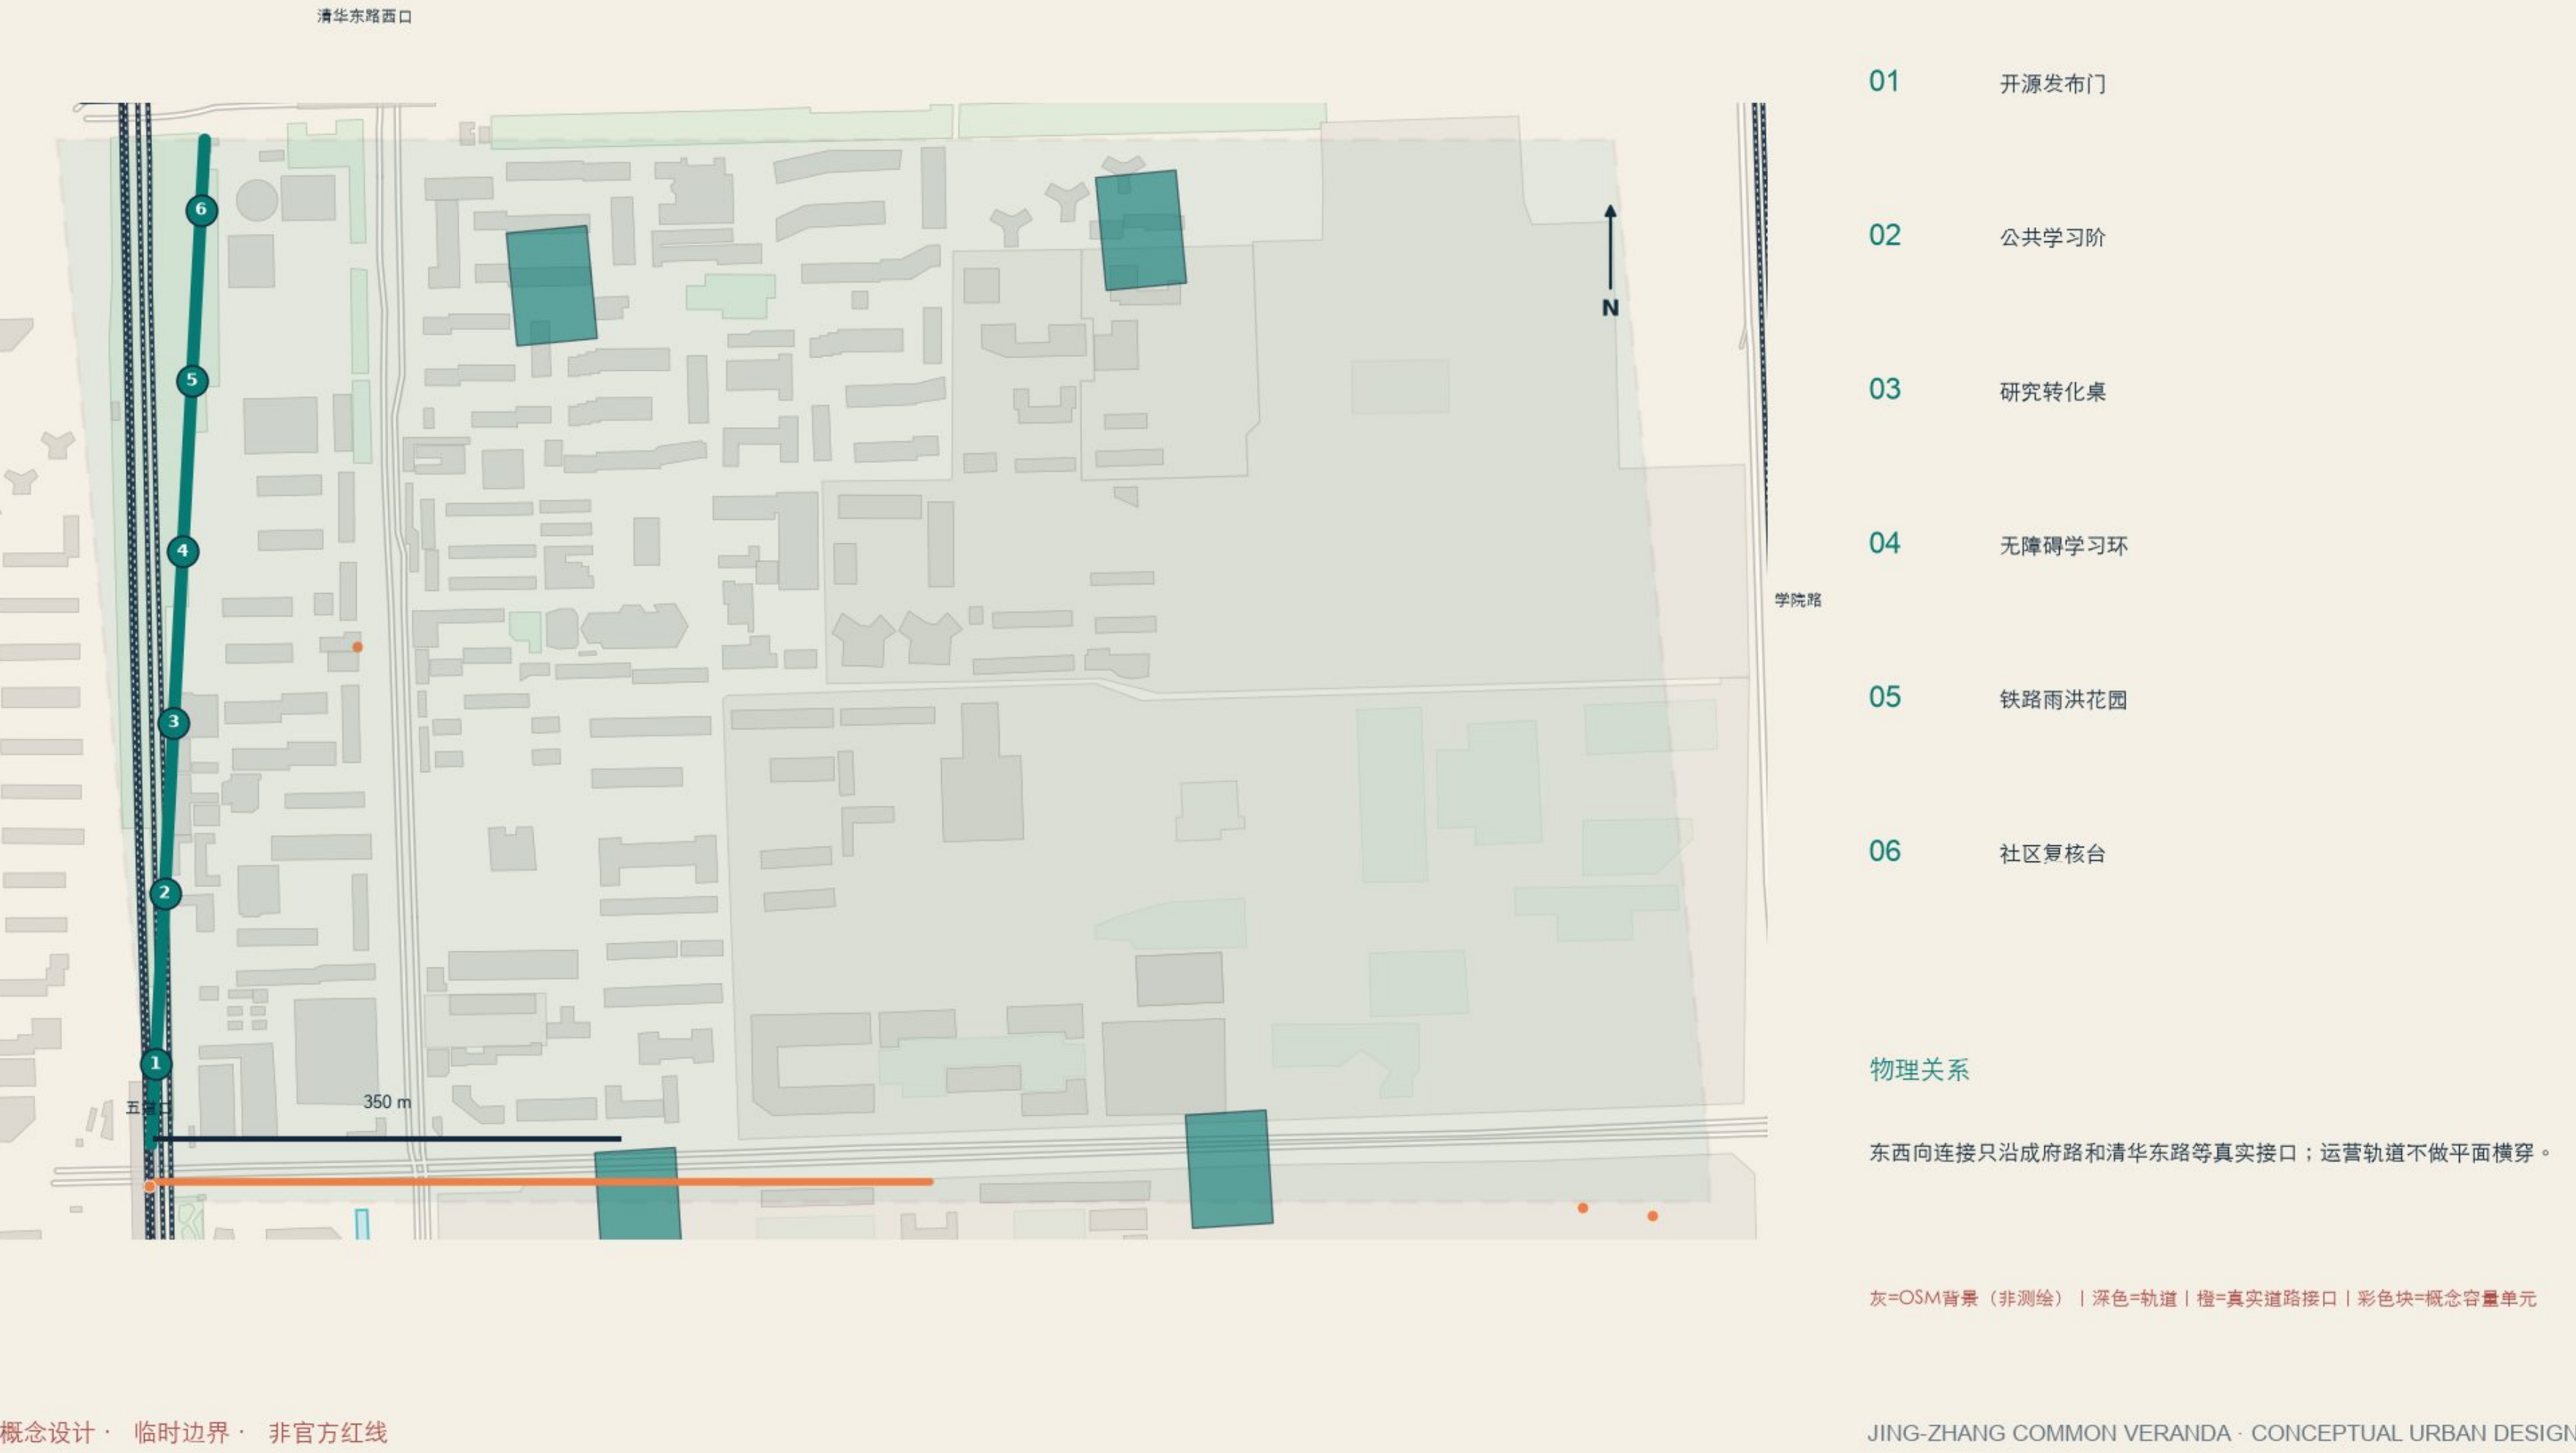


用地与公共底层：真实总体范围上的六段结构

面积和四至来自官方公告；色带是概念功能而非法定用地，AI层不得改变公共底层连续性

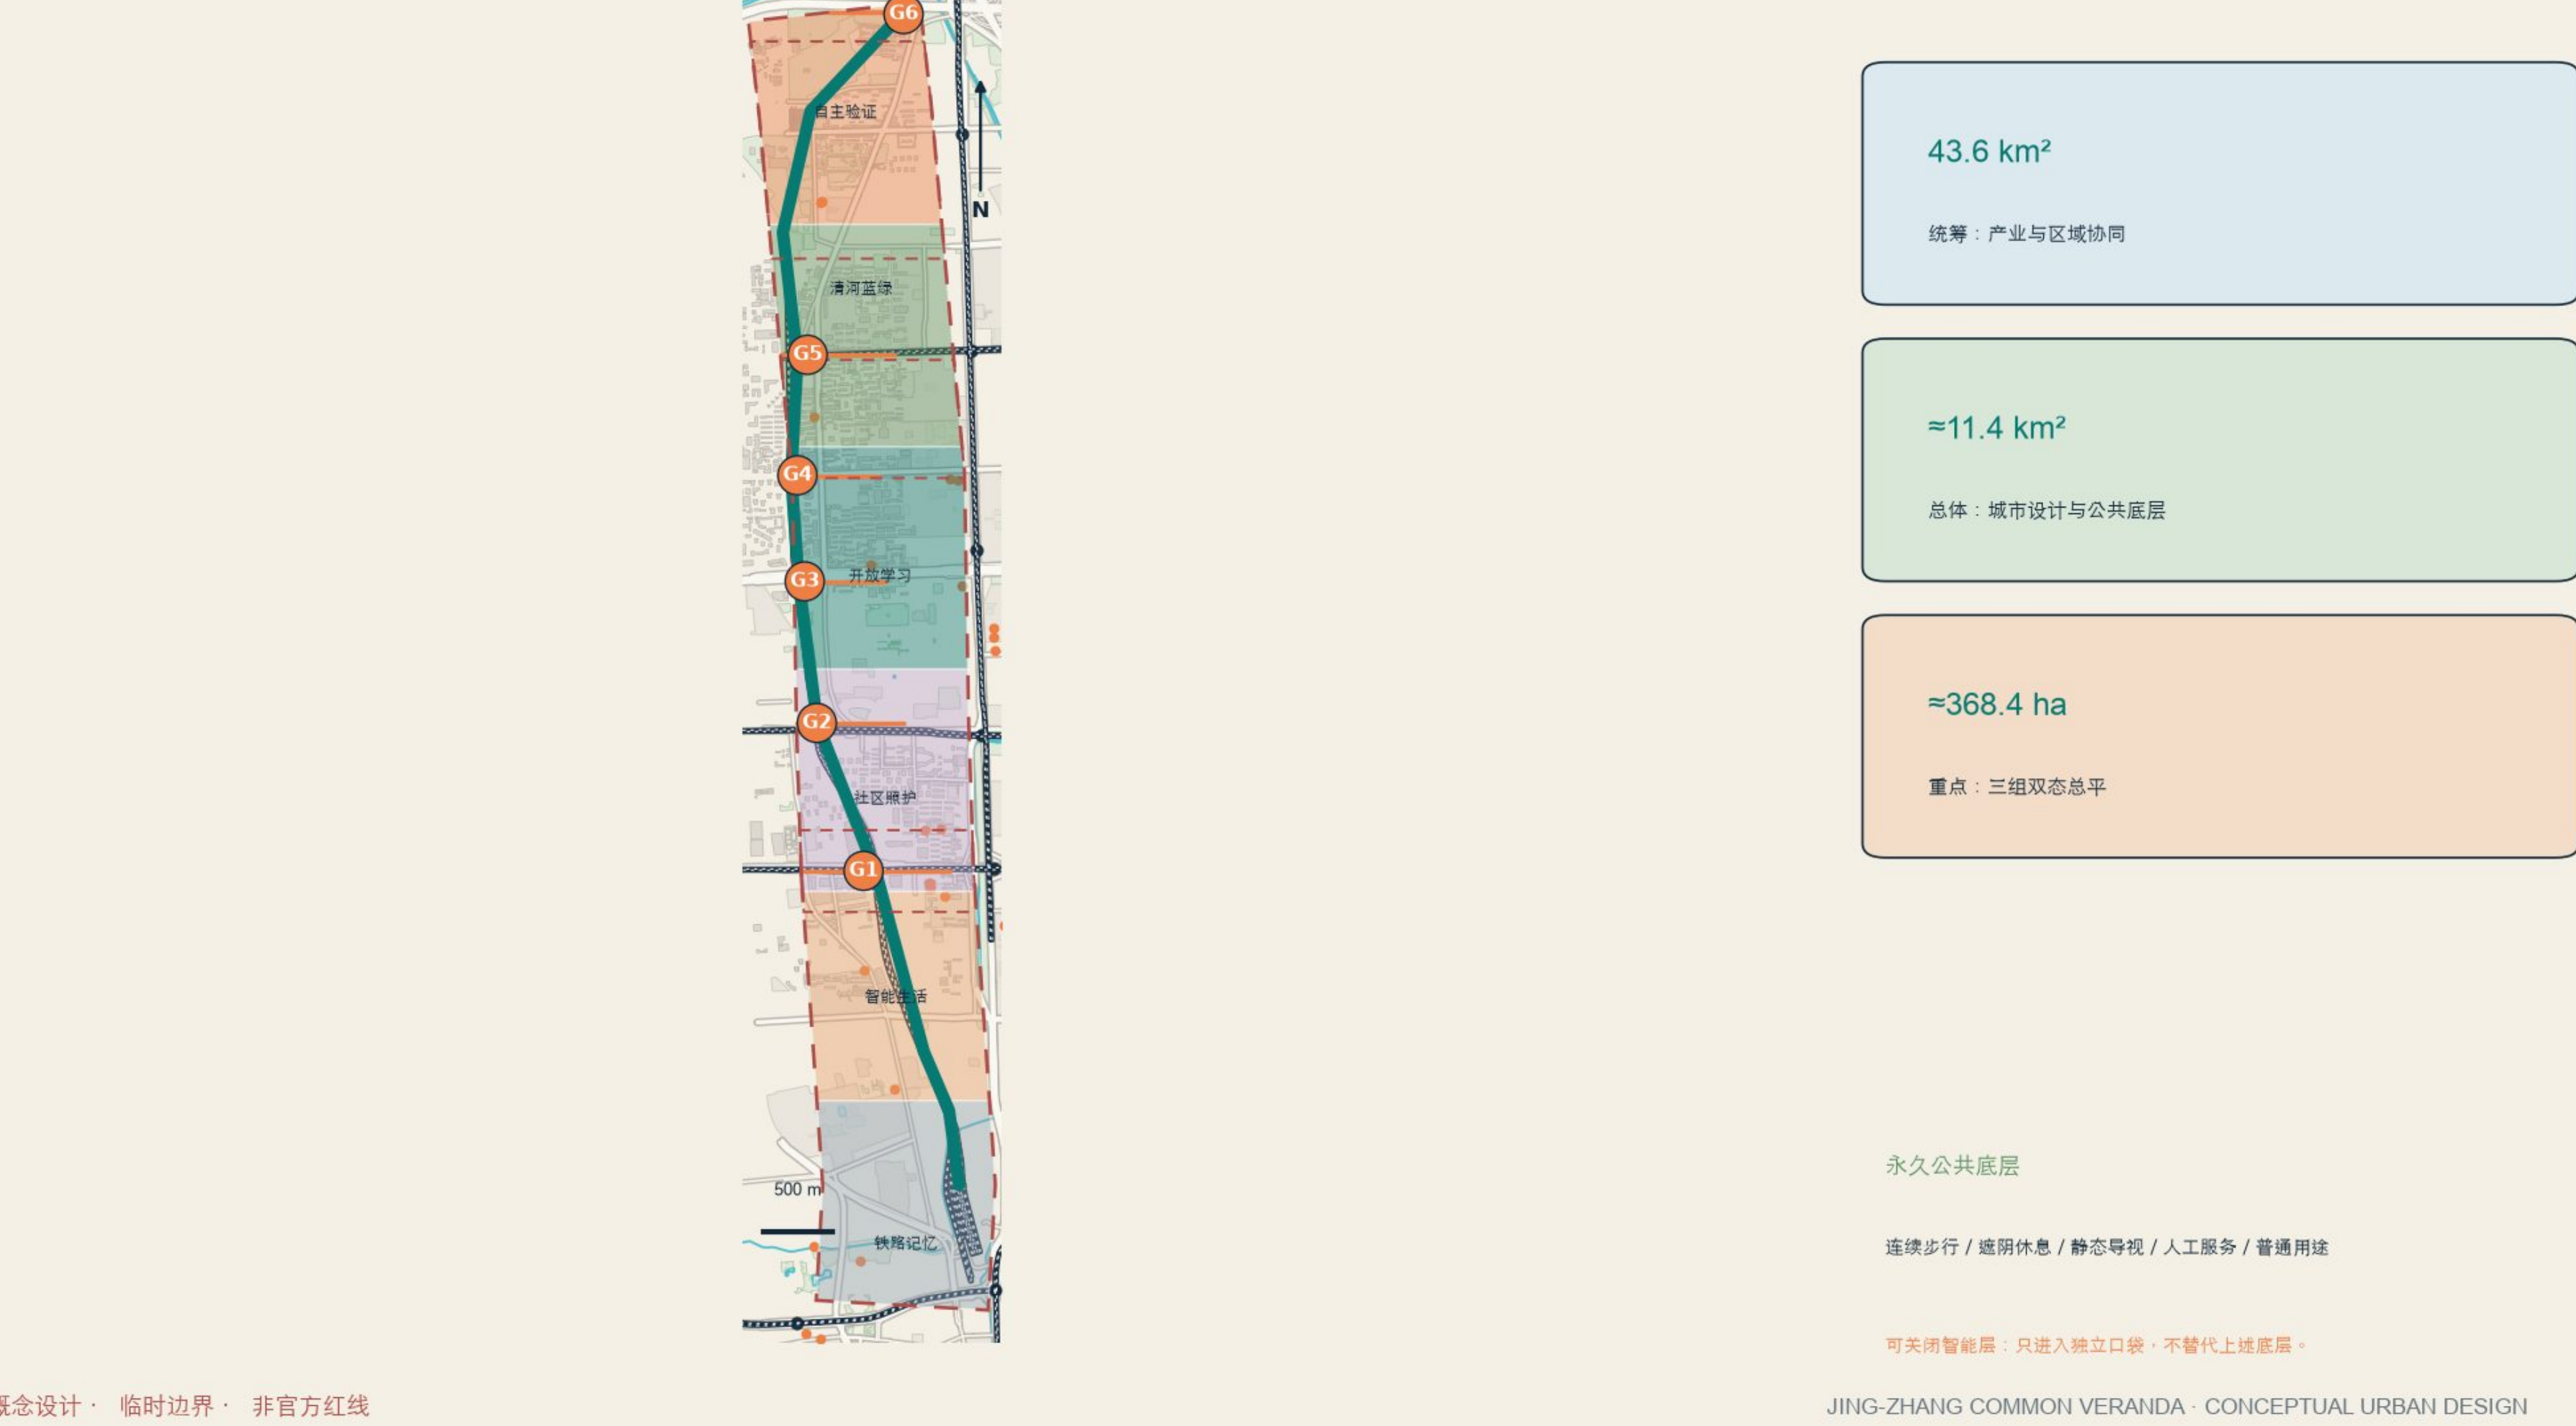

现状建筑背景 ≠ 概念更新容量

OSM建筑只用于定位；22个研究单元只用于容量比较，不是拆建结论

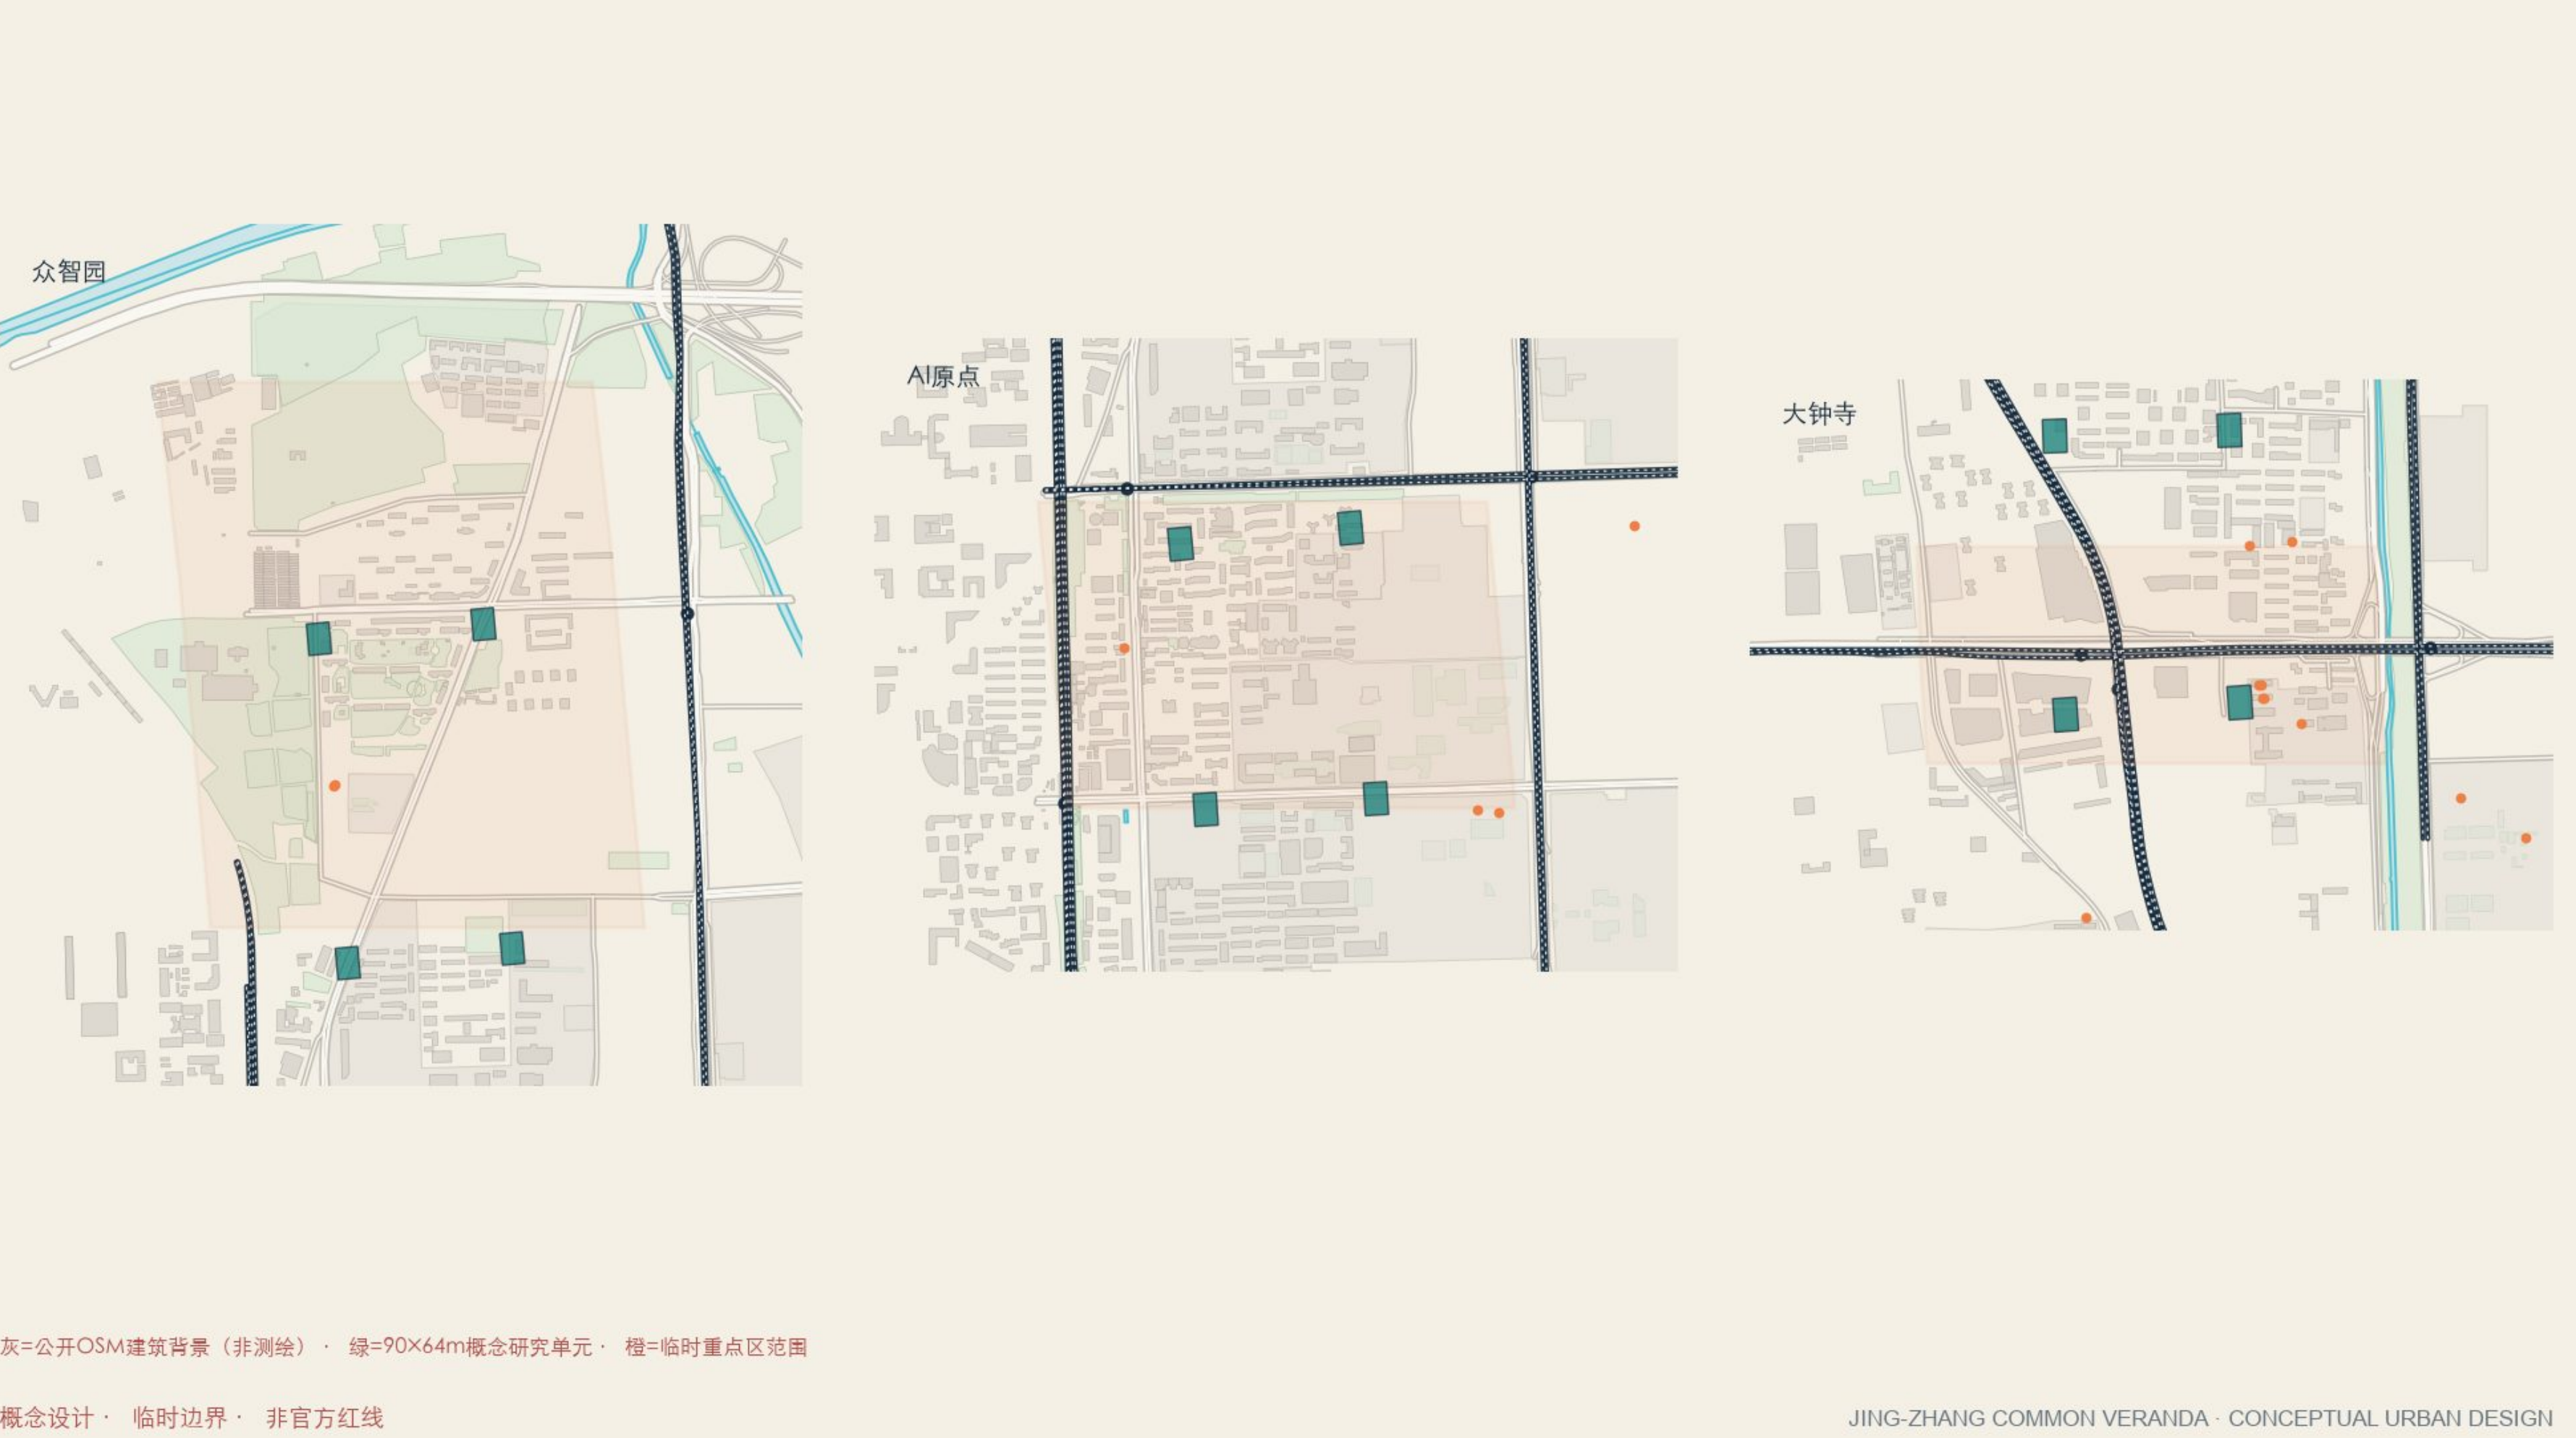



## 真实京张走廊与建设状态

总体设计四至：西直门外大街—北五环；大钟寺东路/荷清路—学院路/西土城路



概念设计 · 临时边界 · 非官方红线

### 01

一期已开放；知春路—清华东路，约2.5公里

### 02

一期已有足球、篮球及跑步设施：先审计，不重复建设

### 03

清华东路南侧公共空间项目已批；本案只补责任与服务层

### 04

二期仍在建；北五环连续性不可提前承诺


### 05

临时边界与重点区仍非官方矢量红线

JING-ZHANG COMMON VERANDA · CONCEPTUAL URBAN DESIGN

## 公共空间剖面：直行、活动与轨道安全互不打架

概念模块只表示关系与优先级；具体净宽、树木、市政、消防和轨道条件须现场复核

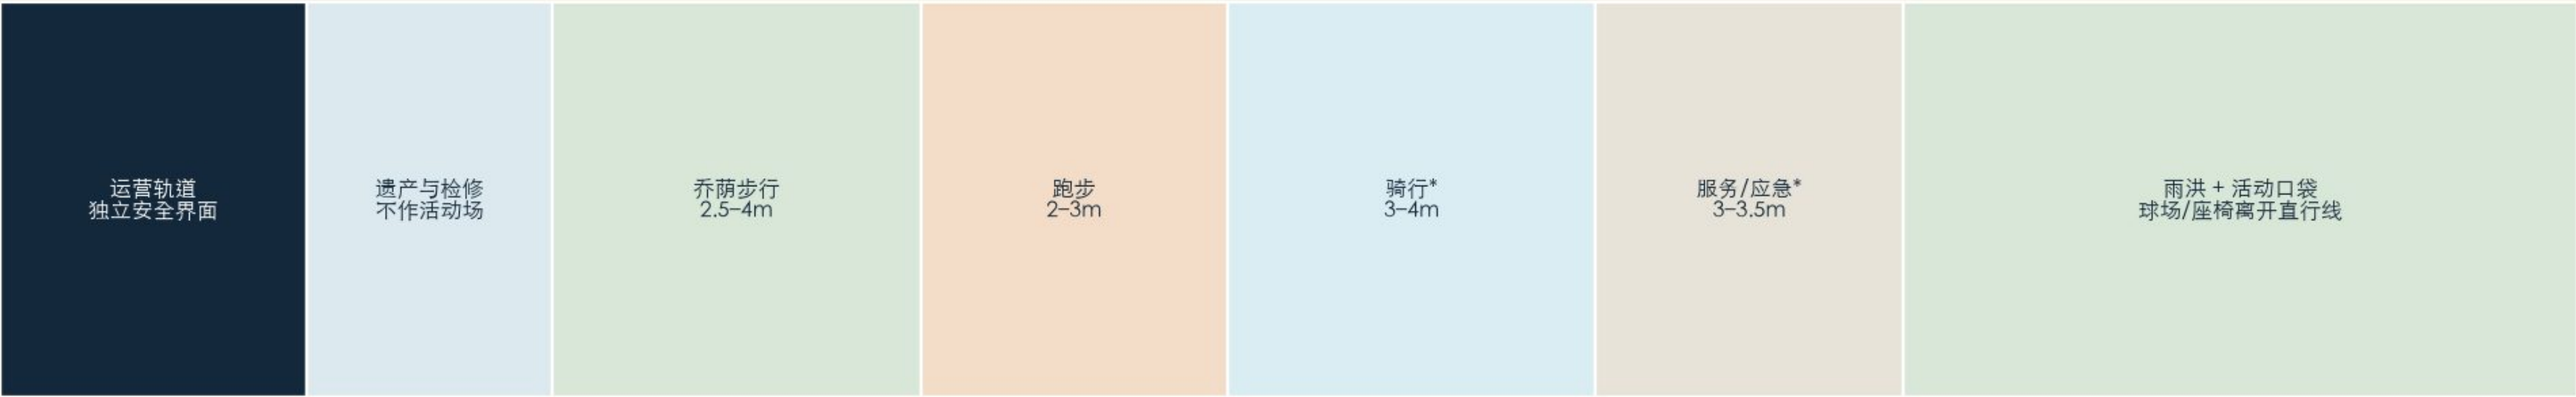

概念设计 · 临时边界 · 非官方红线

JING-ZHANG COMMON VERANDA · CONCEPTUAL URBAN DESIGN

## 人、车、轨道：不靠一条路解决所有问题

走、跑、骑、服务车与轨道按风险和速度分层；宽度不足时骑行绕行城市道路



### ACTIVE RAIL

运营轨道：独立安全界面，禁止平面横穿

### HERITAGE

遗产带：安静解释、检修可达

### WALK

步行：连续无障碍、遮阴、休息

### RUN


跑步：仅在宽段独立；窄段降速并线

### CYCLE

骑行：宽段分流；窄段转城市道路

### SERVICE

服务/应急：限时、限速、步行优先

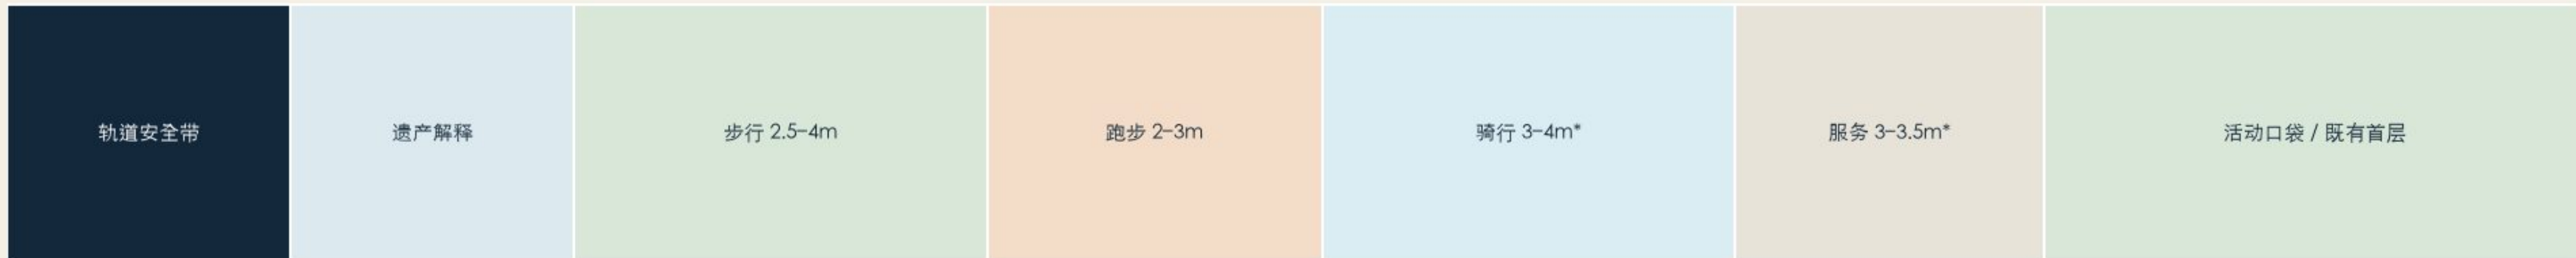

\* 不是全线必设：现场净宽不足时骑行转城市道路；服务车只在维护时靠进入。球场、座椅和排队均放在直行带外。  
概念设计 · 临时边界 · 非官方红线

JING-ZHANG COMMON VERANDA · CONCEPTUAL URBAN DESIGN

## 蓝绿公共空间：一条可遮阴、可滞蓄、可停留的遗产廊道

低技术基础层在断电时仍可使用，智能设施作为独立可关闭的服务层



### 01

树冠：连续遮阴与热环境缓冲

### 02

雨洪：下凹绿地、透水铺装与可见水循环

### 03

停留：座椅、饮水、卫生间与照护接口


### 04

智能：端侧感知、能源计量和人工关闭

概念设计 · 临时边界 · 非官方红线

JING-ZHANG COMMON VERANDA · CONCEPTUAL URBAN DESIGN



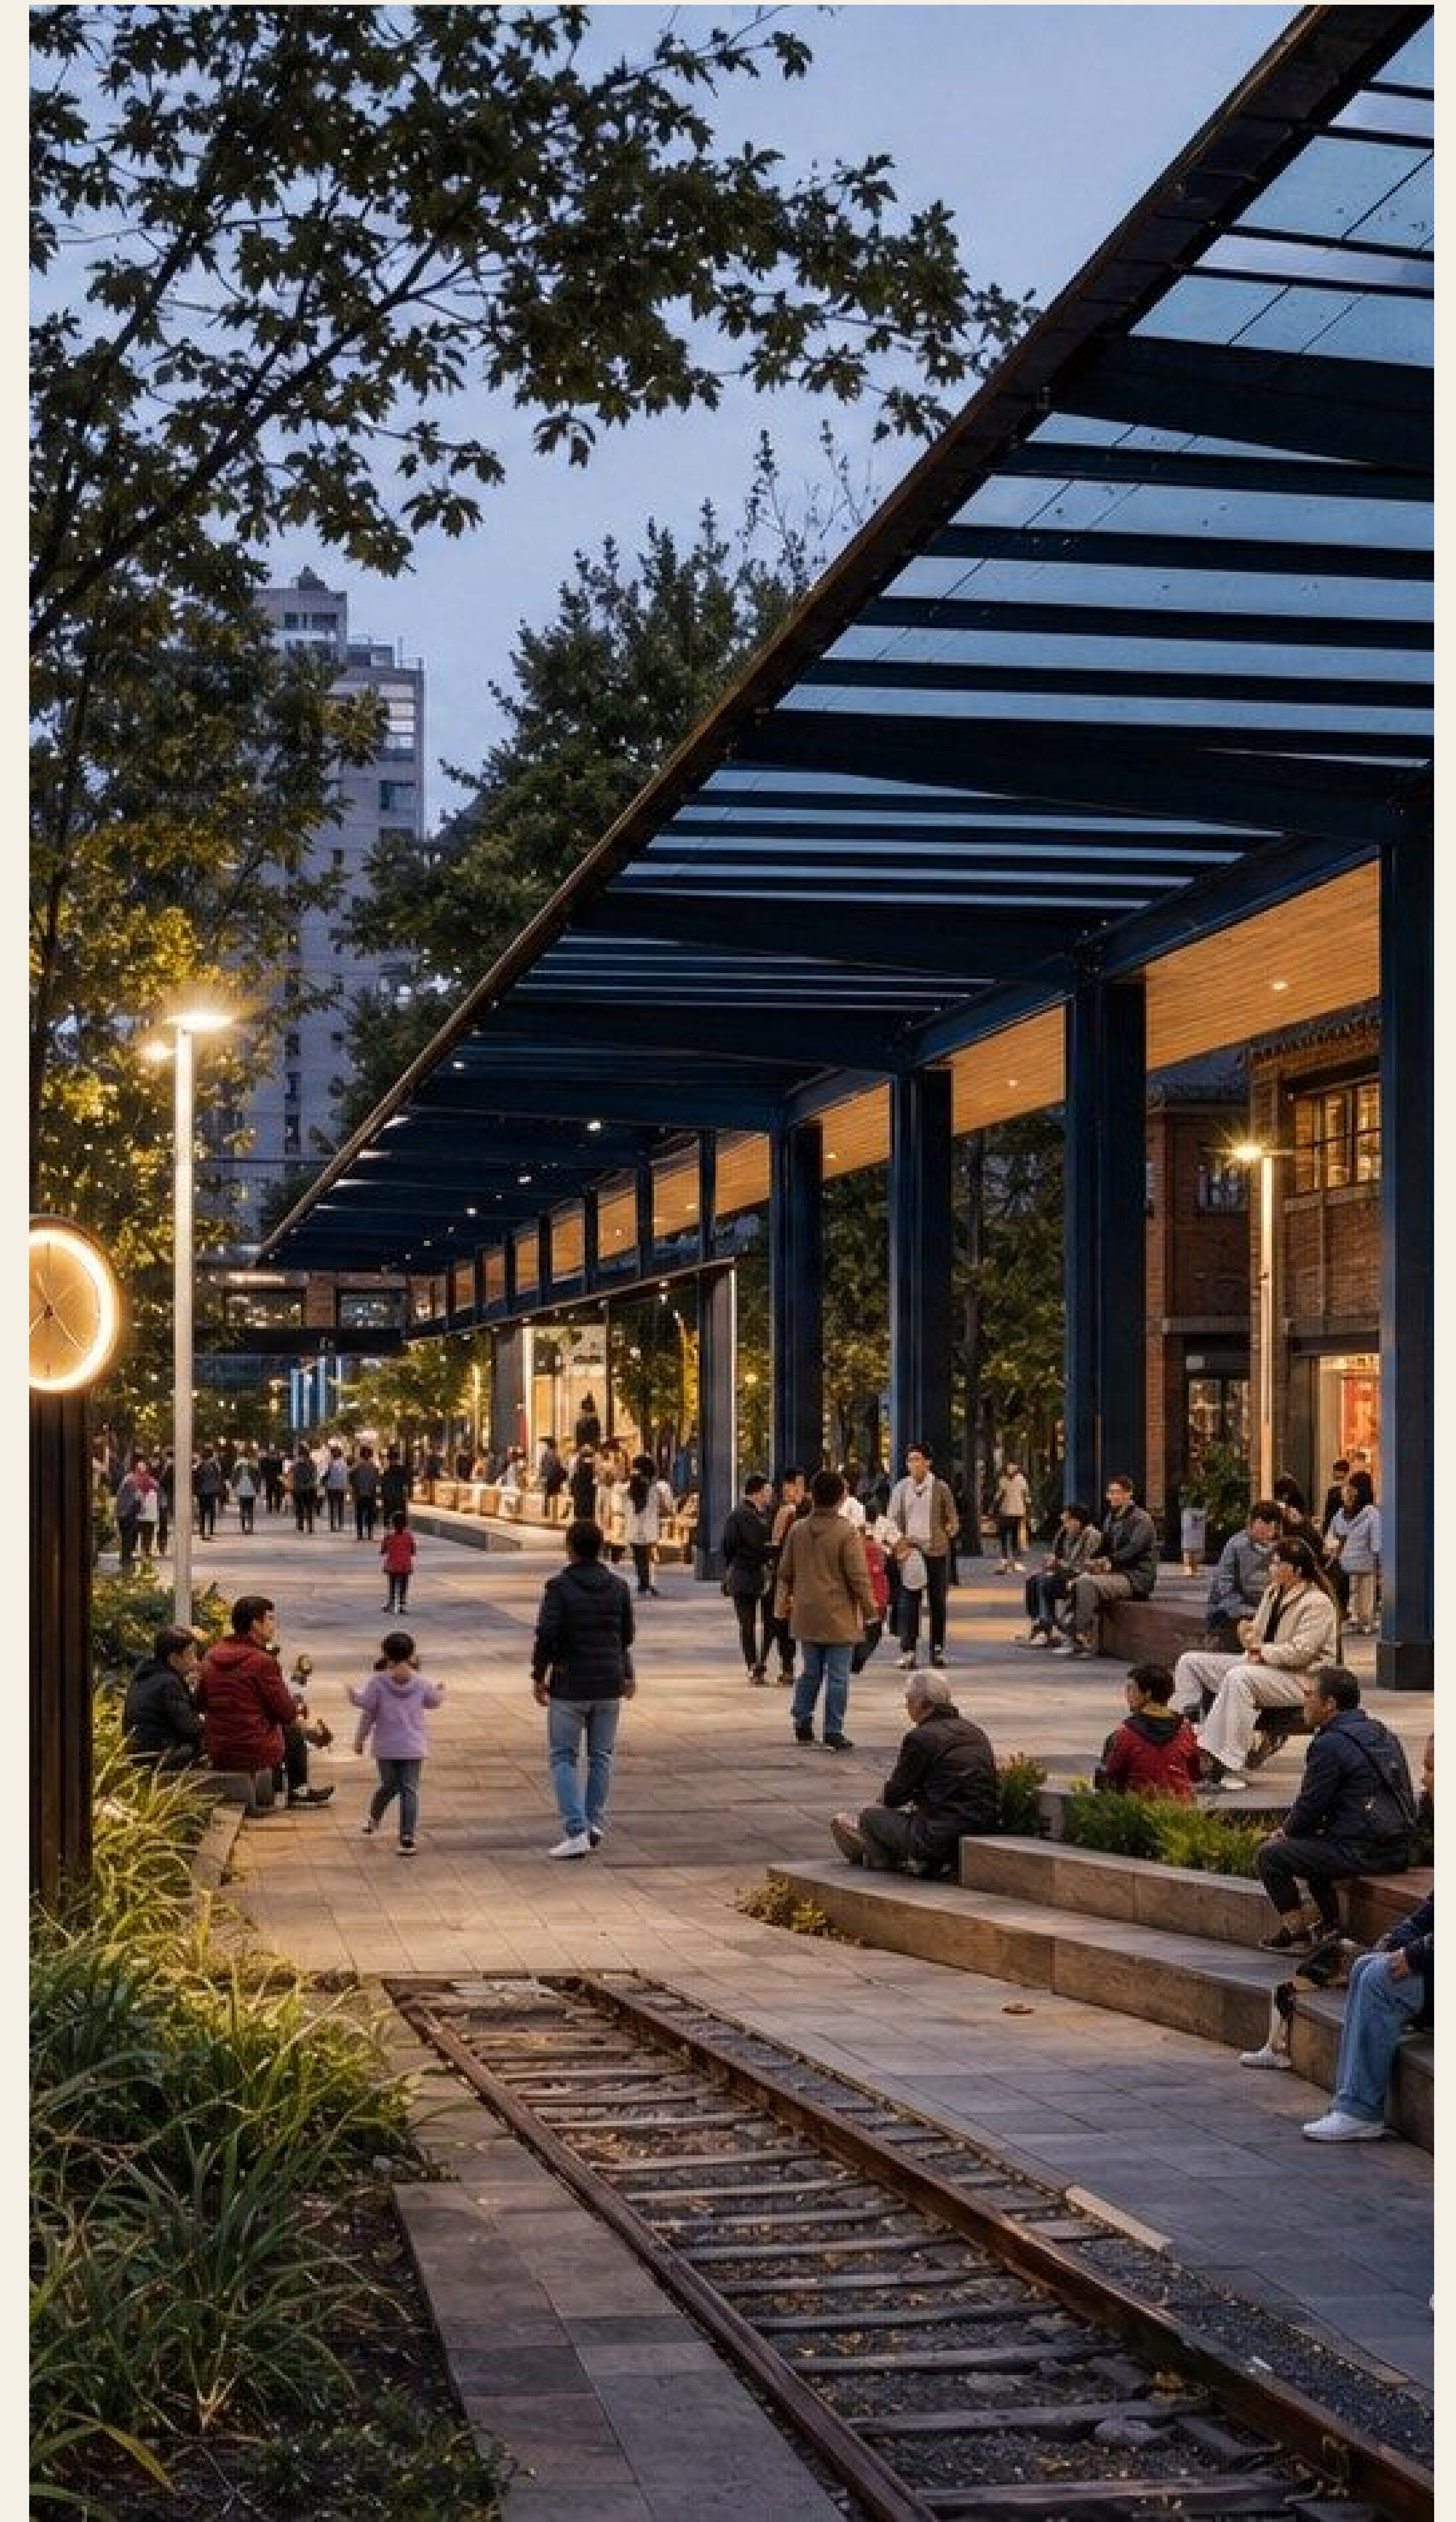



## 十二个可感知场景：空间—数据—人工—退出四联表

场景不是功能清单，而是一组有空间、有责任人、有停机条件的公共服务契约




概念设计 · 临时边界 · 非官方红线

JING-ZHANG COMMON VERANDA · CONCEPTUAL URBAN DESIGN

## 文化与识别：从工程自强到开放责任

品牌不是装饰，而是一套让城市空间和 AI 服务可读的公共语法

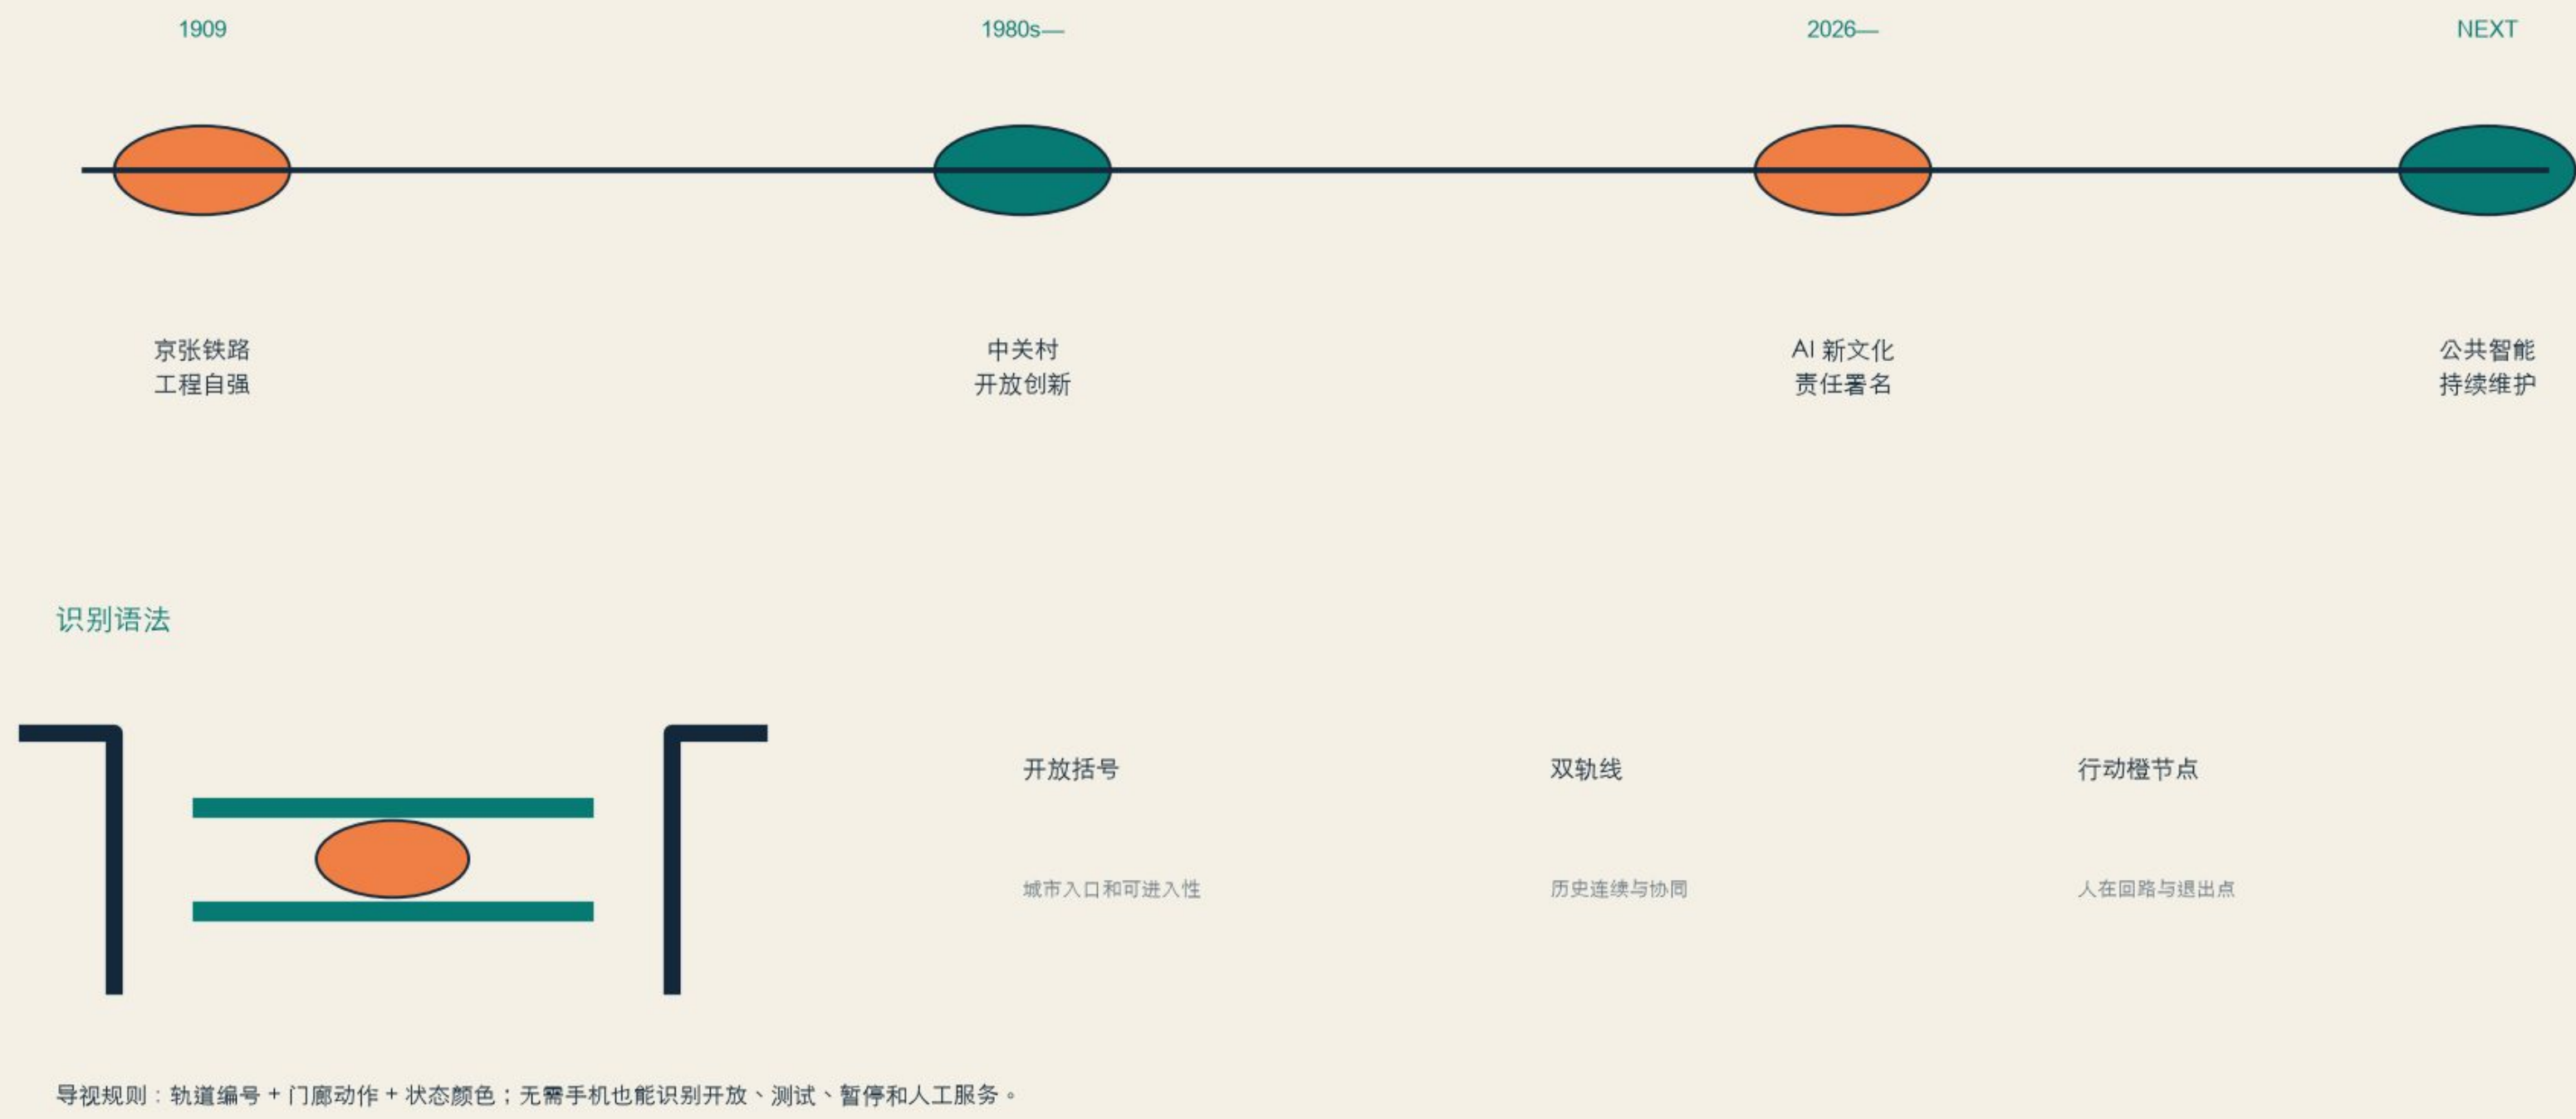


概念设计 · 临时边界 · 非官方红线

JING-ZHANG COMMON VERANDA · CONCEPTUAL URBAN DESIGN

## AI 创新生态：研究—测试—采用—公共回报闭环

产业服务不只服务企业，也必须形成可见、可核验的城市公共收益

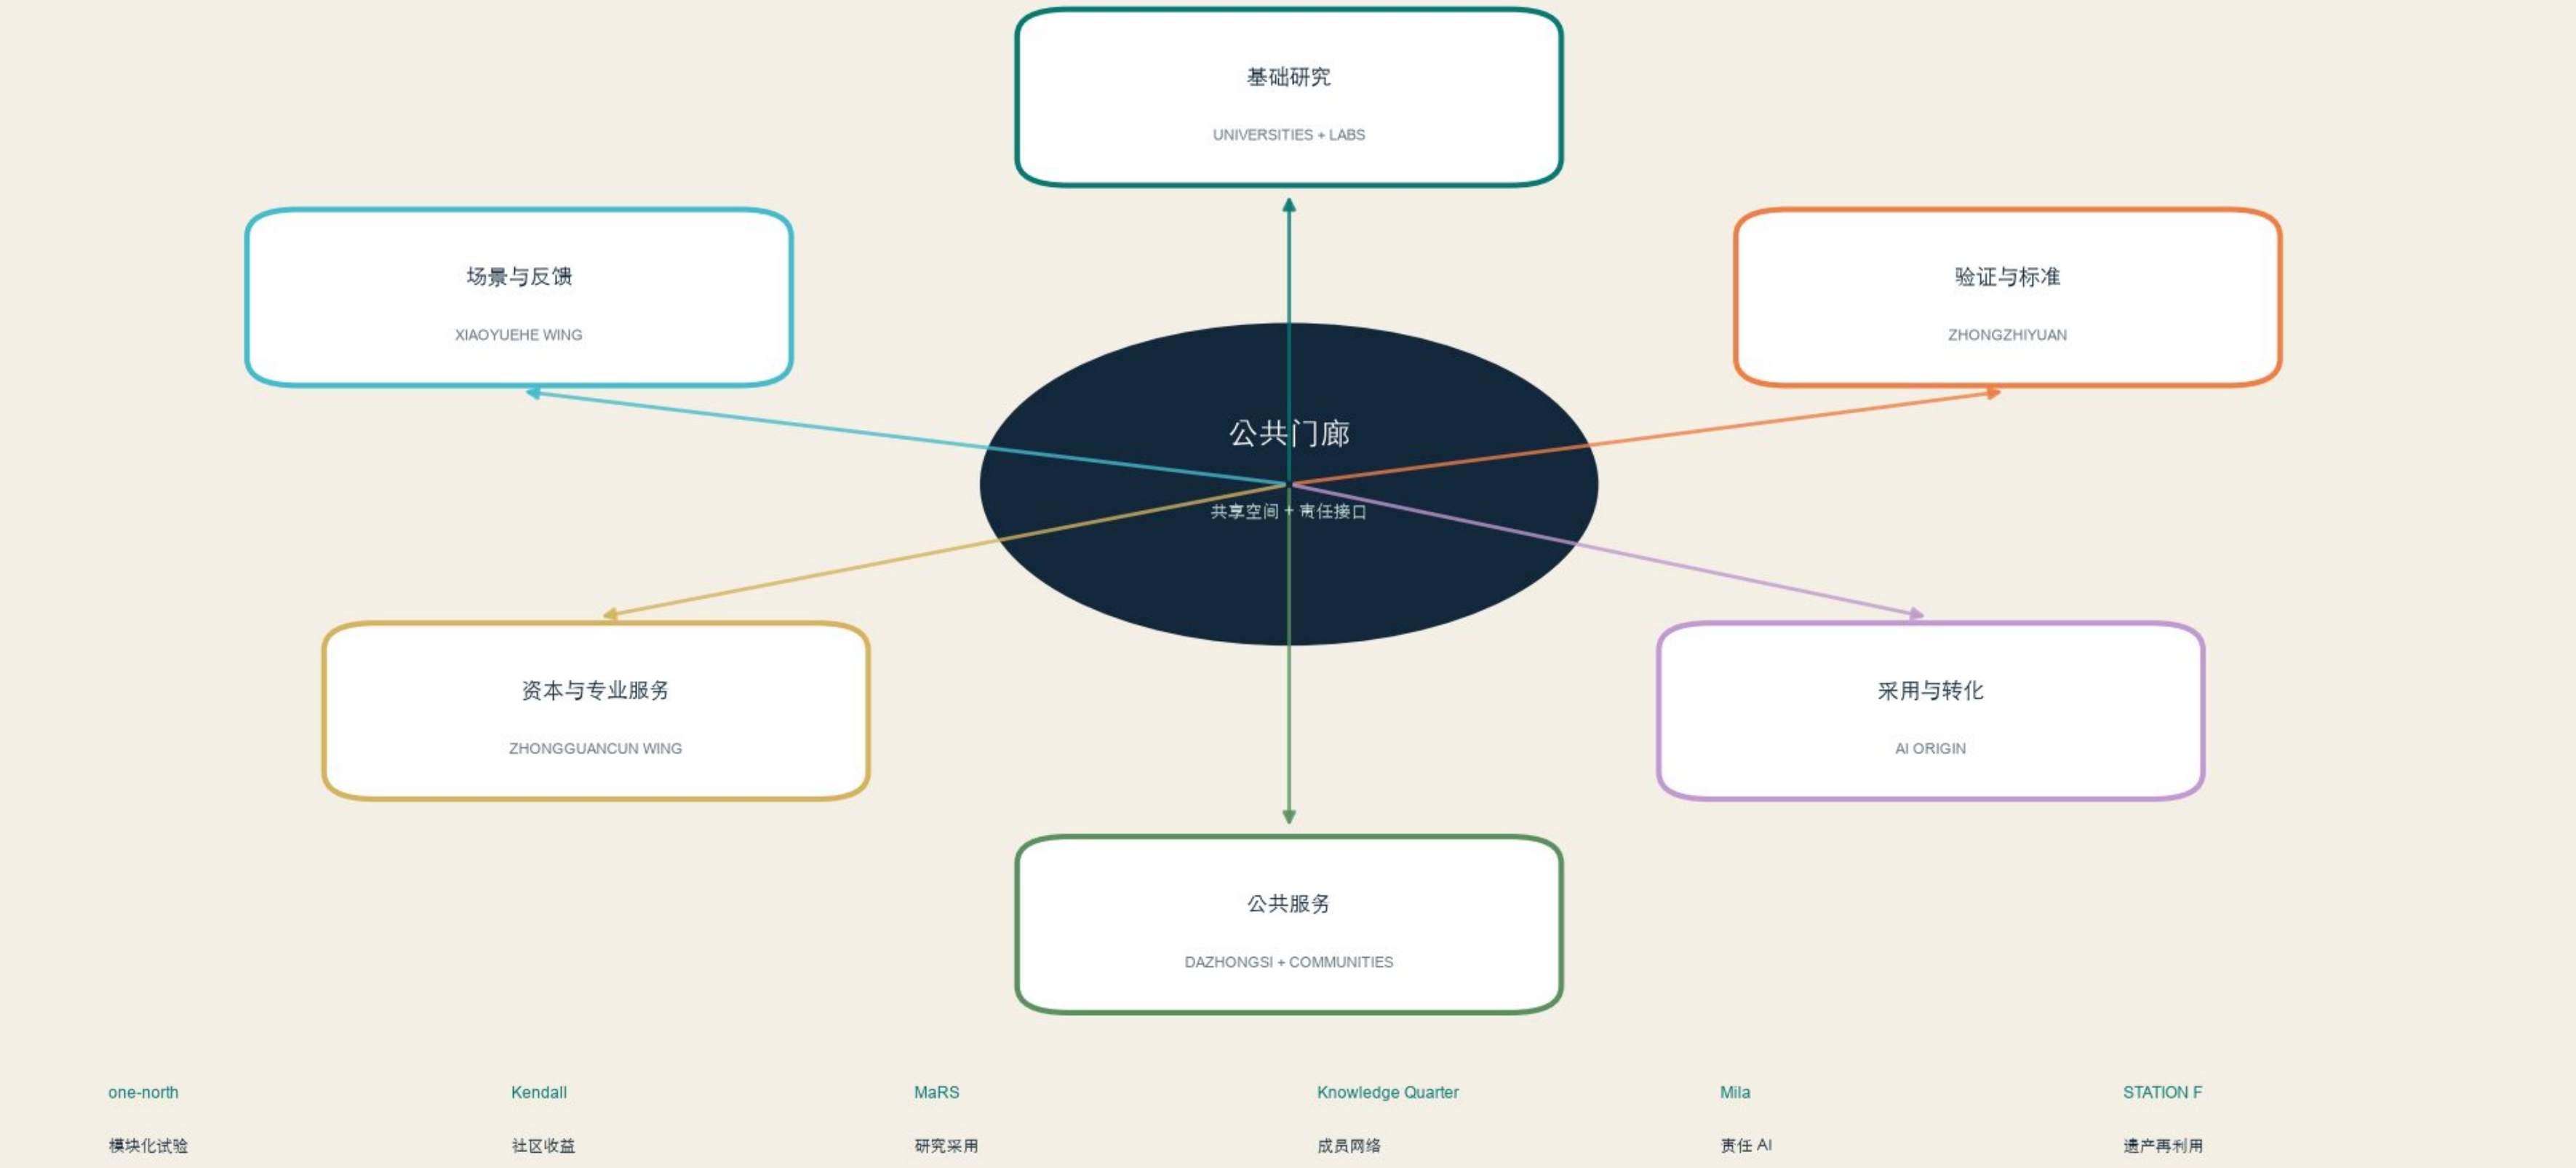

概念设计 · 临时边界 · 非官方红线

JING-ZHANG COMMON VERANDA · CONCEPTUAL URBAN DESIGN

## 门廊回执：一个可暂停的90天公共试验

只验证结构、停止与退出逻辑；尚未获批、未在现场运行



概念设计 · 临时边界 · 非官方红线

JING-ZHANG COMMON VERANDA · CONCEPTUAL URBAN DESIGN



## 可行性结论：先做公共基线，再做可逆试点

成熟度不是效果评分：它只表示当前证据离现场决策还有多远

| 现在 / NOW | 0—6个月                          | 6—18个月                        | 取得官方资料后                                    |
|----------|--------------------------------|-------------------------------|--------------------------------------------|
| 方案与桌面证据  | 现场审计与公共基线                      | 一处90天可逆试点                     | 永久工程与跨线连接                                  |
| 01       | 既有公共空间与六门现场审计<br>可立即启动         | 责任：城市更新牵头+无障碍共审<br>相对成本：S     | 前提：场地授权、现场测量<br>闸门：形成问题/权利/安全清单            |
| 02       | 遮阴、座椅、导视与人工服务基线<br>有条件可行       | 责任：场地运营+公共空间专业<br>相对成本：S—M    | 前提：消防、市政、维护窗口<br>闸门：无维护责任则不开工              |
| 03       | 门廊回执90天桌面到现场试点<br>桌面可行 / 现场待授权 | 责任：试点发起者+现场管家+数据/IP<br>相对成本：M | 前提：G0—G6全部签署<br>闸门：任一闸门失败即转人工并回滚           |
| 04       | 跨铁路、桥梁与永久建筑工程<br>当前不可实施        | 责任：主管部门+权利人+多专业总师<br>相对成本：L   | 前提：官方红线/GIS、权属、勘察、审批<br>闸门：资料未齐保持概念，不出工程结论 |

底线：没有官方几何、权属、勘察和专业审批，不把概念图变成施工图；没有运营、人工替代和退出资金，不开启智能层。

概念设计 · 临时边界 · 非官方红线

JING-ZHANG COMMON VERANDA · CONCEPTUAL URBAN DESIGN

## 十二个工程包：空间动作必须带着责任和退出

S/M/L为相对成本档，不是投资估算；真实金额等待工程量、权属和专业设计

| 众智园 · 实验                   | AI原点 · 学习                   | 大钟寺 · 生活                  |
|----------------------------|-----------------------------|---------------------------|
| 4个可交接工程包                   | 4个可交接工程包                    | 4个可交接工程包                  |
| 01<br>测试申请与解释厅   M   G0-G3 | 05<br>开源发布门   S   G2-G3     | 09<br>轨道到达客厅   L   G1-G5  |
| 02<br>低缝机器人沙盘   L   G1-G4  | 06<br>门廊回执90天试验   M   G0-G6 | 10<br>责任零售柜台   M   G2-G6  |
| 03<br>红队评测庭院   M   G2-G6   | 07<br>公共学习阶   S   G1-G5     | 11<br>长者服务导航   M   G1-G6  |
| 04<br>能源安全审计亭   S   G3-G6  | 08<br>无障碍学习环   M   G1-G6    | 12<br>百年公共账本钟   S   G3-G6 |

每包必须补齐：牵头角色 · 专业依赖 · 相对成本 · 维护窗口 · 验收门槛 · 停止/撤除条件 · P1/P2/P3窗口

概念设计 · 临时边界 · 非官方红线

JING-ZHANG COMMON VERANDA · CONCEPTUAL URBAN DESIGN

## 实施与运营：先建立公共基线，再接入智能服务

每一期都设置进入条件、公开证据、责任主体和回退门槛



概念设计 · 临时边界 · 非官方红线

JING-ZHANG COMMON VERANDA · CONCEPTUAL URBAN DESIGN

## 长期运营：谁维护、谁响应、何时退出

没有维护窗口、人工等价服务和退出资金，智能层就不开启

|                                               |                                                                  |                                                           |                                          |
|-----------------------------------------------|------------------------------------------------------------------|-----------------------------------------------------------|------------------------------------------|
| 每日 / DAILY<br>开放、无障碍、告知、人工、事件                 | 每月 / MONTHLY<br>维护者会客厅、未结修复、异议                                   | 每季 / QUARTERLY<br>公开运行/暂停/申诉/修复回执                         | 每年 / ANNUAL<br>Open Veranda Week、资产与许可审计 |
| 资金前置<br>运营责任人<br>维护与备件窗口<br>人工服务排班<br>保险与退出资金 | 公共账本<br>OPEN / TEST / PAUSED状态<br>投诉与申诉<br>修复与复核<br>继续 / 修改 / 退役 | 开放品牌治理<br>标识可署名复用<br>状态颜色不得删除<br>AI内容保持显式标识<br>所有变化有日期与版本 |                                          |

季度未能公开责任、核算和退出证据时，相关场景默认进入PAUSED；两季仍未闭环则提交退场决定。

概念设计 · 临时边界 · 非官方红线

JING-ZHANG COMMON VERANDA · CONCEPTUAL URBAN DESIGN



## 六门证据表：不用虚构横跨轨道的捷径

每一门先说现状接口、物理冲突和设计规则

|    |          |                  |                |
|----|----------|------------------|----------------|
| G1 | 大钟寺      | 站点四象限：停车、换乘、气口冲突 | 审计现有骑行：不靠平面穿轨  |
| G2 | 知春路      | 一期南端：道路与轨道叠加     | 只用现有或专业论证过街    |
| G3 | 北四环      | 桥下活动与通行混合        | 球场、排队、座椅退出直行带  |
| G4 | 成府路一五道口  | 商业、地铁、骑行高峰       | 步行连接：骑行窄段设城市道路 |
| G5 | 清华东路西口   | 已批公共空间与自行车停放     | 补居住和服务；不重复造景   |
| G6 | 北五环—清河南缘 | 二期在建；开放条件未定      | 施工验收前不承诺连续开放   |

概念设计 · 临时边界 · 非官方红线

JING-ZHANG COMMON VERANDA · CONCEPTUAL URBAN DESIGN

## 证据分级与边界替换：真实背景不冒充官方红线

四条提示只有一个根因：官方精确polygon尚未公开；数据缺口不间断内容评分

|                                                                           |                                                                 |                                                                |                                                                  |
|---------------------------------------------------------------------------|-----------------------------------------------------------------|----------------------------------------------------------------|------------------------------------------------------------------|
| 01<br>官方已知<br><br>文字四象与的面积<br>43.6 km² / 11.4 km² / 368.4 ha<br><br>可正式引用 | 02<br>公开真实背景<br><br>堤岸四轨道四站点四建筑<br>一期已建 / 已批 / 二期在建<br><br>用于定位 | 03<br>概念设计<br><br>六门四三组双态叠平<br>12.1%绿地 / 2.1%公共空间<br><br>可靠算建议 | 04<br>待正式补齐<br><br>官方polygon四现状净宽<br>值守能力 / 关闭恢复时间<br><br>不得冒充已知 |
|---------------------------------------------------------------------------|-----------------------------------------------------------------|----------------------------------------------------------------|------------------------------------------------------------------|

官方边界到位后的确定性替换链

|                            |                            |                               |                           |                                    |                         |
|----------------------------|----------------------------|-------------------------------|---------------------------|------------------------------------|-------------------------|
| 01<br>收件与验收<br><br>来源 / 授权 | 02<br>校验坐标系<br><br>成本 / 精度 | 03<br>替换4个范围<br><br>总修 + 三重分区 | 04<br>重置2类图层<br><br>用地划分图 | 05<br>重置全部交付<br><br>图 / HTML / PDF | 06<br>重置四道门<br><br>边界留痕 |
|----------------------------|----------------------------|-------------------------------|---------------------------|------------------------------------|-------------------------|

11.41 km²

临时范围复算

192.1 / 104.3 / 72.0 ha

三重分区拟合官方约数

4 → 1

四修提示四一个数据修图

0

官方polygon公开数量


结论：保留provisional警示，提升真实证据：只有来源、授权、坐标系可验证的官方文件才能清零。

概念设计 · 临时边界 · 非官方红线

JING-ZHANG COMMON VERANDA · CONCEPTUAL URBAN DESIGN

## 区域协作不是连线，而是可退出的证据接口

每个节点只承诺输入、最低输出、责任类型与停止条件

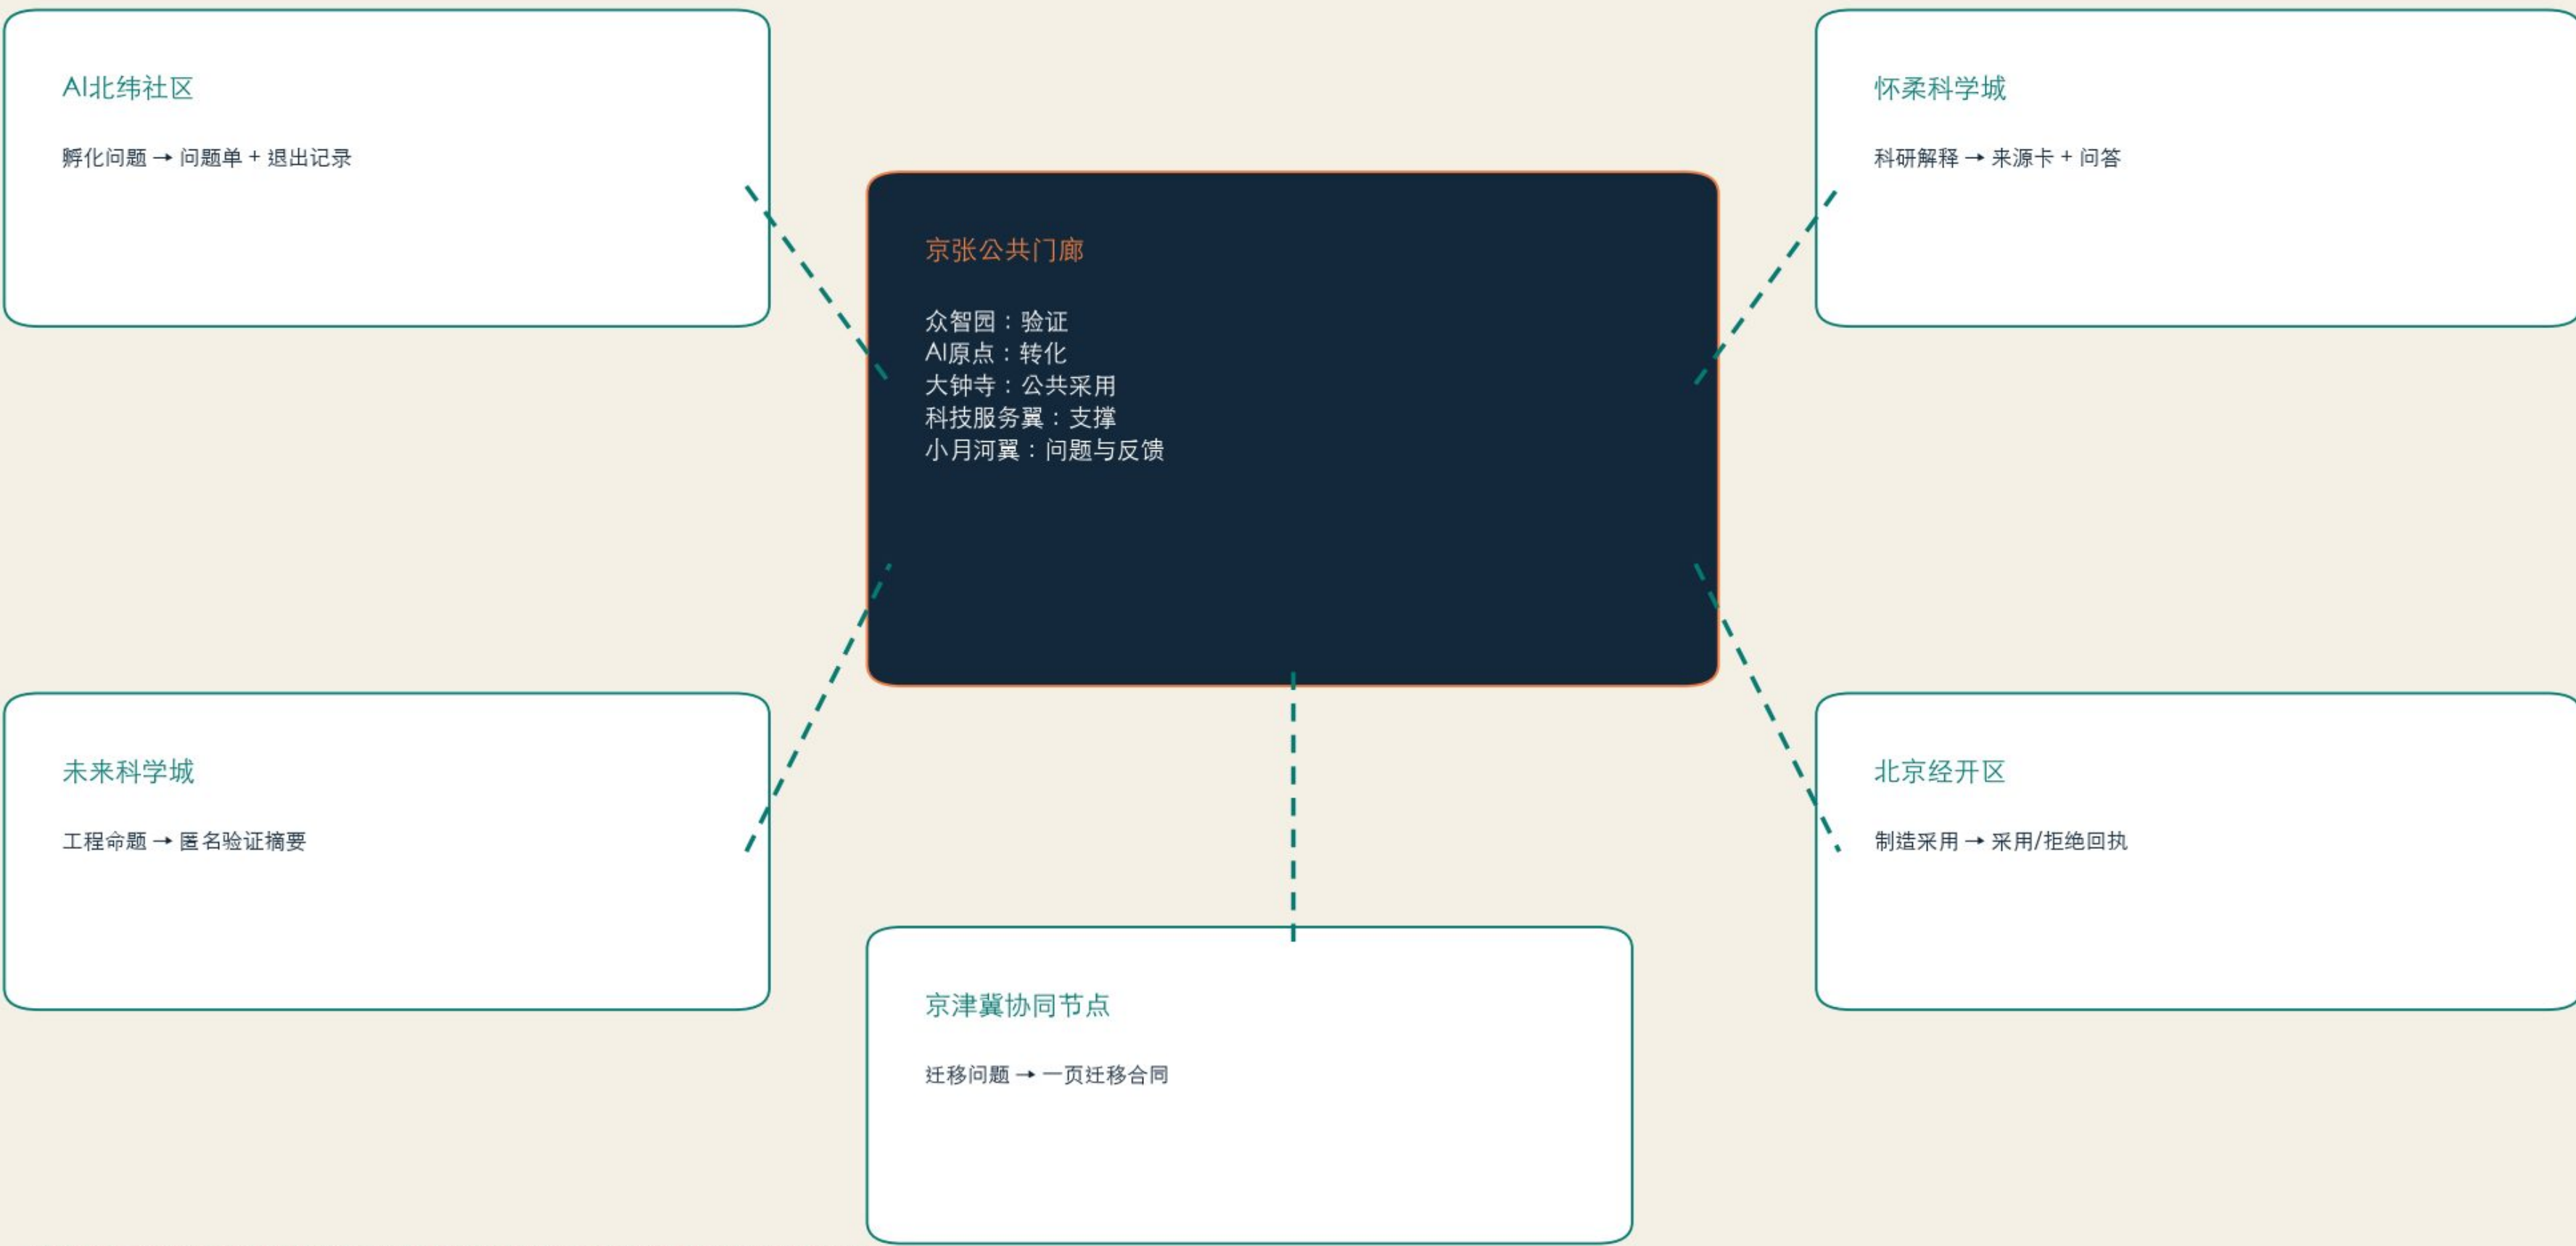

共同隔门：未确认接口人则不代表合作；涉及真实数据、设施、商业秘密或准入时必须另行授权。

概念设计 · 临时边界 · 非官方红线

JING-ZHANG COMMON VERANDA · CONCEPTUAL URBAN DESIGN

## 设计结论：一条公共门廊、六个城市门、三层实施证据

现状基线、概念建议与待专业深化内容在图纸中明确分开

|                                           |                                      |                                          |
|-------------------------------------------|--------------------------------------|------------------------------------------|
| 地理<br><br>公共主脊连接北京北、大钟寺、知春路、五道口、清华东路与北五环。 | 生活<br><br>午饭步行、过街、遮阴、饮水和人工服务落在真实城市门。 | 分流<br><br>轨道保持安全界面；走、跑、骑与服务车按净宽、风险和速度组织。 |
|-------------------------------------------|--------------------------------------|------------------------------------------|

|                                                  |                                                     |
|--------------------------------------------------|-----------------------------------------------------|
| 几何<br><br>22个概念研究单元约12.7ha；六门公共节点约2.1%；现状背景另行标识。 | 交付<br><br>六门审计可先行；低技术公共基线与一处90天可测试点按授权推进；永久工程待专业审批。 |
|--------------------------------------------------|-----------------------------------------------------|

概念设计 · 临时边界 · 非官方红线

JING-ZHANG COMMON VERANDA · CONCEPTUAL URBAN DESIGN