


枕木长链 SLEEPER CHAIN | 总体概念与空间结构


一链 · 两轨 · 三站 · 两场 | 百年京张文化带 × 都市AI生活体验带 × AI融合创新带

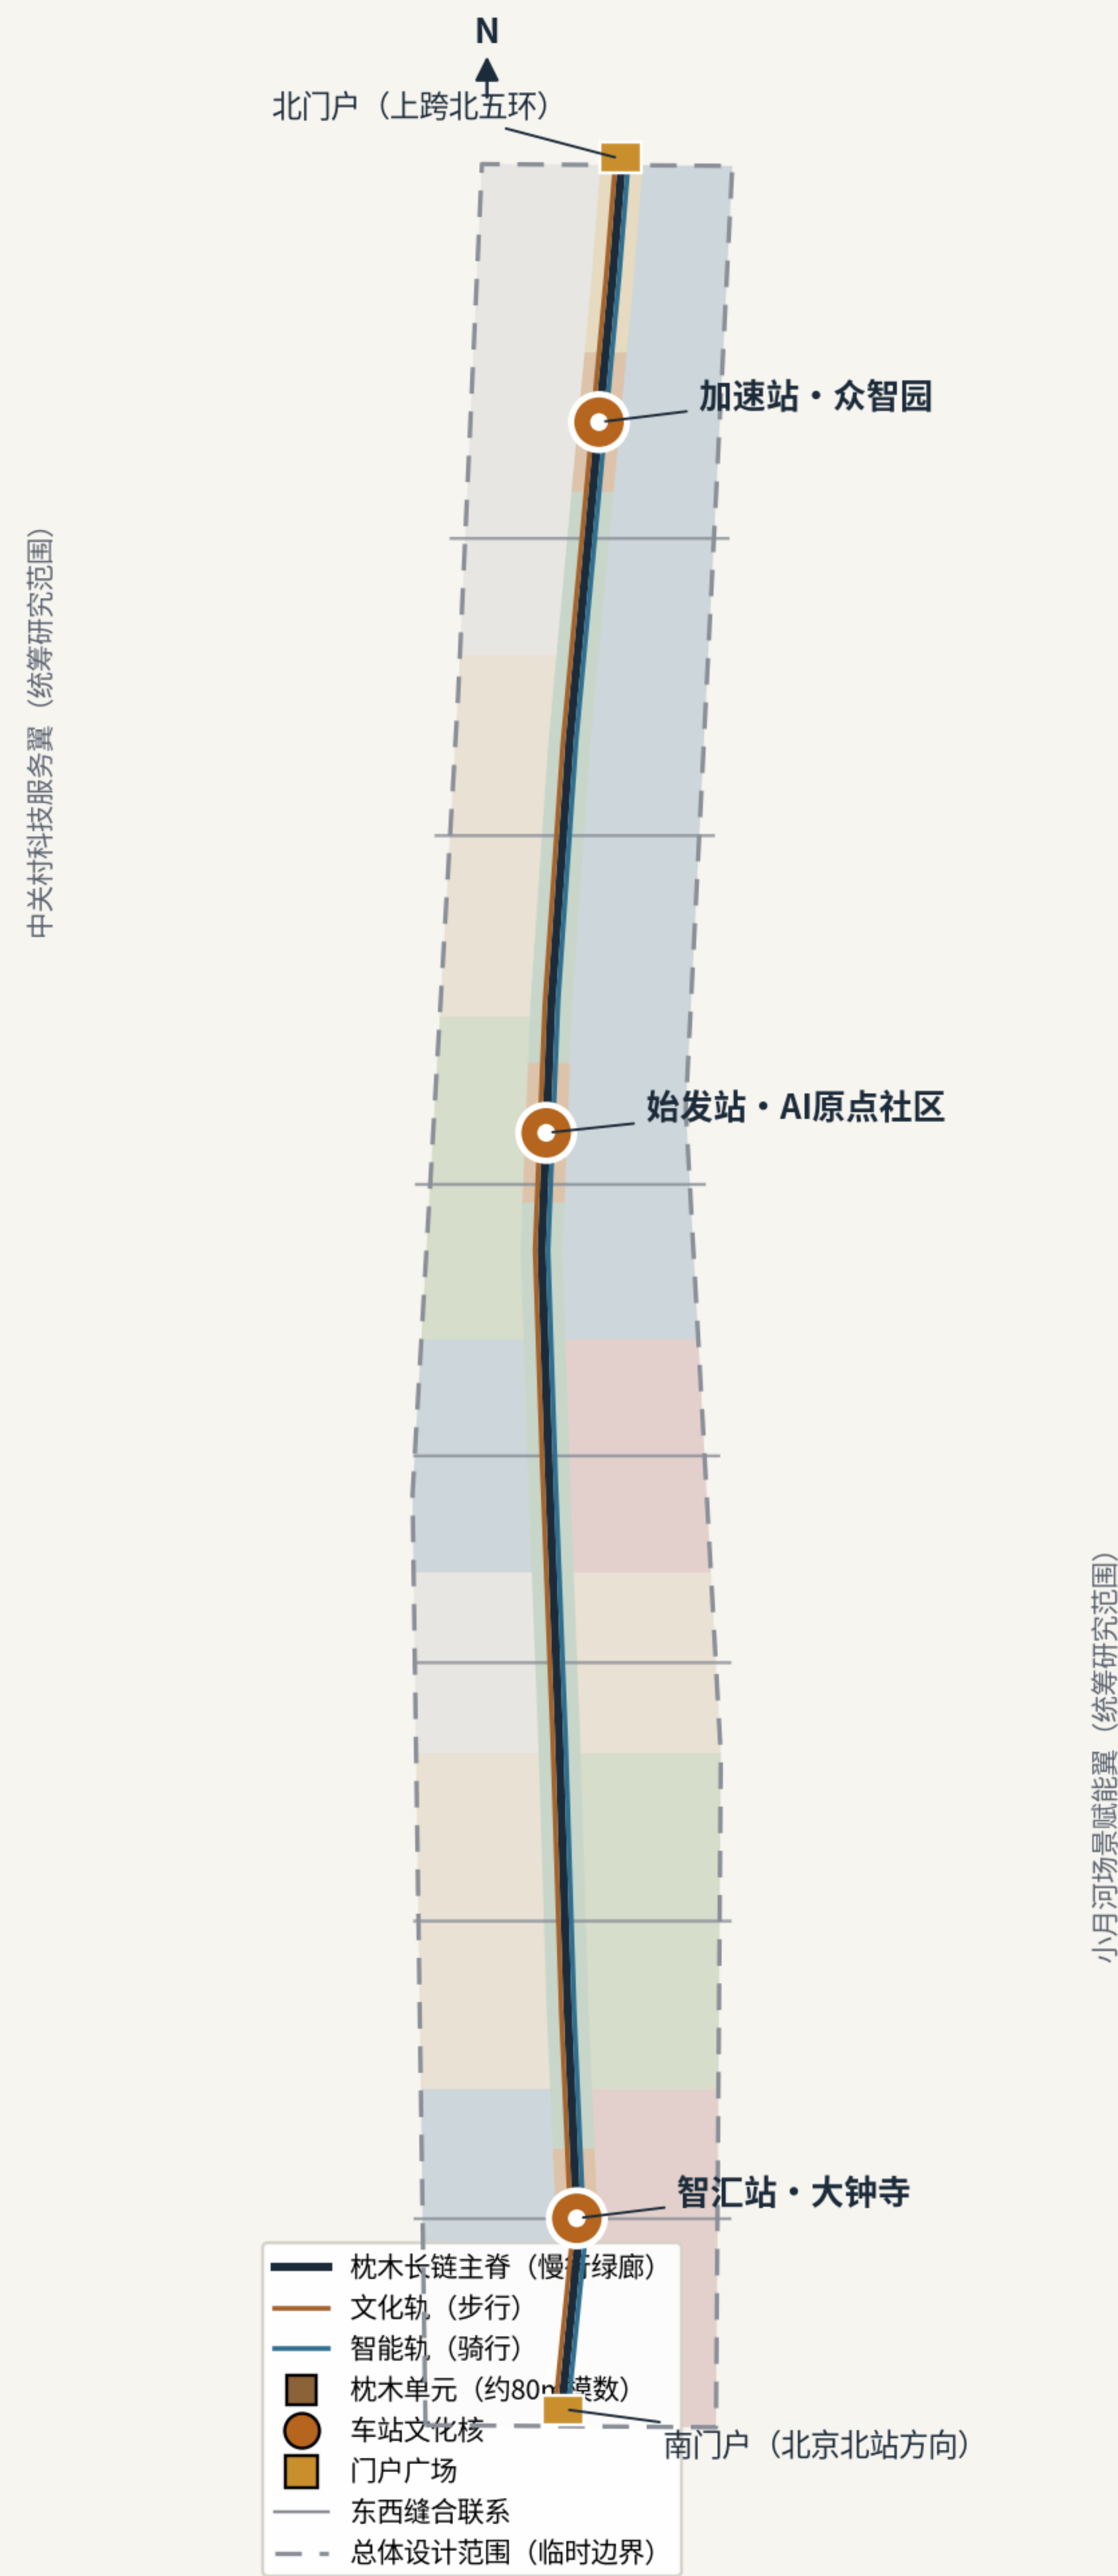

底图为仓库临时粗略边界（provisional constraint），仅用于概念讨论与自检，不构成官方红线；正式红线发布后需重算。数据：geometry/*.geojson + metrics.json（EPSG:4548 复算）。

用地布局与空间结构传导


用地分区由临时边界拓扑切分，与主脊、两轨、三站联动；留白用地为不可预设的未来保留接口

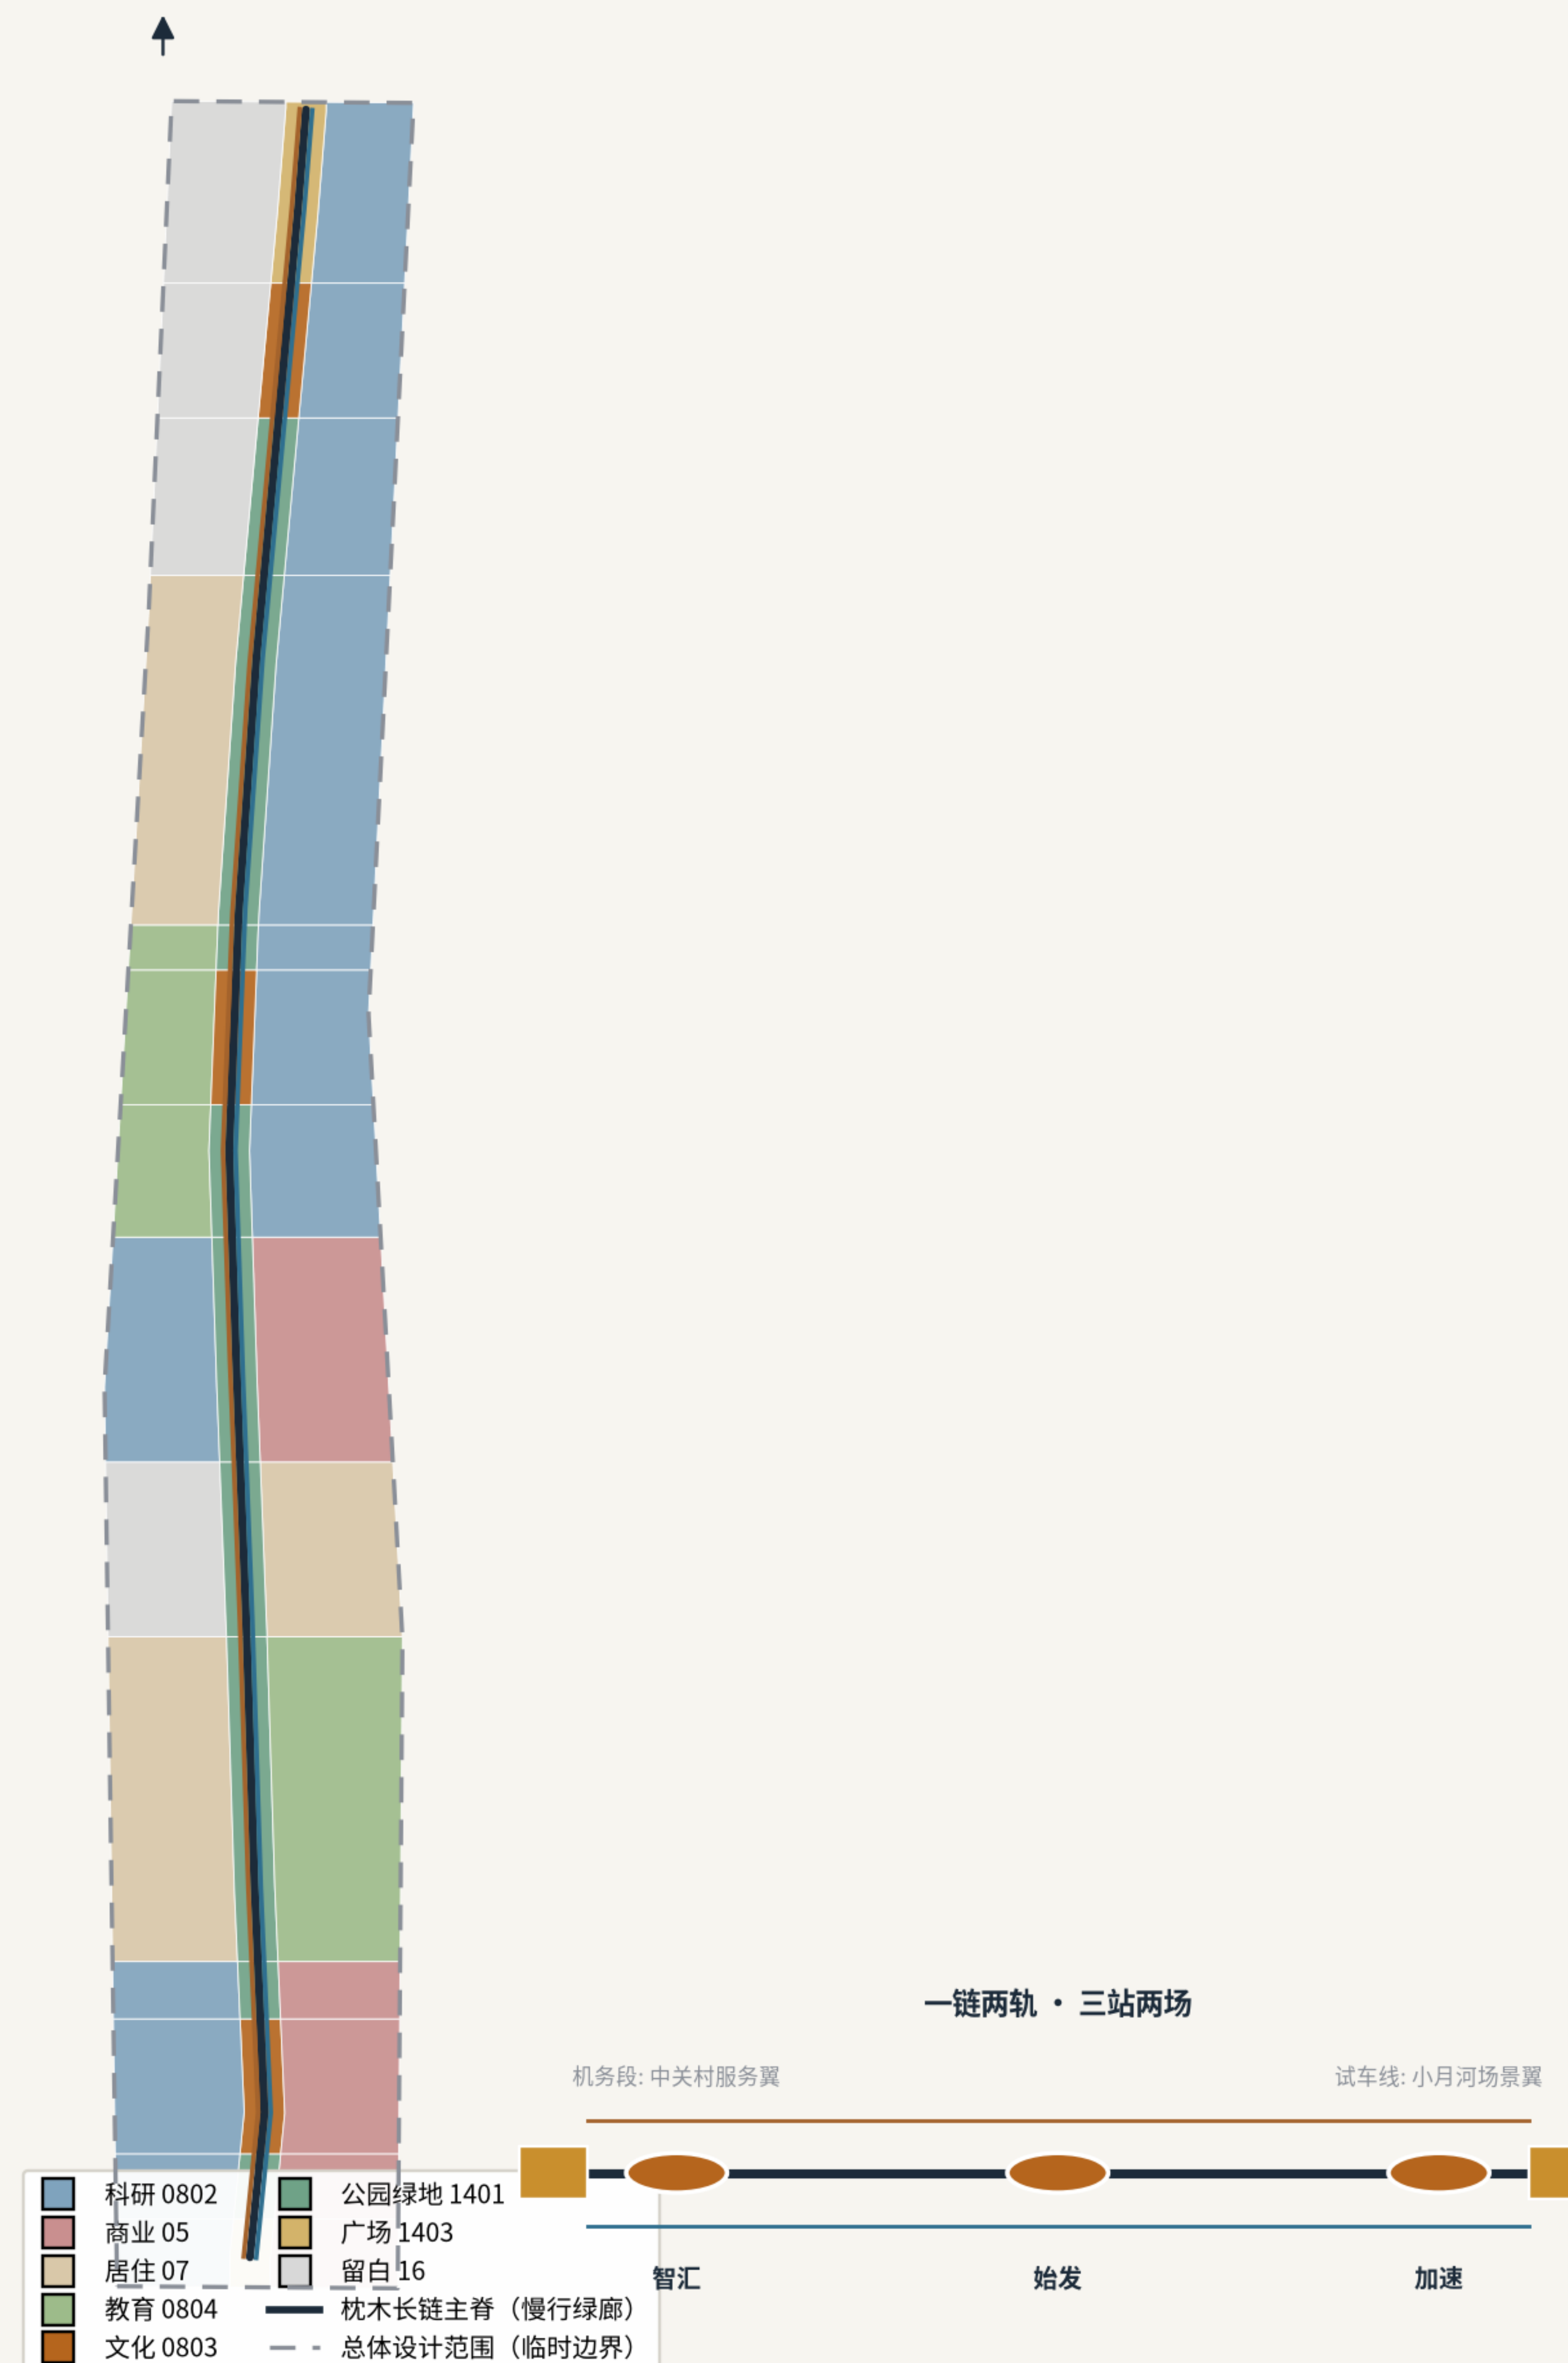

底图为仓库临时粗略边界 (provisional constraint)，仅用于概念讨论与自检，不构成官方红线；正式红线发布后需重算。数据: geometry/*.geojson + metrics.json (EPSG:4548 复算)。

交通慢行与蓝绿公共空间复合系统

慢行主脊 + 两轨 + 七条东西缝合 + 三处轨道接驳概念通道 + 蓝绿网络与 AI 场景节点

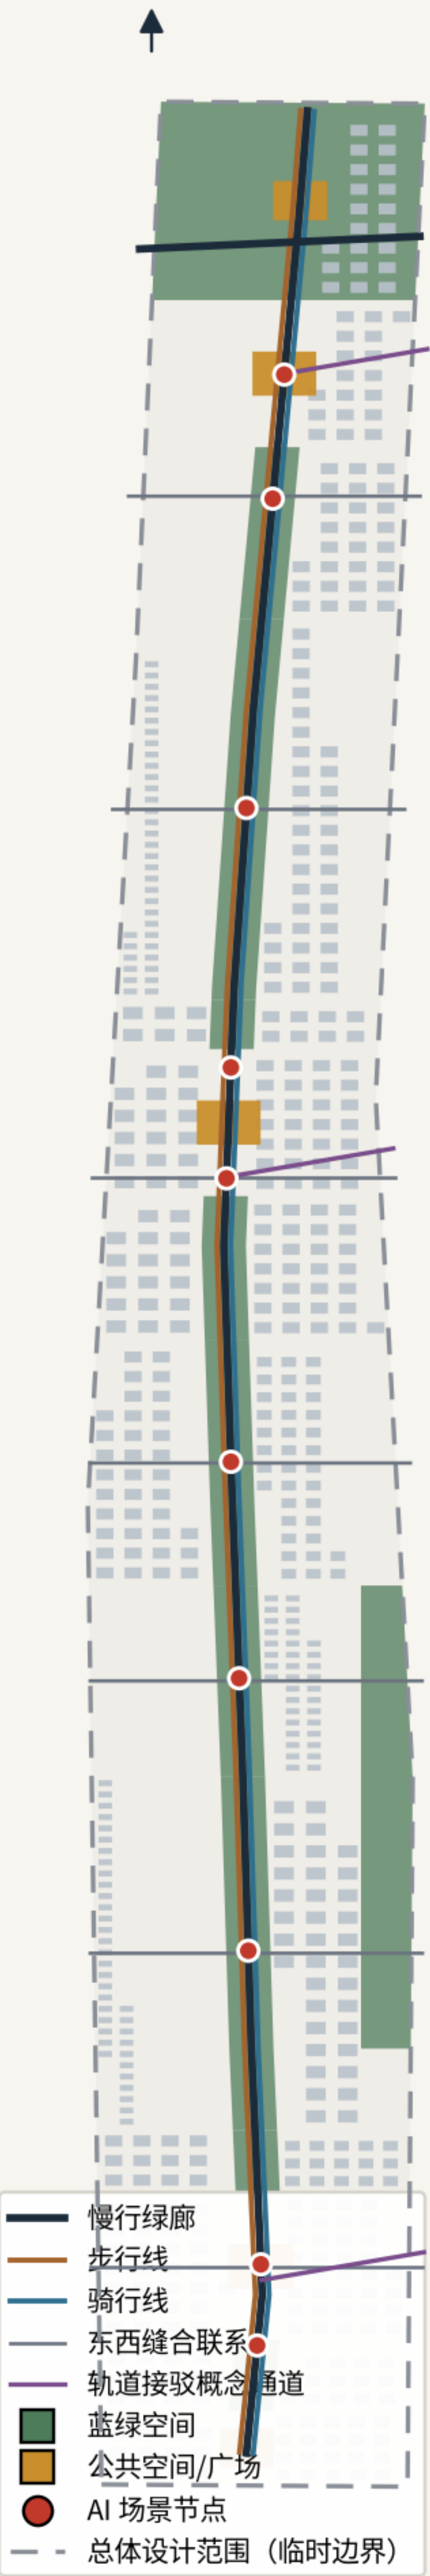


底图为仓库临时粗略边界 (provisional constraint)，仅用于概念讨论与自检，不构成官方红线；正式红线发布后需重算。数据: geometry/*.geojson + metrics.json (EPSG:4548 复算)。

三站 · 重点区域详细设计概念

三处重点区为公告指定详细设计范围；多边形为临时粗略几何，方案为概念设计深度


加速站 ACCELERATOR | 众智园AI自主创新加速区

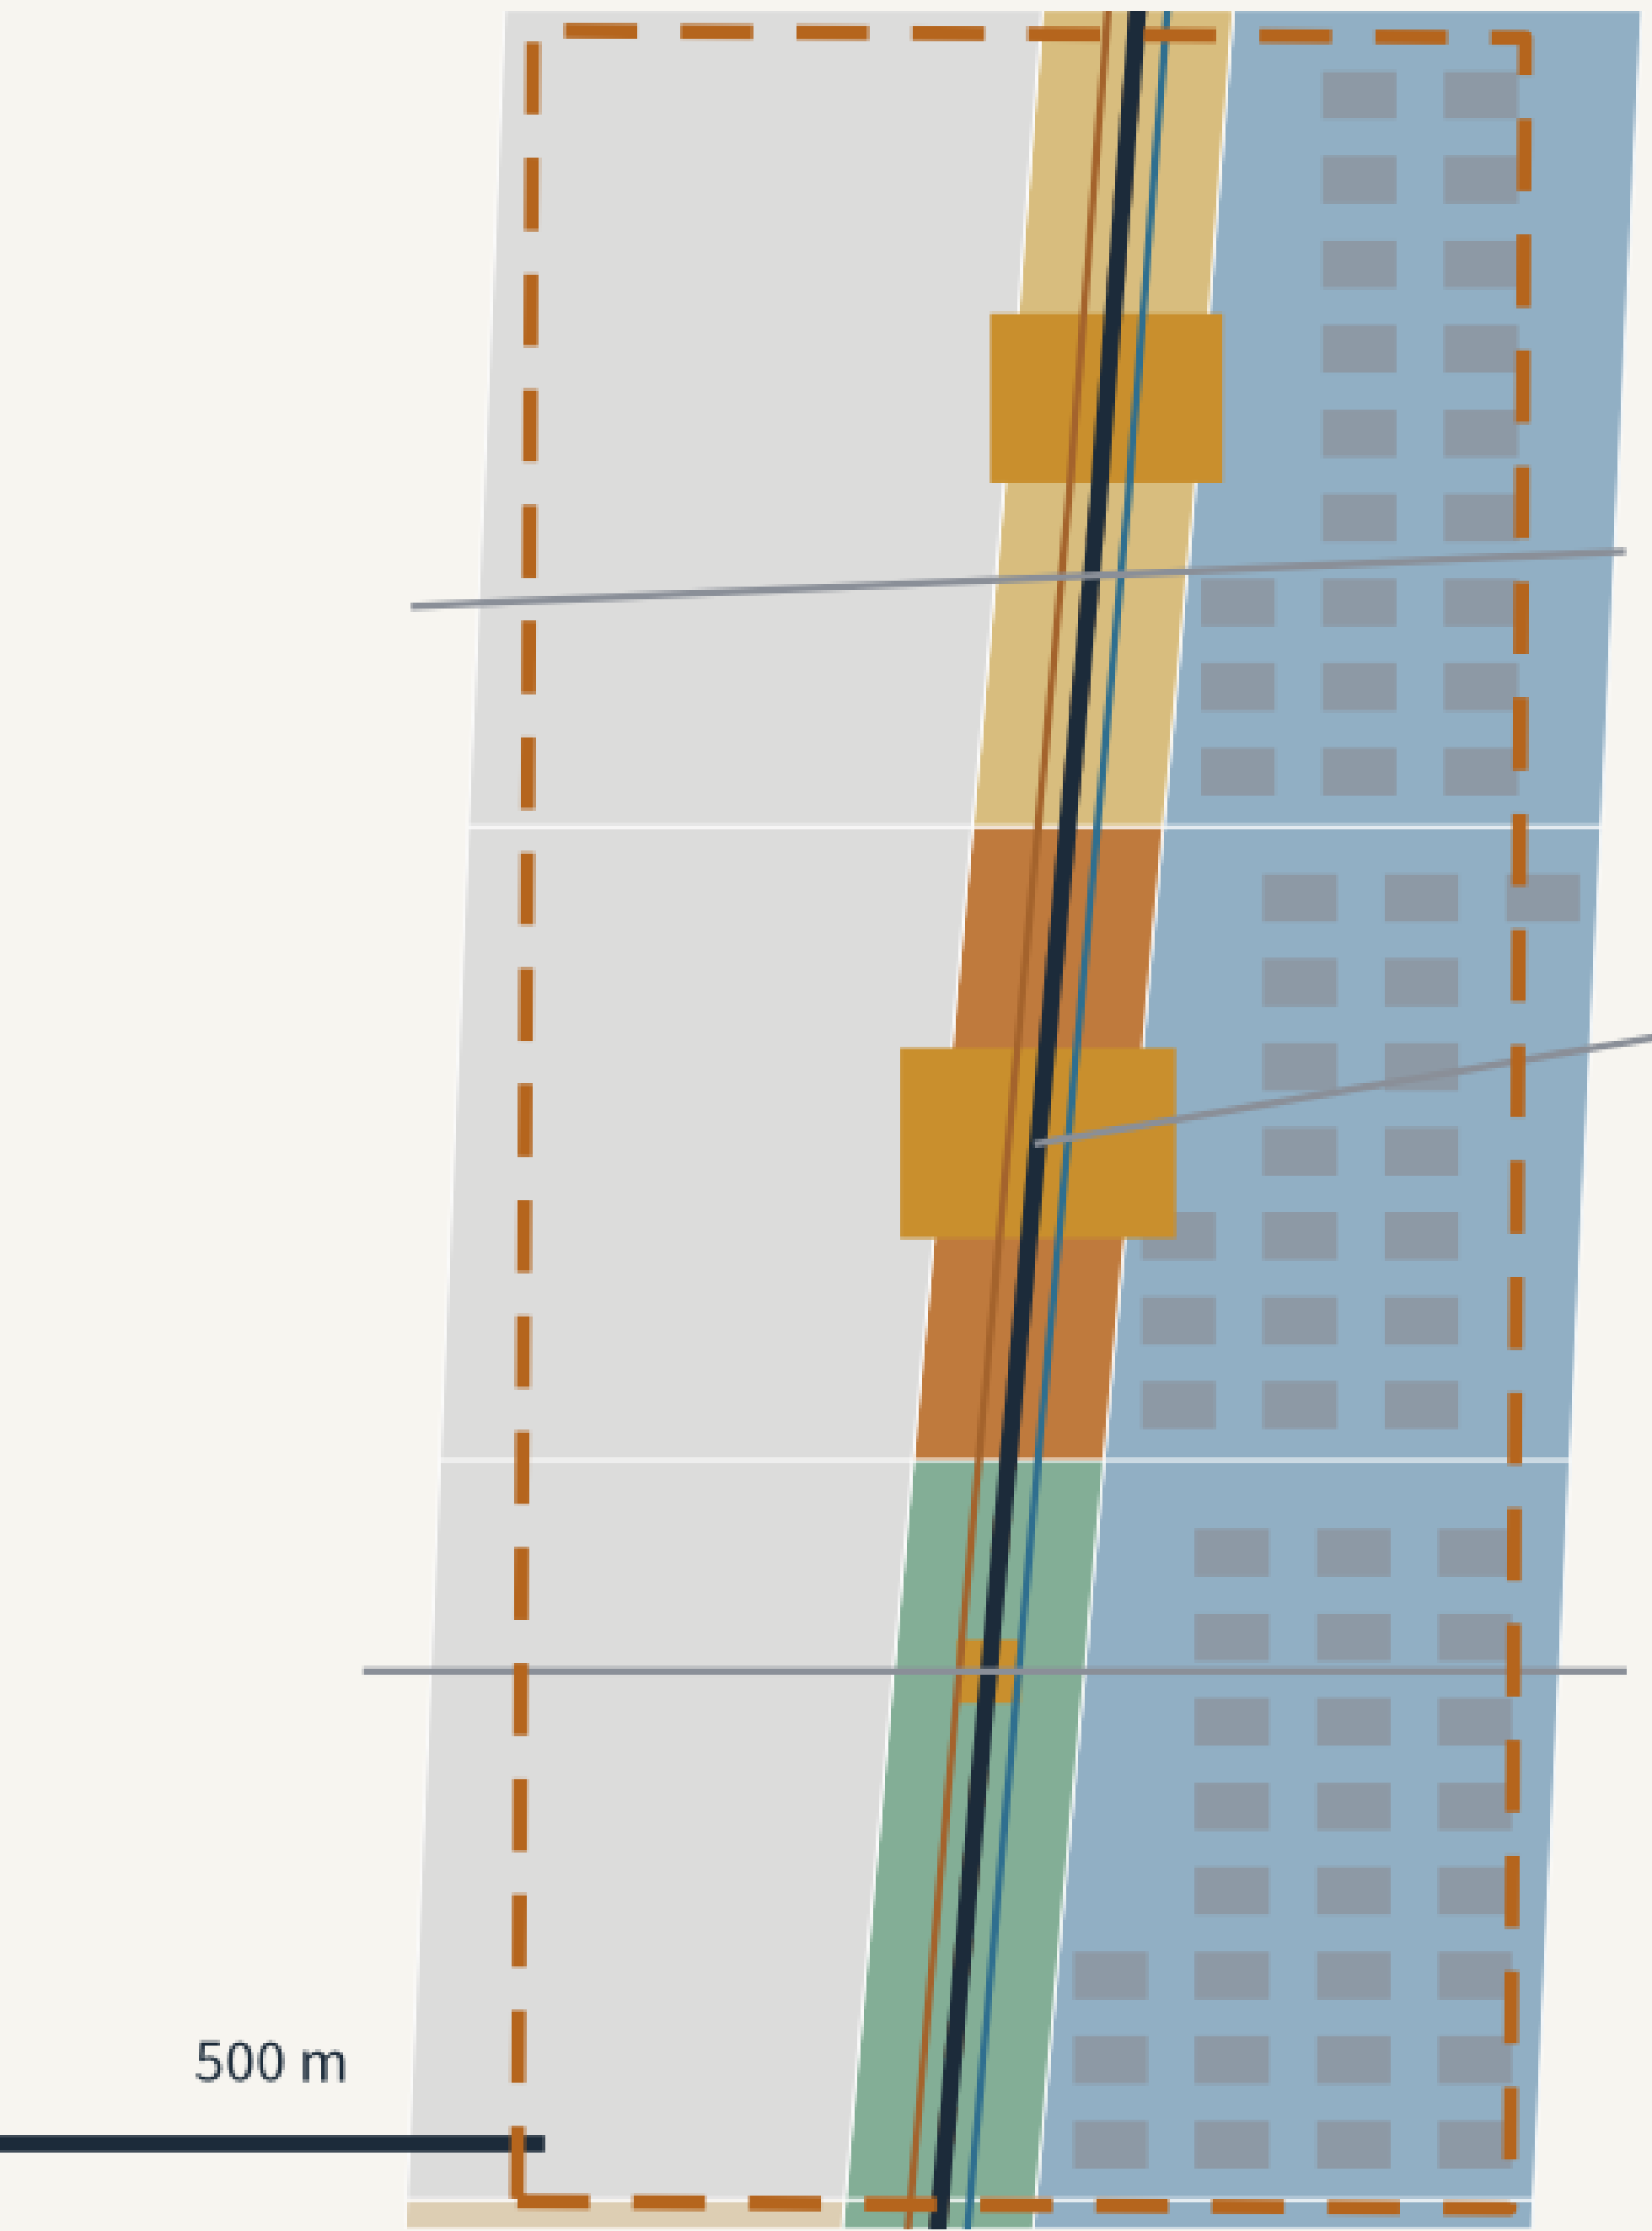

设计要点

花园型AI创新街区：国家AI平台概念承载、全栈自主体系展示、清河绿廊衔接、枕木试验段


始发站 ORIGIN | 北京AI原点社区

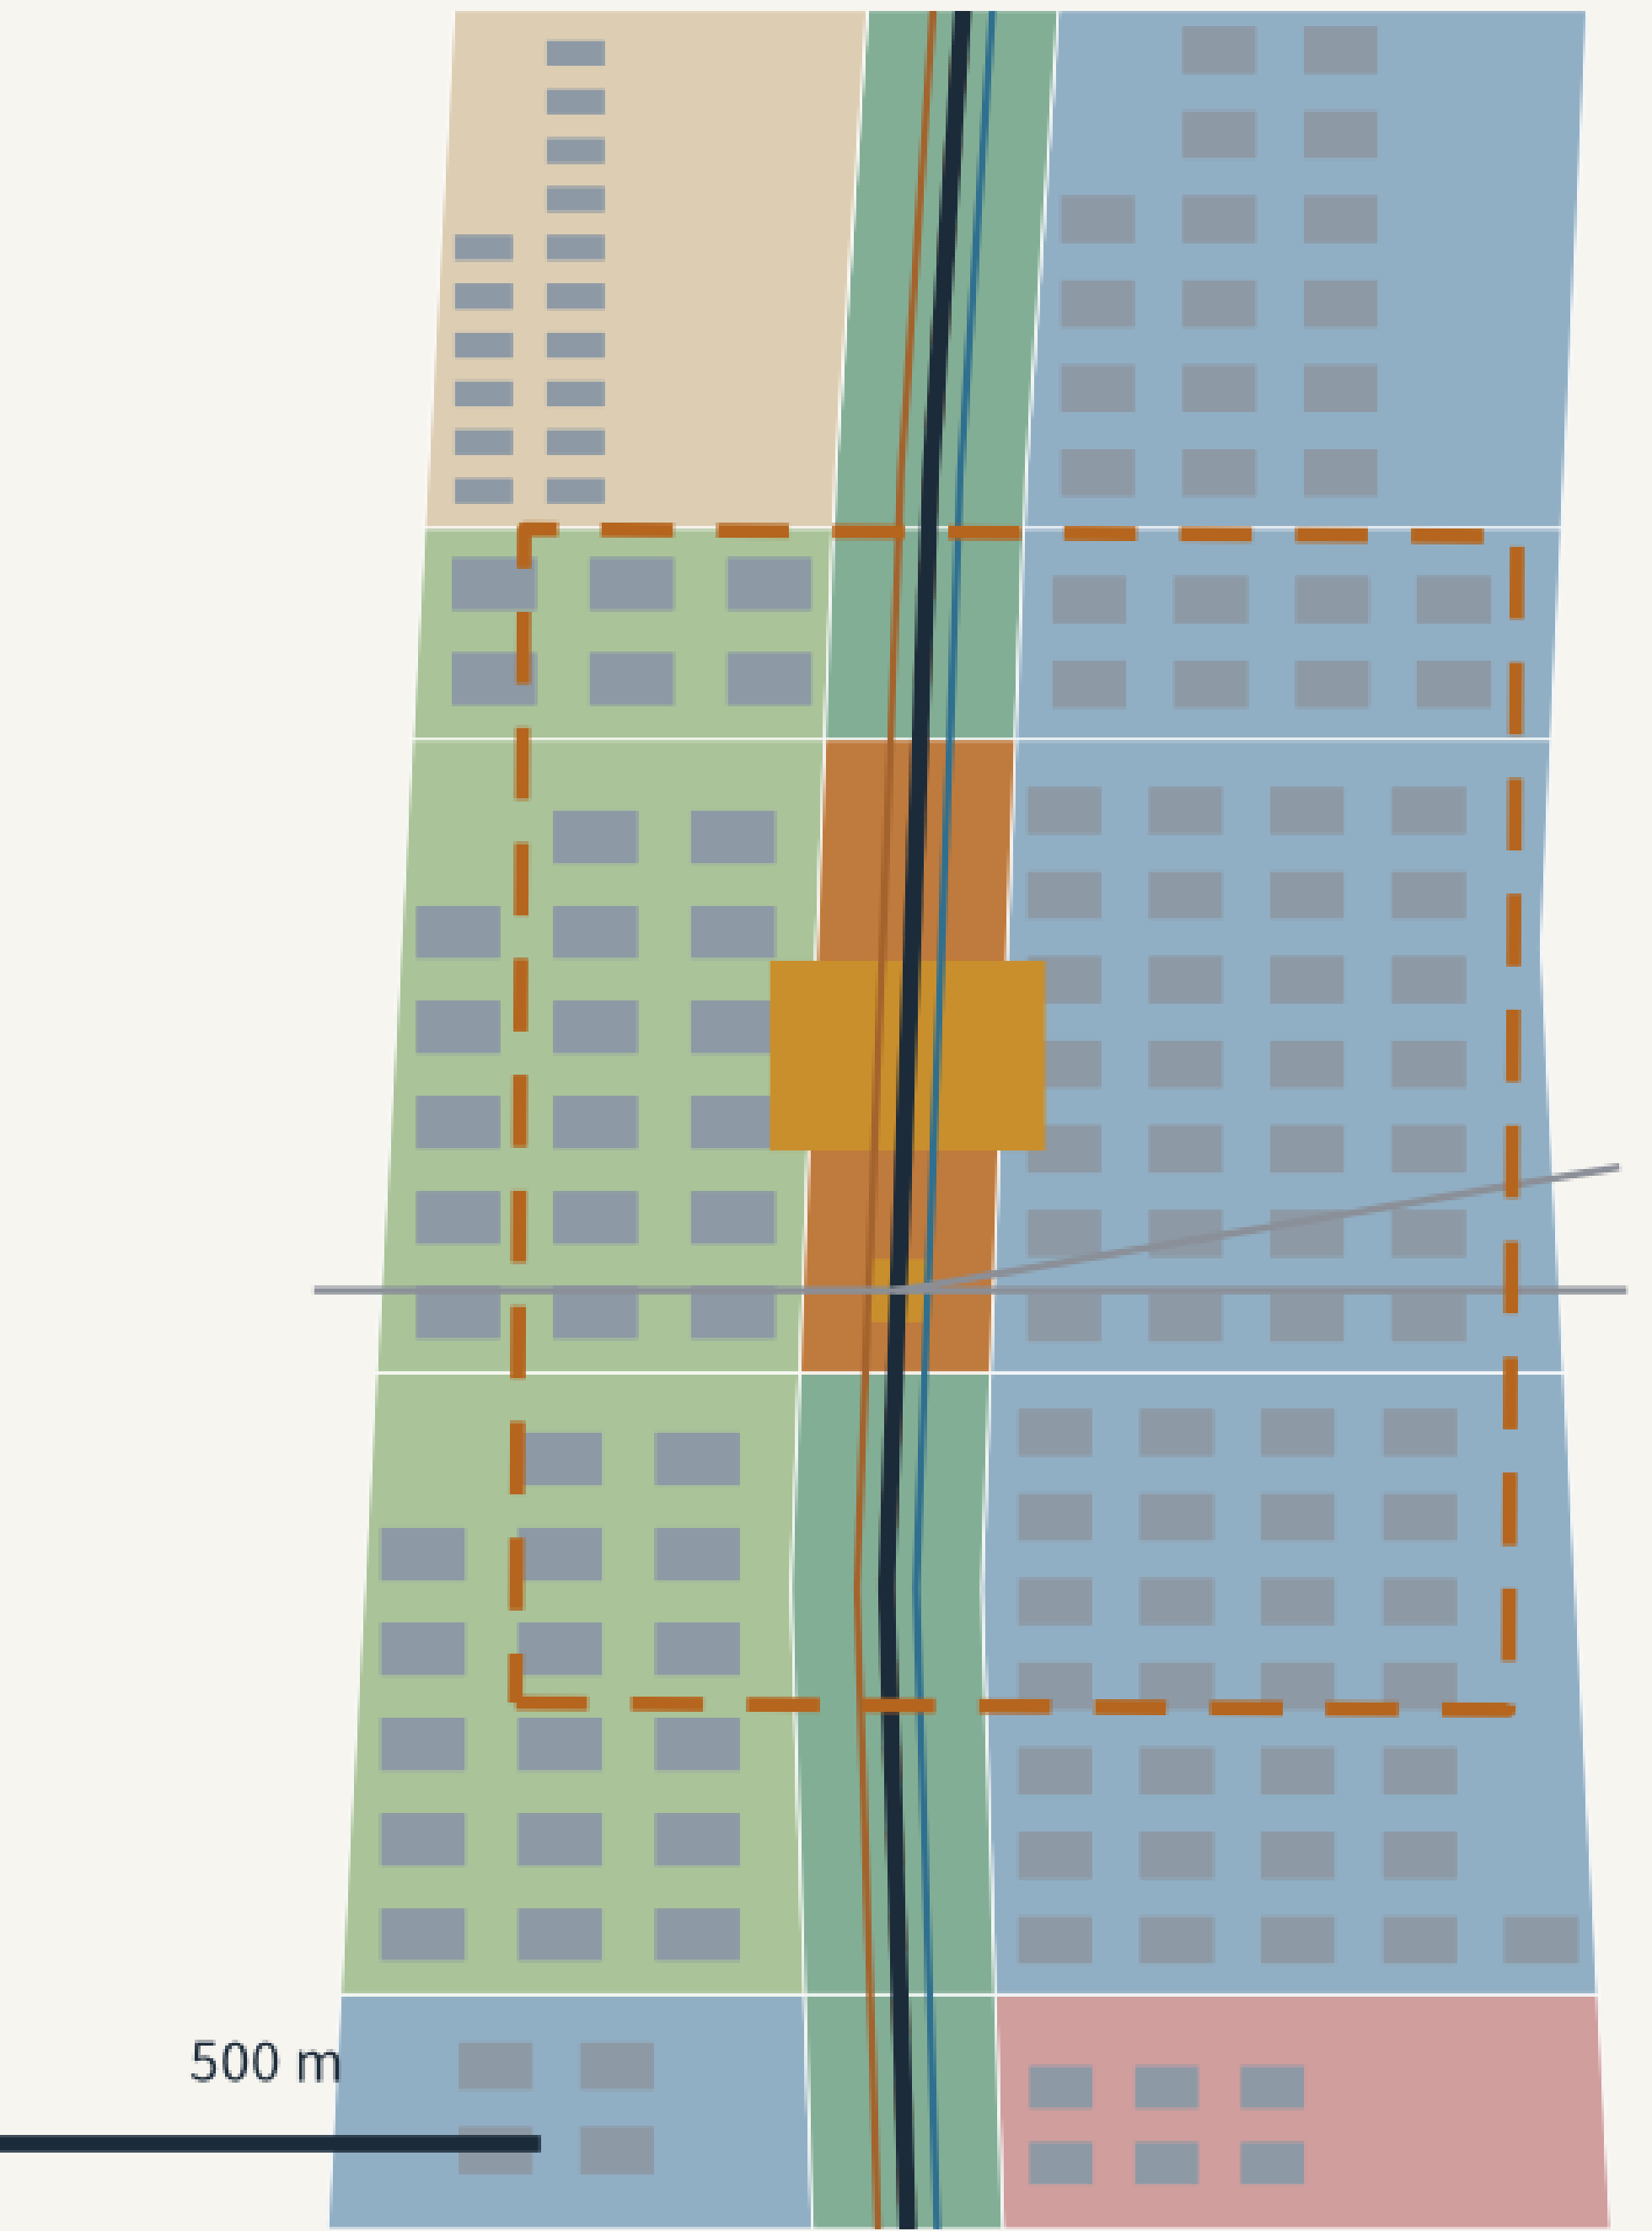

设计要点

近校型AI创新街区：清华园车站记忆、成果孵化转化、开源展示廊、开发者散步道、荣誉墙首段

智汇站 HUB | 大钟寺AI产业聚集区

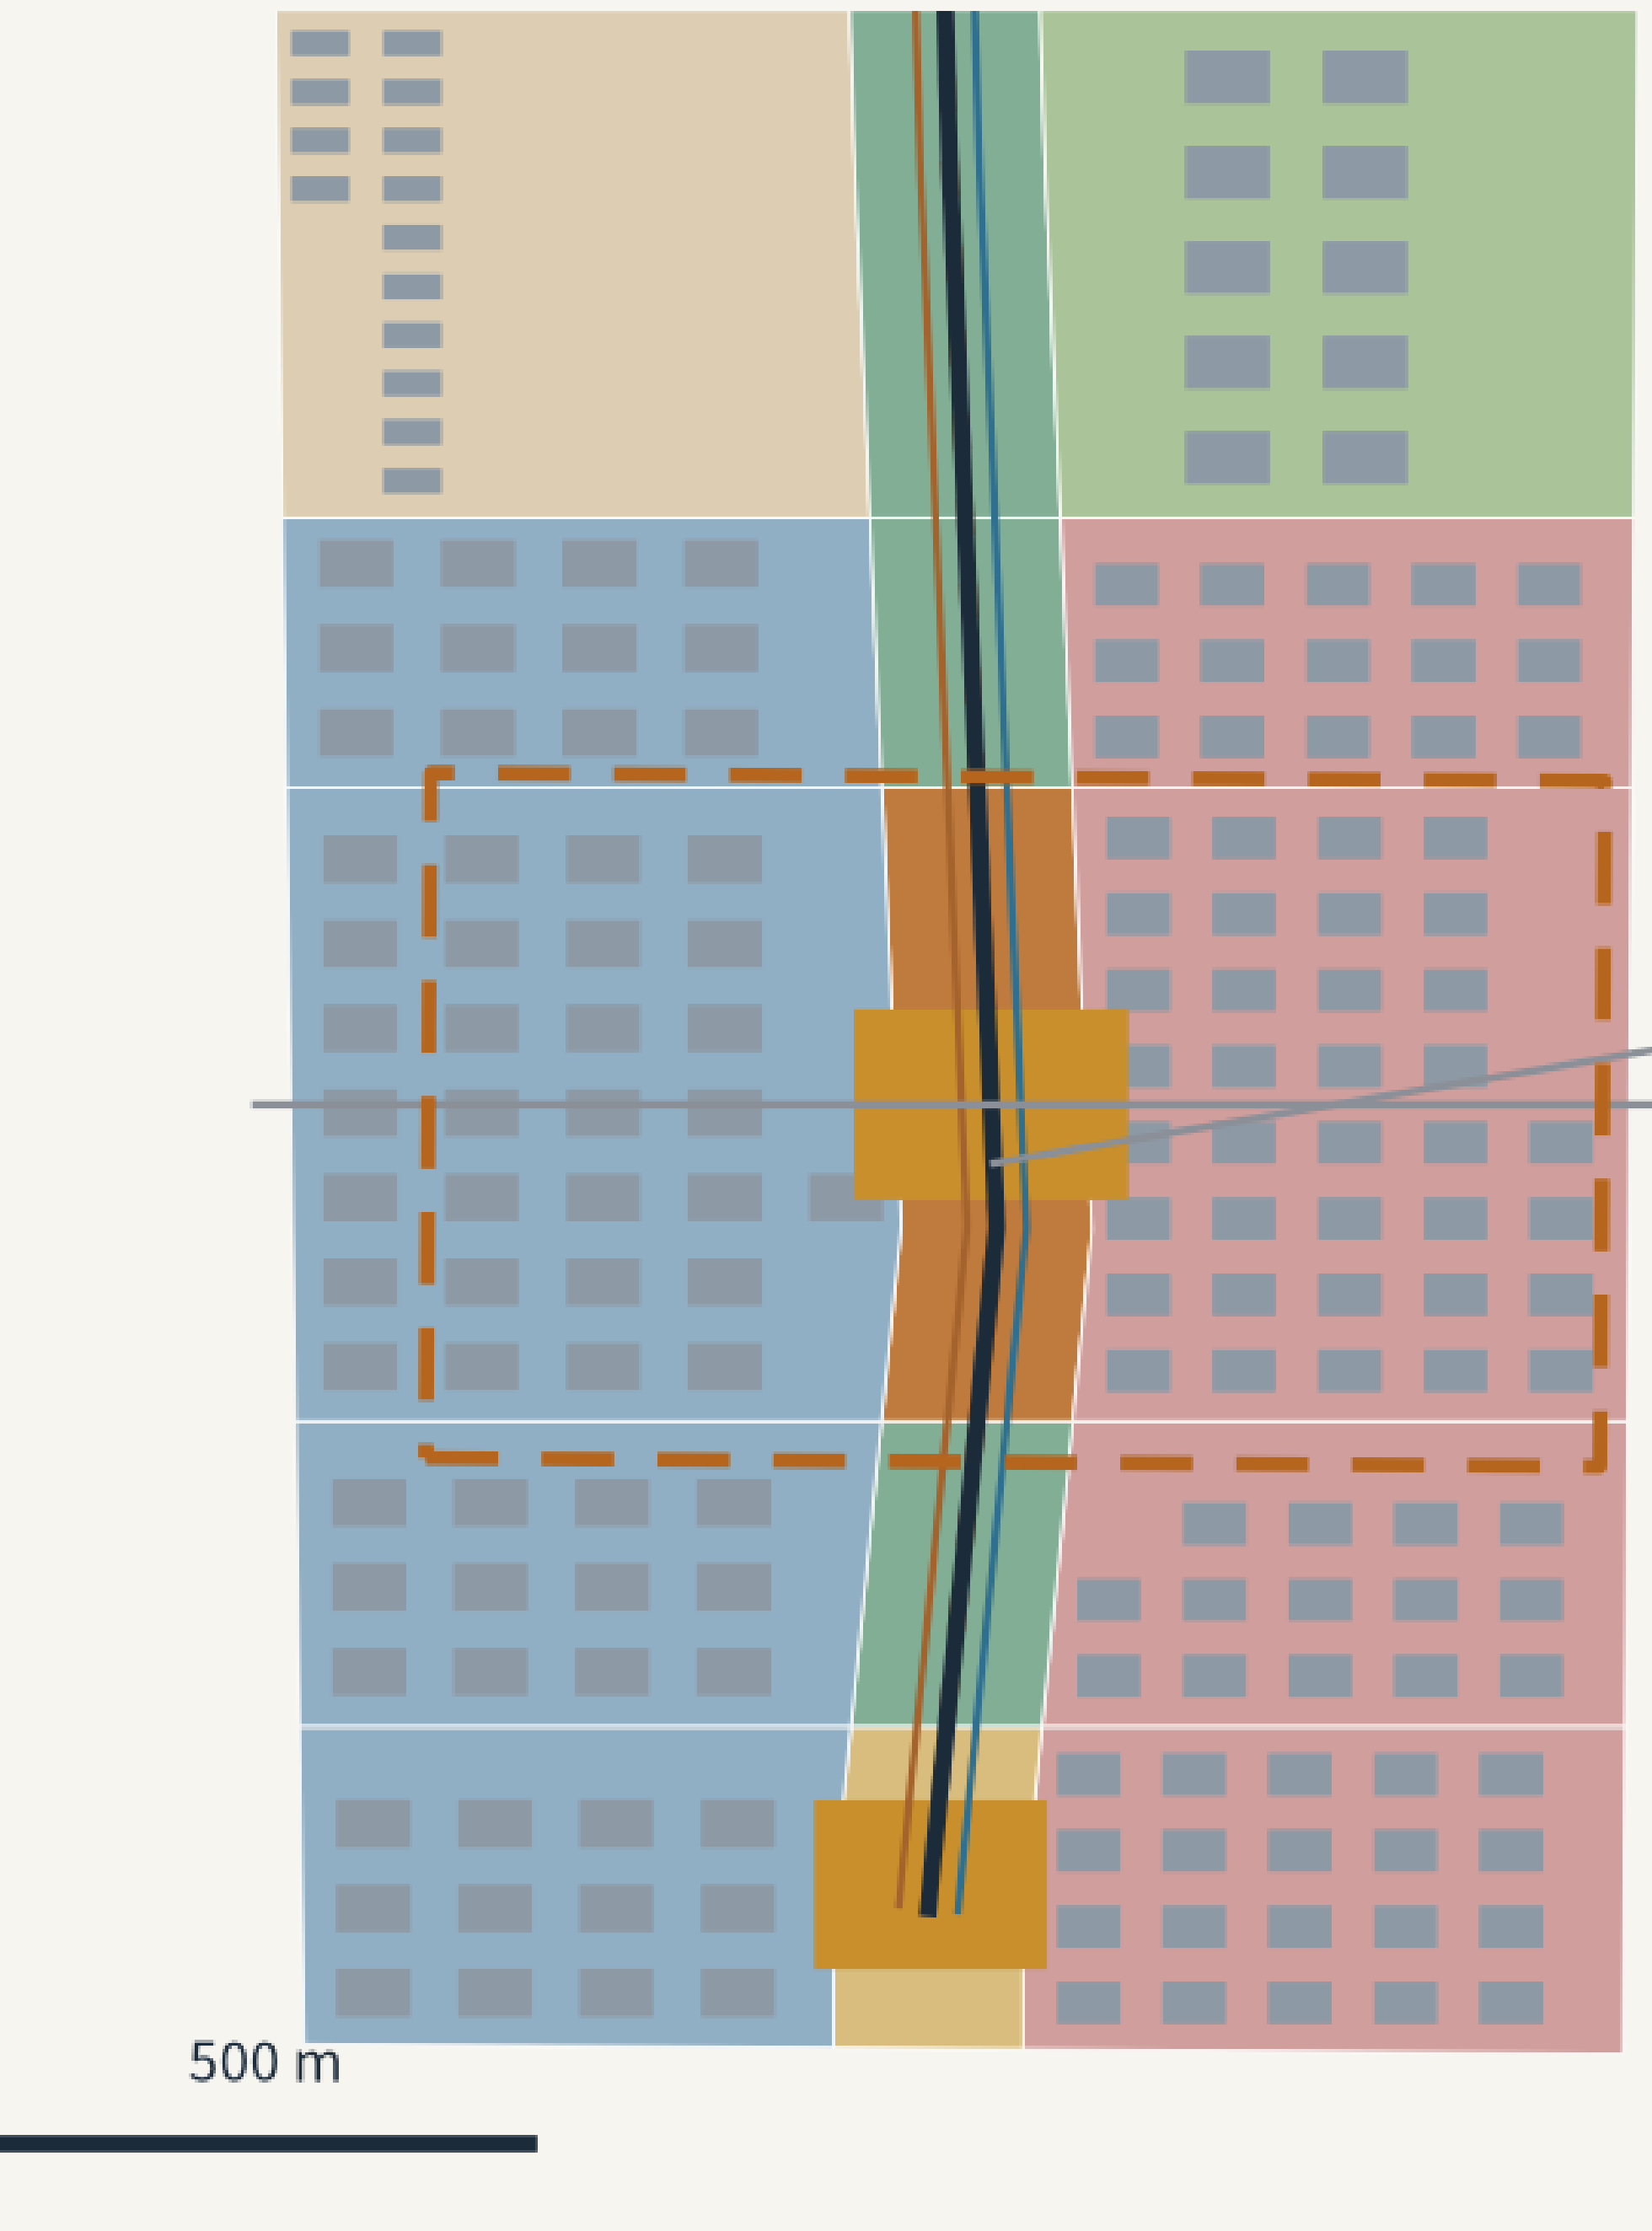

设计要点

城市型AI创新街区：智能原生消费、AI原生业态市集、四象限步行连通、轨道站一体化概念

底图为仓库临时粗略边界 (provisional constraint)，仅用于概念讨论与自检，不构成官方红线；正式红线发布后需重算。数据: geometry/*.geojson + metrics.json (EPSG:4548 复算)。

指标复算与证据链

全部已知指标由本包 GeoJSON 在 EPSG:4548 下复算；未知控规指标保持“待正式数据补齐”

总体设计范围面积

site_area_sqm

11,412,825 m²

≈11.41 km² · 公告口径约11.4km²

绿地比例

green_ratio

21.6%

246.8 ha

公共空间比例

public_space_ratio

2.5%

28.8 ha

概念建筑密度

building_density

13.9%

概念体量，非法定强度

枕木单元

sleeper_module_count

110

约80m模数化组件

慢行主脊长度

heritage_spine_length_m

9.57 km

概念线位复算

概念总建筑规模

concept_total_floor_area_sqm

1,063 万m²

低置信度量级估计

重点区域

key_area_count

3

192.1 + 104.3 + 72.0 ha（公告口径）

证据链



待正式数据补齐 (pending official data)

容积率 / 建筑高度 / 建筑密度上限 / 绿地率下限 / 退线 — 待控规与资格预审文件包公开后复算；当前不写入结论。

自检状态

确定性格式✓空间复核✓可视化封装✓专业证据链✓