

Centennial Jing-Zhang

AI Innovation Belt

百年京张AI创新带 · 概念城市设计（中文对照）

Beijing · Haidian | Jing-Zhang Railway Heritage Park Corridor | Xizhimen — Wudaokou — Qinghe

1,141.3

Site Area (ha)

22.55%

Green Ratio 绿地率

3

Key Areas 重点片区

12

AI Scenario Nodes 场景节点

Disclaimer

- All content is a conceptual recommendation; it does NOT replace statutory planning.
- All boundaries are provisional rough constraints, NOT official red lines (official_boundary=false).
- Areas and ratios are recomputed under EPSG:4548 from provisional boundaries; discussion only.
- Statutory intensity controls (FAR, building height) are missing; to be recomputed once official data arrives.

Design Basis & Three-Level Scope

设计依据与三层范围

Design Basis

- Official Pre-qualification Announcement (Haidian Branch, BMCRMB, 2026-05-09)
- Competition taskbook: tasks 1.3 / 1.4 / 1.5 and agent.1–agent.6
- MNR / MOHURD standards (land-use classification, urban design depth)
- Provisional rough boundary data (official_boundary=false) — NOT official red lines


Positioning: the Jing-Zhang Railway Heritage Park as a linear public spine, linking three differentiated AI innovation nodes in a 'one spine · three cores · two wings · multiple points' corridor structure.

Level	Scope	Scale	Depth
Coordination Study	Wider Haidian AI innovation district	Macro study	Strategic research
Overall Design Area	Jing-Zhang heritage corridor (provisional)	≈1,141.3 ha (recomputed)	Concept urban design
Key Areas	Zhongzhiyuan / AI Origin / Dazhongsi (provisional)	192.1 / 104.3 / 72.0 ha (announced)	Detailed concept design

Note: key-area boundaries are provisional rough extents, not official; announced areas from the announcement; recomputed values on the metrics page.

Overall Structure — One Spine, Three Cores, Two Wings, Multiple Points

总体结构 · 一脊三核两翼多点

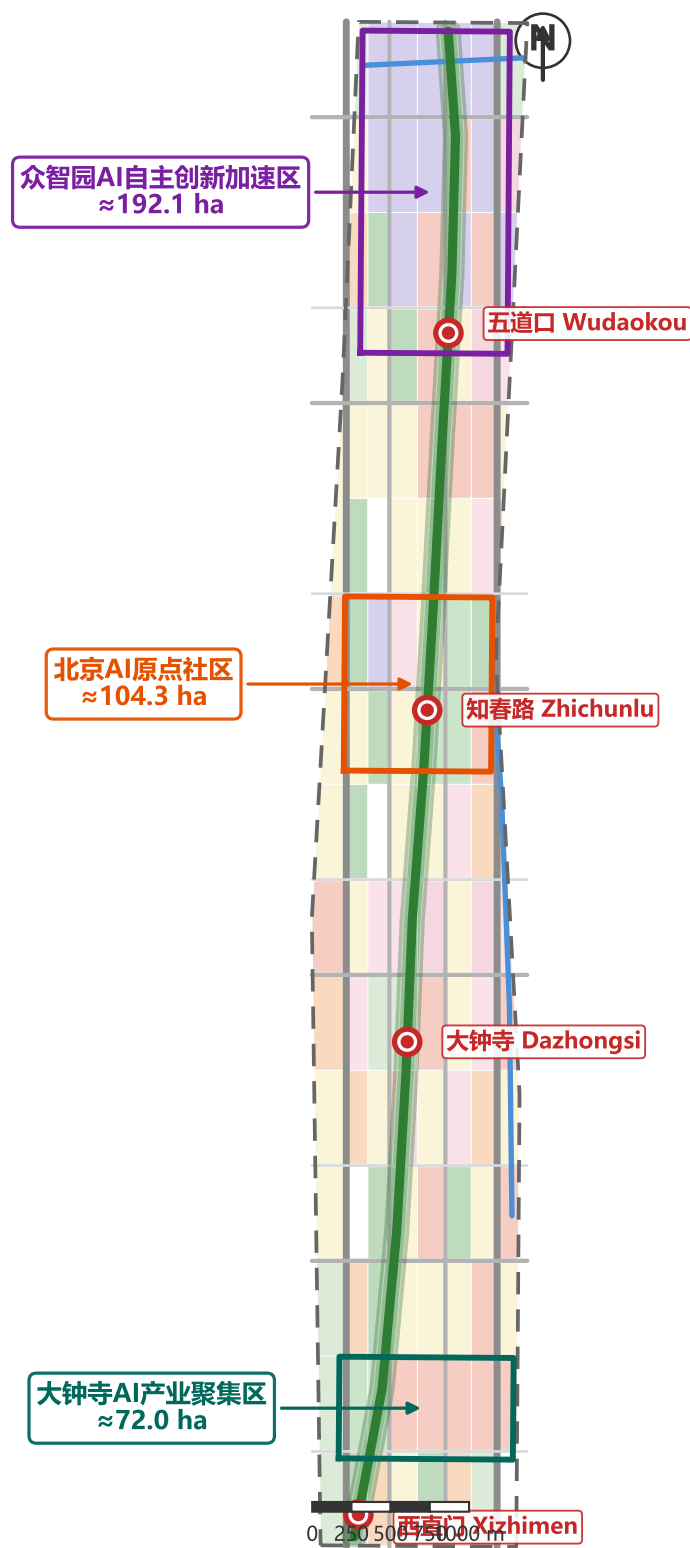

Structure Reading

SPINE — the Jing-Zhang heritage greenway: ~9.6 km corridor (≈136.2 ha) layering the 1909 railway memory with future AI scenarios.


CORES — North: Zhongzhiyuan AI Acceleration Area (≈192.1 ha); Middle: Beijing AI Origin Community (≈104.3 ha); South: Dazhongsi AI Industry Cluster (≈72.0 ha).

WINGS — existing fabric flanking the corridor, infilled with housing and public services.

POINTS — 4 station TOD circles (Xizhimen / Dazhongsi / Zhichunlu / Wudaokou) + 12 AI scenario nodes along the spine.

Land Use & Retain–Renovate–Demolish–New Logic

用地结构与留改拆新建逻辑

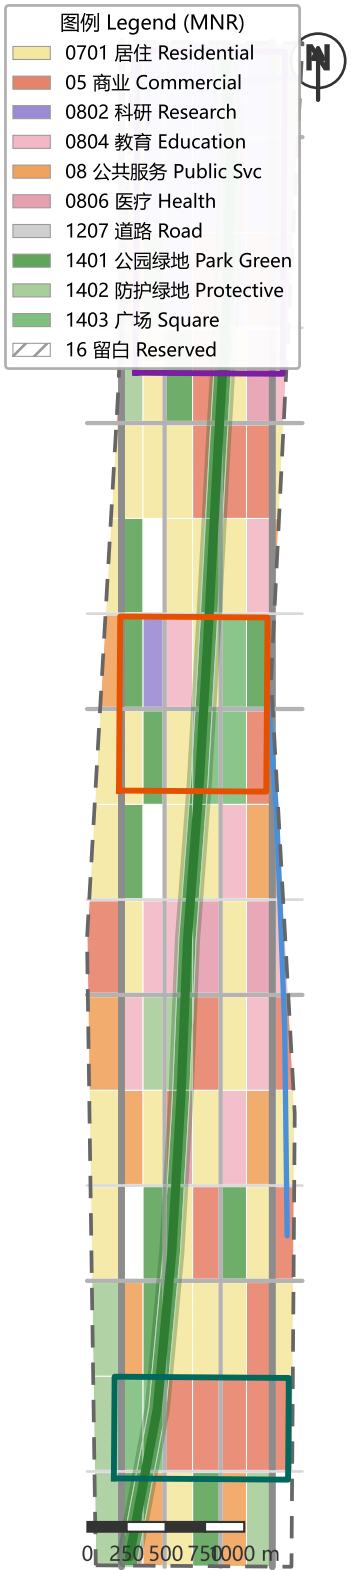


Retain · Renovate · Demolish · New (concept strategy, n=91)

- RETAIN — 66 existing buildings kept, respecting the urban fabric.
- RENOVATE — micro-renewal of corridor-facing frontages into innovation services.
- DEMOLISH — only scattered inefficient structures blocking the spine and blue-green links (concept judgement).
- NEW — 13 AI R&D + 9 mixed-use + 2 residential + 1 education buildings, clustered in the three cores and TOD circles.

Land-use strategy: Commercial 05 and Research 0802 cluster along the spine and cores; Reserved 16 (≈ 29.2 ha) held for future strategic facilities.

Key Area — Zhongzhiyuan AI Acceleration Area

重点片区 · 众智园AI自主创新加速区

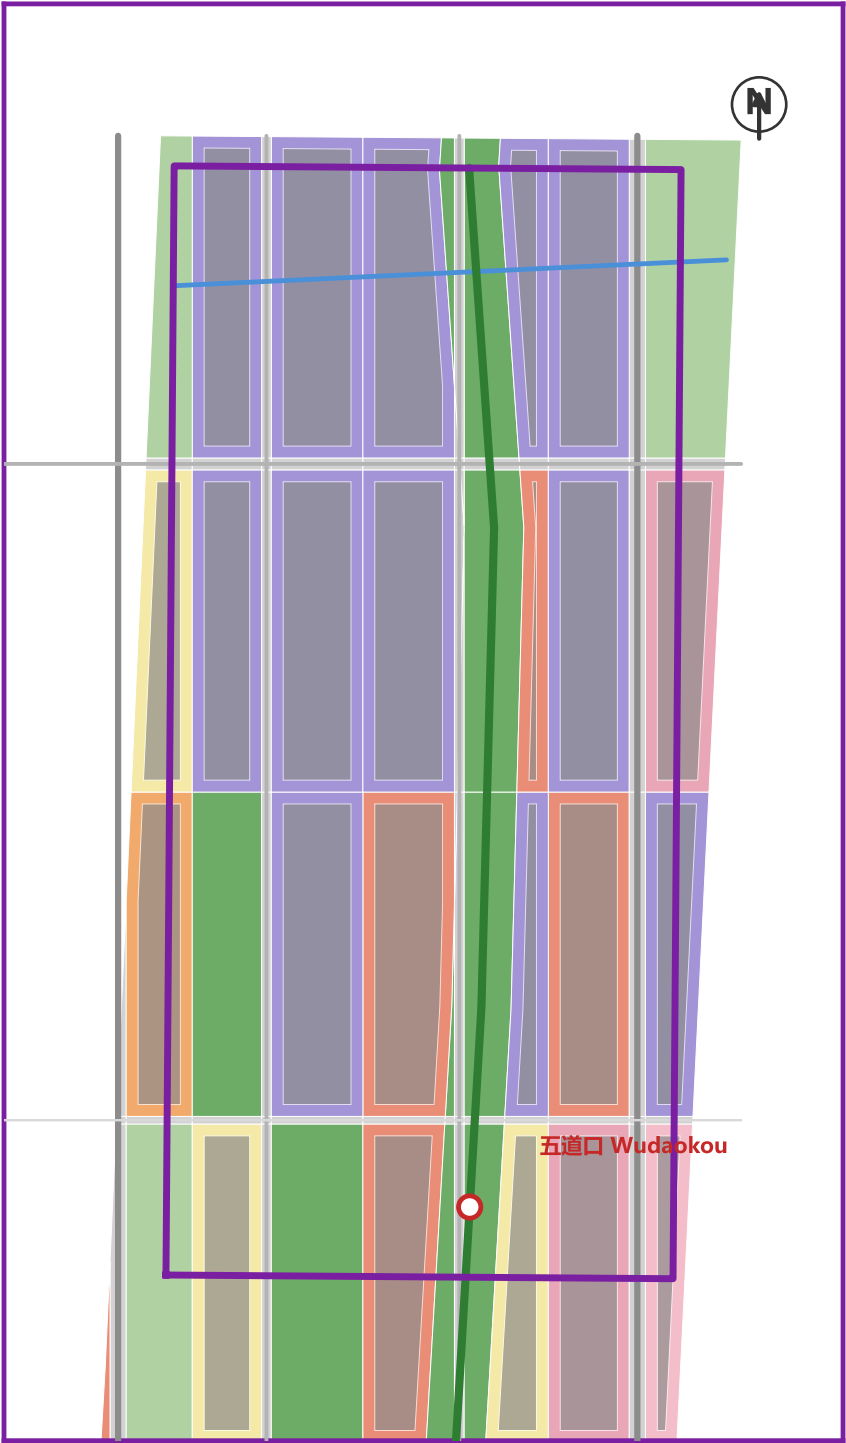

Design Intent 设计意图


- Full-stack indigenous R&D clusters (chips-frameworks-models-apps)
- Qinghe cultural green waterfront + Valley Overlook
- Research 0802 coupled with Reserved 16 strategic land
- Wudaokou TOD gateway: rail + slow-mobility arrival

Scale: announced ≈ 192.1 ha; provisional recompute 192.9 ha (reference only).

Map: concept land use, building footprints, greenway/roads, station; provisional rough boundary.

Key Area — Beijing AI Origin Community

重点片区 · 北京AI原点社区

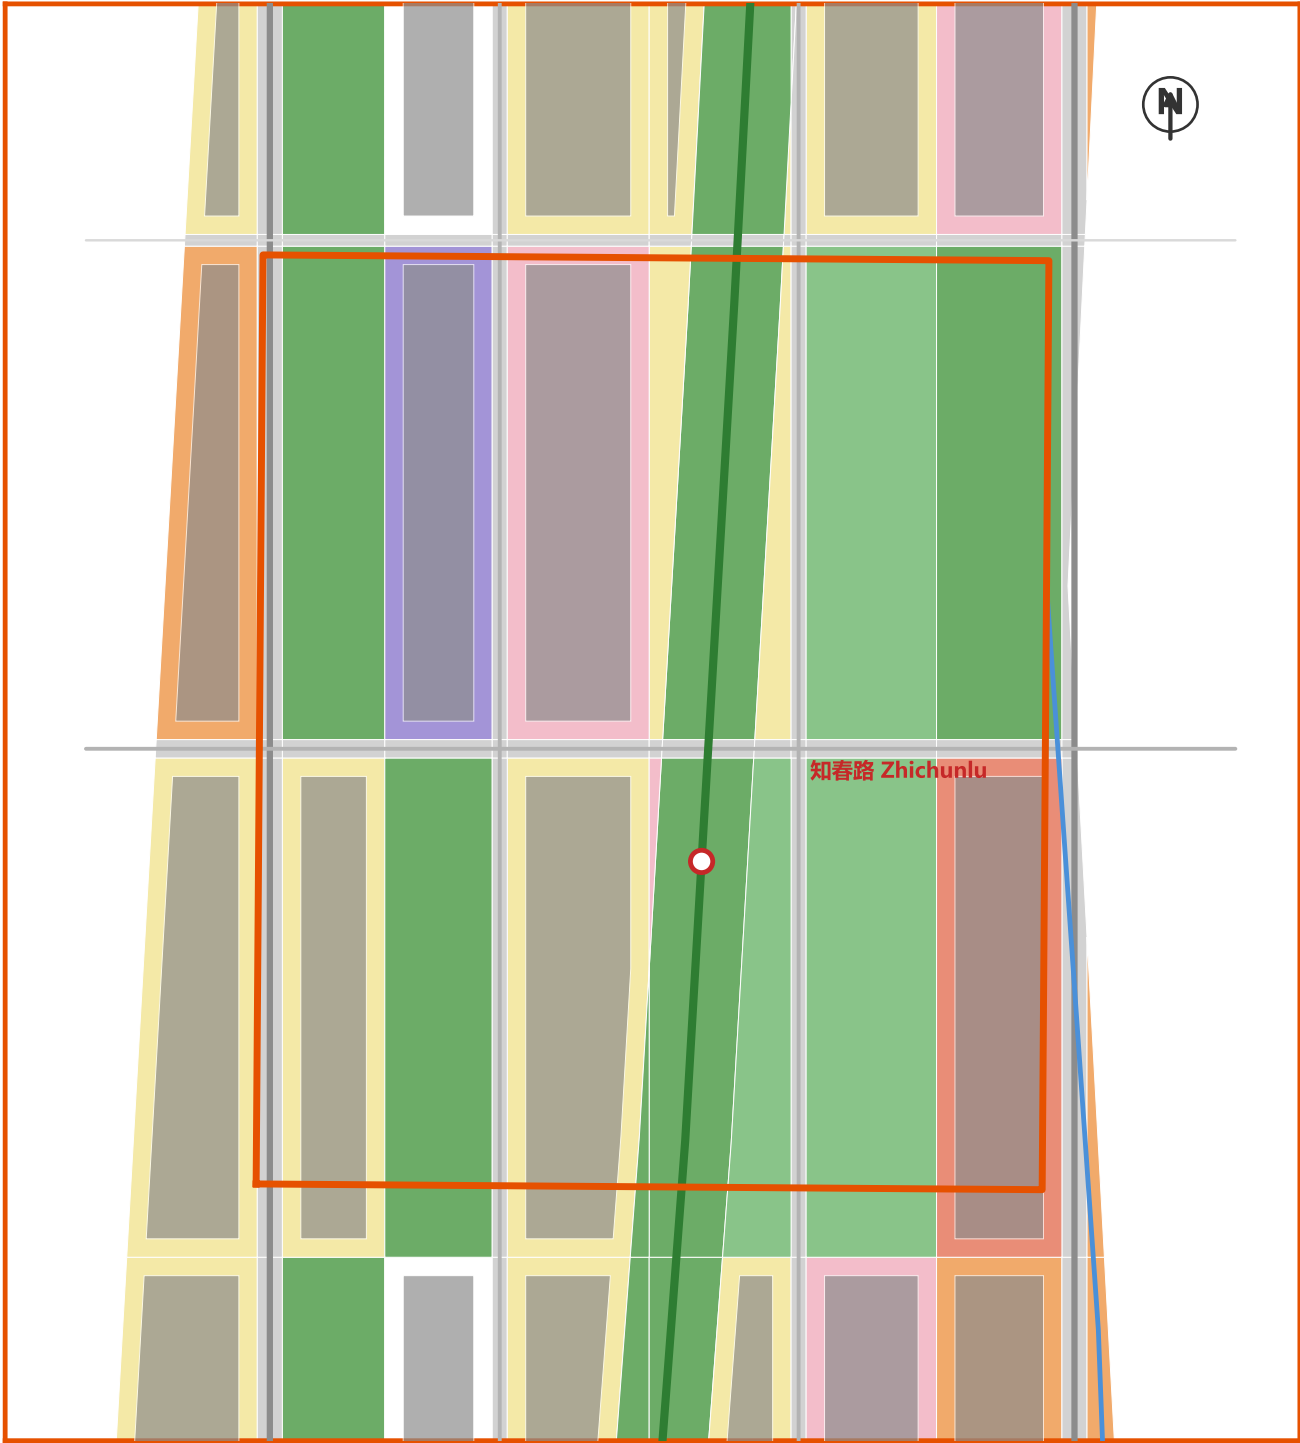

Design Intent 设计意图

- Tech-transfer blocks: alumni innovation & proof-of-concept
- Campus-side slow-mobility-first community fabric
- AI Origin Plaza: mid-corridor landmark civic living room
- Research 0802 + Residential 0701 mix, 15-min innovation circle

Scale: announced ≈ 104.3 ha; provisional recompute 104.3 ha (reference only).

Map: concept land use, building footprints, greenway/roads, station; provisional rough boundary.


Key Area — Dazhongsi AI Industry Cluster

重点片区 · 大钟寺AI产业聚集区

Design Intent 设计意图

- AI-native consumption: first-launch showcases & scenario retail
- Dazhongsi TOD: four-quadrant seamless pedestrian links
- South gateway of heritage park: Jing-Zhang Memory Gate
- Commercial 05 + Public Service 08 mix, all-day vitality

Scale: announced ≈ 72.0 ha; provisional recompute 72.0 ha (reference only).

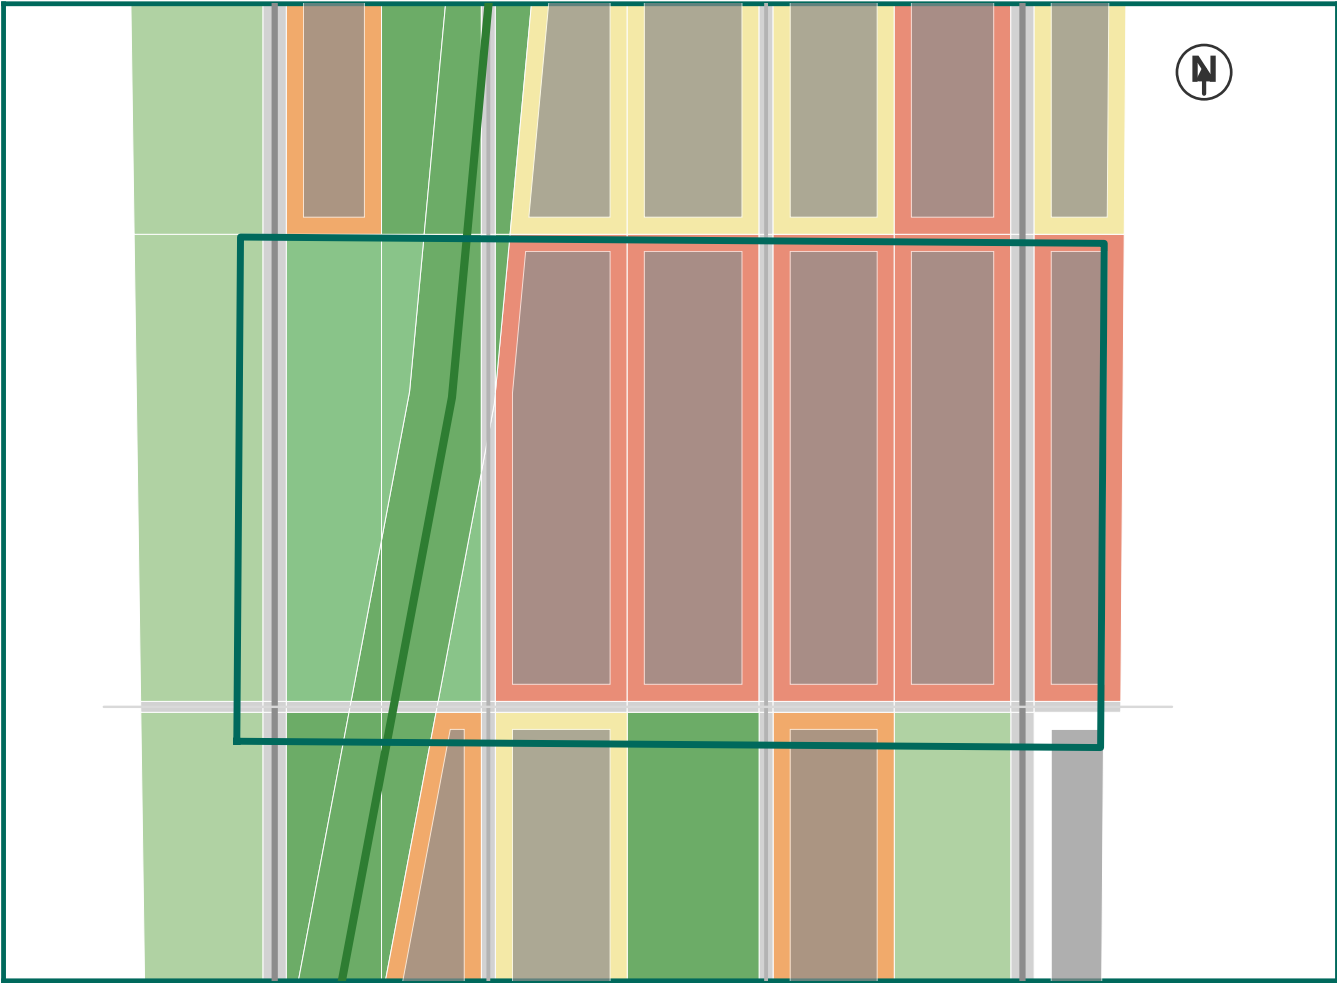

Map: concept land use, building footprints, greenway/roads, station; provisional rough boundary.

Base boundaries: provisional rough constraint, NOT official red lines; areas recomputed in EPSG:4548; concept reference only

Mobility & Blue-Green Network

交通慢行与蓝绿网络




Mobility & Blue-Green Strategy

- Greenway first: the ~9.6 km heritage greenway fully walkable/cyclable, with 12 AI scenario nodes along it.
- TOD circles: 300–800 m walking sheds of Xizhimen / Dazhongsi / Zhichunlu / Wudaokou cover the three cores.
- Road hierarchy: arterial – secondary – branch; slow-mobility first, fine-grain network inside the corridor.
- Blue-green network: Xiaoyue River (east) and Qinghe River (north) + park green 1401 / protective green 1402 / squares 1403; green ratio 22.55%, public space 11.31%.
- Waterfront: Qinghe cultural green waterfront hosts the north-core R&D living room and overlook.

AI Scenarios & Pilgrimage Landmarks

AI 场景与朝圣地标

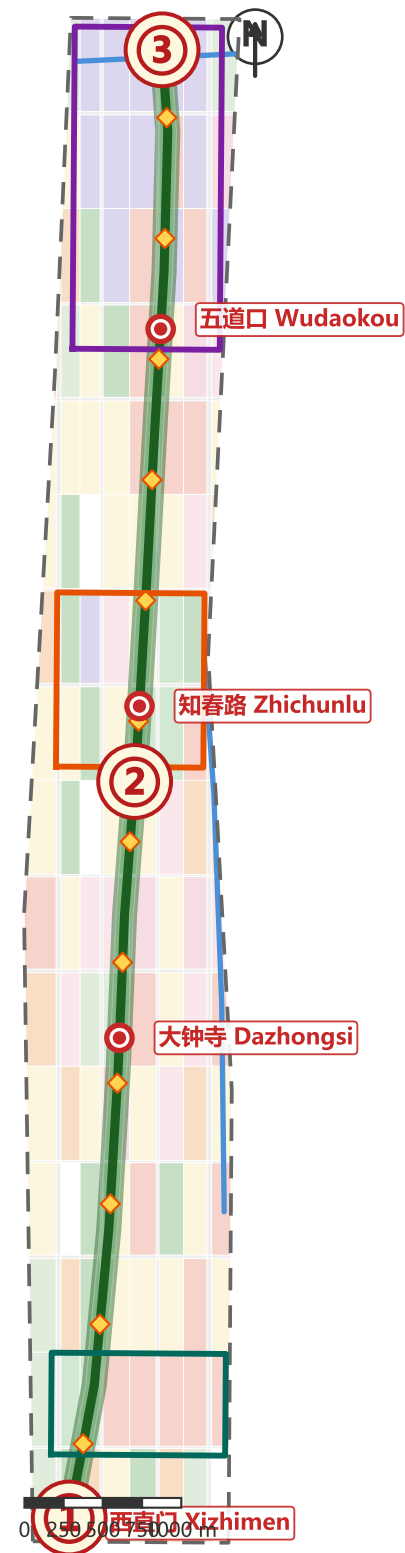




Three Pilgrimage Landmarks (south → north)

- ① Jing-Zhang Memory Gate — south gateway, start of the heritage narrative
- ② AI Origin Plaza — mid-corridor civic living room of innovation
- ③ Qinghe Valley Overlook — north end panorama over the Qinghe riverfront

12 AI scenario nodes along the spine: AI commute carriage, heritage AR interpretation, autonomous delivery corridor, smart running track, AI market, forest classroom, data garden, low-carbon station, community computing kiosk, maker rooftop, night-light track and waterfront overlook (concept scenarios).

Metrics • Phasing • Compliance Summary

指标体系 · 分期实施 · 合规摘要

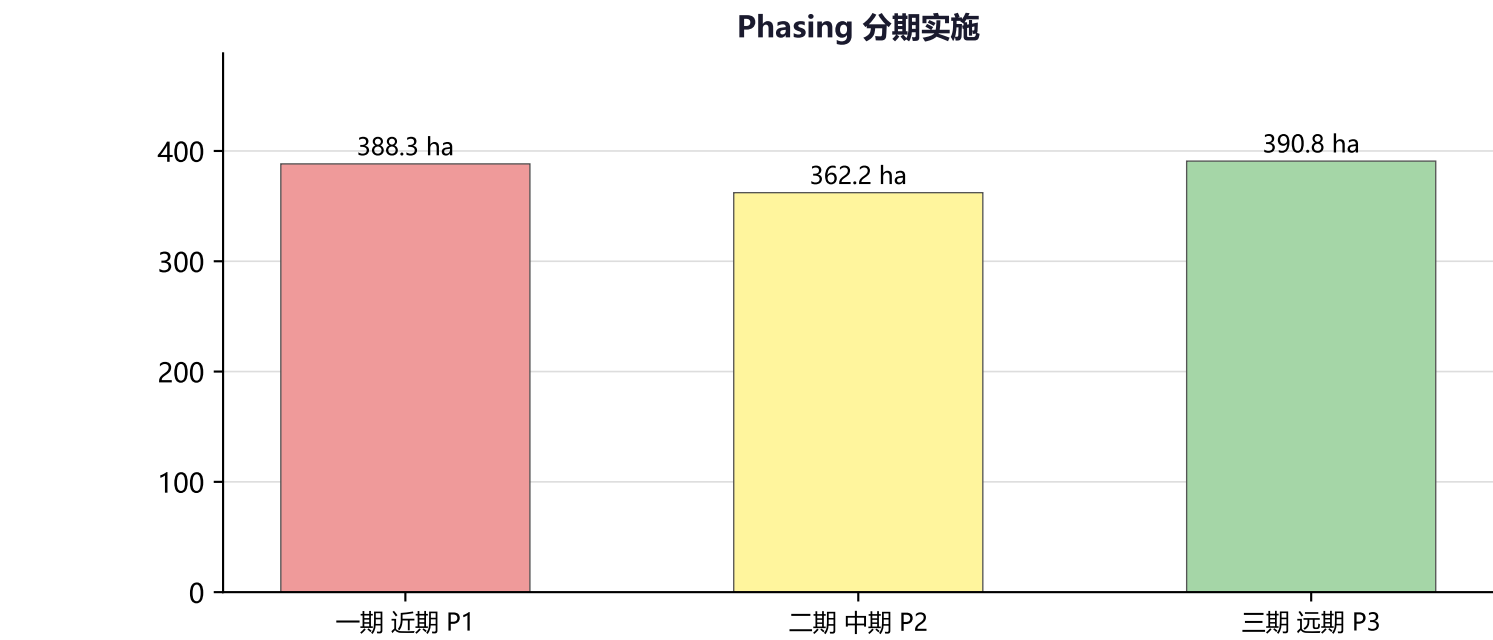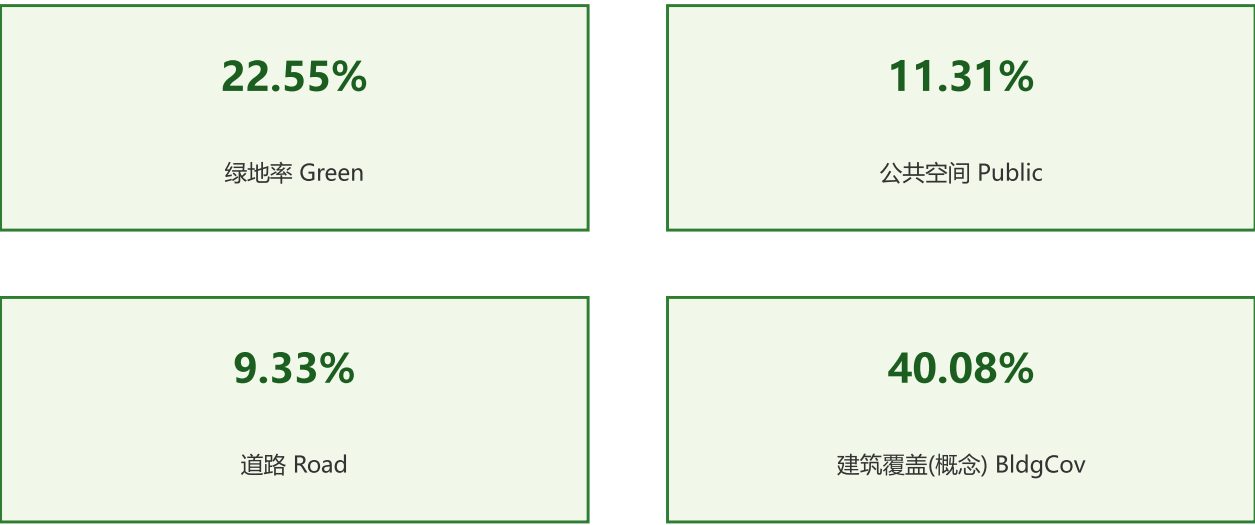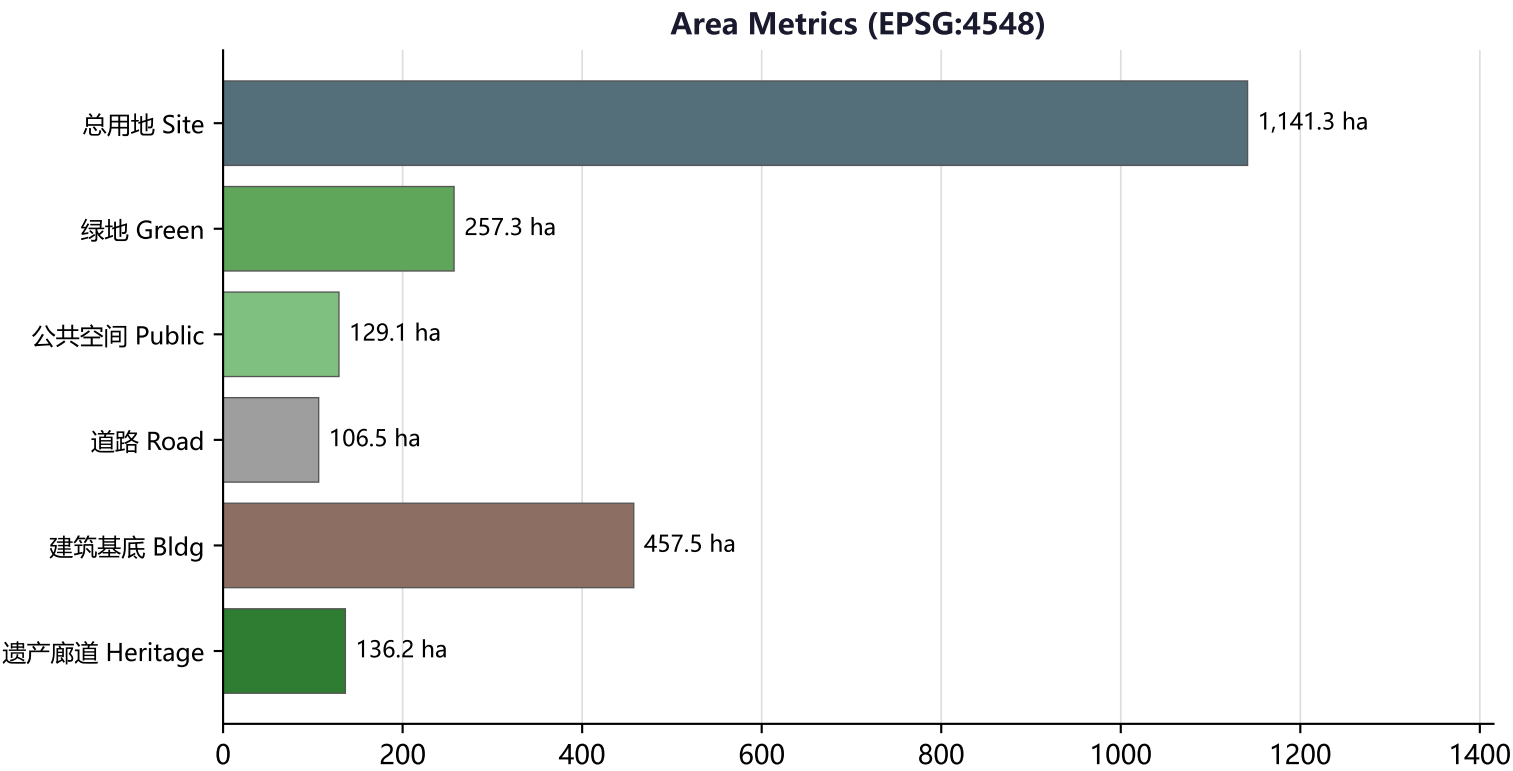

Compliance & Self-check Summary

- Task coverage: announcement tasks 1.3 / 1.4 / 1.5 and agent.1–agent.6 all mapped in compliance / design-depth / standard matrices.
- Four-gate self-check (self_check.json): determinism, spatial review, visual packaging, professional evidence — all passing locally.
- Standards: MNR land-use classes and announcement depth addressed.
- Data gaps: statutory FAR / height controls missing (status=unknown); to be recomputed once official data arrives — nothing invented.
- Evidence chain: geometry → metrics.json → matrices → self_check.