


何以京张：The Openline 100

海淀京张遗址公园走廊城市设计提案 · A3 图版册


本册为图版集：24 张图版，全部基于真实 OSM 城市肌理与提案几何数据重新渲染。
完整论述文本见 proposal.md / proposal.en.md 与 report/proposal.html。
图纸规范：Sasaki v1.2 图面标准（色板 / 字阶 / 比例尺 / 指北针 / 图签）。

Openline 100 Studio · kenshin-ai-101 · 2026-08 · v1.2

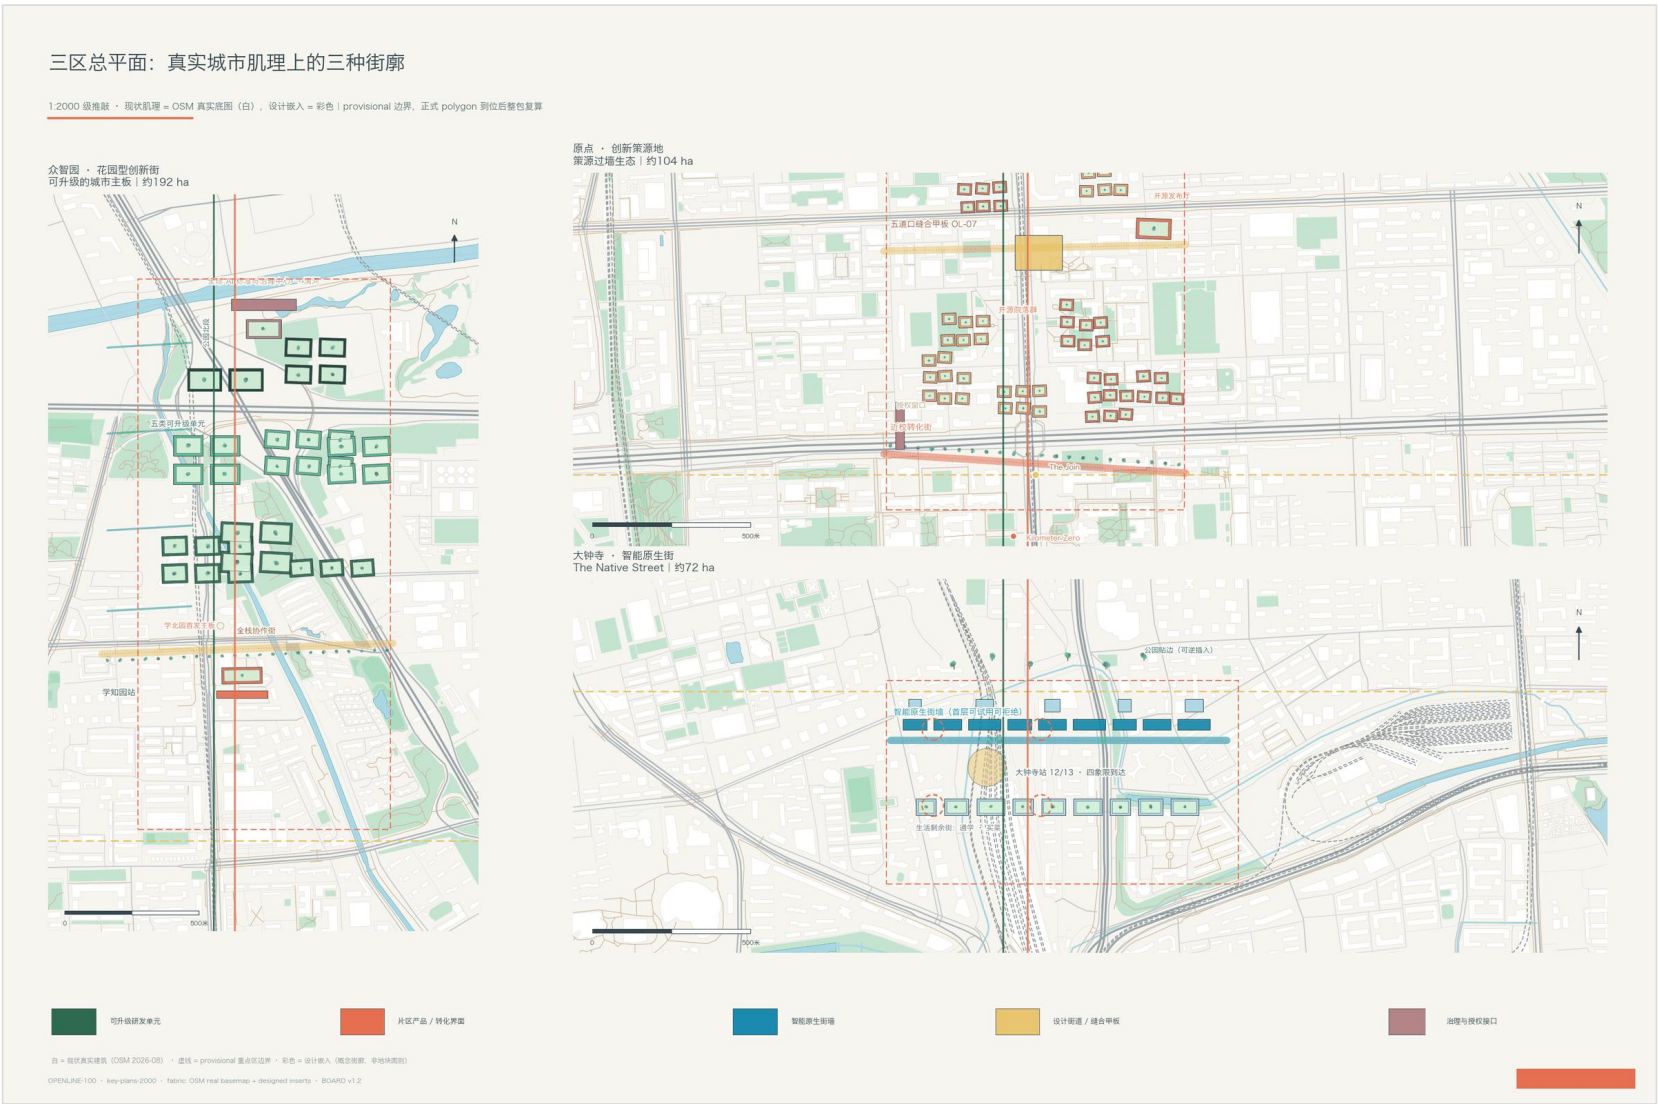


五层如何叠成一条可想象的 Openline


左：五层爆炸图（南→北 = 左→右） · 右：走廊轴测（真实肌理 OSM 2026-08） | 边界 provisional

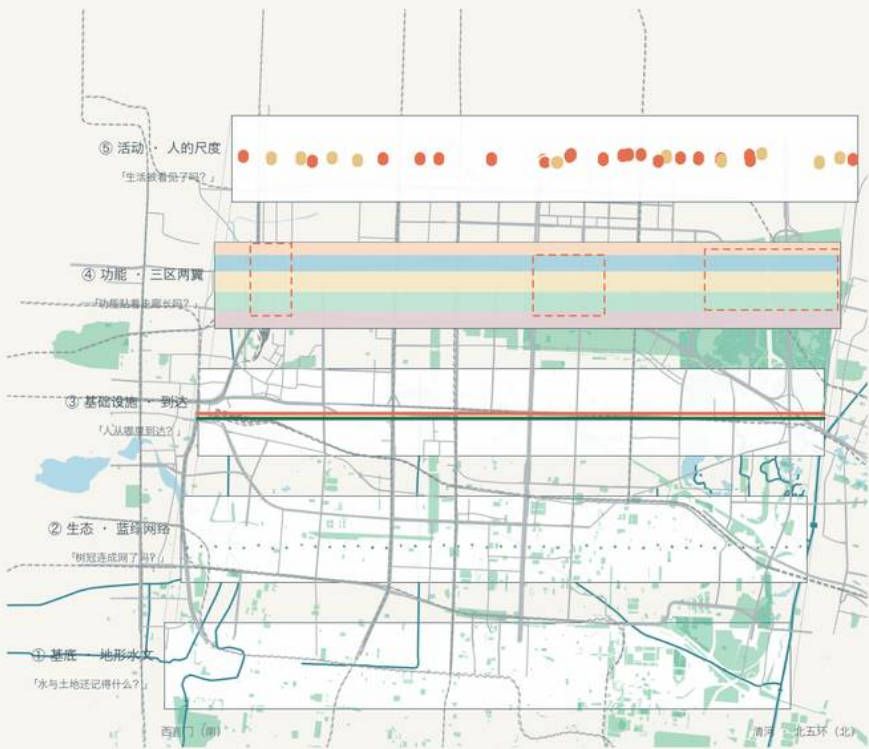

01 场地总览：五层结构 × 斜轴测走廊全貌

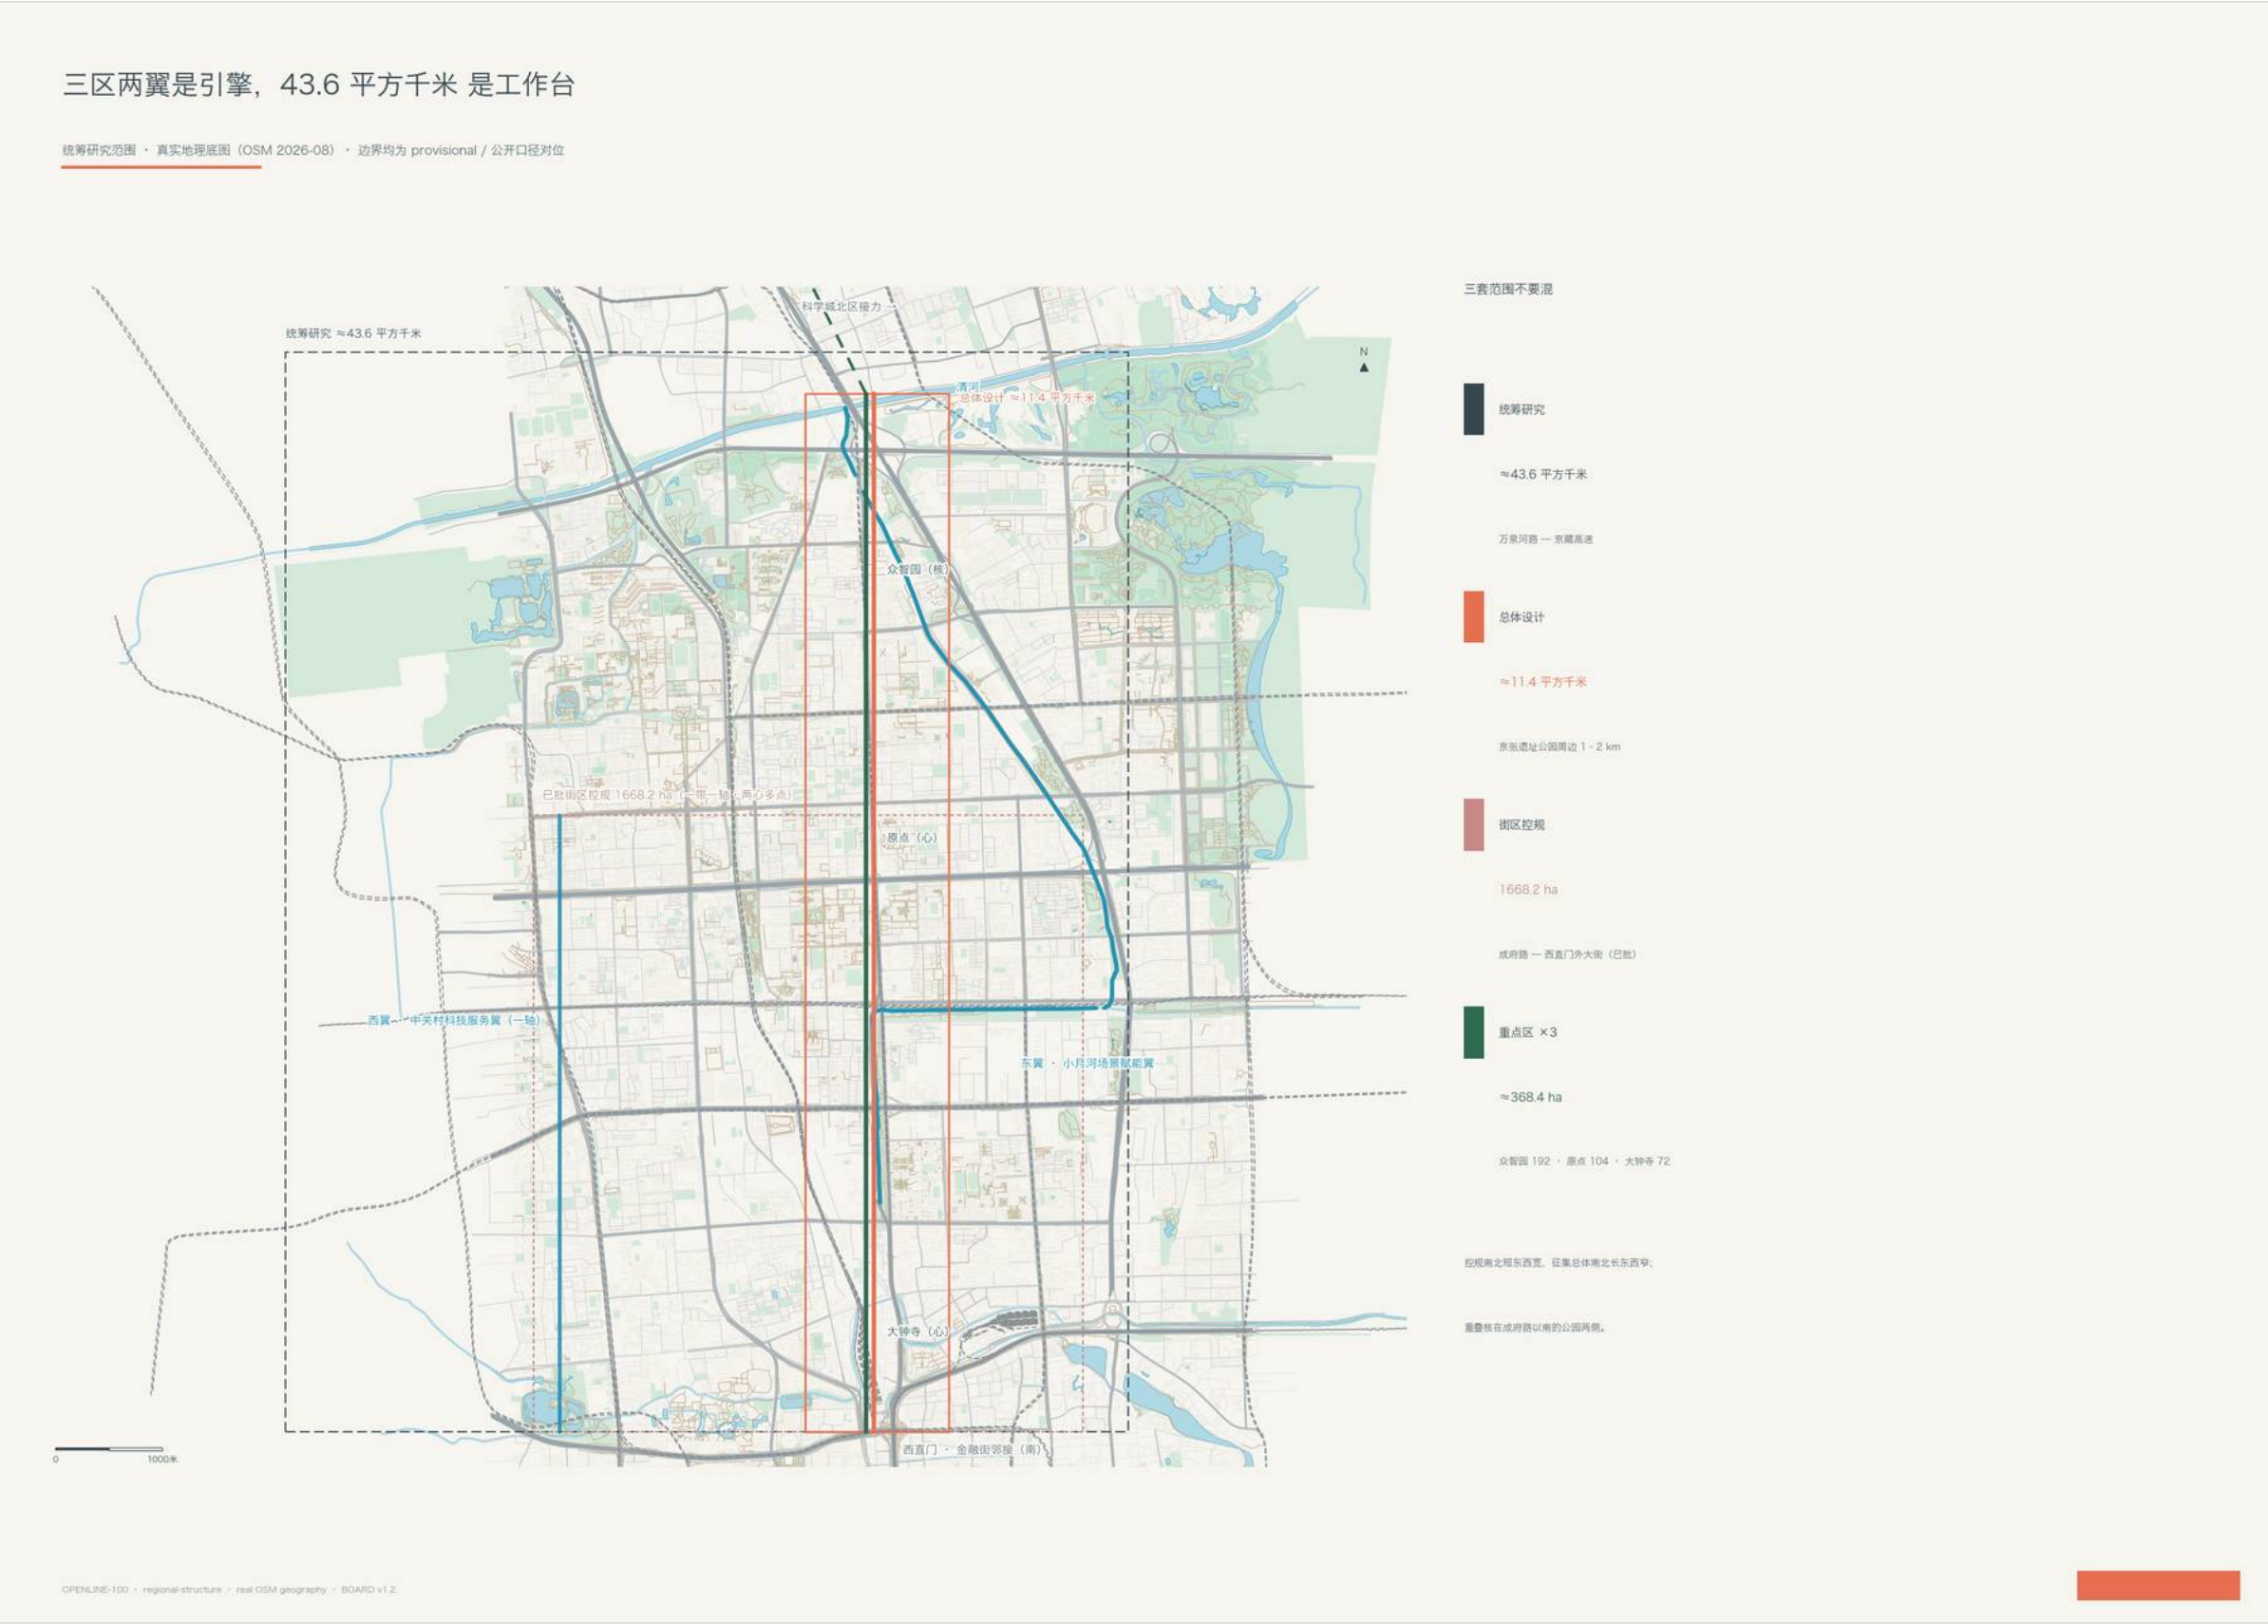


02 区域结构：京张走廊在北京西北的位置

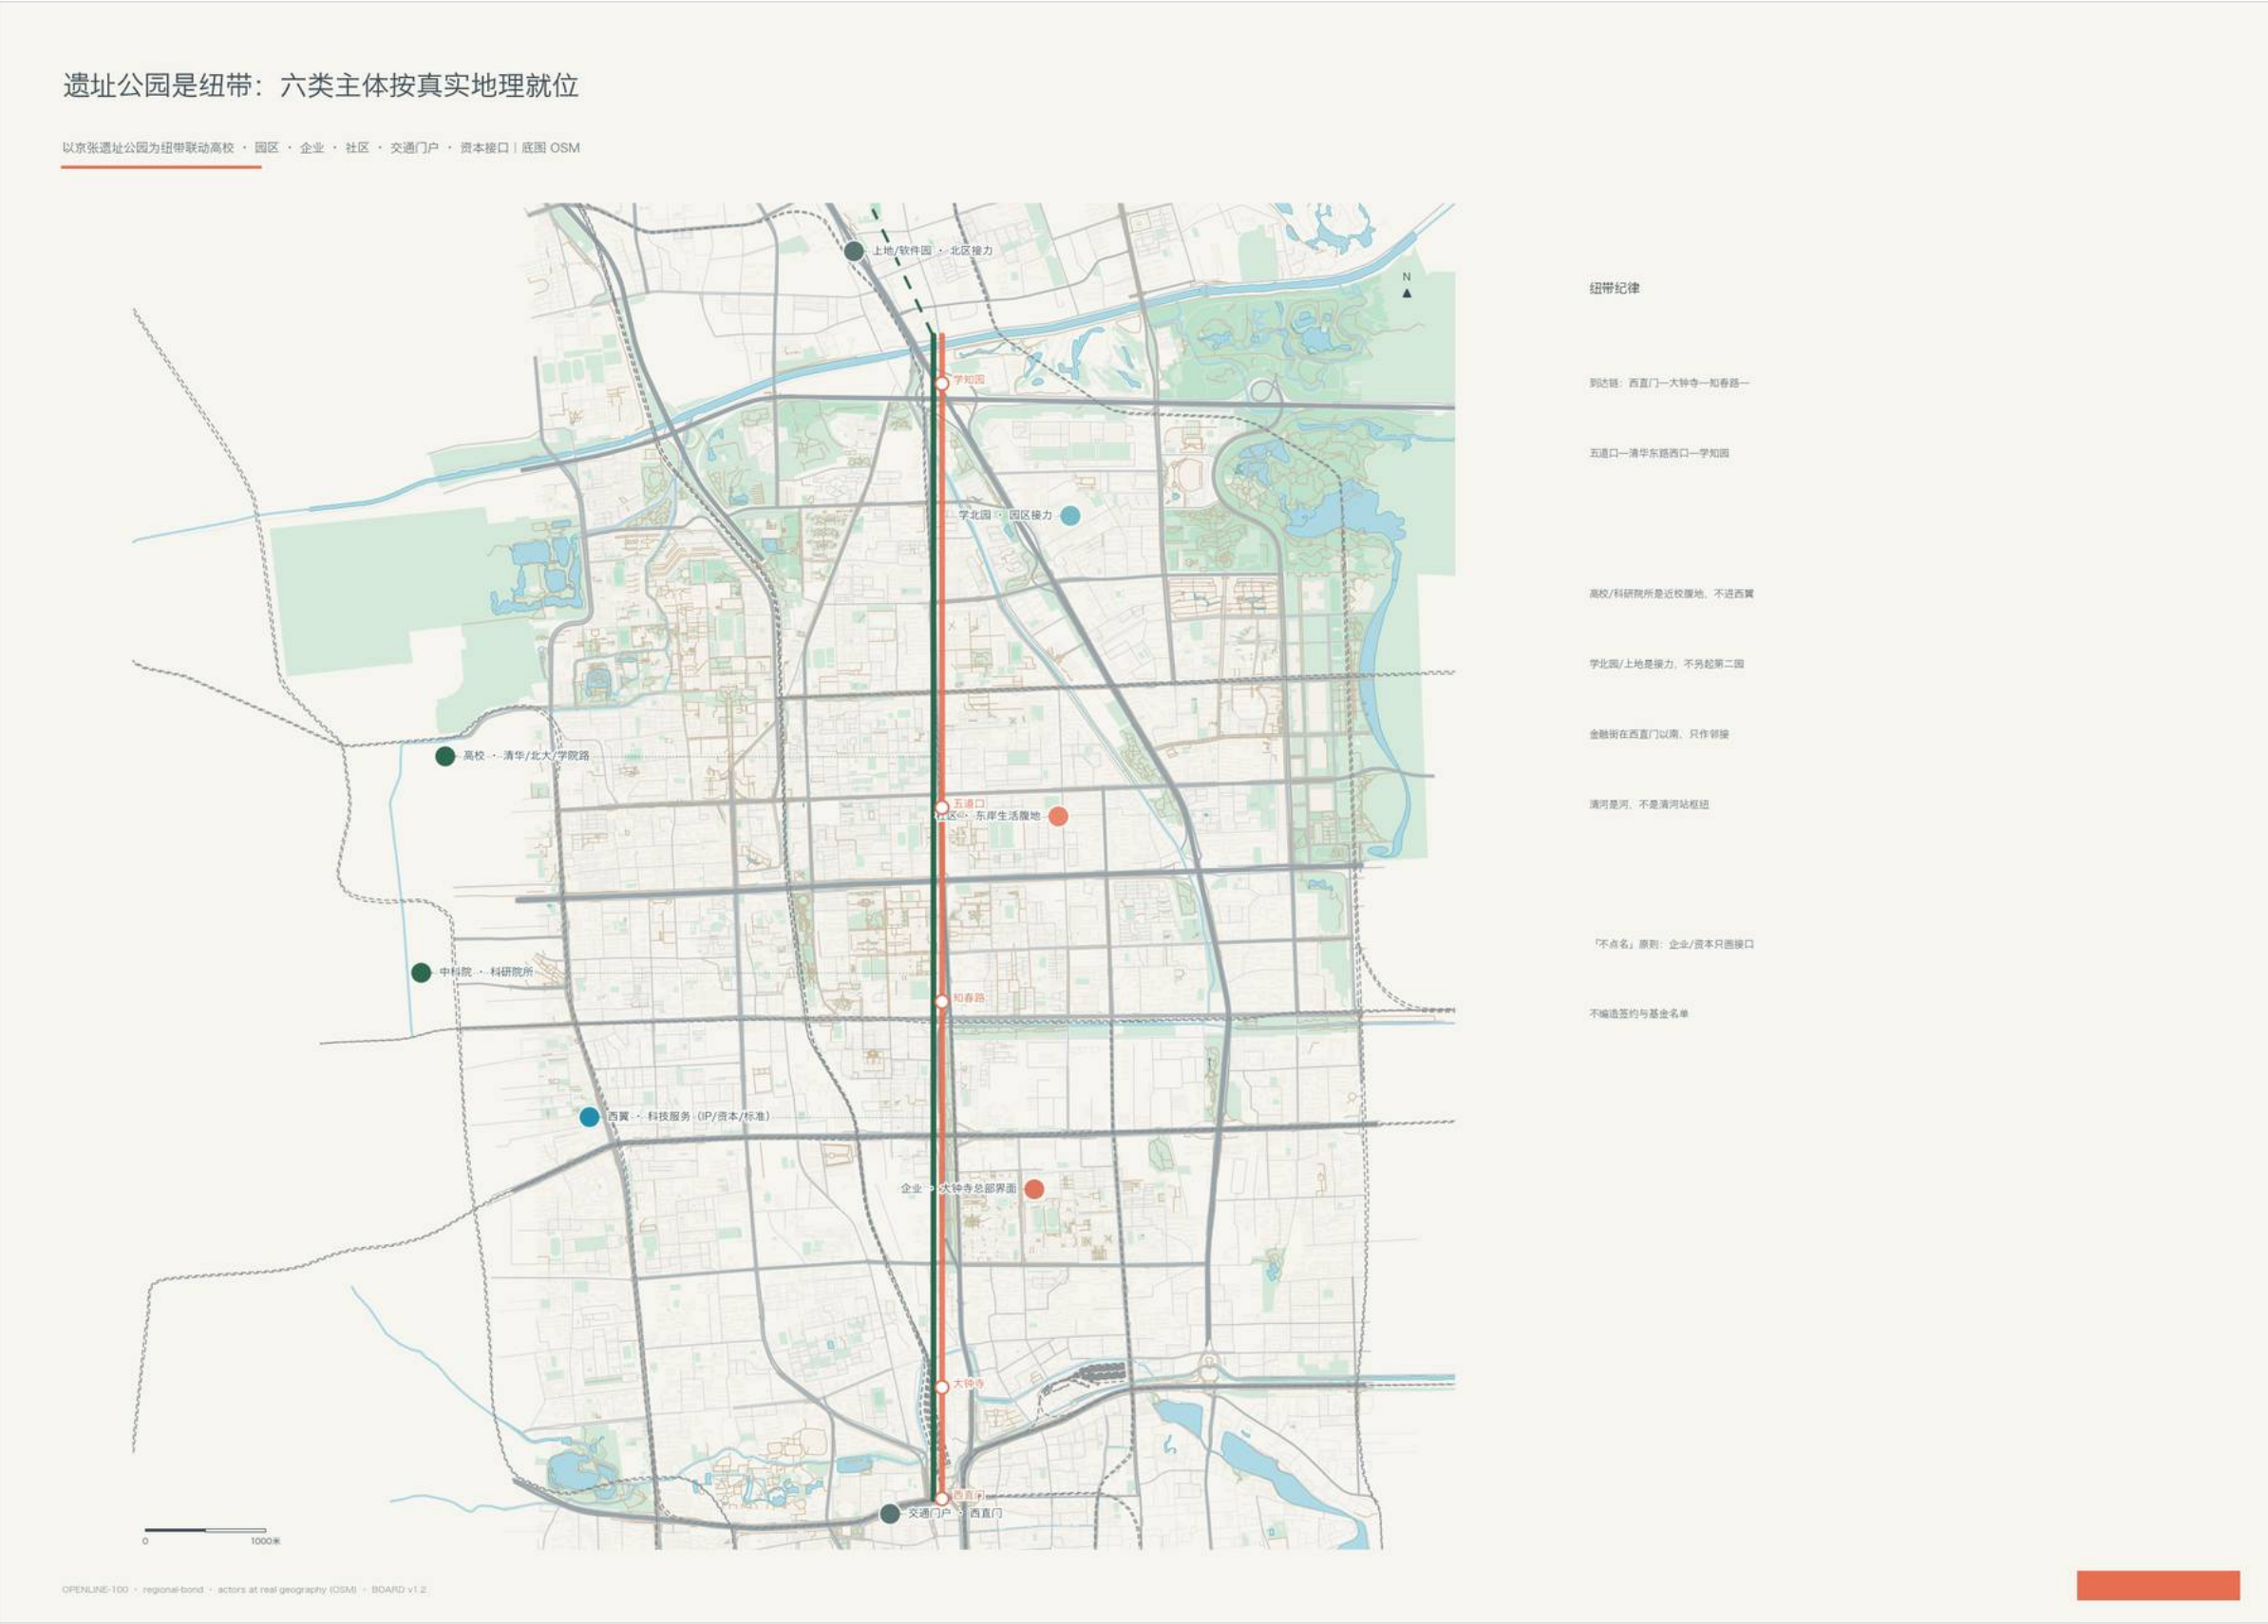

03 区域纽带：高校—科创—文化资源连结

用地分区挂在 Openline 上：廊道优先于地块填空

概念触媒分区（国土空间分类语义、非法定图则） · 底图 = OSM 真实肌理 | 面积 EPSG:4548 复算口径

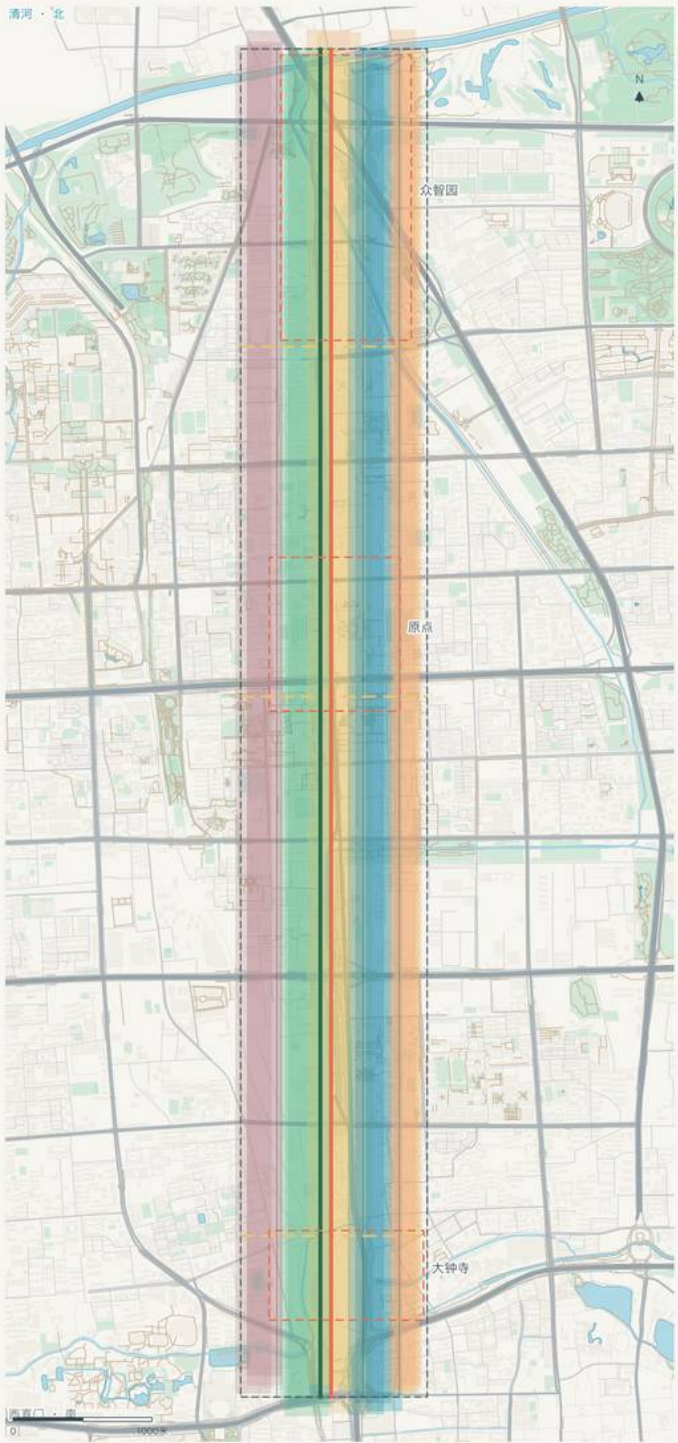

OPENLINE-100 · land-use-structure · zones washed on real OSM fabric · BOARD v1.2

分区	代码	面积 ha	占比	Openline 角色
LU-001 西岸研发与协作带	0802	≈138.3	12.1%	全栈研发 · 评测 · 开放提问
LU-002 Openline 蓝绿公共群	1401	≈258.6	22.7%	遗址公园活力带 · 承载 L1/L2
LU-003 文脉与公共文化界面	0803	≈220.1	19.3%	L1 两侧遗产叙事界面
LU-004 南端智能原生街	05	≈297.8	26.1%	智能体/终端/内容消费
LU-005 东岸社区服务与生活配套带	0702	≈226.5	19.8%	人才生活 · 近校转化


合计 ≈1141.3 ha · 100% (与提交边界闭合, 误差 <0.1%)

校验行

- 概念绿地 ≈227.8 ha (20.0%) · 公共空间 ≈90.1 ha (7.9%)
- 概念建筑基底 48.2 万 m² (≈4.2%) = 节点包络占位, 非法定密度
- 不把 1668.2 ha 控规范围与 1141 ha 提交足迹混算
- 正式图则到位后整包复算, 区间上限服从图则

三区为何不是同一套园区模板

同一 Openline 语法 · 三种制度 / 断面 / 公共组件 / 场景入口 | 底图 = OSM 真实肌理

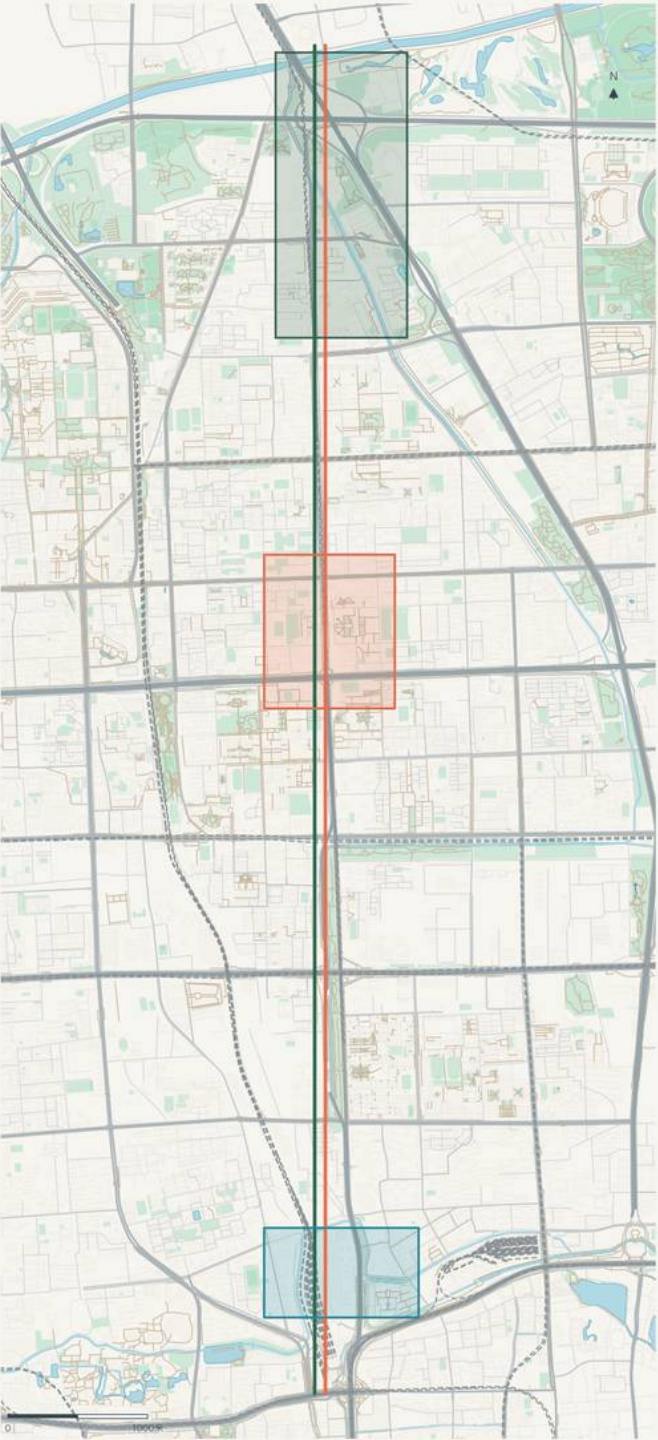

OPENLINE-100 · key-areas · three district products on real fabric · BOARD v1.2

众智园 · 花园型创新街 ≈192 ha

可升级的城市主板：共享底板 + 五类单元 + 全线协作街 + 治理中心

控规地位：征集必做 · 本份控规公开四至未覆盖

少一步即毁：底板不稳则换代筑城

原点 · 创新策源地 ≈104 ha

策源过墙生态：授权窗口 + 八找并置 + 开源发布 + 微场景 + 失败案例库

控规地位：两心之一（五道口）

少一步即毁：无授权窗口则策源还在墙上

大钟寺 · 智能原生街 ≈72 ha

The Native Street：首层业态协议 + 站城四象限到达 + 数据会客

控规地位：两心之一（大钟寺）

少一步即毁：无说明条则街道是广告街

三区共用 Openline 语法，但制度、断面、组件、场景入口各不相同。

矩形边不是地块红线 —— provisional，正式 polygon 到位后重算。

1:2000 级推鼓 · 现状肌理 = OSM 真实底图 (白), 设计嵌入 = 彩色 | provisional 边界, 正式 polygon 到位后整包复算

片区产品 / 转化界面

设计街道 / 缝合甲板

治理与授权接口

白 = 现状真实建筑 (OSM 2026-08) · 虚线 = provisional 重点区边界 · 彩色 = 设计介入 (概念规划, 非地块规划)


OPENLINE-100 • key-plans-2000 • fabric: OSM real basemap + designed inserts • BOARD v1.2

06 1:2000 三重点区总平面 (真实 OSM 城市肌理)

体量服从街廓，天际线不另立塔

上排：三区白模轴测（体量 = 概念区间，z 轴略夸张）· 下条：沿公园南→北天际线剖面


众智园 · 18 - 36 m 花园型院落（体量服从街廓）

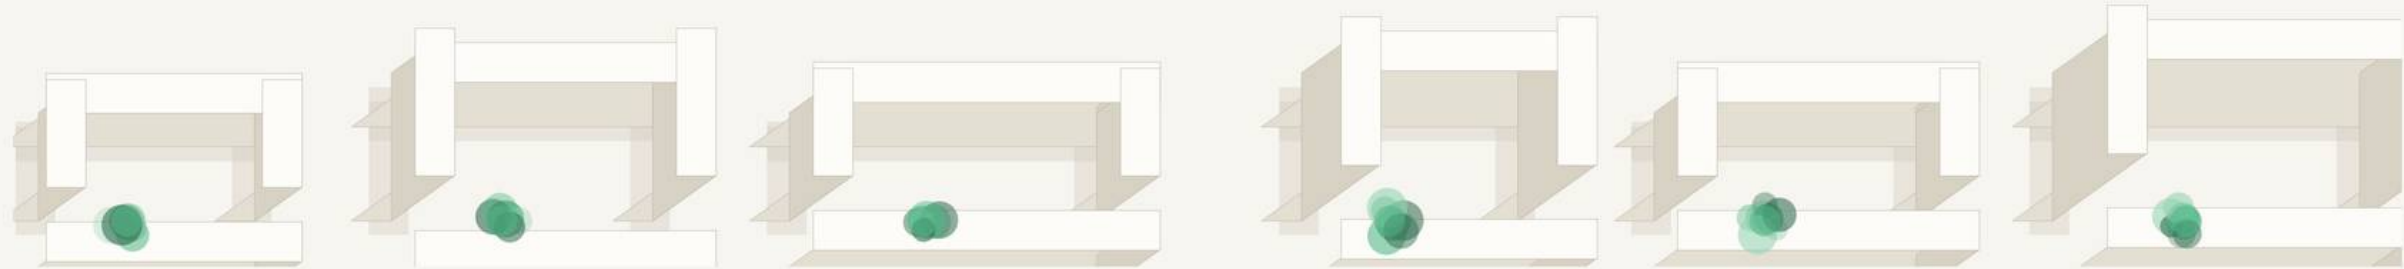

原点 · 近校压低 ≤45 m（小肌理开源院落）




大钟寺 · 街墙连续 24 - 36 m，服从既有总部体量

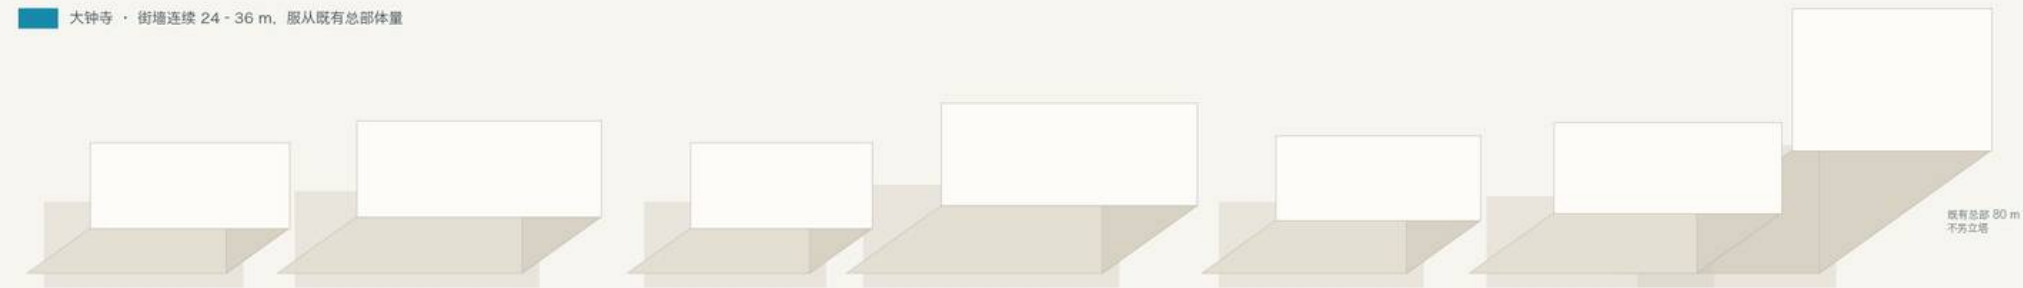

既有总部 80 m
不另立塔

沿公园南 → 北：不另立塔，天际线让位树冠

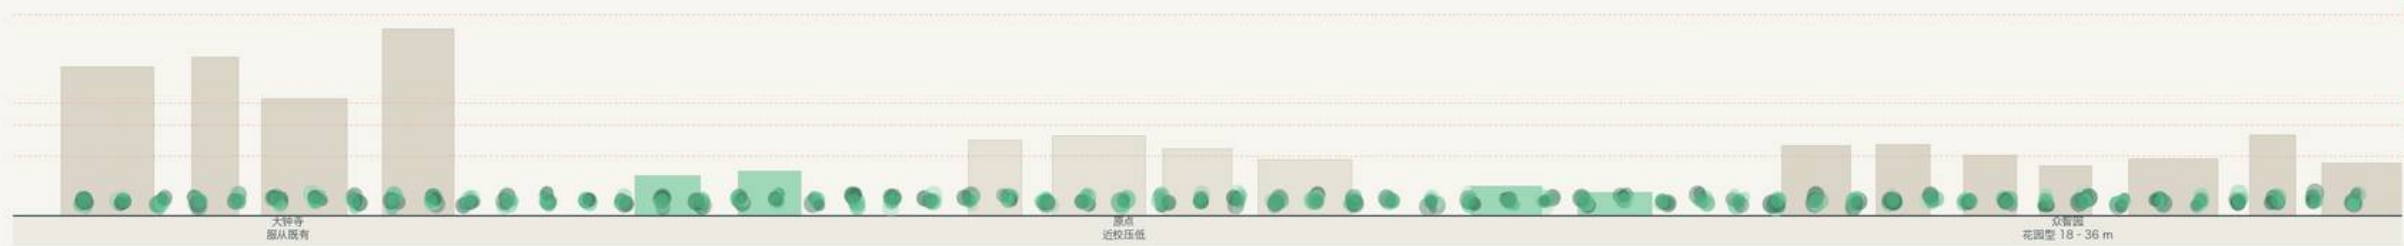

OPENLINE-100 · key-massing-skyline · concept heights, caps yield to official parcels · BOARD v1.2

07 体量与天际线控制


六条典型街道，一种 Openline 语法

断面系列 A - F · 非工程设计 · 步行路权全时 ≥50% · 机器带永不升级为机动车道

A · L1 证据线 (轨可走)



B · L2 服务线 (驿站可挂)

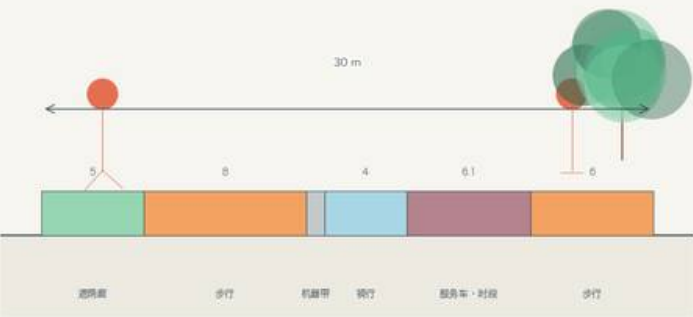

C · 协作街 (物流在背街)




D · 转化街 (窗口贴边)



E · 原生街面 (试用/生活分行)



F · 甲板 (电/人/景三层)

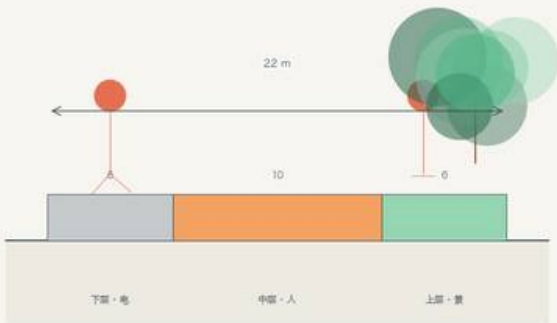


OPENLINE-100 · key-sections · walking ≥50% always · BOARD v1.2

五处地点，切开就能认

地点剖面（非符号街）：院落/授权窗口/三层甲板/站到达/清河界面 · 与「走进」氛围图对话


01 众智园 · 院落与公园带

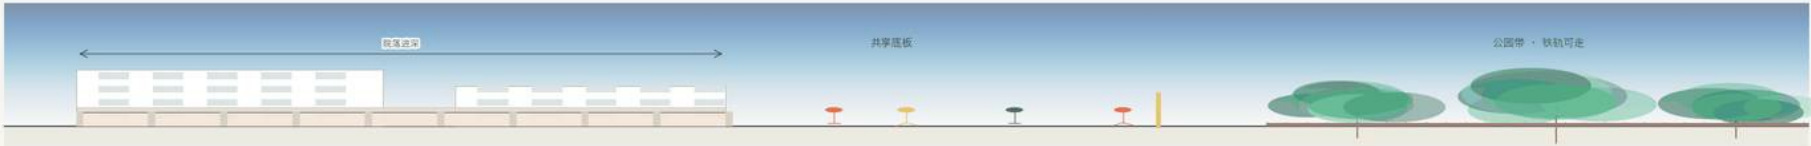


02 原点 · 授权窗口与 KM0



03 五道口 · 三层缝合甲板

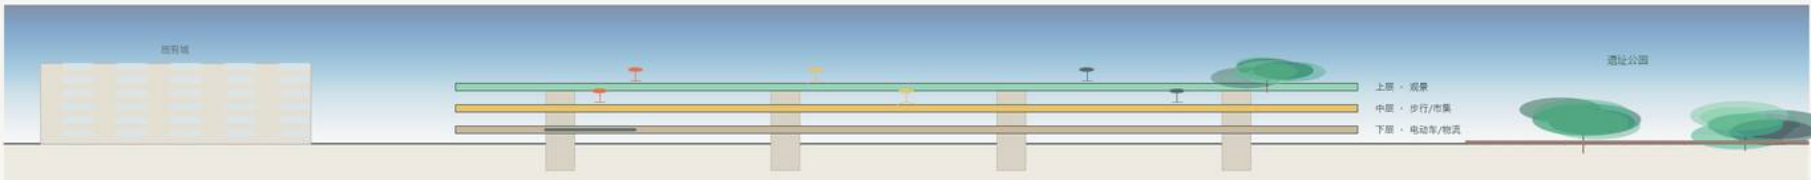

04 大钟寺站 · 只做到达

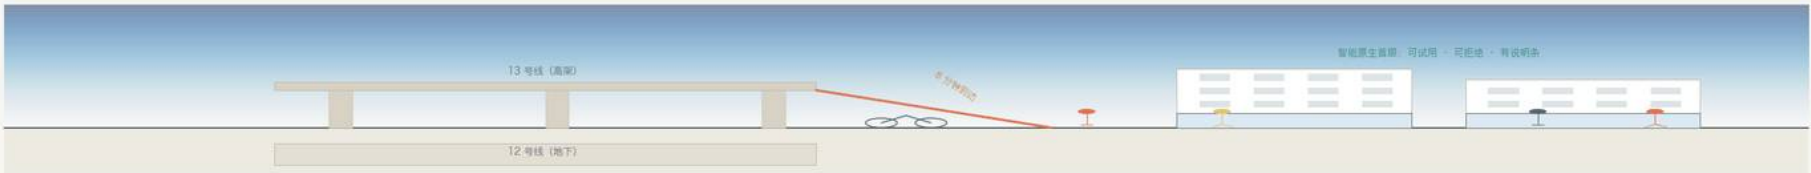

05 清河 · 治理面河界面



读法

每张都是

切开的地：

有墙、有轨、

有水、有人、

不是一点透视

的符号街。

深度 = 制度在

剖面里成立：


可加入 · 可核验

可退出 · 可继承

OPENLINE-100 · Key-eyes · five place sections · BOARD v1.2

五道口缝合甲板：三层可逆跨线结构

利用既有桥墩逻辑 · 不发明未论证深隧 · 待红线确认后深化（概念工程，非施工图）

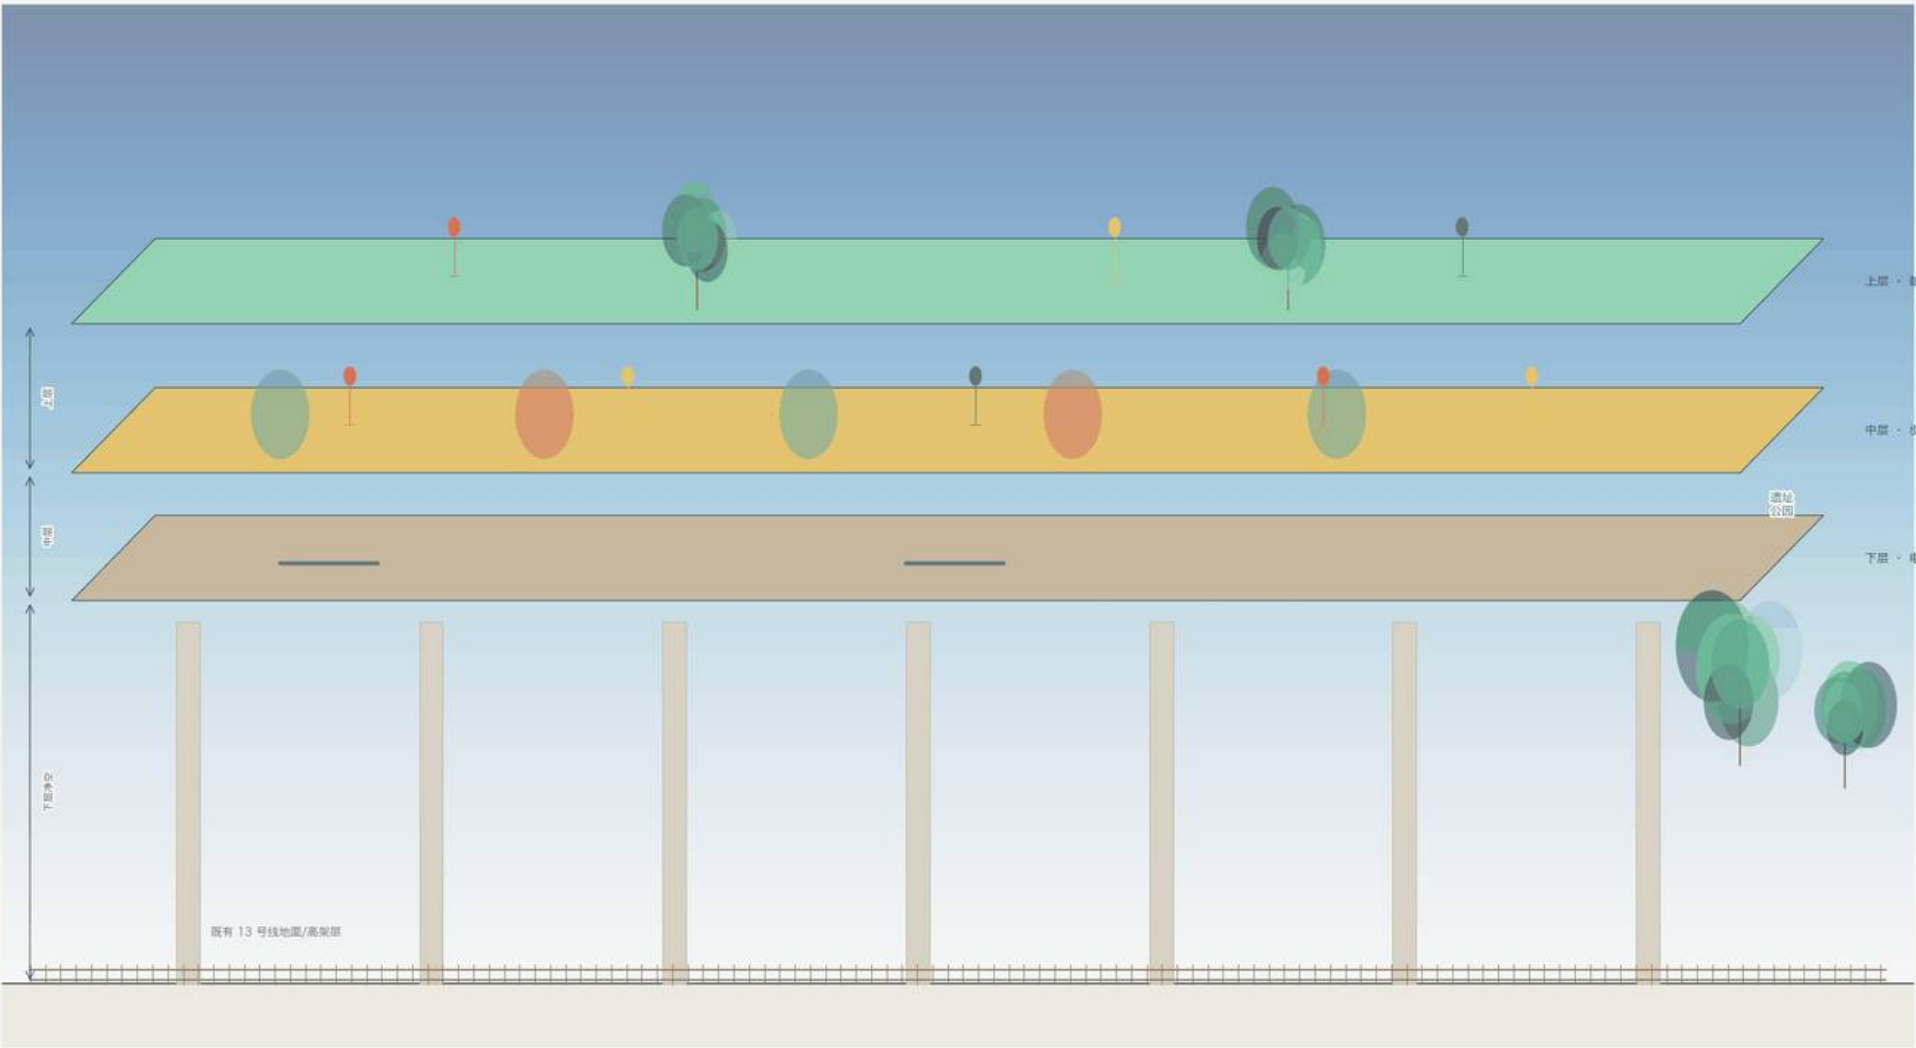

设计界气边界

○ 绘制面逻辑与

层间关系

○ 给接驳口概念位置

上层 · 胡同公园的观景

中层 · 步行与临时市集

下层 · 电动车与物流楼

× 不给跨度/荷载

× 不给施工组织

× 不冒充已批线位

B 计划：该不下桥墩

→ 独立柱 → 平面过街

强化 + 信号优先

OL-07 · 待红线确认后深化 · 概念工程，非施工图

OPENLINE-100 · wudaokou-stitch-deck · reversible 3-level structure on existing pier logic · BOARD v1.2

10 五道口缝合甲板：三层竖向

五道口缝合甲板：把最大胆的动作画成可信的日常

剖透视 · 材质 / 高差 / 真实人物 · 手绘边缘保留概念的不确定性，不冒充实景 | OL-07



11 镇版之图：缝合甲板剖透视 · 材质 / 高差 / 真实人物



12 铁轨显形：京包线线位扎进真实街廓

让铁轨长进地面：五种物质转译


组件进公共空间组件库，随 Inherit 版本化 · 声景与碑文须许可与人工审核后试点

地面层 · 轨作铺装




禁忌：不做不可达展品

叙事层 · 里程思辨碑

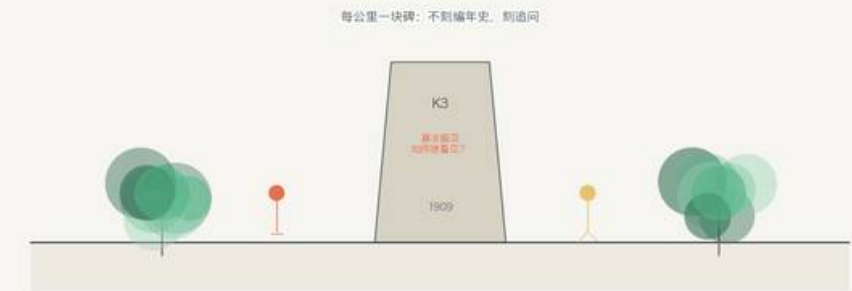


禁忌：不娱乐化京张史

剖面层 · 考古展示沟

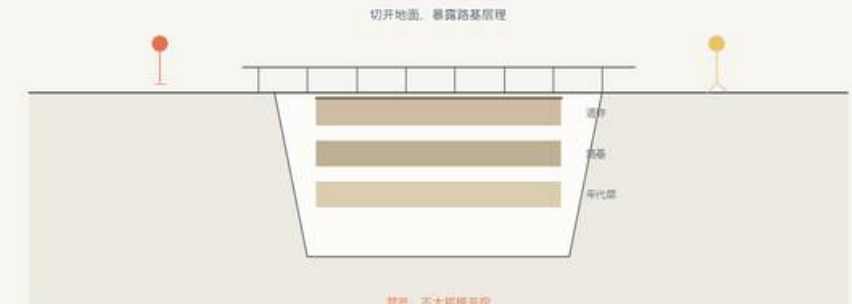

禁忌：不大规模开挖

声景层 · 蒸汽×白噪

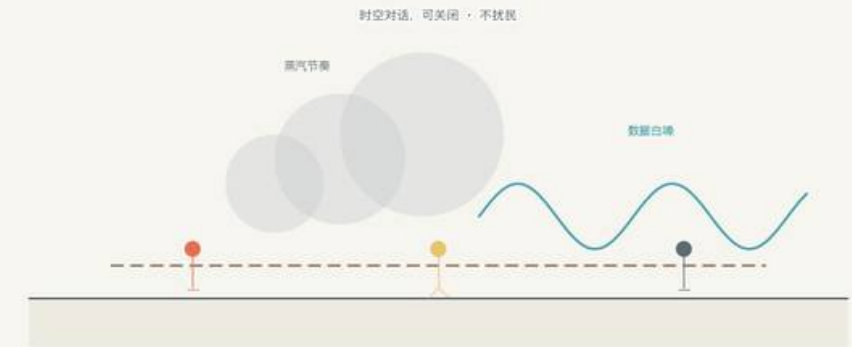

禁忌：不做噪声装置

设施层 · 轨成家具



禁忌：不伪造遗址原件


进组件库的三条规则

- ① 清权 + 安全检测之后，才谈转译
- ② 随 Inherit 版本化：可加入 · 可退出 · 可继承
- ③ 声景与碑文先试点，许可与人工审核前置

五种转译共用一条地面：轨不离地，地不离街。

遗产显魂：分级 · 口述 · 以人为轨

从保护遗产到续写京张 | 考古三级 × 口述三声 × 人字坡三次转身 | A-HERITAGE-001 方法框架

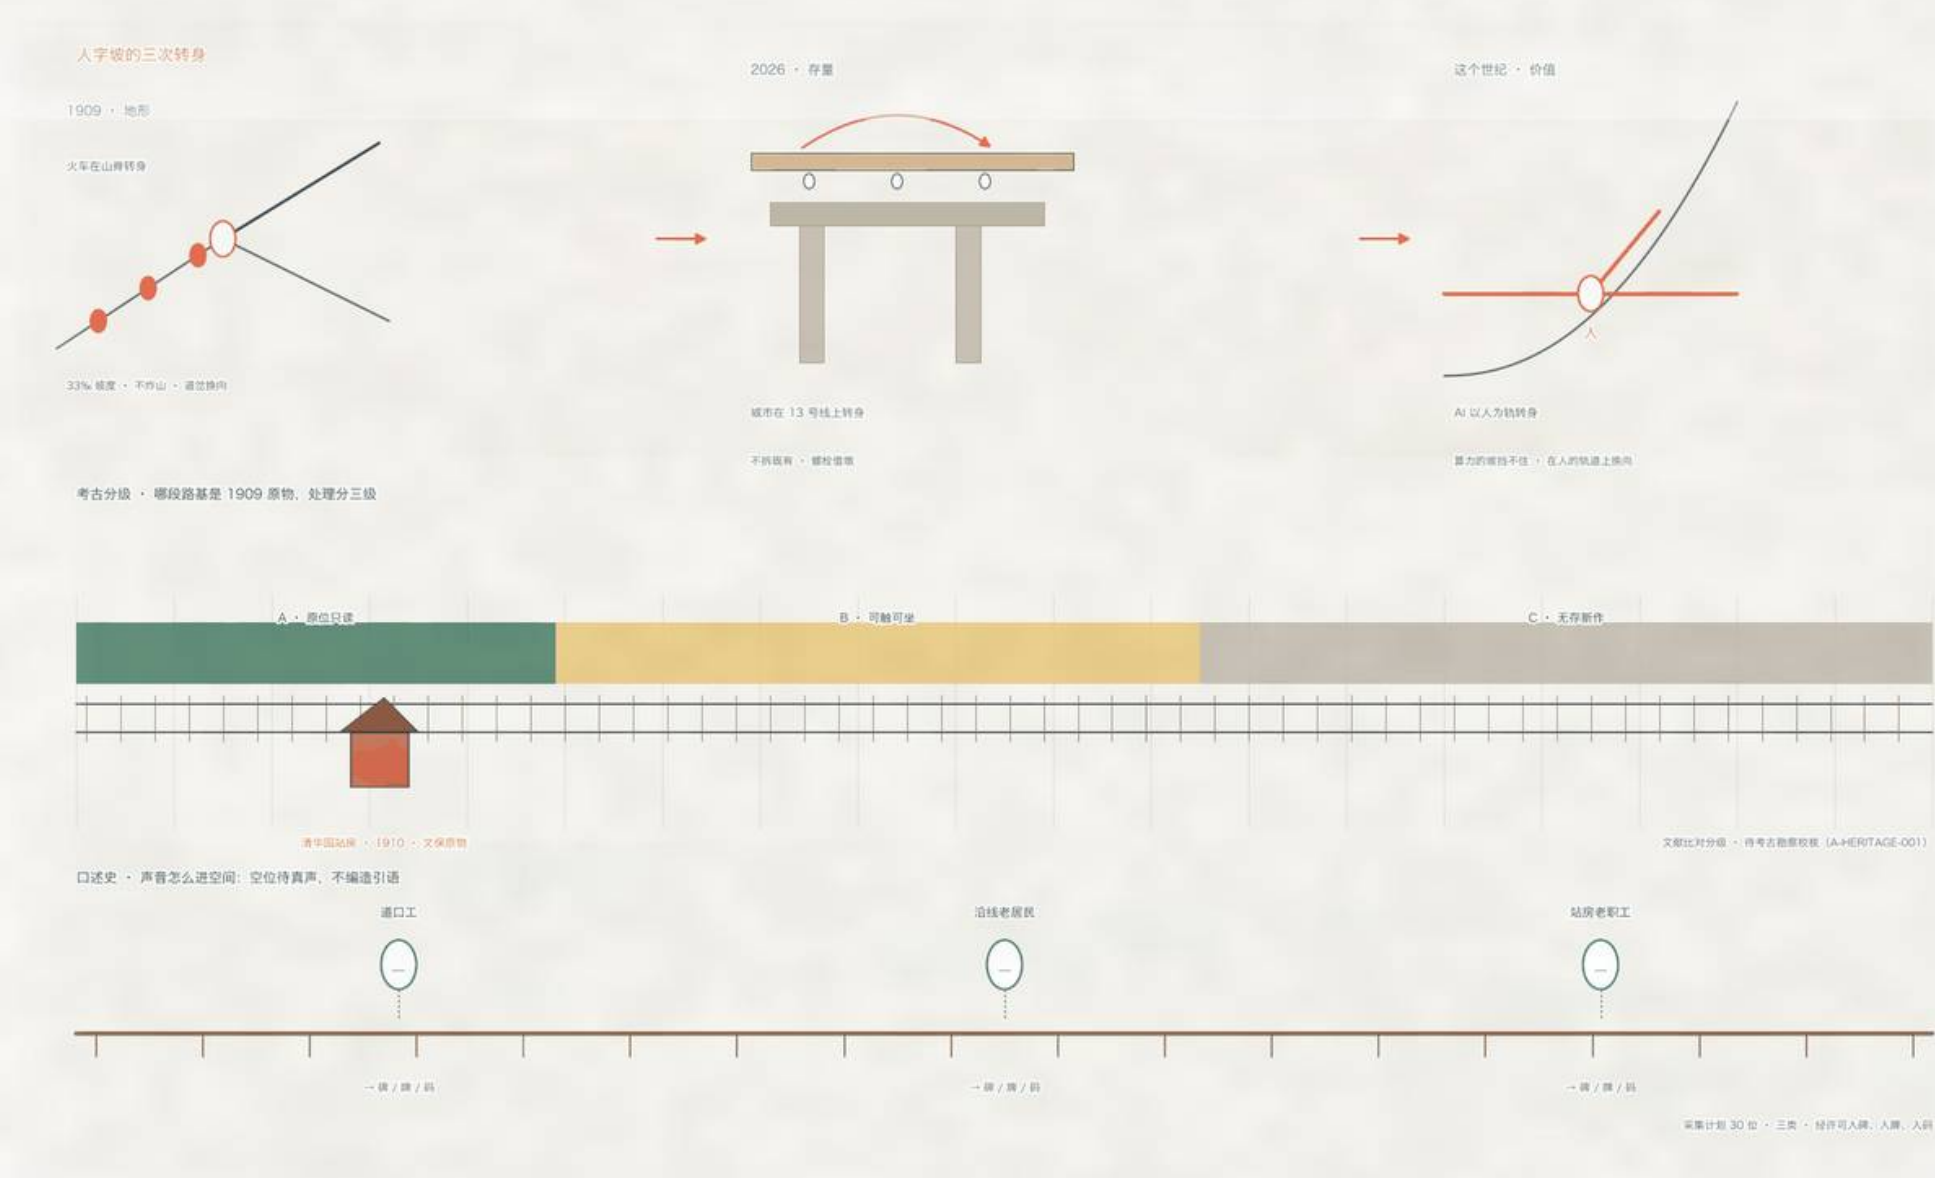

以人为轨

人字坡的「人」

1909 的「人」字，
写的是线路的形状。
这个世纪的「人」字，
写的是价值的归属。

铁路解剖学 → 当代对应物


- 道岔（转向）= 枢纽 / 退出端
- 避难线（收容失控）= 失败案例库
- 试车线（新车不上正线）= 治理沙盘
- 轨 = 人类价值系（不是算力）

三层各就各位

- 分级 · 对物（1909 原物分级处理）
- 口述 · 对人（声音经许可进空间）
- 转身 · 对时代（AI 以人为轨）


分级为文献比对框架 · 待勘察校核

口述为空白 · 待真实采集（A-HERITAGE-001）

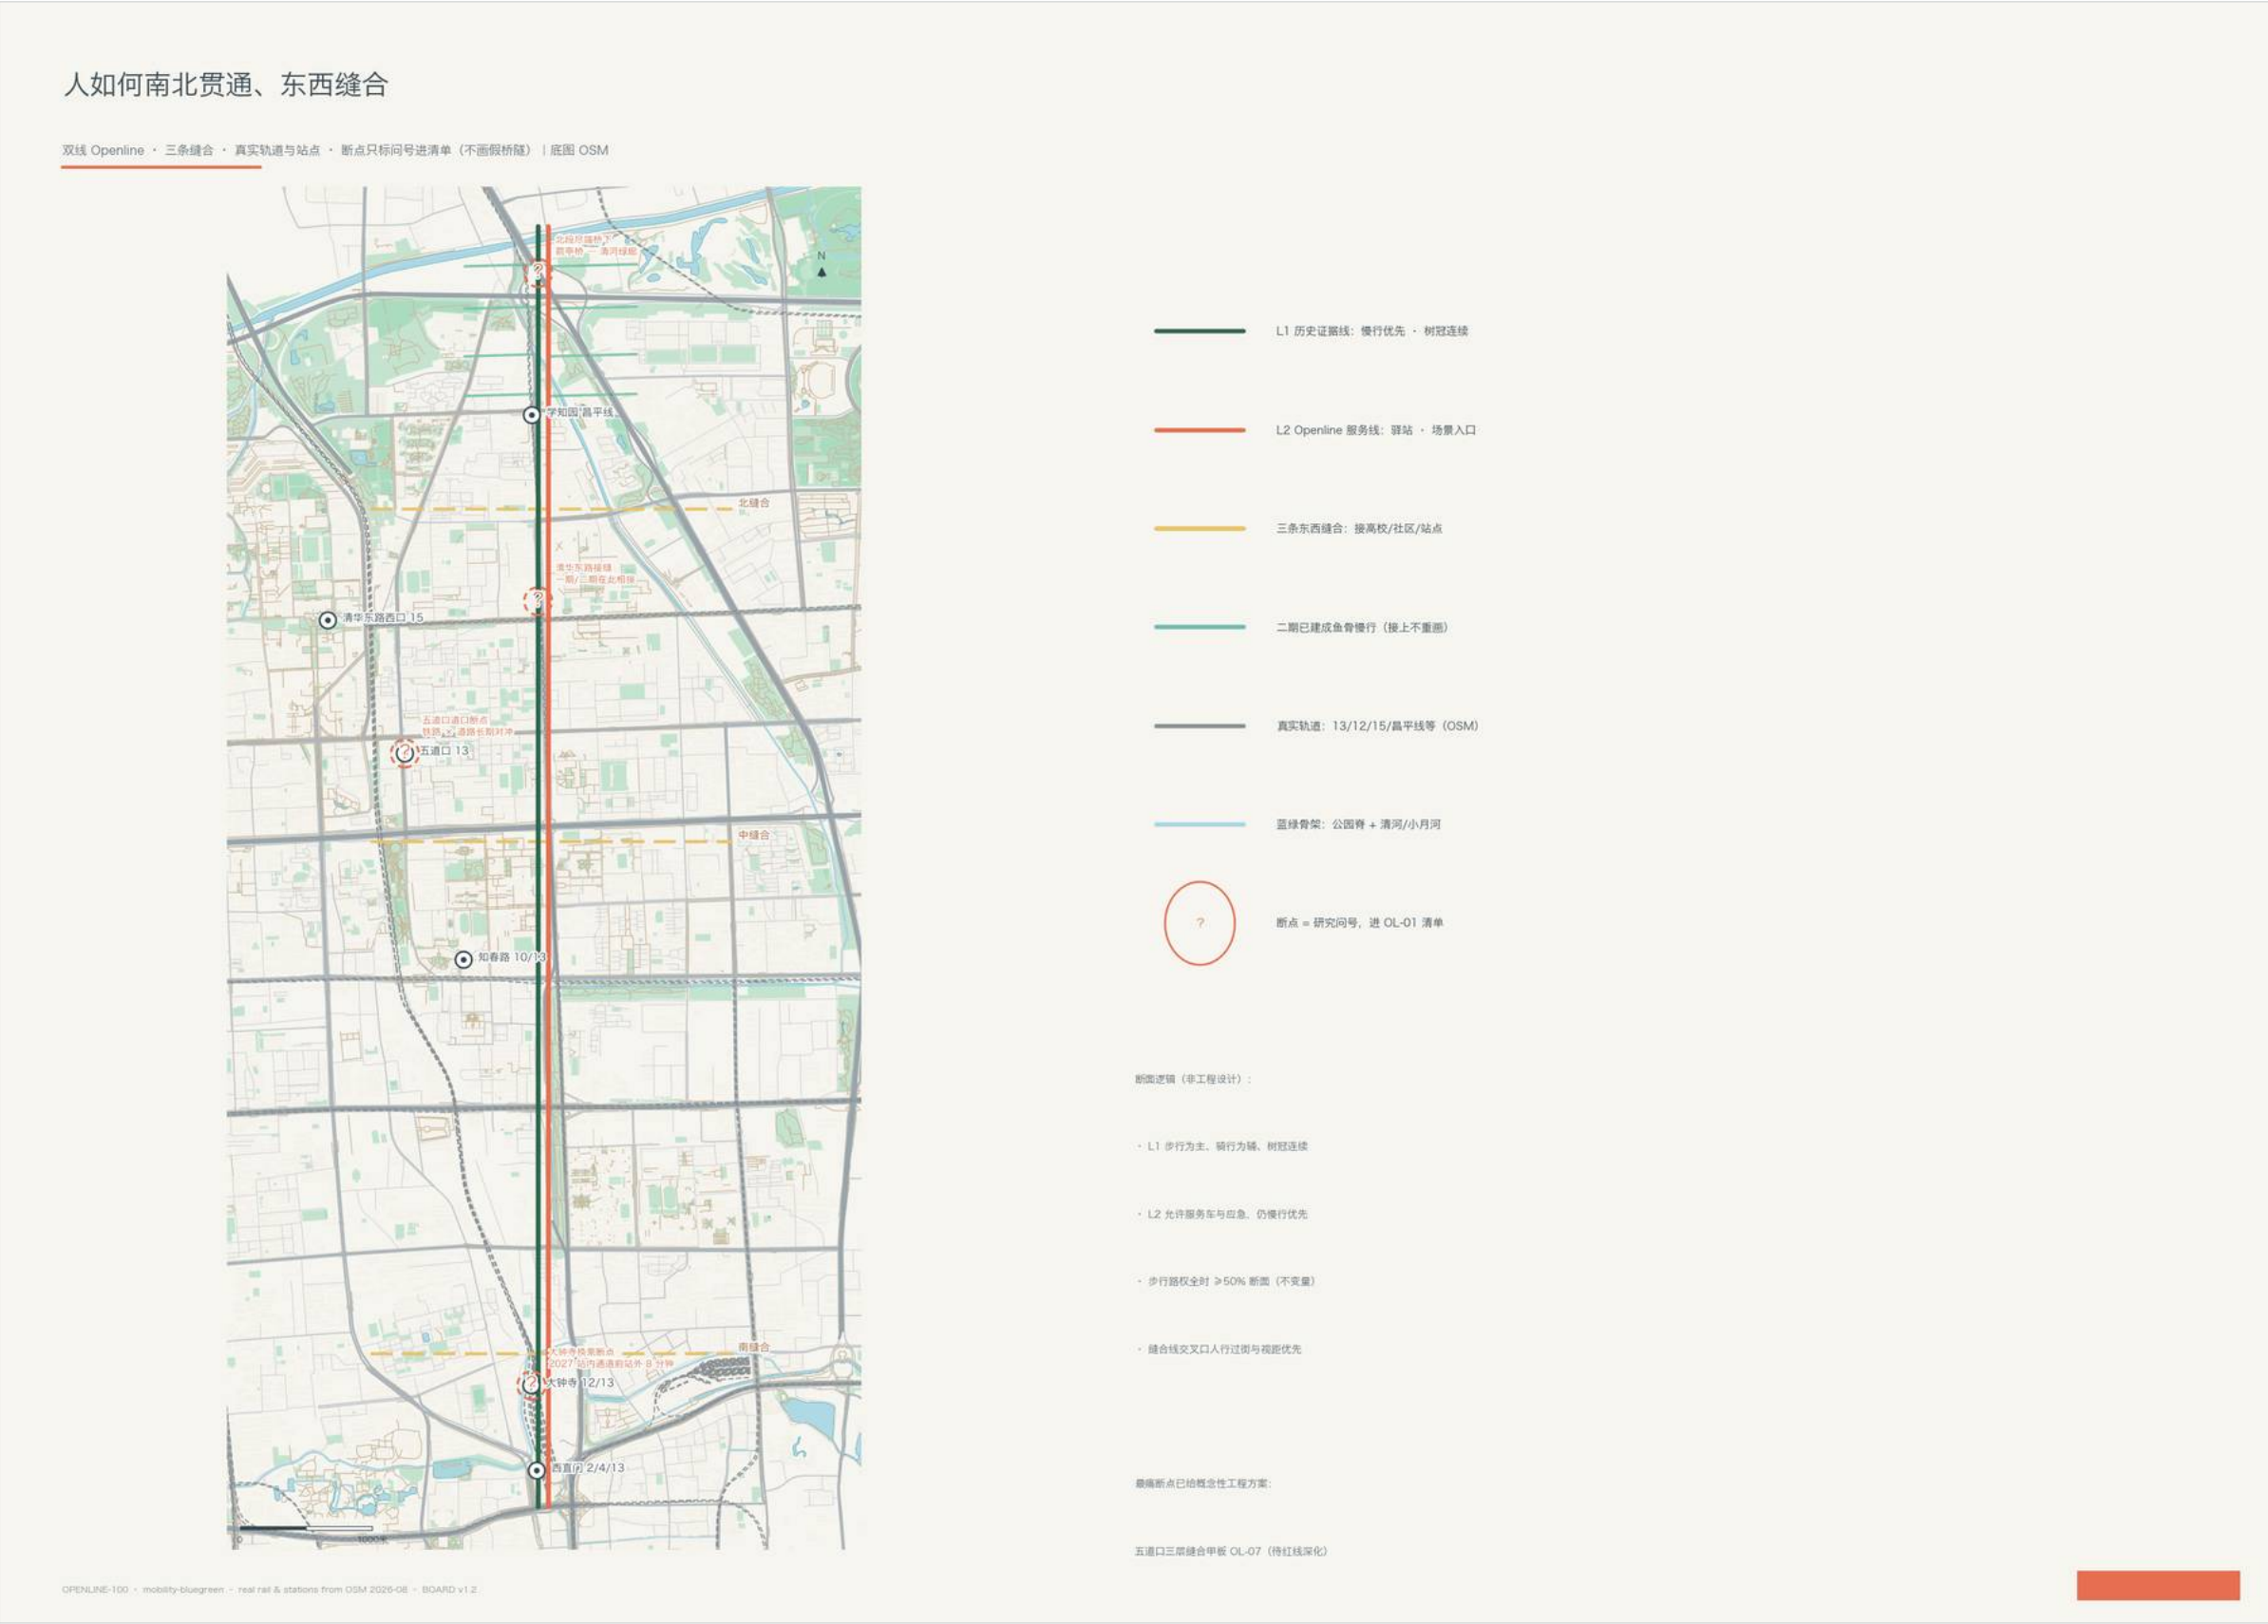

生态的数字承诺：每期可核验的目标

破预算 · 径流控制率 · 热岛降幅 · 生物多样性净增益 · 树冠覆盖 | 传感进信托, Verify 隔公开 | 目标承诺 A-ECO-001

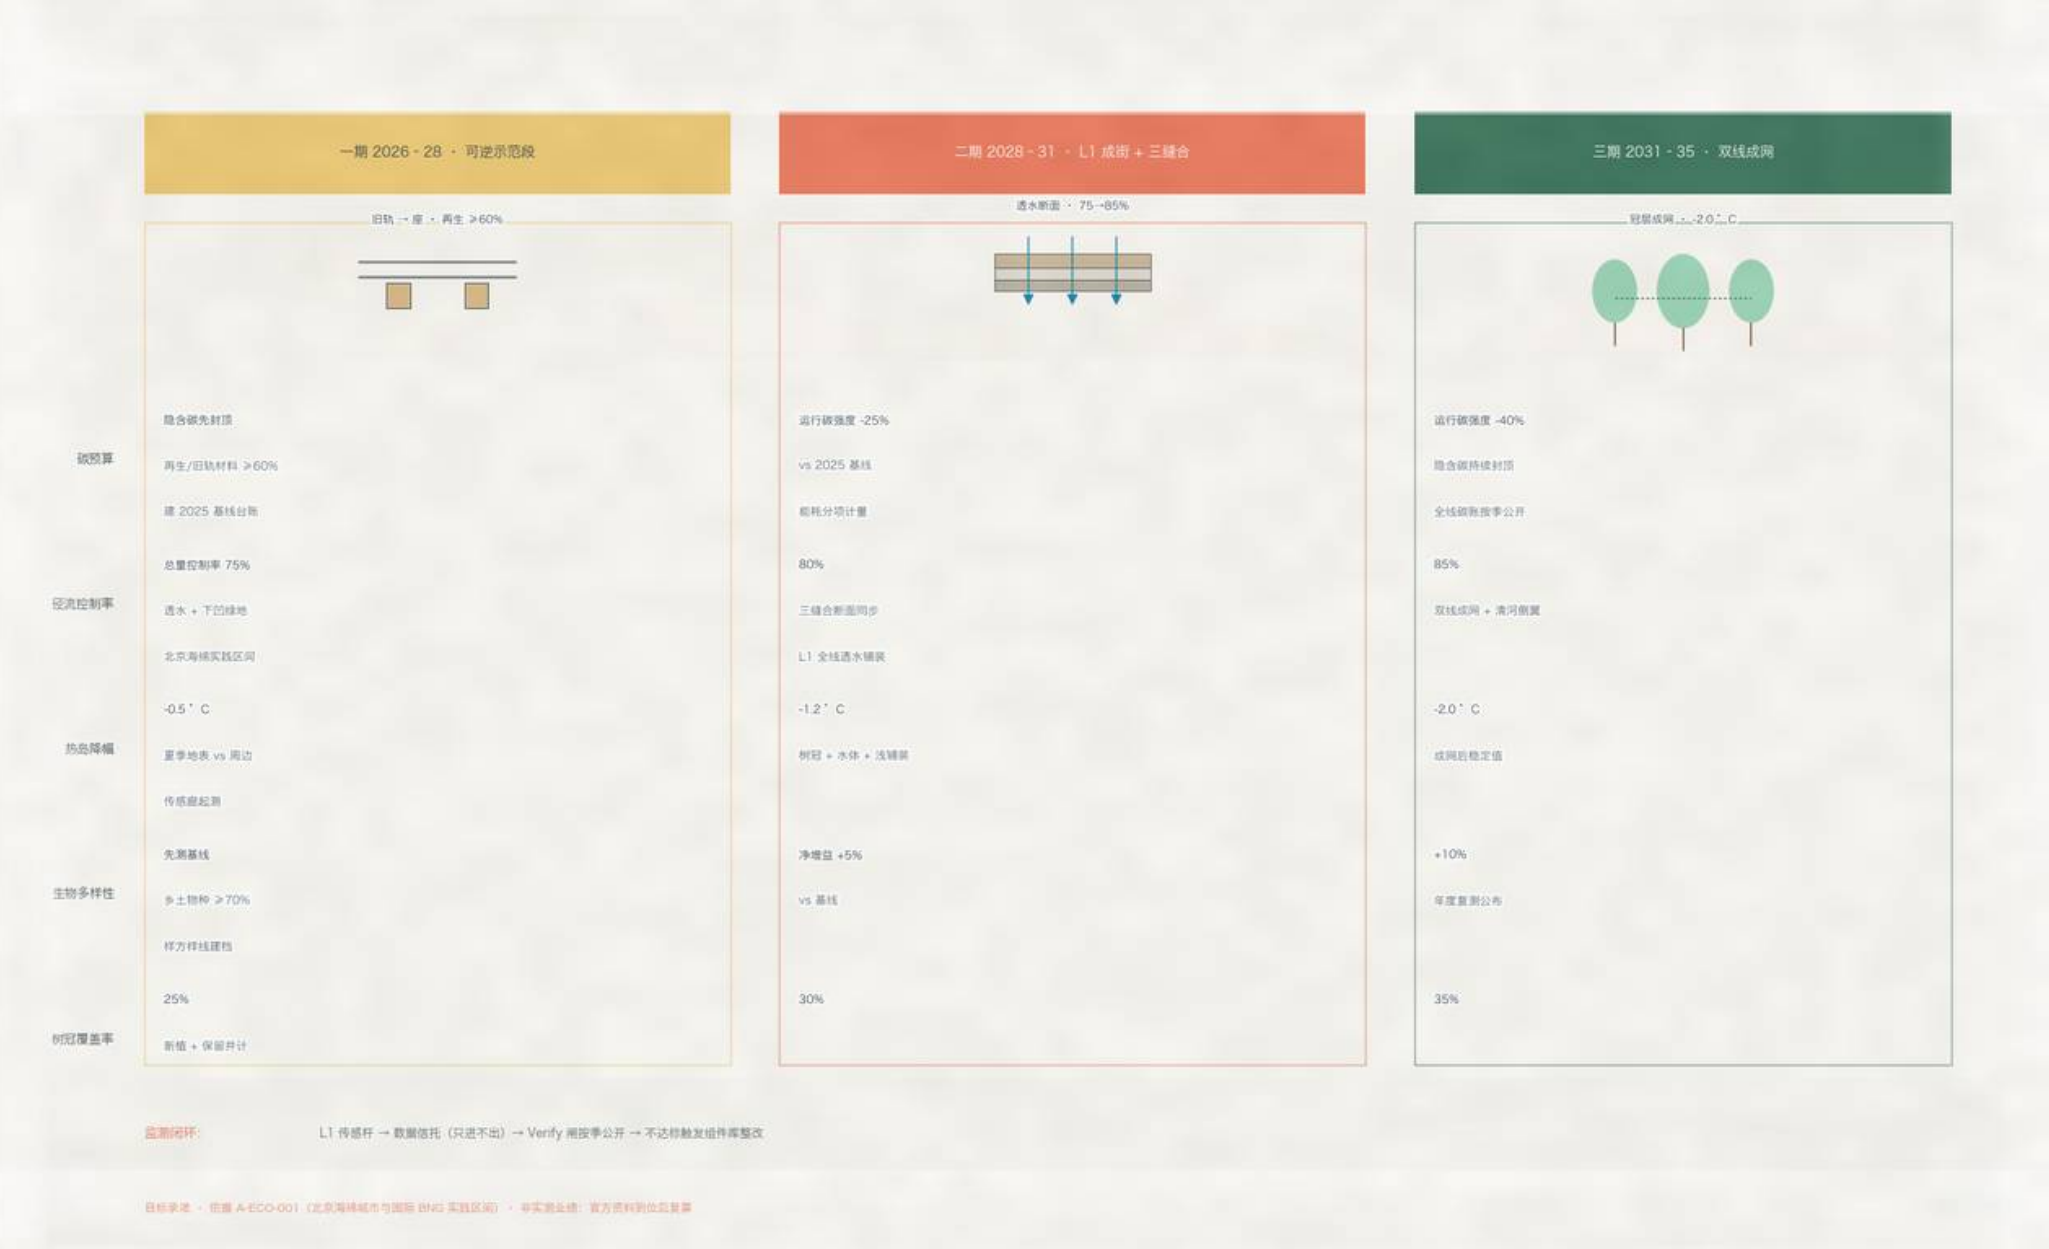

承诺不是口号 · 每个数都接监测

怎么测

L1 传感杆 + 年度调查

径流计量 · 地表温度

材料台账 · 能耗分项

样方样线 · 树冠遥感

谁来验

数据信托只进不出

受托人持证开启

Verify 隔按季公开

不达标怎么办

组件库版本化整改

目标不撤销改写


缺口写进公开纪要

为什么敢承诺

可建先行 → 试错成本低

目标取自公开实践区间


官方数据到位置复算

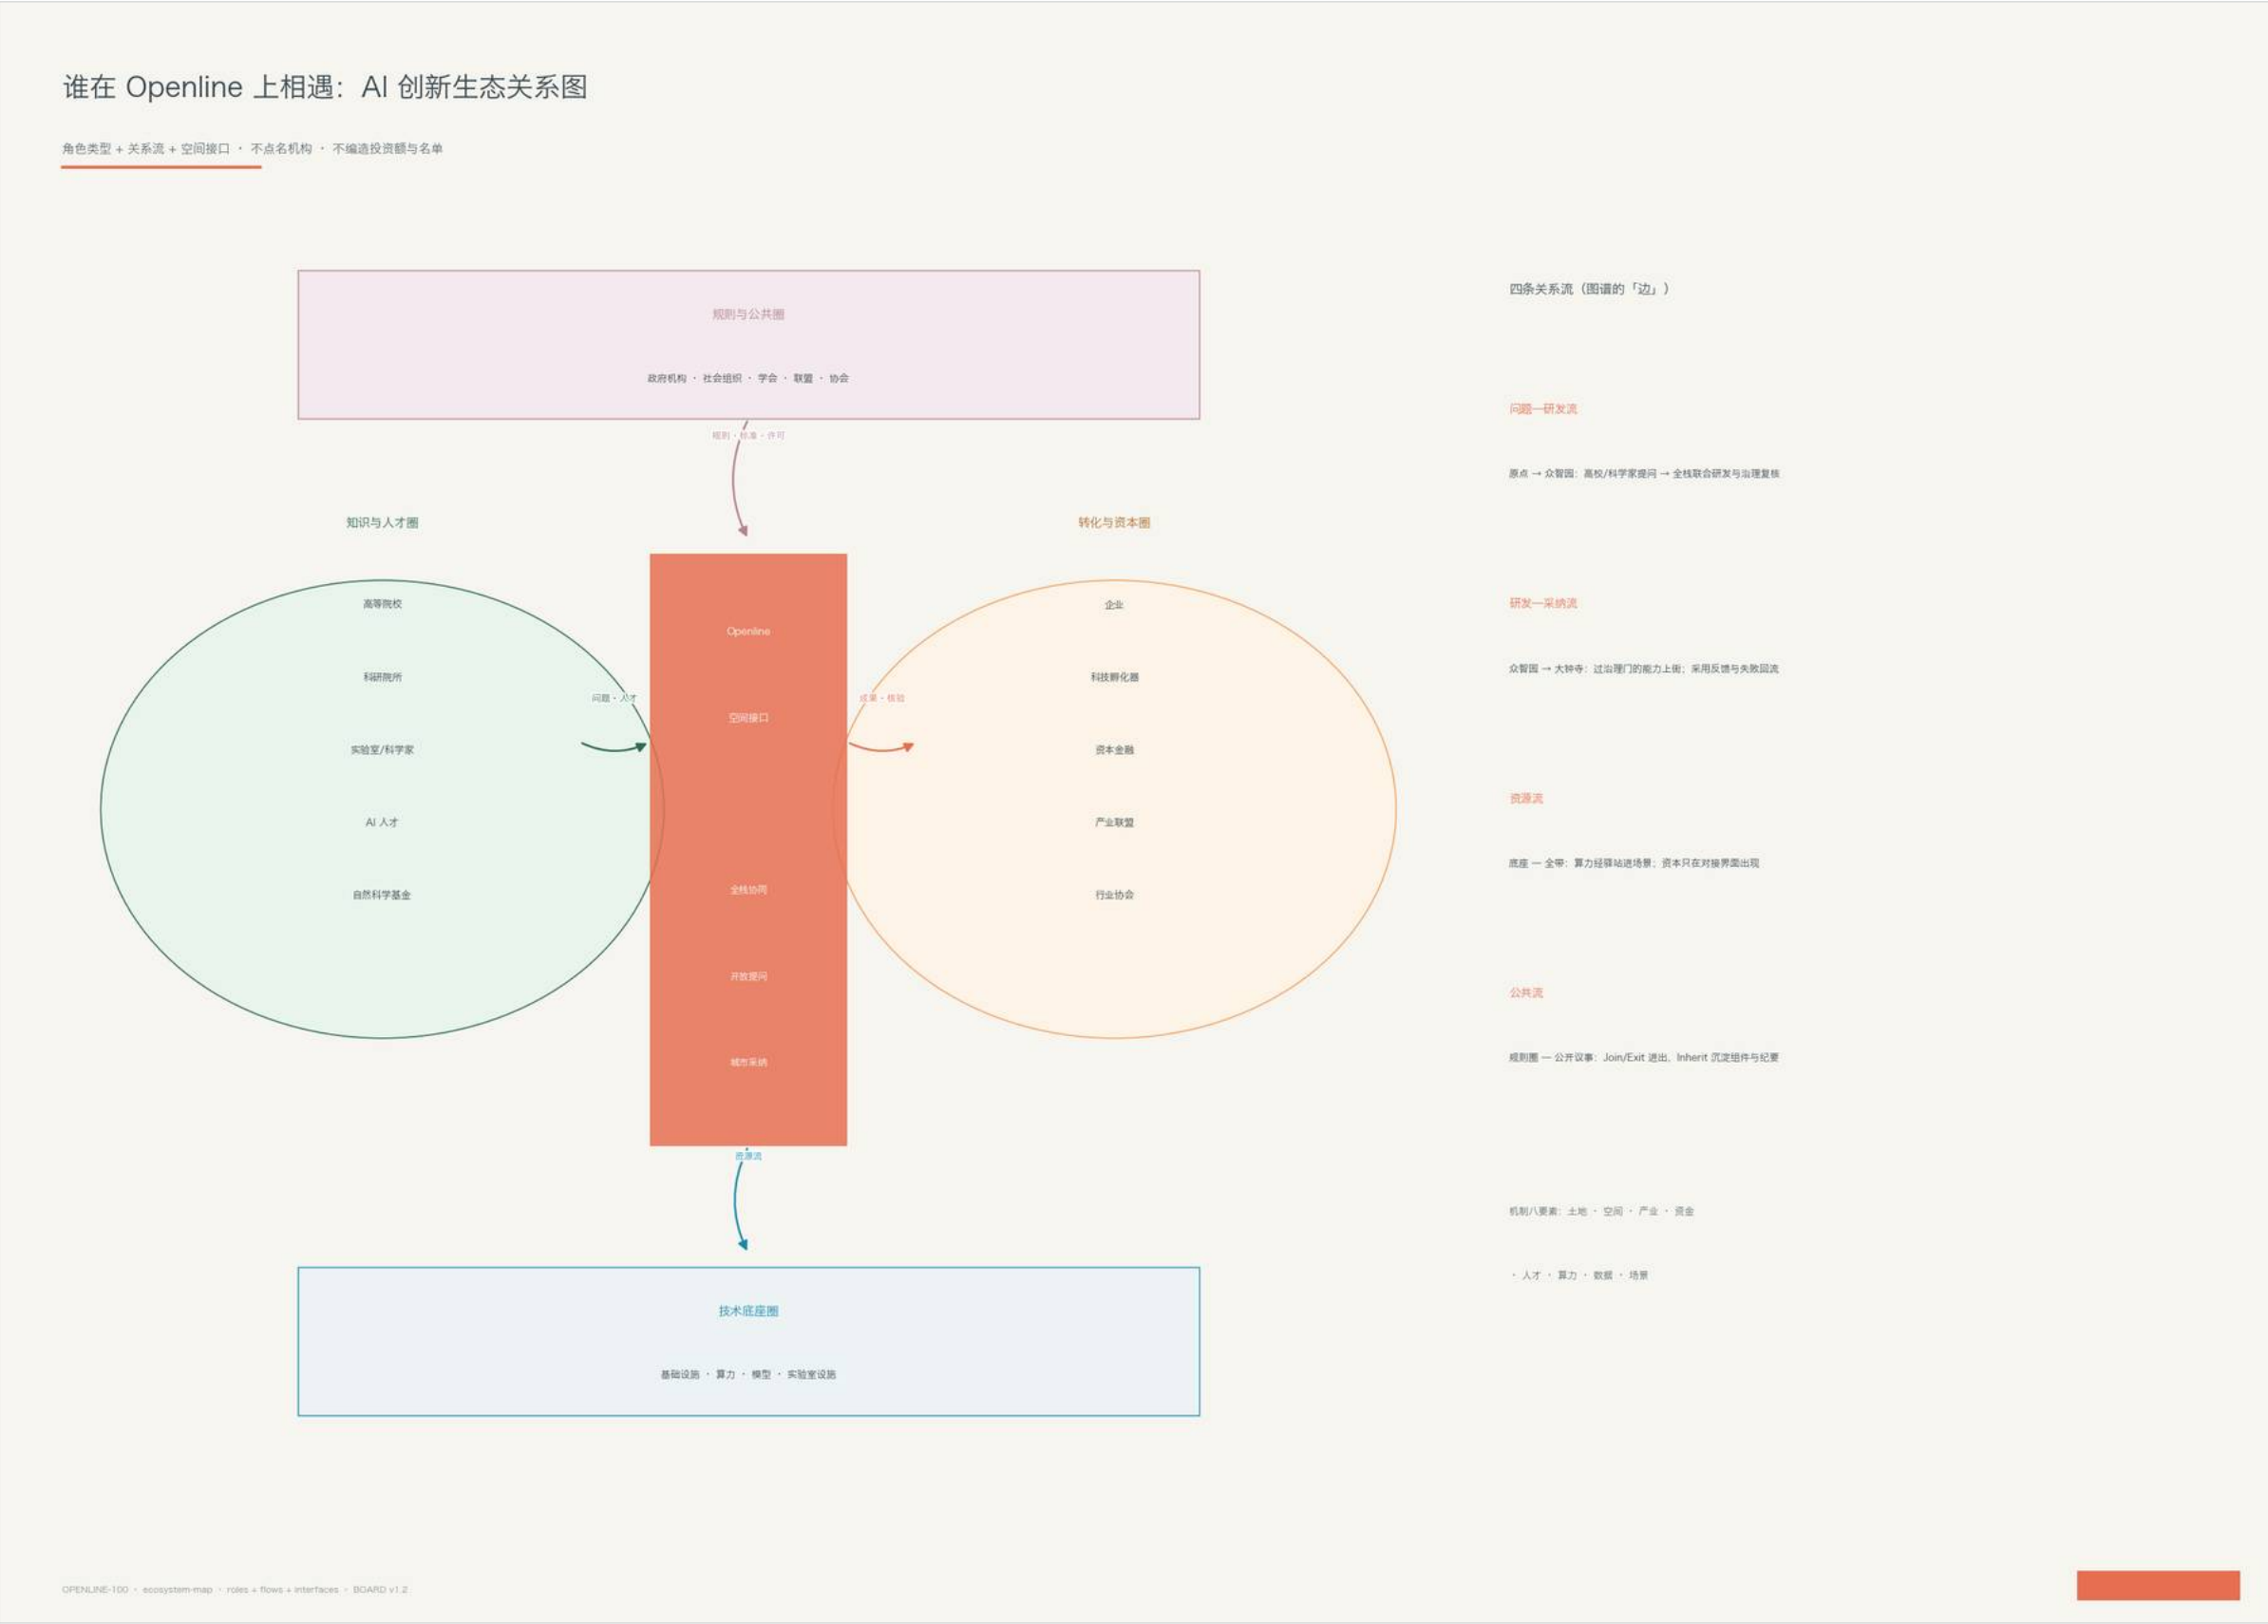

17 生态图谱：五类生境圈

Open Ticket 制度剖面：Openline 的票制

路权在数字时代的续写 | 加入 · 核验 · 退出 · 继承 × 治理 / 空间 / 数据 / 时间 四层 | 治理概念图

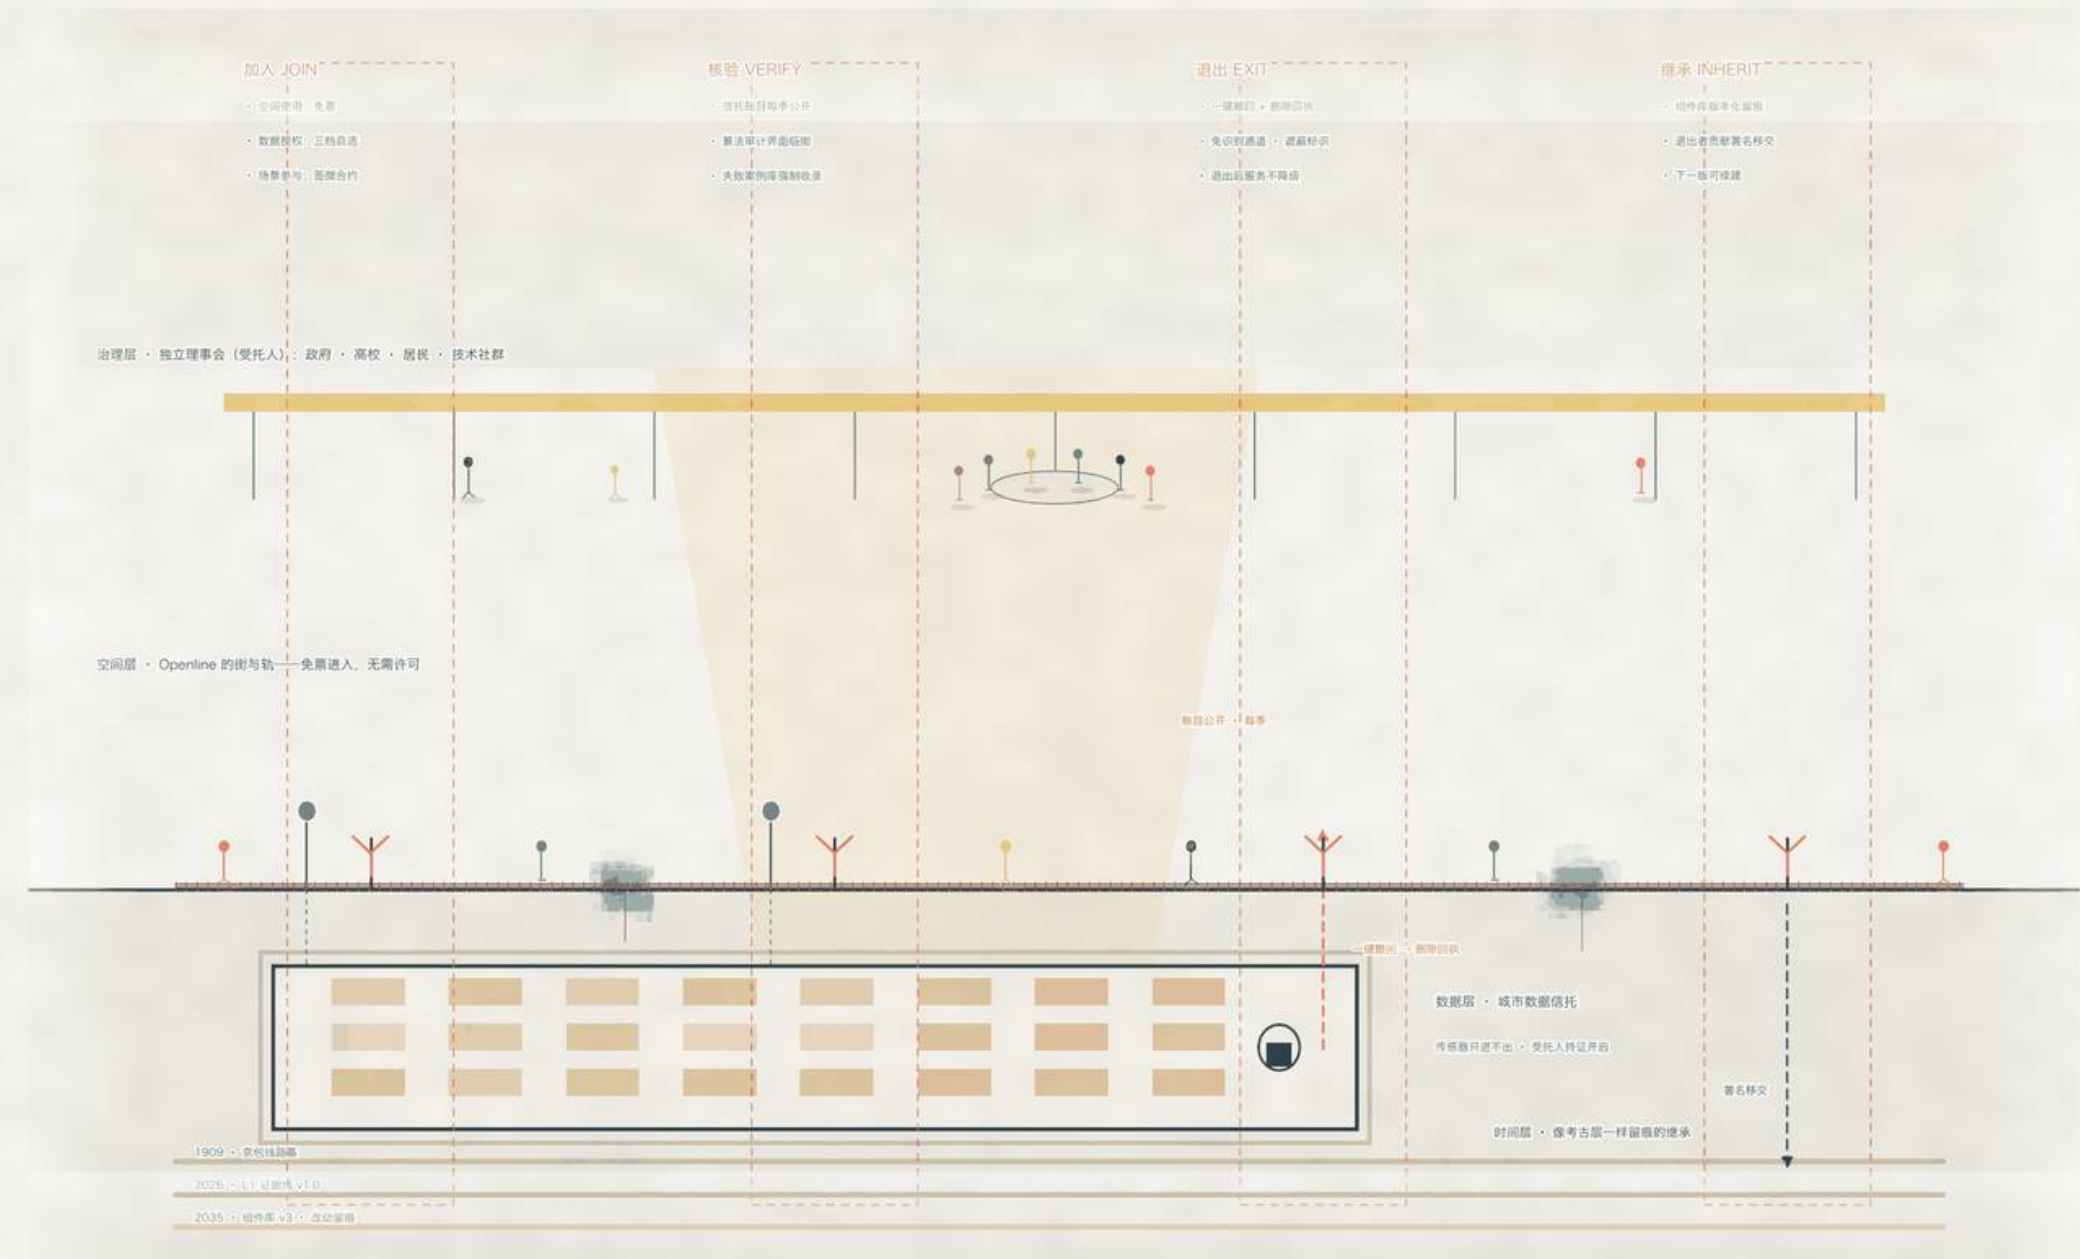

路是 Openline,
票是 Open Ticket。

- 1909: 京张争的是路权自立
- 2026: 续写数字时代的市民路权
- 路没有票制只是工程
- 有了票制才是公共服务

四层 × 四道闸


治理 信任委托 · 空间 免费进入
数据 信托上链 · 时间 留痕继承

治理概念图 · 非已定制度

机制待与再造 / 数据主管部门共建

哪些量已复算、哪些仍待正式数据

第一类可复算 (provisional 置信度) · 第二类街区结构已知/地块强度未知 · 第三类运营绩效入 assumptions

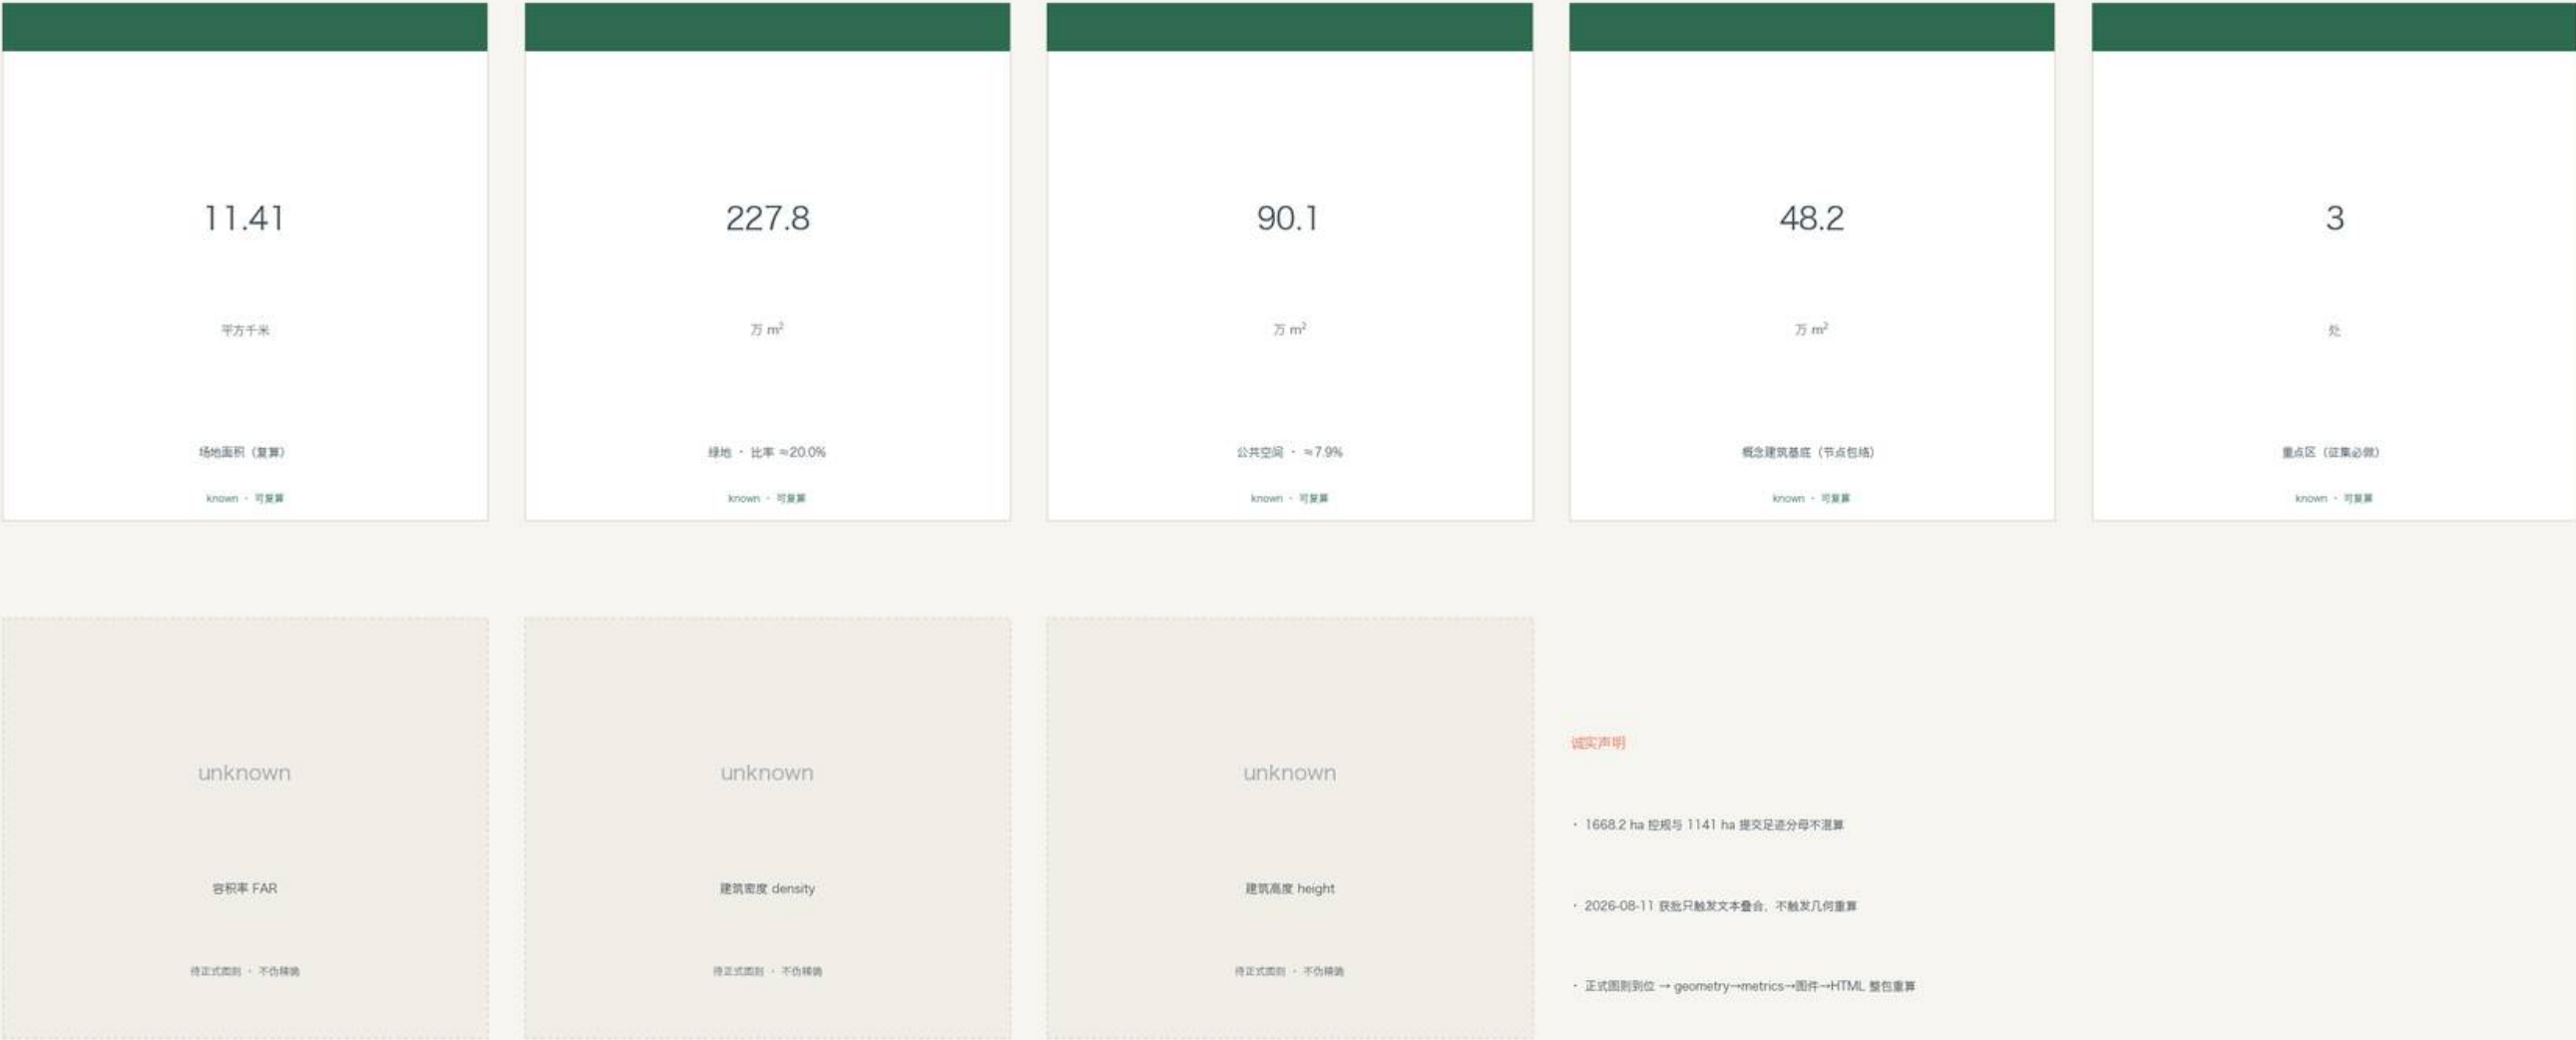

OPENLINE-100 · metrics-evidence · source: metrics.json recalculated in EPSG-4548 · BOARD v1.2

公共空间先行，强度奖励跟进：0 - 1 · 1 - 3 · 3 - 10

与 OL-01 - 10 项目清单同一套动作 · 分期不是资金计划 | 底图 OSM 真实肌理 | 虚线 = 尚未落地

0 - 1 年 · 样板



1 - 3 年 · 成街



3 - 10 年 · 网络



0 - 1 年 · 样板

- 原点到达图先动
- KMO + 中缝合样板
- 驿站单点原型

1 - 3 年 · 成街

- 一组可升级单元成街
- 智能原生街面试点
- 授权窗口与发布厅

3 - 10 年 · 网络

- 三区协同网络展开
- OL-07 甲板进中期库
- 治理中心深化

OPENLINE-100 · key-phasing · 0 - 1 / 1 - 3 / 3 - 10 on real fabric · BOARD v1.2


20 分期实施：2026 → 2030 → 2035

OPENLINE 100 · A3 PLATES


何以京张 The Openline 100 · 海淀京张遗址公园走廊 · v1.2

分期资本逻辑：可逆即低风险

每期同时回答 建设 / 出钱 / 运营 / 回流 | 专项债 → 片区统筹 → 企业认养 接力 | 量级估算 A-CAPITAL-001

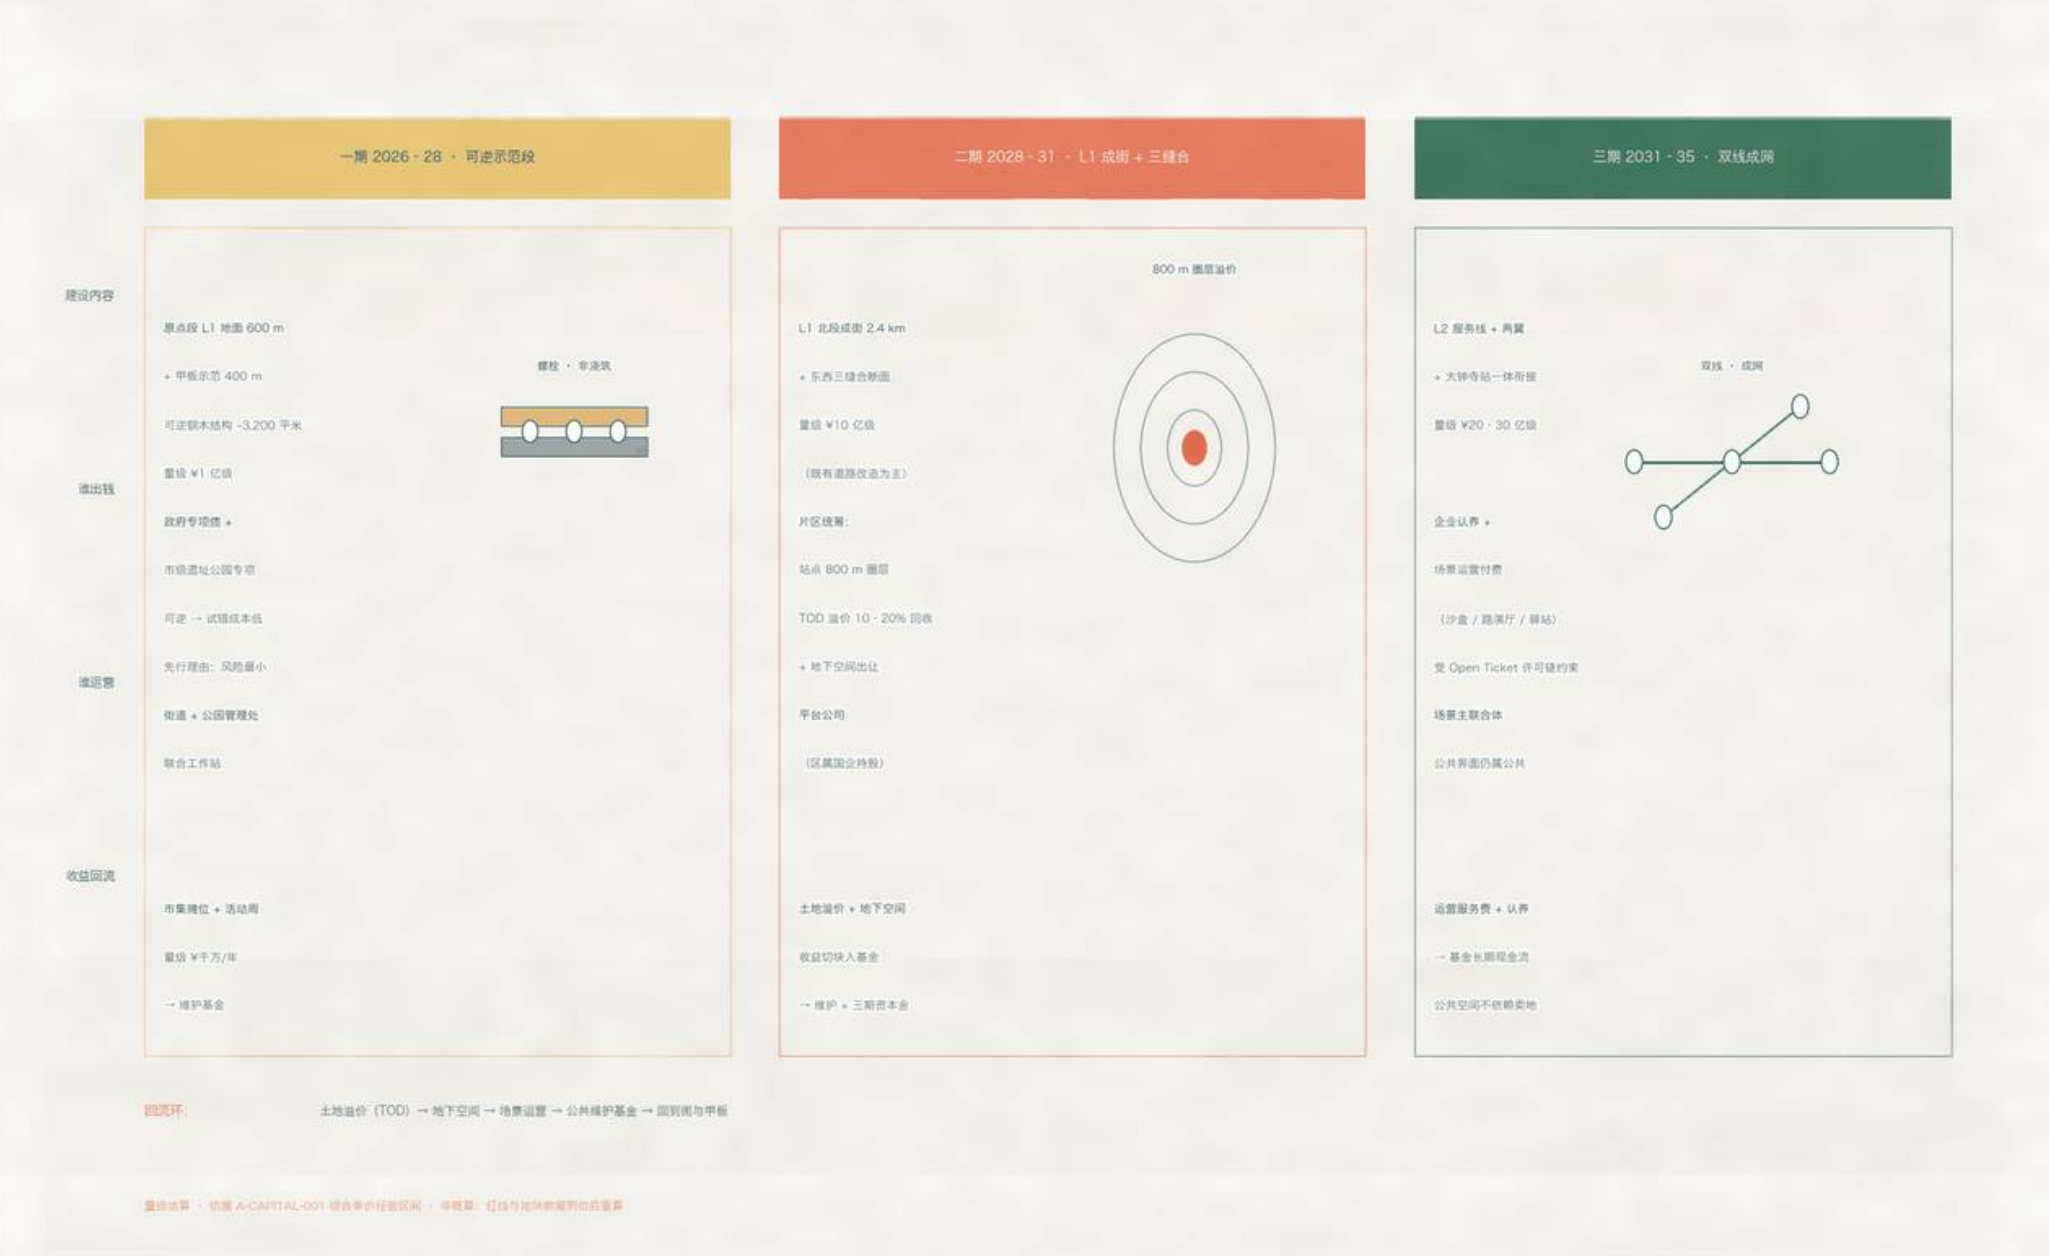

三种融资情景 · 接力而非三选一

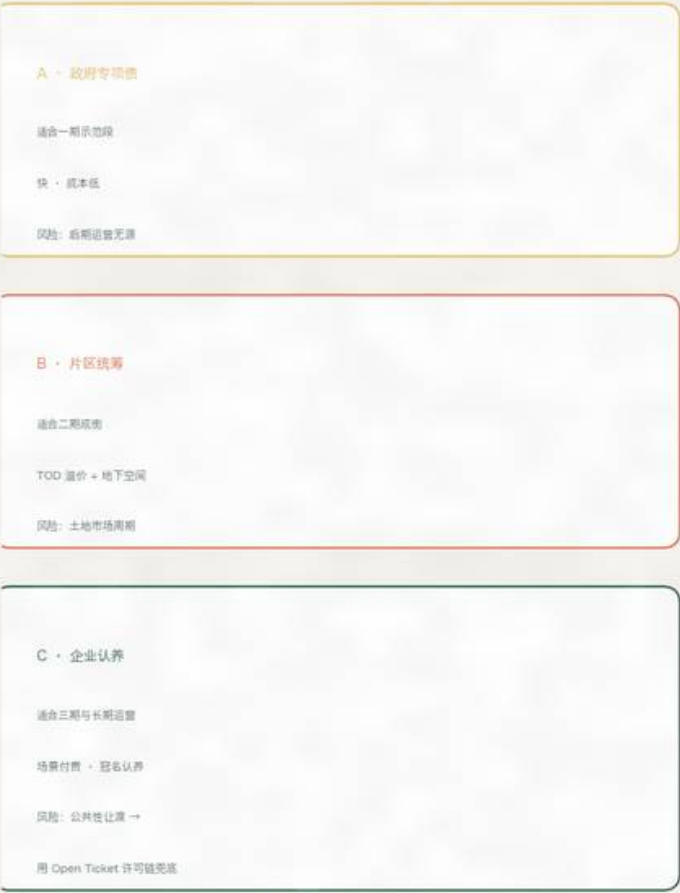

可逆性的财务含义

甲板可拆可走 → 资产可迁移

示范段错了不是沉没成本

这是能先行的真正理由



22 走进①：L1 地面步道晨景



23 走进去 ②：五道口甲板午后



24 走进 ③: 大钟寺段鸟瞰黄昏