


JZ-1909 AI Belt

Overall proposal — One Rail, Two Rivers, Three Stations • Six Axes, Multiple Nodes

Overview map · land-use structure and design elements (Amap base, north up)

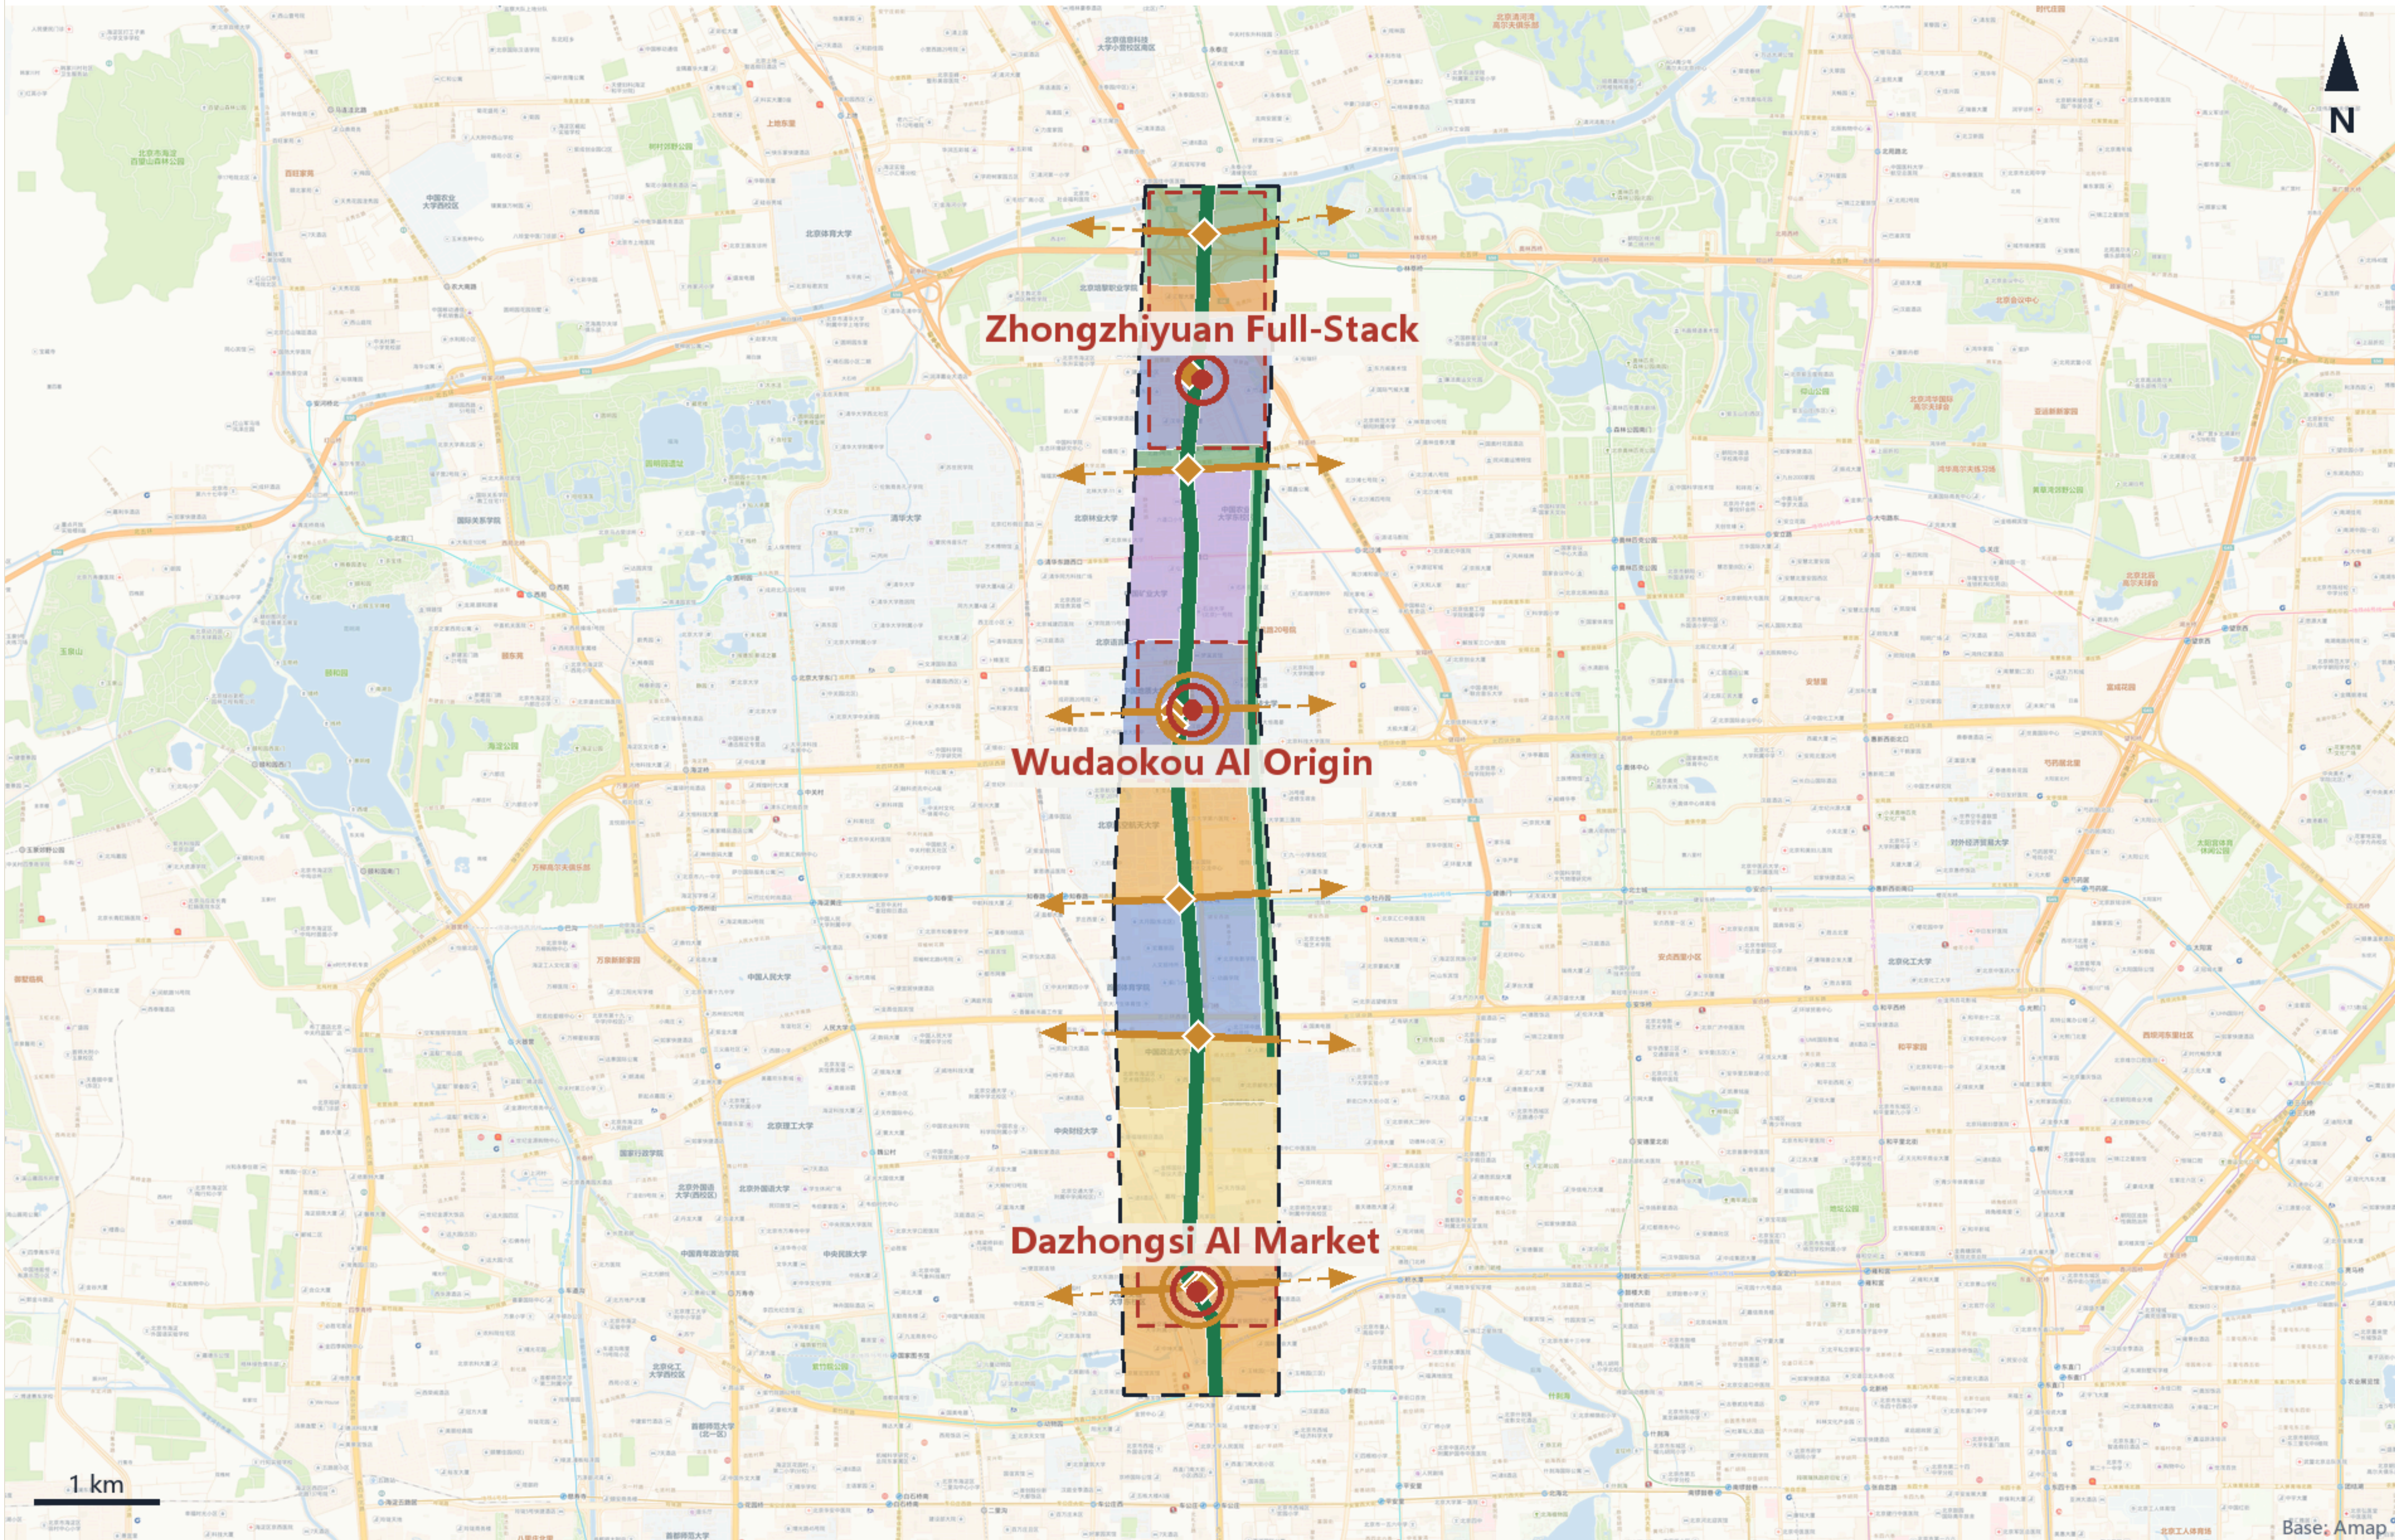

Commercial services 05 256 ha Residential 0701 132 ha Community services 0702 66 ha Research 0802 306 ha Education 0804 113 ha Park green 1401 245 ha Protective green 1402 18 ha Square 1403 5 ha Former Jing-Zhang Railway alignment (heritage spine) Existing primary road

Key area (provisional constraint) Forecourt plazas & public space Demonstration building footprint Blue-green open space

Provisional constraint boundary: all drawings and area metrics in this booklet derive from the maintainer-registered provisional extent — for design discussion and self-check only; fully recomputed once official boundaries are published.

One Rail

Jing-Zhang heritage slow-mobility spine: a ≈9.8 km, ≈116 m-wide heritage park ridge along the 1909 alignment, combining walking, cultural display and AI scenarios (core segment of the plan's 'belt').

Six Axes • Nodes

Six east-west stitch axes (Dazhongsi / Xueyuan Rd / Zhichun Rd / Wudaokou / Ring-5 / Qinghe) answer the plan's 'N-S continuity, E-W connection'; 9 switch plazas at 18 corridor crossings of 9 transverse lines, one point per line, match the plan's 'multiple nodes'.

Two Rivers

Qinghe riverside living room (≈83.4 ha waterfront at the north) × Xiaoyue River scenario-connection corridor (in-site segment ≈62 m inside the east edge; the river channel itself runs outside the site) — linking the plan's 'three belts'.

Three Stations

Dazhongsi AI Market, Wudaokou AI Origin and Zhongzhiyuan Full-Stack as relay switch points (AI Market and AI Origin carry the plan's 'two centers'); the Two Wings (Zhongguancun tech-services westward, Xiaoyue scenario eastward) diverge at Wudaokou and converge at Zhongzhiyuan — the two strokes of 人.

Key metrics

≈ 1,141.3 ha

Overall design area

Announcement ≈ 11.4 sqkm; provisional recompute matches

23.5%

Green ratio (recomputed)

green_space layer union / submitted area; calibers reconciled in the proposal

≈ 9.8 km

Heritage rail slow-mobility spine

Links three stations and all cultural nodes

63

Land-use parcels

Planar partition from shared cut lines; seamless full coverage

19

Demonstration renewal buildings

8 new - 9 converted - 2 retained; demolition pending survey

3 / ≈ 368.4 ha

Key areas

Zhongzhiyuan - AI Origin - Dazhongsi (provisional)

Phasing

Phase 1

≈ 748.9 ha

Three-station opening districts and spine demonstration segment

Phase 2

≈ 167.6 ha

Origin Community depth and Qinghe waterfront; Zhongzhiyuan concept pilot starts

Phase 3

≈ 224.7 ha

Zhongzhiyuan full-stack district and two-river living rooms completed

JZ-1909 AI Belt

Evidence & operations — verifiable, auditable, iterable

AI+ scenario system			
No.	Scenario	Carrier	Summary
01	AI slow-mobility navigation	Entire heritage spine	Explainable wayfinding and low-intrusion sensing identify walking breaks and crowding; output remains human-reviewable
02	Enterprise-service Copilot	Service posts at three stations	Policy retrieval, space matching and application guidance with sources and confidence attached
03	Public-safety and event-operations review	Forecourt plazas	Aggregate-only crowd and event-risk alerts; decisions remain human
04	Low-speed robot delivery test	Origin Community local streets	Route-limited, speed-limited, reversible delivery pilot with tiered data opening
05	AI cultural guide	1909 memory route	Multilingual narration of Jing-Zhang Railway and Zhongguancun innovation history, fact-checked
06	AI health-service navigation	Community service nodes	Connects nearby health resources without diagnostic conclusions; medical and other listed public-service venues keep on-site guidance and human-operated channels, with traditional and smart services running in parallel per State Council Document 2020 No.45 as policy background (its phased goals have expired; referenced for scenario design only)
07	Safety-governance sandbox (test)	Zhongzhiyuan laboratory	Visit-able, bookable and auditable node for standards, trusted evaluation and red-team testing
08	Edge-compute posts (test)	Public service points at three stations	New-infrastructure prototype fusing distributed compute and low-carbon energy, for professional deepening
09	Open-source release hall	Origin Station plaza	Achievement release, code-contribution display and small roadshows
10	Low-carbon operations monitoring (test)	Qinghe riverside living room	Stormwater, energy and carbon monitoring with public metric definitions
11	Data-element reception hall	Dazhongsí district	A compliant, authorized and auditable urban interface for data circulation
12	1909 global AI week route	Belt-wide public spaces	Annual operations mix of developer festival, scenario open days and pilgrimage route

Recomputed metrics	
Submitted area	1,141.3 ha
Blue-green open space	267.9 ha
Blue-green share	23.5%
Public space area	6.3 ha
Public space share	0.6%
Demonstration footprint	13.0 ha
Demonstration footprint share (design)	1.1%
Road centerline length	25,471 m
Heritage spine length	9,800 m
Phase 1 area	748.9 ha
Phase 2 area	167.6 ha
Phase 3 area	224.7 ha
Key area count	3
Land-use parcels	63
Data gaps (pending official data): Floor area ratio · Building height limit · Statutory coverage · Statutory green ratio · Setback control — Pending official data	


Task coverage & professional matrices	
Announcement tasks 17/17 covered	
Agent tasks 6/6 covered	
Formal design depth 15/15 complete	
9 professional standards answered (incl. 3 new non-mandatory)	

Source tiers	
SITE-PACKAGE — 任务书、枚举、设计空间、限值、模式与临时边界等场地包材料。	
SOURCE-REGISTRY — 区分 formal 可用、背景、临时与待审资料的登记册。	
PROCESSED-FACT-PACK — 范围、任务、资料用途与缺资料清单的导航层，非新权威来源。	
BOUNDARY-SOURCE — 提交总体设计范围（临时约束），仅用于生成、展示与临时自恰。	
KEY-AREA-SOURCE — 三处重点区域范围（临时约束），仅用于生成、展示与临时自恰。	
OFFICIAL-ANNOUNCEMENT — 公告 1.3/1.4/1.5 的任务、范围、面积、语言与成果数据主控制据。	
AGENT-TASKBOOK — 十条共创原则、六项智能体任务、场景/品牌/运营要求与边界条款。	
GLOBAL-CASE-BACKGROUND — 全球创新生态案例为背景研究（匠社圈、伦敦国王十字、Kista、Kendall Square、深圳南山、杭州城西、慕尼黑 Werksviertel），仅作参考参照，不作为正式证据。	
KG-DRAFT-2024 — 《北京海淀区京张铁路遗址公园沿线（人工智能创新街区重点地区）HD00-1601等街区控制性详细规划（街区层面）（2022-2035年）（草案）》公示规则（北京市规划和自然资源委员会海淀分局，2024-12-20 公示）：空间结构“一带一轴、两心多点”，三大目标定位，规模控制（常住约36.4万人、城乡建设用地约1648.1公顷、建筑面积约2369.3万平方米）、九类主导功能分区、配套设施（公共服务298处等）、整体景观结构“三带六轴、多廊多中心”、交通体系（道路网密度约8.0公里/平方公里、绿色出行80%）等结构性衔接依据。	
KG-APPROVAL-2026 — 北京日报报道（2026-08-12）：市规划自然资源委于 2026-08-11 批复《北京海淀区京张铁路遗址公园沿线（人工智能创新街区重点地区）HD00—1601等街区控制性详细规划（街区层面）（2024年—2035年）》；范围东至新街口外大街、西至中关村大街、北至成府路、南至西直门外大街，共 9 个街区约 1668.2 公顷；以绿色公共空间建设引领区域城市更新，发展大模型、智能体、具身智能等新业态，构建生活圈与创新圈融合的一刻钟社区服务圈。	
HD-YUANDIAN-2026 — 北京市海淀区人民政府官网《北京AI原点社区，全球AI人才创新创业的“第一站”》：北京AI原点社区约 3 平方公里（以东开大厦为中心），立足“创新策源、创业首选”特色定位，目标打造“全球AI人才创新创业第一站”，东升产业空间集聚 AI 领域企业 300 多家、占比超七成（2025 年 AI 相关专利商标超 2000 项）、1 公里半径内聚集 30 多所高校和科研机构、超 1000 位 AI 科学家、1.5 万名开发者、10 万名相关专业学子；康桥智汇（免费工位、全生命周期创业服务）、大悦城生态服务站（“找政策、找资金、找智力、找人才、找伙伴、找智力、找空间、找场景”八大核心问题一站式解决）、“15分钟活力生活圈”（4000 余套人才公寓、海淀未来学校等）；社区已纳入北京市首批人工智能创新街区，北京市打造以海淀为核心的“一核多点”布局。本案五道口-原点站空间承接与功能须呼应依据。	
AMAP-POI-2026 — 高德开放平台周边检索 API（2026-08 检索，检索范围 lng 116.300~116.380 / lat 39.925~40.035（控规范围+北段至清河），双中心检索，GCJ02→WGS84 转换）：地铁站 37、高等院校 76、公园广场 121、综合医院 57、购物中心 48，用于全部地图图层（spatial-structure / overview-map / land-use-structure / mobility-bluegreen / key-areas）的设施分布权重叠加与详细设计对标标注；底图为高德地图 webrd 瓦片（z15）。	

Overall Spatial Structure Plan | One Rail, Two Rivers, Three Stations • Six Axes (Ama

Amap geographic base × submitted GeoJSON structure × Amap POI facility check — aligned with the regulatory plan's 'belt-axis-centers-nodes' and carrying Beijing AI Or

Overall design area 11.4 sqkm (provisional): rail as trunk • three-station relay • six-axis stitch • node network

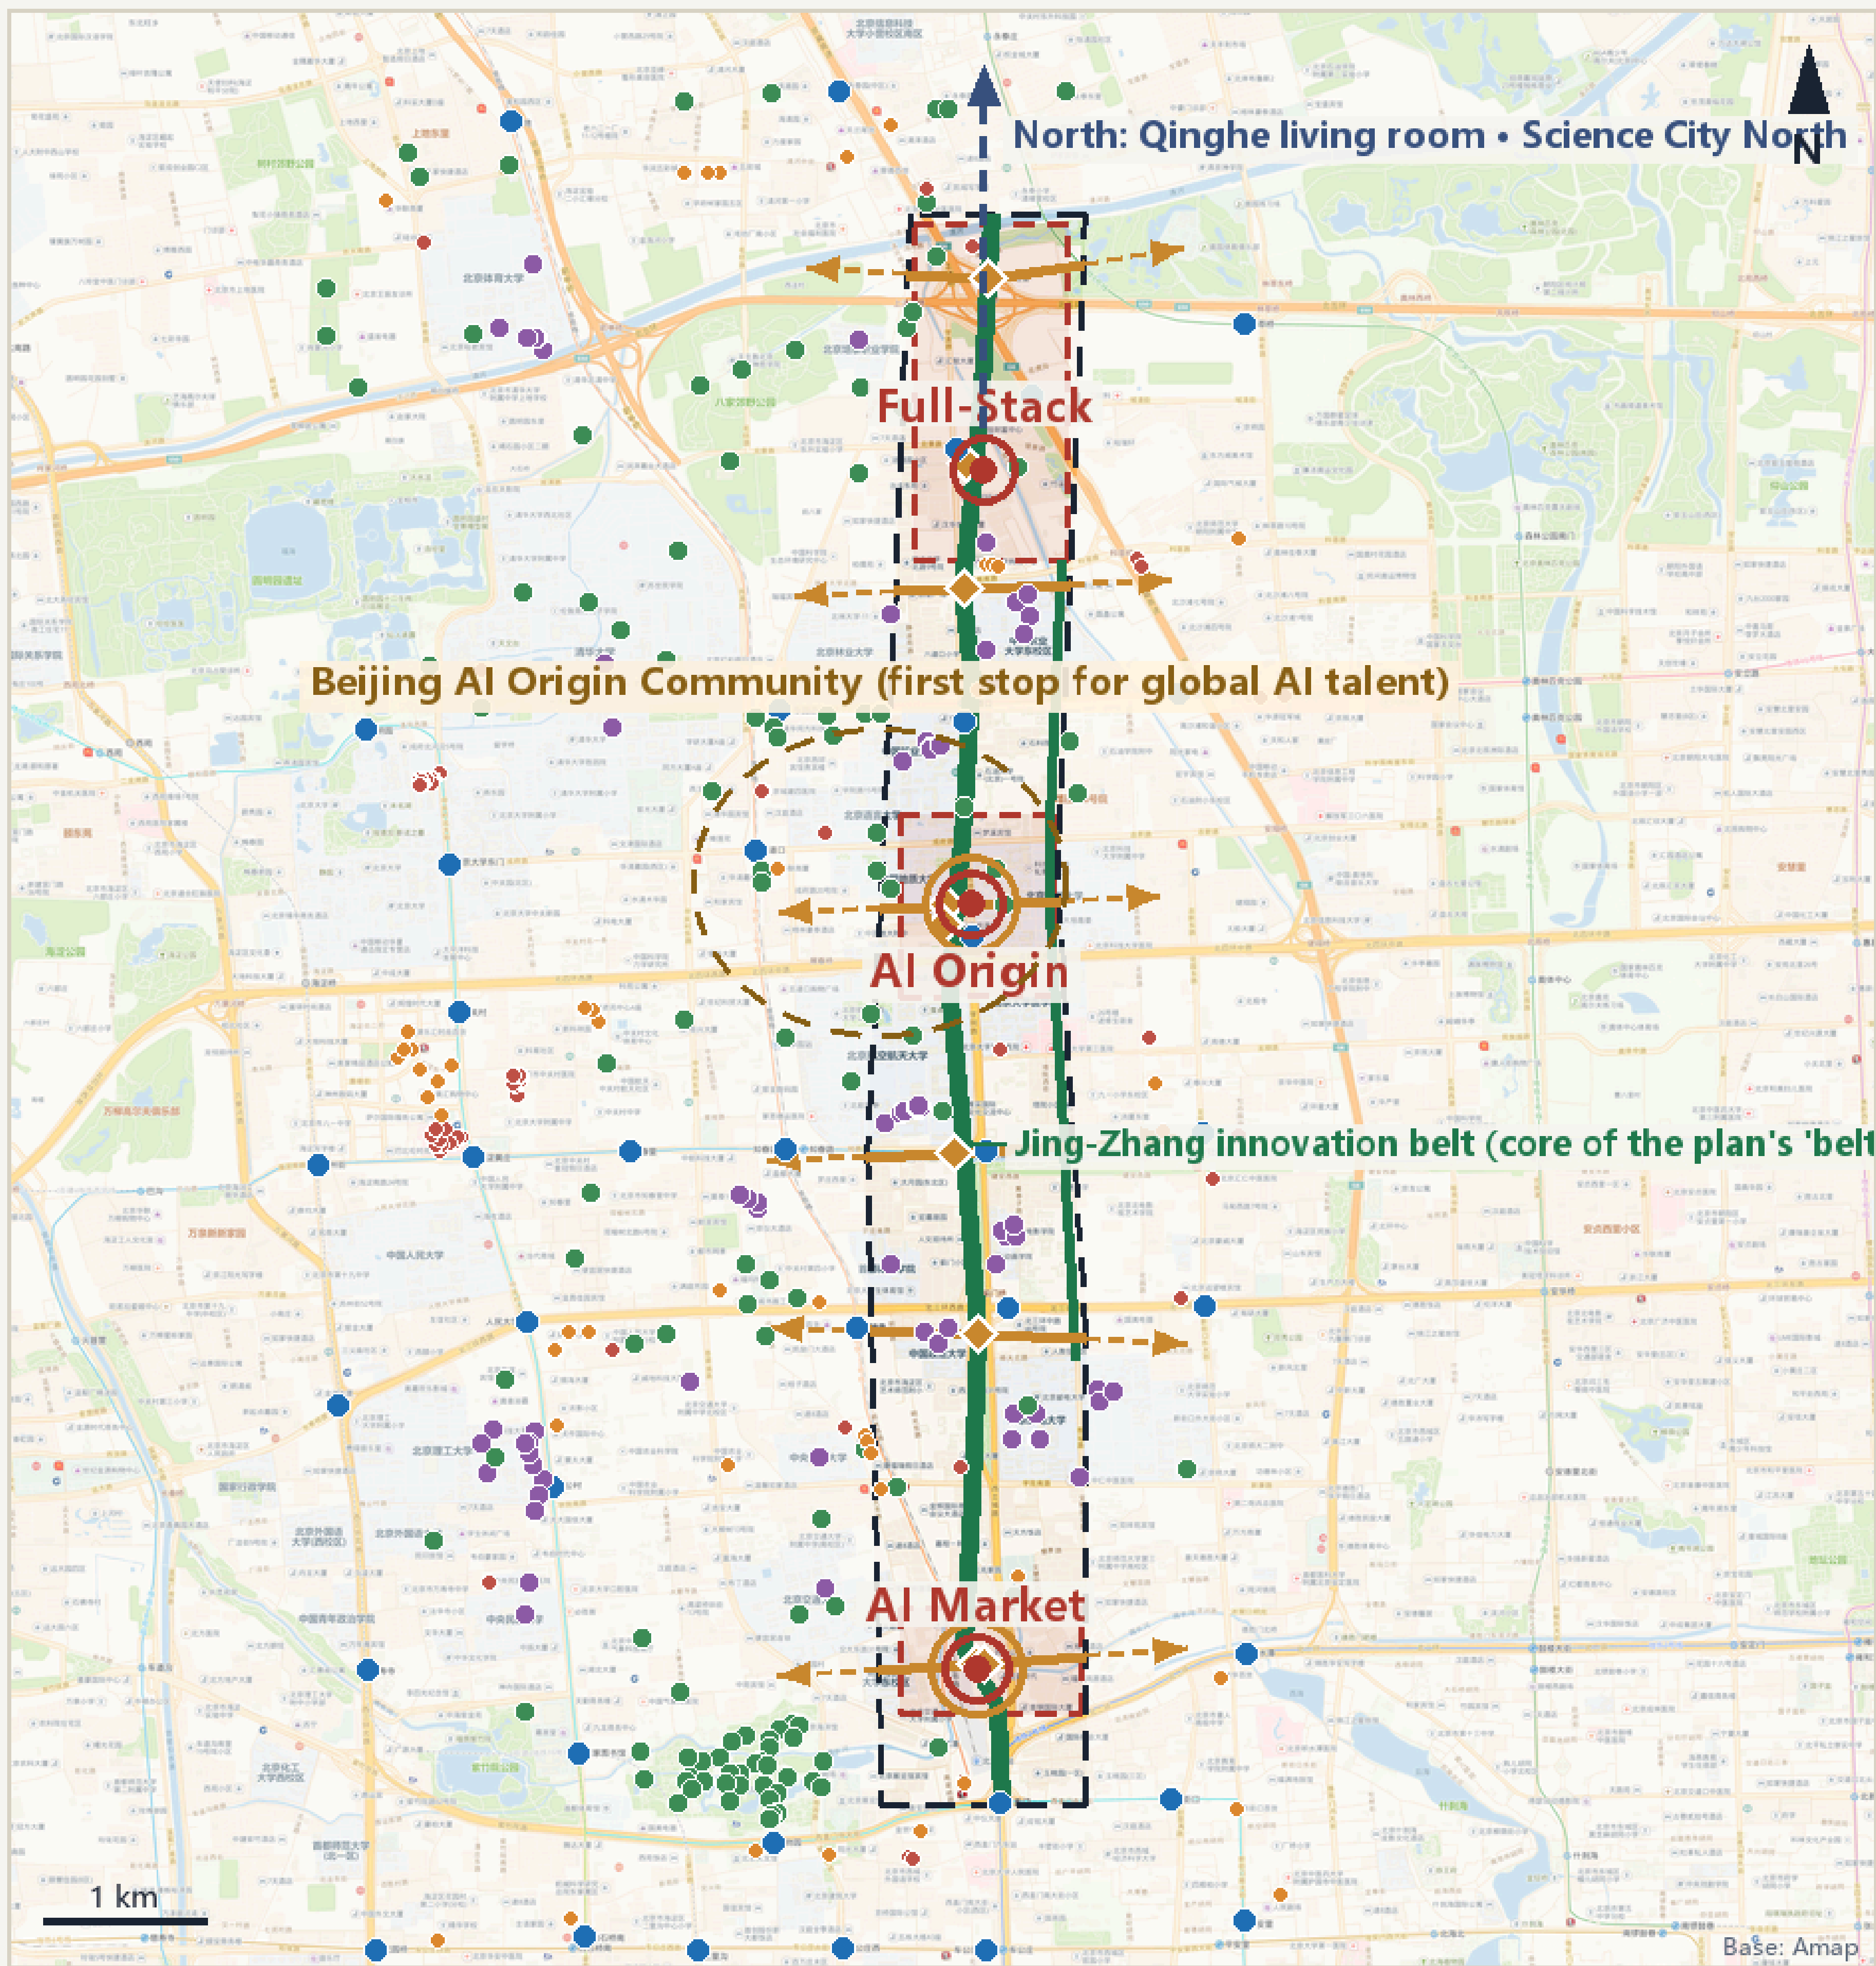

Base: Amap webdr tiles (z15, GCJ02 Mercator, 2026-08); POI: Amap around-search within the regulatory-plan-belt (radius 3700m); structure overlaid via EPSG:4548→WGS84

STRUCTURE / key points

- One rail: ≈9.8 km heritage spine — spatial skeleton of the plan-belt's core segment (Jing-Zhang innovation-and-exchange belt)
- Two rivers: Qinghe living room × Xiaoyue corridor (linking the 'three belts')
- Three stations: AI Market · AI Origin · Full-Stack relay points — carrying the 'two centers'; AI Origin matches Beijing AI Origin Community
- Six axes: east-west stitch axes answering 'N-S continuity, E-W connection'
- Multiple nodes: 9 switch plazas matching the plan's node system

ALIGNMENT / regulatory plan & AI Origin Community

- Plan: one belt, one axis, two centers, nodes**
→ one rail, three stations, six axes, nodes (aligned since v1.5)
- Beijing AI Origin Community: 'innovation source, first choice'**
→ carried by Wudaokou AI Origin — spatial anchor of the 'first stop' for global AI talent
- Campus-park-block fusion • 15-min lively living circle**
→ the AI Origin 'campus—park—block' slow-mobility stitch is its spatial landing
- Foundation-model ecosystem station: eight-factor services**
→ echoed by the Origin Hall + open-source collaboration center programming
- Beijing's first AI innovation blocks: 'one core, multiple nodes'**
→ this proposal's 'one rail, three stations, node network' plugs in

POI CHECK / facilities (Amap)

- metro stations 37
- universities 76
- parks & squares 121
- hospitals 57
- shopping malls 48

Station-level facilities match the 15-minute service-circle structure: metro stations spread evenly along the corridor and axes; the university cluster underpins the Wudaokou campus-park-block stitch.

LEGEND

- overall design area (provisional)
- key areas (provisional)
- heritage spine (one rail)
- E-W stitch axes (six)
- switch plazas (nodes)
- three stations