


Overall Framework

Beijing-Zhangjiakou AI Innovation Corridor · 2026 · CC-BY-4.0 · organizer's provisional boundaries · site 11.41 km²

Beijing-Zhangjiakou AI Innovation Belt • Overall Design Area

11.41 km² · EPSG:4548 · based on organizer's provisional boundaries


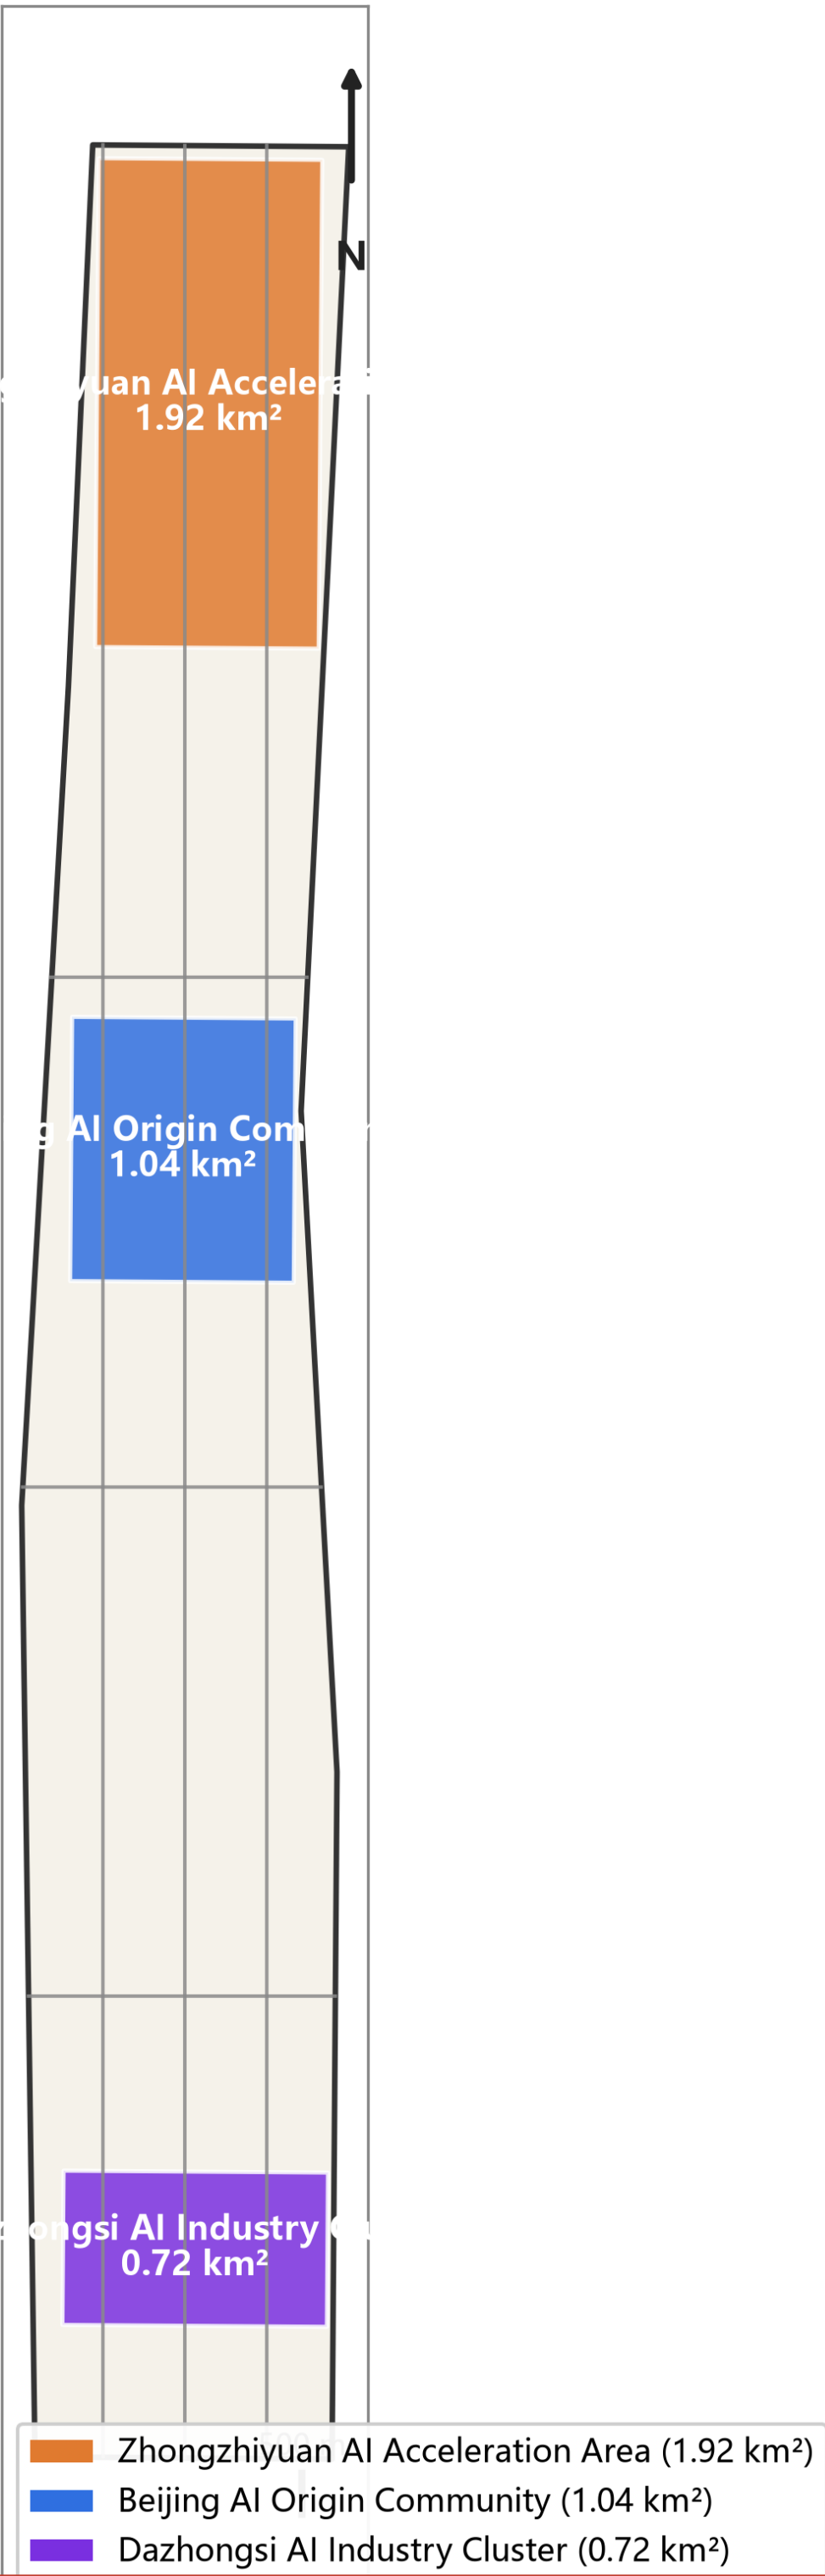


[Boundary note] Drawn from the organizer's provisional rough boundaries; conceptual urban-design illustration only, not a statutory planning boundary.

Key Detailed Design Areas




[Boundary note] Drawn from the organizer's provisional rough boundaries; conceptual urban-design illustration only, not a statutory planning boundary.

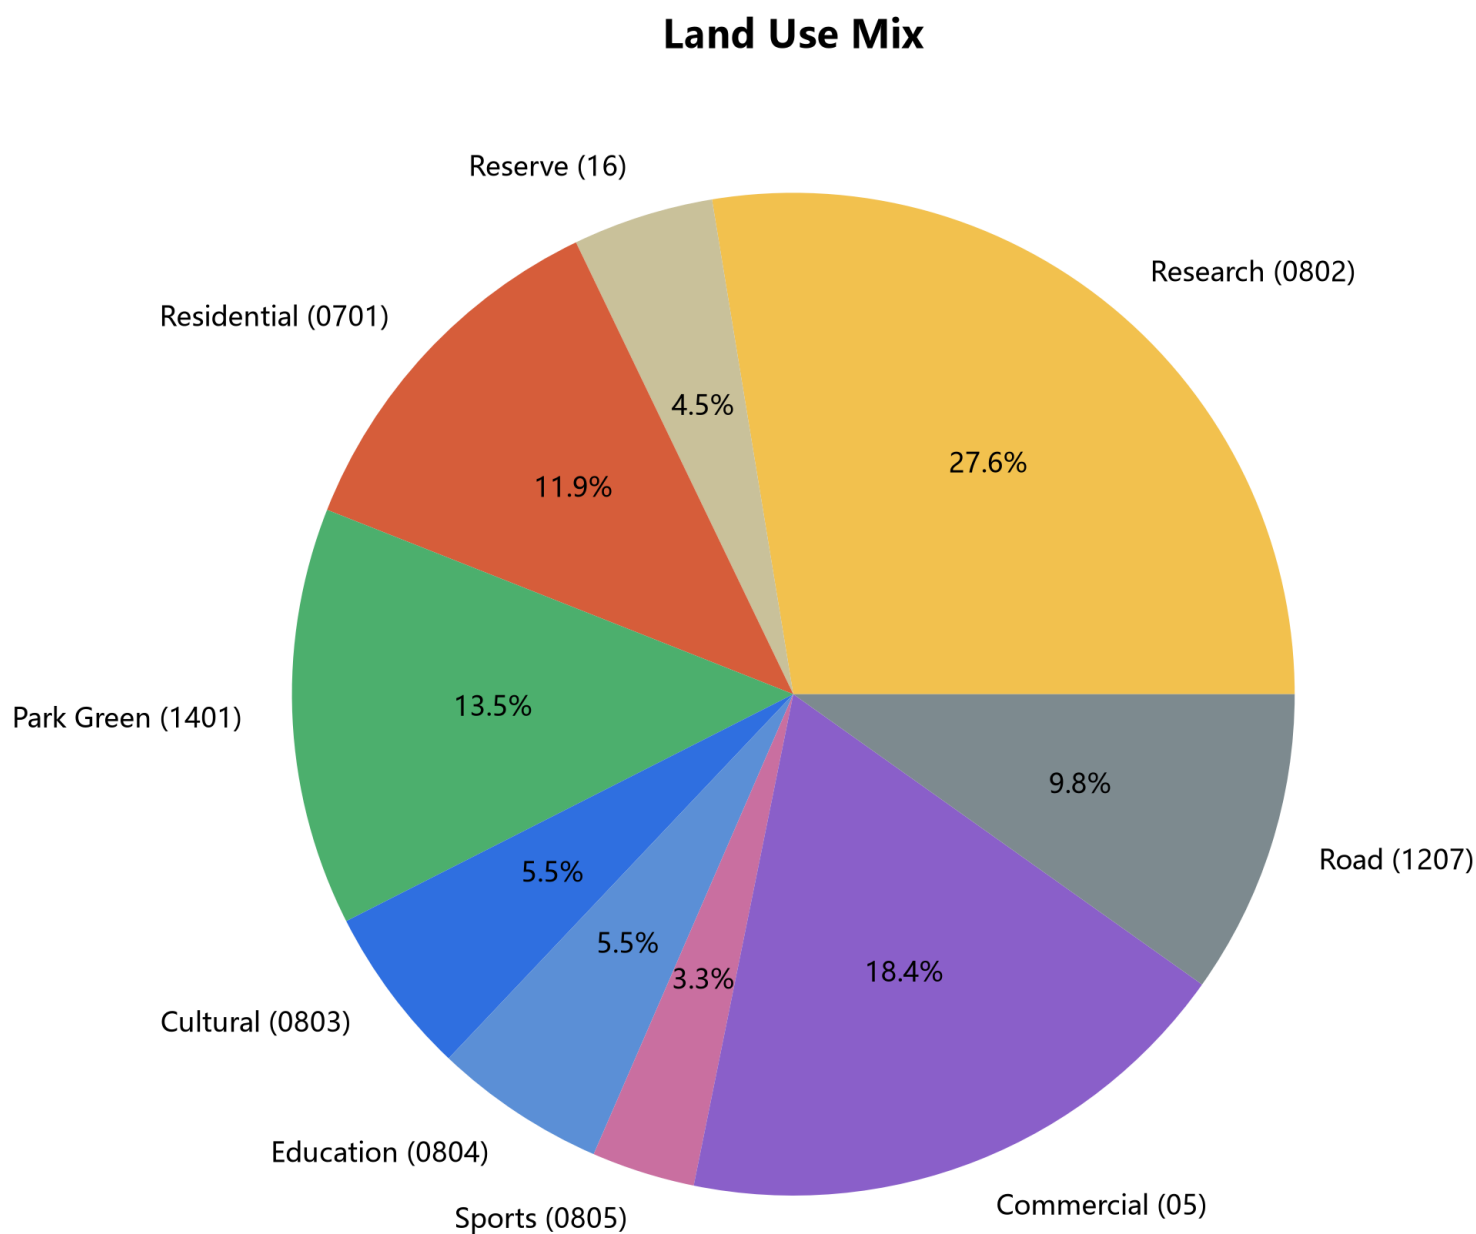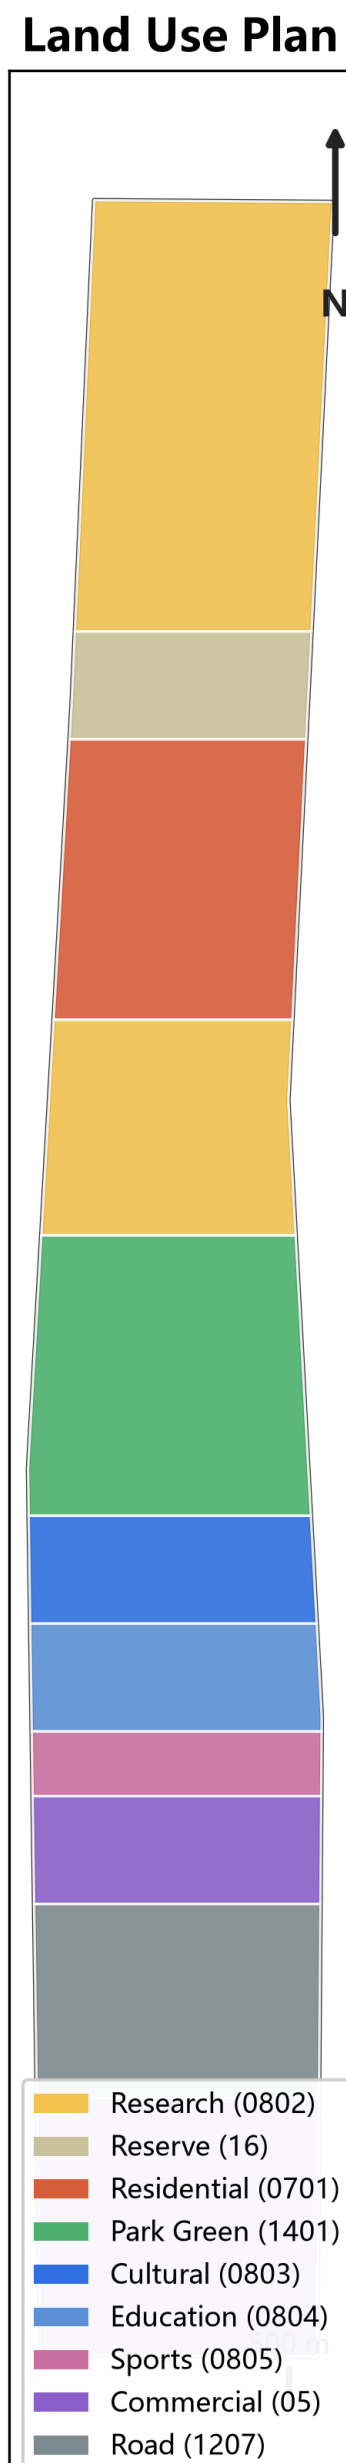

[Boundary note] Drawn from the organizer's provisional rough boundaries; conceptual urban-design illustration only, not a statutory planning boundary.

Mobility & Blue-Green Network

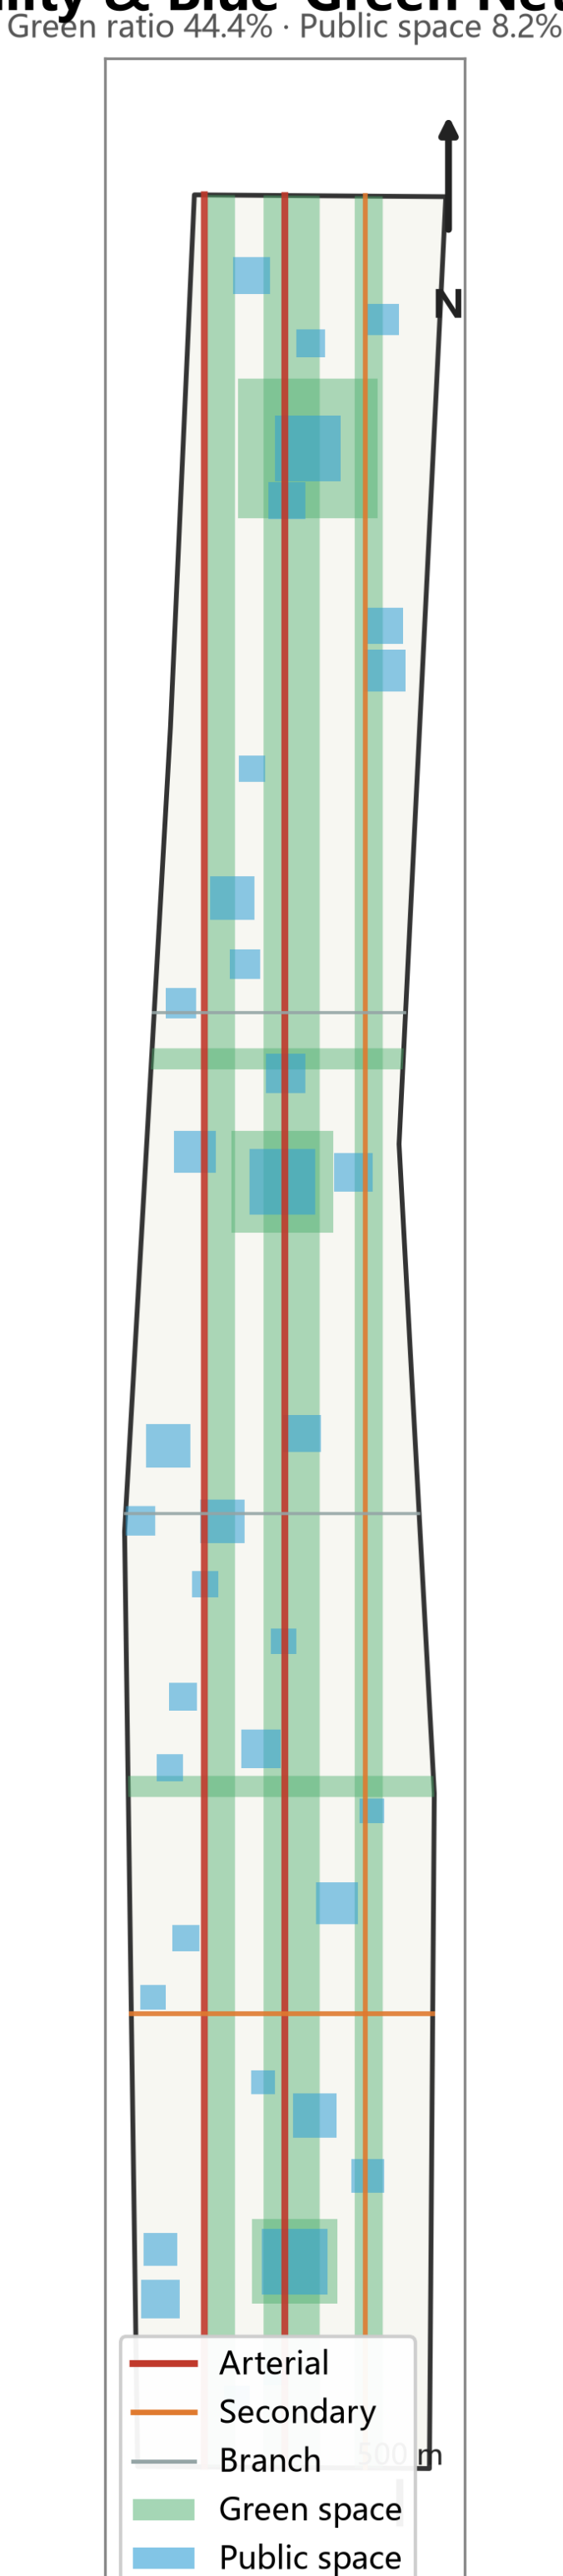


[Boundary note] Drawn from the organizer's provisional rough boundaries; conceptual urban-design illustration only, not a statutory planning boundary.

Metrics & Evidence


Beijing-Zhangjiakou AI Innovation Corridor · 2026 · CC-BY-4.0 · organizer's provisional boundaries · site 11.41 km²

Metrics Recalculation & Evidence

Implementation Phasing

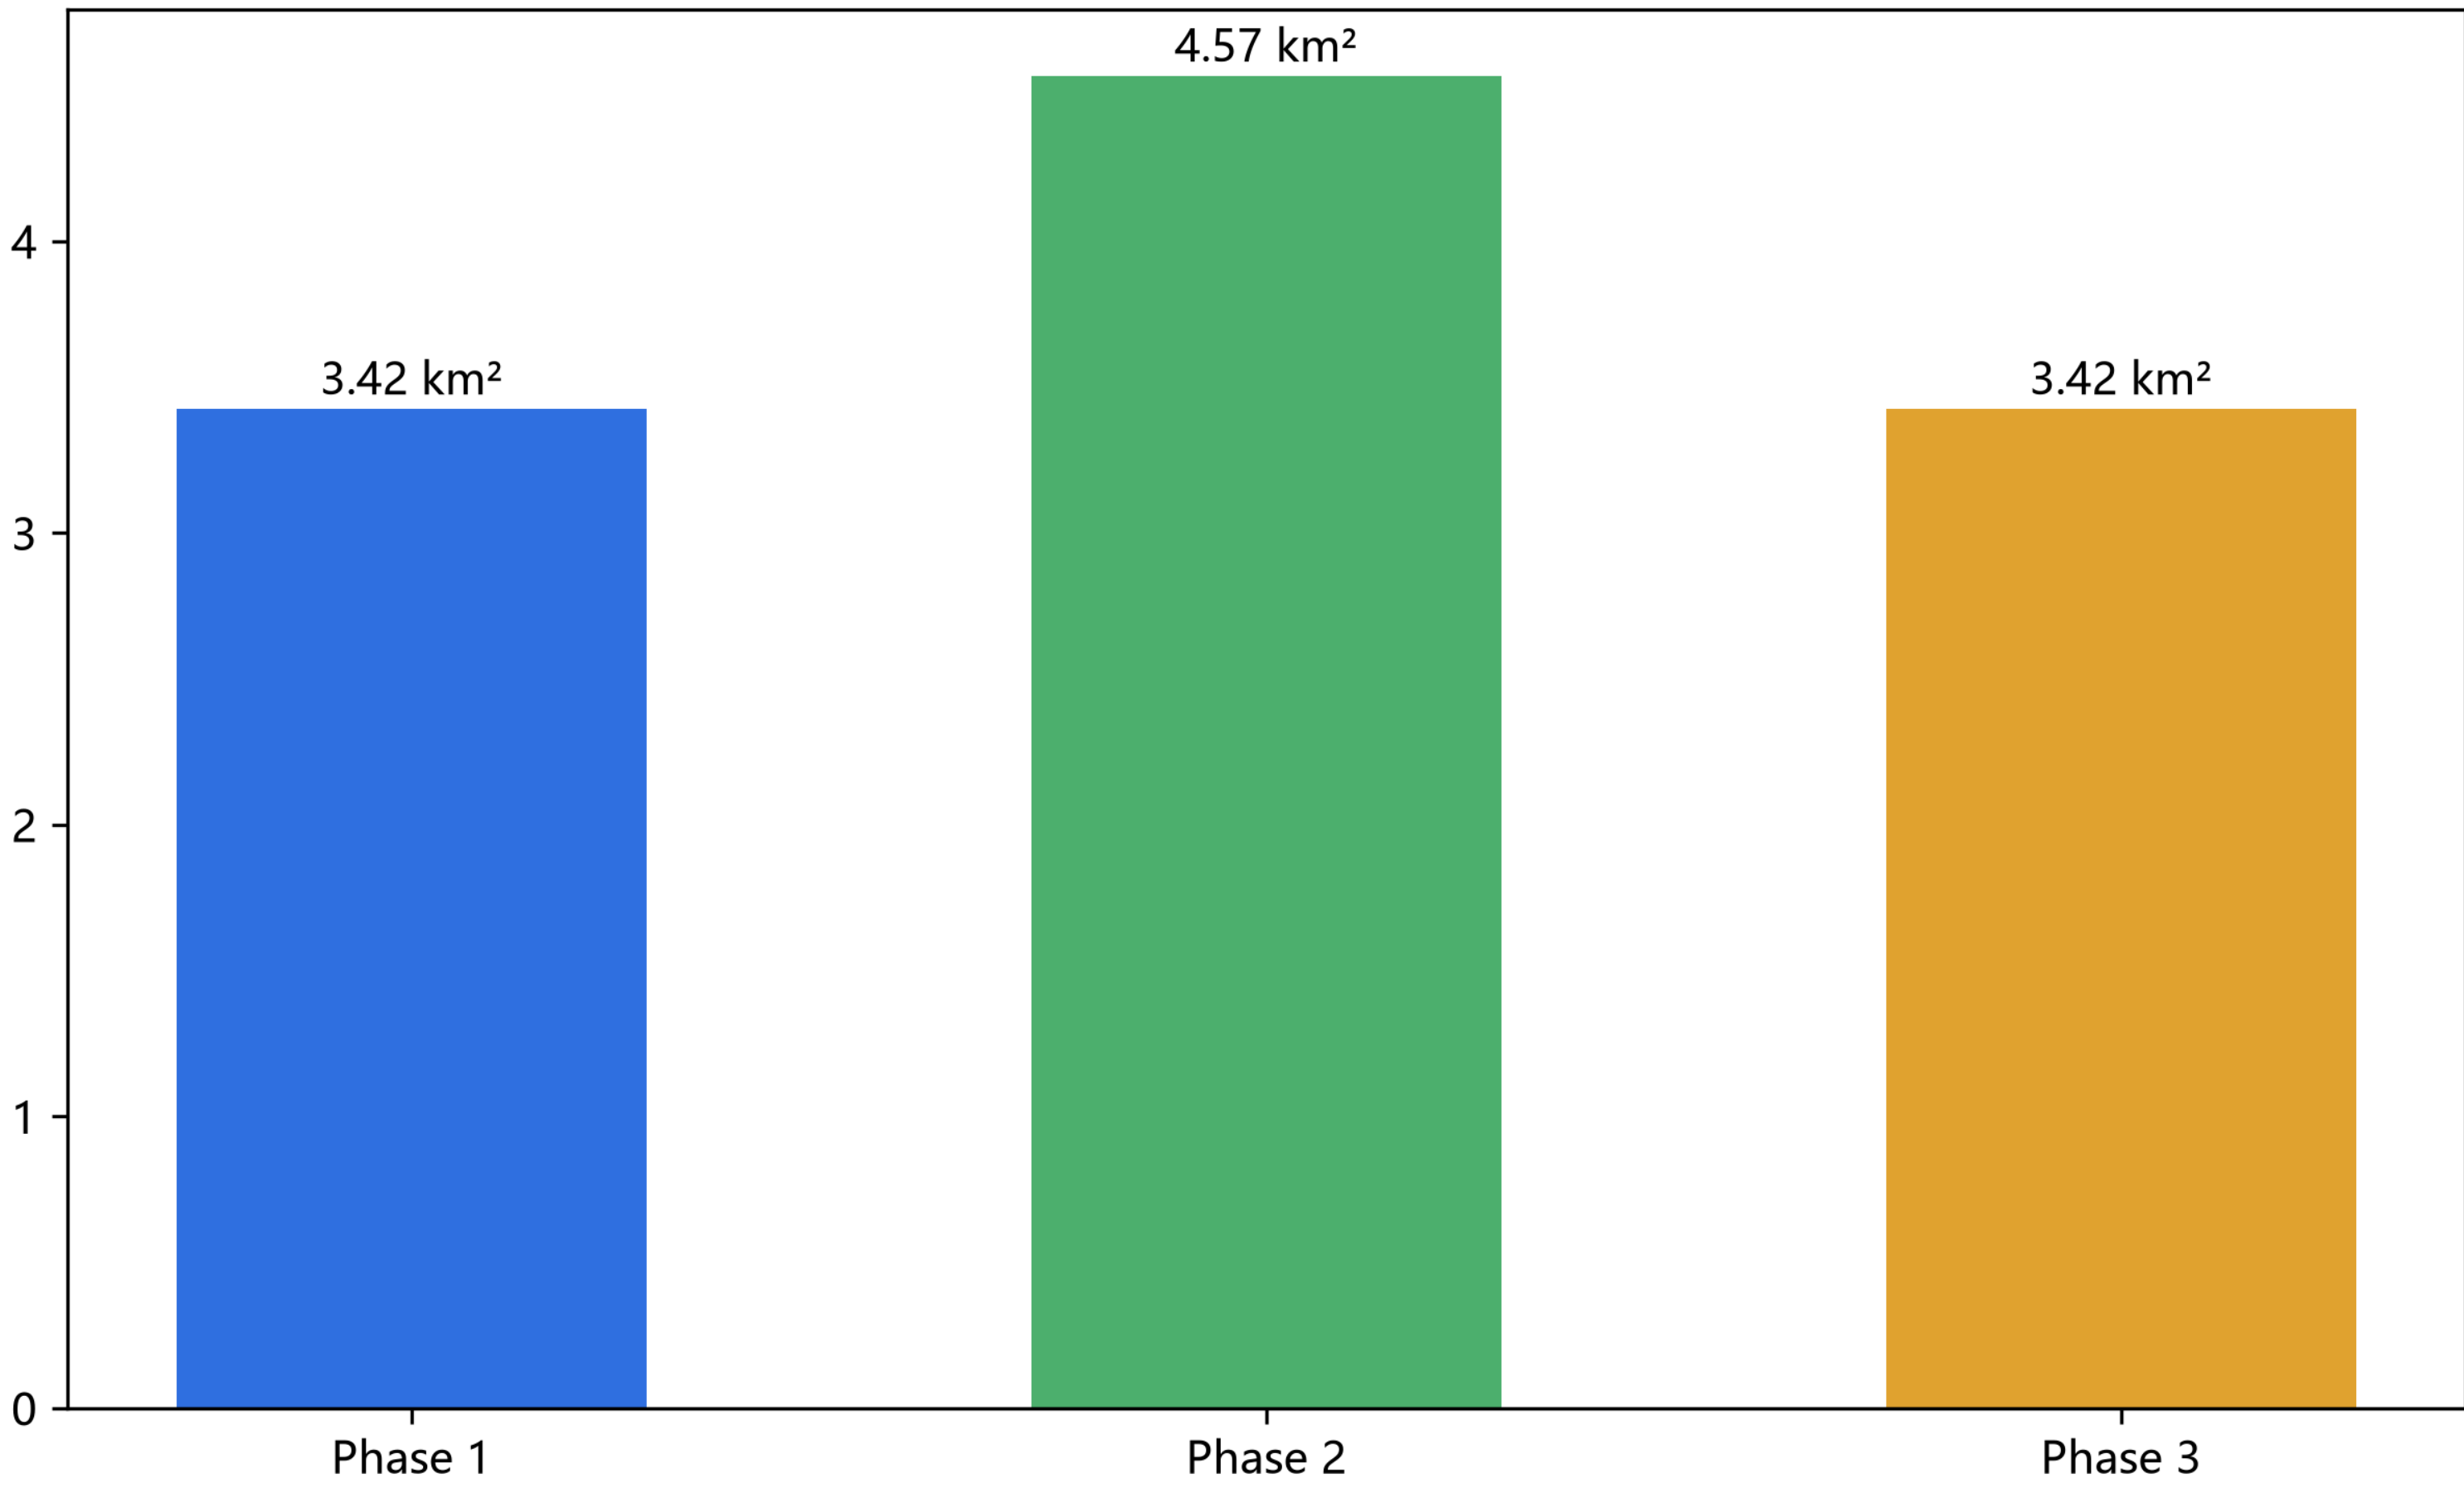

Key Ratios Radar

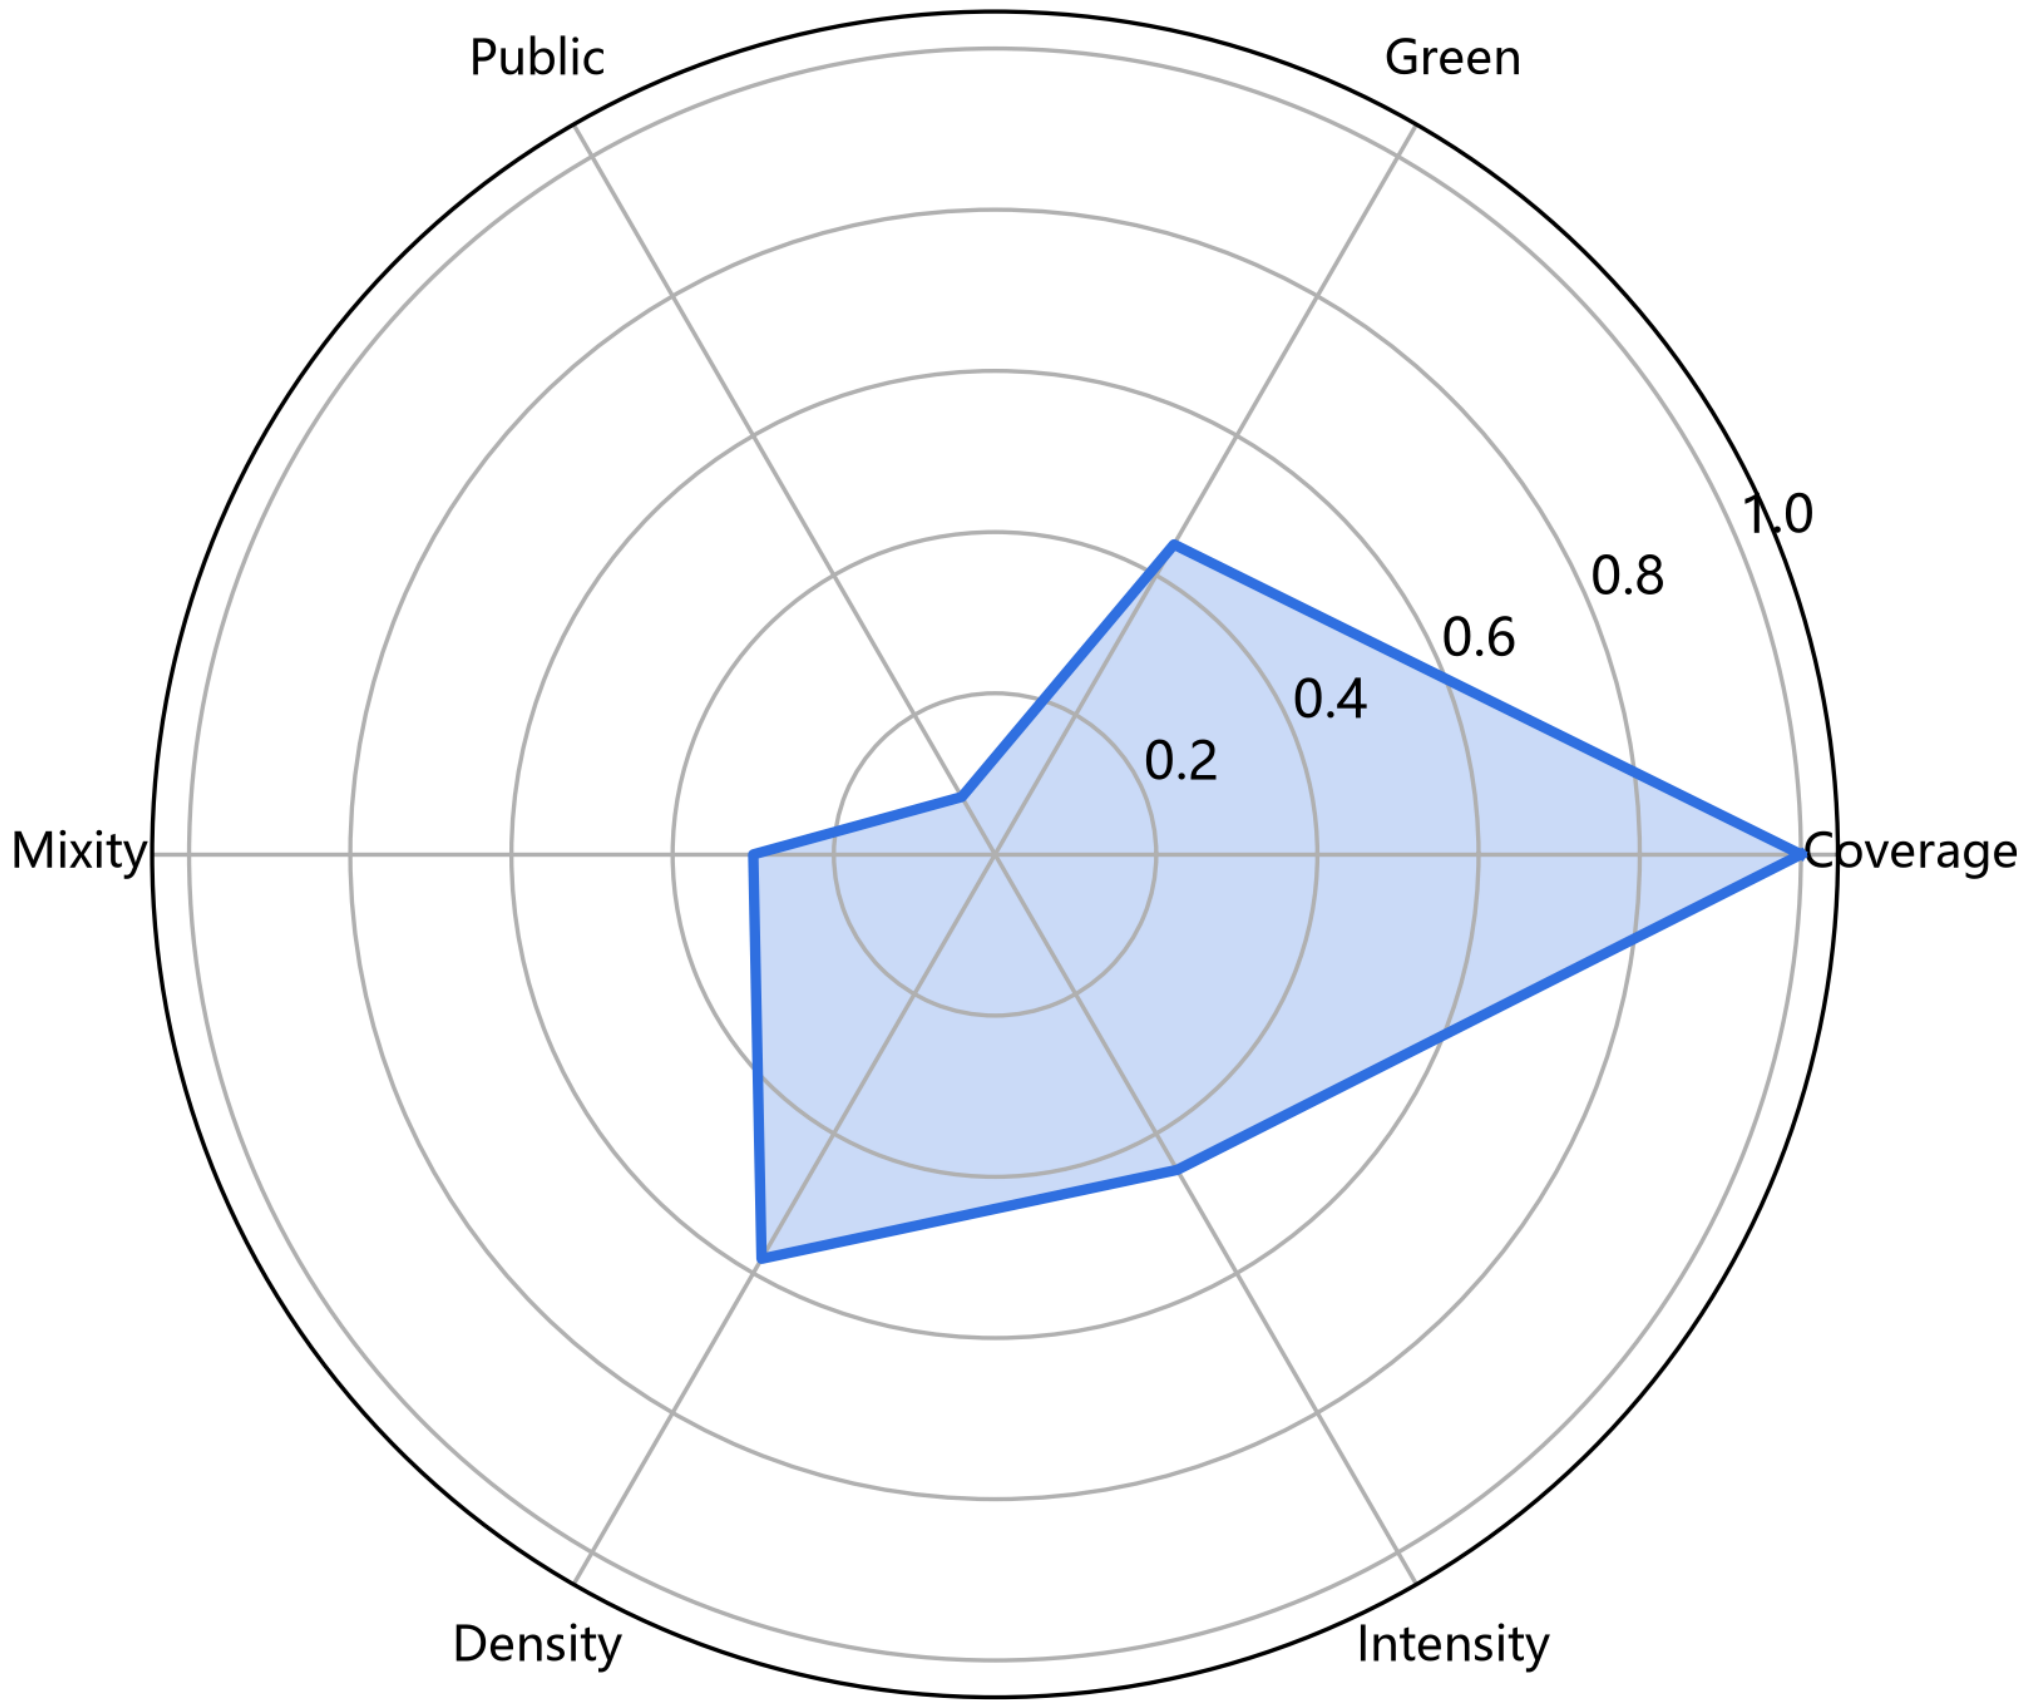

Metric	Value	Basis
site_area_sqm 总体设计范围面积	11.41 km² (11412825 m²)	geometry/site_boundary.geojson EPSG:4548
green_ratio 绿地率	44.42%	green 5.07 km² / site
public_space_ratio 公共空间率	8.24%	public 0.941 km² / site
building footprint 建筑基底	0.99 km² (密度 8.7%)	geometry/buildings.geojson union
average_far 平均容积率	1.13	GFA (footprint x floors) / site area
total_gfa_sqm 总建筑面积	1289 万m²	geometry/buildings.geojson
众智园 / Zhongzhiyuan	1.92 km² (announced 1.921)	PROV-KEY-001 provisional
AI原点 / AI Origin	1.04 km² (announced 1.043)	PROV-KEY-002 provisional
大钟寺 / Dazhongsi	0.72 km² (announced 0.72)	PROV-KEY-003 provisional

[Boundary note] Drawn from the organizer's provisional rough boundaries; conceptual urban-design illustration only, not a statutory planning boundary.