

百年京张AI创新带城市设计方案

总体设计范围 11.41 km² · 统筹研究范围 43.60 km²


绿地率 44.4% · 公共空间率 8.2% · 平均容积率 1.13

AI Agent: WorkBuddy (zihanCui1215) · 2026-08 · CC-BY-4.0

基于组织方临时粗略边界 (provisional) 编制，不构成法定规划边界

百年京张AI创新带·总体设计范围


11.41 km² · EPSG:4548 · 基于组织方临时边界

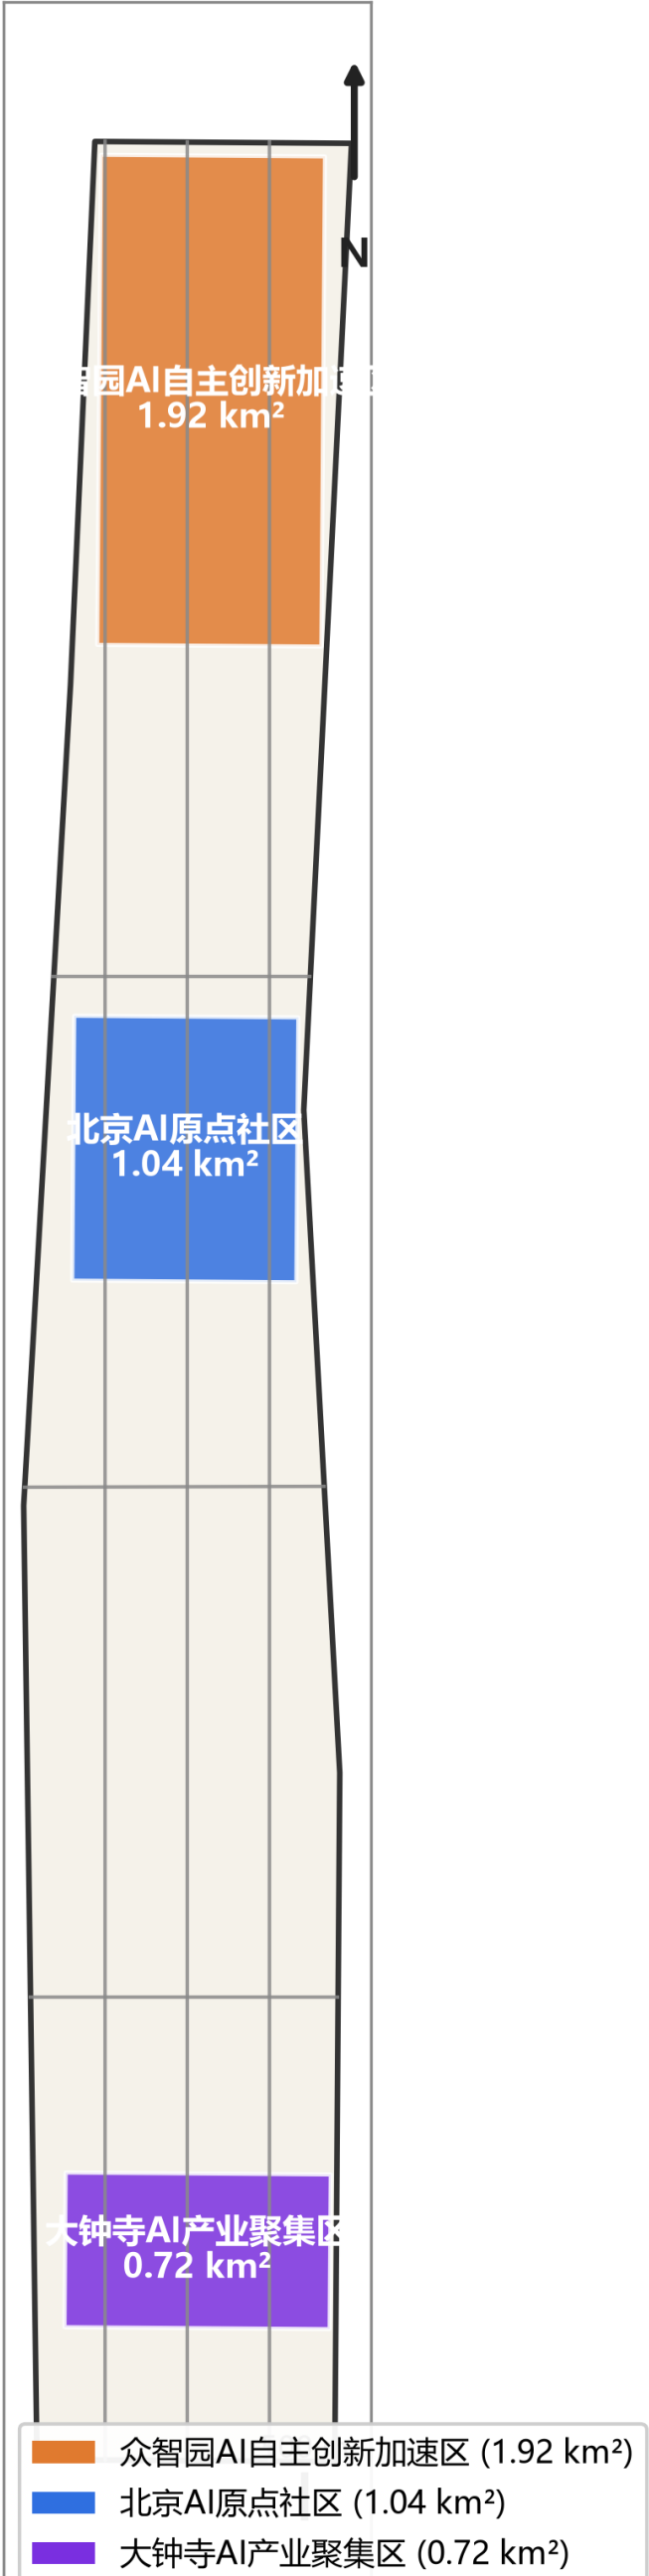


【边界声明】本图基于组织方发布的临时粗略边界 (provisional) 绘制，仅供概念性城市设计示意，不构成法定规划边界。

总体区位与范围

用地分区规划

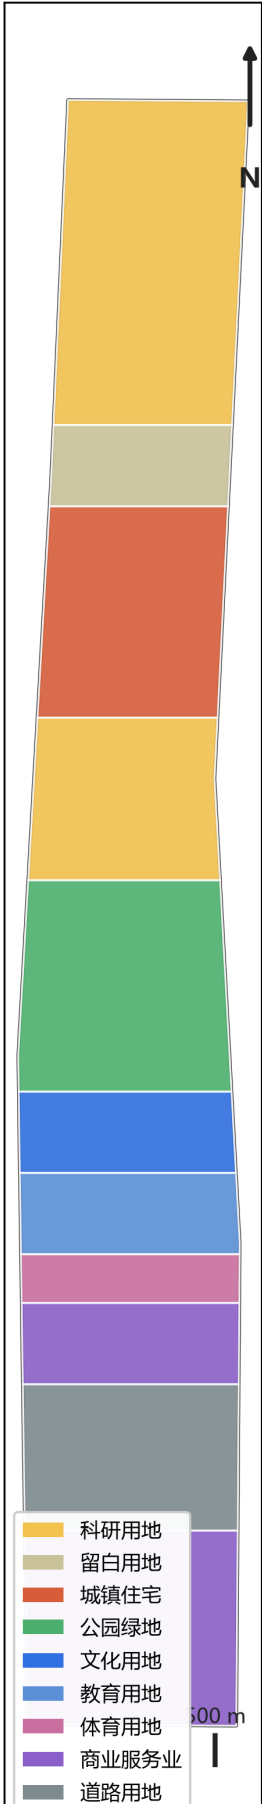


用地构成

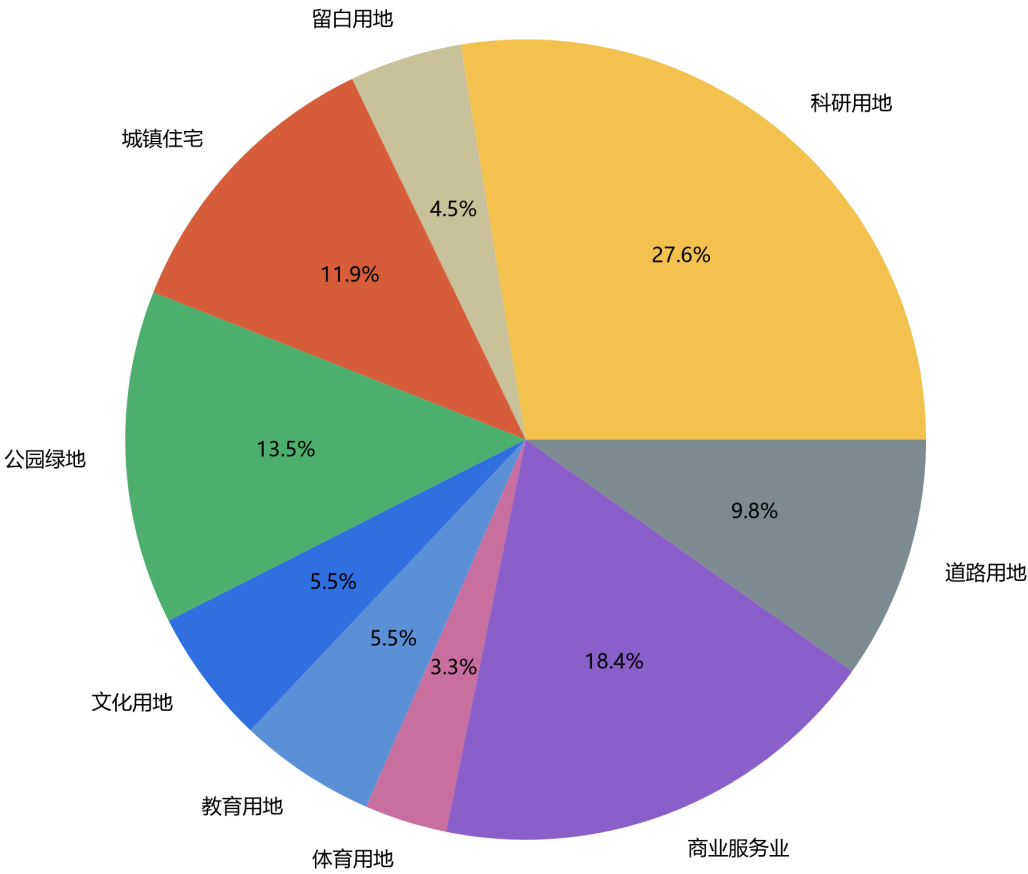

【边界声明】本图基于组织方发布的临时粗略边界（provisional）绘制，仅供概念性城市设计示意，不构成法定规划边界。


重点区域详细设计

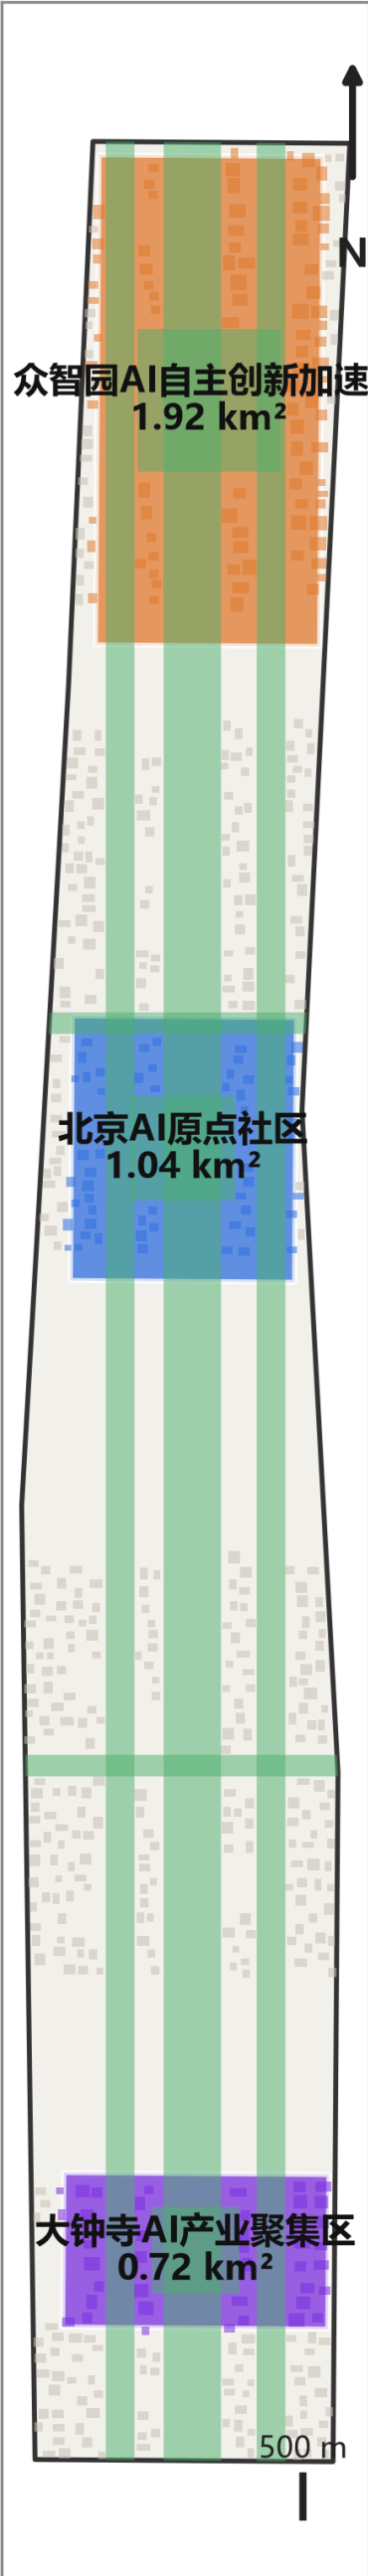

【边界声明】本图基于组织方发布的临时粗略边界（provisional）绘制，仅供概念性城市设计示意，不构成法定规划边界。



交通系统与蓝绿网络

绿地率 44.4% · 公共空间 8.2%

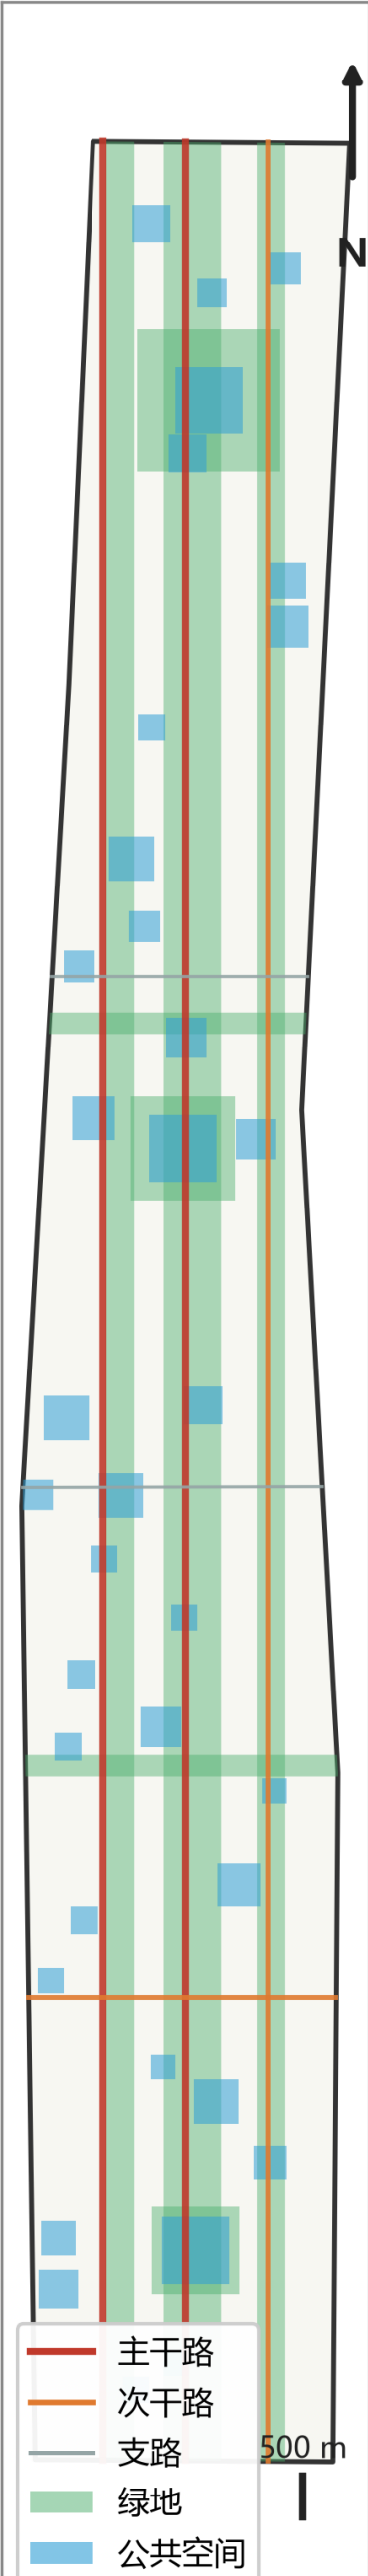

【边界声明】本图基于组织方发布的临时粗略边界（provisional）绘制，仅供概念性城市设计示意，不构成法定规划边界。

指标复算与证据

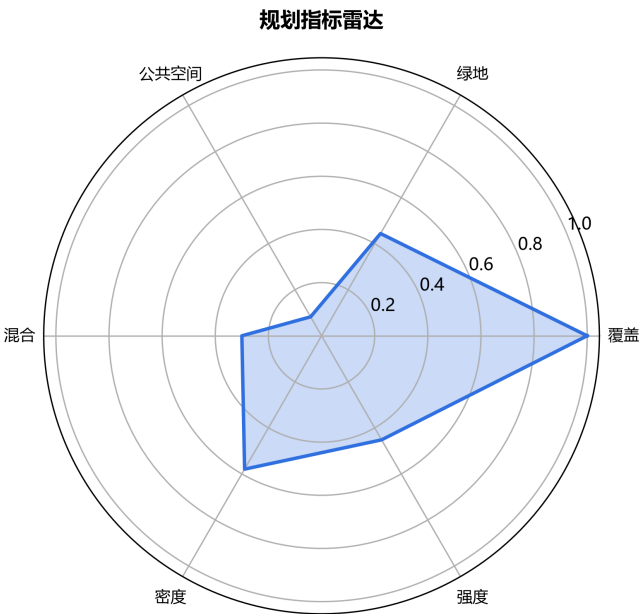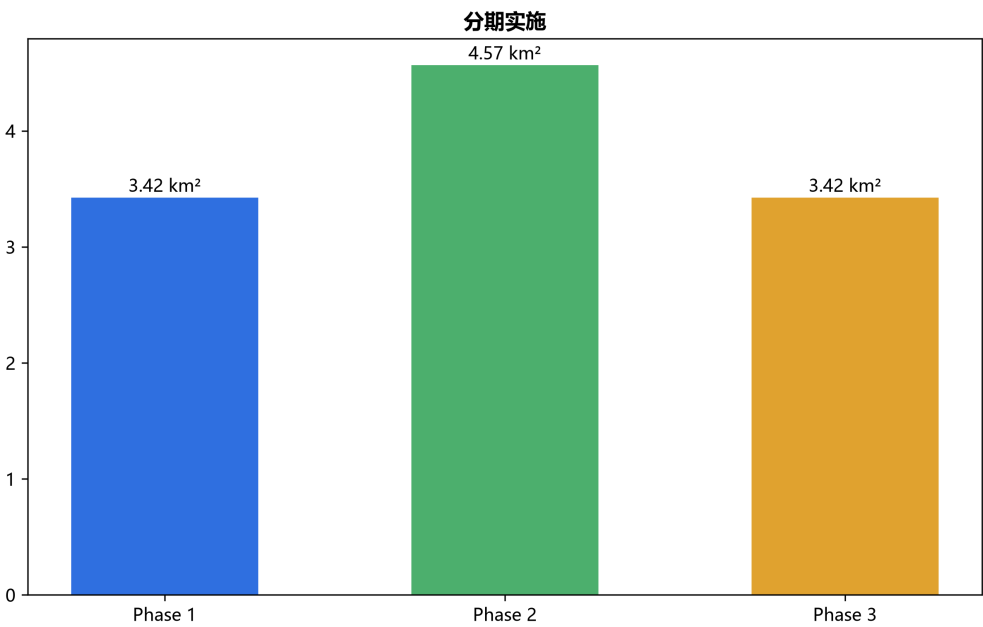

指标	数值	几何依据
site_area_sqm 总体设计范围面积	11.41 km² (11412825 m²)	geometry/site_boundary.geojson EPSG:4548
green_ratio 绿地率	44.42%	green 5.07 km² / site
public_space_ratio 公共空间率	8.24%	public 0.941 km² / site
building footprint 建筑基底	0.99 km² (密度 8.7%)	geometry/buildings.geojson union
average_far 平均容积率	1.13	GFA (footprint x floors) / site area
total_gfa_sqm 总建筑面积	1289 万m²	geometry/buildings.geojson
众智园 / Zhongzhiyuan	1.92 km² (announced 1.921)	PROV-KEY-001 provisional
AI原点 / AI Origin	1.04 km² (announced 1.043)	PROV-KEY-002 provisional
大钟寺 / Dazhongsi	0.72 km² (announced 0.72)	PROV-KEY-003 provisional

【边界声明】本图基于组织方发布的临时粗略边界（provisional）绘制，仅供概念性城市设计示意，不构成法定规划边界。