


从自主铁路到自主智能

把百年自主铁路的工程精神，转译为一条可步行、可验证、可退出的公共创新带。

11.4 km² 总体设计主总平


连续公共创新带 | 顺时针旋转 90°

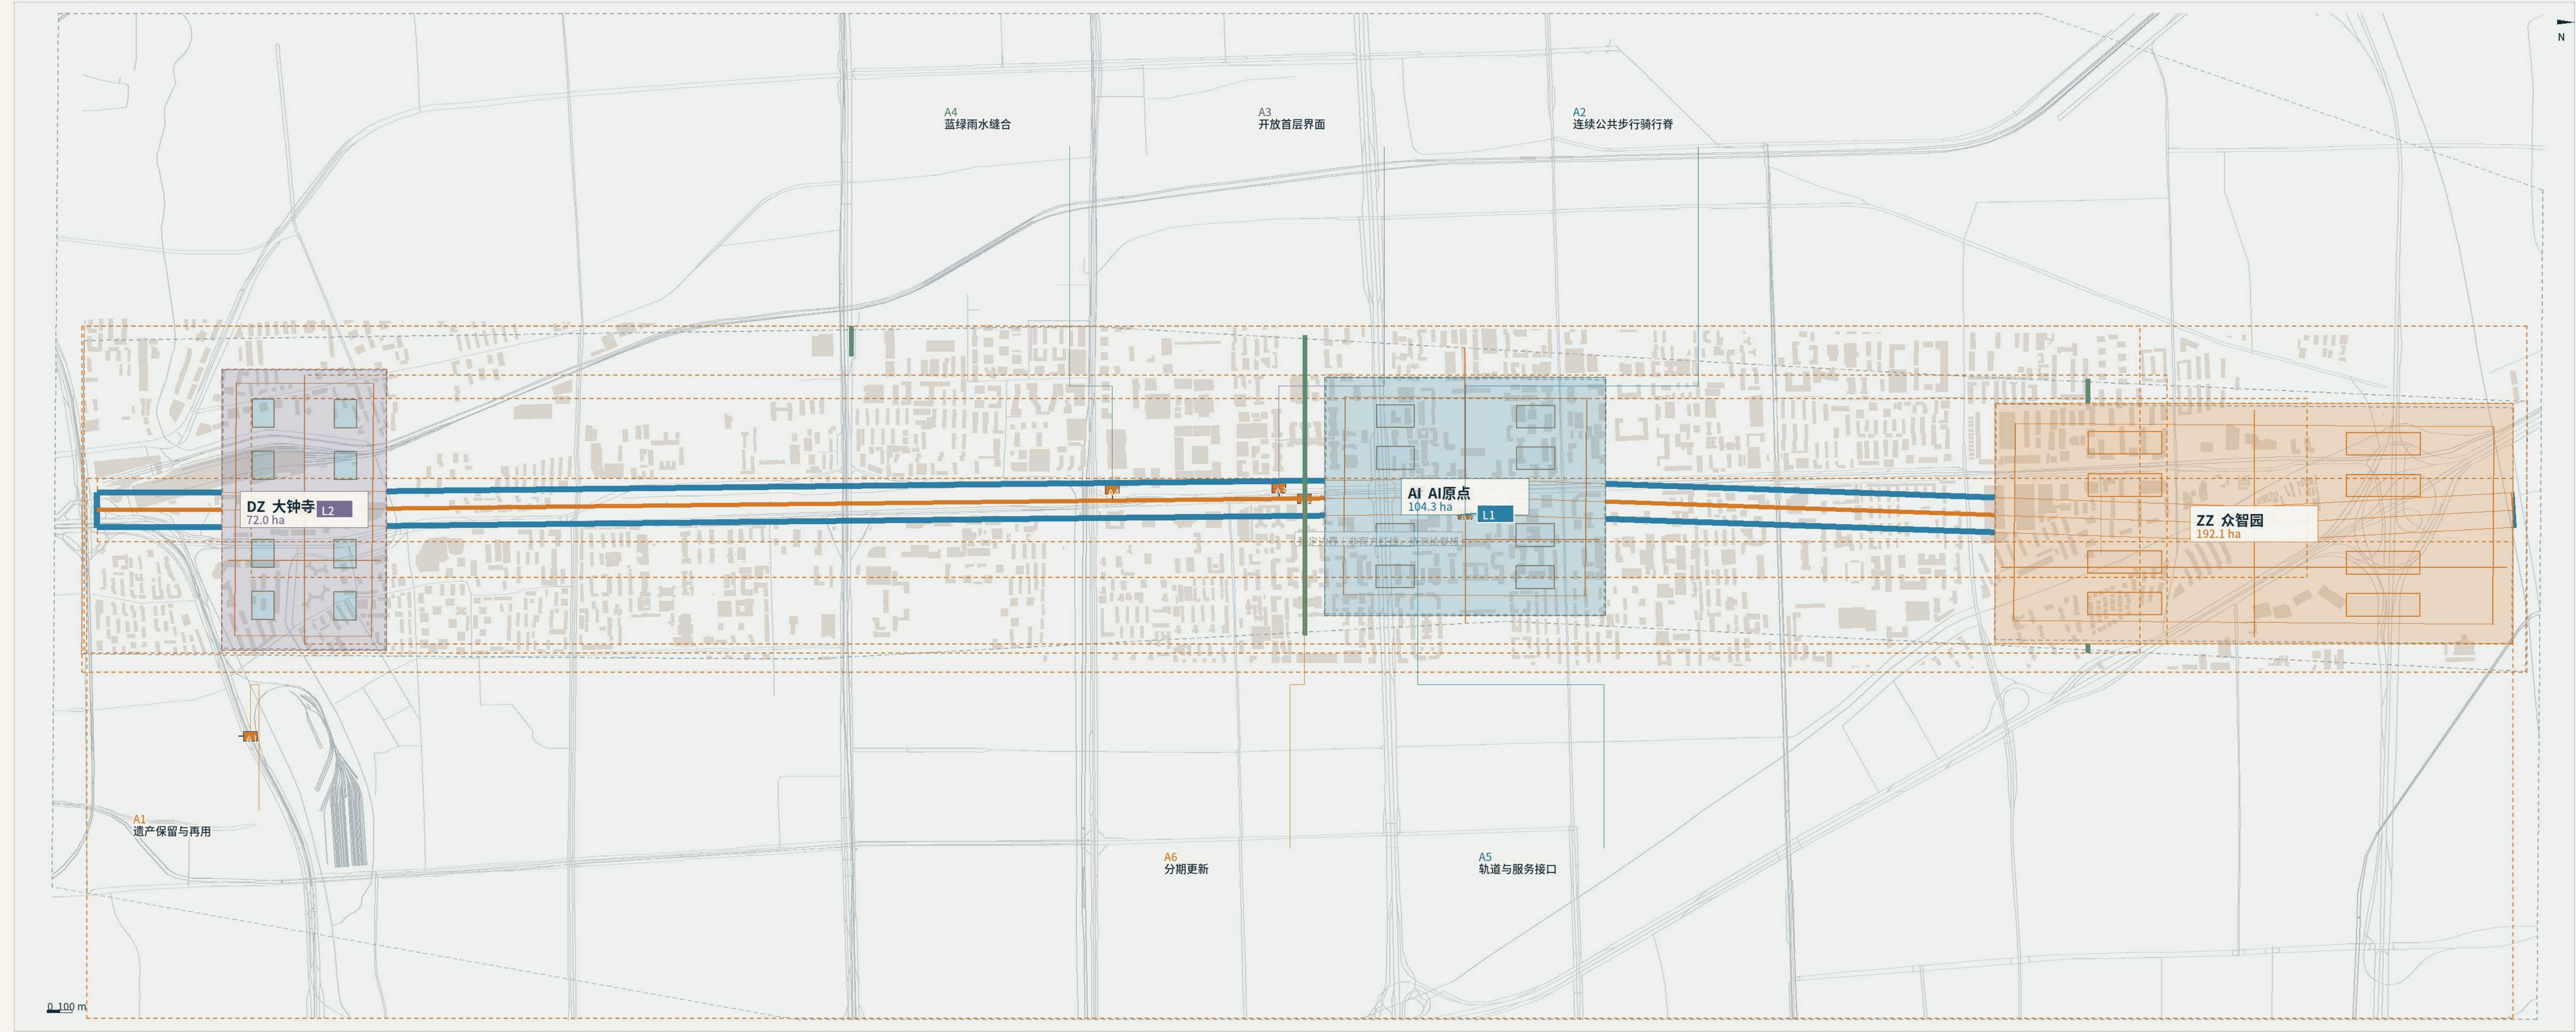

L-B01-01, L-B01-02 | 面积数字为官方文本事实；边界为暂定、建筑与空间动作属于概念设计，待测绘、法定程序与多专业复核。

43.6 km² 区域脉络

京张走廊 | 北—中—南

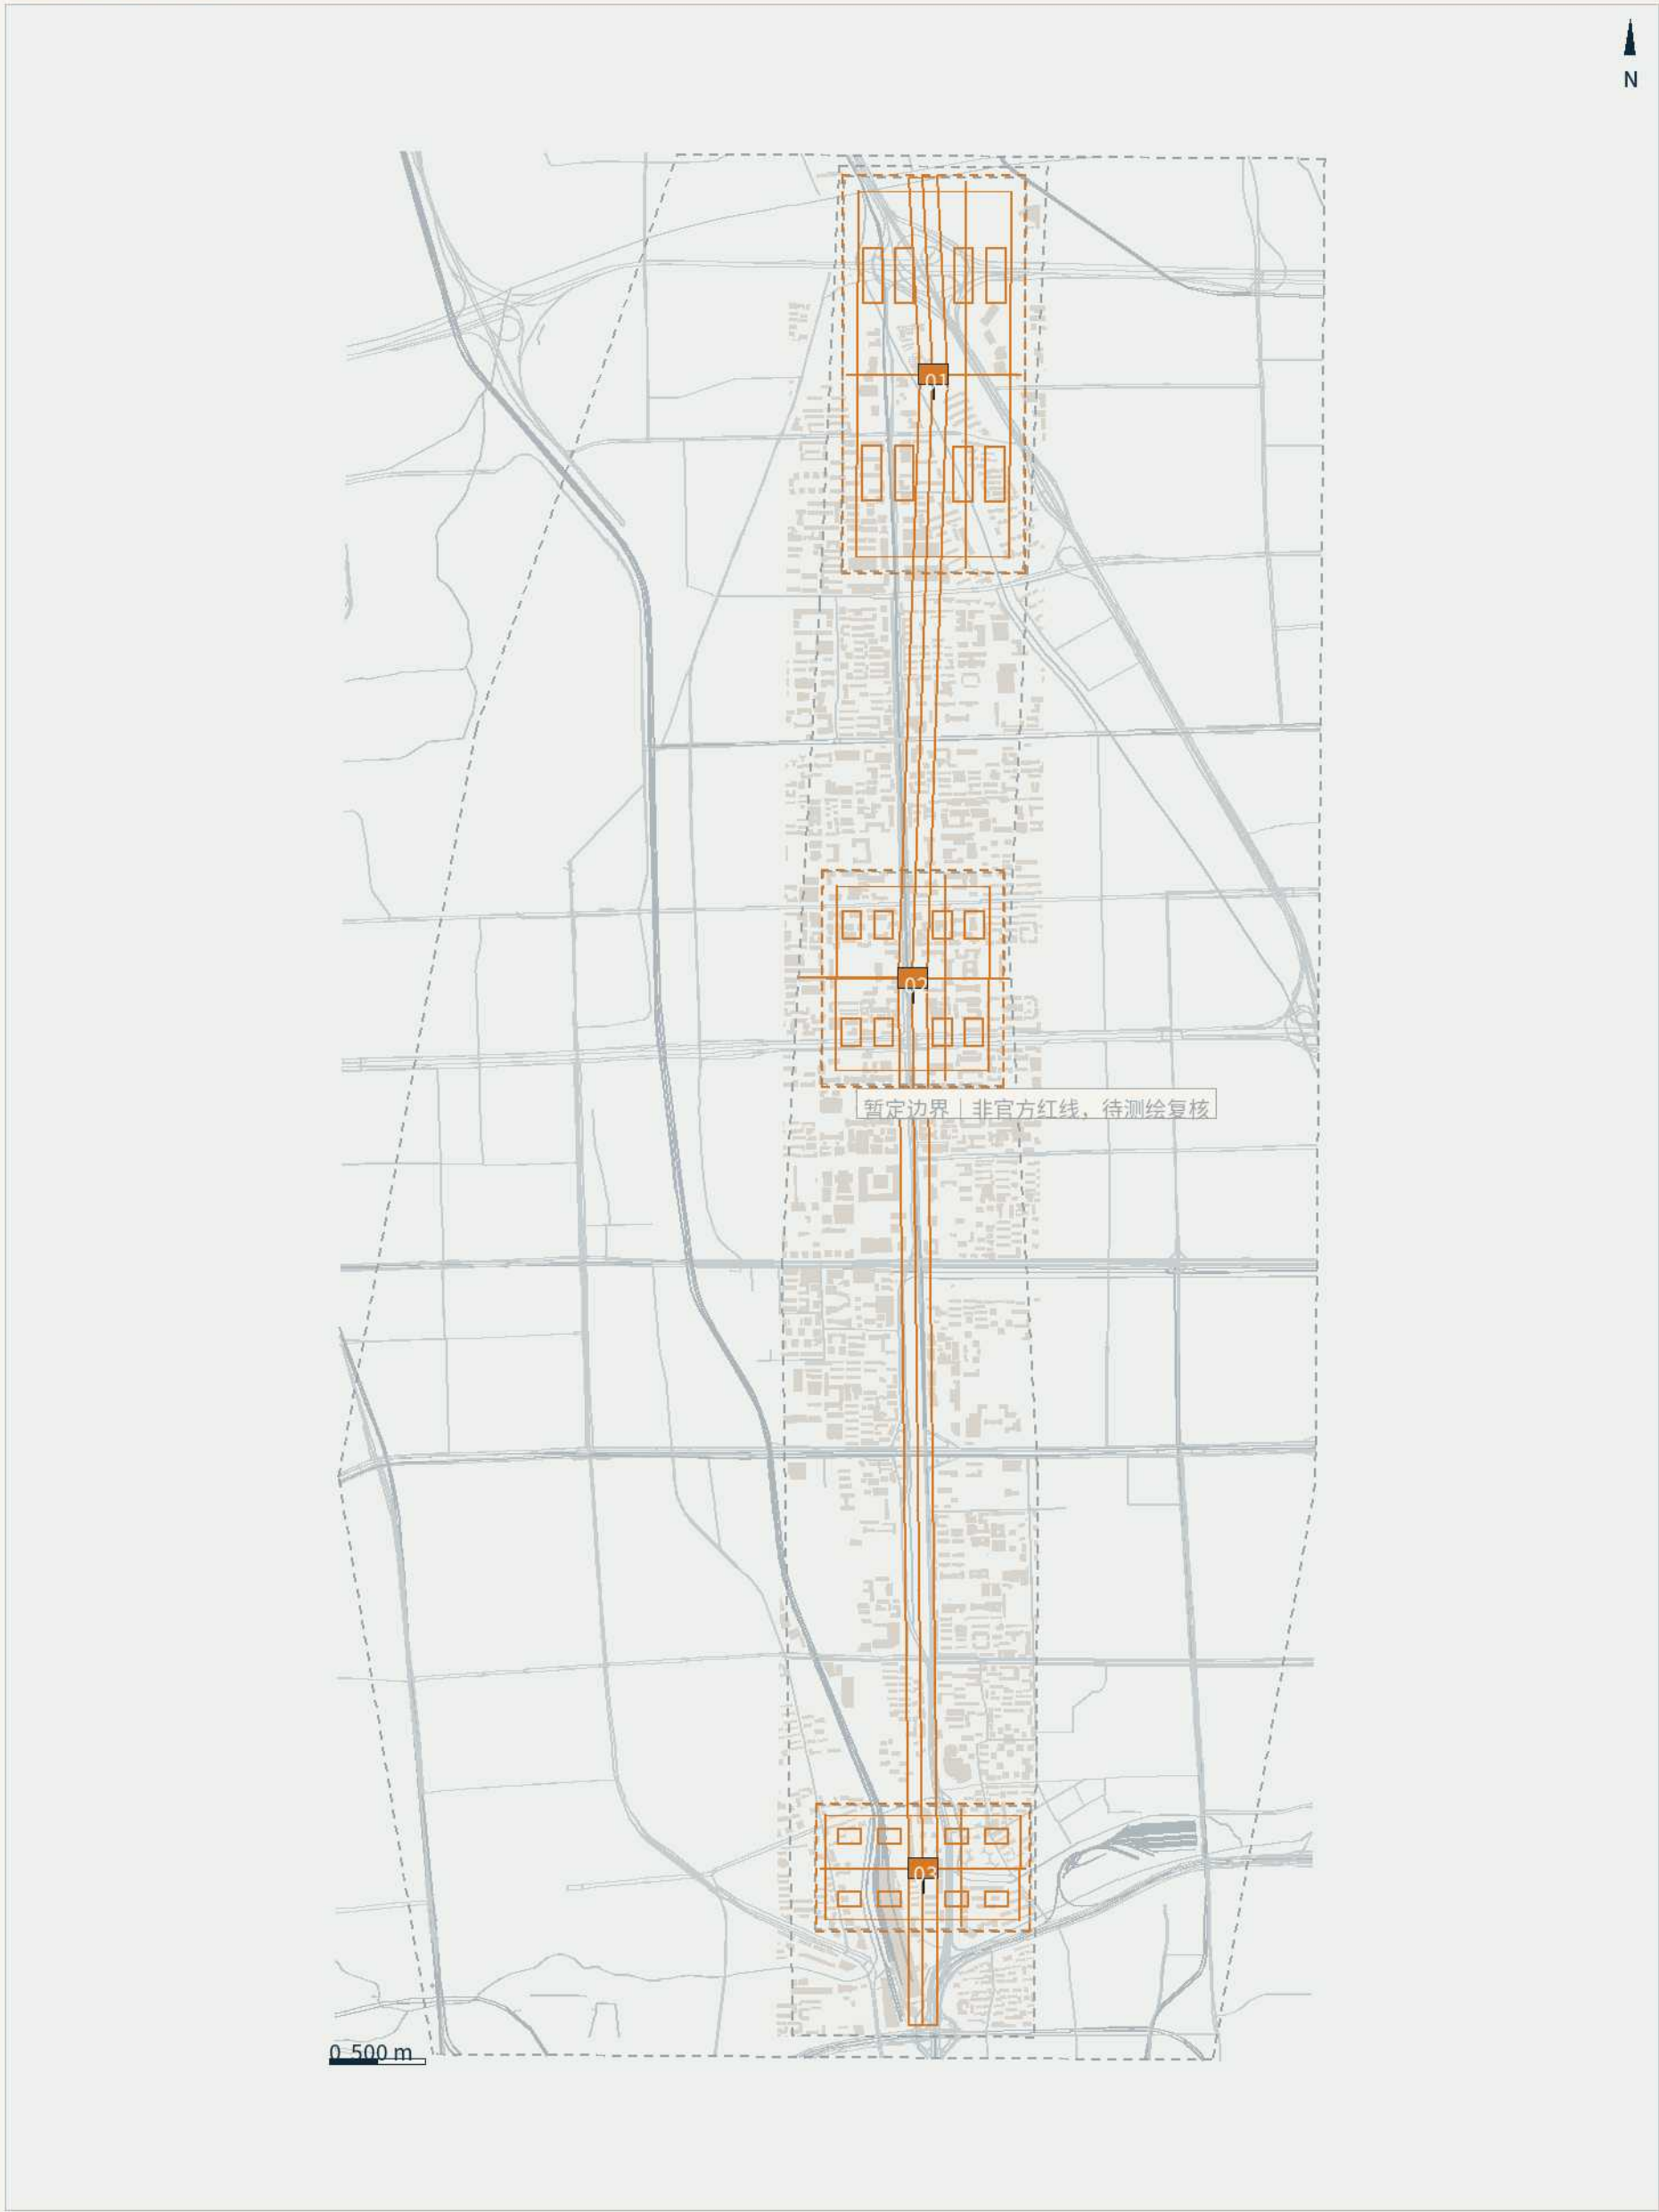

| 面积数字为官方文本事实；边界为暂定、建筑与空间动作属于概念设计，待测绘、法定程序与多专业复核。



L1 走廊全景 | 总平派生轴测；高度仅示意




L2 大神寺概念场景 | 非地理证据




ZZ 众智园 | 独立概念场景



AI AI原点 | 独立概念场景

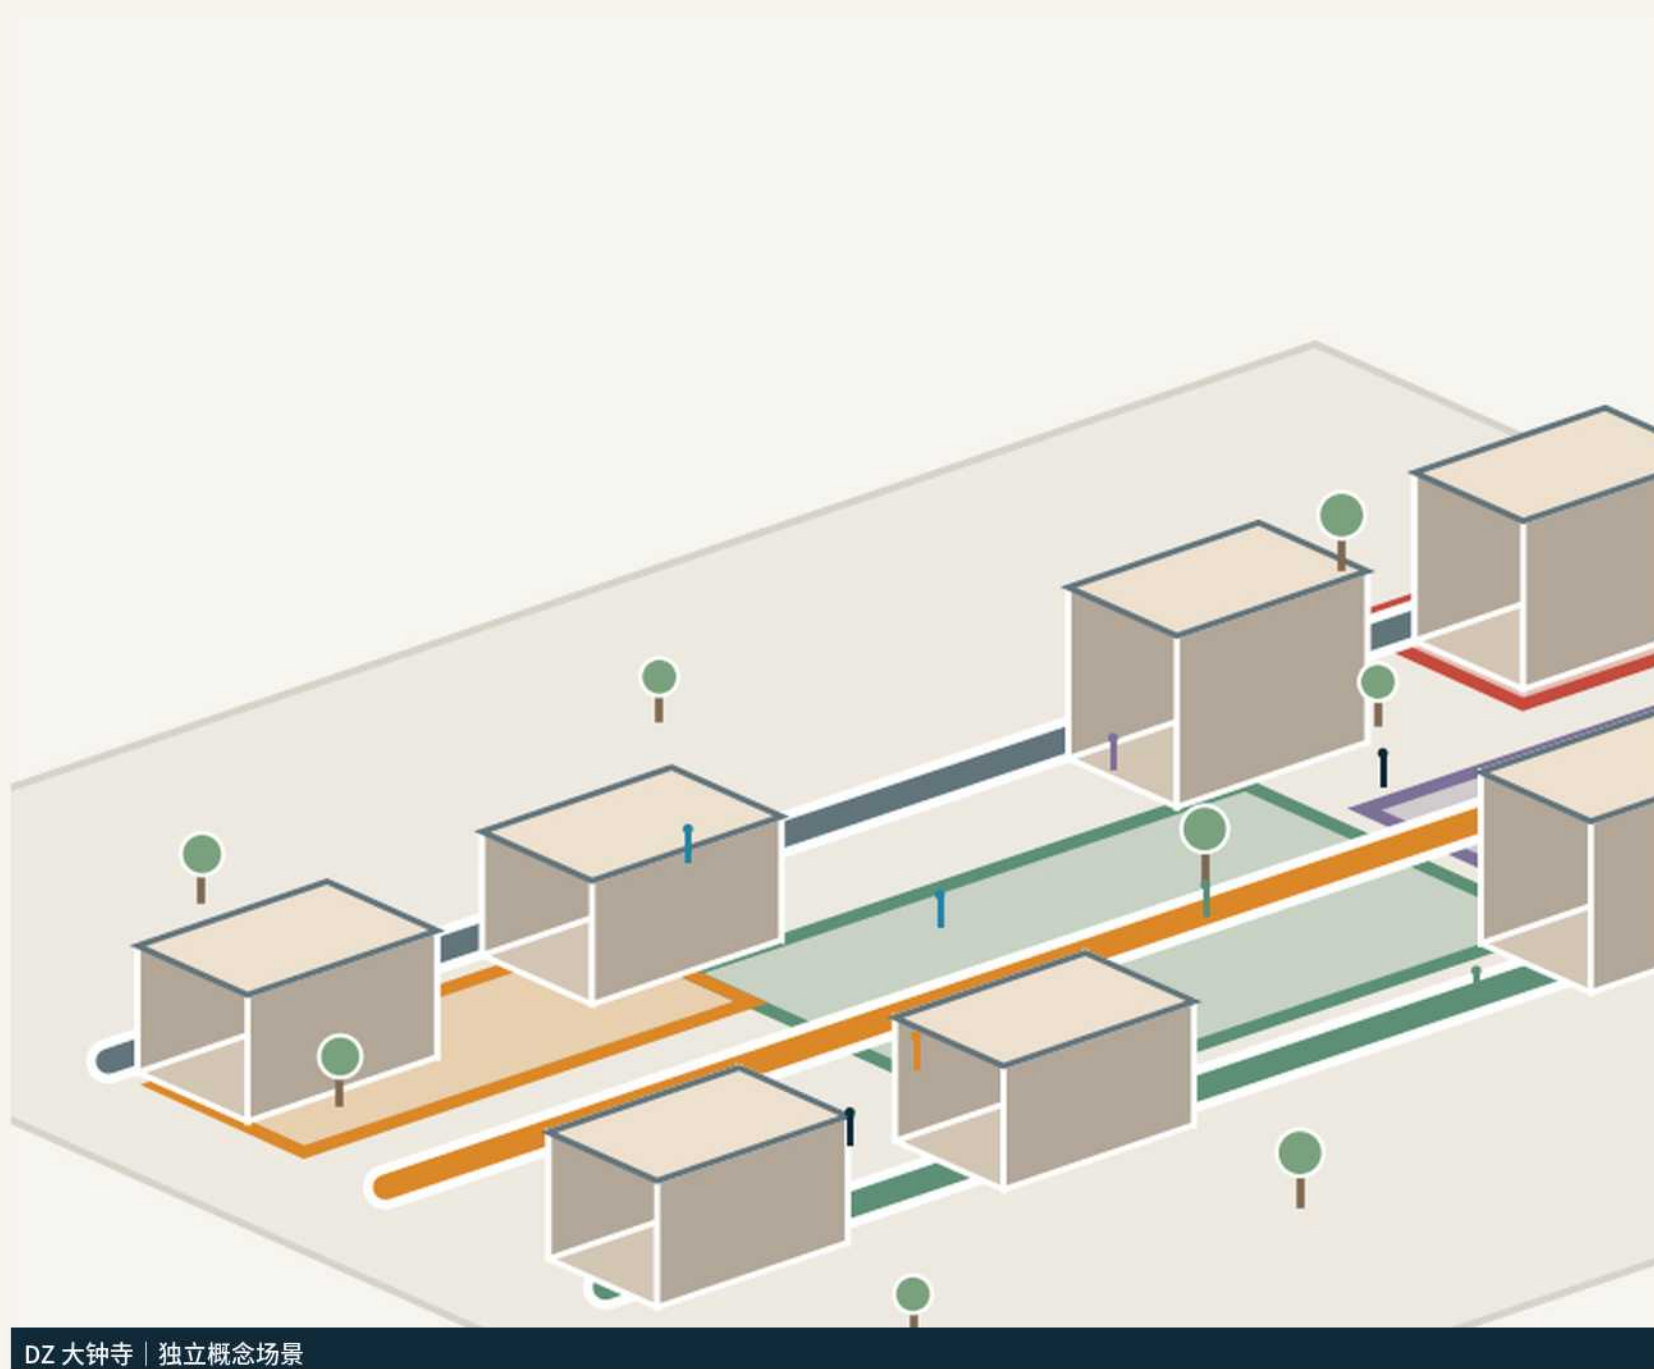


DZ 大神寺 | 独立概念场景

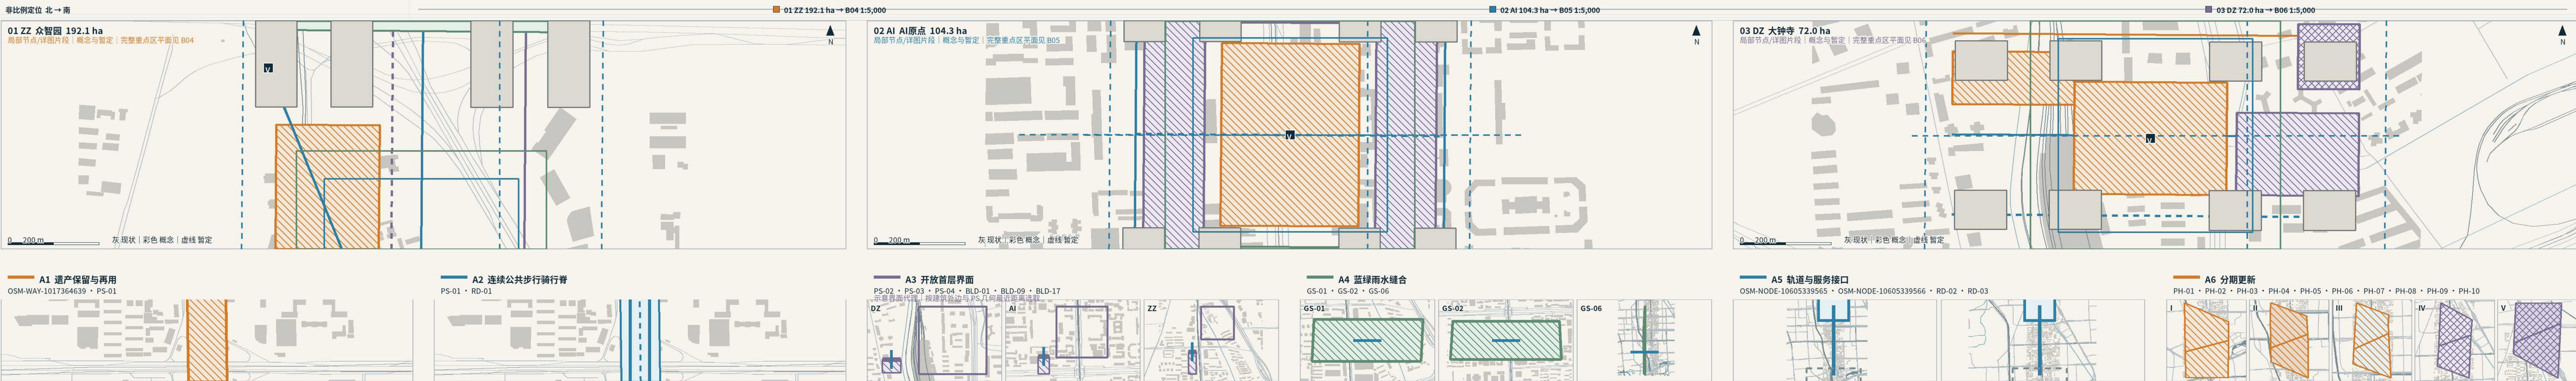


面积为官方文本事实 | 边界暂定 | 公共背景来自注册数据 | 建筑/动作/高度为概念与示意 | 待测绘、法定与多专业复核

城市更新与产业空间


以公开方位为底、概念放置为动作、专业交接为边界，形成可验证、可调整、可退出的渐进更新框架。

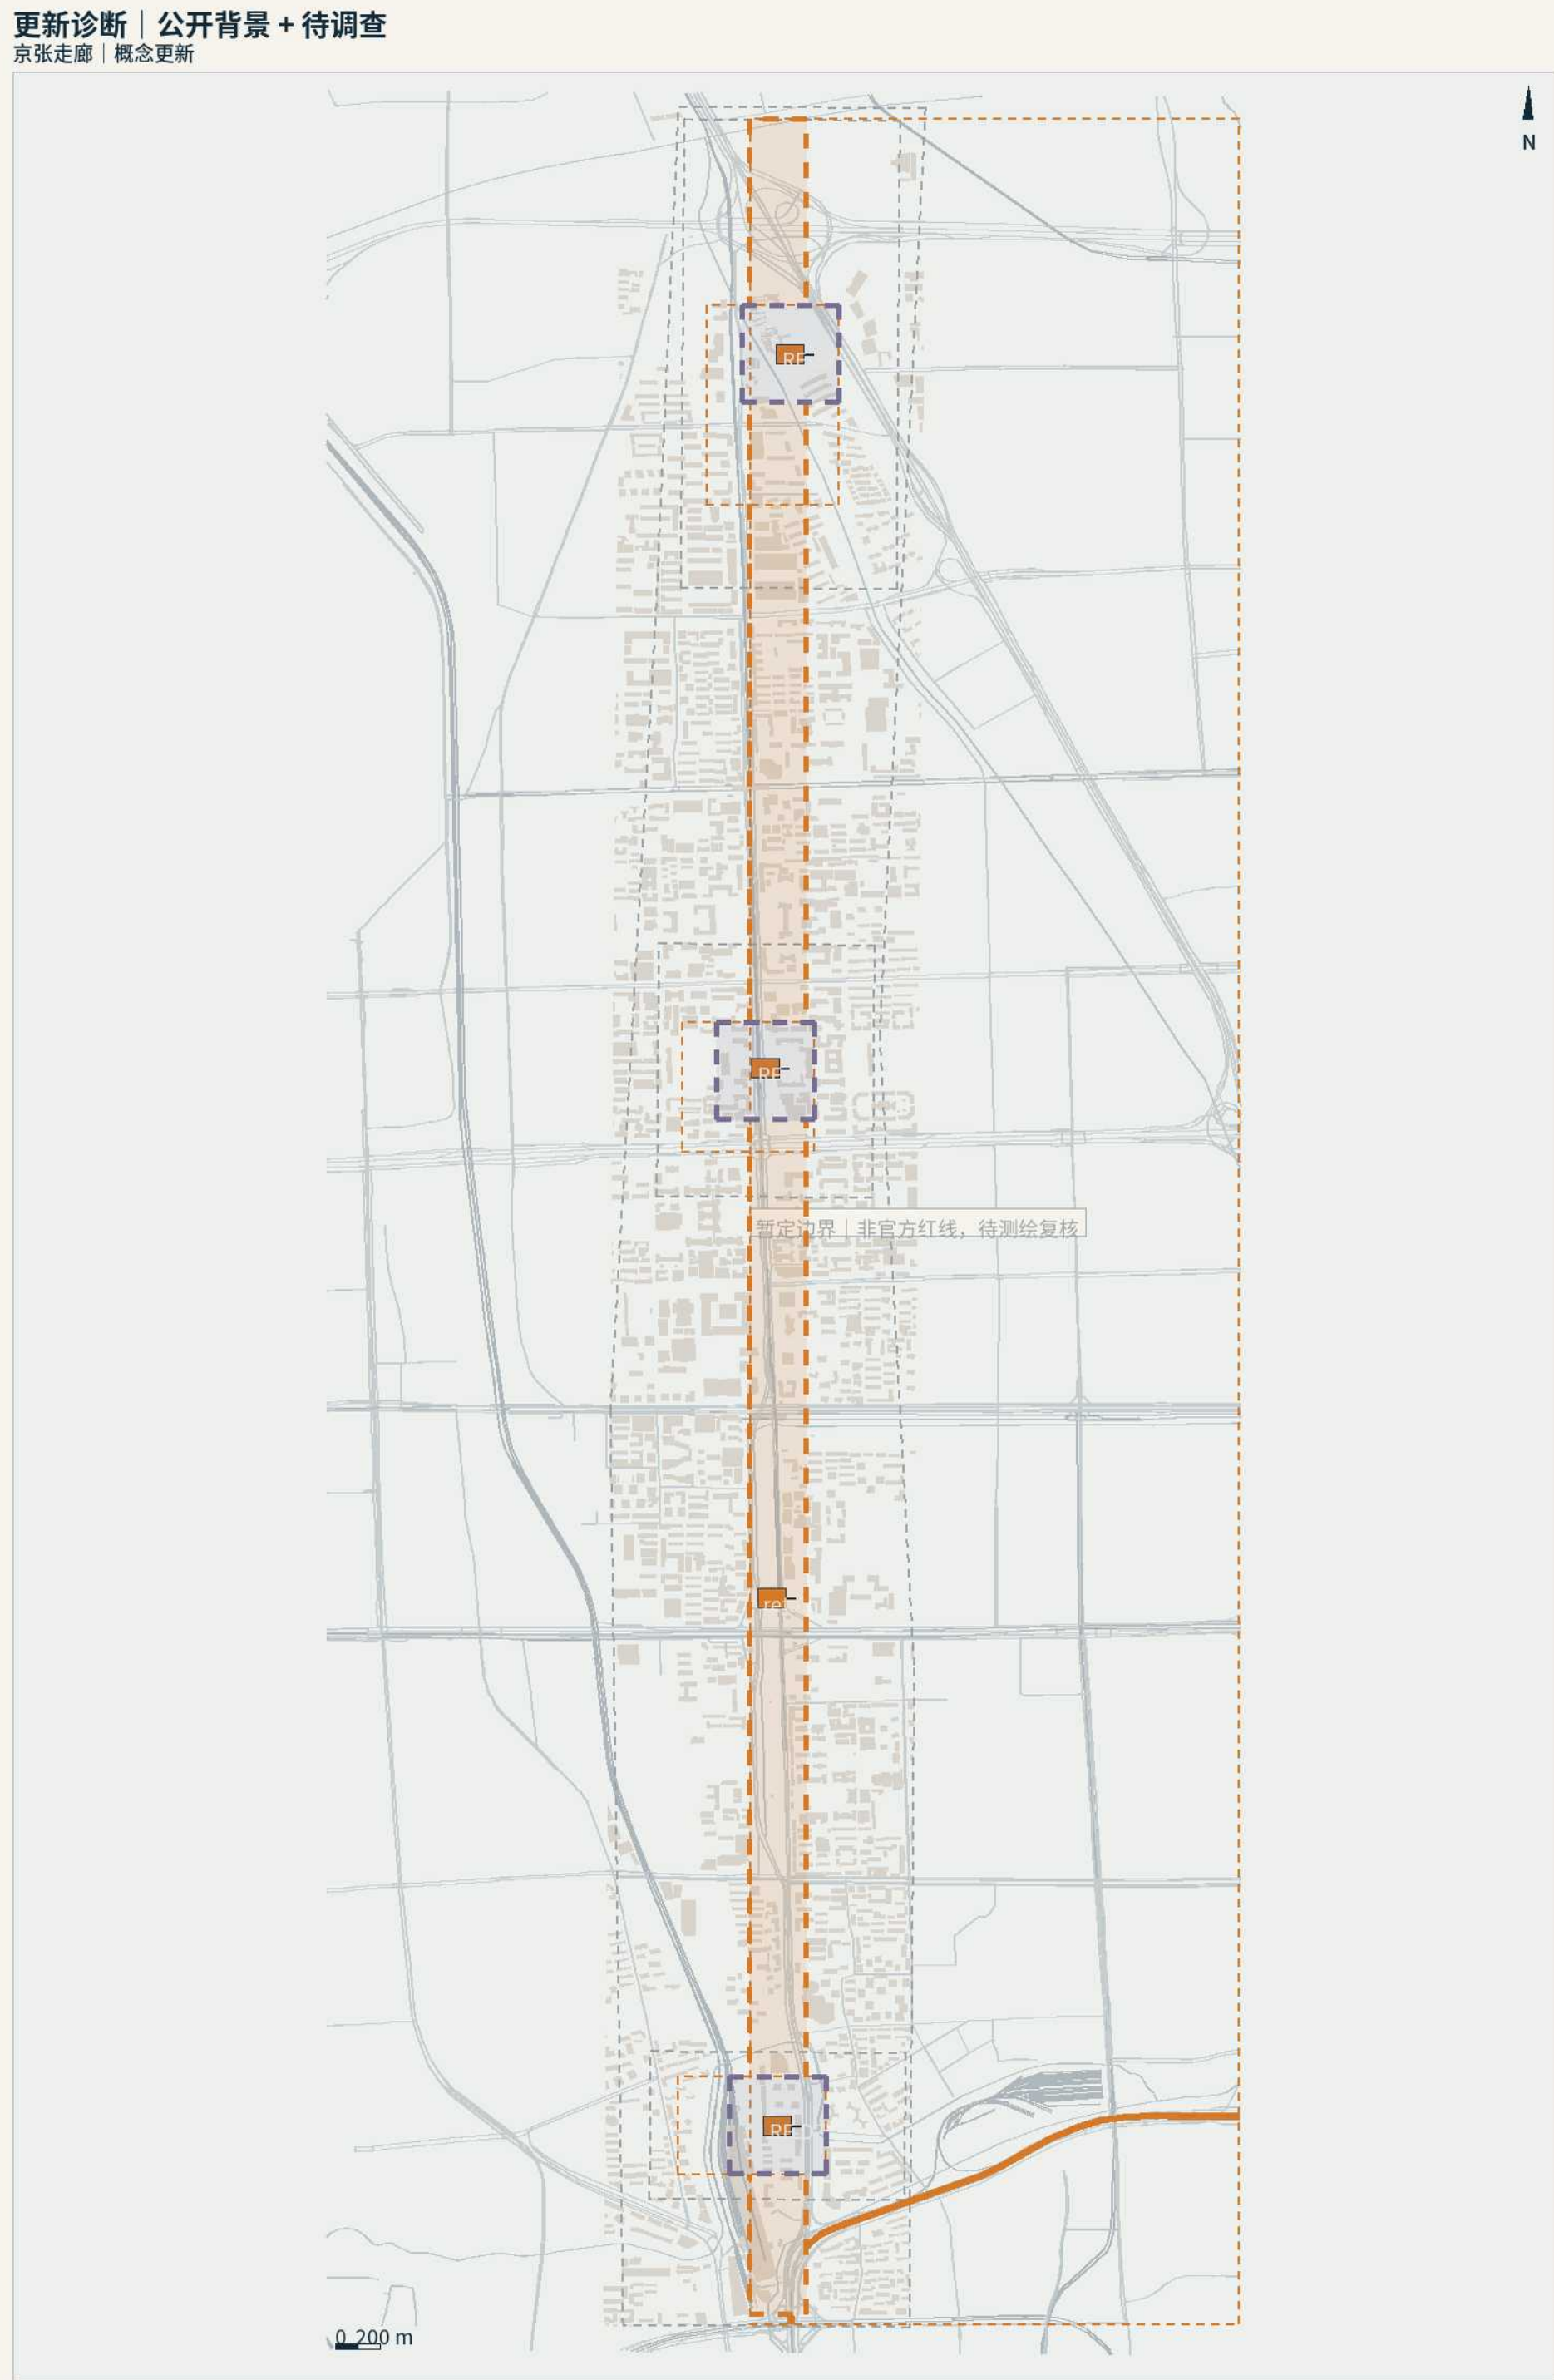


| 灰色为公开方位背景；彩色为参与者概念放置；虚线边界与所有更新、业主、强度和实施关系均待测绘、法定与多专业确认。

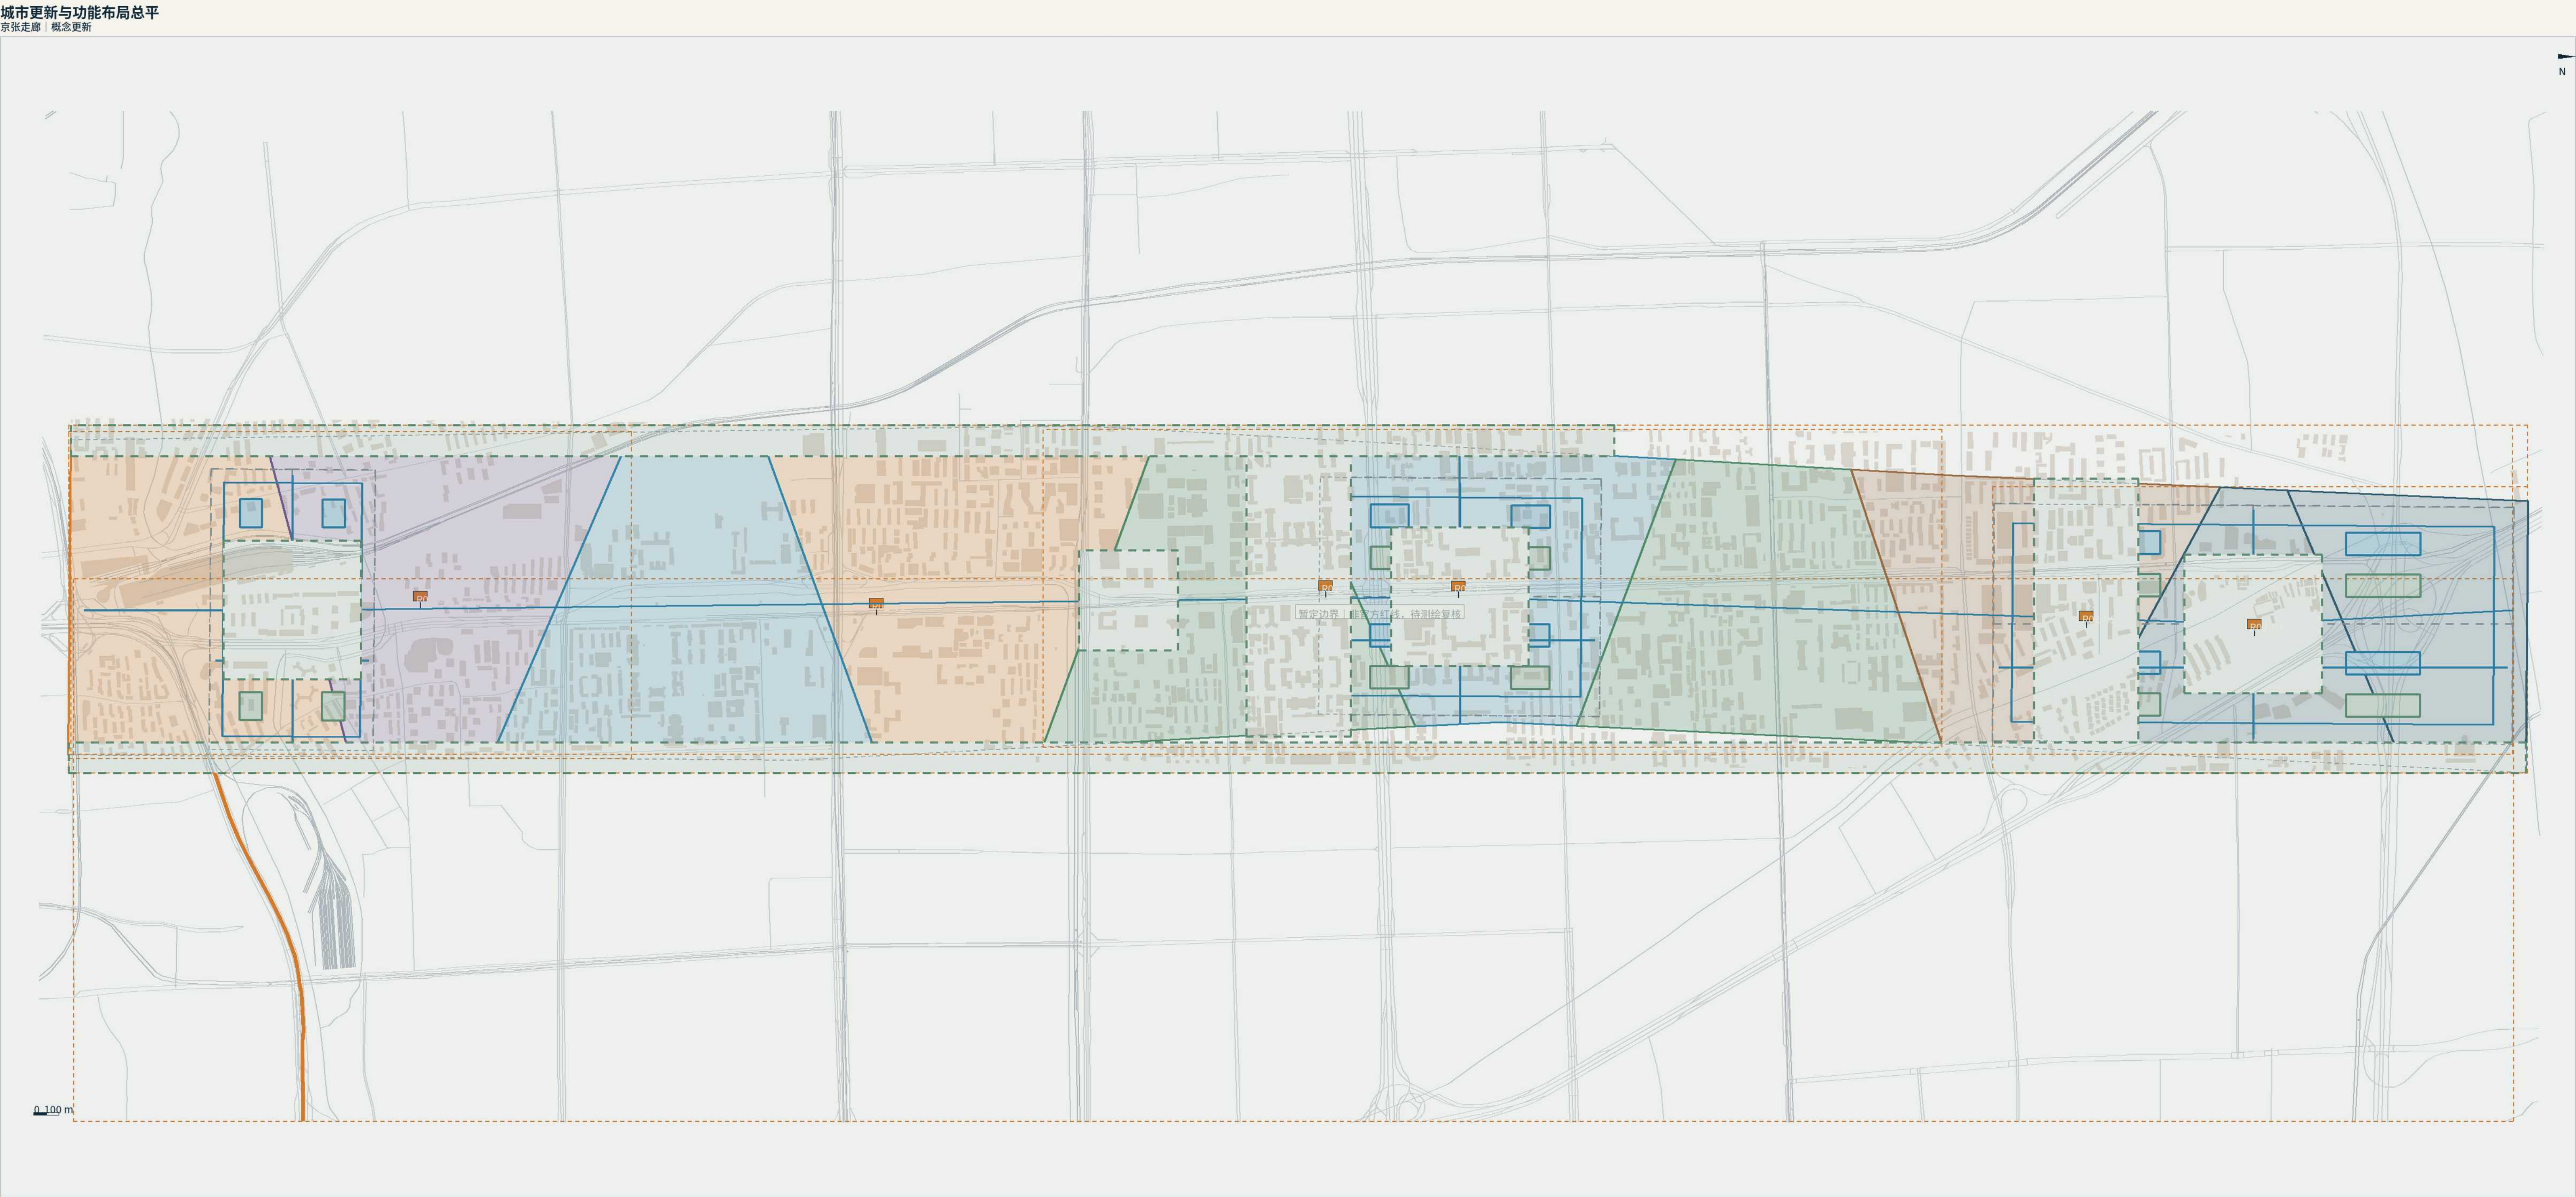


| 灰色为公开方位背景；彩色为参与者概念放置；虚线边界与所有更新、业主、强度和实施关系均待测绘、法定与多专业确认。

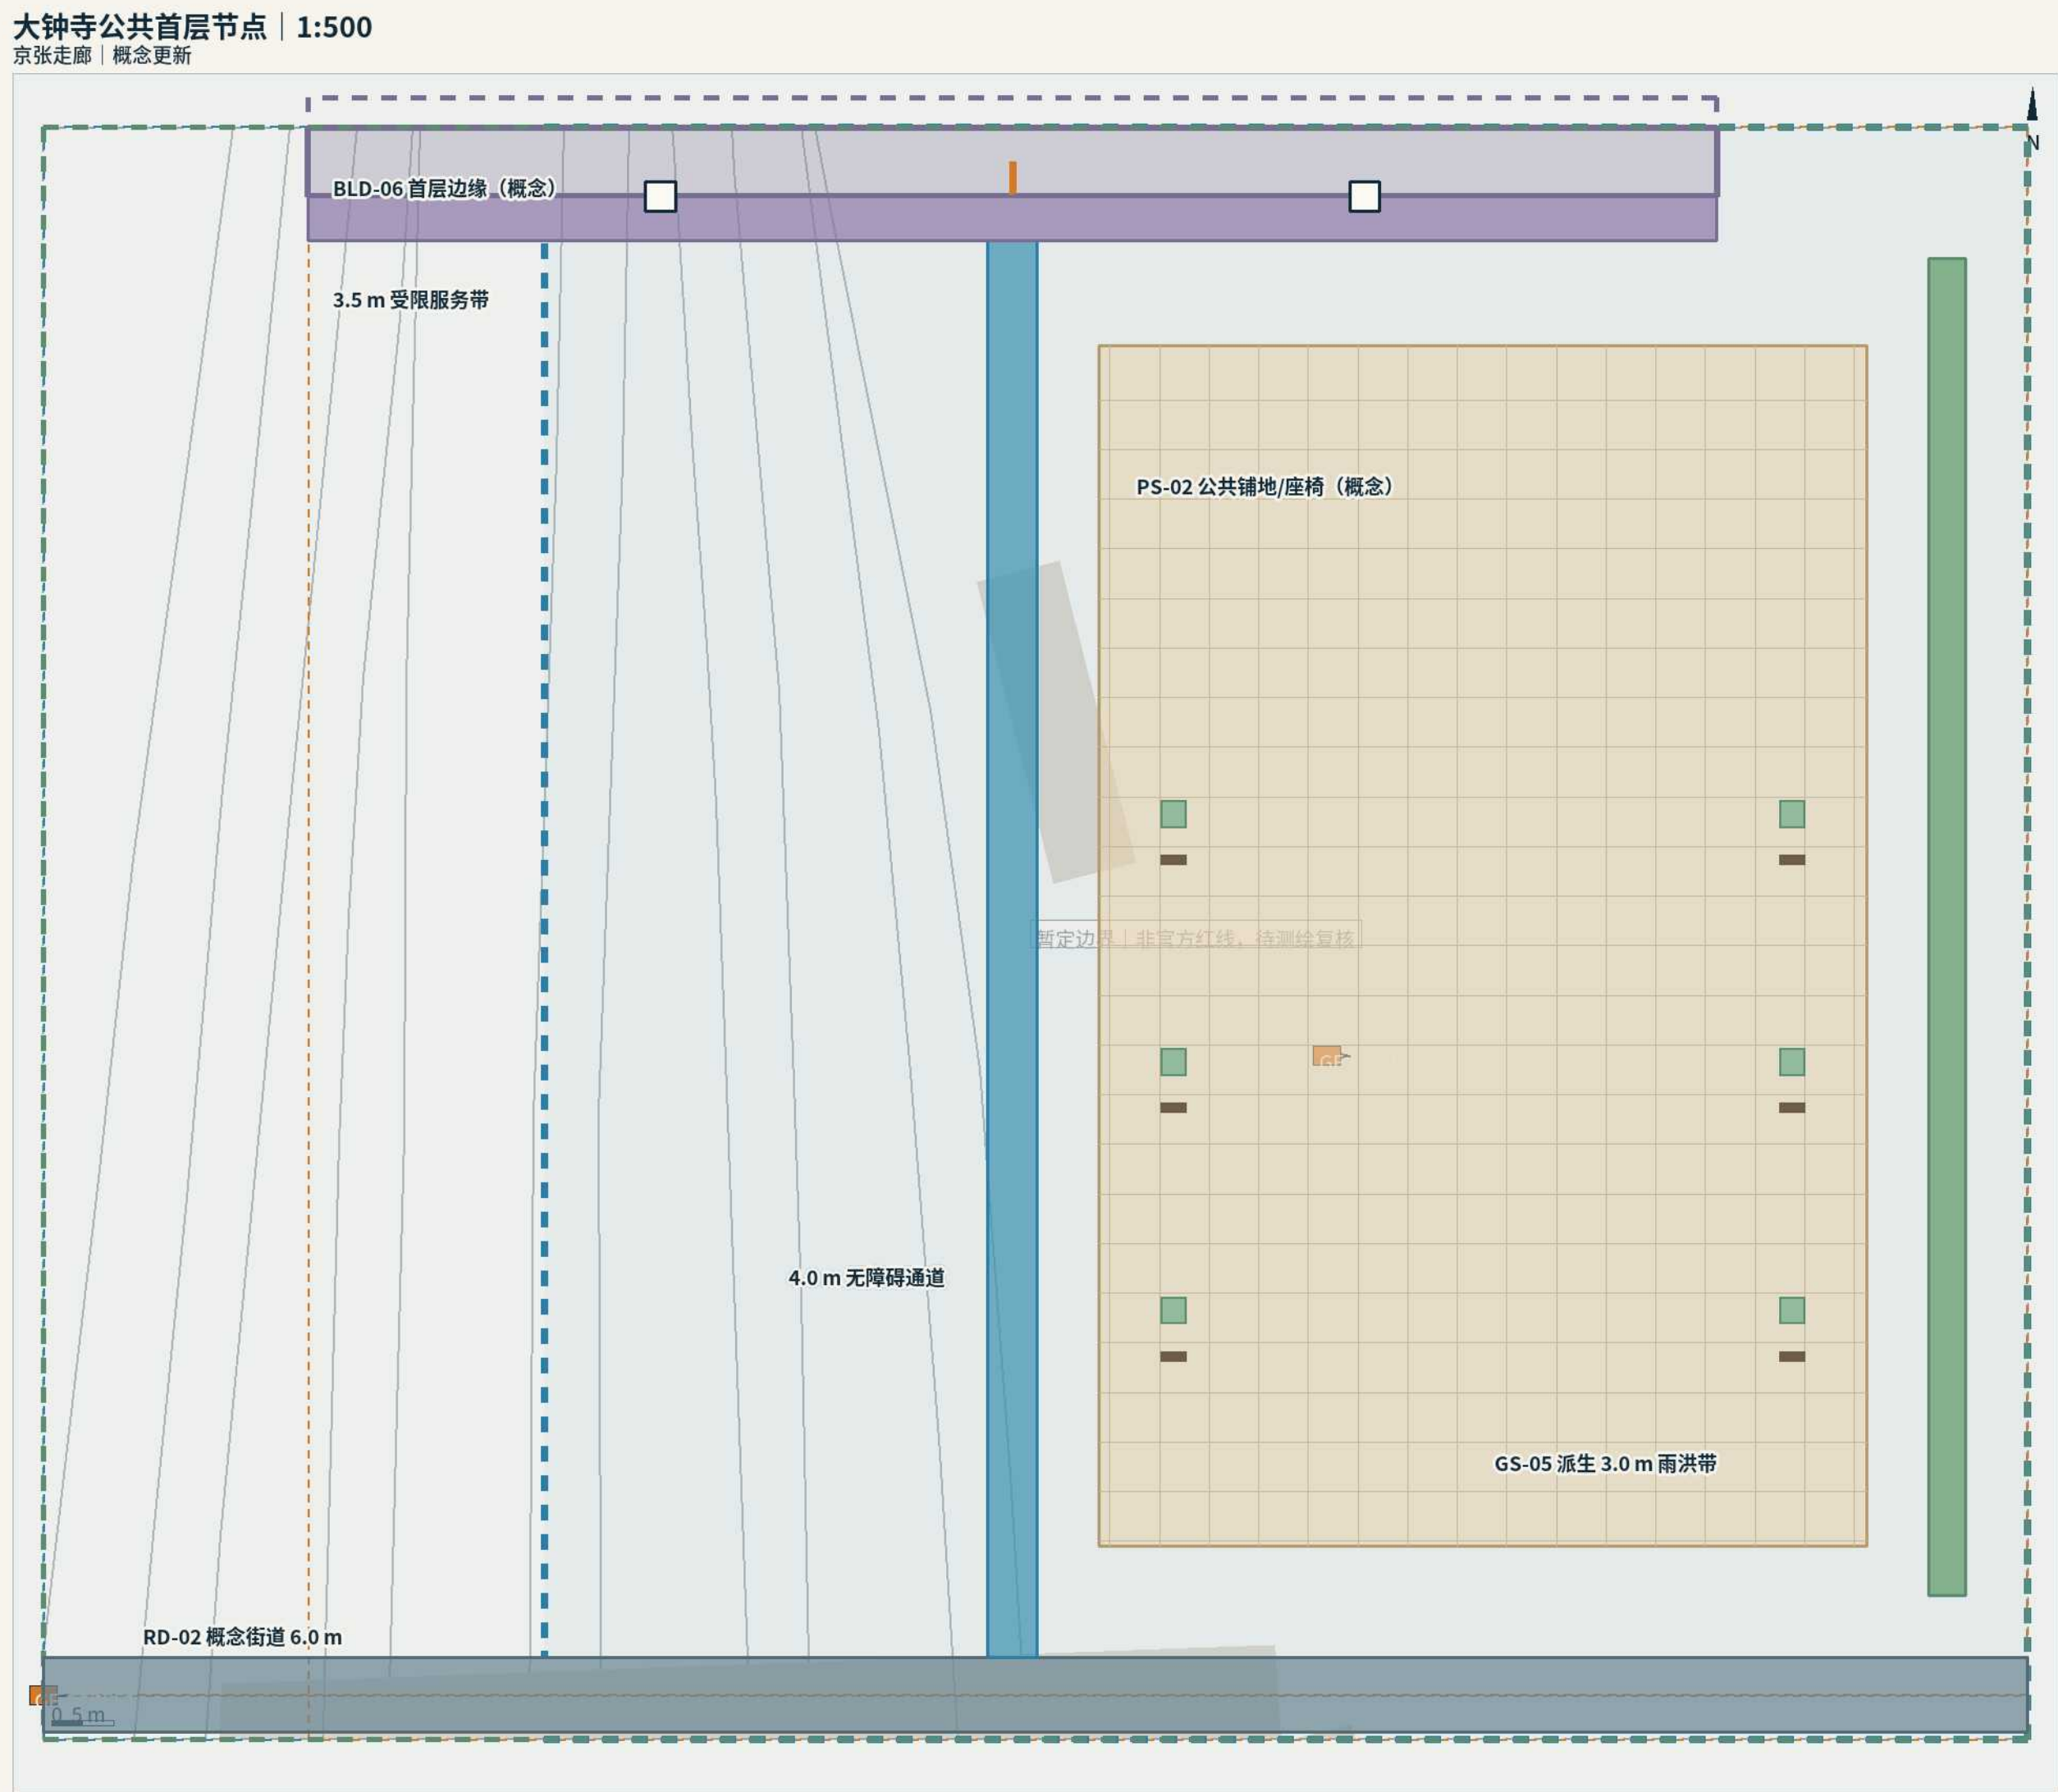

L-B02-01 | 灰色为公开方位背景；彩色为参与者概念放置；虚线边界与所有更新、业主、强度和实施关系均待测绘、法定与多专业确认。

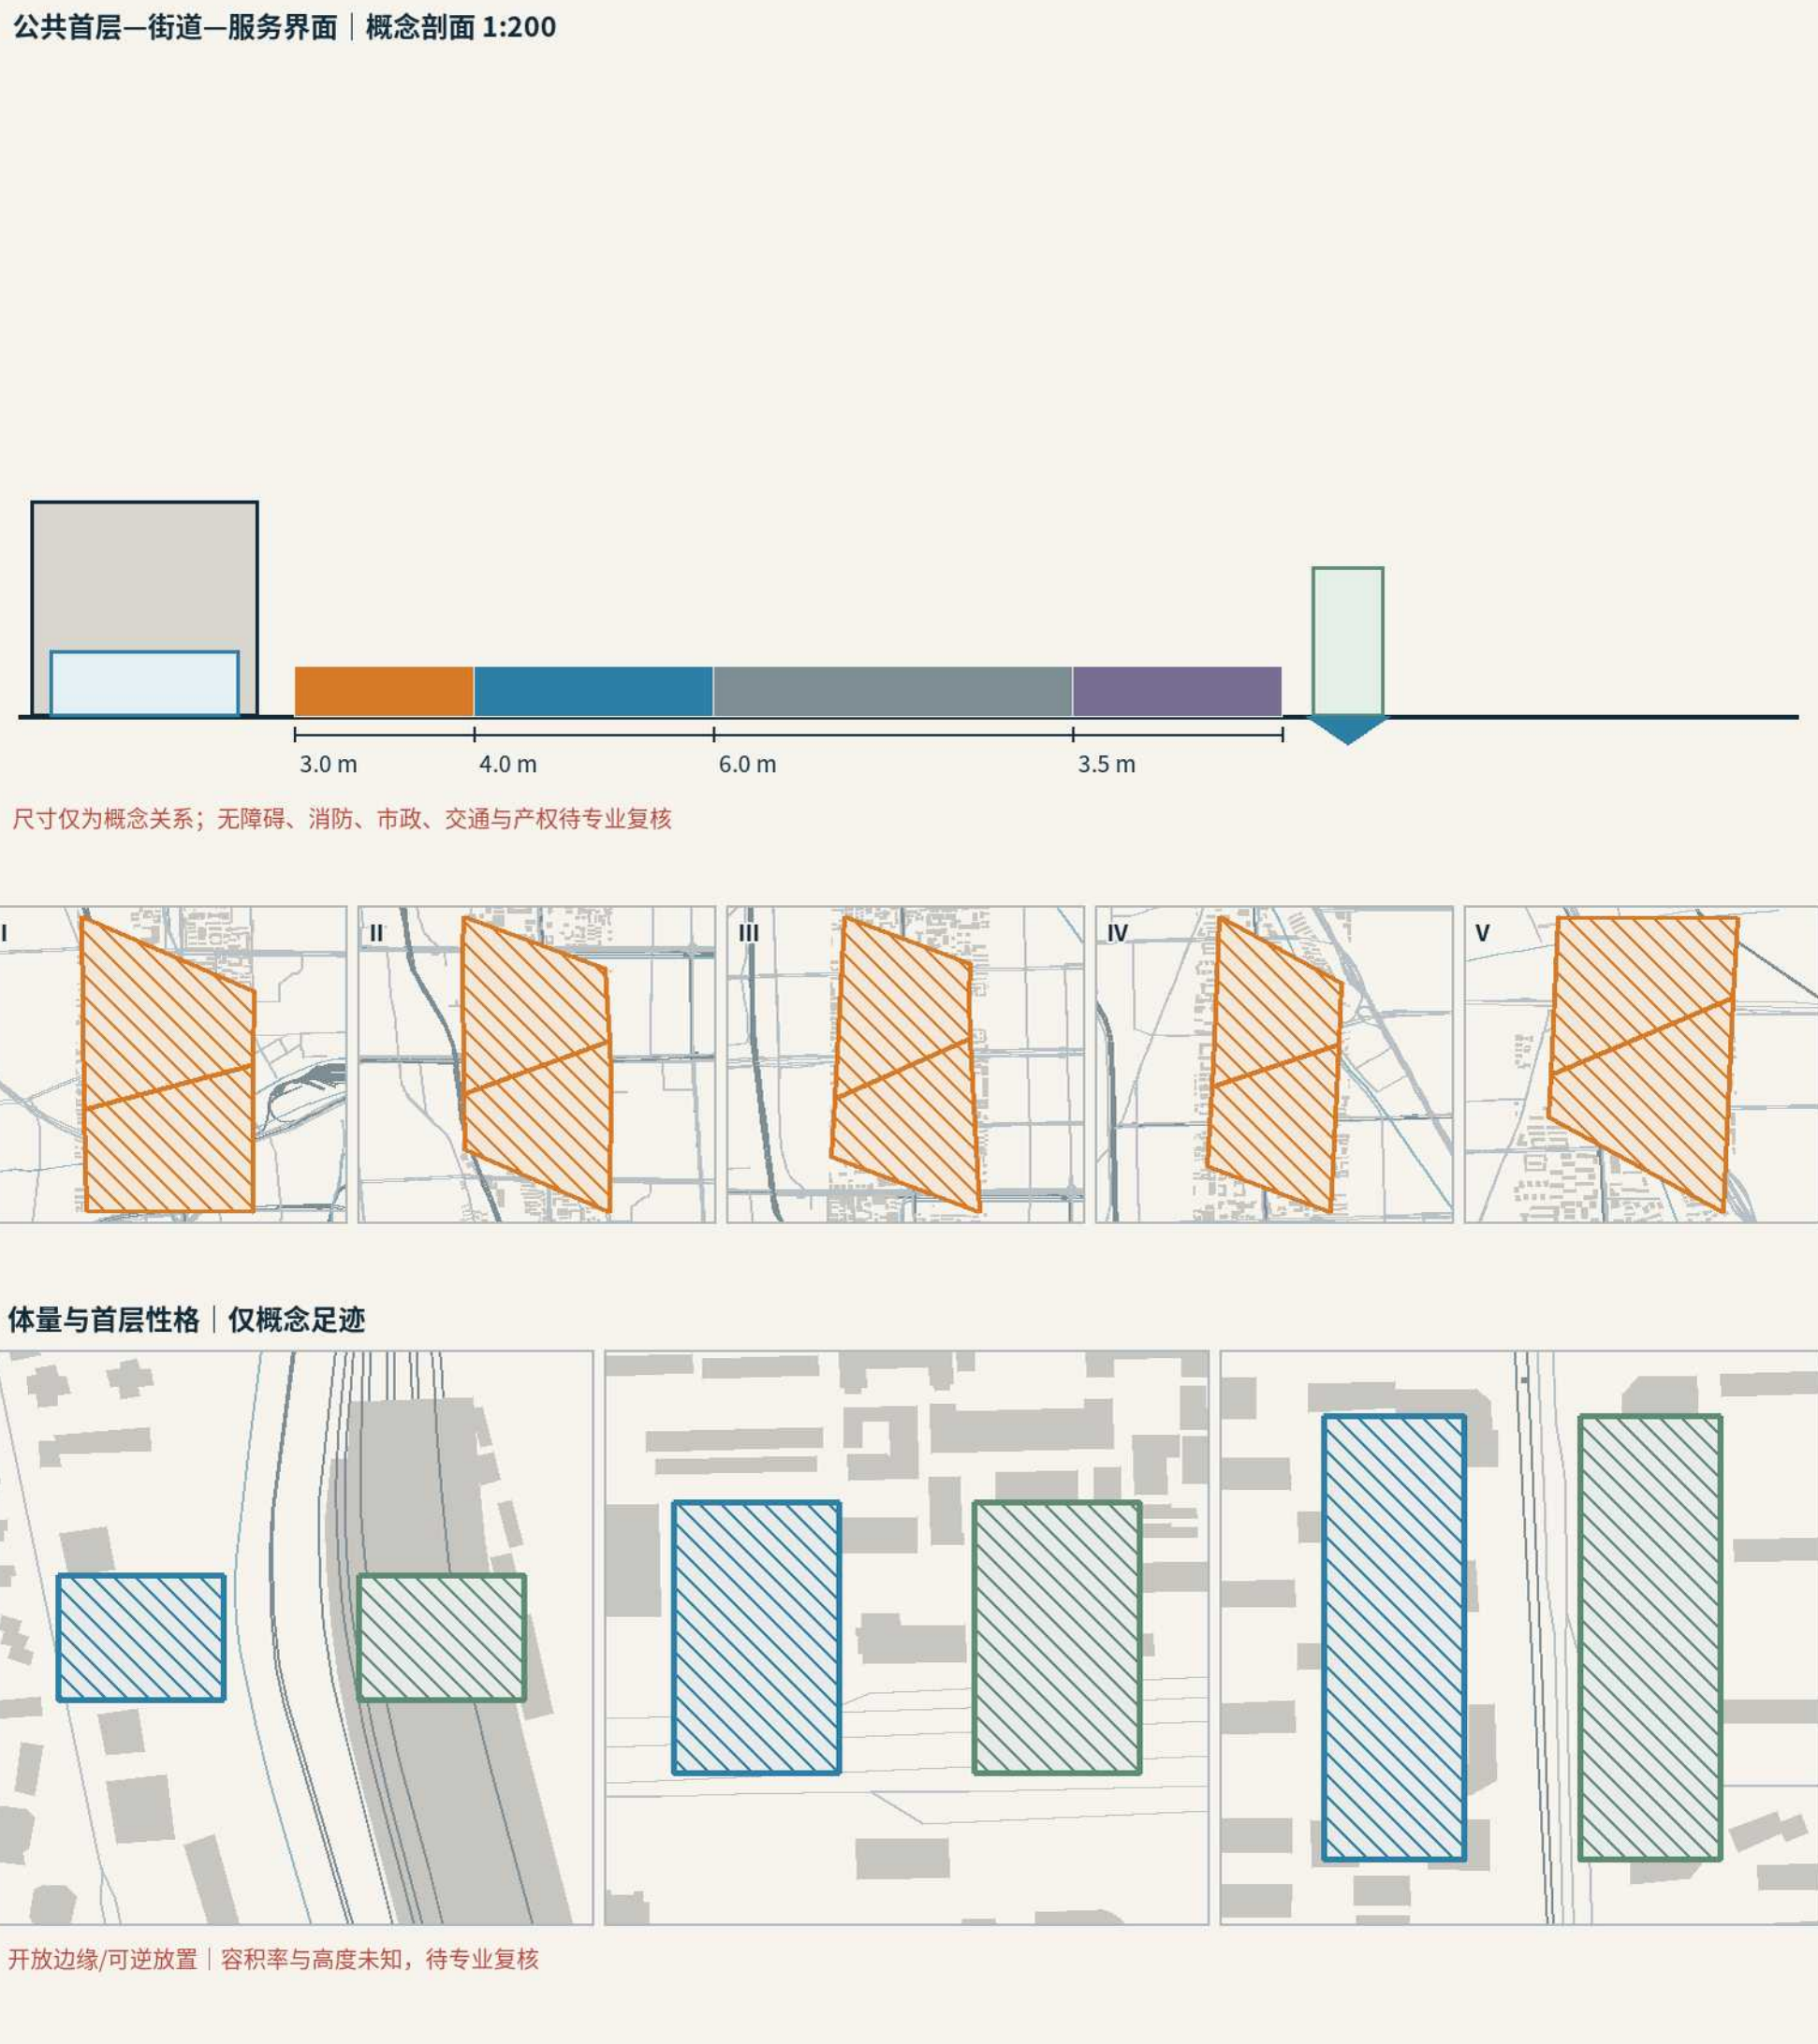


专业确认待补：现状/权属/遗产/法定控制/容量/投资/审批。所有更新类别与项目均为概念定位，可调整、可退出。

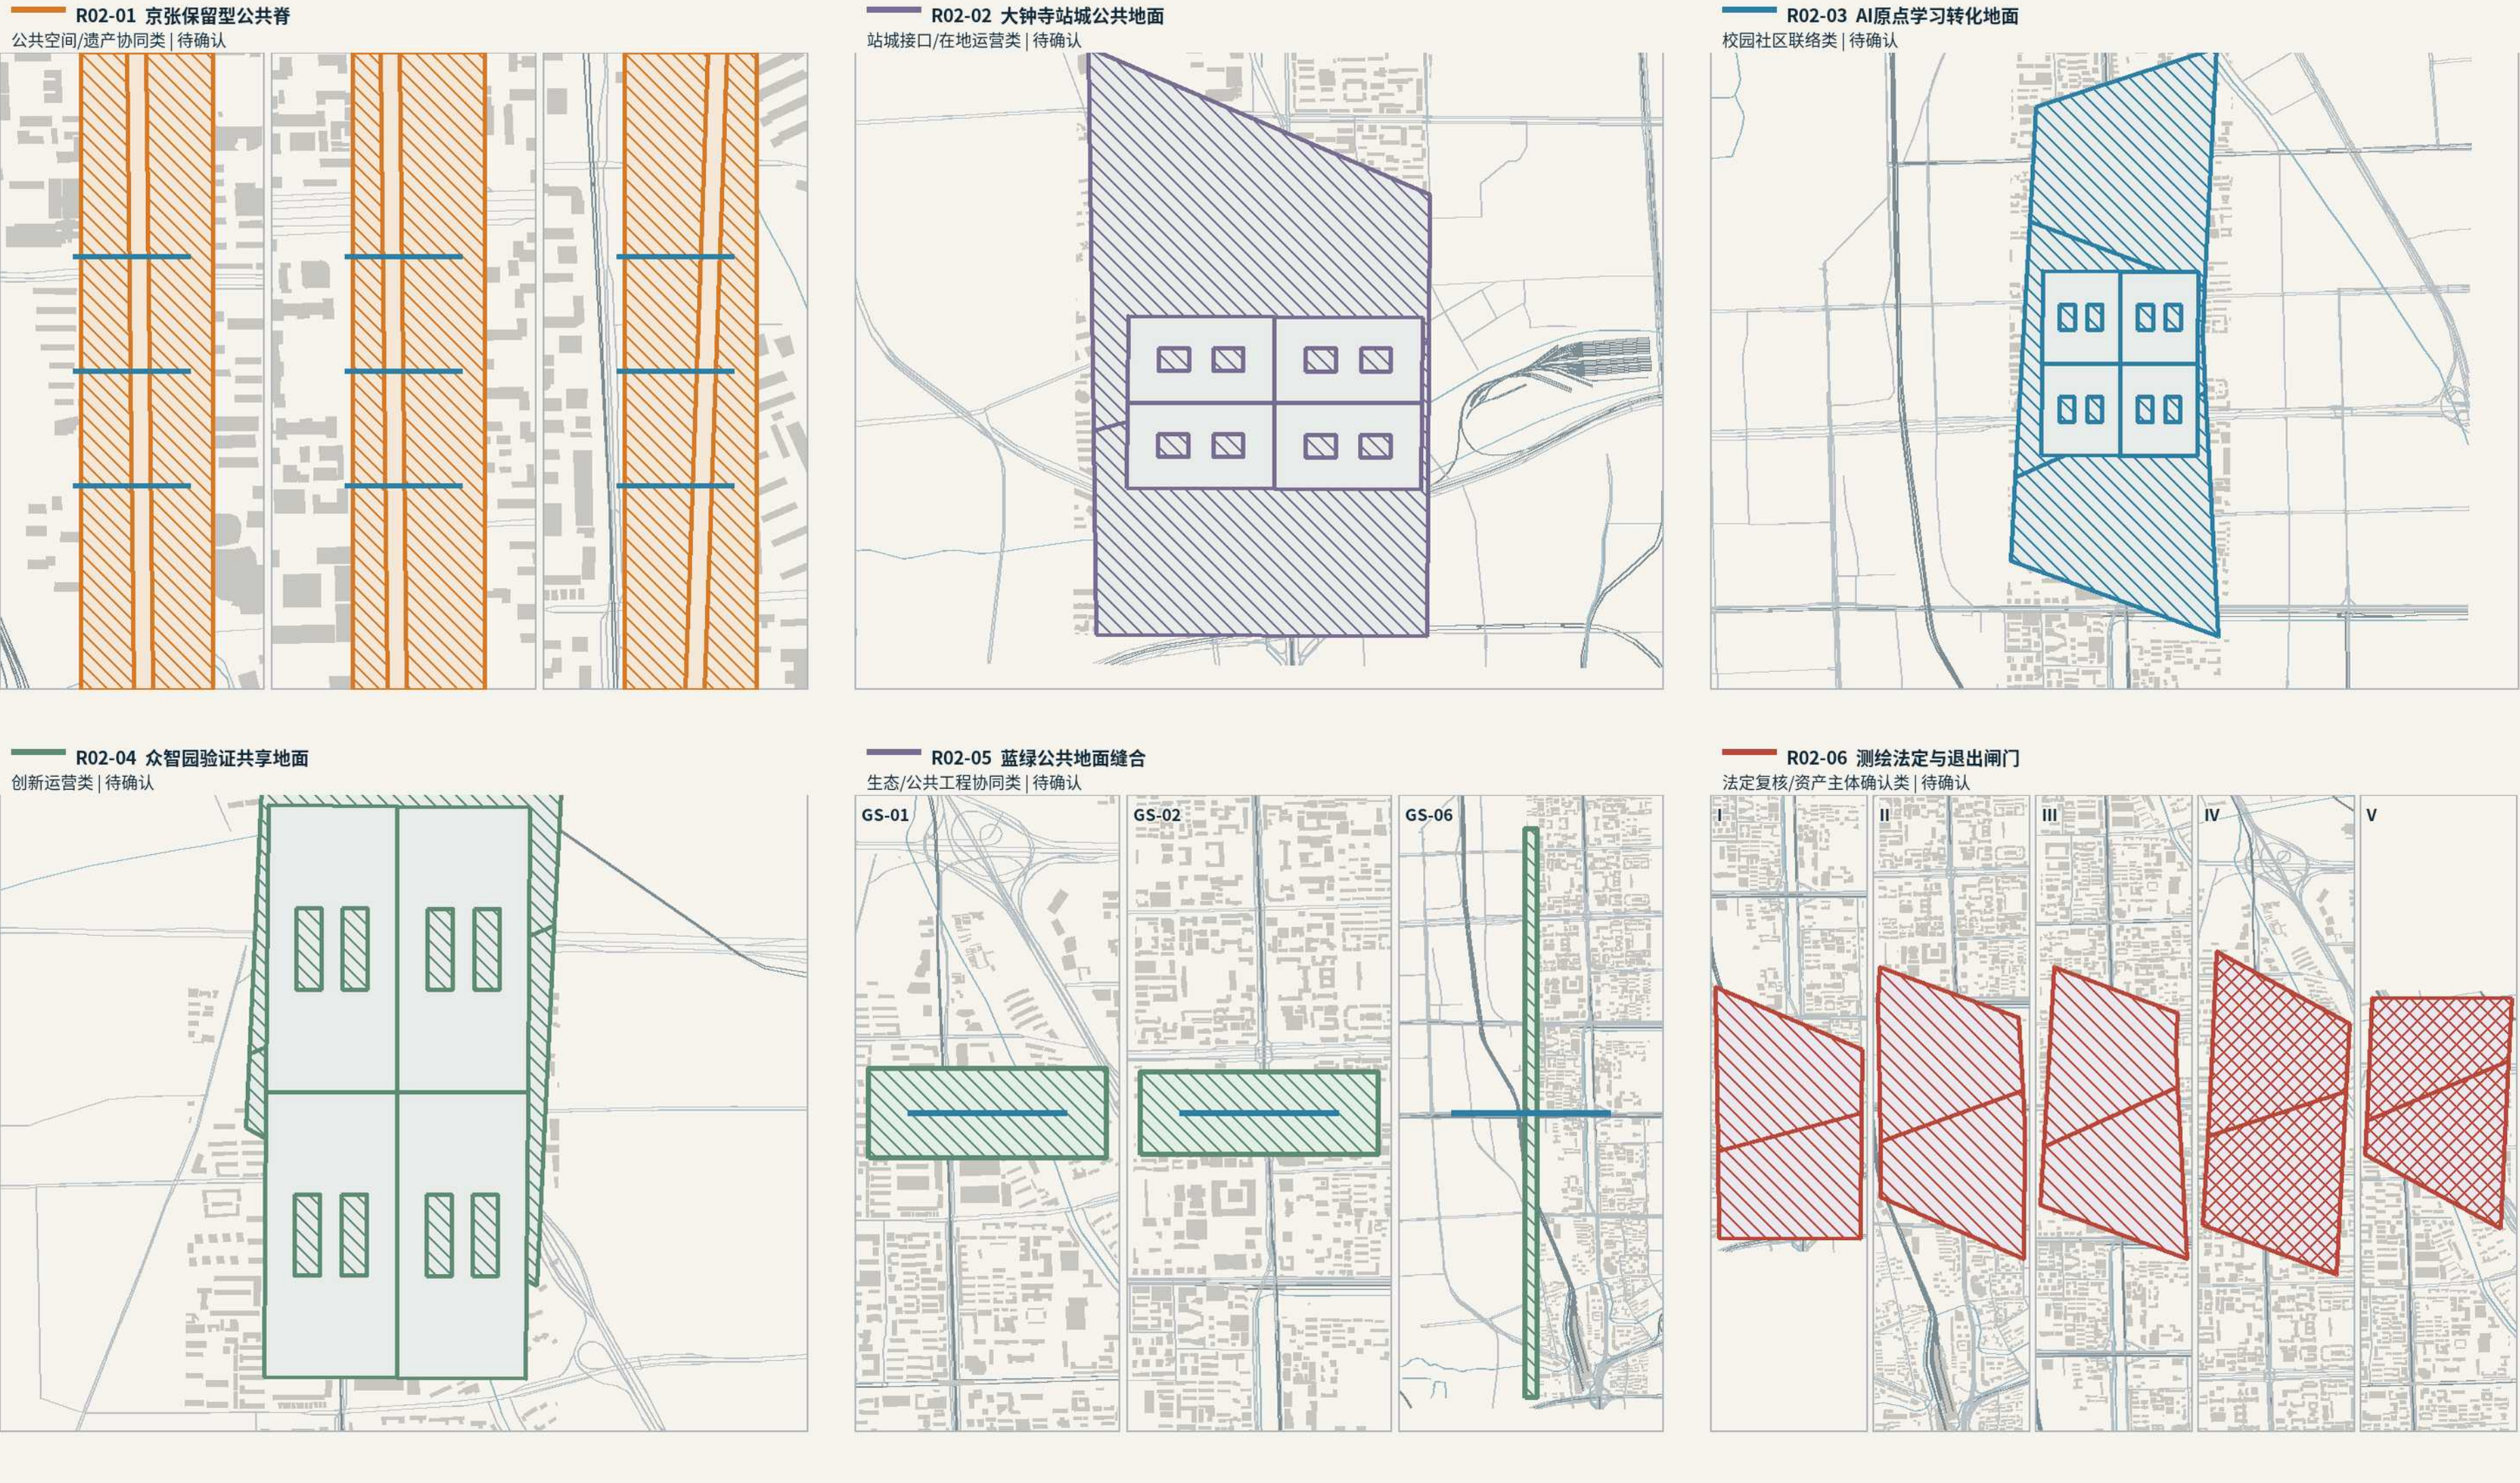

遗产公园、慢行与蓝绿生命线

六处接口修补，把铁路记忆、无障碍出行与水绿停留连接成连续公共地面

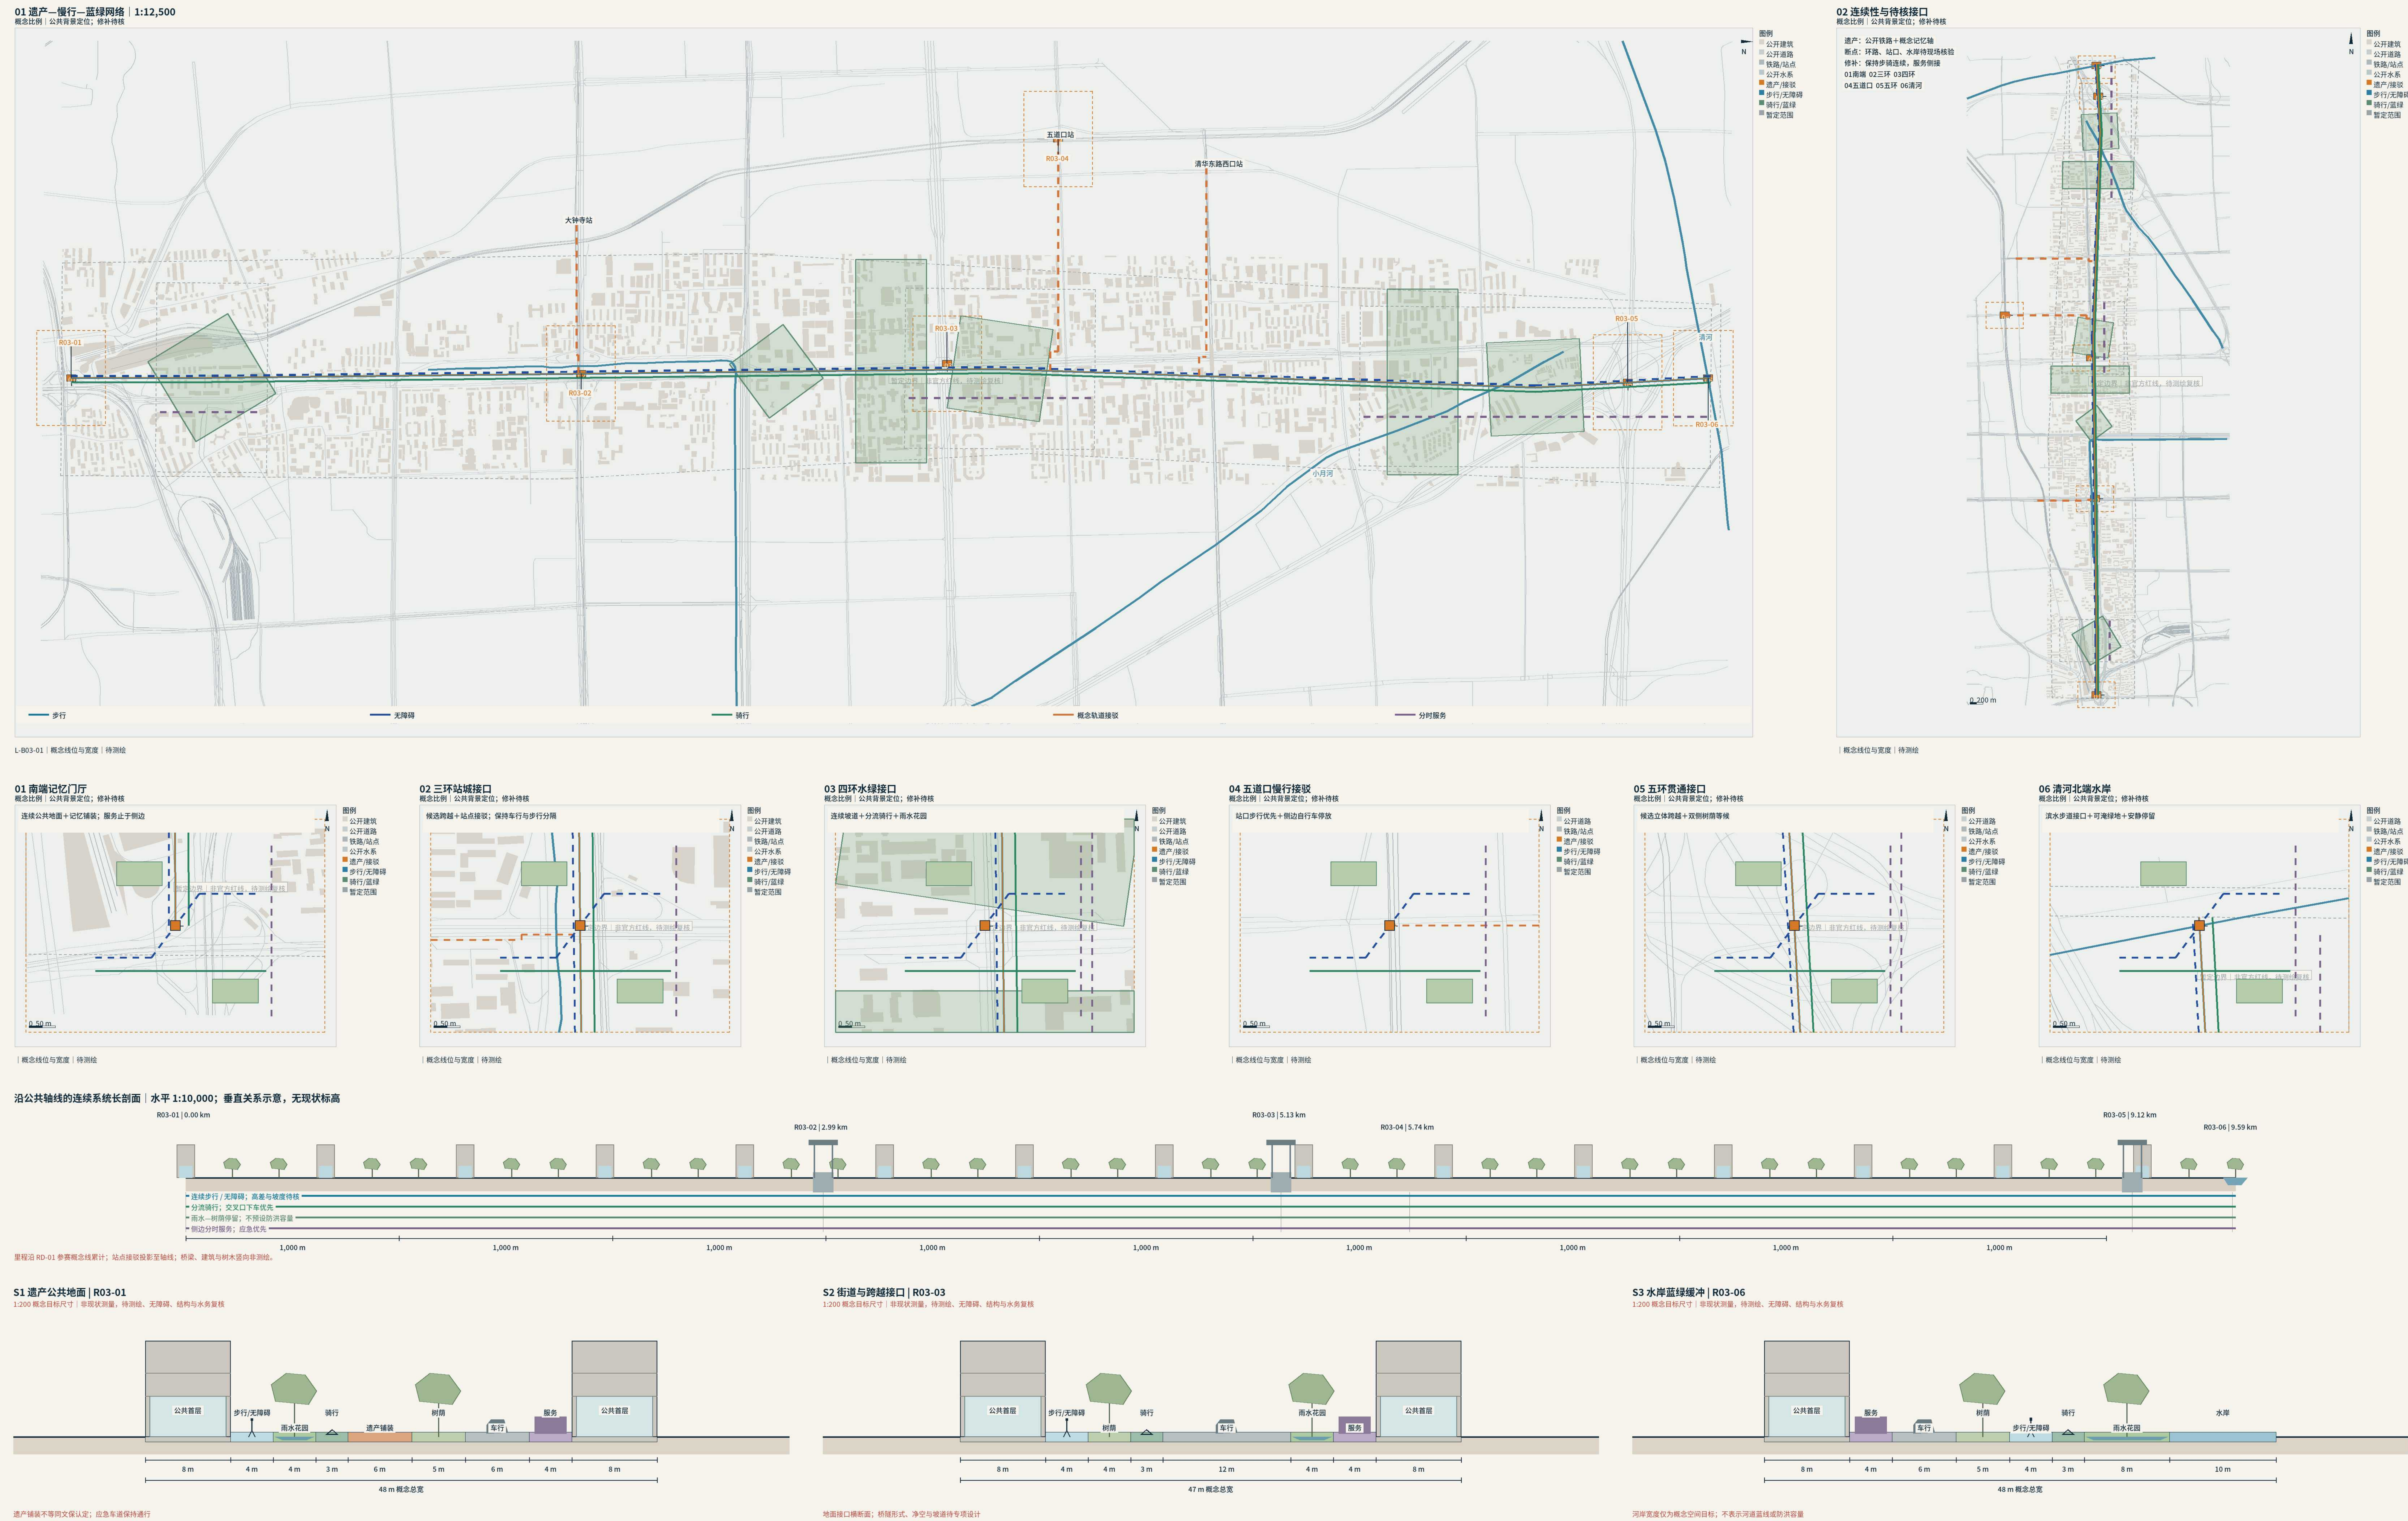


B04 众智园 | 花园型自主创新城区

192.1 ha：清河与公共展廊连续开放，研发、测试、后勤分界运行。

01 全区结构与更新 | 1:5000


EP5G-4548 | 概念比例 / 待测绘复核

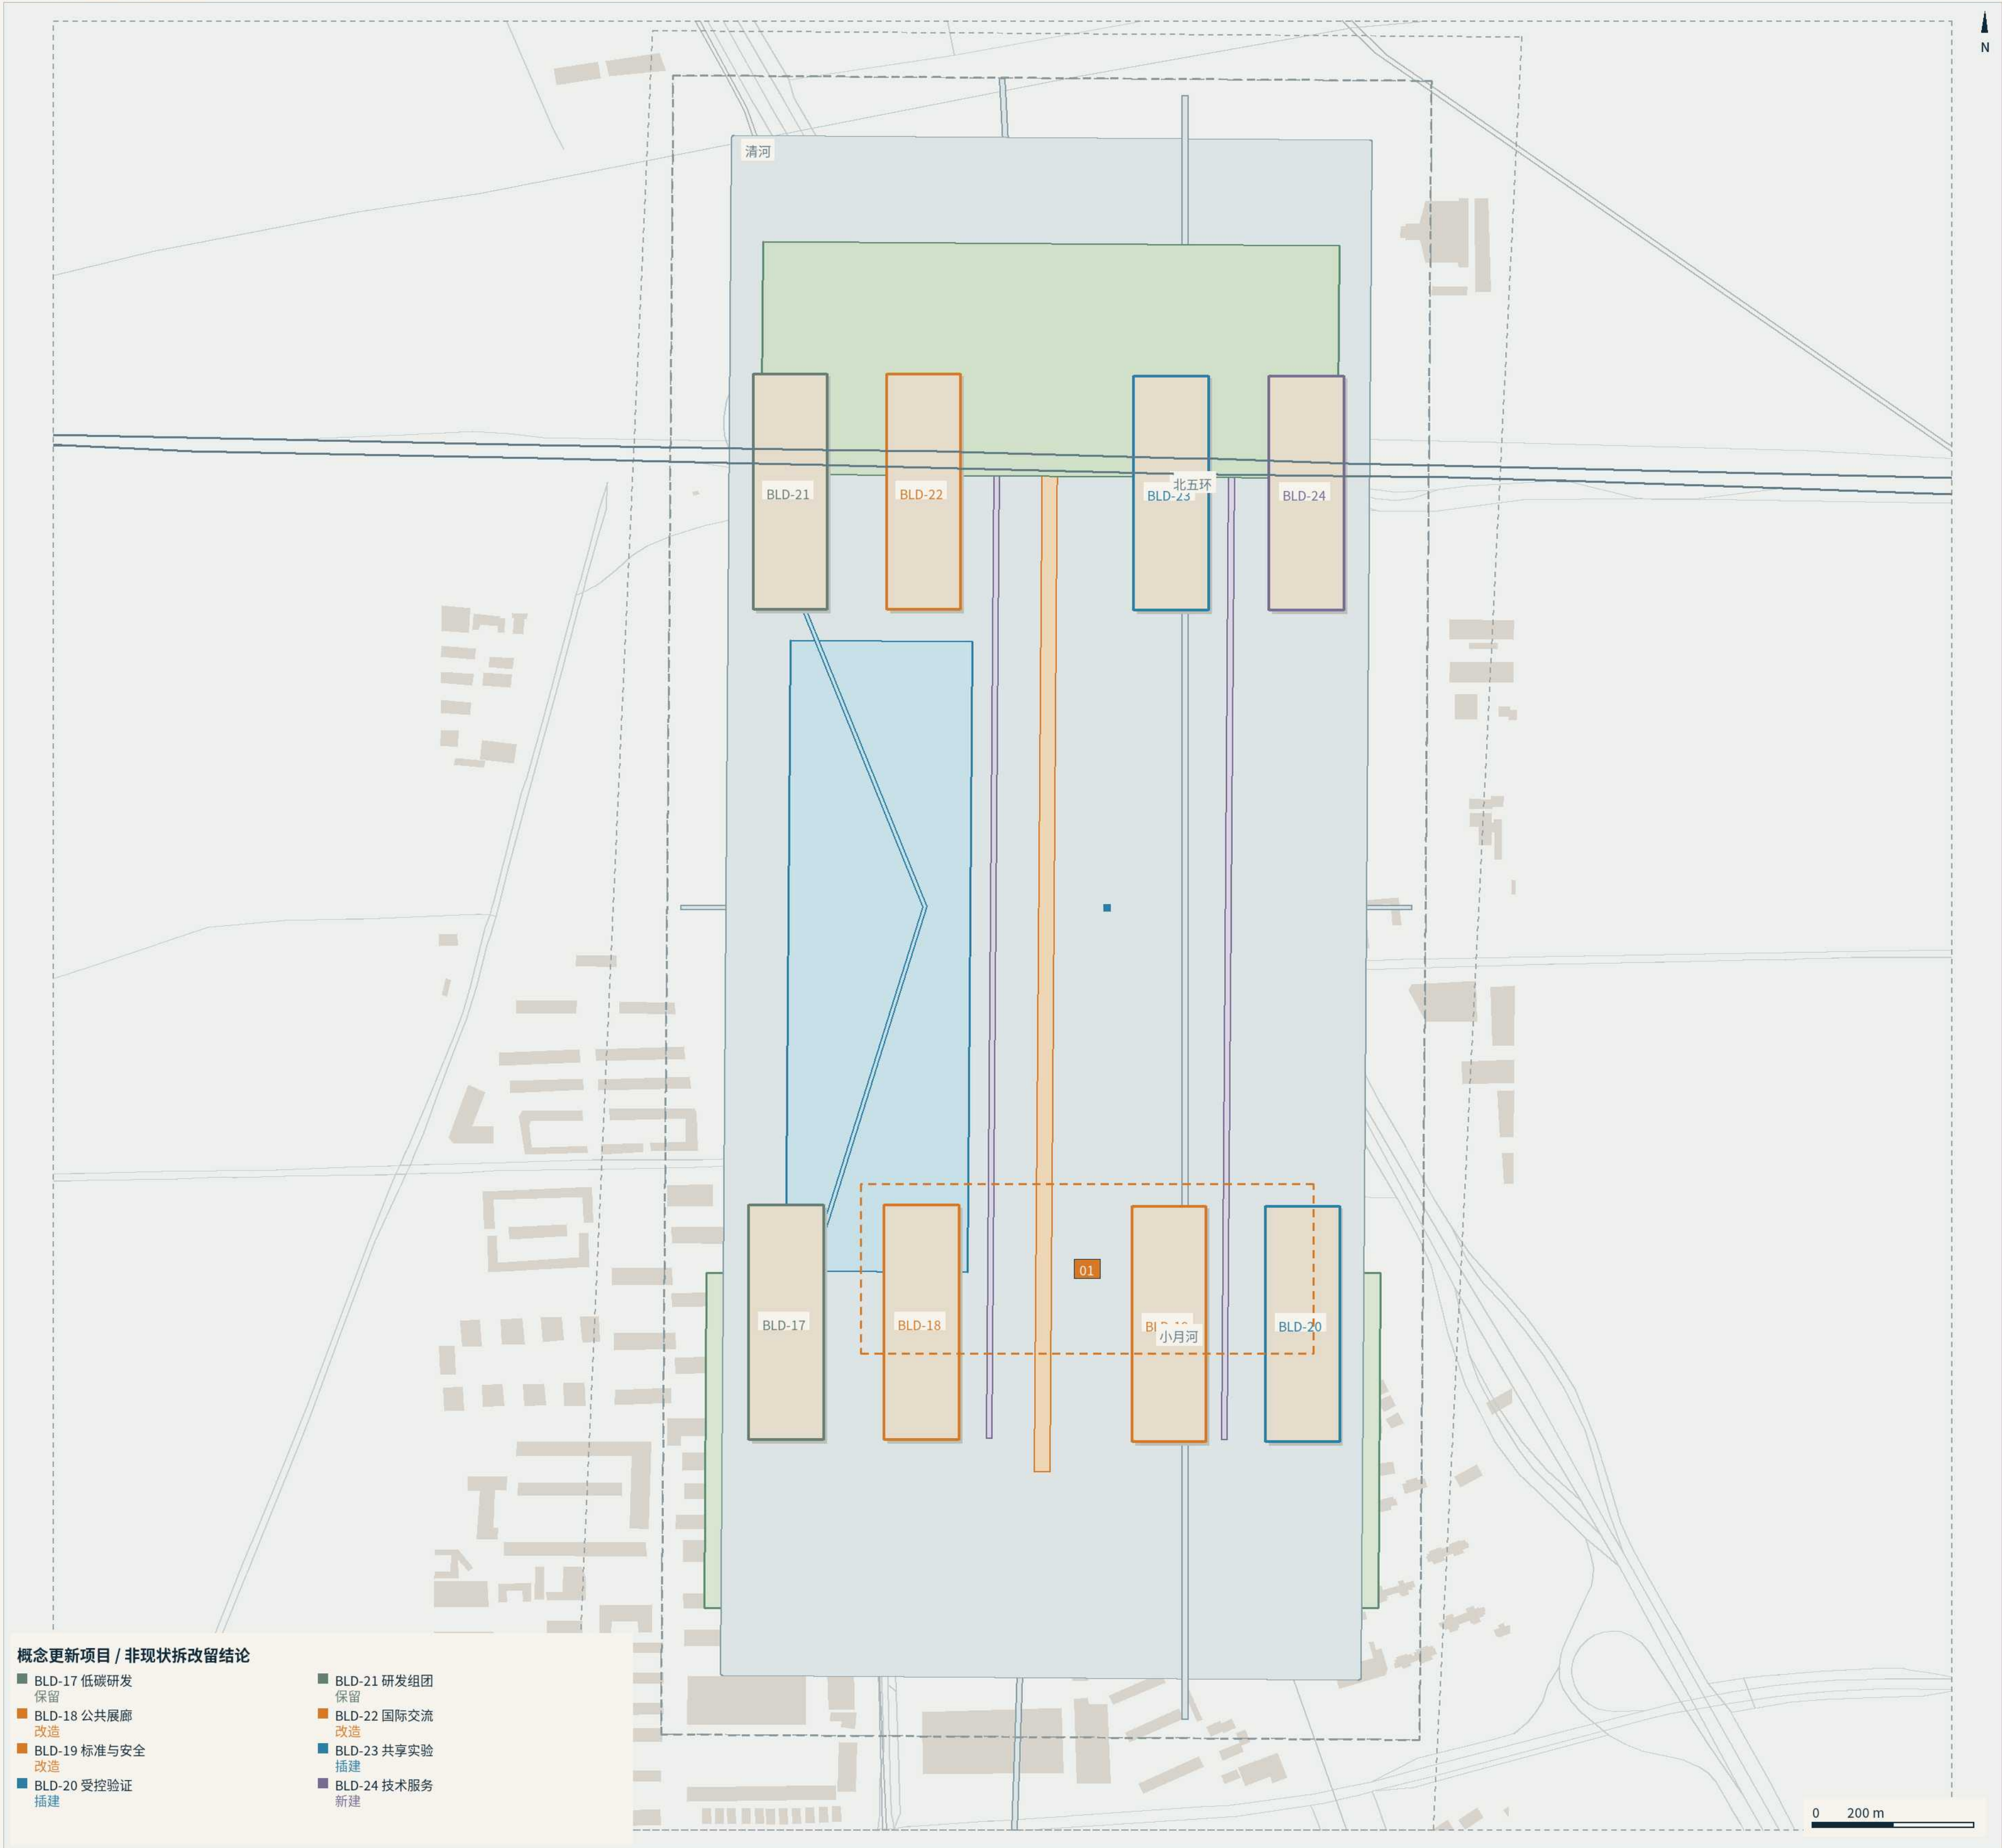

暂定边界 | 非官方红线，待测绘复核

04 A-A 水绿低碳研发组团 | 1:200


典型模块尺寸；首层净高为概念目标，非实测工程剖面。与节点 A-A 对应。

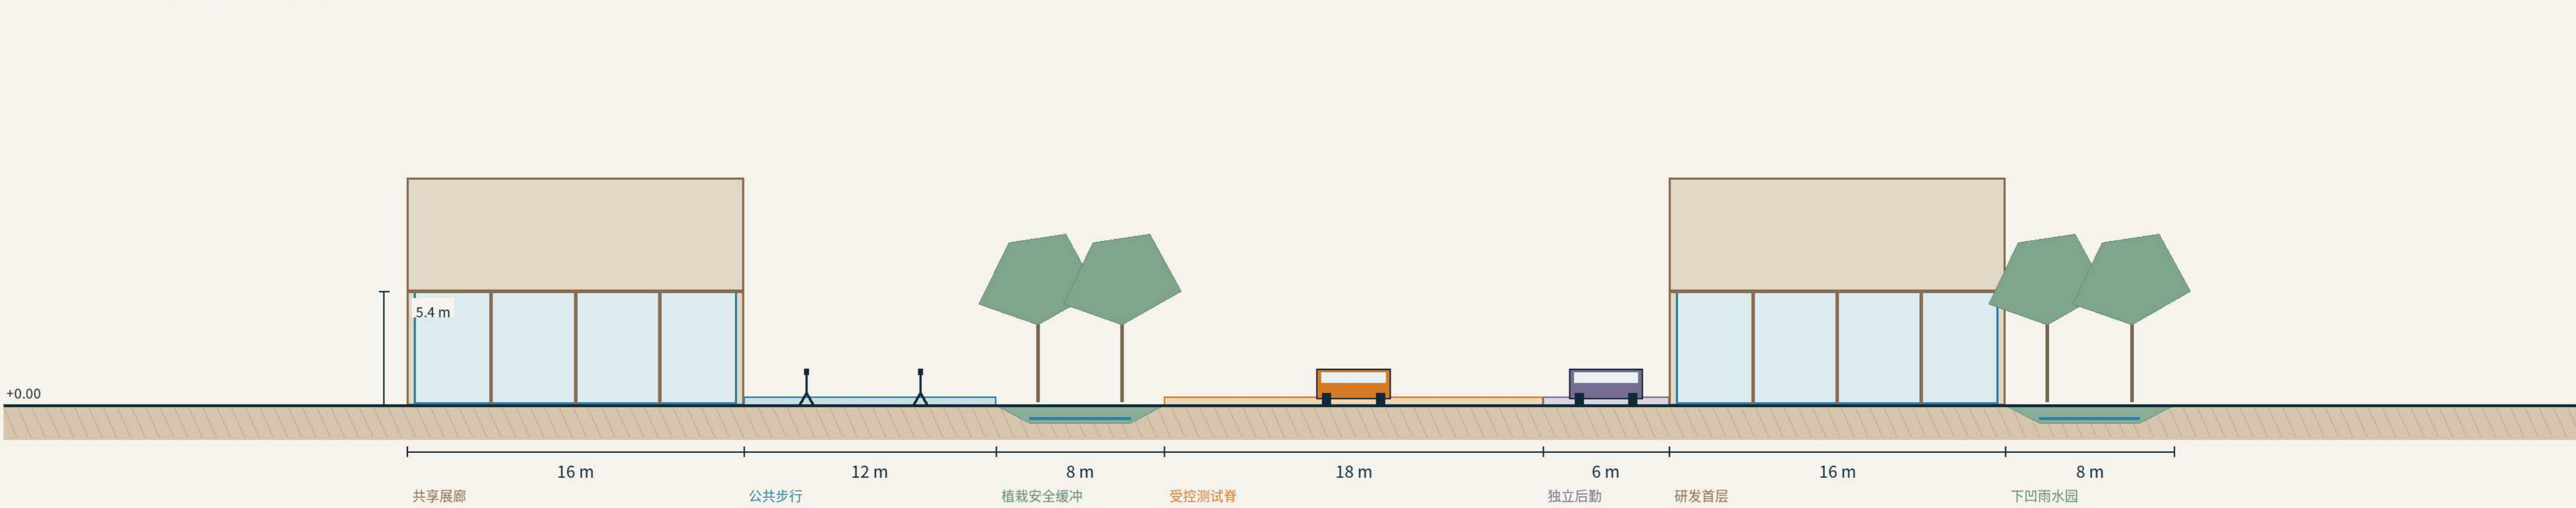

1:200 / 所有宽度、高度、排水及安全要求待测绘、规范与专业复核。

02 展示—安全—测试核心节点 | 1:1000


EP5G-4548 | 概念比例 / 待测绘复核

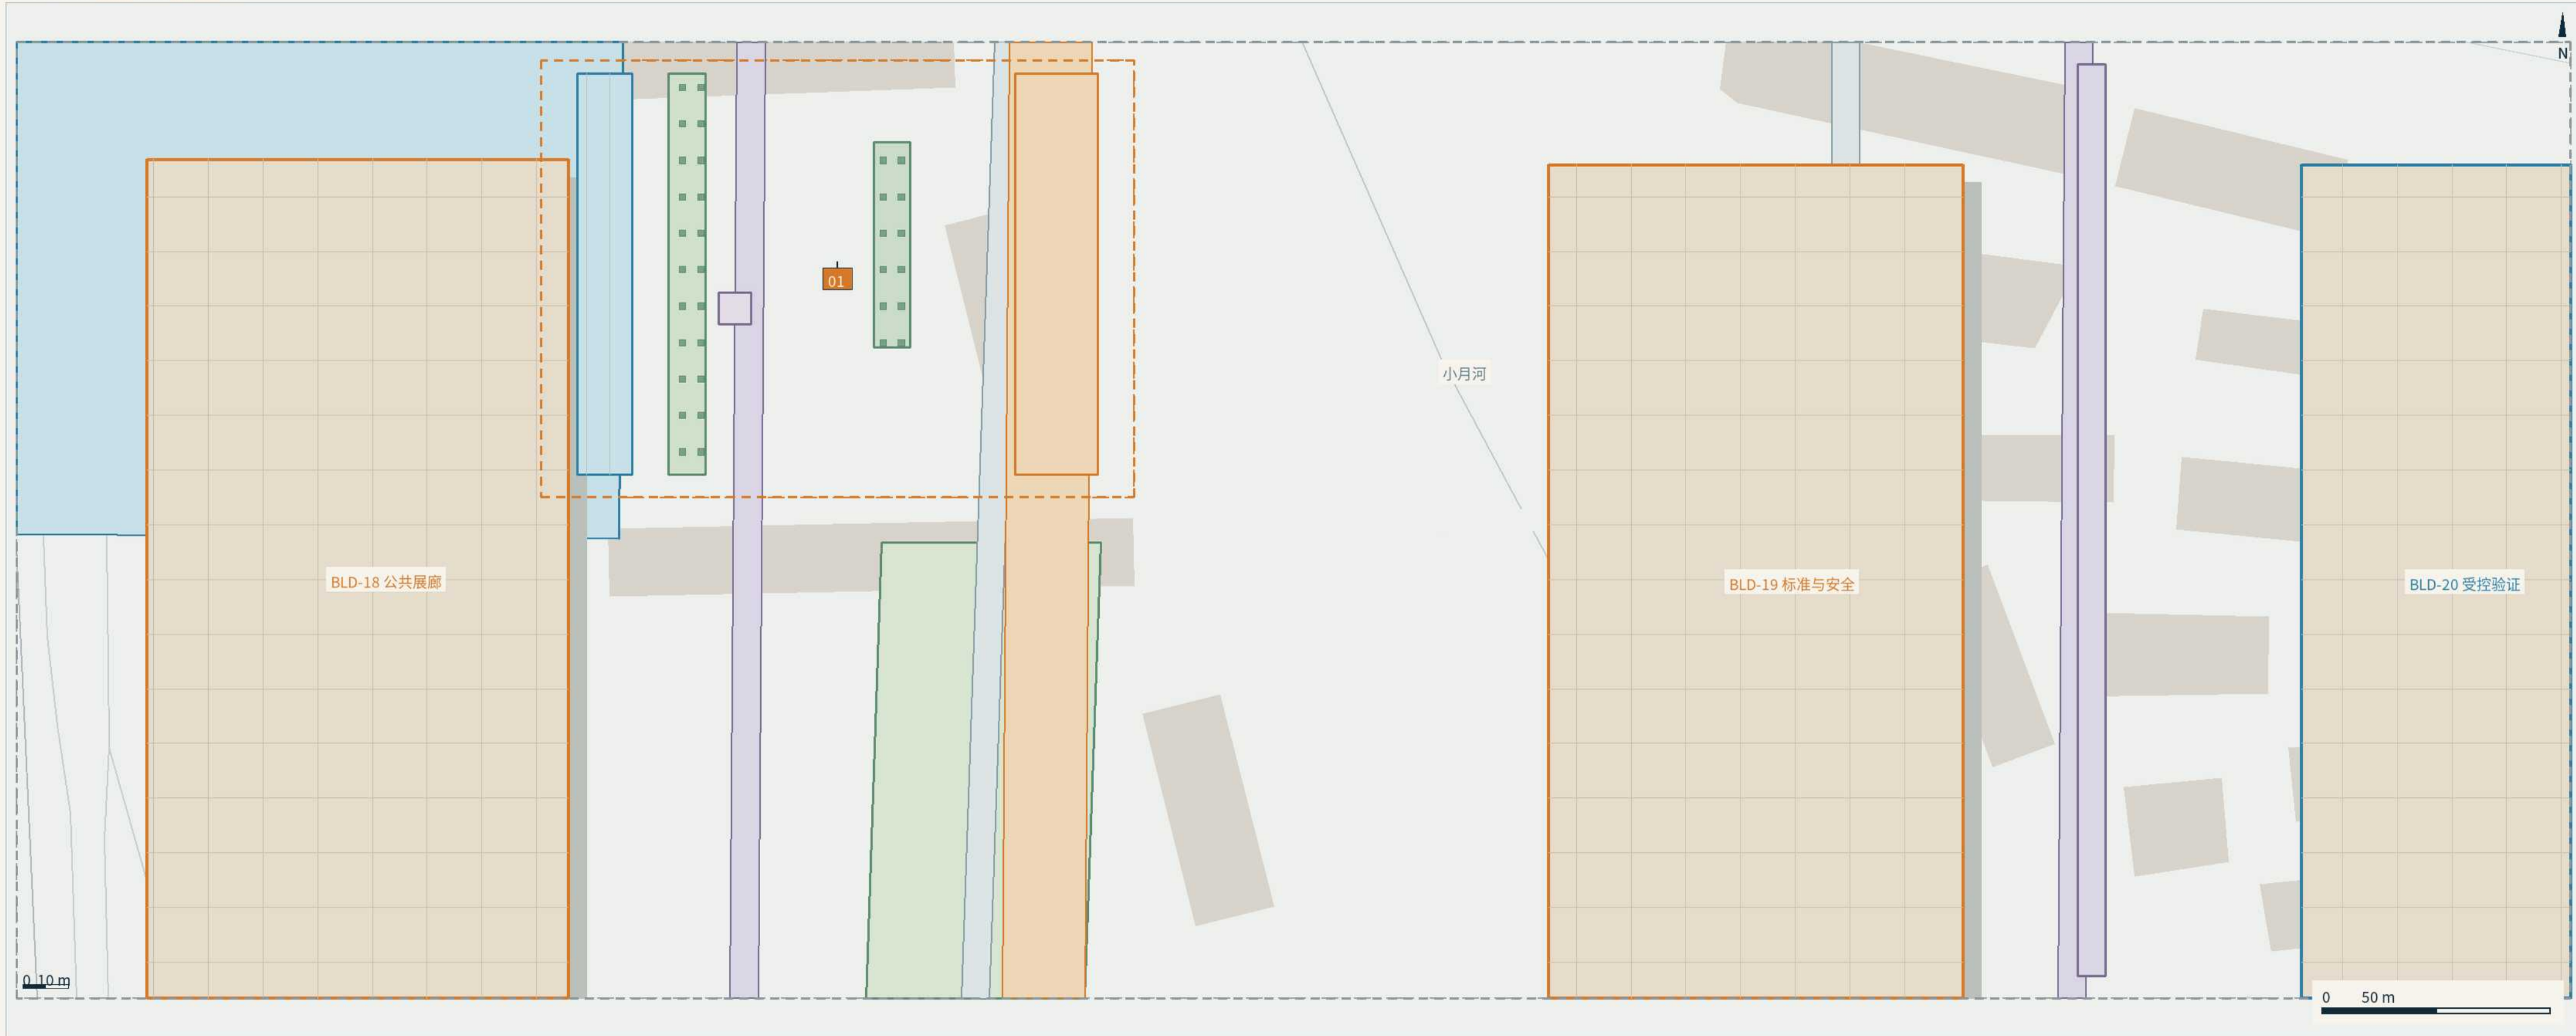

暂定边界 | 非官方红线，待测绘复核

03 公共与受控阈值 | 1:500

EP5G-4548 | 概念比例 / 待测绘复核

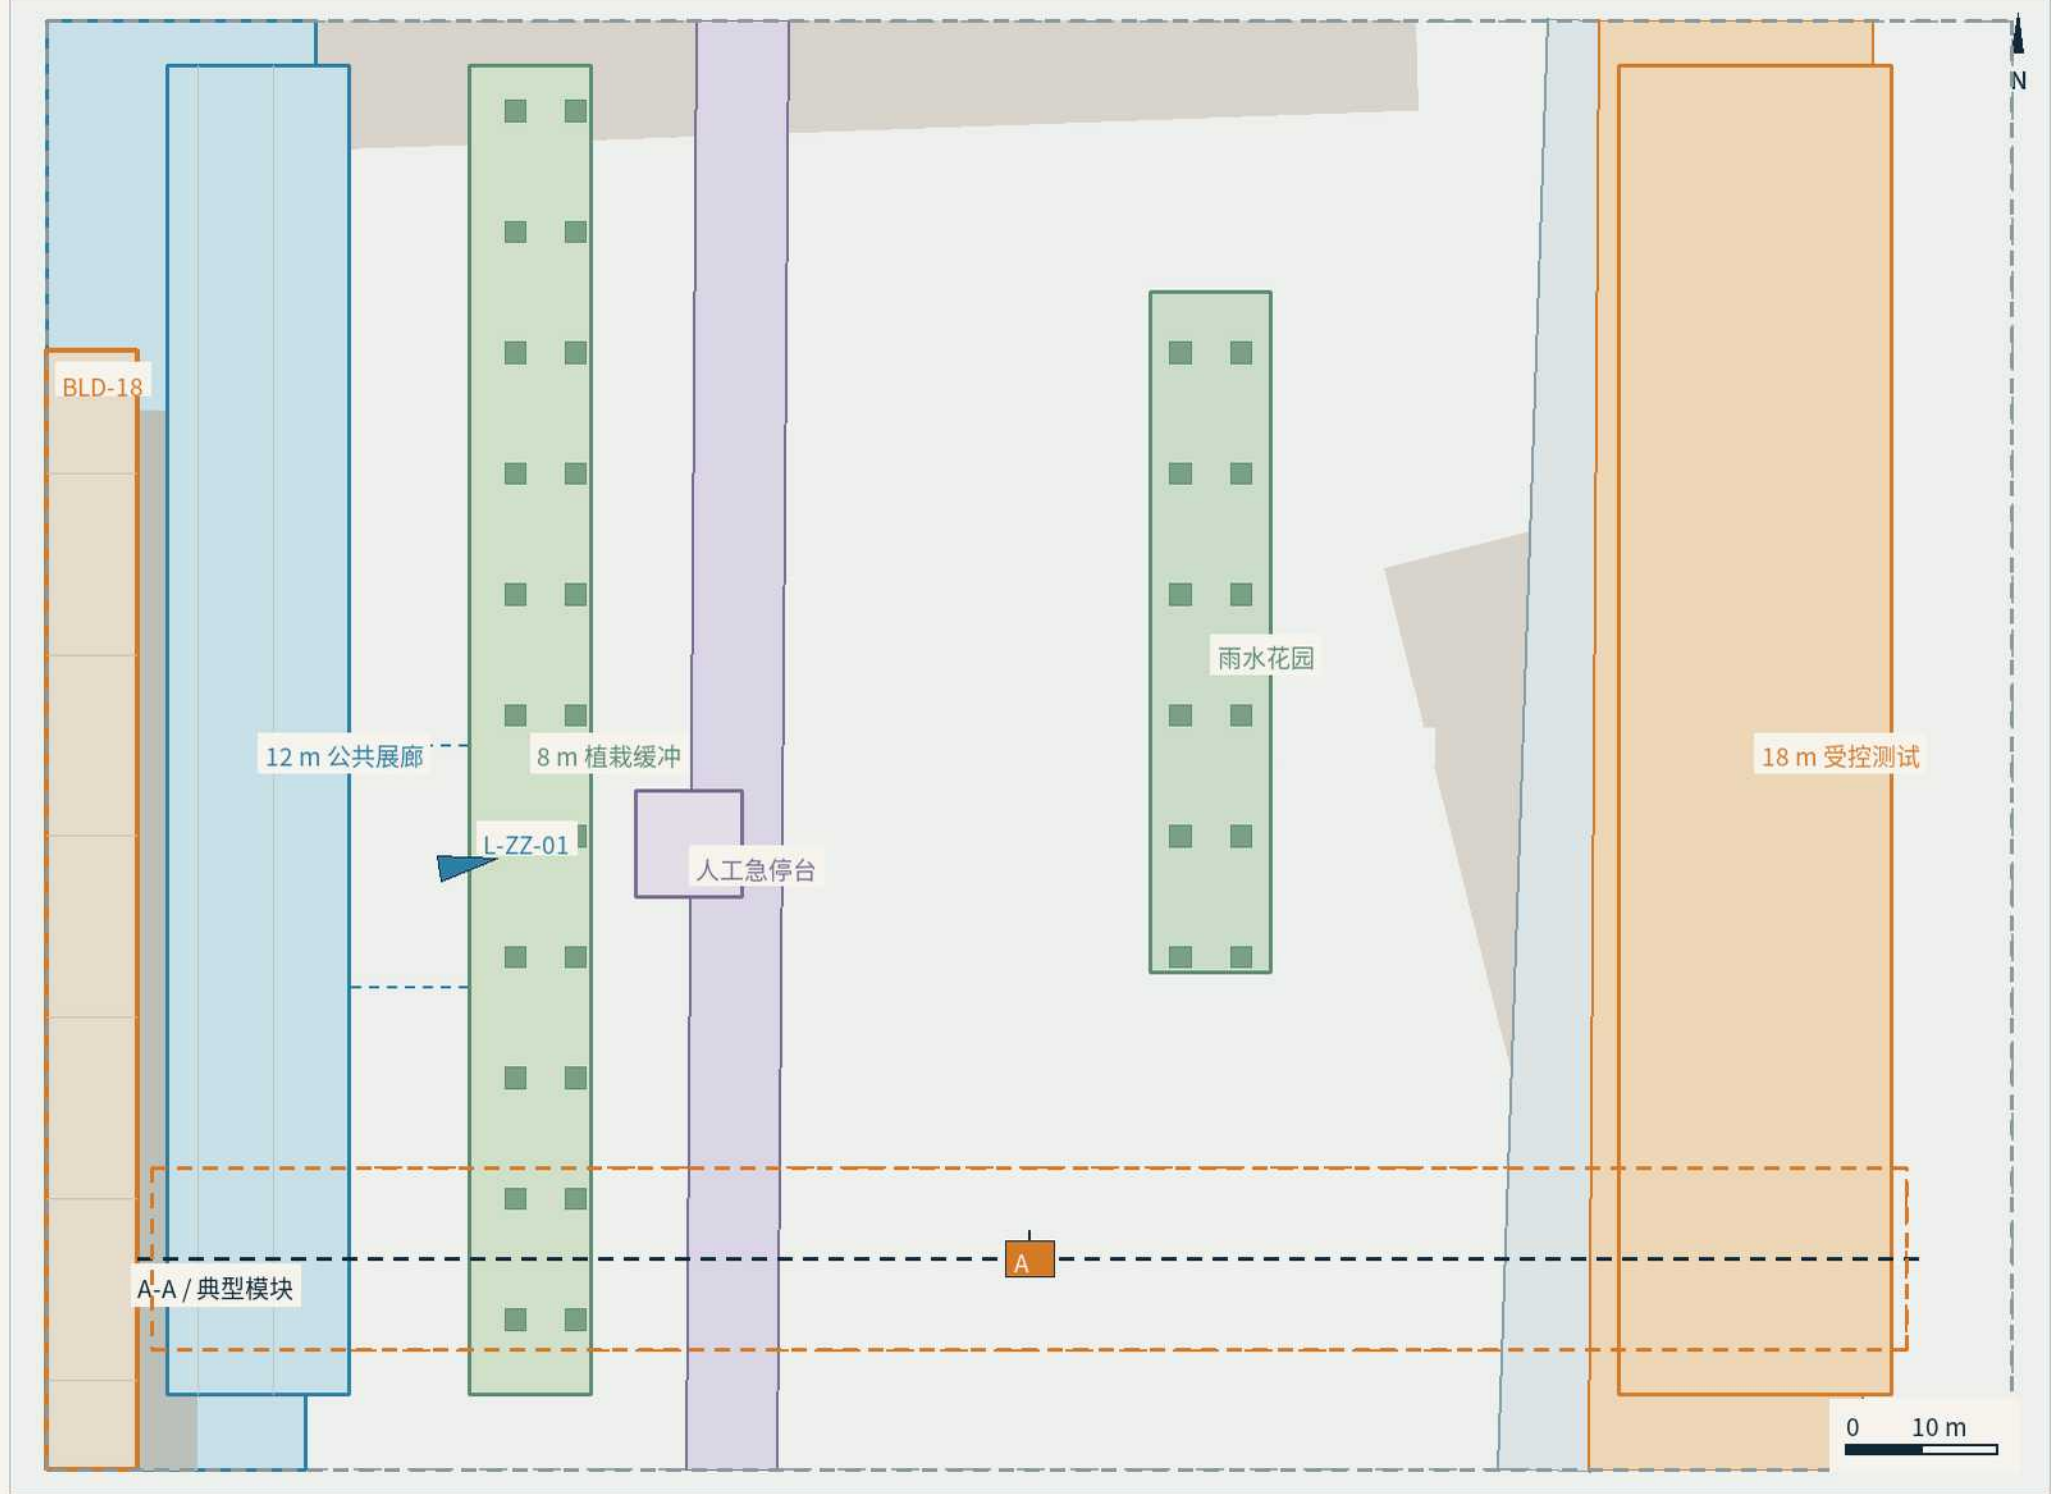

暂定边界 | 非官方红线，待测绘复核




L-ZZ-01 | 已登记概念氛围图；镜头落在公共阈值，非现场照片或工程定案。

PUBLIC / PROVISIONAL / CONCEPT
公开背景 / 暂定边界 / 参与者概念

05 清河生态与外部慢行接口 | 1:5000

EP5G-4548 | 概念比例 / 待测绘复核

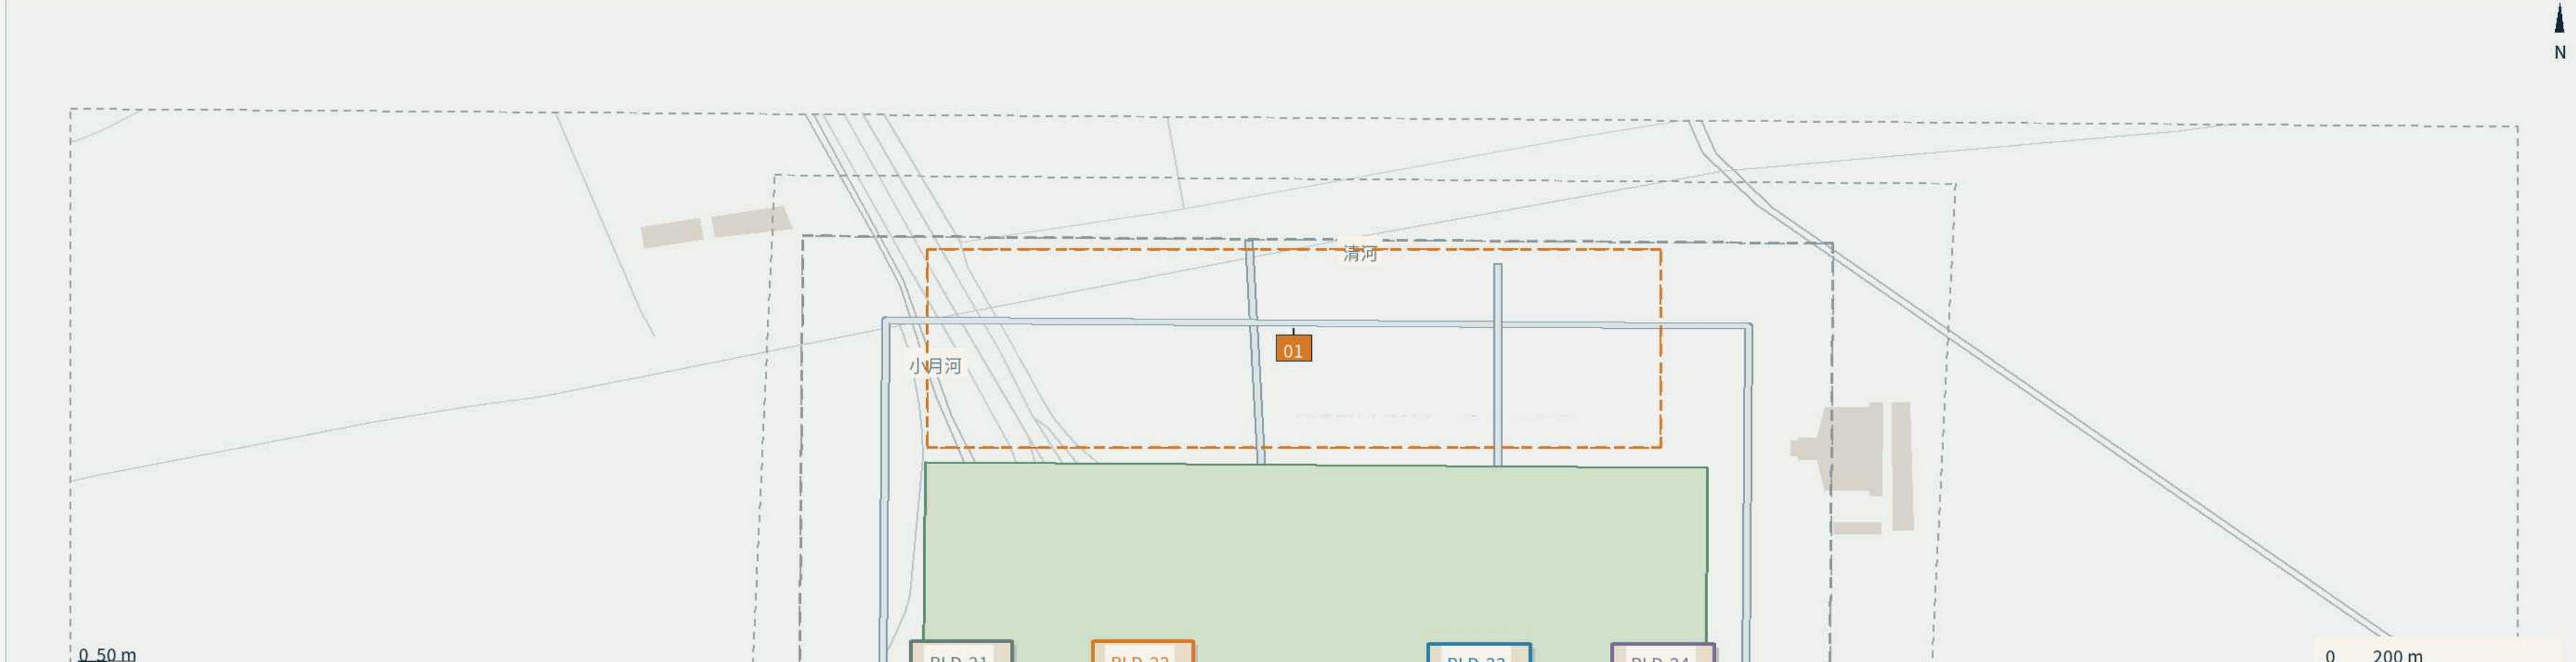

暂定边界 | 非官方红线，待测绘复核




公共地面 | 建议 06:00–22:00 开放；通行和人工柜台不依赖账号或算法。

测试与后勤 | 测试须预约、有人值守；后勤建议 07:00–09:00，入口与公共路线分开。

停止条件 | 隔离、噪声或证据链失效即实体急停；撤回测试占用，保留公共缓冲与人工服务。

B05 AI 原点 | 近校型成果转化社区

104.3 ha：以学习庭院和连续慢环，把私域创作、协作转化与公共生活逐级连接。

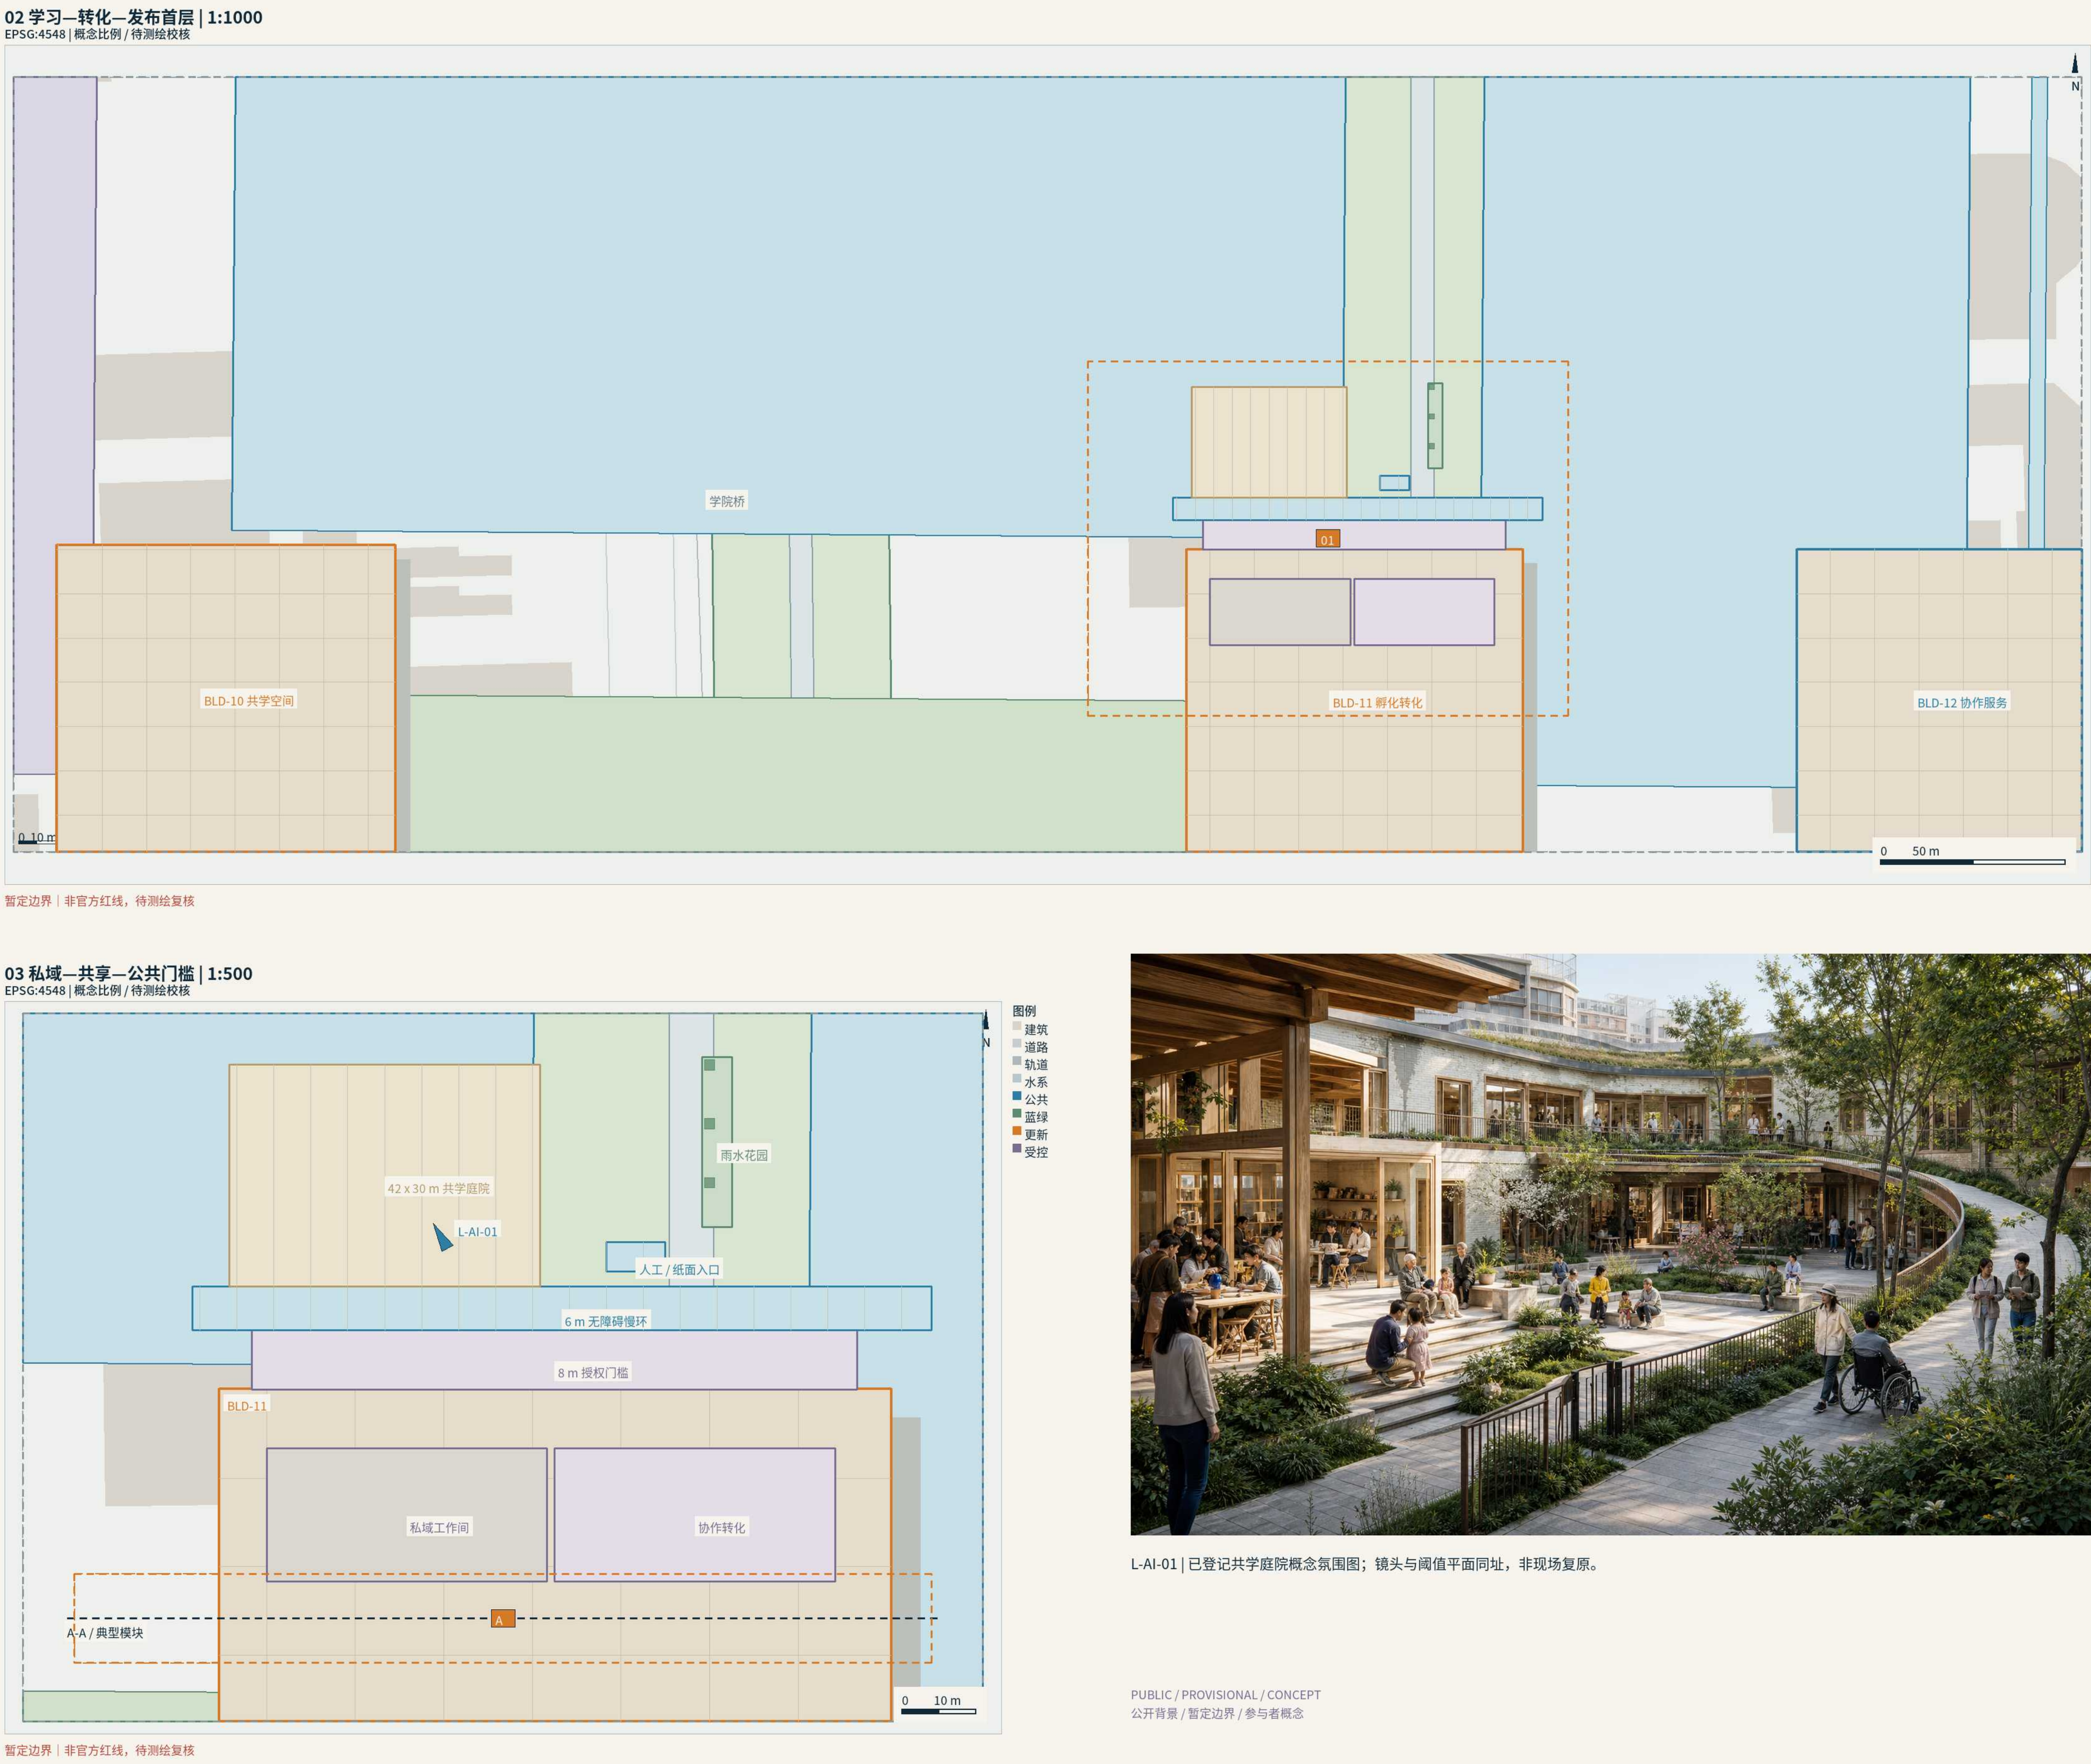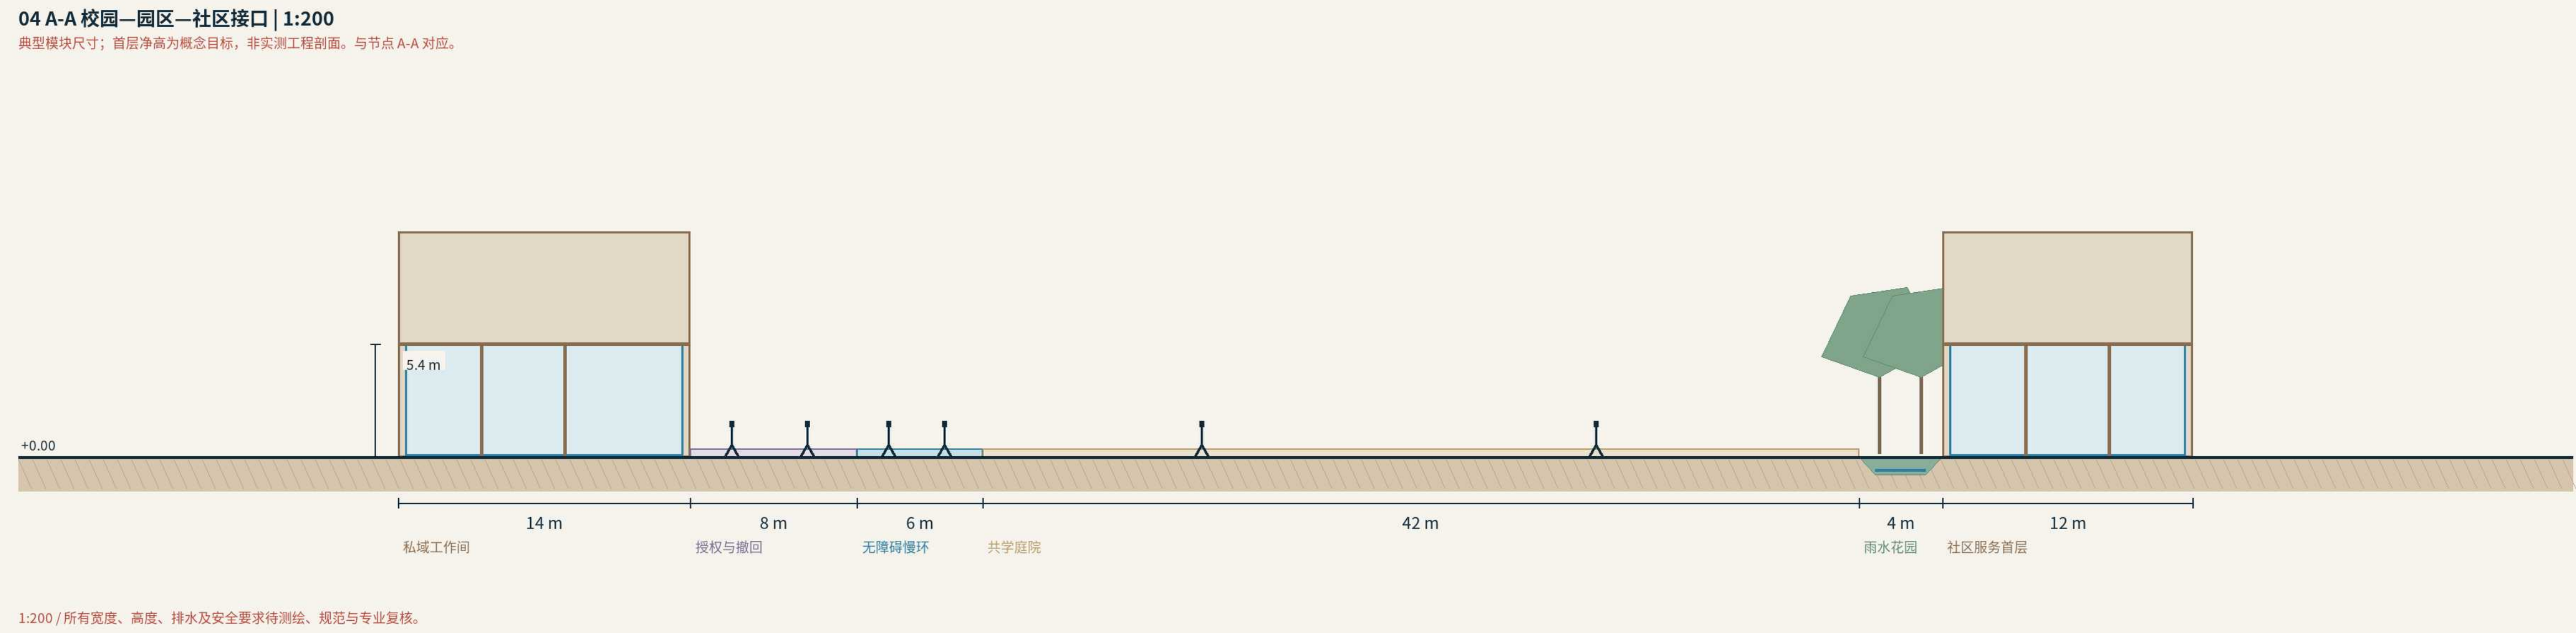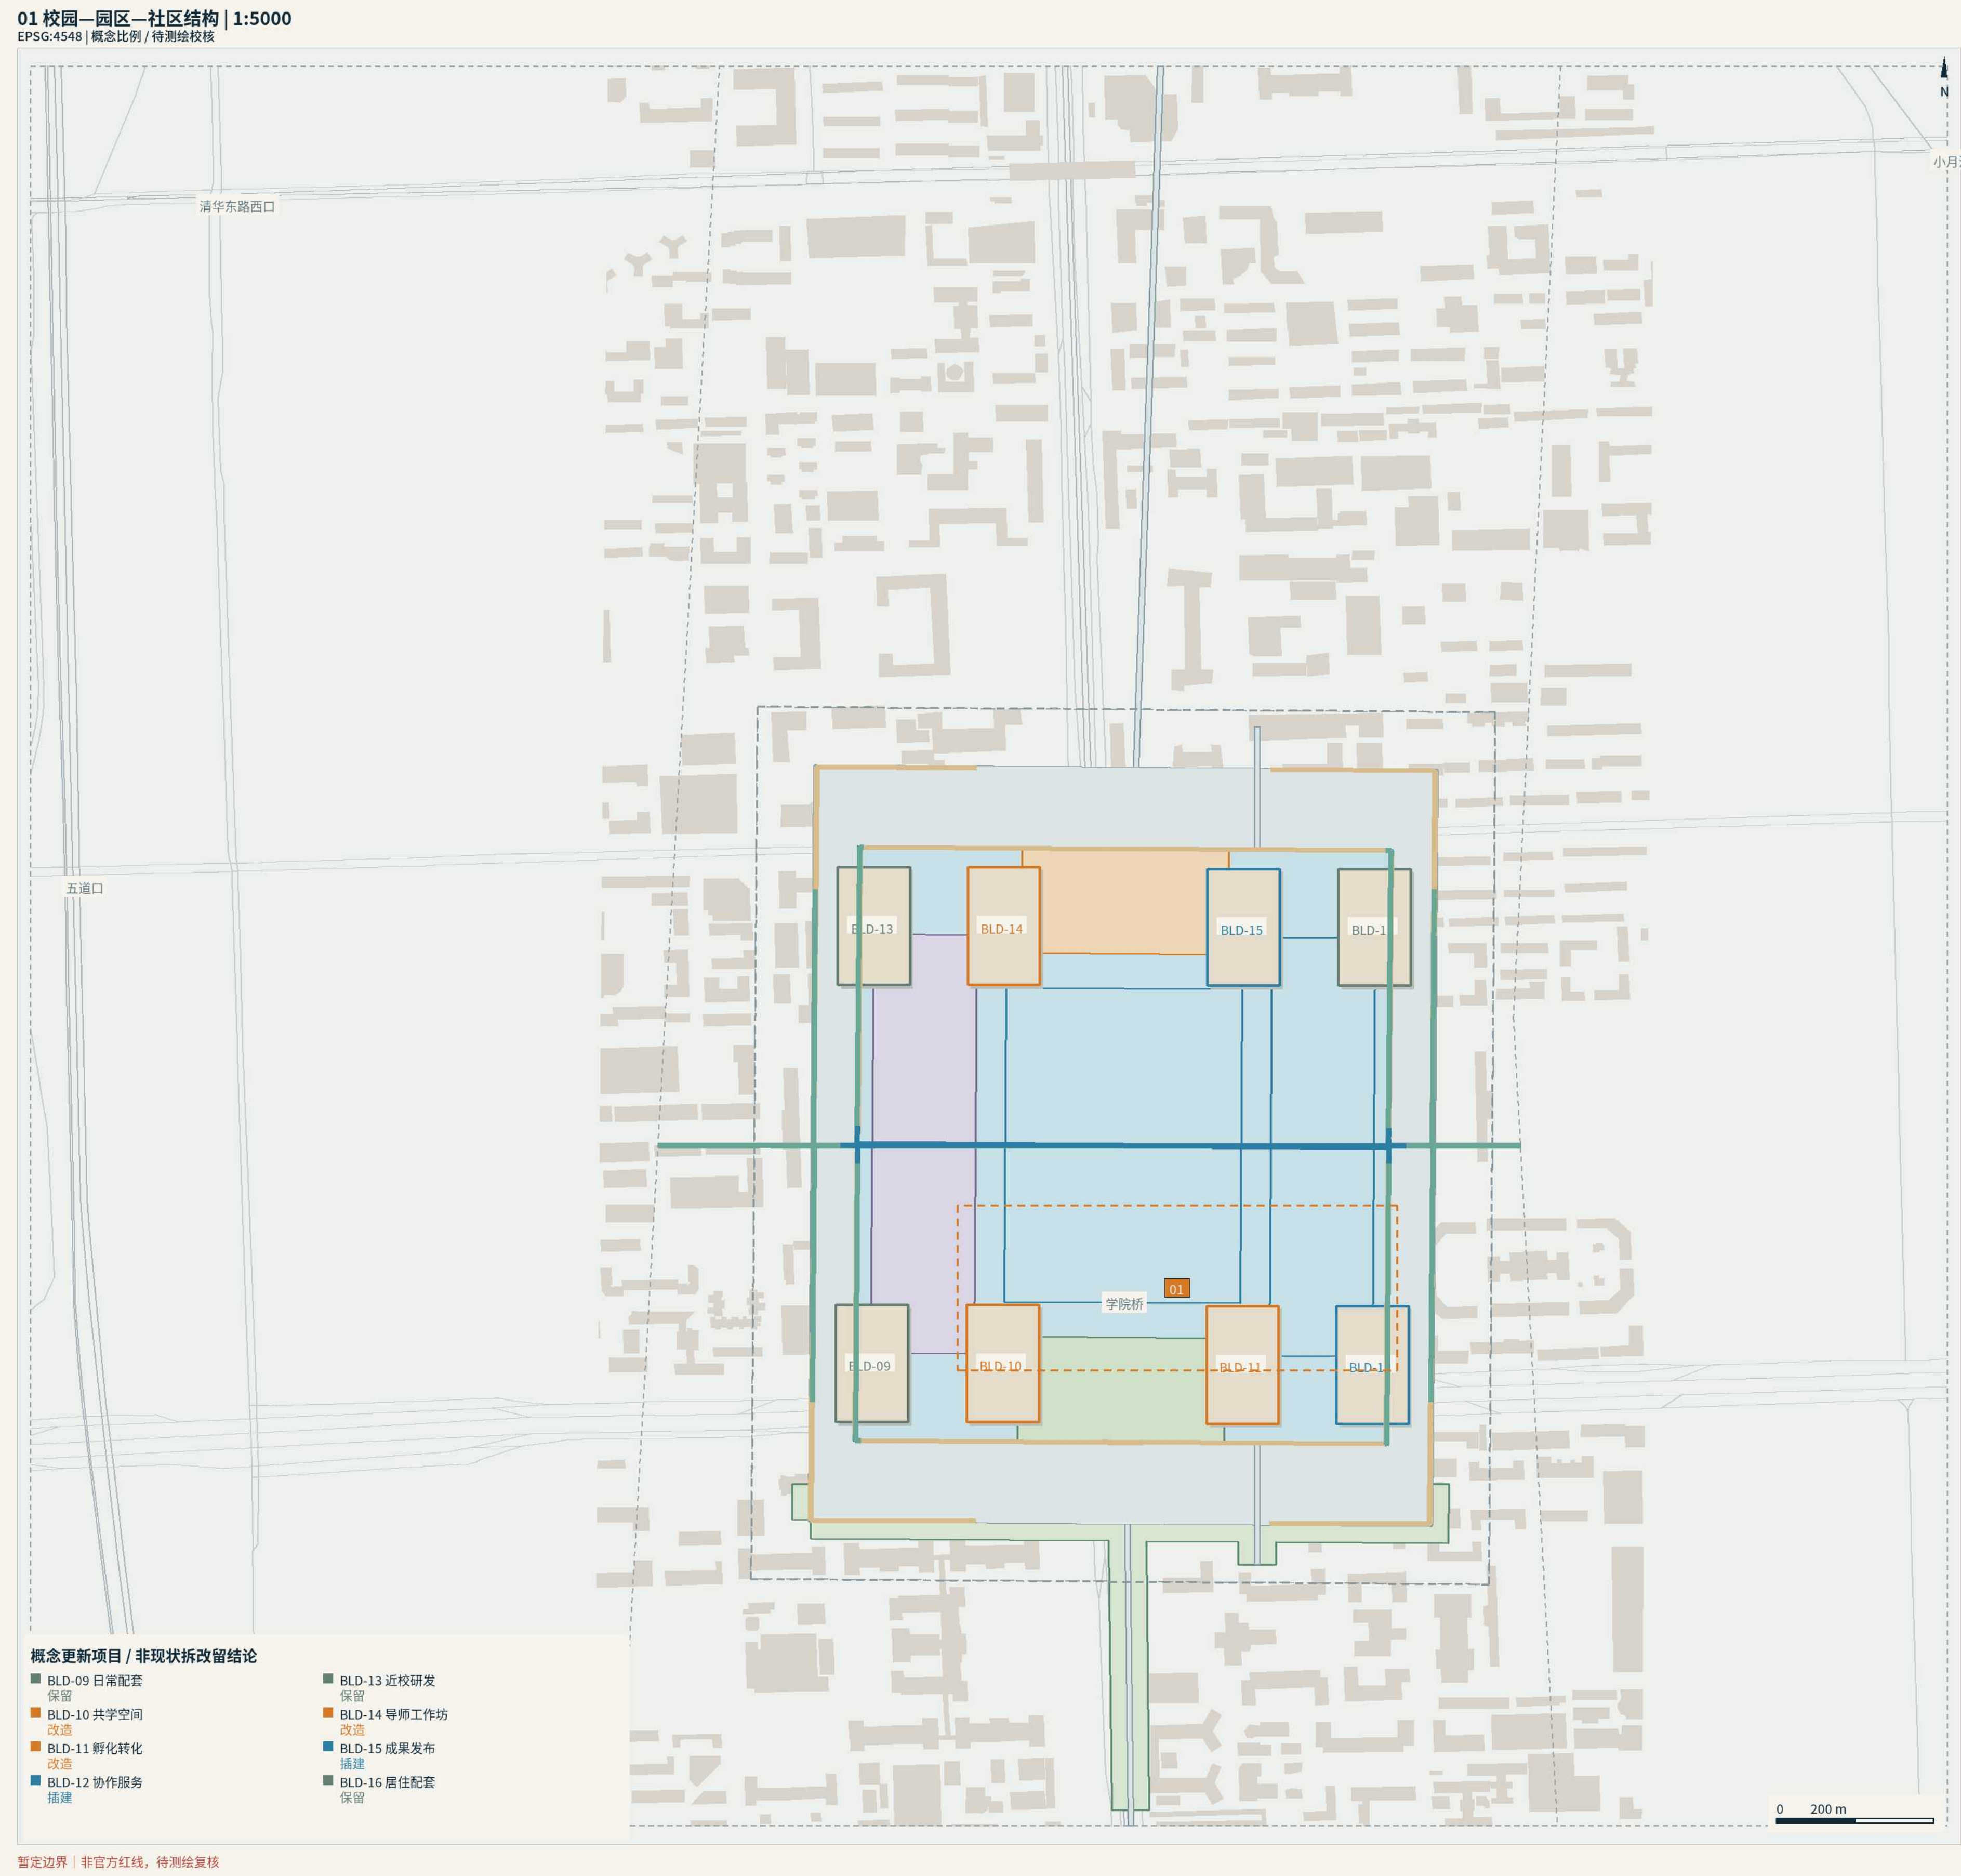


B06 大钟寺 | 高密城市型 AI 客厅

72.0 ha：公共、商业、安静与后勤分层；实际站点四象限单独定位，绝不平移暂定边界。

01 暂定 72.0 ha 全区结构 | 1:5000


EPSG:4548 | 概念比例 / 待测绘复核

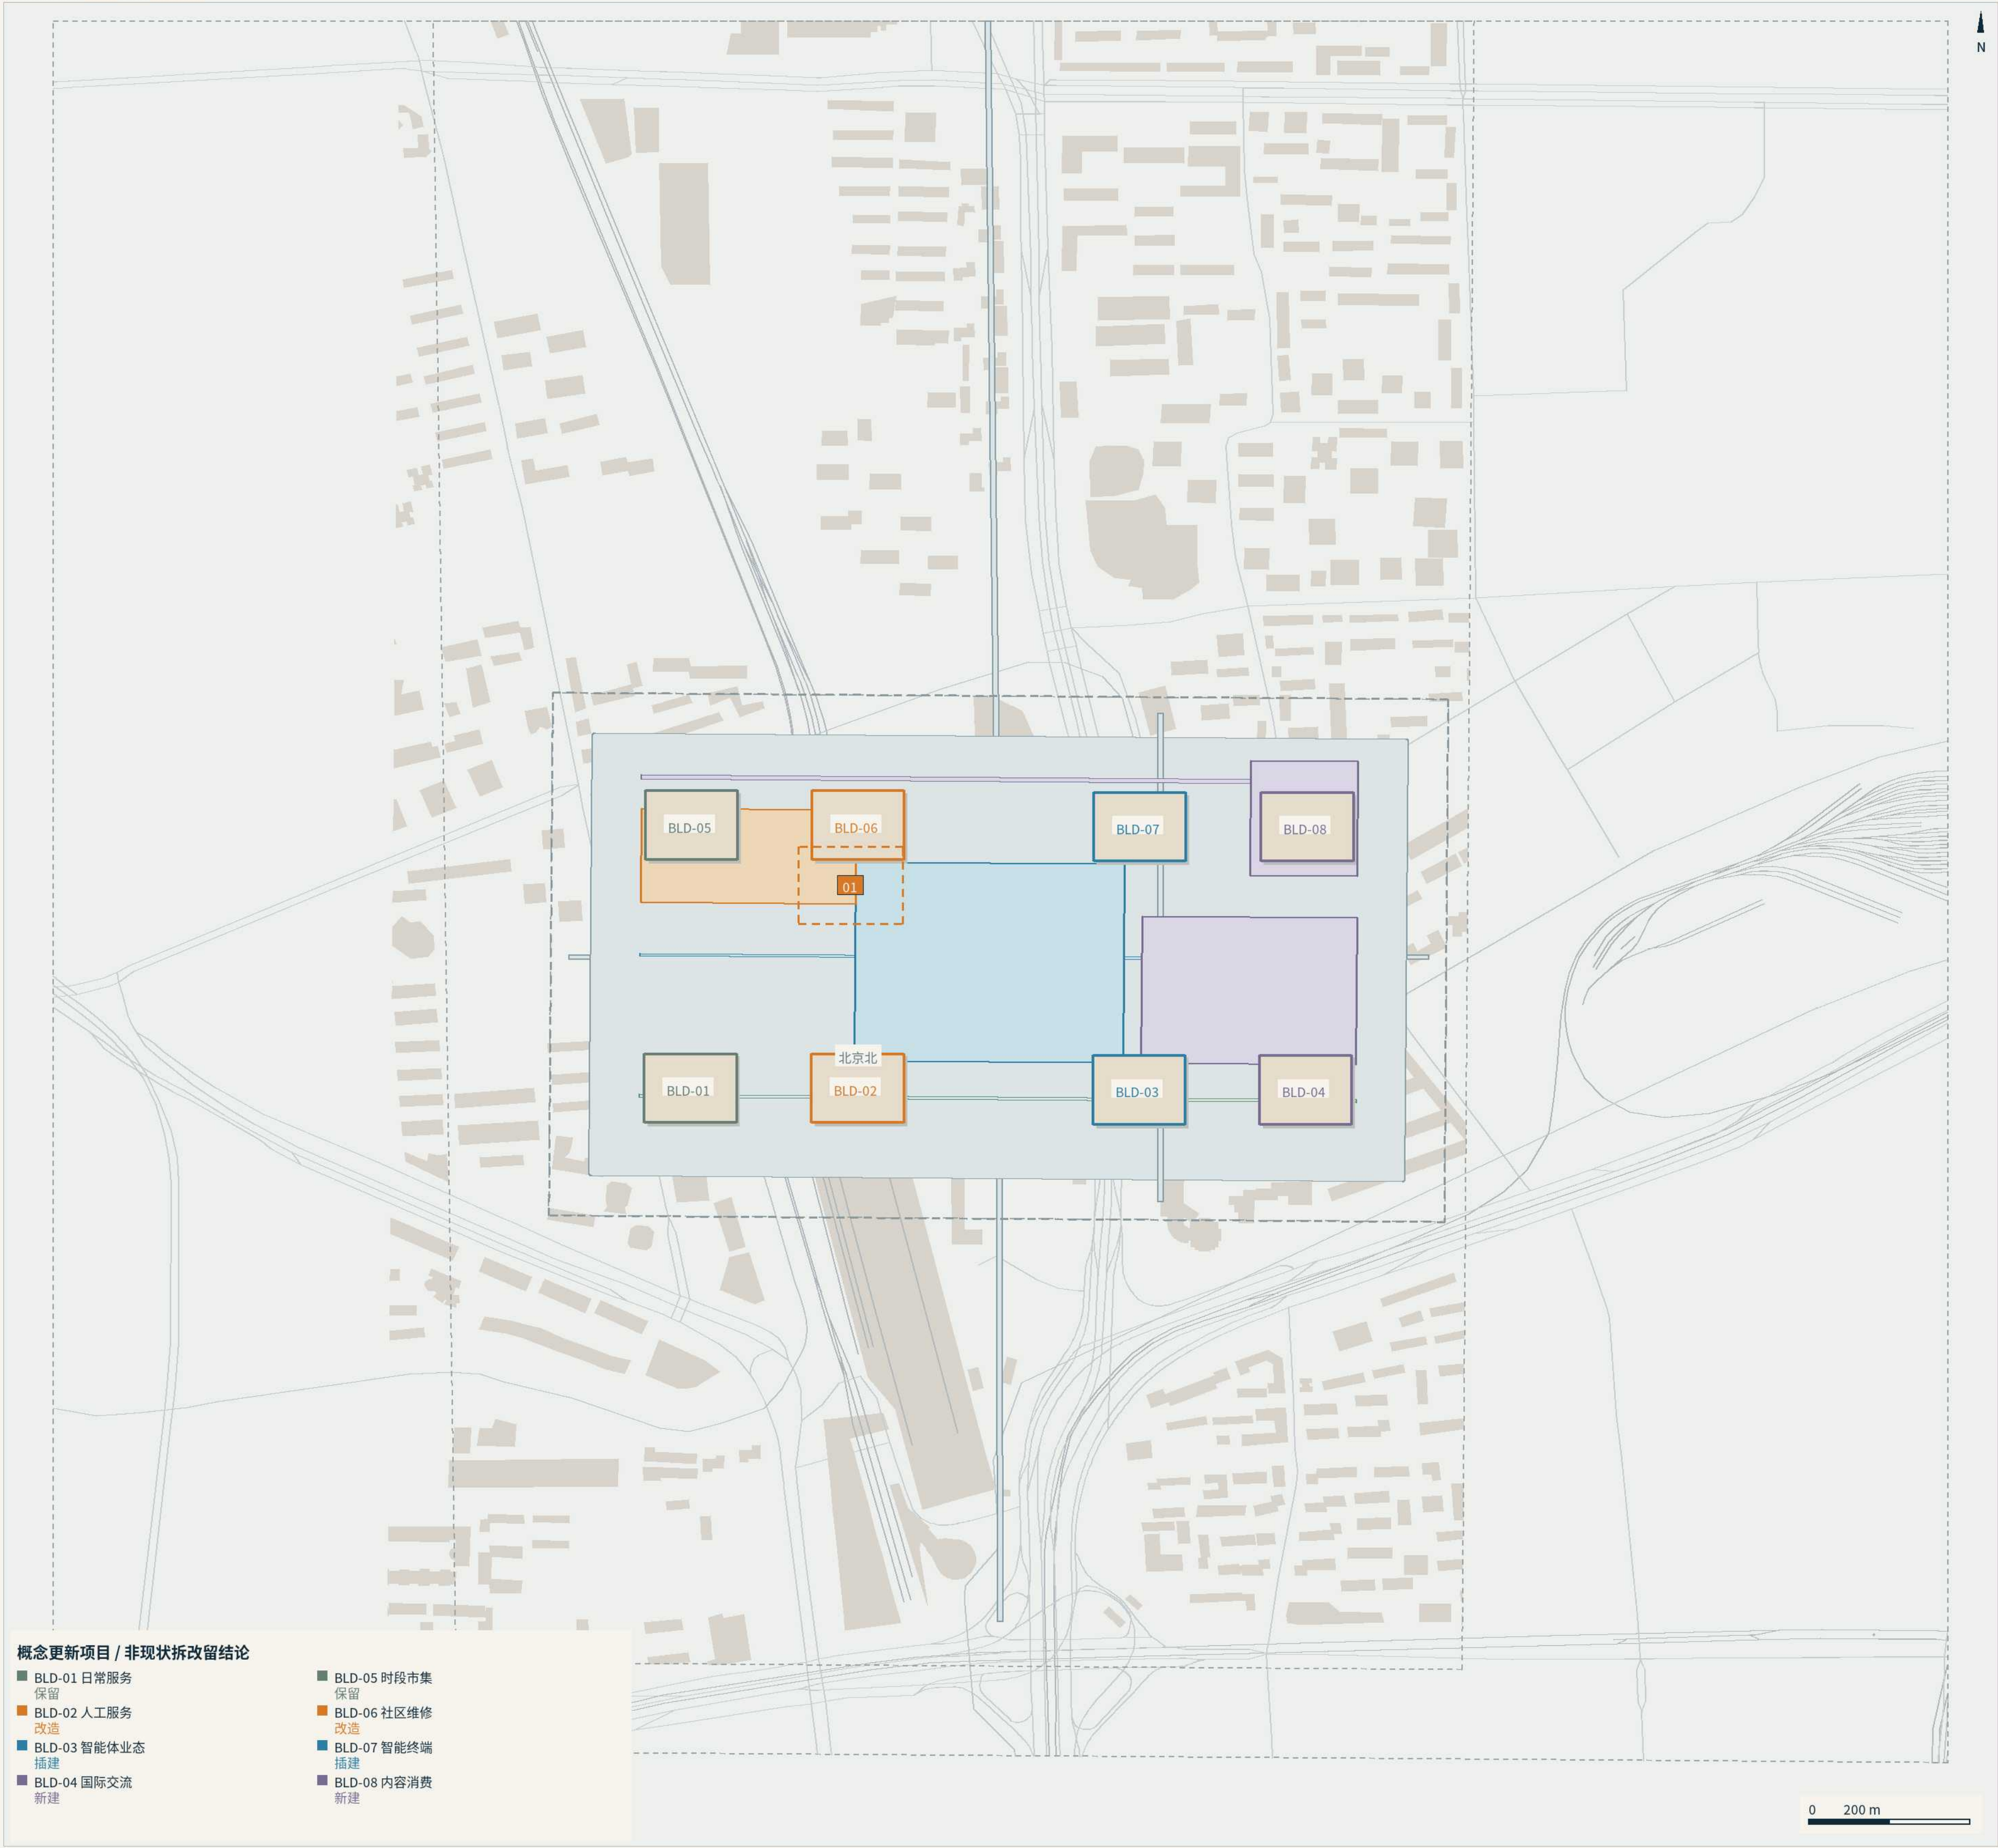

暂定边界 | 非官方红线，待测绘复核

04 A-A 条件性站城—街道—公共首层 | 1:200

典型模块尺寸；首层净高为概念目标，非实测工程剖面。与节点 A-A 对应。

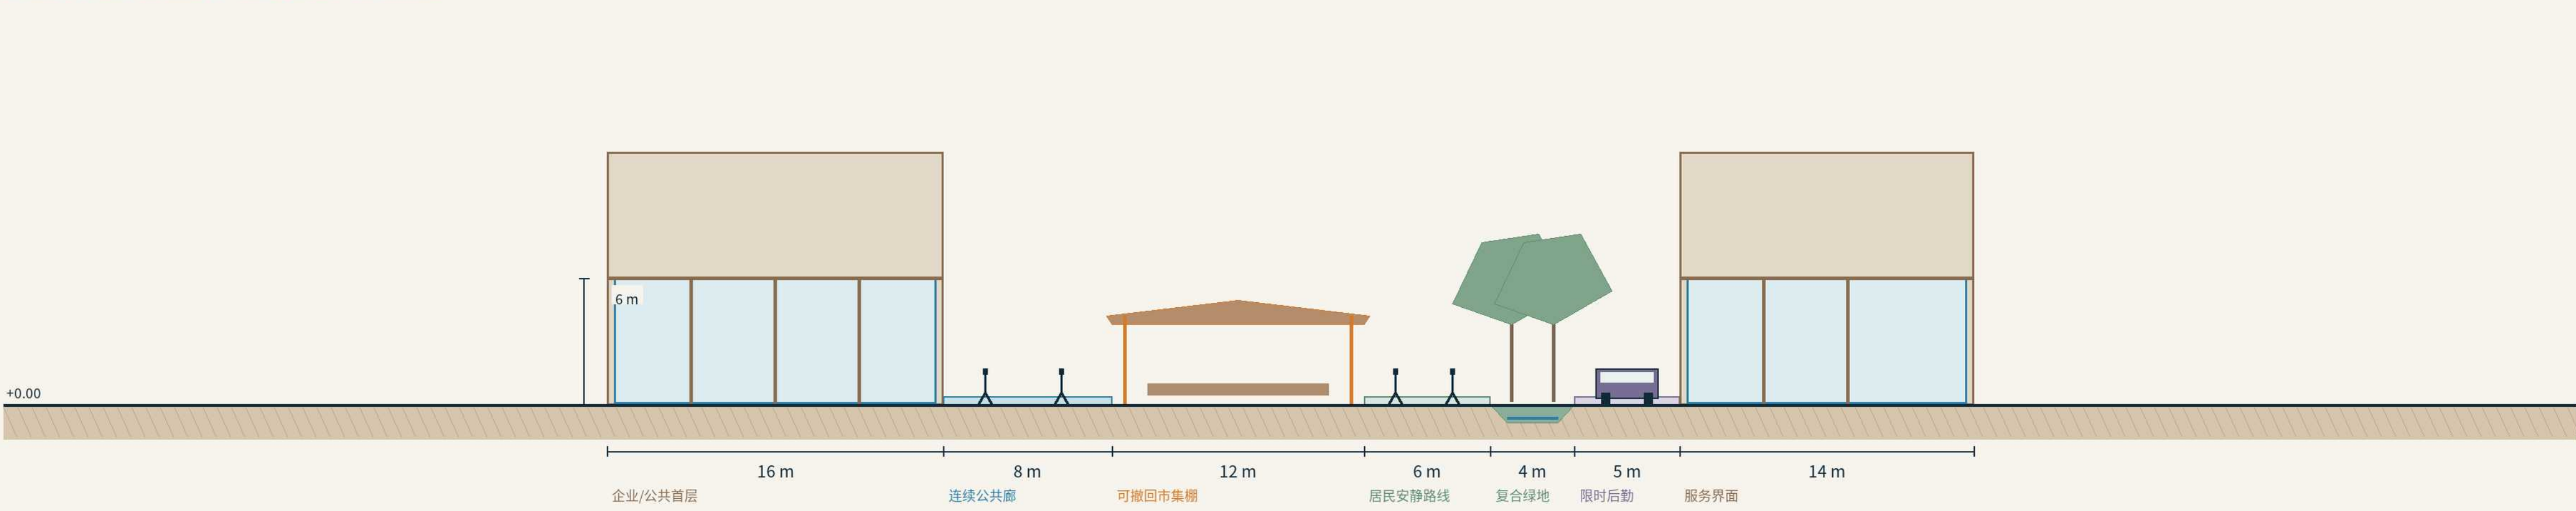


1:200 / 所有宽度、高度、排水及安全要求待测绘、规范与专业复核。

公共与商业 | 安静通行优先；建议 10:00-20:00 活动，开放首层留非消费座位和人工窗口。

骑行与后勤 | 集中车架不占净宽；建议 07:00-09:00 装卸，实体分隔；冲突即暂停，不挤占安静路线。

02 实际大钟寺站四象限提案 | 1:1000


EPSG:4548 | 概念比例 / 待测绘复核

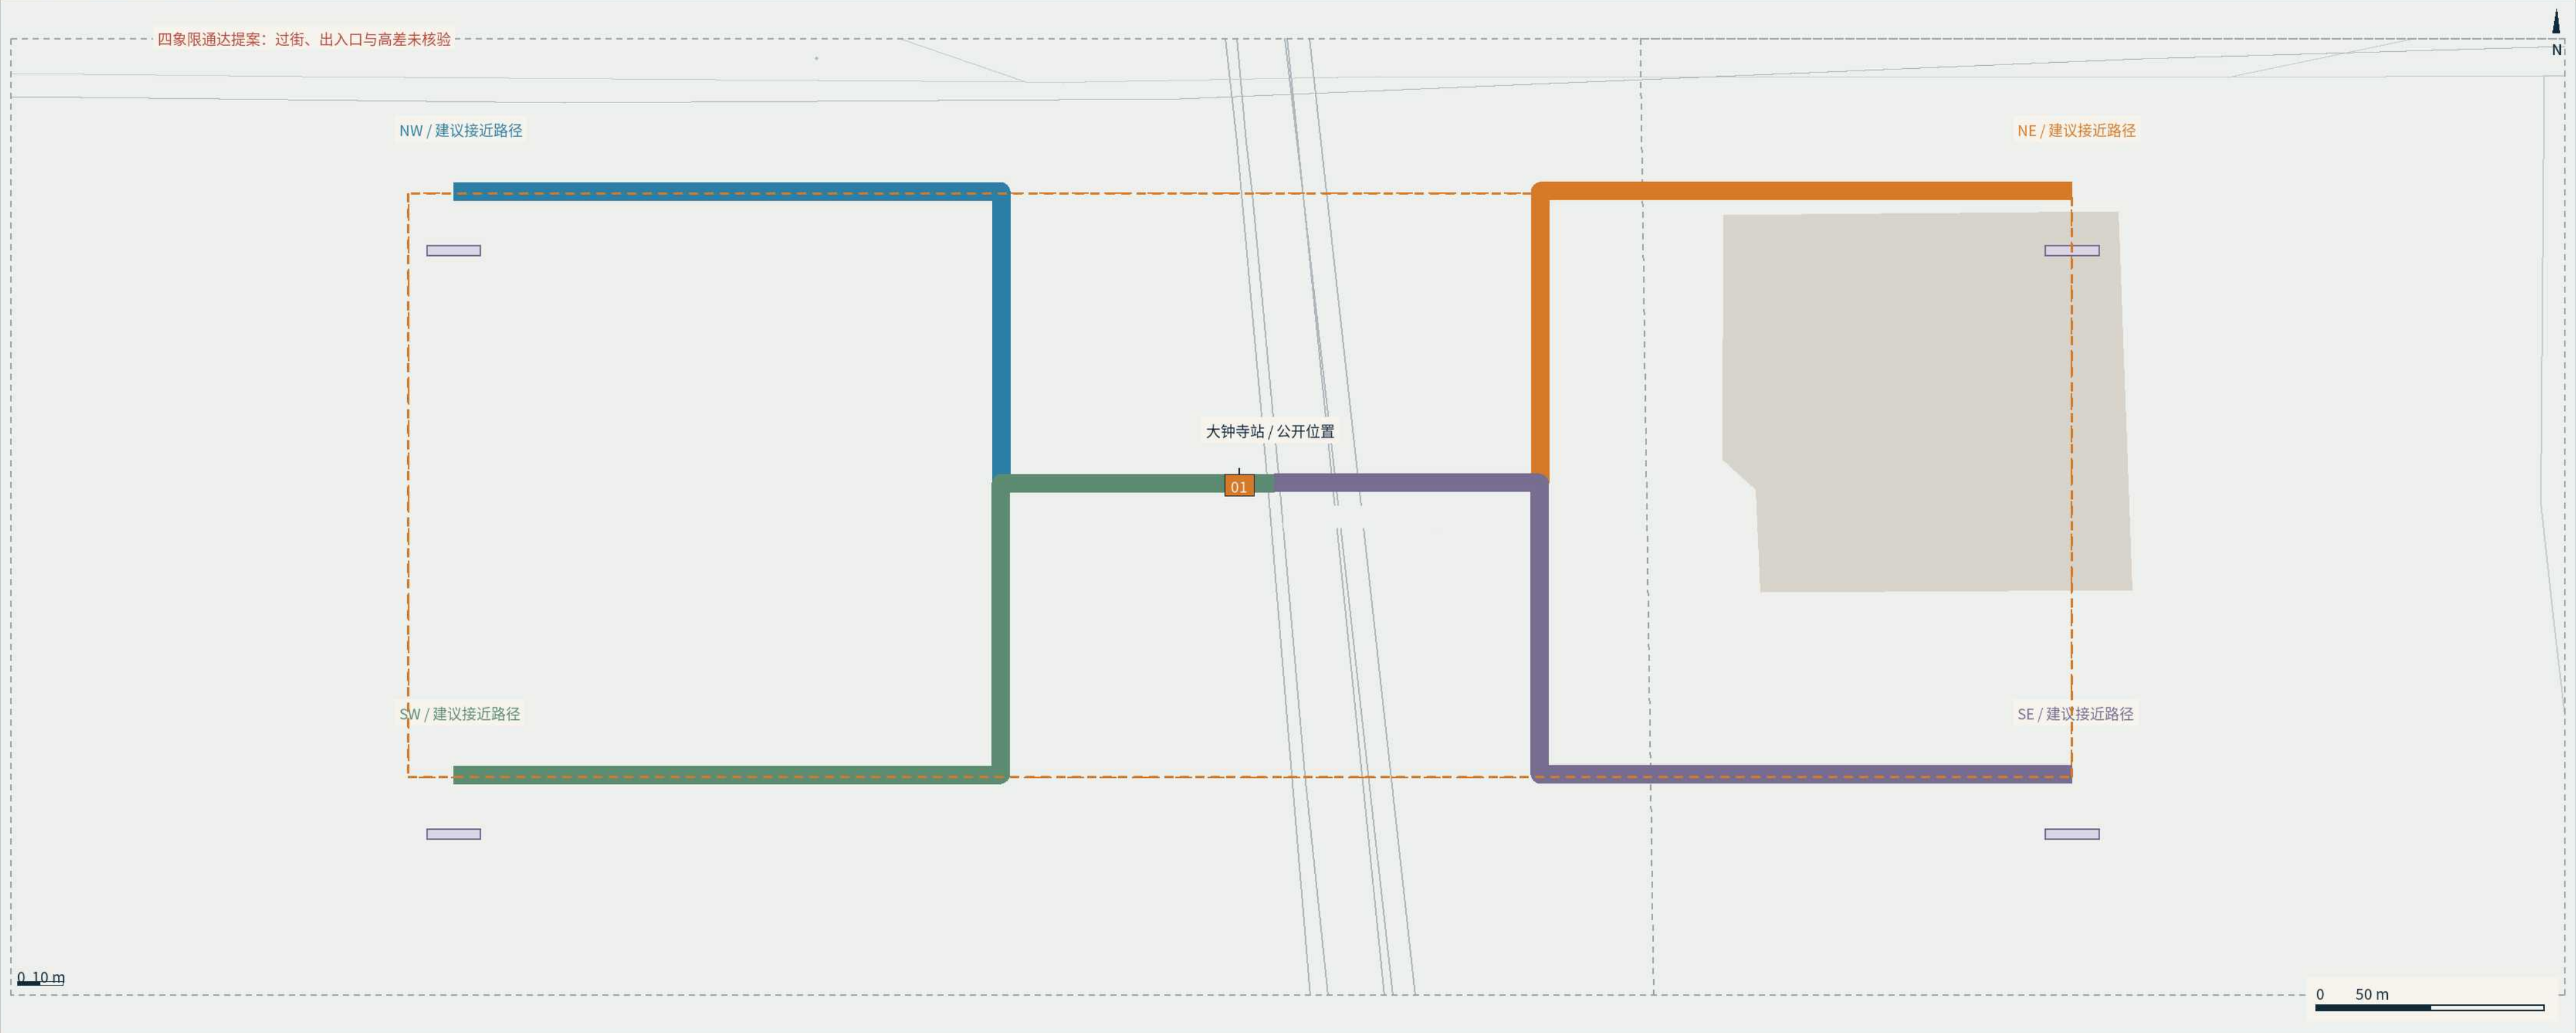

暂定边界 | 非官方红线，待测绘复核

03 暂定区公共首层与安静路线 | 1:500

EPSG:4548 | 概念比例 / 待测绘复核

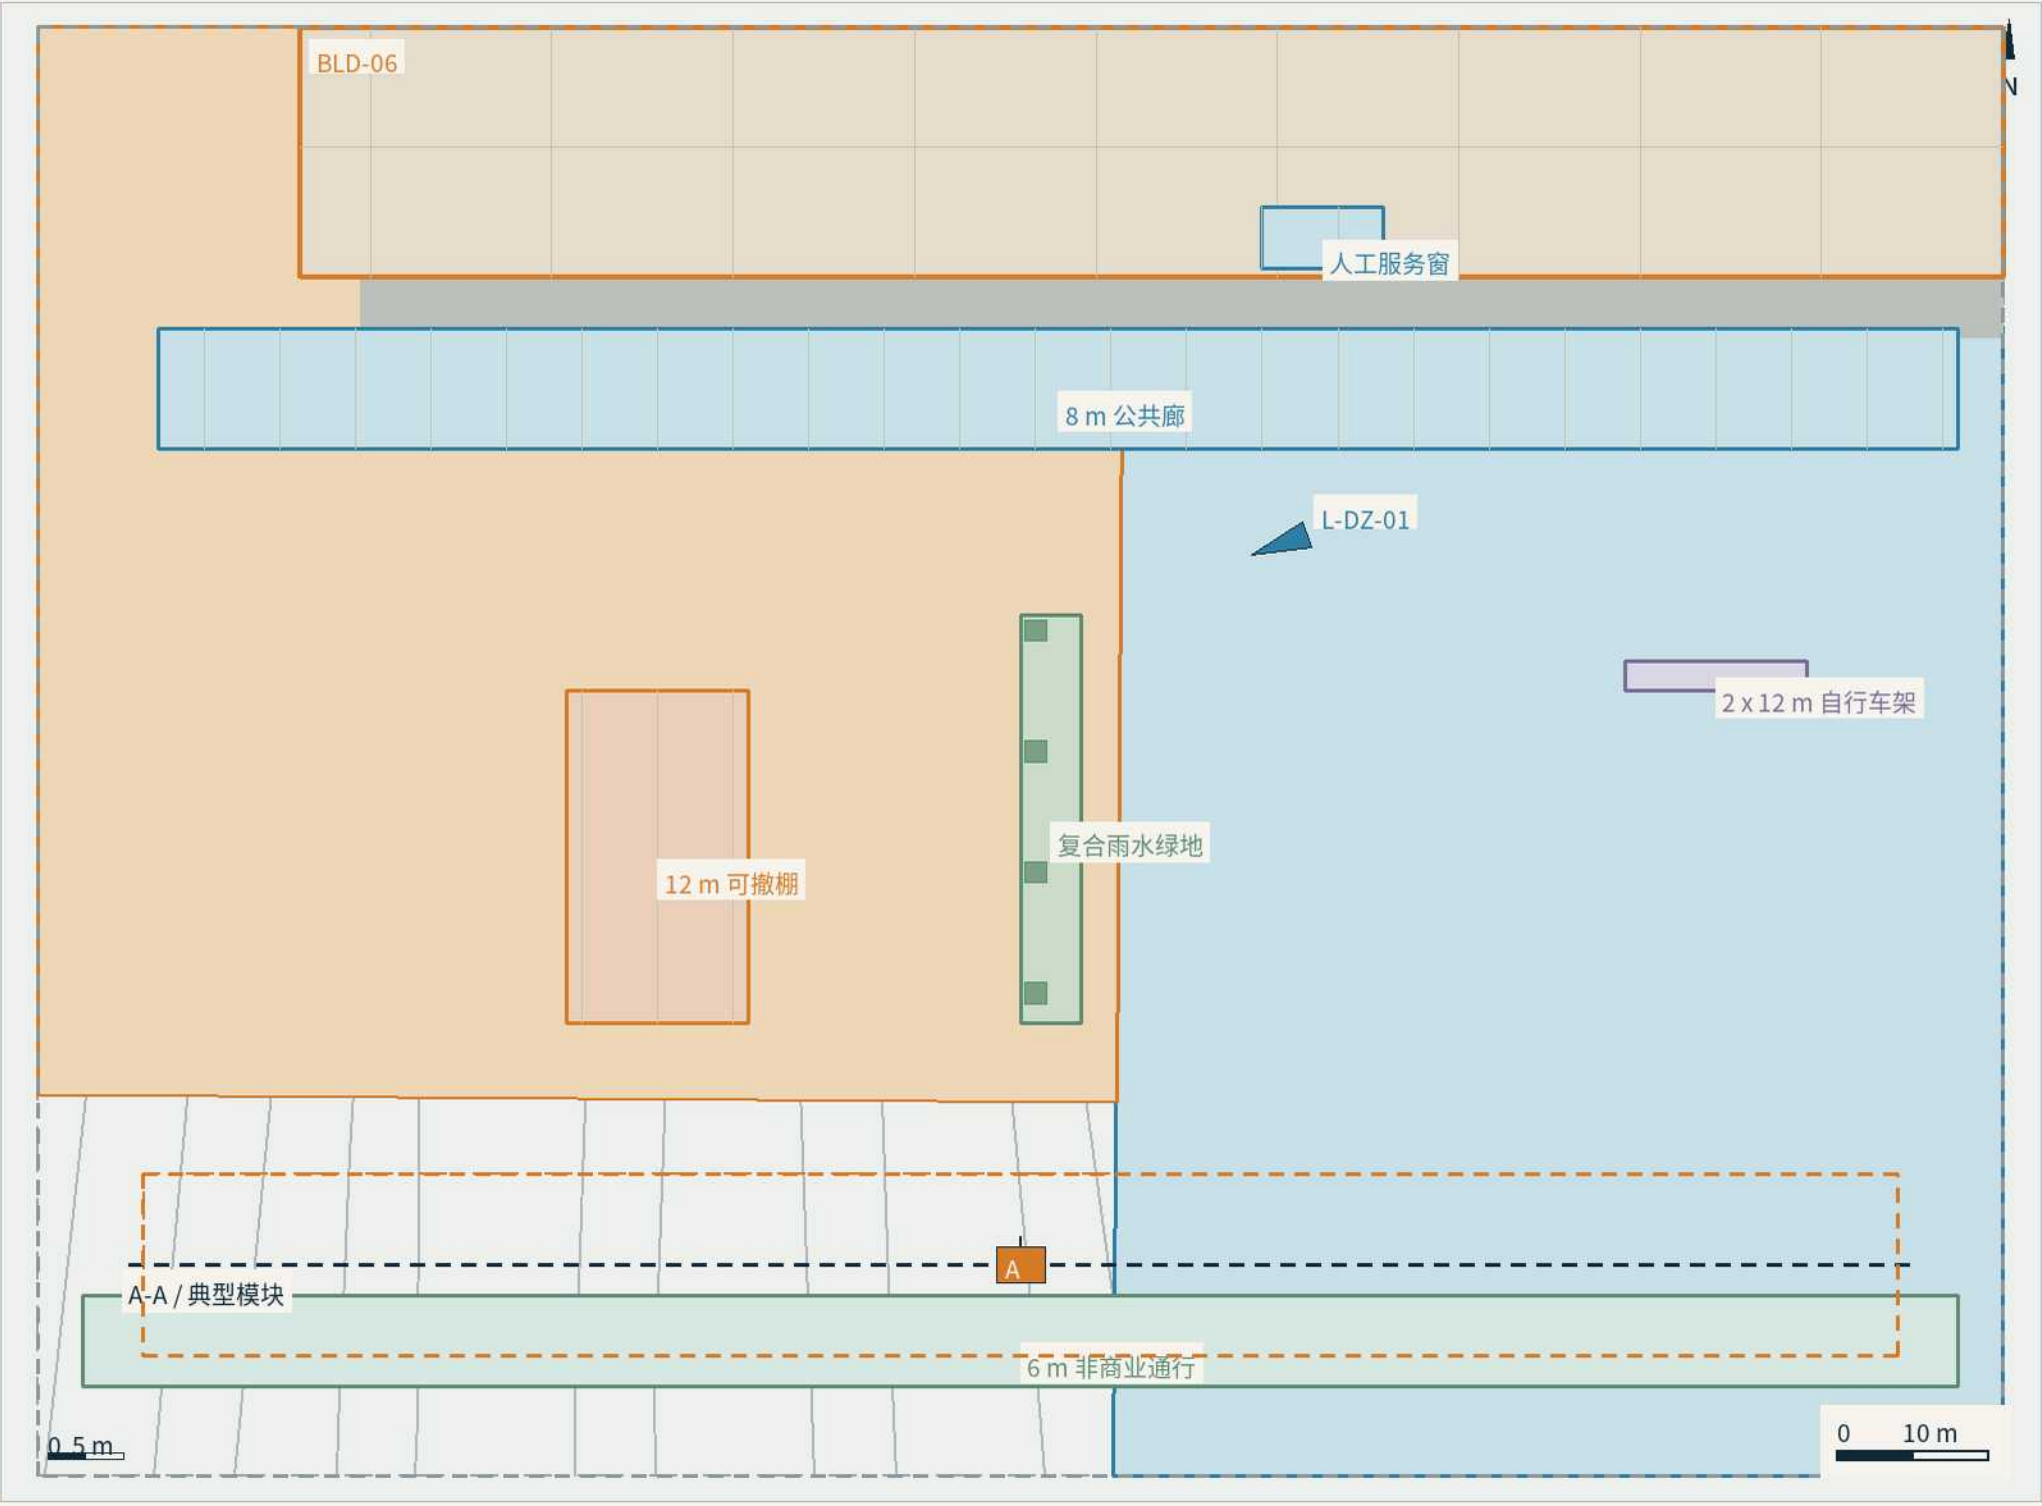

暂定边界 | 非官方红线，待测绘复核




L-DZ-01 | 暂定公共首层的已登记概念氛围图；不是实际大钟寺站立面或站城工程。

PUBLIC / PROVISIONAL / CONCEPT
公开情景 / 暂定边界 / 参与者概念

05 安静—公共—物流分层 | 1:6000

EPSG:4548 | 概念比例 / 待测绘复核

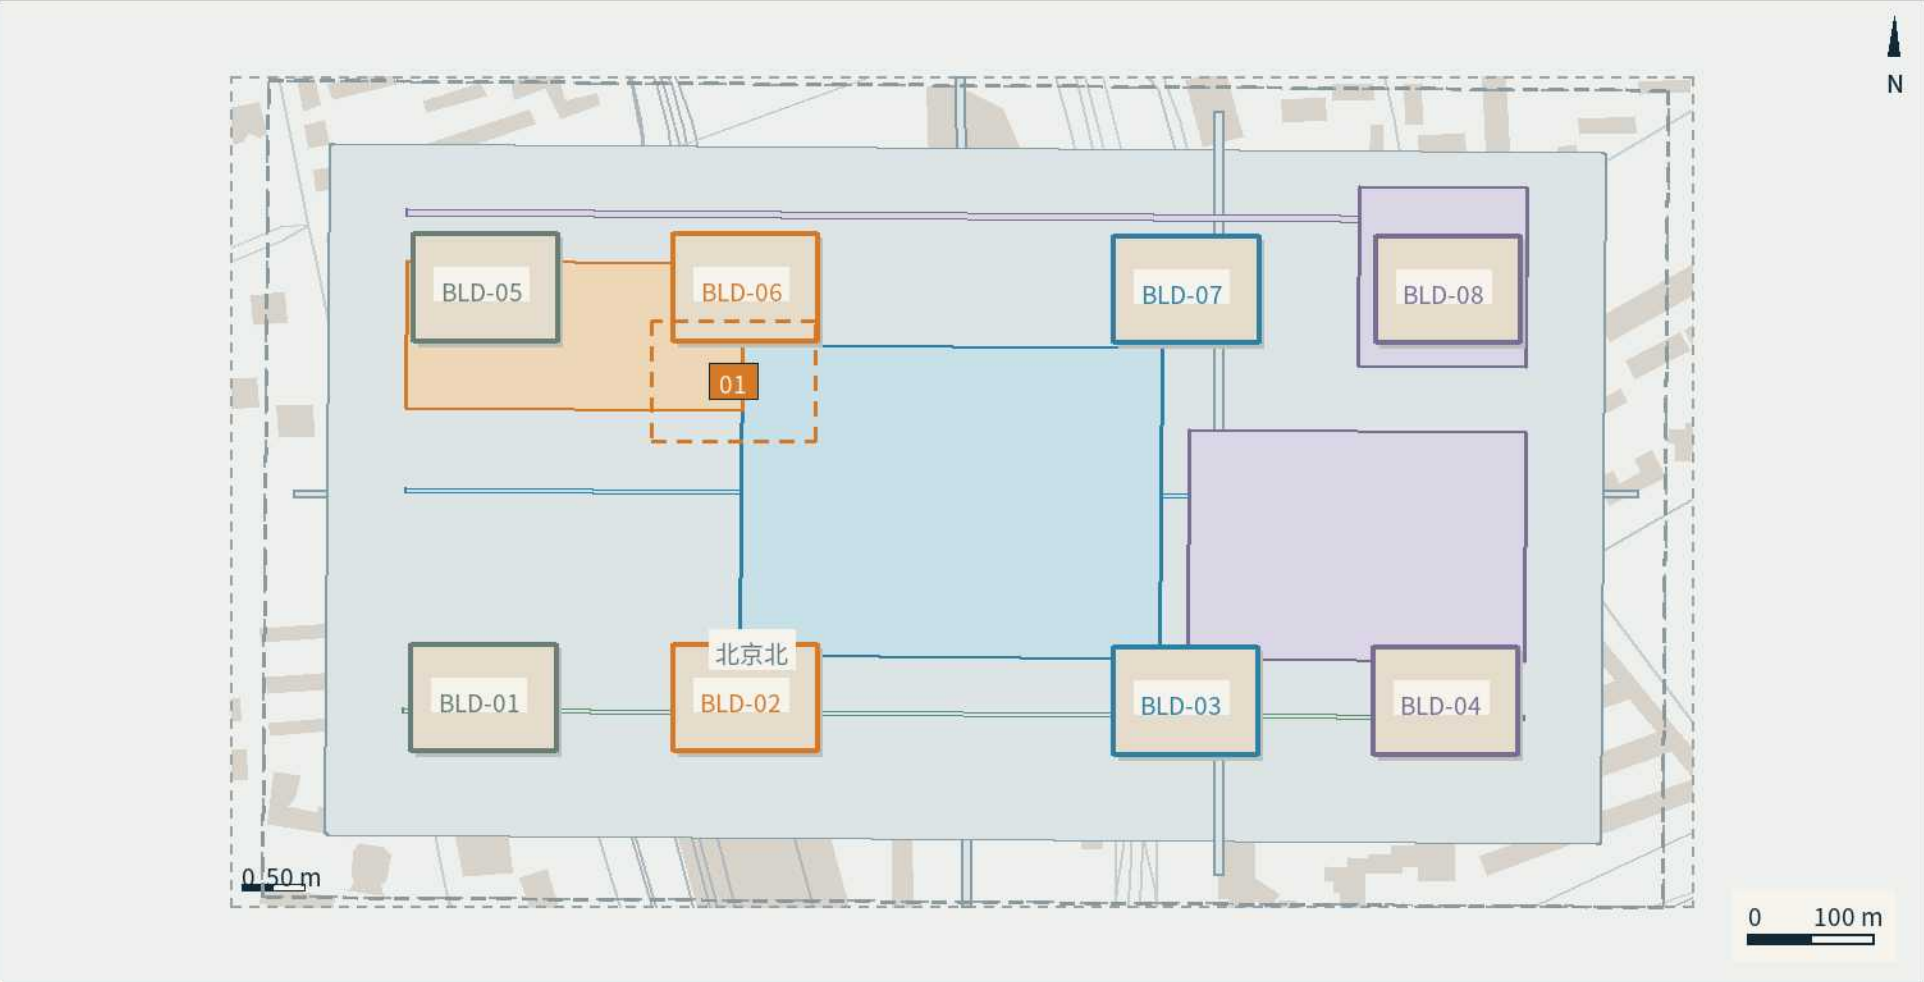

暂定边界 | 非官方红线，待测绘复核

安静路线：全天保留，非消费也可使用。

公共首层：社区维修、国际交流与 AI 原生业态并置。

建议活动 10:00-20:00；装卸 07:00-09:00；冲突即停止。

本图仍为暂定重点区；实际大钟寺站在北侧约 2.2 km，见节点 02。


站城交接 | 暂定区距公开大钟寺站约 2.2 km；桥、隧、站口与接驳均未批准，须正式边界与交通复核后再定。

从项目到实施


先开放公共地面，再验证城市服务；用有人负责、可停止、可恢复的项目连接三种城市。

01 条件性分期项目地图 | 1:12500 | 北向在右

概念比例 | 待测绘确认

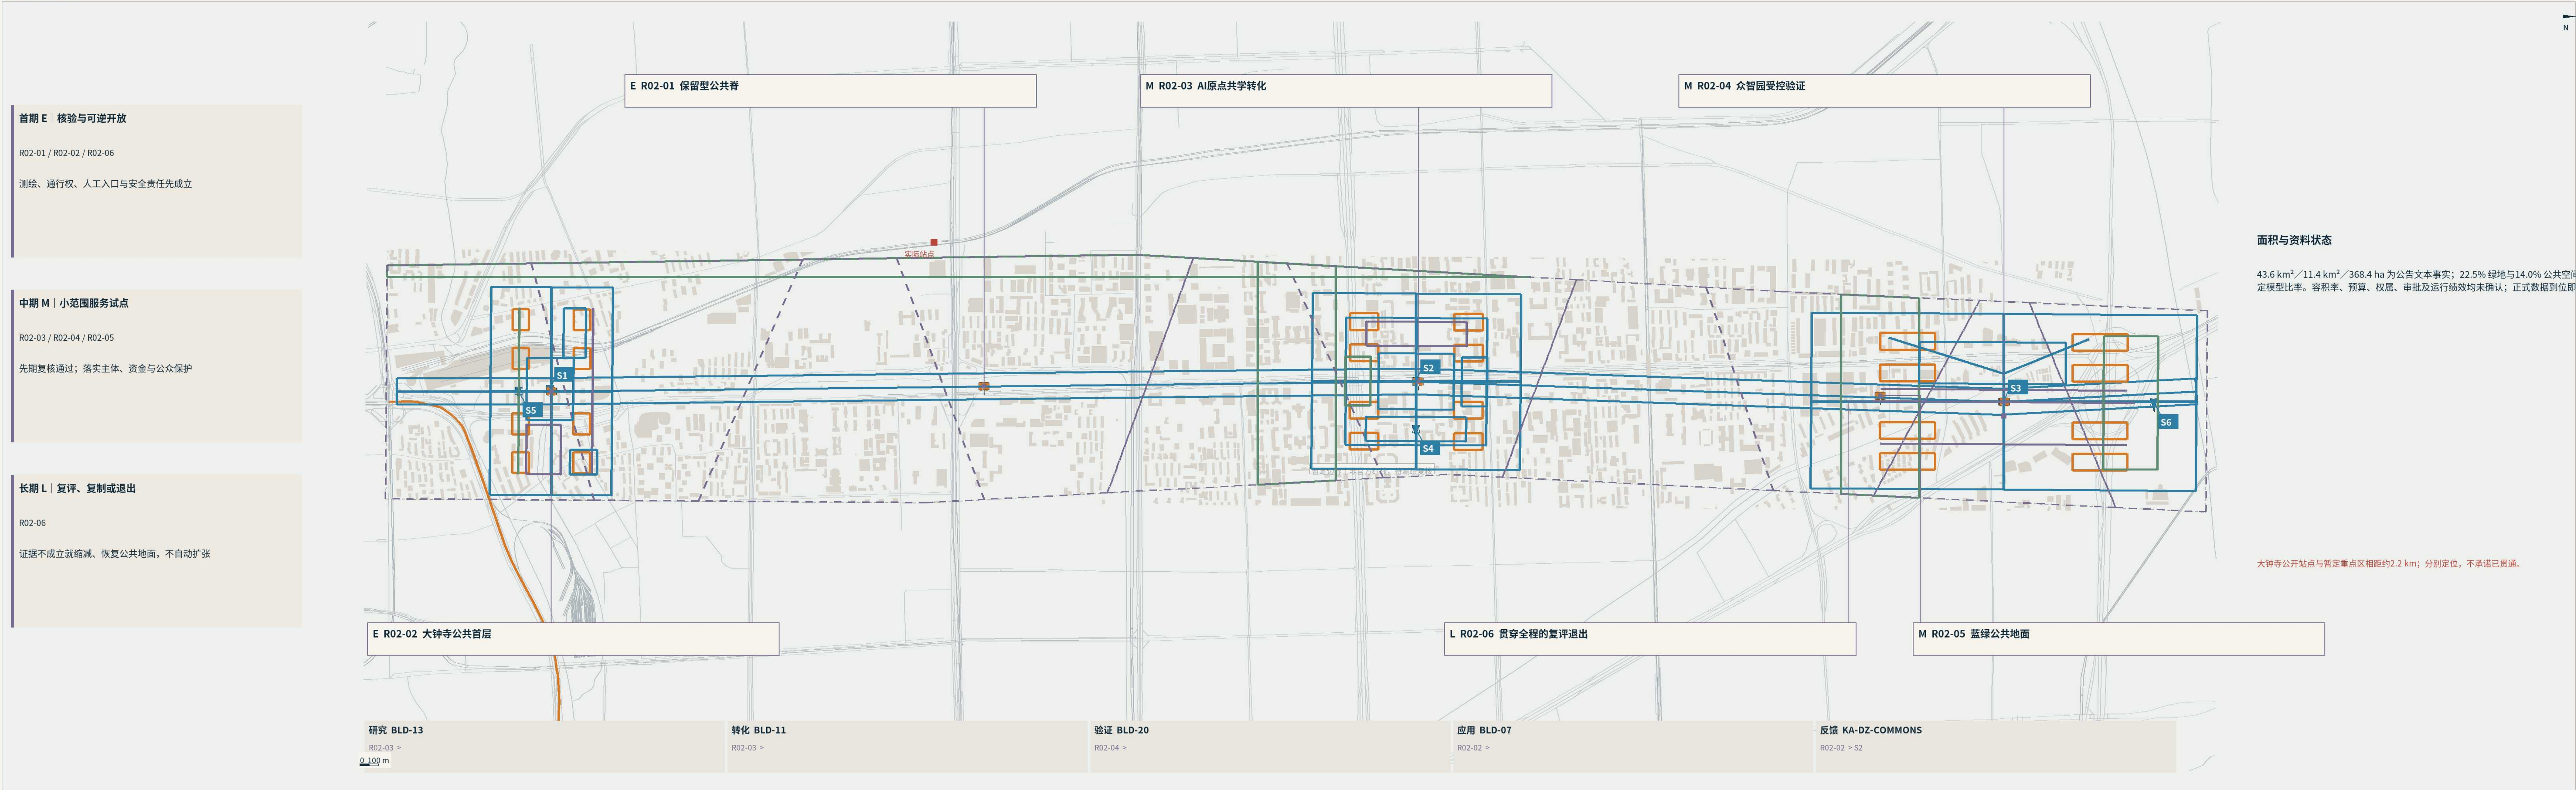

L-B07-01,L-B07-02,L-B07-03,L-B07-04,L-B07-05,L-B07-06 | 概念动作；虚线非官方红线

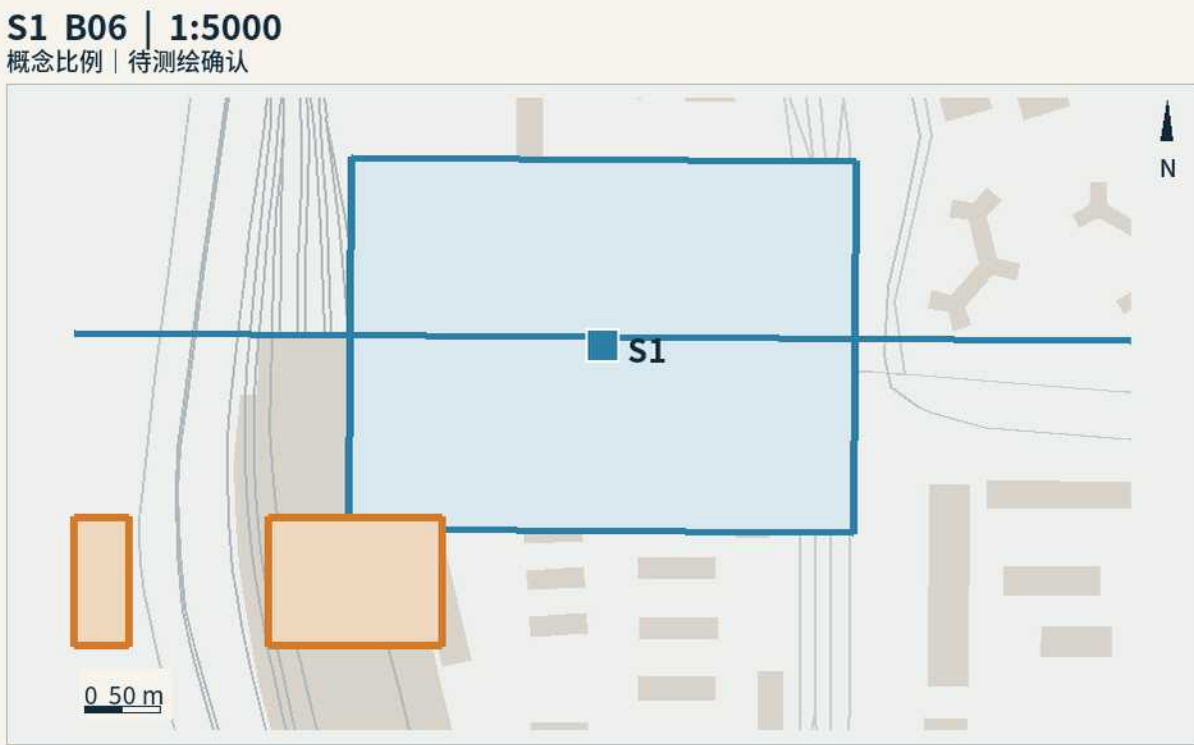

| 概念动作；虚线非官方红线

不用账号也能办事

R02-02 | B06 | KA-DZ-COMMONS

人物/地点 不会用智能手机的居民/大钟寺暂定区人工首层


空间动作 留无消费座位、无障碍入口与人工柜台

运营 在地公共服务类（待确认）

非AI 窗口、电话、纸质回执

成功待验 核验无账号服务闭台及等价体验

停止 强制登录或超权取数就停止采集

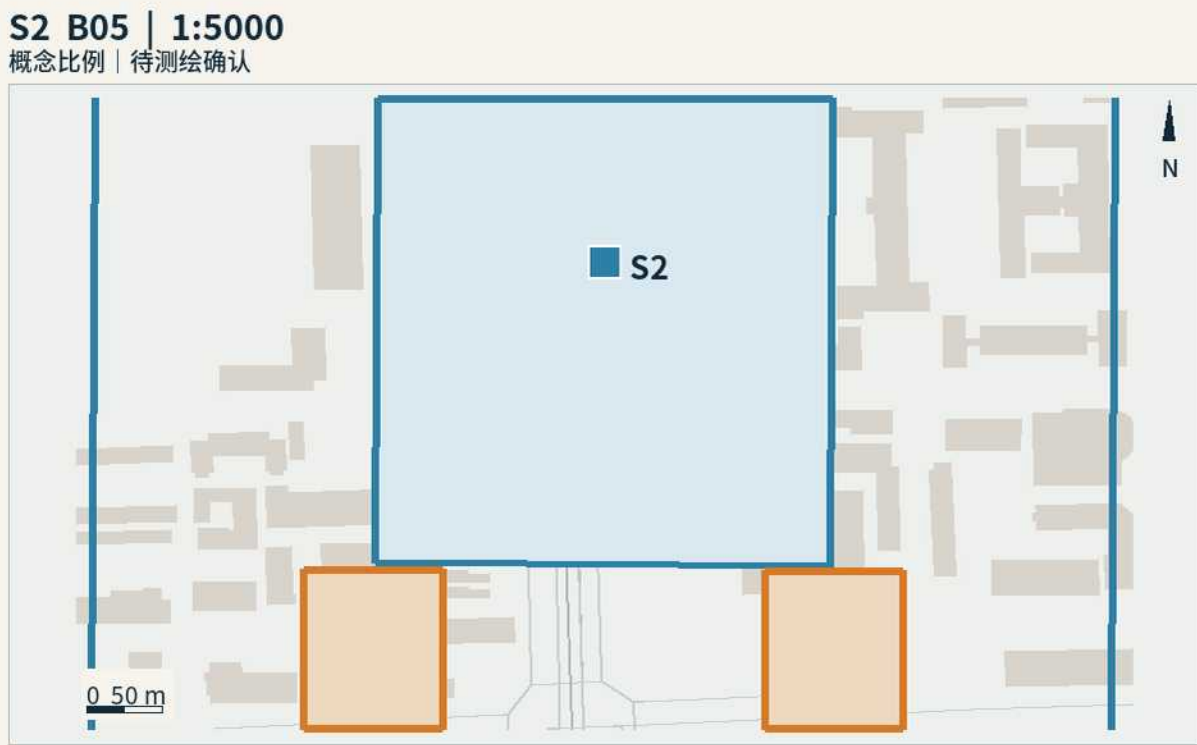

| 概念动作；虚线非官方红线

从学习到真实转介

R02-03 | B05 | KA-AI-COMMONS

人物/地点 学生与转岗学习者/AI原点共享庭院与导师首层


空间动作 开放庭院接共享工作间，私域仍可关闭

运营 校园社区导师类（待确认）

非AI 真人导师、电话预约、纸面作品集

成功待验 核对导师转介与学习者自愿确认

停止 未成人保护或同意失效即停止匹配

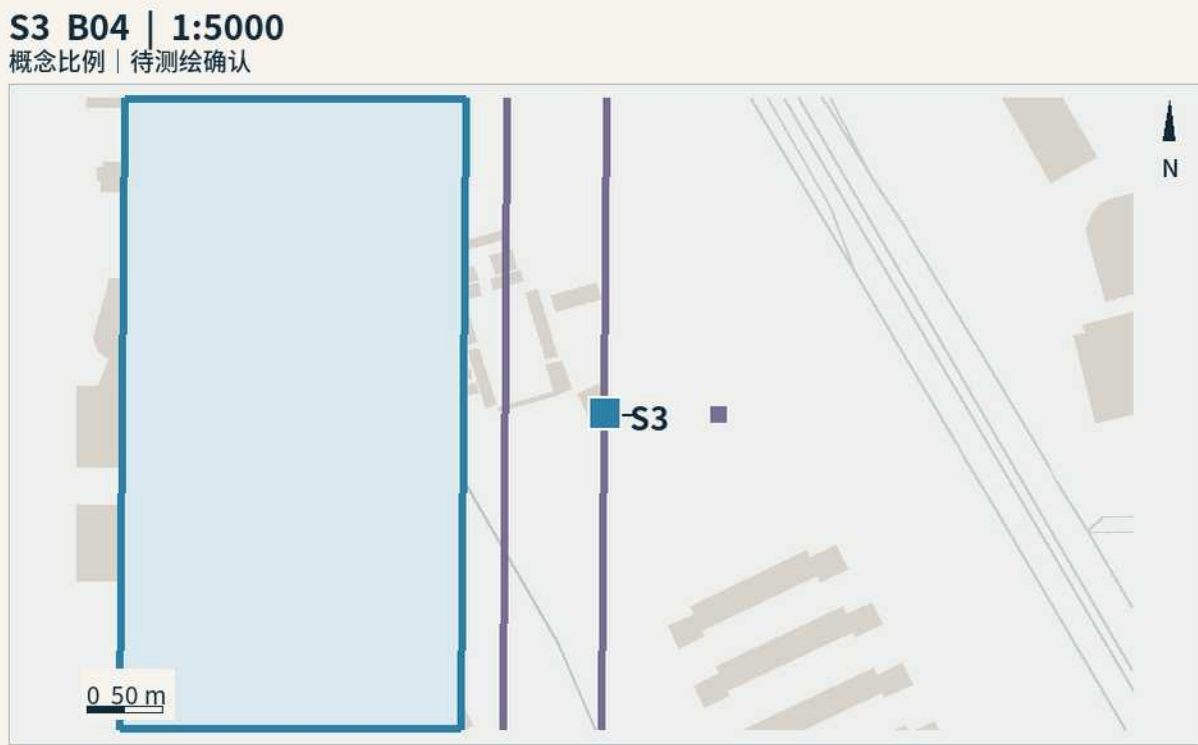

| 概念动作；虚线非官方红线

验证先于扩张

R02-04 | B04 | KA-ZZ-TEST-SPINE

人物/地点 小型研发团队与安全值守人/众智园受控测试带


空间动作 实体分隔测试、公共展廊与独立后勤

运营 创新安全运营类（待确认）

非AI 人工预约、实体急停与人工接管

成功待验 复核测试带与独立复现记录

停止 隔离、噪声或证据失效即急停

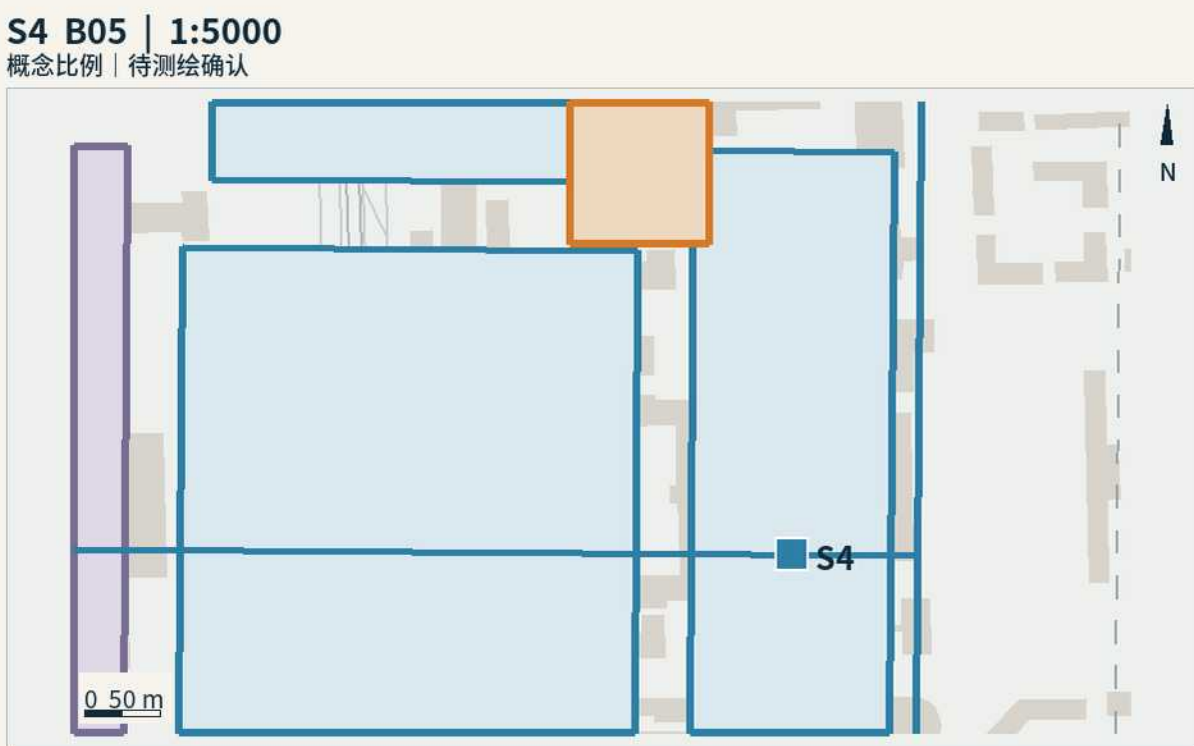

暂定边界 | 非官方红线，待测绘复核

发布由创作者决定

R02-03 | B05 | KA-AI-PUBLIC-EDGE

人物/地点 学生创作者与协作者/AI原点私域—共享—发布阈值


空间动作 可关闭工作间接授权台，展廊只放获准内容

运营 创作空间/权利复核类（待确认）

非AI 纸质授权、真人复核与人工下架

成功待验 逐项许可、署名与回执可核对

停止 撤回、权属不明或旁观者未同意即发布

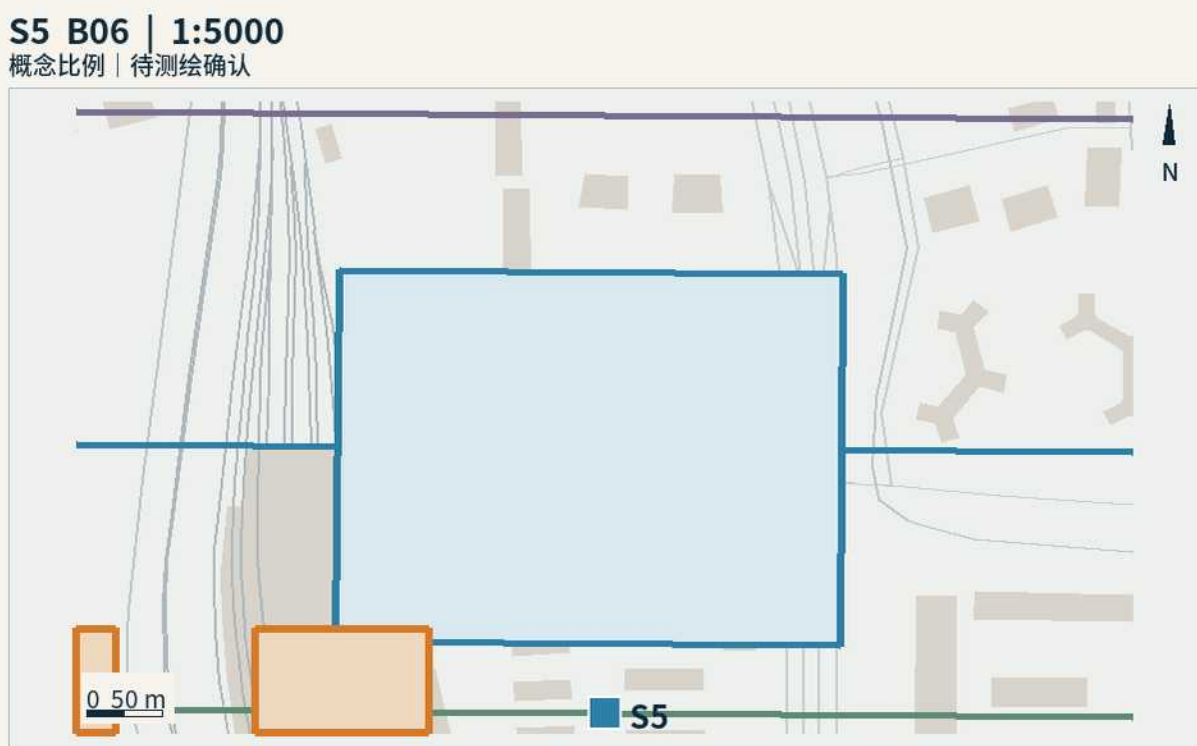

| 概念动作；虚线非官方红线

安静通行不让位

R02-02 | B06 | KA-DZ-QUIET-ROUTE

人物/地点 轮椅使用者、老人和照护者/大钟寺暂定区安静路线


空间动作 净宽不断，车架与装卸移到路线外

运营 公共地面/后勤协调类（待确认）

非AI 纸质导视、人工协助和绕行指引

成功待验 由使用者实走验收，不用半径替代可达

停止 堵塞、碰撞风险或噪声冲突就停活动

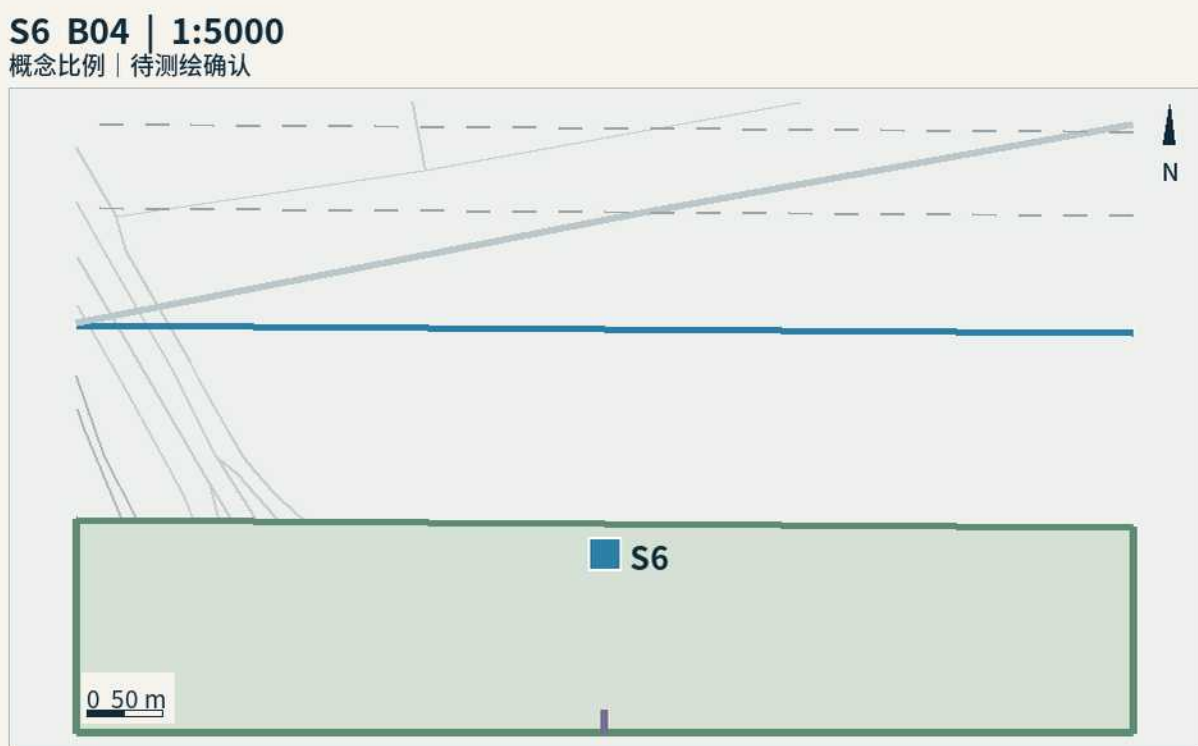

暂定边界 | 非官方红线，待测绘复核

河岸反馈进入维护

R02-05 | B04 | KA-ZZ-QINGHE-BUFFER

人物/地点 散步居民与养护巡查员/清河—众智园生态缓冲带

空间动作 留可滩绿地、采样接口与安全绕行

运营 水务生态养护类（待确认）

非AI 电话报告、纸面巡查、专业采样

成功待验 核对报告、采样和维护反馈闭台

停止 预警或专业阈值触发则分段人工接管

02 项目—责任—实施矩阵 | 主体与审批待确认；资金仅为筹措选项，无已批预算

项目/分期	主体类别 · 待确认	审批/核验事项	资金选项 · 未承诺	运维与非AI路径	成功/停止判断 · 待试点
E R02-01 保留型公共青	公共空间/遗产协同类	通行权与遗产复核	公共维护资金选项	人工巡查；公共通行不断	实走连续；阻断即改线
E R02-02 大钟寺公共首层	站城接口/在地运营类	正式边界、交通与消防	业主改造+公共服务选项	安静通行；装卸限时	无账号可用；冲突即停
M R02-03 AI原点共享转化	校园/社区联络类	开放协议、隐私与消防	共建空间/小额试点选项	真人导师；纸面授权撤回	真实转介；无同意不发布
M R02-04 众智园受控验证	创新运营/安全专业类	试验边界、安全与环境	受控测试服务资金选项	有人值守；测试与公众分隔	闸门完备；失效实体急停
M R02-05 蓝绿公共地面	生态/公共工程协同类	水务、生态与岸线通行	生态养护资金选项	实测采样；预警时段绕行	公众反馈核验；超限即停
L R02-06 贯穿全程的复评退出	法定复核/资产确认类	每阶段复核；不默认启动	启动前确认恢复资金	证据复评；人工接管与恢复	恢复验收；无责任不启动

E/M/L 是条件性优先次序；PH-01—10 是五层依赖矩阵，不是施工时序。运营、绩效与阈值试点及专业确认。完整职责、指标定义和证据留在A3/机器文件。

03 0+13 精简校核

动作→单元→能力→项目（对应左表主体/指标）

A1 8/12 C5/7 01
A2 1/3 C5 01/02
A3 2/5/6/7/11 C1/2/3/4/6/7 02/03/04
A4 4 C8 05
A5 1/7 C5/6 02
A6 0/9/10/13 C8 06

A 表达与授权；B 公共连接；C 公共连接；L 保留法定决定。全部运营主体仅为候选类别。