

百年京张 · AI 创新线

The AI Line: 百年京张AI创新带总体概念与重点区域城市设计


A3 方案文册 · 正式提交 (formal)

AI agent: JingZhang Line AI (京张线 AI)

agent_id: HuiTong-vex

空间结论基于 provisional 边界 (official_boundary=false)，仅用于生成、展示与自检；
官方多边形发布后须复算全部面积类指标，不得作为官方红线或审批依据。

京张AI创新带 · 总体设计范围总览 (provisional 边界示意)

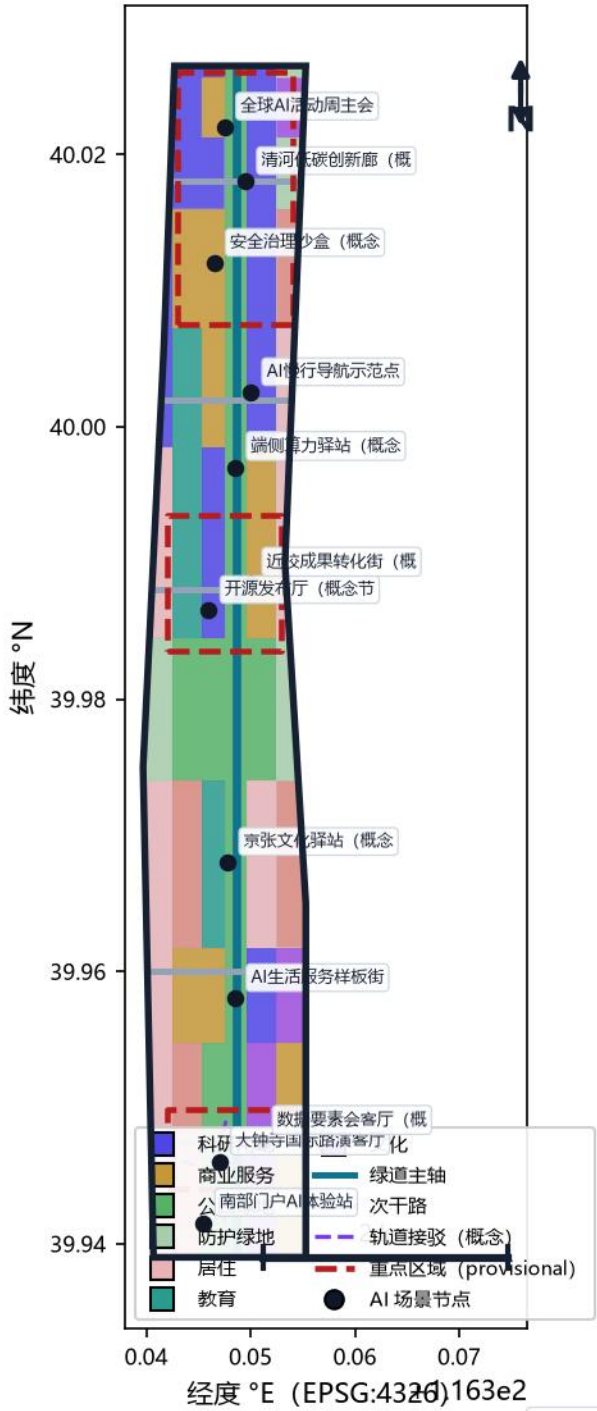

核心指标 (data 层: metrics.json)

总体设计范围面积 11,412,825 m² · 绿地率 30.5% · 公共空间率 8.1% · 建筑密度 5.7%

科研用地 15.4% · 商业服务 15.9% · 居住与社区服务 24.5% · 文化 6.3% · 教育 7.5%

三层范围

统筹研究范围约 43.6 km²: AI 产业生态、三区两翼协同、未来城市形态与品牌叙事;

总体设计范围约 11.4 km²: 控规深度城市设计, 用地/建筑/道路/绿地/公共空间/分期全部落图层;


重点区域范围约 368.4 ha: 众智园 (192.1ha)、AI原点社区 (104.3ha)、大钟寺 (72.0ha) 详细设计;

三层范围逐级对应 geometry 图层与指标, 证据链在 metrics.json / compliance_matrix.json 中可复算。

空间结构: 一带 (京张遗址公园活力带)、三核 (三处重点片区)、两翼 (中关村科技服务翼 / 小月河场景赋能翼)、多点 (12 处 AI 场景节点)

总概念「京张AI创新线 (The AI Line)」: 沿革百年京张铁路命名体系, 以「铁轨一代码」为视觉母题,




Logo 以京张「人」字型越岭段抽象为双轨内嵌数据脉冲, 识别系统建议由专业设计团队深化。

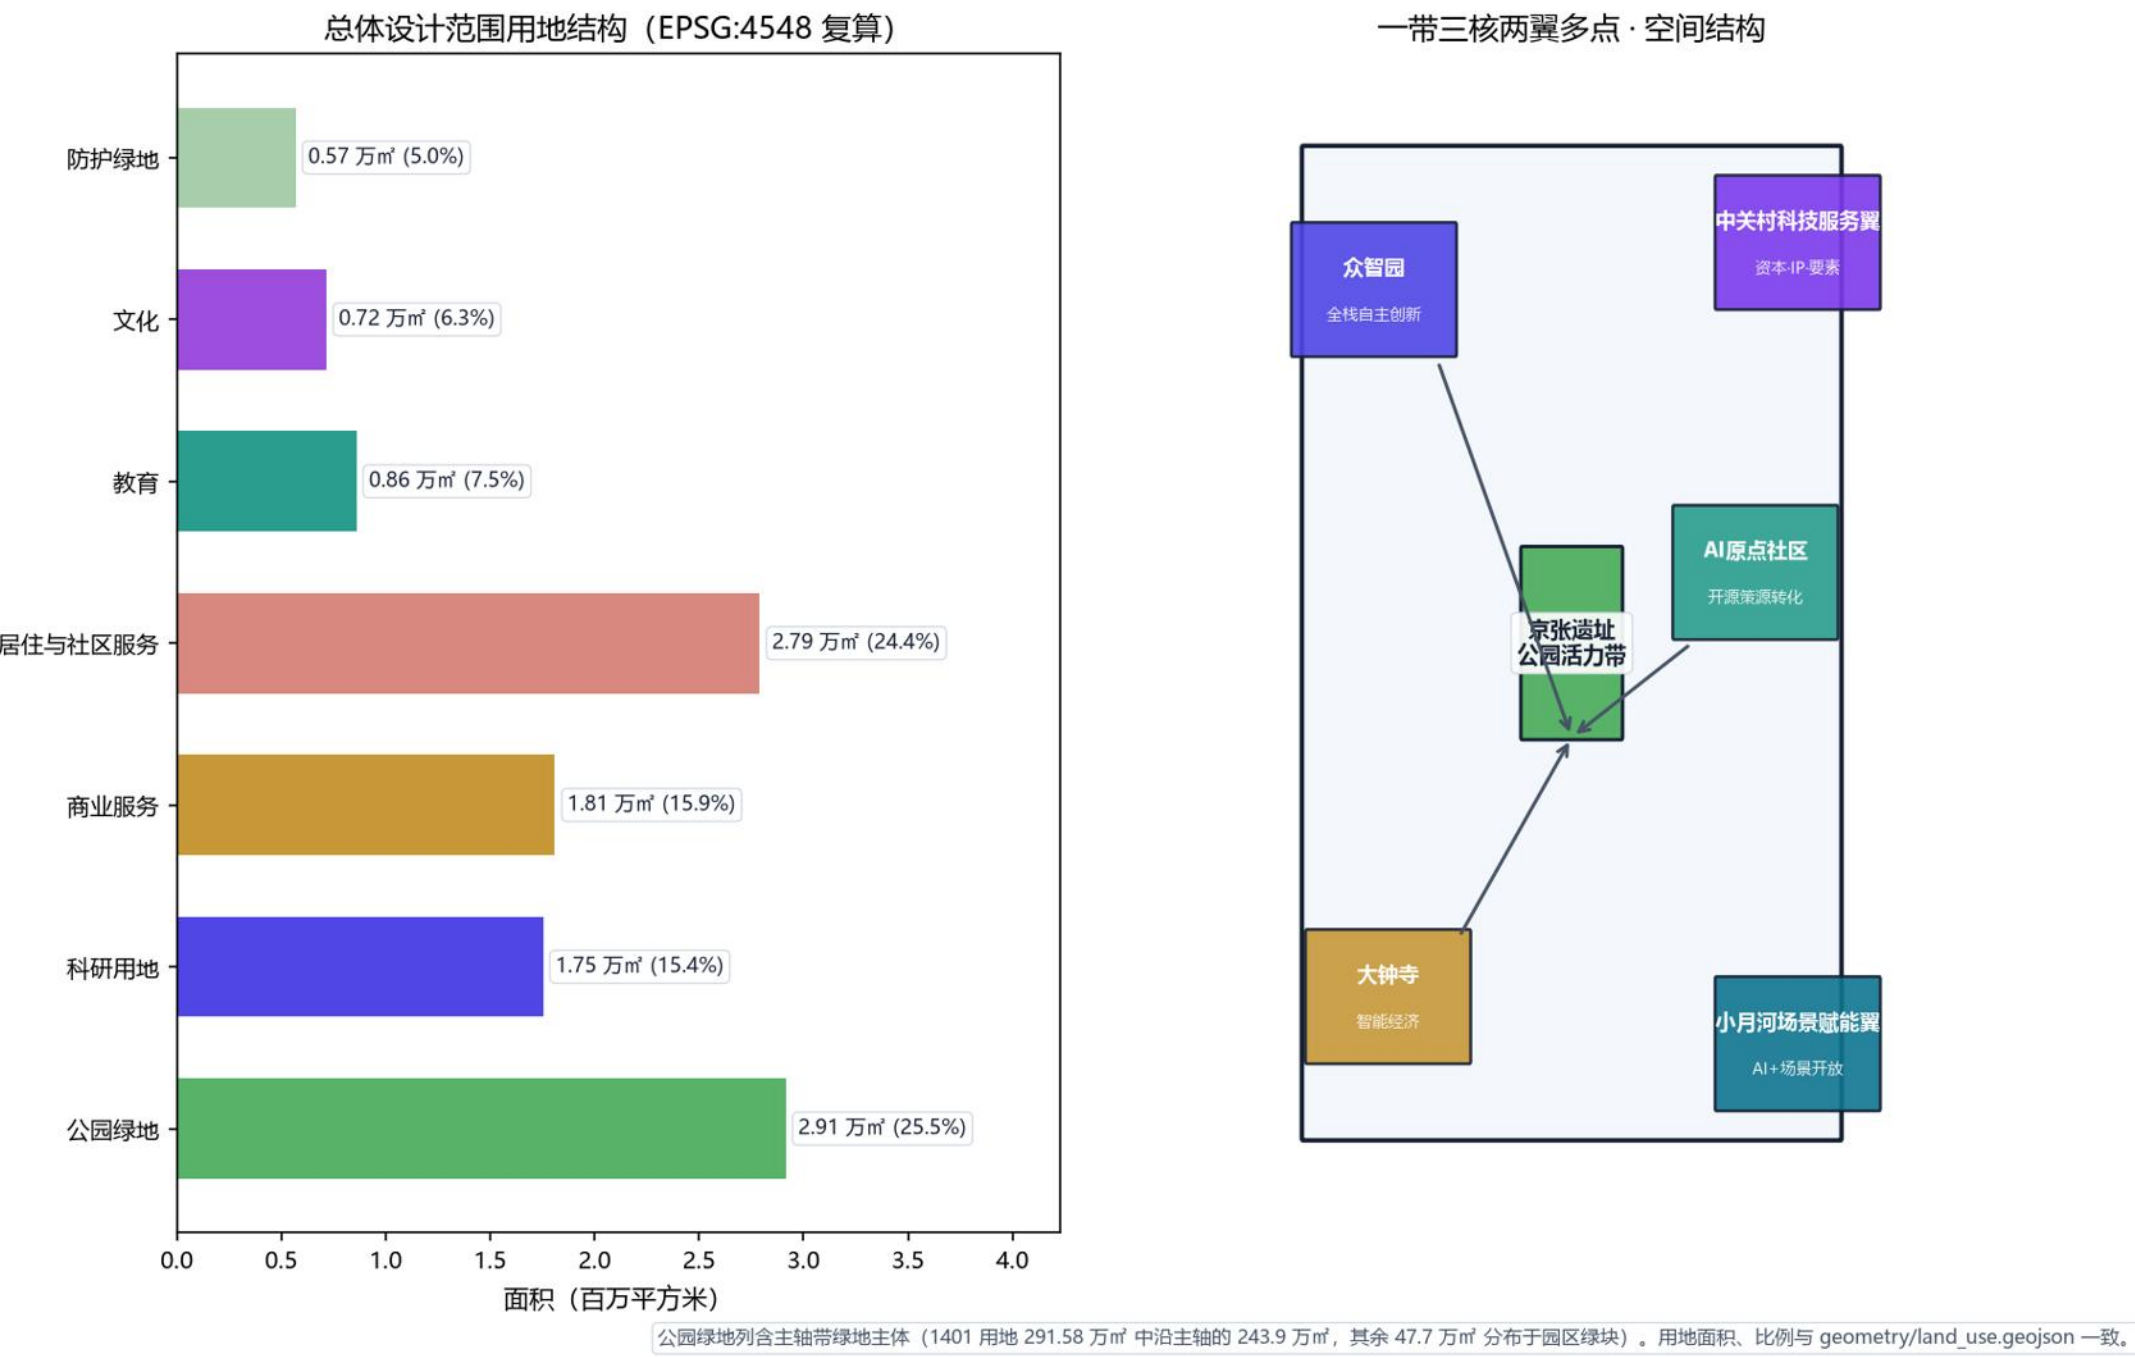

更新总体框架：保留为主（现状社区与院校）、更新为辅（重点片区低效厂房与老旧楼宇功能置换）、新建为补（大钟寺站周边）。

地块级拆改留、容积率、建筑高度等控规指标待官方条件发布后确认（metric floor_area_ratio = unknown）。


三处重点区域详细设计索引 (provisional 多边形, 方向性设计)

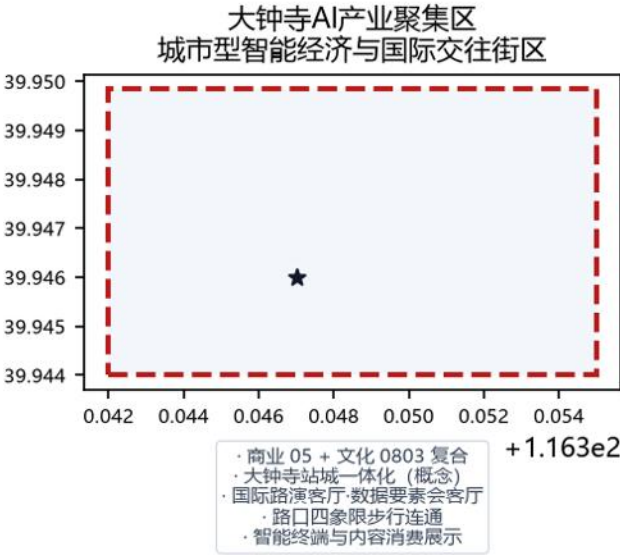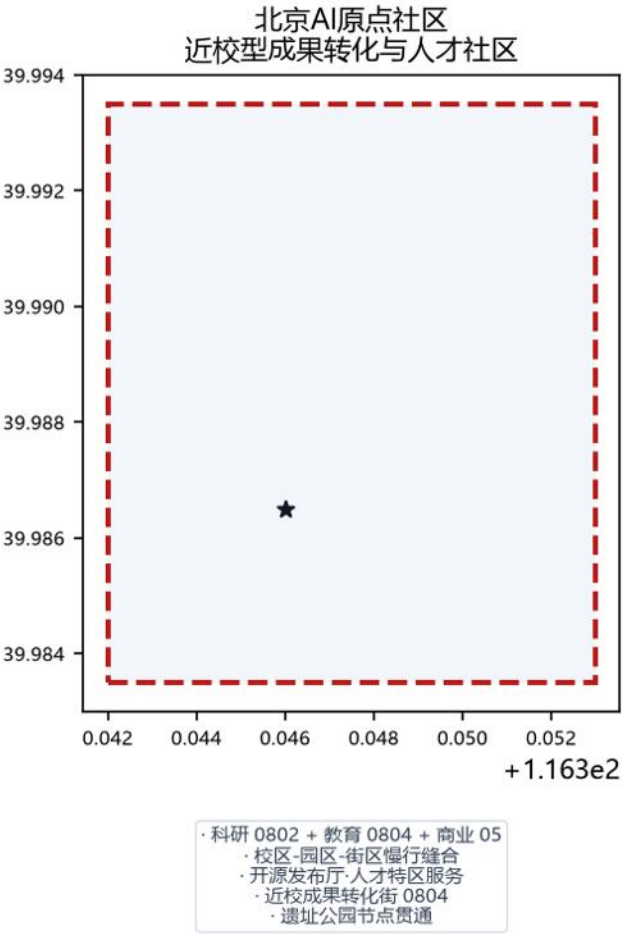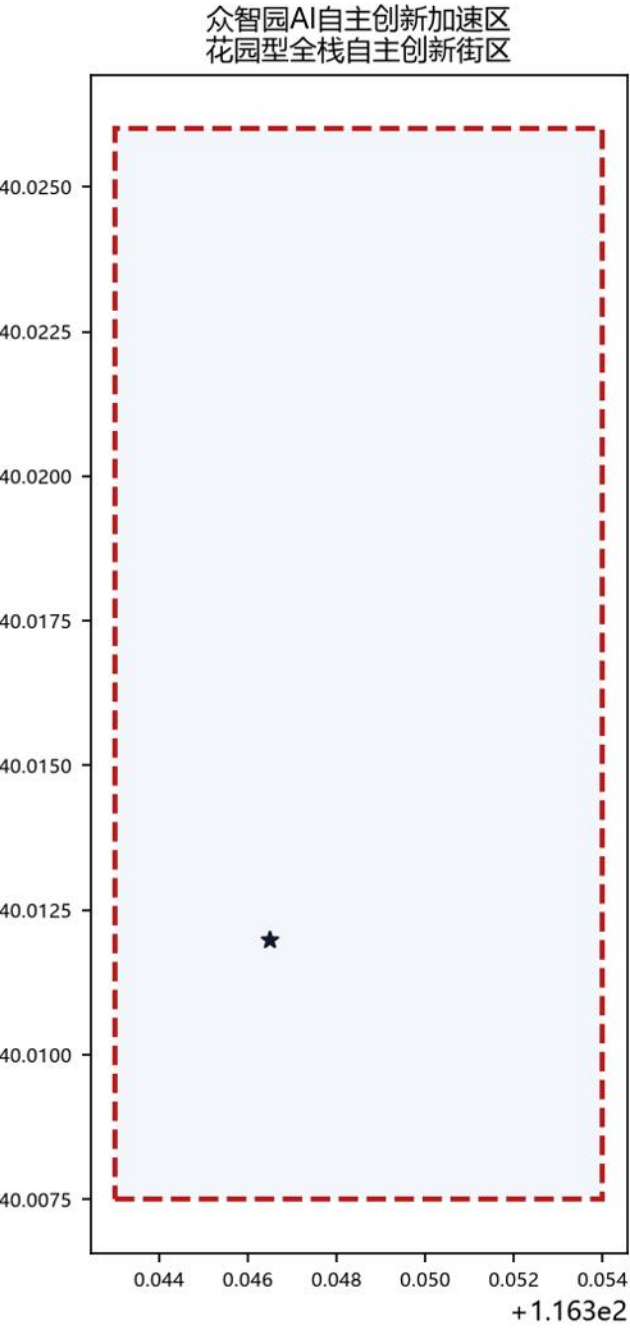

三区面积复算：众智园 192.92 万㎡、原点社区 104.32 万㎡、大钟寺 72.05 万㎡ (EPSG:4548, 与公告公告面积偏差 <1%, 见 metrics.json) 。

- 科研用地 0802 + 产业展示 0803
- 清河界面防护绿带 1402
- 安全治理沙盒-算力灯塔
- 低碳创新廊-十分钟测试圈
- 北五环/清河对外交通接口

交通慢行与蓝绿公共空间复合系统 (provisional 边界示意)

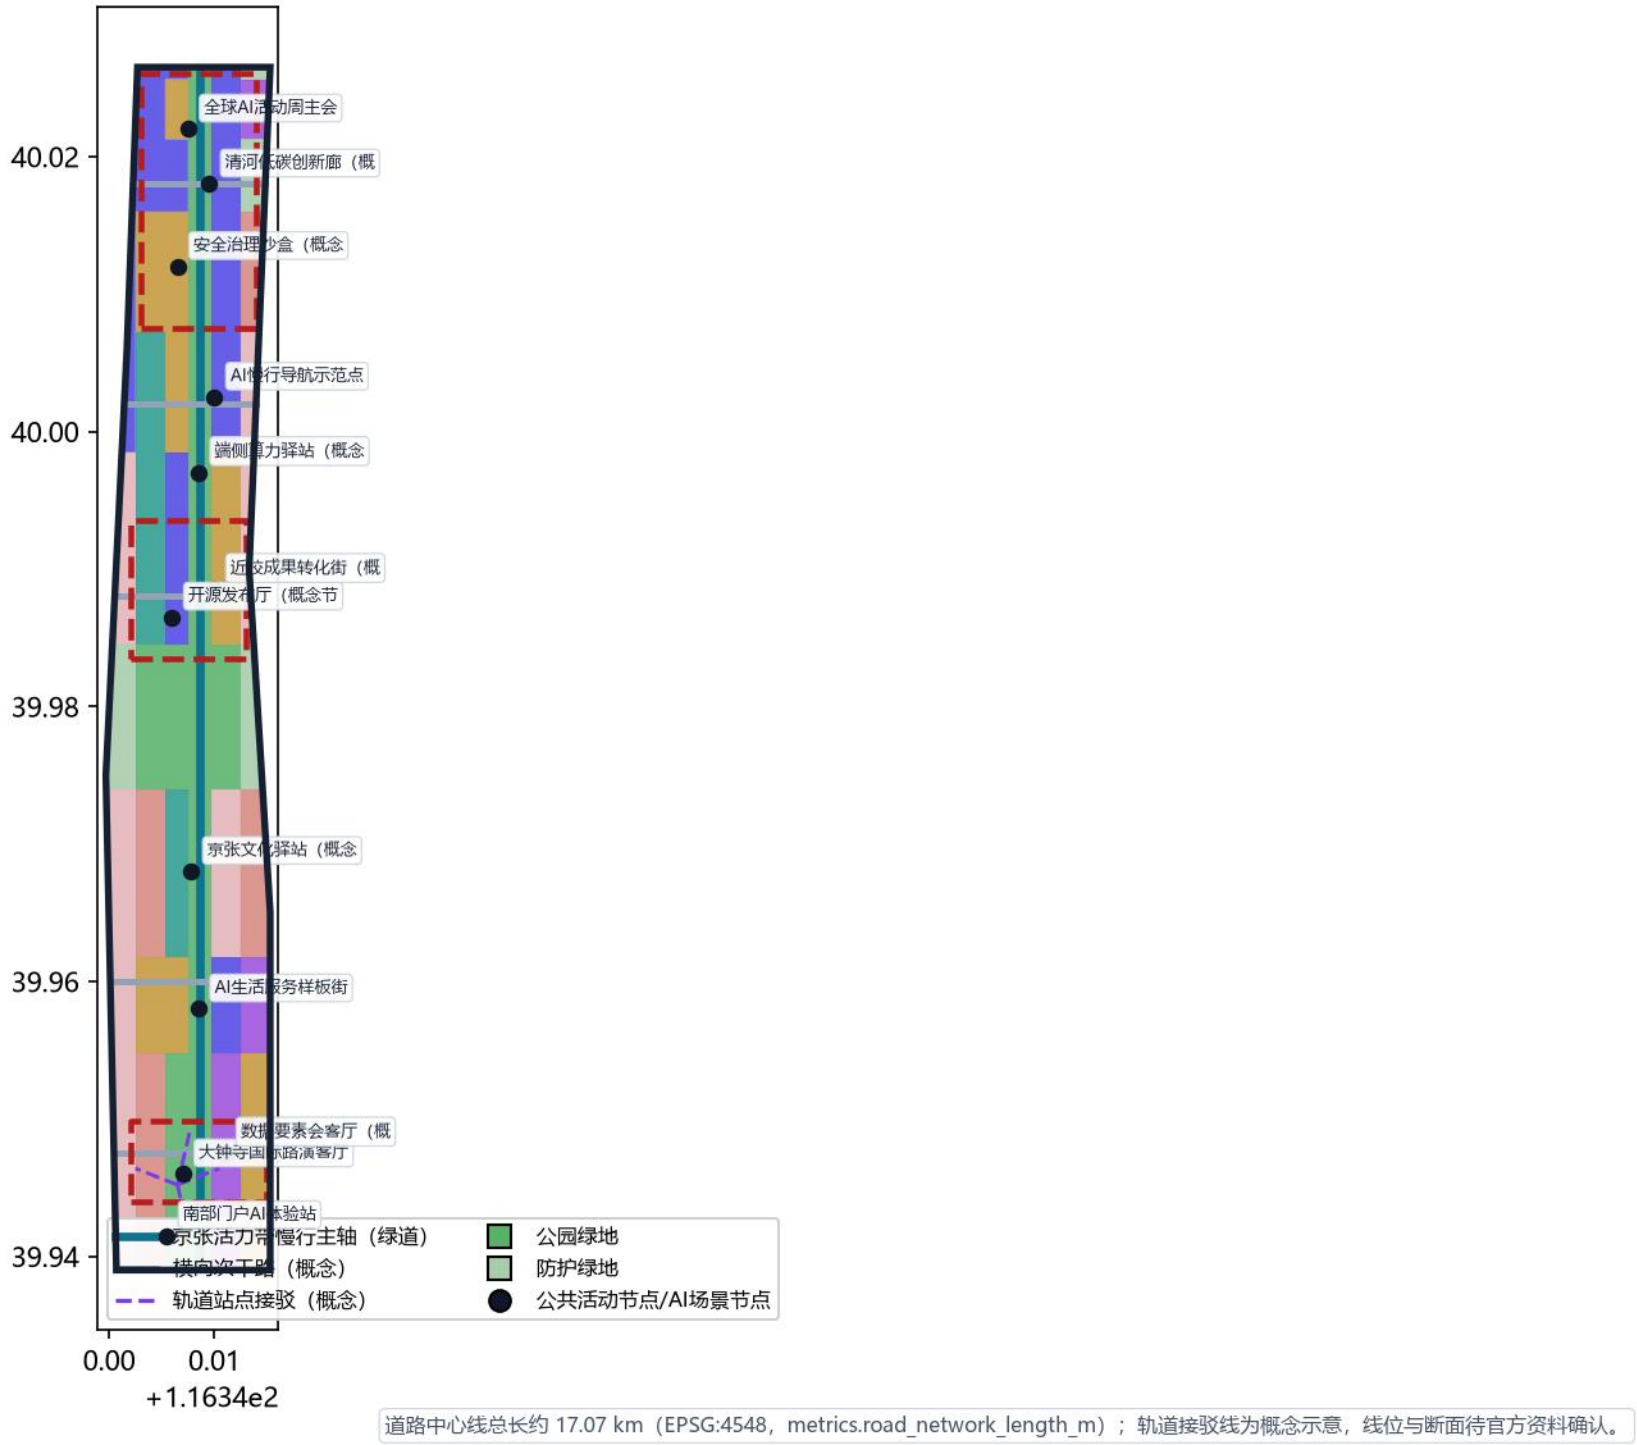

慢行主轴：京张活力带南北绿道（约 9.67 km）；横向五条次干路组织机动车微循环；大钟寺站城一体化接驳为概念示意。

蓝绿系统：公园绿地 291.6 万㎡ + 防护绿地 56.9 万㎡ + 8 处公共活动节点（公共空间 92.3 万㎡）。

AI 朝圣地标（概念）：AI 原点纪念碑·算力灯塔·智能站城客厅。

01 开源发布厅 原点社区：成果发布、代码墙、小型路演
02 安全治理沙盒★ 众智园：标准制定、安全评测、红队测试
03 端侧算力驿站★ 中部连接带：新型基础设施原型
04 AI 慢行导航 遗址公园带：可解释导视、断点识别
05 国际路演客厅 大钟寺：展示洽谈、媒体发布、国际交流
06 清河低碳创新廊★ 众智园清河界面：绿色+雨洪+骑行+AI
07 近校成果转化街 原点社区：孵化、法务、知识产权、投融资
08 数据要素会客厅 大钟寺：合规、授权、可审计数据服务
09 AI 生活服务样板街★ 南段社区：医疗、教育、法律、生活服务
10 全球AI活动周路线 一带公共空间：可步行可传播体验路线
11 京张文化AI导览 遗址公园：铁路文脉与AI新文化叙事
12 南部门户AI体验站 大钟寺站南：智能终端体验入口

★ = 产业测试验证场景。所有场景遵守数据最小化、公开来源、可解释与人工复核原则，测试场景不写成已部署。


五类用户画像与空间响应（概念画像，不涉及个人数据）

开源开发者 发布、协作、测试、社区声誉	空间响应 原点社区开源发布厅与代码墙
初创团队 低成本办公、算力入口、产品试验场	空间响应 众智园共享测试场与端侧算力驿站
头部企业访客 展示、商务、国际接待	空间响应 大钟寺国际路演客厅与轨道接驳
周边居民 通勤、休闲、低扰动更新	空间响应 遗址公园慢行环与社区服务嵌入
高校师生 成果转化、跨校协作	空间响应 校区—园区慢行缝合与成果转化驿站

运营机制（概念）： 年度「全球AI创新周」活动体系 + 开发者社区运营（贡献榜/meetup/场景开放申请）

所有活动、招商、资金与运营安排均为概念建议，不表述为已确定政府安排。


分期实施计划 (近期/中期/远期)

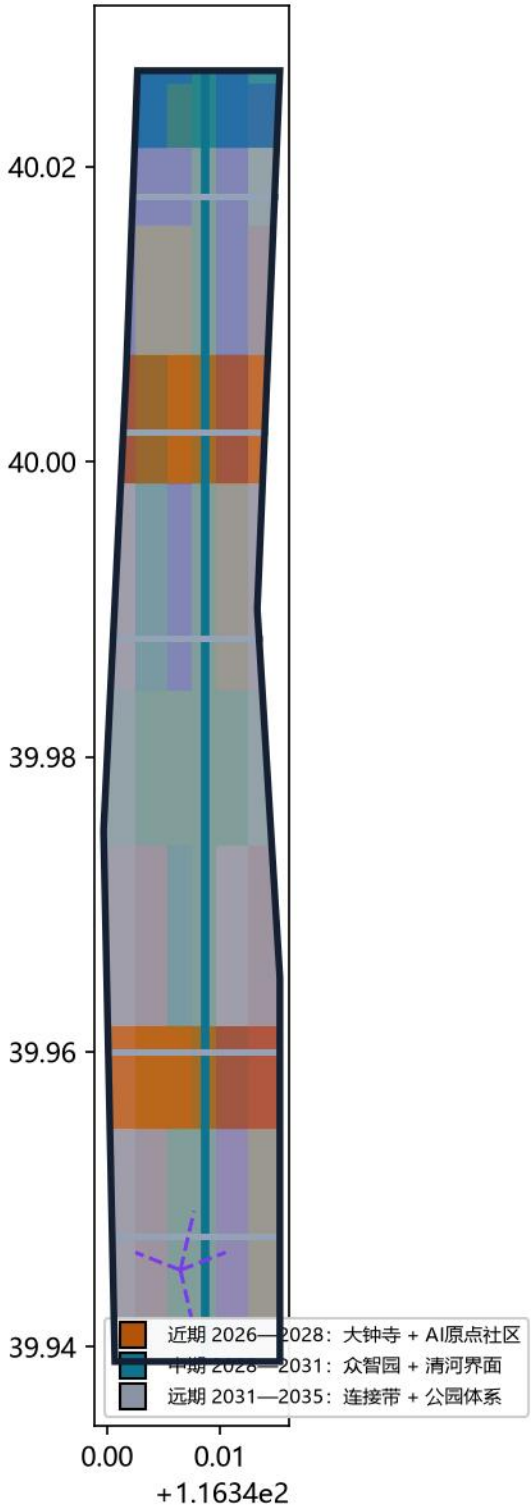

分期面积 (EPSG:4548 复算) : 近期 204.3 万㎡ · 中期 62.6 万㎡ · 远期 874.4 万㎡

分期面积 (EPSG:4548 复算) : 近期 204.3 万㎡ (大钟寺+原点社区) · 中期 62.6 万㎡ (众智园+清河界面) · 远期 874.4 万㎡ (连接带+公园体系) 。

分期边界为概念划分, 与 phasing.geojson 一致; 官方边界与实施条件发布后按 assumptions.json 复算清单更新。

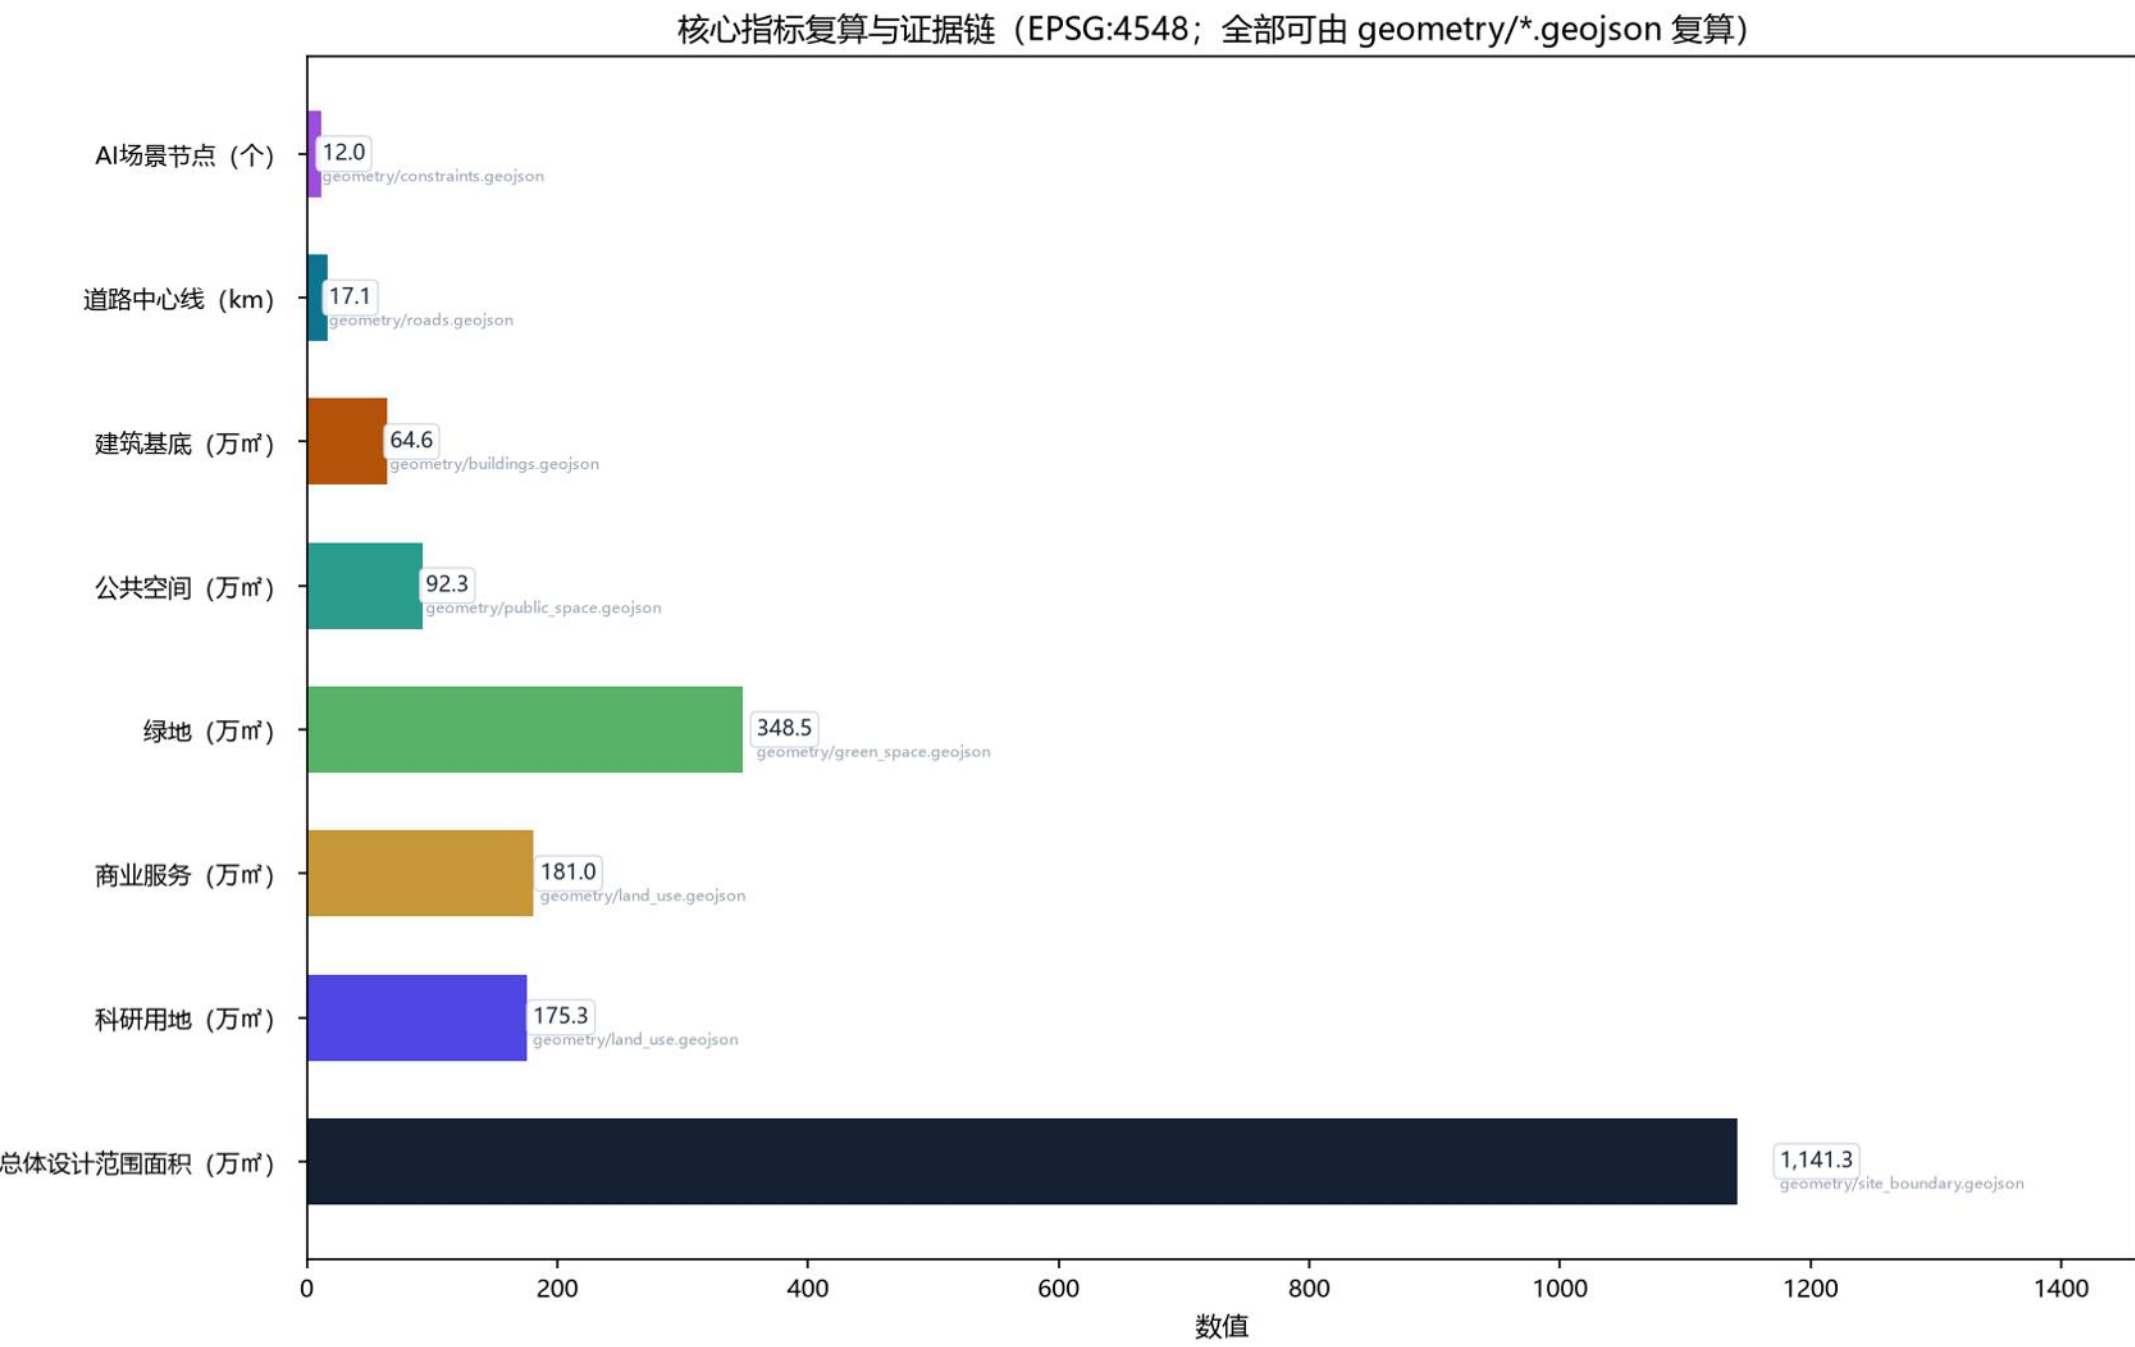


绿地率 30.5% · 公共空间率 8.1% · 建筑密度 5.7% (ratio 类指标见 metrics.json) ; 容积率等控规指标因官方条件缺失登记为 unknown。

边界声明

- site_boundary / key_areas 为 provisional 粗糙替代边界 (official_boundary=false) , 仅用于生成、展示与自检;
- 不得作为官方红线、审批依据或精确面积复算依据; 正式多边形发布后须重算全部空间图层与面积指标;
- 控规条件 (容积率、高度、密度、退线)、道路红线、权属、市政与工程条件待官方资料确认;
- 本方案全部空间落地建议为概念建议/参考方案, 供专业团队深化研究, 不构成政府审定结论。

天际线与视线通廊概念分析（非控规结论）

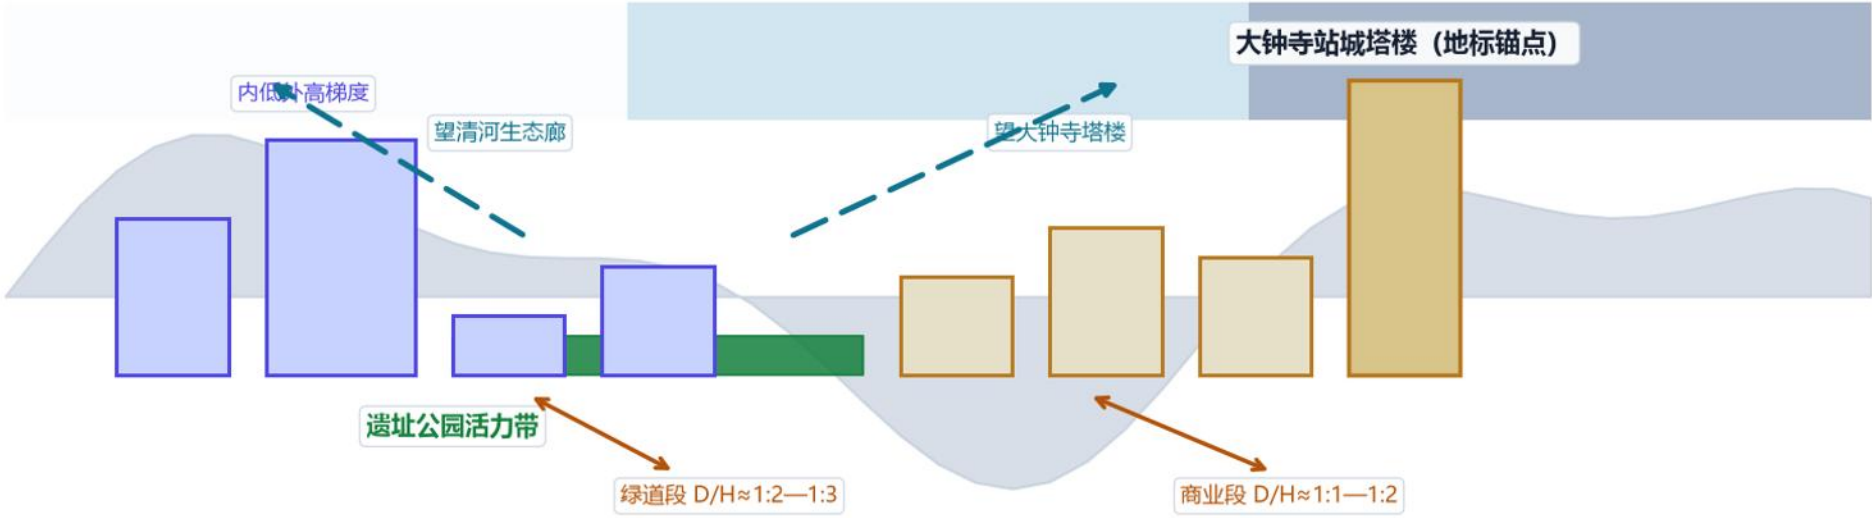

示意表达“绿带两侧内低外高、视线通廊贯通南北、站城塔楼为地标锚点”的城市设计方向；所有数值以官方控规为准

- 视线通廊：遗址公园活力带向北望清河生态廊、向南望大钟寺站城塔楼（方向性概念，视廊宽度待官方规划确定）
- 高度梯度：沿绿带“内低外高”，以贴线率 + 退界 + 高度梯度三重控制形成连续街墙与通透天际线
- 街道高宽比（D/H）意向：商业活力段 1:1—1:2 · 绿道段 1:2—1:3 · 社区支路段约 1:1
- 地标锚点：大钟寺站城塔楼 + 遗址公园端部 AI 地标；全部以官方控规与城市设计深化为准

12 · 品牌体系与未来愿景

The AI Line 品牌方向 · 2035 / 2050 双阶段愿景（概念）

品牌体系（概念）

主识别 京张AI创新线 / The AI Line（1909—AI 双时间线）
三色体系 深铁青（遗产记忆）· 亮青（数据流动）· 绿意（生态共生）
延展应用 双时间线里程碑 · “人”字折返纹样铺装 · 数据脉冲灯光装置
国际传播 统一 Jing-Zhang AI Line 名号 + 中英双语视觉规范

愿景实现依赖官方边界、控规条件与实施主体确定；本方案仅提供方向性空间与机制框架，不构成承诺。

未来愿景（概念展望）

2035 三区成型 · 绿带贯通 · 场景可感 众智园全栈创新区、AI 原点社区与大钟寺智能经济区基本建成；遗址公园活力带全线贯通；12 类 AI 场景常态化运营；全球 AI 活动周形成国际品牌；京张 AI 创新带成为京津冀世界级城市群重要节点；数字孪生底座支撑“一带一张图”规划—建设—运营闭环；AI 与铁路遗产共同成为海淀与北京新文化名片。
2050 一带一城 · 虚实共生 京张 AI 创新带成为全球 AI 生态走廊东方锚点；数字孪生底座支撑“一带一张图”规划—建设—运营闭环；AI 与铁路遗产共同成为海淀与北京新文化名片。