


展板A 总体策略与空间结构(京张智脉·一带三核双翼)

百年京张AI创新带城市设计开源征集 · formal 概念方案 · 机器证据: geometry/*.geojson + metrics.json


边界为 provisional 临时粗略范围,非官方红线,官方 polygon 发布后整体复算。

京张智脉——总体设计范围总览(一带三核·双翼协同)

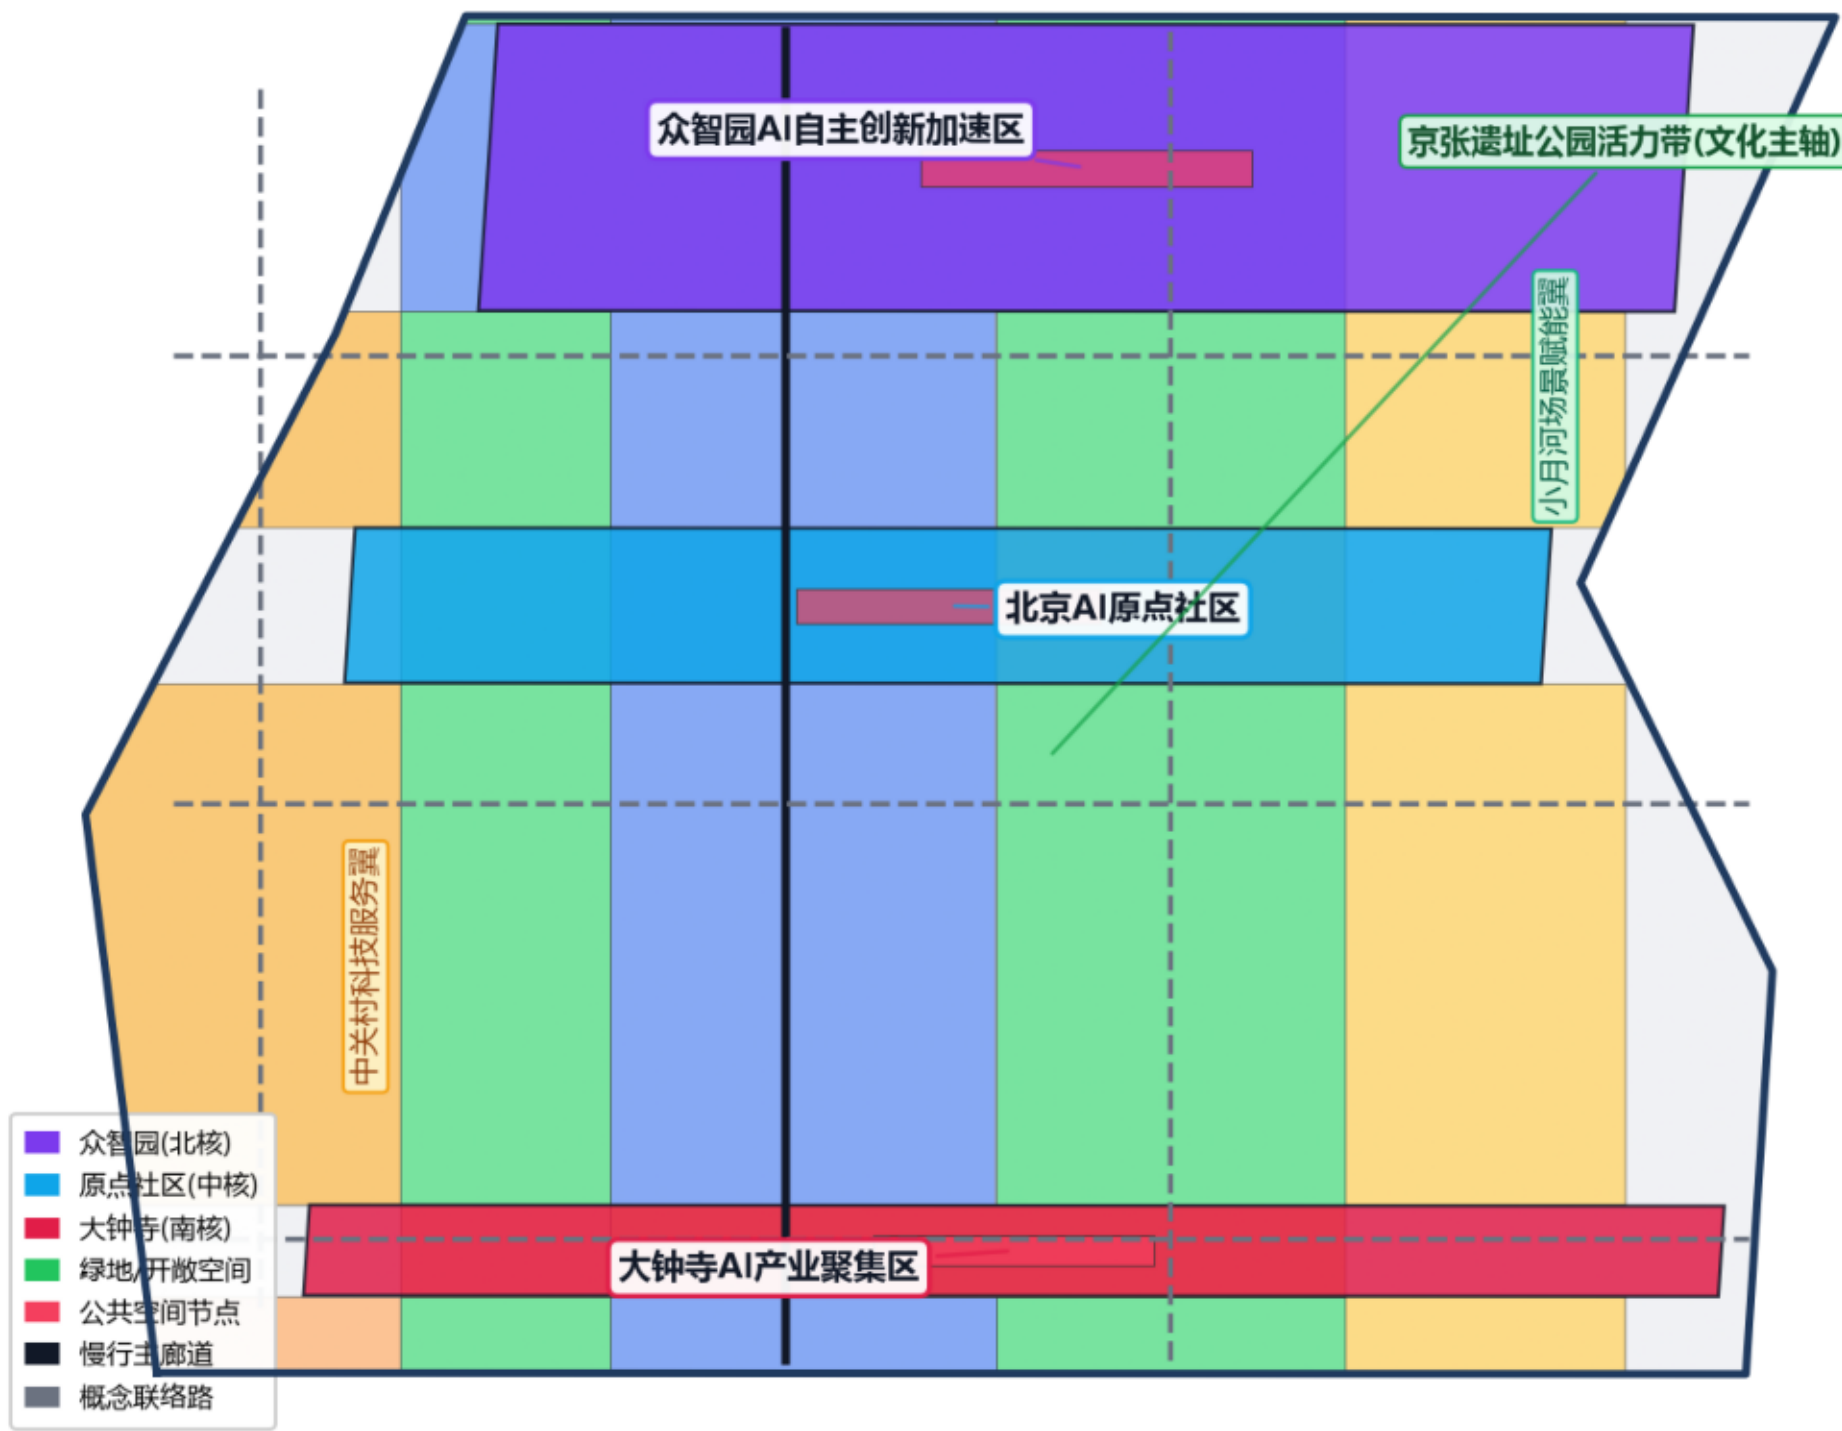


总体设计范围约11.4 km²(provisional边界),三处重点区合计约369.3 ha, boundaries.geojson + 本方案设计图层,边界为临时粗略范围,非官方红线

用地功能结构(26个地块,覆盖提交边界无缝无重叠)

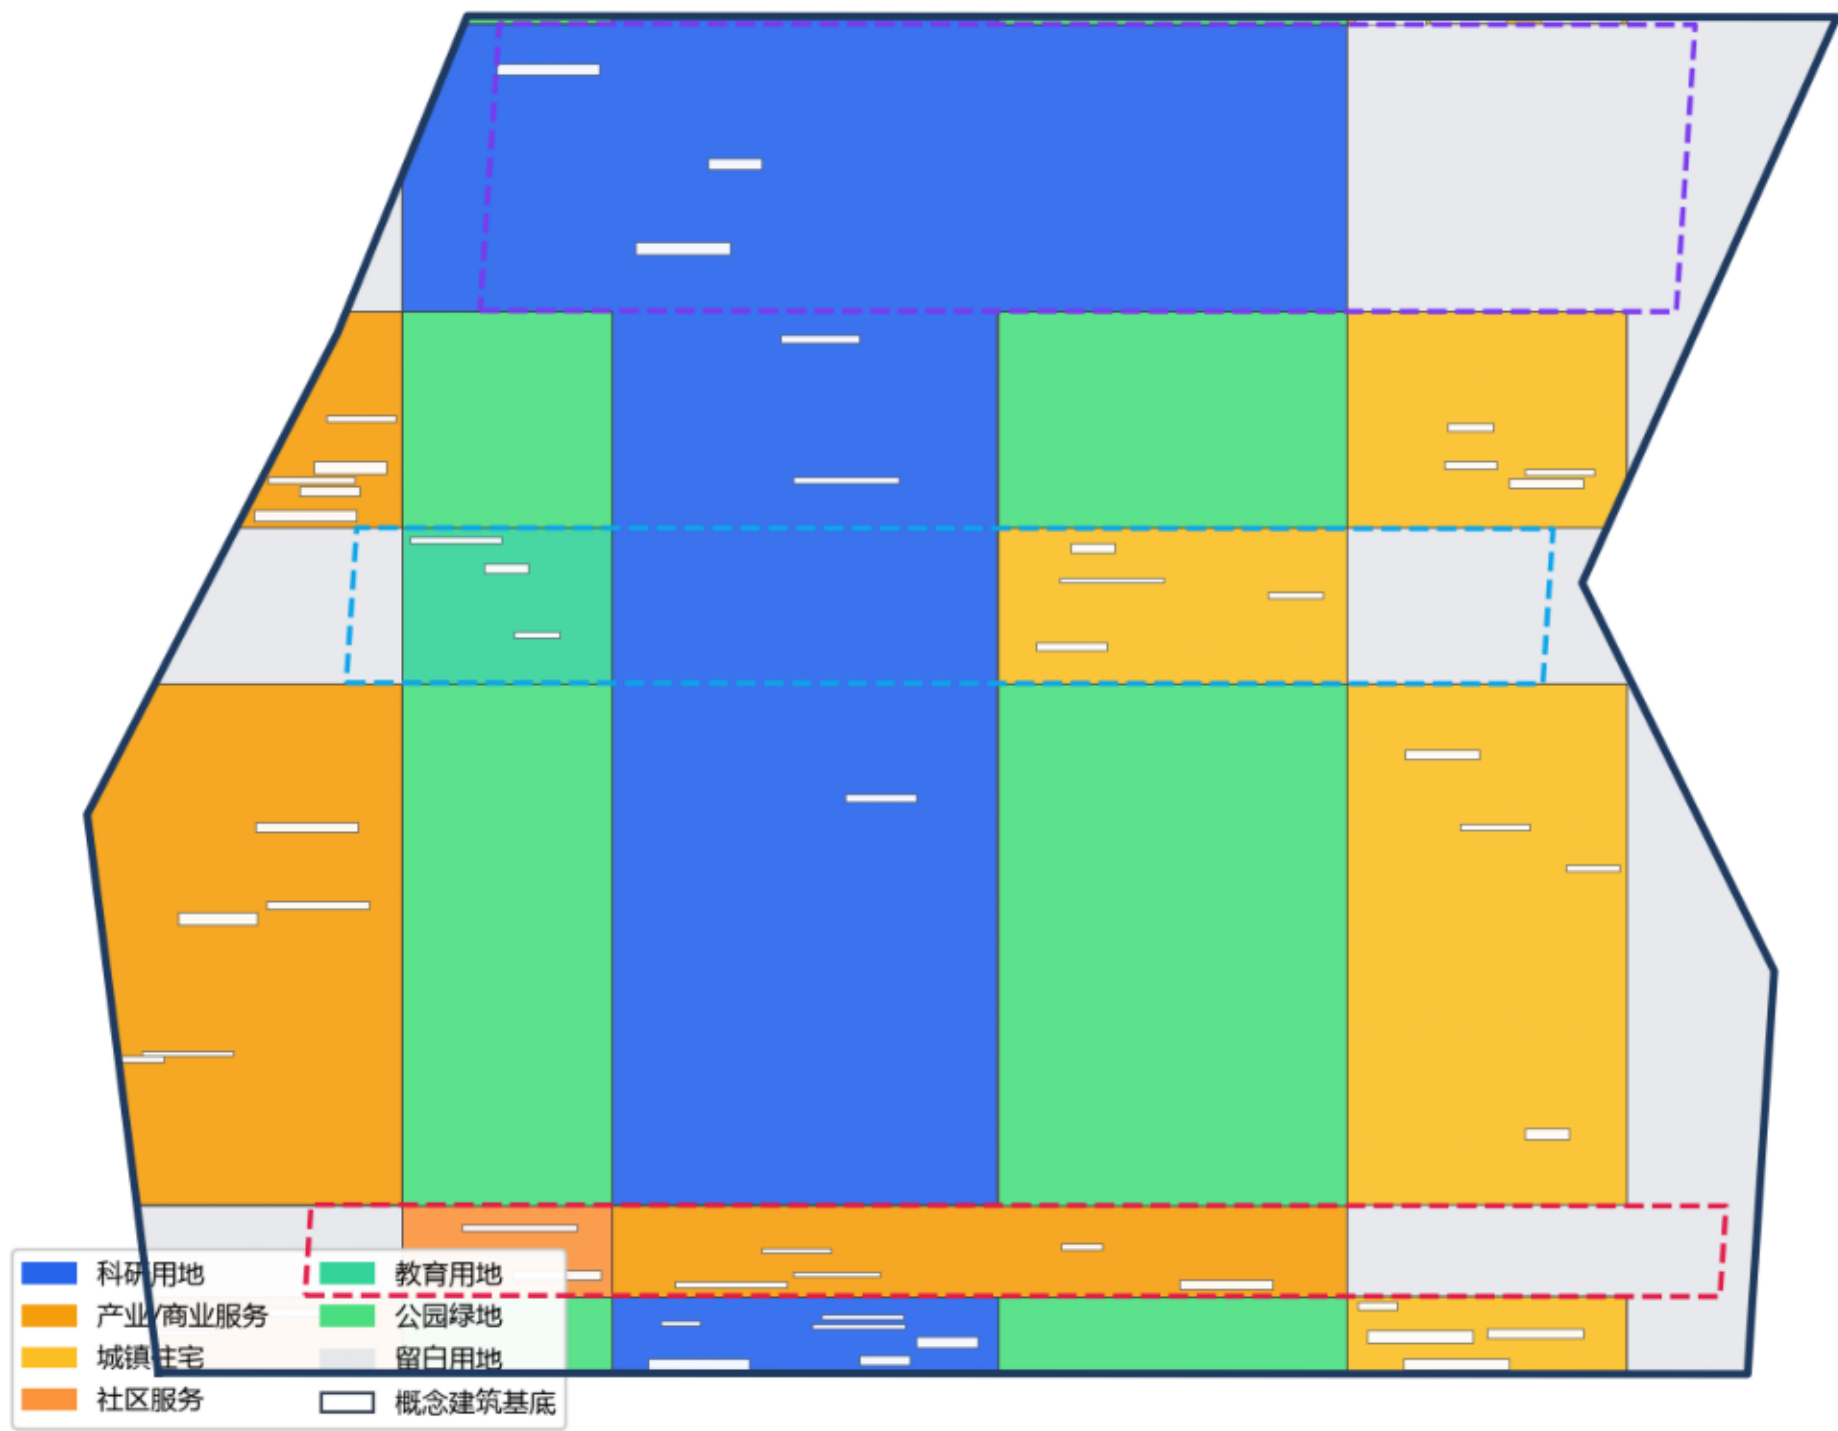


科研/产业服务沿三核与遗址公园带布局,居住与社区服务沿两翼,绿地形成蓝绿网络, land_use.geojson;分类依据《国土空间用地用海分类指南》;为概念分区非控规

三处重点区域详细设计索引(provisional边界,概念方案)

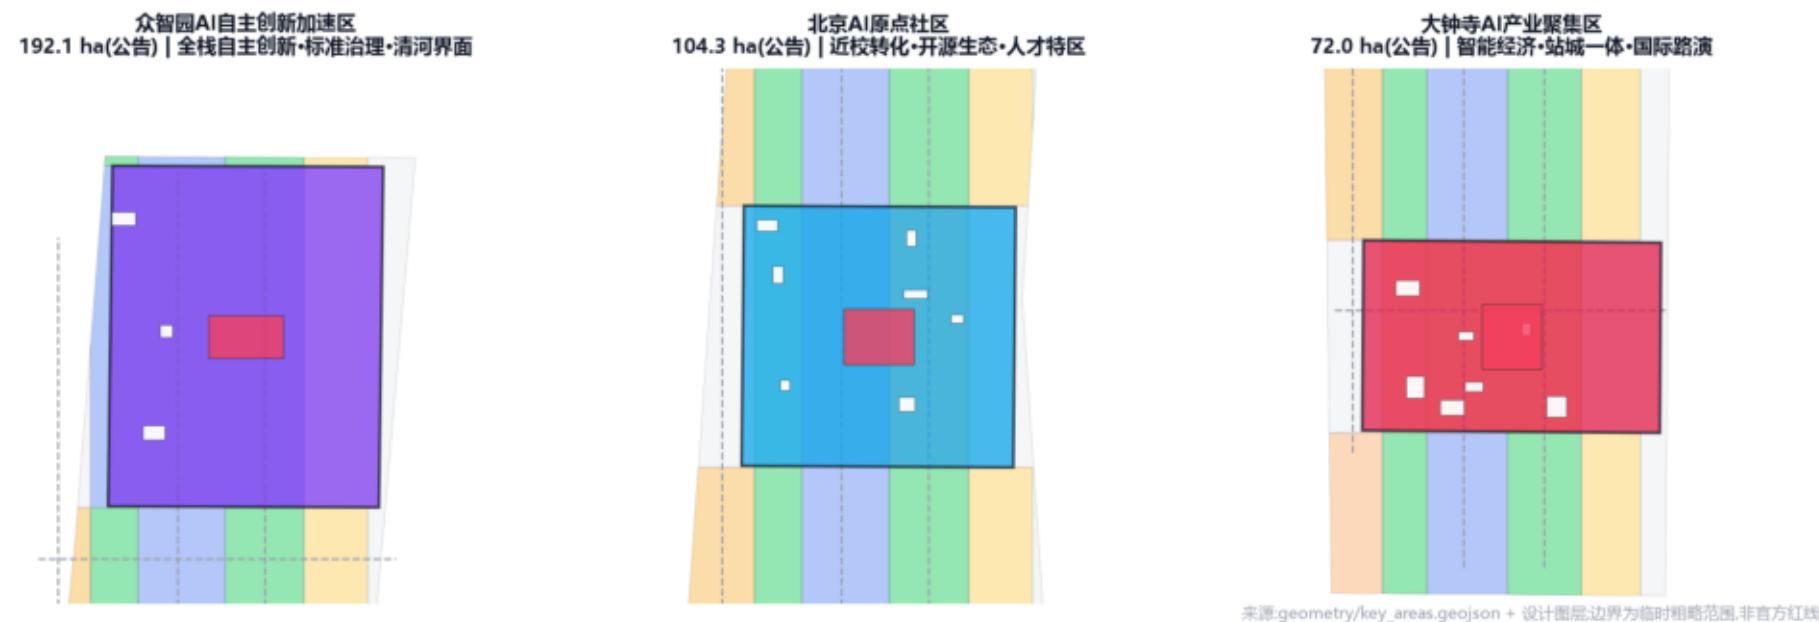

来源: geometry/key_areas.geojson + 设计图层边界为临时粗略范围,非官方红线



交通慢行与蓝绿公共空间复合系统

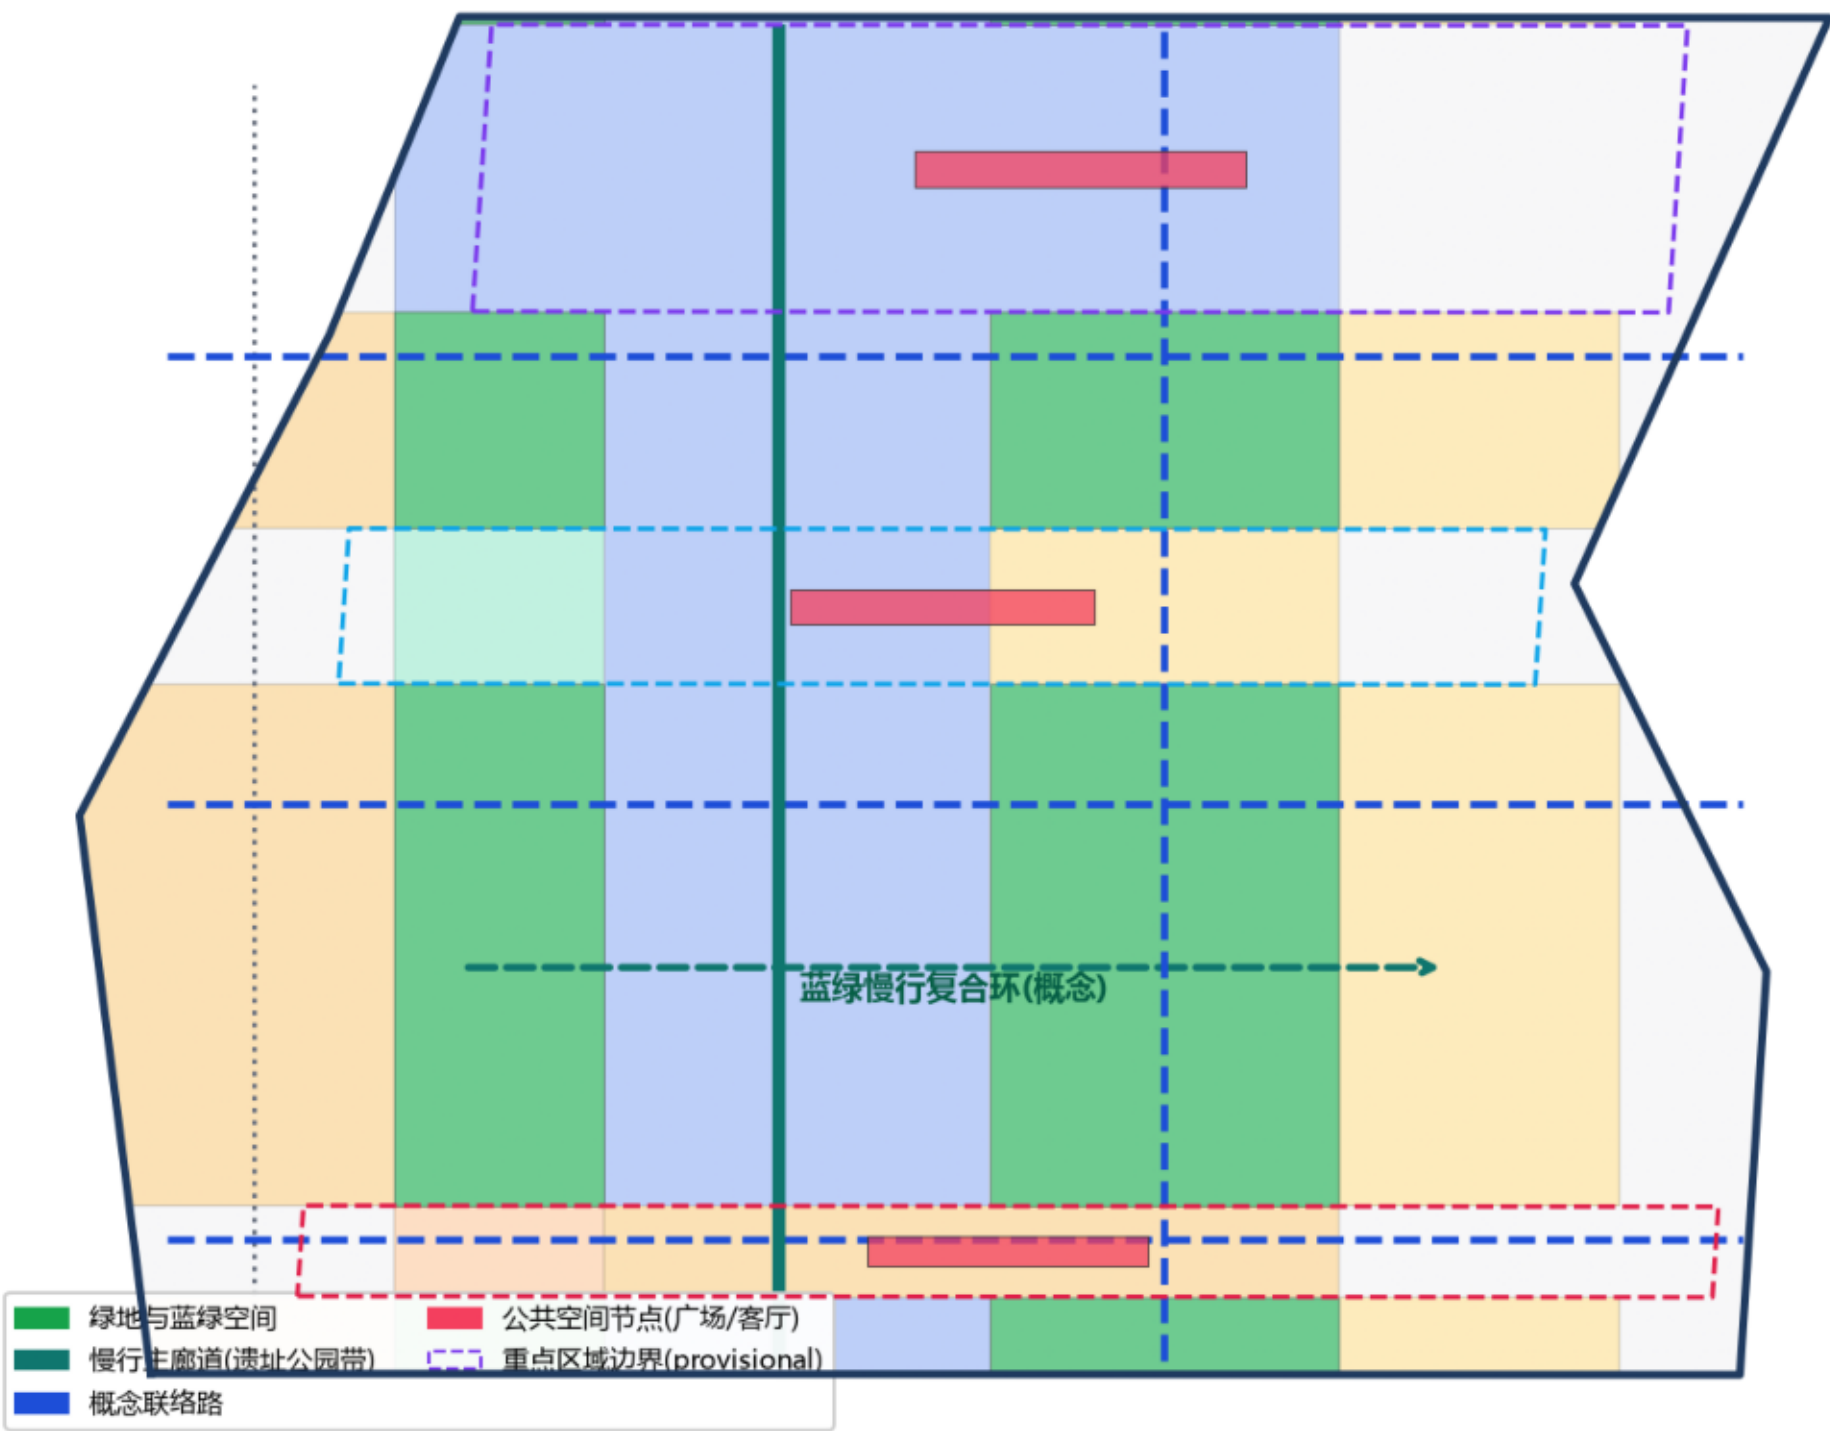

慢行主廊道串联三核,联络路缝合两翼;道路为概念,廊道非道路红线。oads.geojson + green_space.geojson + public_space.geojson;provisional边界

京张智脉 · JINGZHANG INTELLIGENCE SPINE

人字轨·智脉 | The Switchback & The Pulse

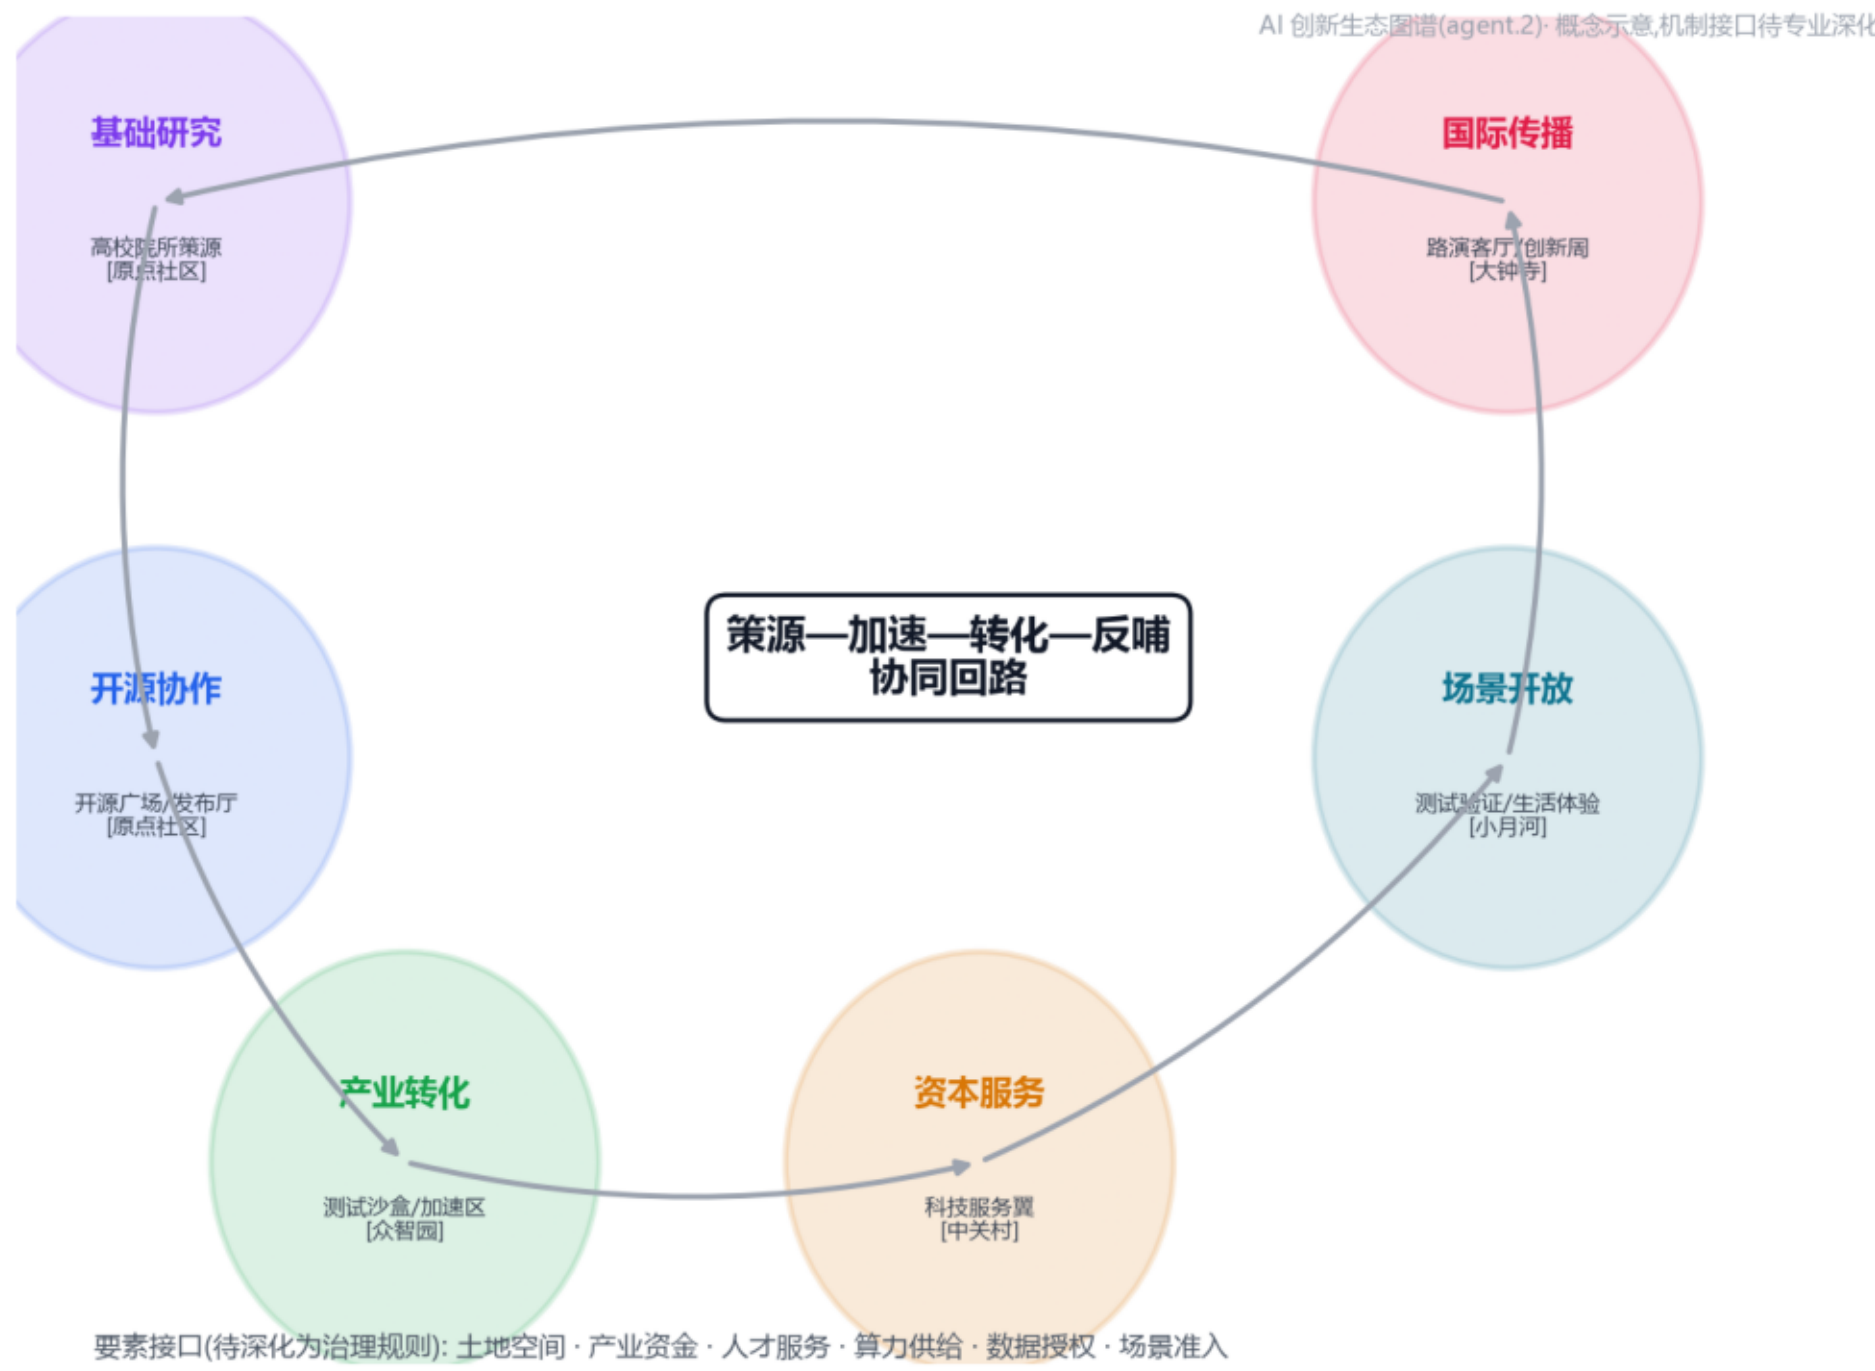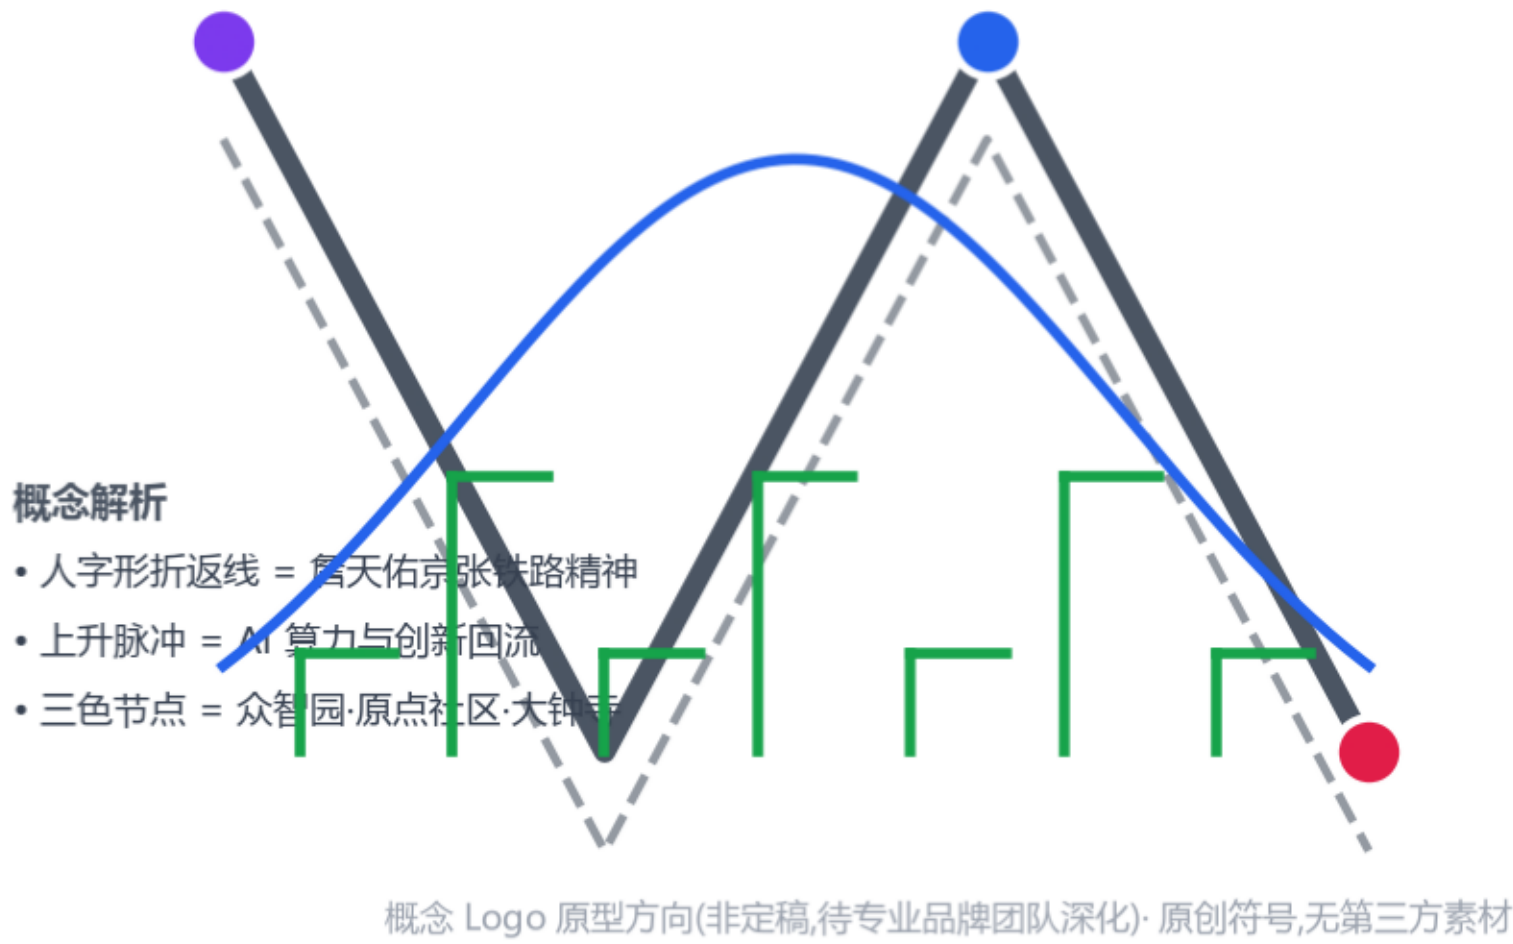

要素接口(待深化为治理规则): 土地空间 · 产业资金 · 人才服务 · 算力供给 · 数据授权 · 场景准入

百年京张AI创新带城市设计开源征集 · formal 概念方案 · 机器证据: geometry/*.geojson + metrics.json

边界为 provisional 临时粗略范围,非官方红线;官方 polygon 发布后整体复算。

Diagram illustrating various smart infrastructure components:

- 导航标识 (Navigation Signage):** 人字路 V 形微内标 (Human-shaped road V-shaped micro-internal mark)
- 智慧灯杆 (Smart Pole):** 传播·照明·显示 (Communication·Lighting·Display)
- 座椅单元 (Bench Unit):** 轨道式太阳能座椅 (Track-style solar bench)
- 数字屏 (Digital Screen):** 开源成果/活动信息 (Open source results/Activity information)
- 艺术装置 (Art Installation):** 脉冲感应地面 (Pulse-sensing ground)
- 地面铺装 (Ground Paving):** 钢轨采样引钢线 (Steel rail sampling guide wire)

组件均为原创概念线稿,不含第三方素材;规格与材质待专业深化

● 公共体验 ● 测试验证 ● 产业服务 ● 运营/品牌

场景均为概念建议不构成已批准运营,测试场景须按审批流程开放

