


京张智脊·总体概念与三层范围框架

一带一脊·三核联动·蓝绿慢行复合环 | 百年京张文化带 / 都市AI生活体验带 / AI融合创新带



三层范围工作框架

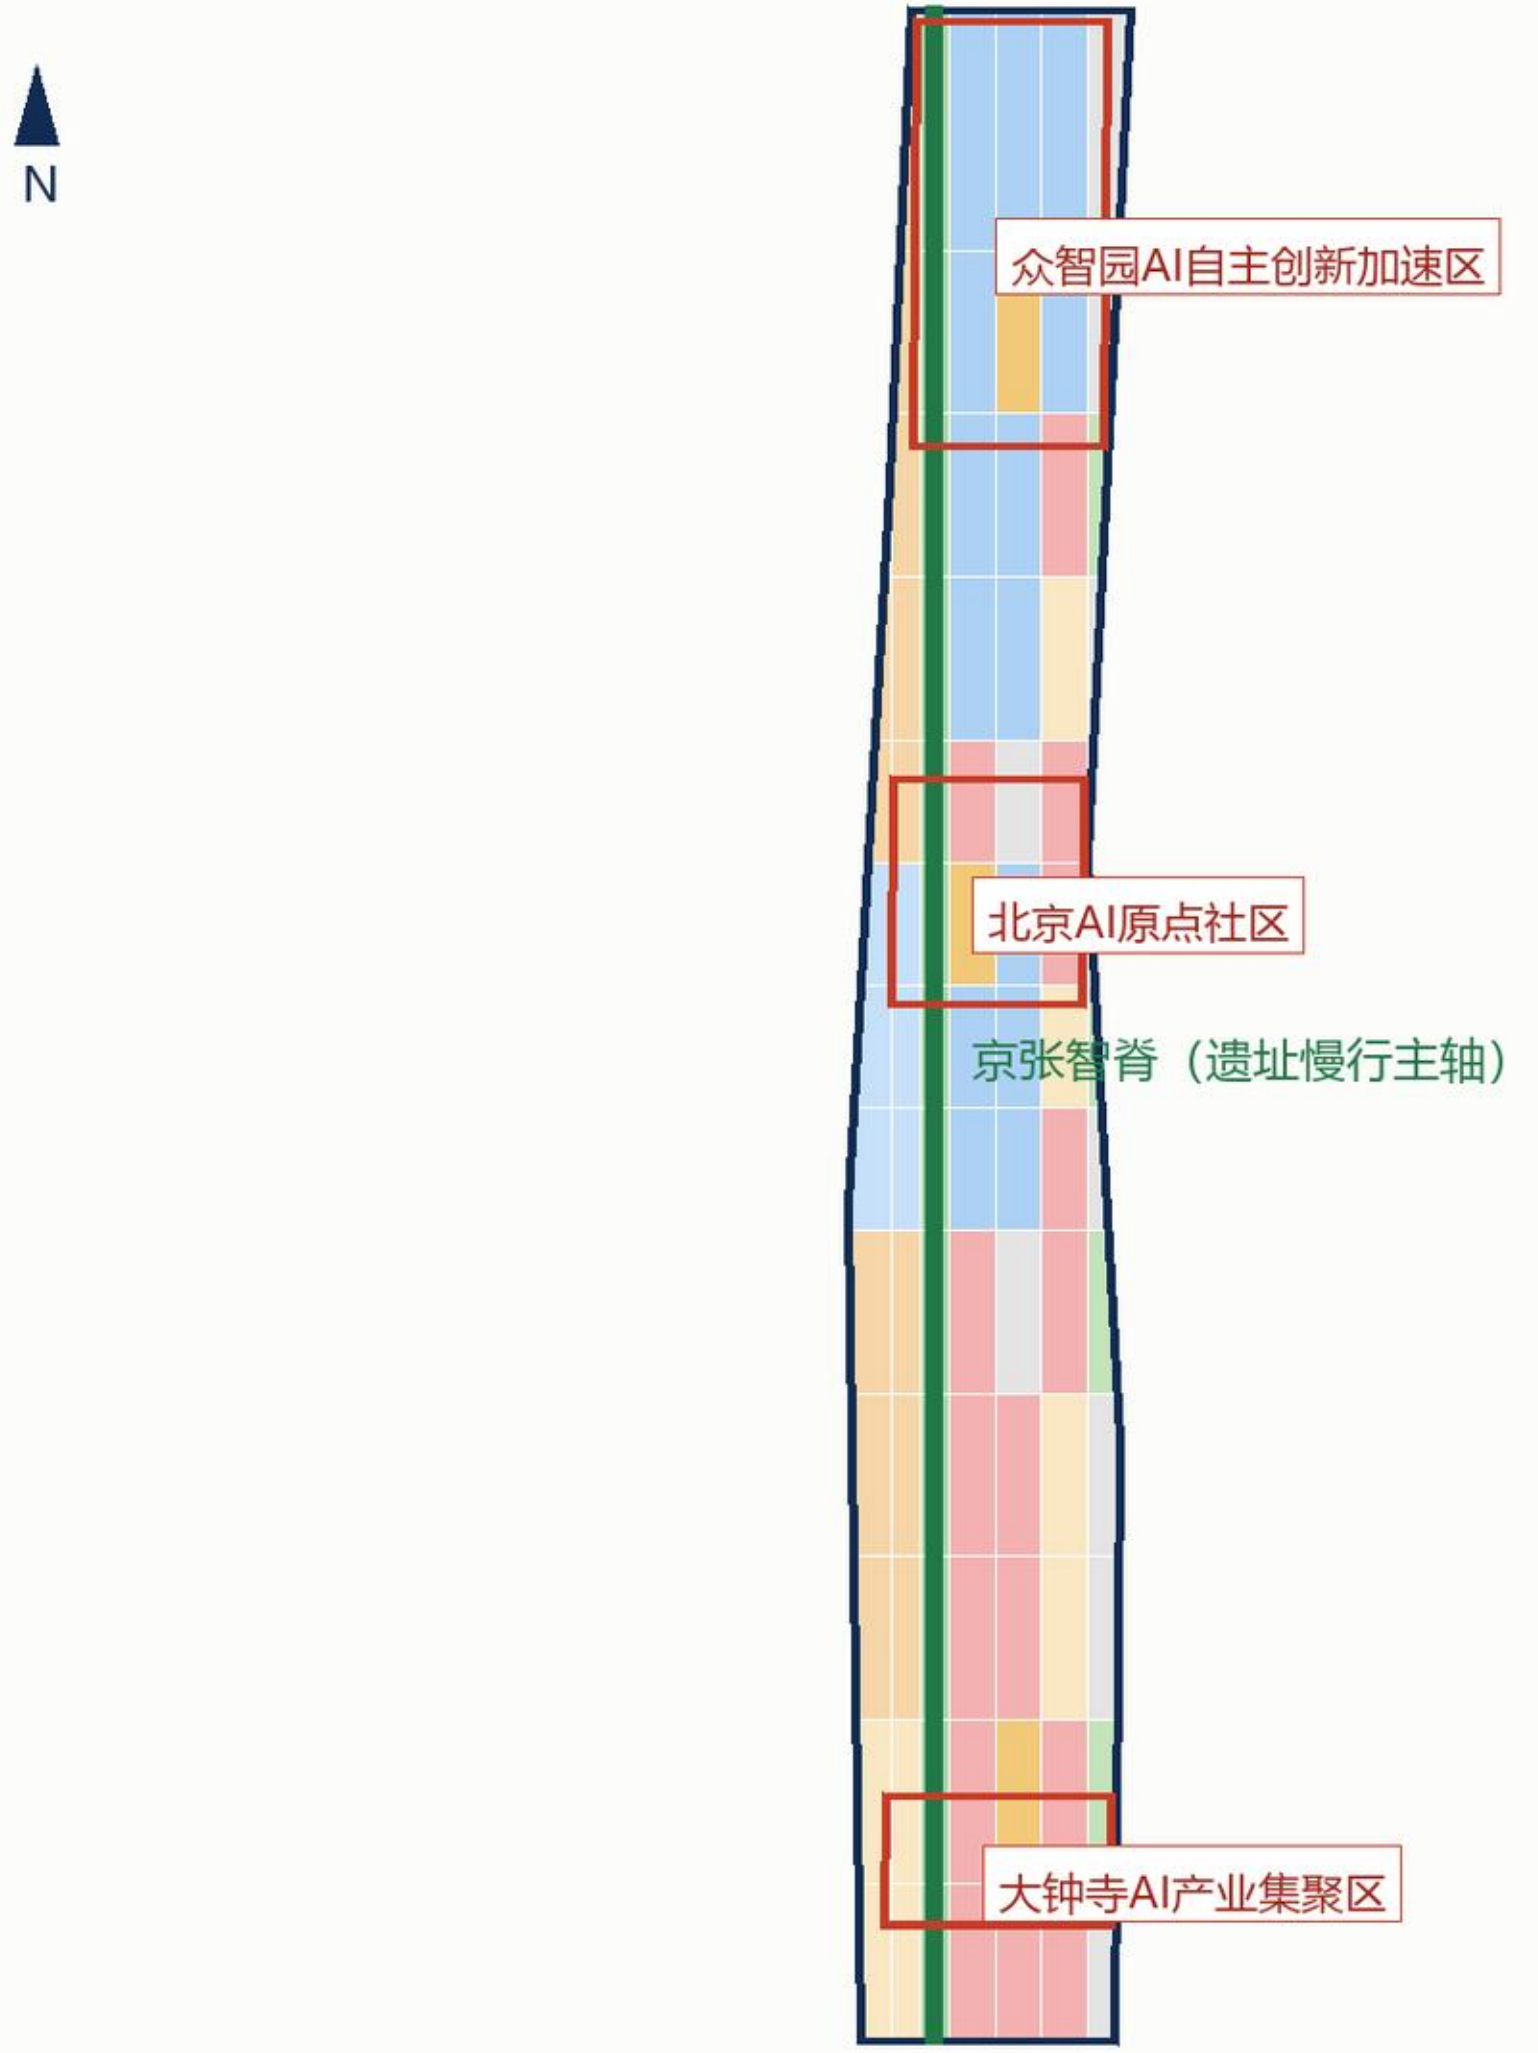

三区两翼


三区两翼协同：众智园加速区（全栈自主/AI治理）→
原点社区（创新生态）→
大钟寺集聚区（智能原生生态）；中关村科技服务翼 × 小月河场景赋能翼

图例 Legend

- 京张智脊绿道主轴
- 重点详细设计区（临时边界）
- 总体设计范围（临时边界）

用地结构总图（概念性用地分区，拓扑无缝覆盖）

国土空间用地用海分类代码 | 与 geometry/land_use.geojson 一致

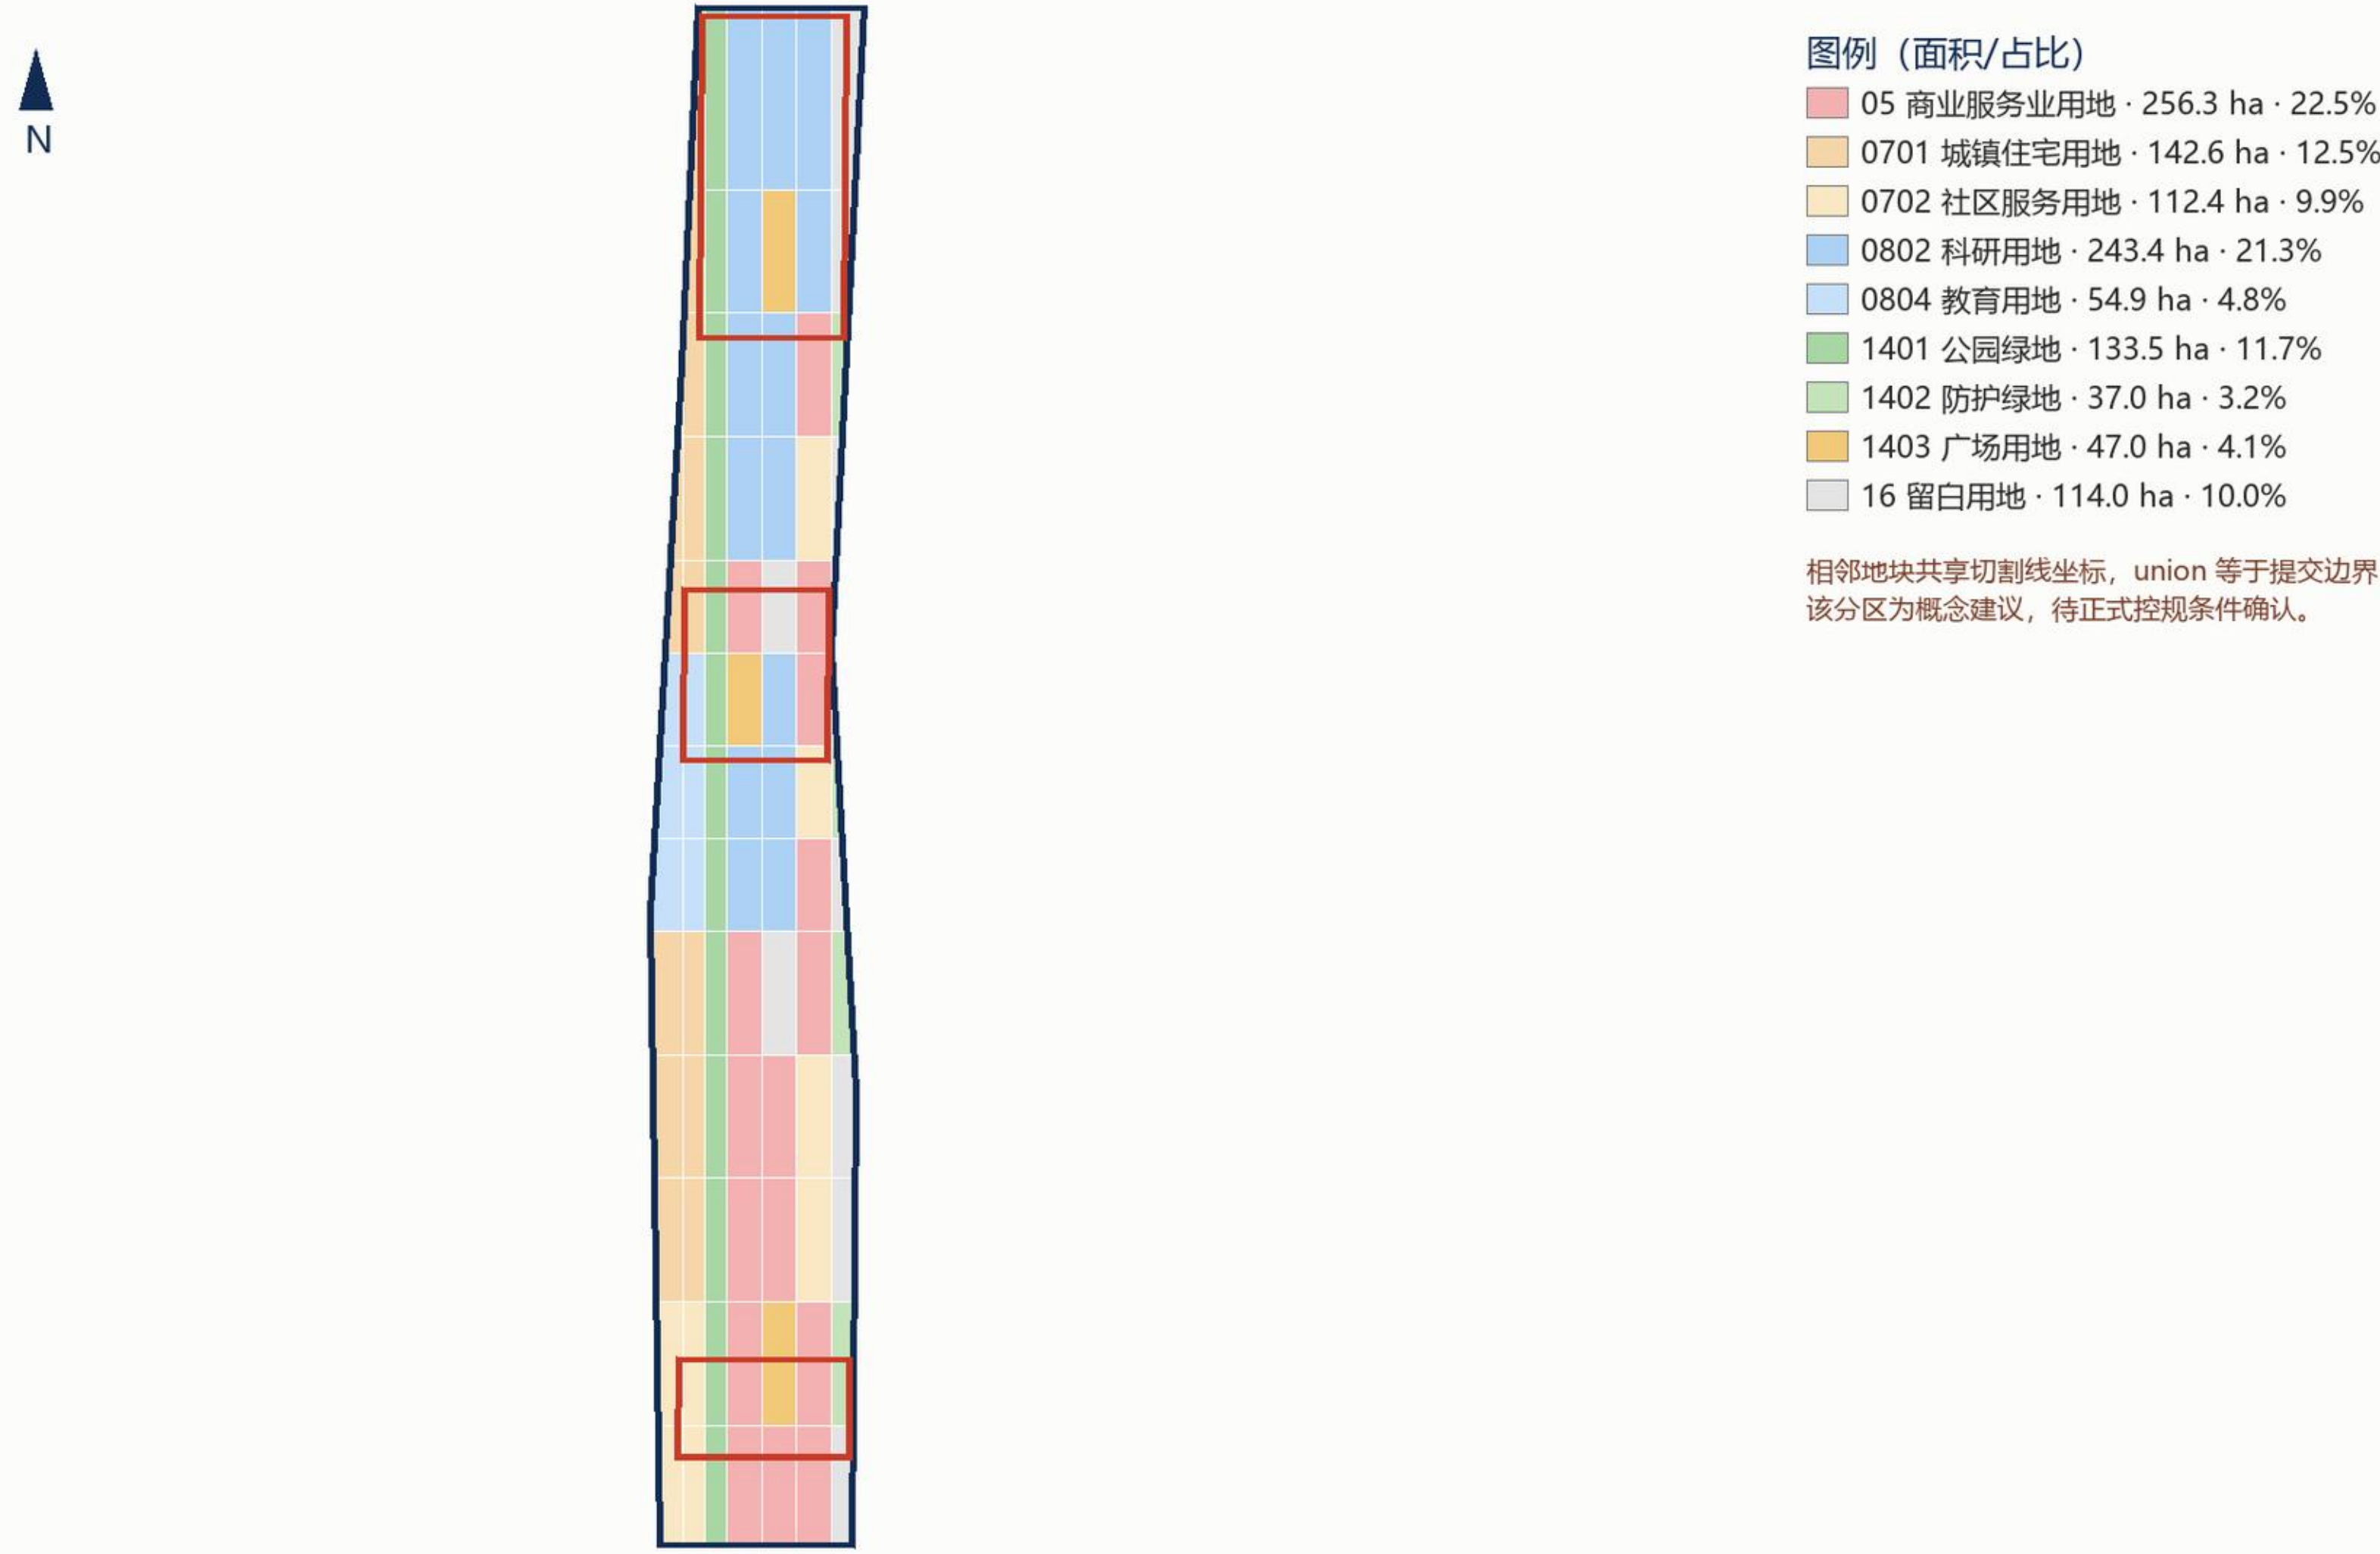

图例（面积/占比）

- 05 商业服务业用地 · 256.3 ha · 22.5%
- 0701 城镇住宅用地 · 142.6 ha · 12.5%
- 0702 社区服务用地 · 112.4 ha · 9.9%
- 0802 科研用地 · 243.4 ha · 21.3%
- 0804 教育用地 · 54.9 ha · 4.8%
- 1401 公园绿地 · 133.5 ha · 11.7%
- 1402 防护绿地 · 37.0 ha · 3.2%
- 1403 广场用地 · 47.0 ha · 4.1%
- 16 留白用地 · 114.0 ha · 10.0%


相邻地块共享切割线坐标，union 等于提交边界；
该分区为概念建议，待正式控规条件确认。

资料来源：北京市规自委海淀分局征集公告（2026-05-09）与维护者临时边界（provisional constraint，非正式红线）；图形由 GeoJSON/指标复算生成，EPSG:4548。

资料来源：北京市规自委海淀分局征集公告（2026-05-09）与维护者临时边界（provisional constraint，非正式红线）；图形由 GeoJSON/指标复算生成，EPSG:4548。

核心指标复算与证据链

全部 known 指标可由 geometry/*.geojson 在 EPSG:4548 下复算；unknown 指标待正式控规条件补齐

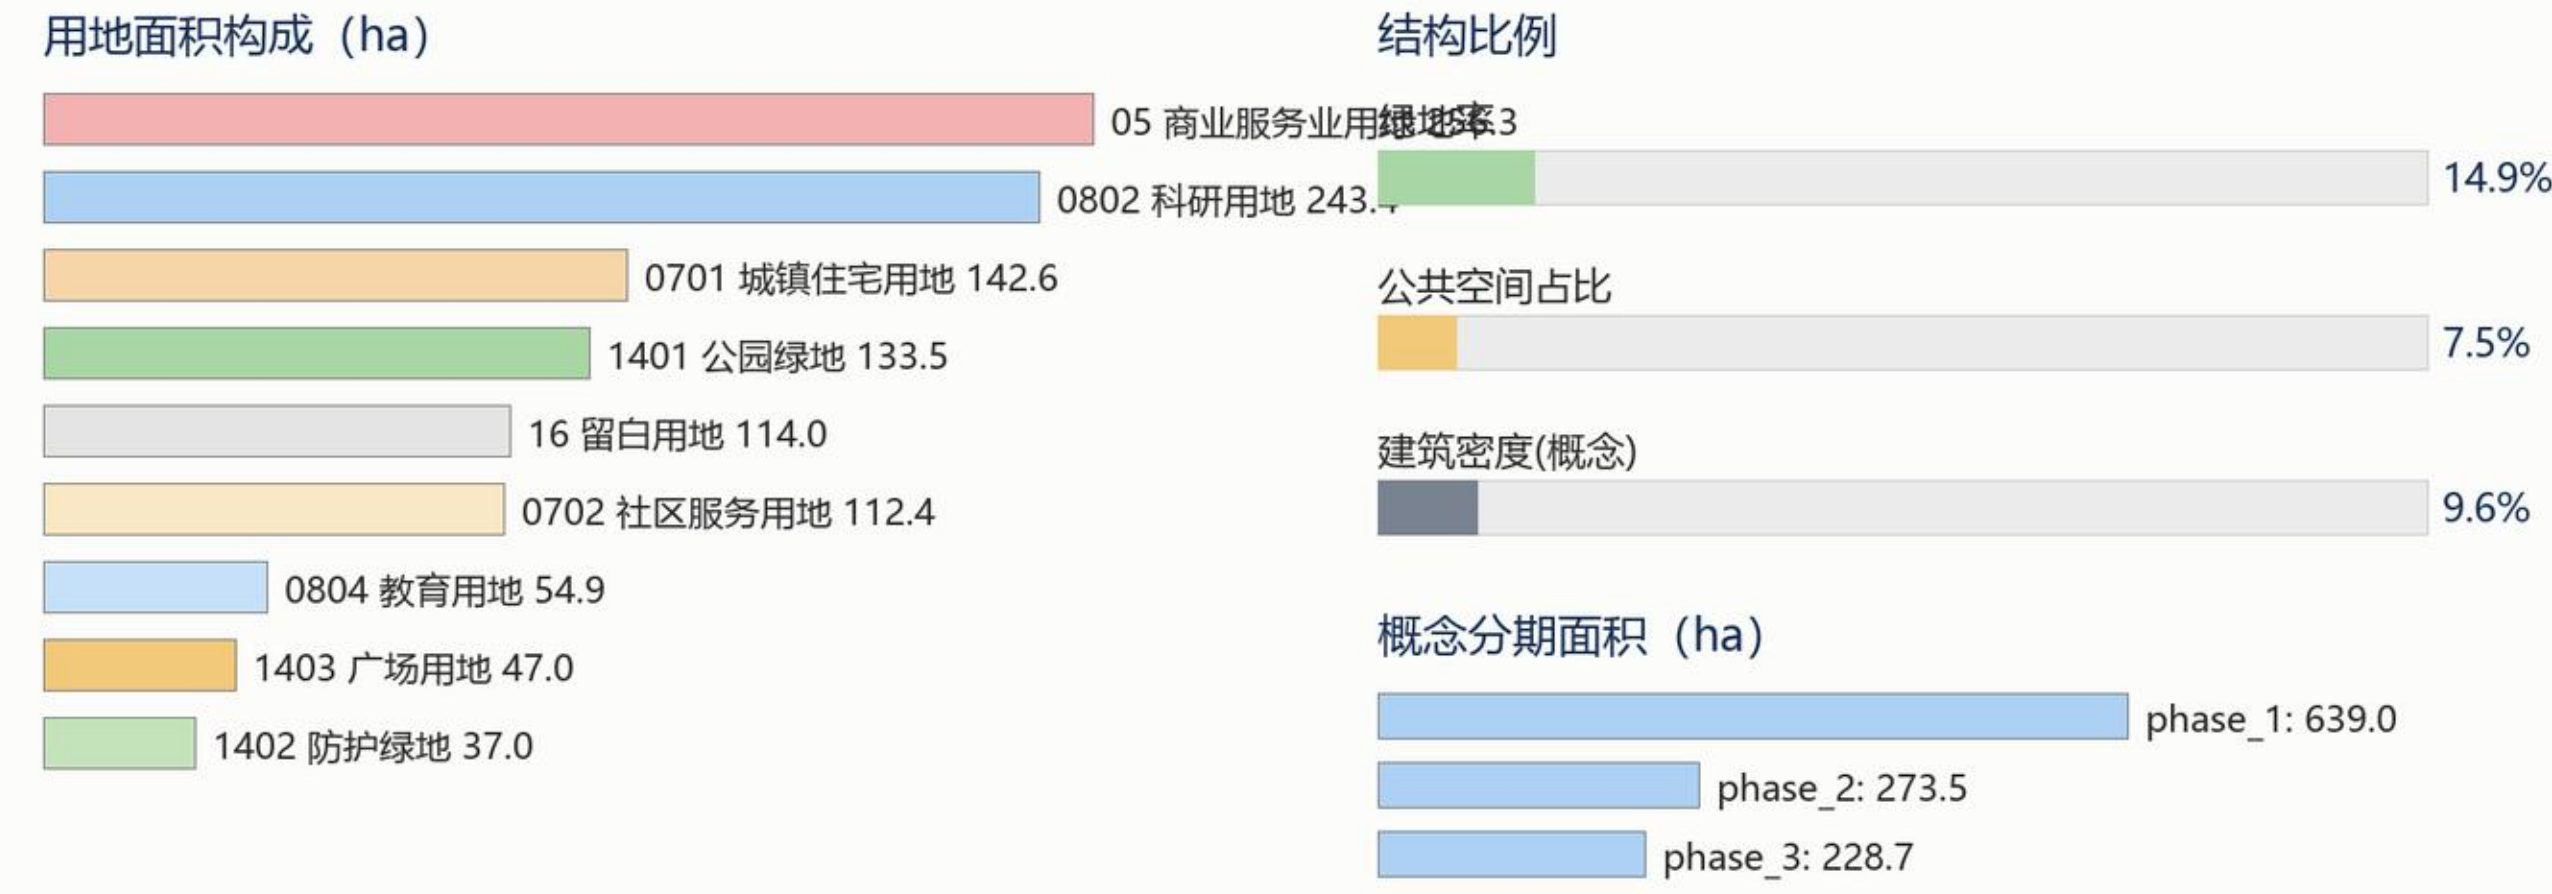

证据链：指标 → 复算公式 → 来源文件


site_area_sqm	polygon_area(site_boundary)	geometry/site_boundary.geojson	known
green_ratio	green_space_area / site_area	geometry/green_space.geojson	known
public_space_ratio	public_space_area / site_area	geometry/public_space.geojson	known
building_footprint_area_sqm	sum(polygon_area(buildings))	geometry/buildings.geojson	known
road_centerline_length_m	sum(line_length(roads))	geometry/roads.geojson	known
floor_area_ratio	unknown — 待正式控规条件	brief/site-package/ranges/planning_limits.js	unknown

资料来源：北京市规自委海淀分局征集公告（2026-05-09）与维护者临时边界（provisional constraint，非正式红线）；图形由 GeoJSON/指标复算生成，EPSG:4548。


总体概念：以京张遗址公园为历史与公共空间主轴，串联众智园、AI原点社区、大钟寺三处创新锚点，形成 ‘一脊三核两翼多点’ 的空间组织。用地为拓扑无缝概念分区（复算自 geometry/land_use.geojson），全部指标可在 EPSG:4548 下复算。

三处重点区域详细设计索引


众智园AI自主创新加速区 192.1ha | 北京AI原点社区 104.3ha | 大钟寺AI产业集聚区 72.0ha（公告值，临时边界复算接近）

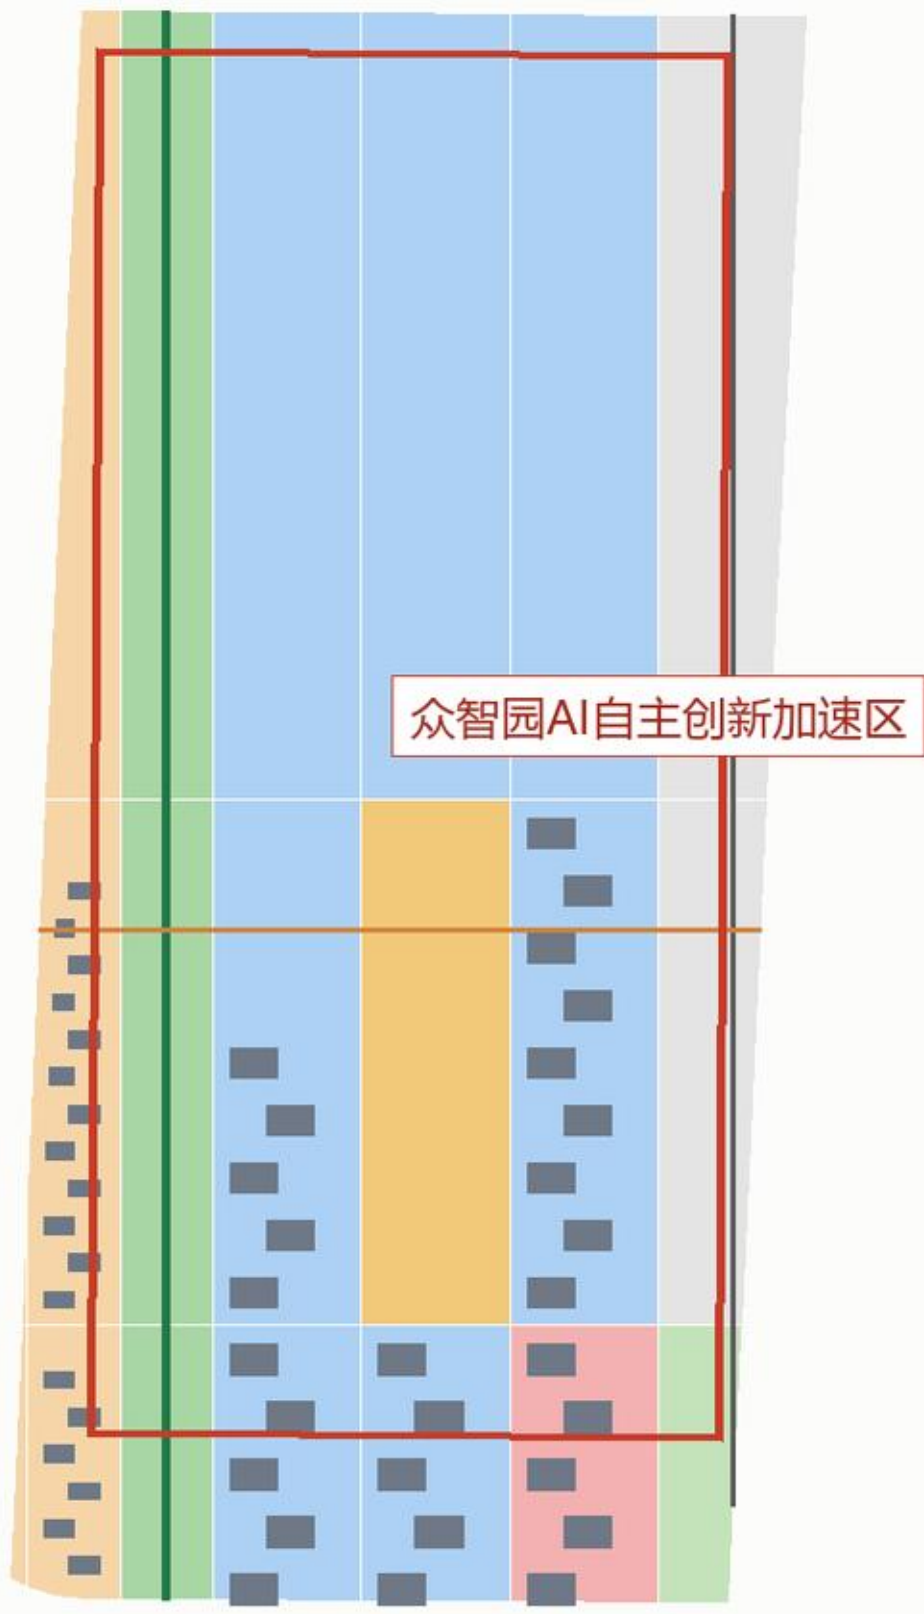

花园型全栈自主创新街区：清河界面、标准治理展示、低碳测试场

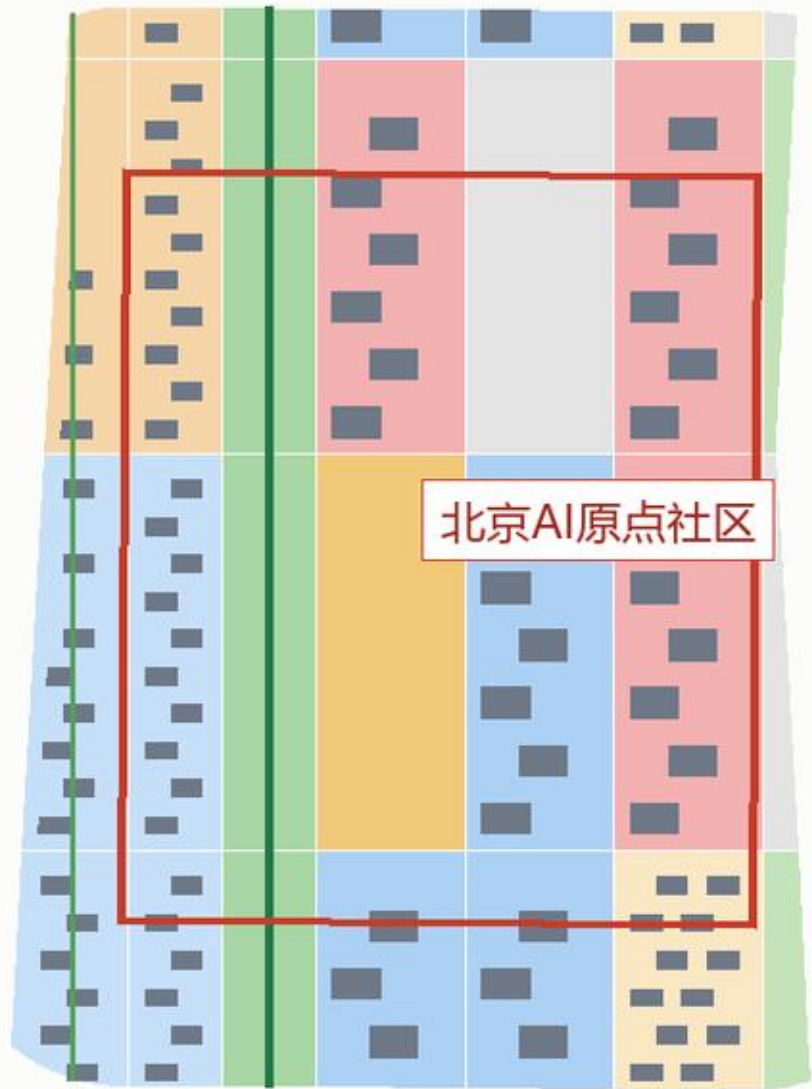

近校型成果转化与人才社区：开源发布厅、校区园区慢行缝合

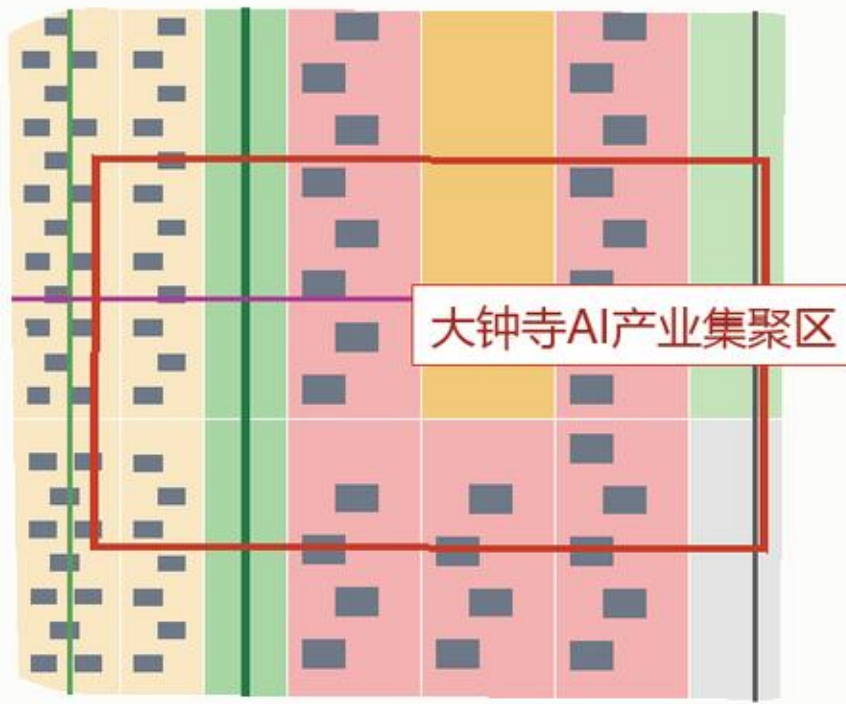


城市型智能经济街区：站点一体化、四象限步行连通、国际路演

资料来源：北京市规自委海淀分局征集公告（2026-05-09）与维护者临时边界（provisional constraint，非正式红线）；图形由 GeoJSON/指标复算生成，EPSG:4548。

交通慢行 × 蓝绿公共空间复合系统

一脊两环多联：遗址慢行主轴 + 东西翼循环 + 三处站点/片区缝合廊

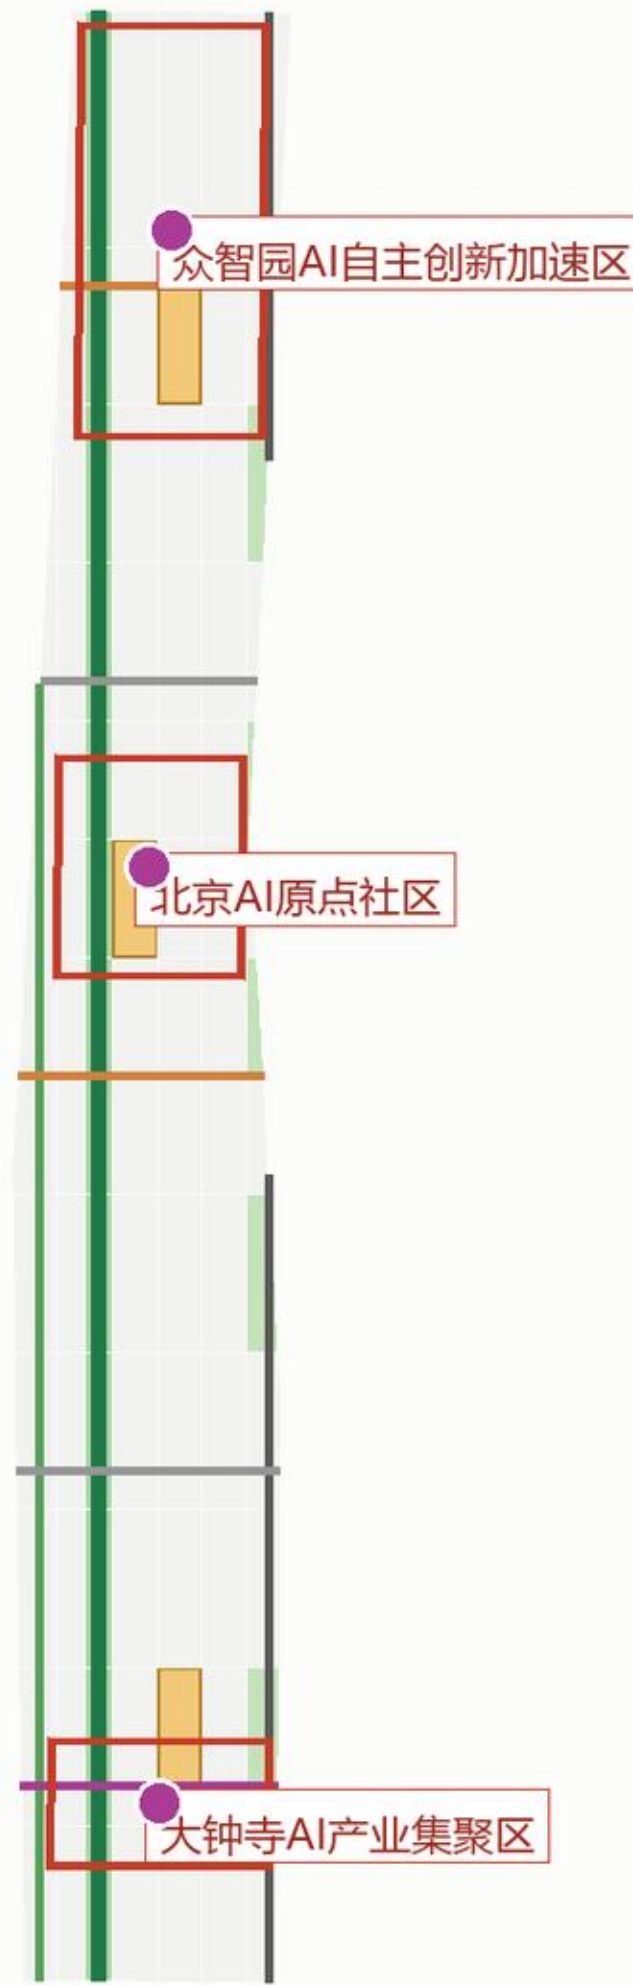

图例 Legend

- 智脊绿道主轴
- 骑行廊
- 次干路
- 支路微循环
- 步行缝合廊
- 轨道接驳
- 公园绿地
- 防护绿带
- 广场/公共节点

慢行/道路中心线总长 28.2 km
绿地率 14.9% | 公共空间占比 7.5%

资料来源：北京市规自委海淀分局征集公告（2026-05-09）与维护者临时边界（provisional constraint，非正式红线）；图形由 GeoJSON/指标复算生成，EPSG:4548。

AI 场景卡 Scenario Cards

01 开源发布厅

北京AI原点社区 | 高校/开源社区/初创的成果发布与小型路演；不采集个人行为轨迹

02 安全治理沙盒

众智园 | 标准制定、安全评测、模型红队测试的可参观协作节点

03 端侧算力驿站

总体范围节点 | 与公共服务和低碳能源结合的新型基础设施原型

04 AI慢行导航

京张遗址公园活力带 | 可解释导视与低侵入传感识别慢行断点

05 国际路演客厅

大钟寺 | 智能体/智能终端/内容消费企业的展示与国际交流

06 清河低碳创新廊

众智园临清河界面 | 绿色空间、雨洪、骑行与AI展示复合

07 近校成果转化街

原点社区 | 孵化、法务、知识产权与投融资服务街

08 数据要素会客厅

大钟寺 | 合规授权可审计的数据要素流通城市界面

09 AI生活服务样板街

社区商业交汇处 | 医疗教育法律生活服务的AI+小尺度样板

10 全球AI活动周路线

一带公共空间 | 遗址文化-开源社区-产业展示-国际路演步行路线

11 遗址公园夜光跑道

遗址公园 | 夜间活力与安全照明分级管理的运动场景

12 无障碍AI导览

全带 | 多语种无障碍导览，保留人工服务兜底（无障碍环境建设法第39条边界）