


FIG-03

万·北京AI原点社区 试错力

亿·众智园AI自主创新加速区
联结力

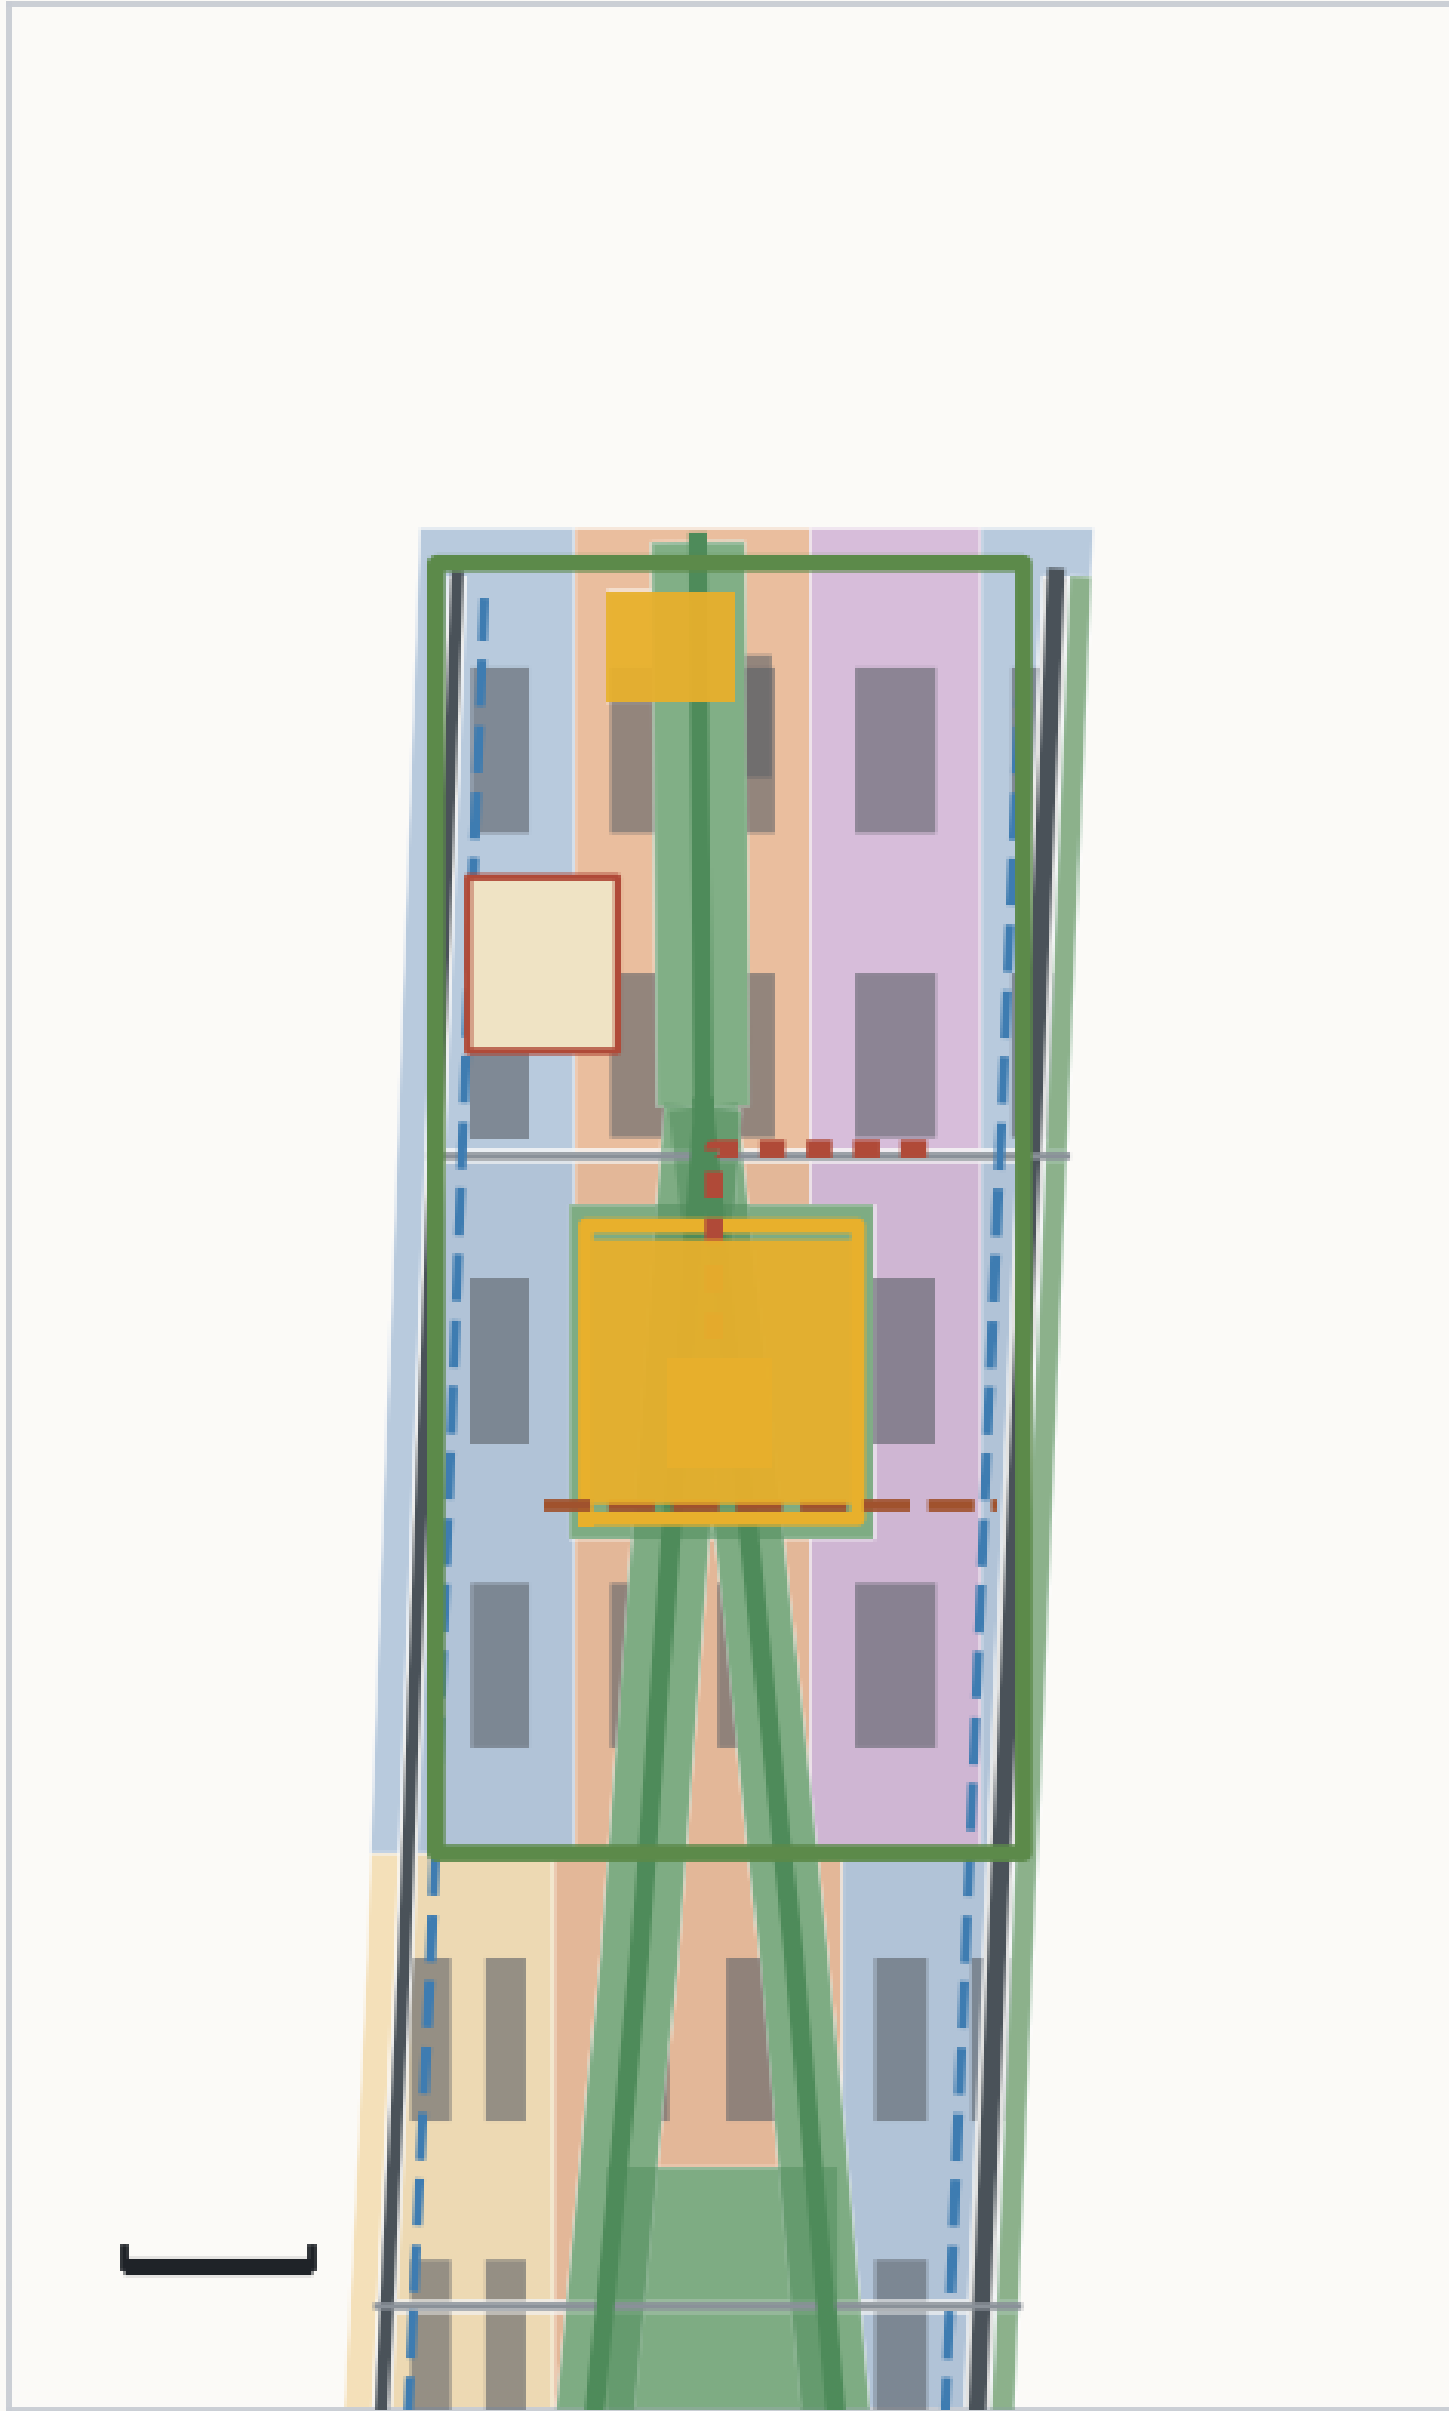

跨区约束建议：① 8 岁儿童须能在成人视线可及范围内独立活动 ② 80 岁长者须能在 150 米内找到座椅与遮荫 ③ 每区至少一块不建设的少年留白地 ④ 首层公共开放界面连续不被打断

空间动作（概念建议）

- 清河文化与低碳创新交往环境
- 亿联广场：产业与市民年度对话场
- 共享街道：机器人配送低速让行
- 首层开放比例作为「自主而不封闭」观察点

公告约面积 192.1 ha
临时范围复算 192.9 ha
偏差 0.43% (容差 3%)
provisional_rough · 非红线依据


本图册基于临时期前边界 (official_boundary=false, geometry_role=provisional_constraint) 生成; 用于开源共创讨论与自检, 不作为法定红线、精确面积或审批依据; 官方边界发布后整体重算。所有空地落地建议均为概念建议, 可供专业团队深化研究。

land-use-structure

图 02 · 用地结构与成长带功能分区

教育与社区服务有意加厚 | 留白单列为一类用地 | 建筑高度与强度为研究性示意值，非控规结论
用地结构与建筑基底（示意，按用地用海分类指南口径）

FIG-02

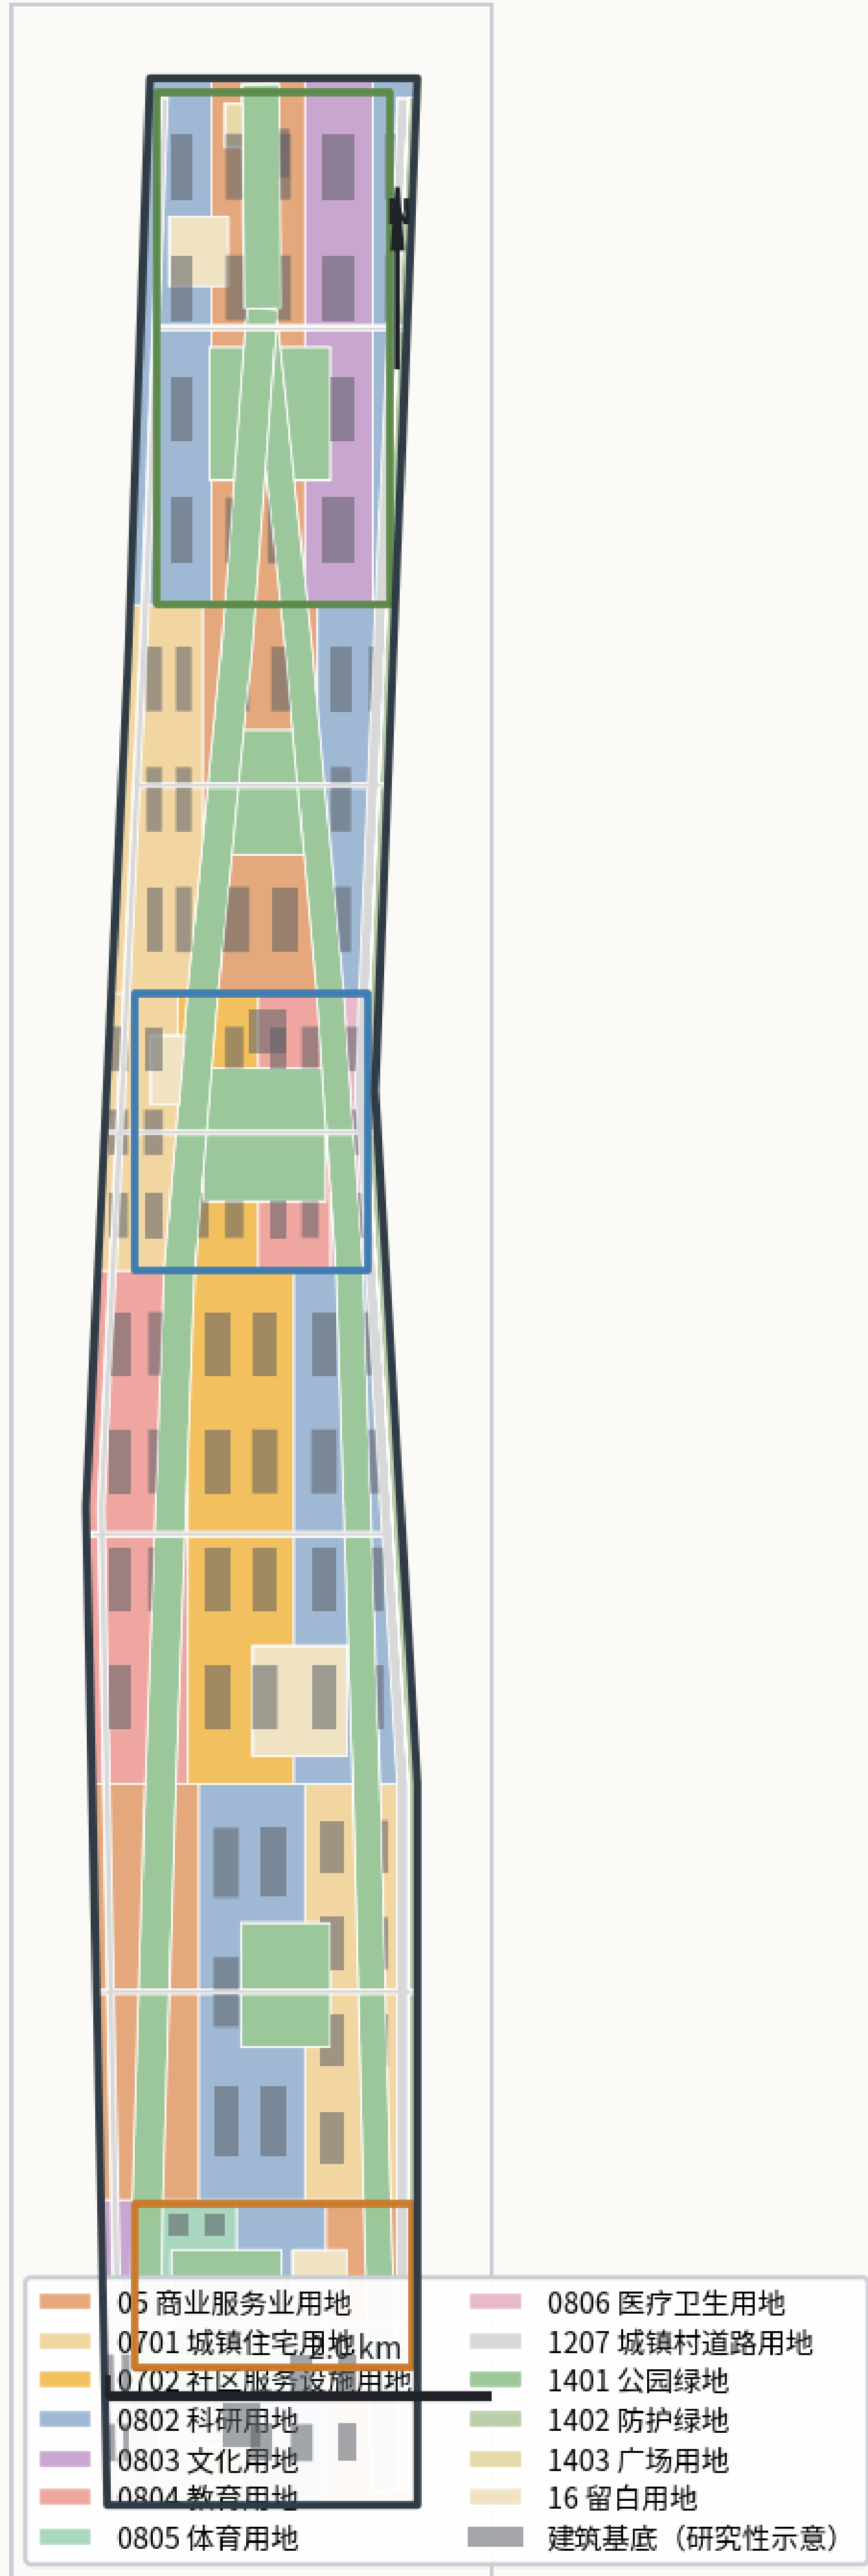

用地构成（临时边界复算，公顷／占比）

1401 公园绿地	304.5 ha		26.7%
0802 科研用地	213.8 ha		18.7%
05 商业服务业用地	122.4 ha		10.7%
0701 城镇住宅用地	106.2 ha		9.3%
0702 社区服务设施用地	90.8 ha		8.0%
1207 城镇村道路用地	83.7 ha		7.3%
0804 教育用地	65.3 ha		5.7%
0803 文化用地	61.5 ha		5.4%
1402 防护绿地	34.1 ha		3.0%
16 留白用地	32.1 ha		2.8%
0805 体育用地	20.0 ha		1.8%
1403 广场用地	4.2 ha		0.4%
0806 医疗卫生用地	2.8 ha		0.2%

家庭友好在法定分类里的落点

· 教育用地 0804	65.3 ha	AI少年学园与家庭学习中心
· 社区服务设施 0702	90.8 ha	家庭AI素养站主要载体
· 留白用地 16	32.1 ha	少年留白地，三年一议

首层向公共开放建筑 39 处 | 「城市的第一层属于孩子和老人」

关键复算指标

用地覆盖率	0.999999	无缝无重叠
建筑基底面积	148.7 ha	94 处示意基底
建筑密度	0.1303	低密度高绿量

数据说明：本图基于临时粗略边界（official_boundary=false, geometry_role=provisional_constraint）生成，仅用于开源共创讨论与自检，不得作为法定红线、精确面积或审批依据；官方边界发布后需整体重算。面积与长度按 EPSG:4548 投影复算。来源：OFFICIAL-ANNOUNCEMENT / AGENT-TASKBOOK / SITE-PACKAGE / BOUNDARY-SOURCE。所有空间落地建议均为概念建议，可供专业团队深化研究。

图 05 · 指标体系、面积复算与证据链核对

27 项 known 指标全部可从 GeoJSON 原样复算 | 4 项 unknown 显式标注原因 | 口径与评审脚本一致

FIG-05

核心复算指标（临时边界 · EPSG:4548）

设计范围面积	11.41 km ²	site_boundary
重点区合计	369.3 ha	key_areas ×3
用地覆盖率	0.999999	land_use 37 图斑
绿地／绿地率	345 ha ／ 30.2%	green_space 9
公共空间／占比	165 ha ／ 14.5%	public_space 14
建筑基底／密度	149 ha ／ 13.0%	buildings 94
示意规模／毛FAR	942 万m ² ／ 0.826	研究性示意值
慢行／车行	44.9 km ／ 27.4 km	roads 21
一期面积	112.1 ha	phasing PHASE-001

8-80 友好度专项指标（本方案自设，可被脚本复核）

家庭AI素养站	11处
亲子同桌 · 围坐不排排坐 · 可退出可匿名	
少年学习场	19处
AI+PBL 项目式学习 · 成果公开不进抽屉	
共创元素空间	4处
34.6 ha · 三年一议	
全龄公园节点	5处
千问园 · 万试园 · 亿联园 + 两处过渡公园	
首层开放建筑	39处
城市的第一层属于孩子和老人	
轨道接驳枢纽	3处
无高差 · 有遮蔽 · 有座椅	

指标状态分布：诚实标注不知道的部分

known 27		unknown 4
· floor_area_ratio	公开资料未提供经批准的容积率控制值与官方范围线面积。	
· resident_population	公开征集资料未提供范围内常住人口与人口结构数据。	
· population_within_300m_of_park_ratio	缺少人口空间分布数据，300米见园覆盖率无法定量核算，仅做几何可达性推演。	
· existing_building_retention_ratio	缺少现状建筑普查、结构安全评估与产权数据，保留-改造-拆除比例暂无法定量。	
承认不知道，是让后续专业团队能顺利接手的前提。官方人口、现状建筑普查、控规条件与市政容量数据发布后，全部指标须整体重算而非局部替换。		

证据链闭合：五类机读引用 × 三张矩阵

[source:…]	资料来源（含需求侧依据 FAMILY-AI-LITERACY-PROGRAM）	8
[standard:…]	标准依据（公告 · 任务书 · 城市设计 · 控规 · 分类 · 深度）	6
[depth:…]	设计深度项，逐条对应 design_depth_matrix.json	15
[data:…]	结构化图层引用，覆盖全部 9 个 geometry 文件	9
[metric:…]	known 指标全部在正文被引用并可复算	27

三张矩阵
compliance 23 条（公告 1.3–1.5 + agent.1–agent.6） standard 6 条 depth 15 条

复算口径：交换用 EPSG:4326，面积长度投影至 EPSG:4548（CGCS2000 3度带 CM 117°E）；
图层内部先合并再取并集面积；比值统一以设计范围面积为分母，与仓库空间评审脚本一致。


数据说明：本图基于临时粗略边界（official_boundary=false, geometry_role=provisional_constraint）生成，仅用于开源共创讨论与自检，不得作为法定红线、精确面积或审批依据；官方边界发布后需整体重算。面积与长度按 EPSG:4548 投影复算。来源：OFFICIAL-ANNOUNCEMENT / AGENT-TASKBOOK / SITE-PACKAGE / BOUNDARY-SOURCE。所有空间落地建议均为概念建议，可供专业团队深化研究。

图 04 · 交通慢行、轨道接驳与蓝绿公共空间

FIG-04

人字脊三段慢行主轴 | 六条横向支路缝合东西 | 三处轨道接驳 | 三条全龄无障碍步行环

交通慢行与蓝绿系统叠合（中心线为设计示意，红线待官方核校）

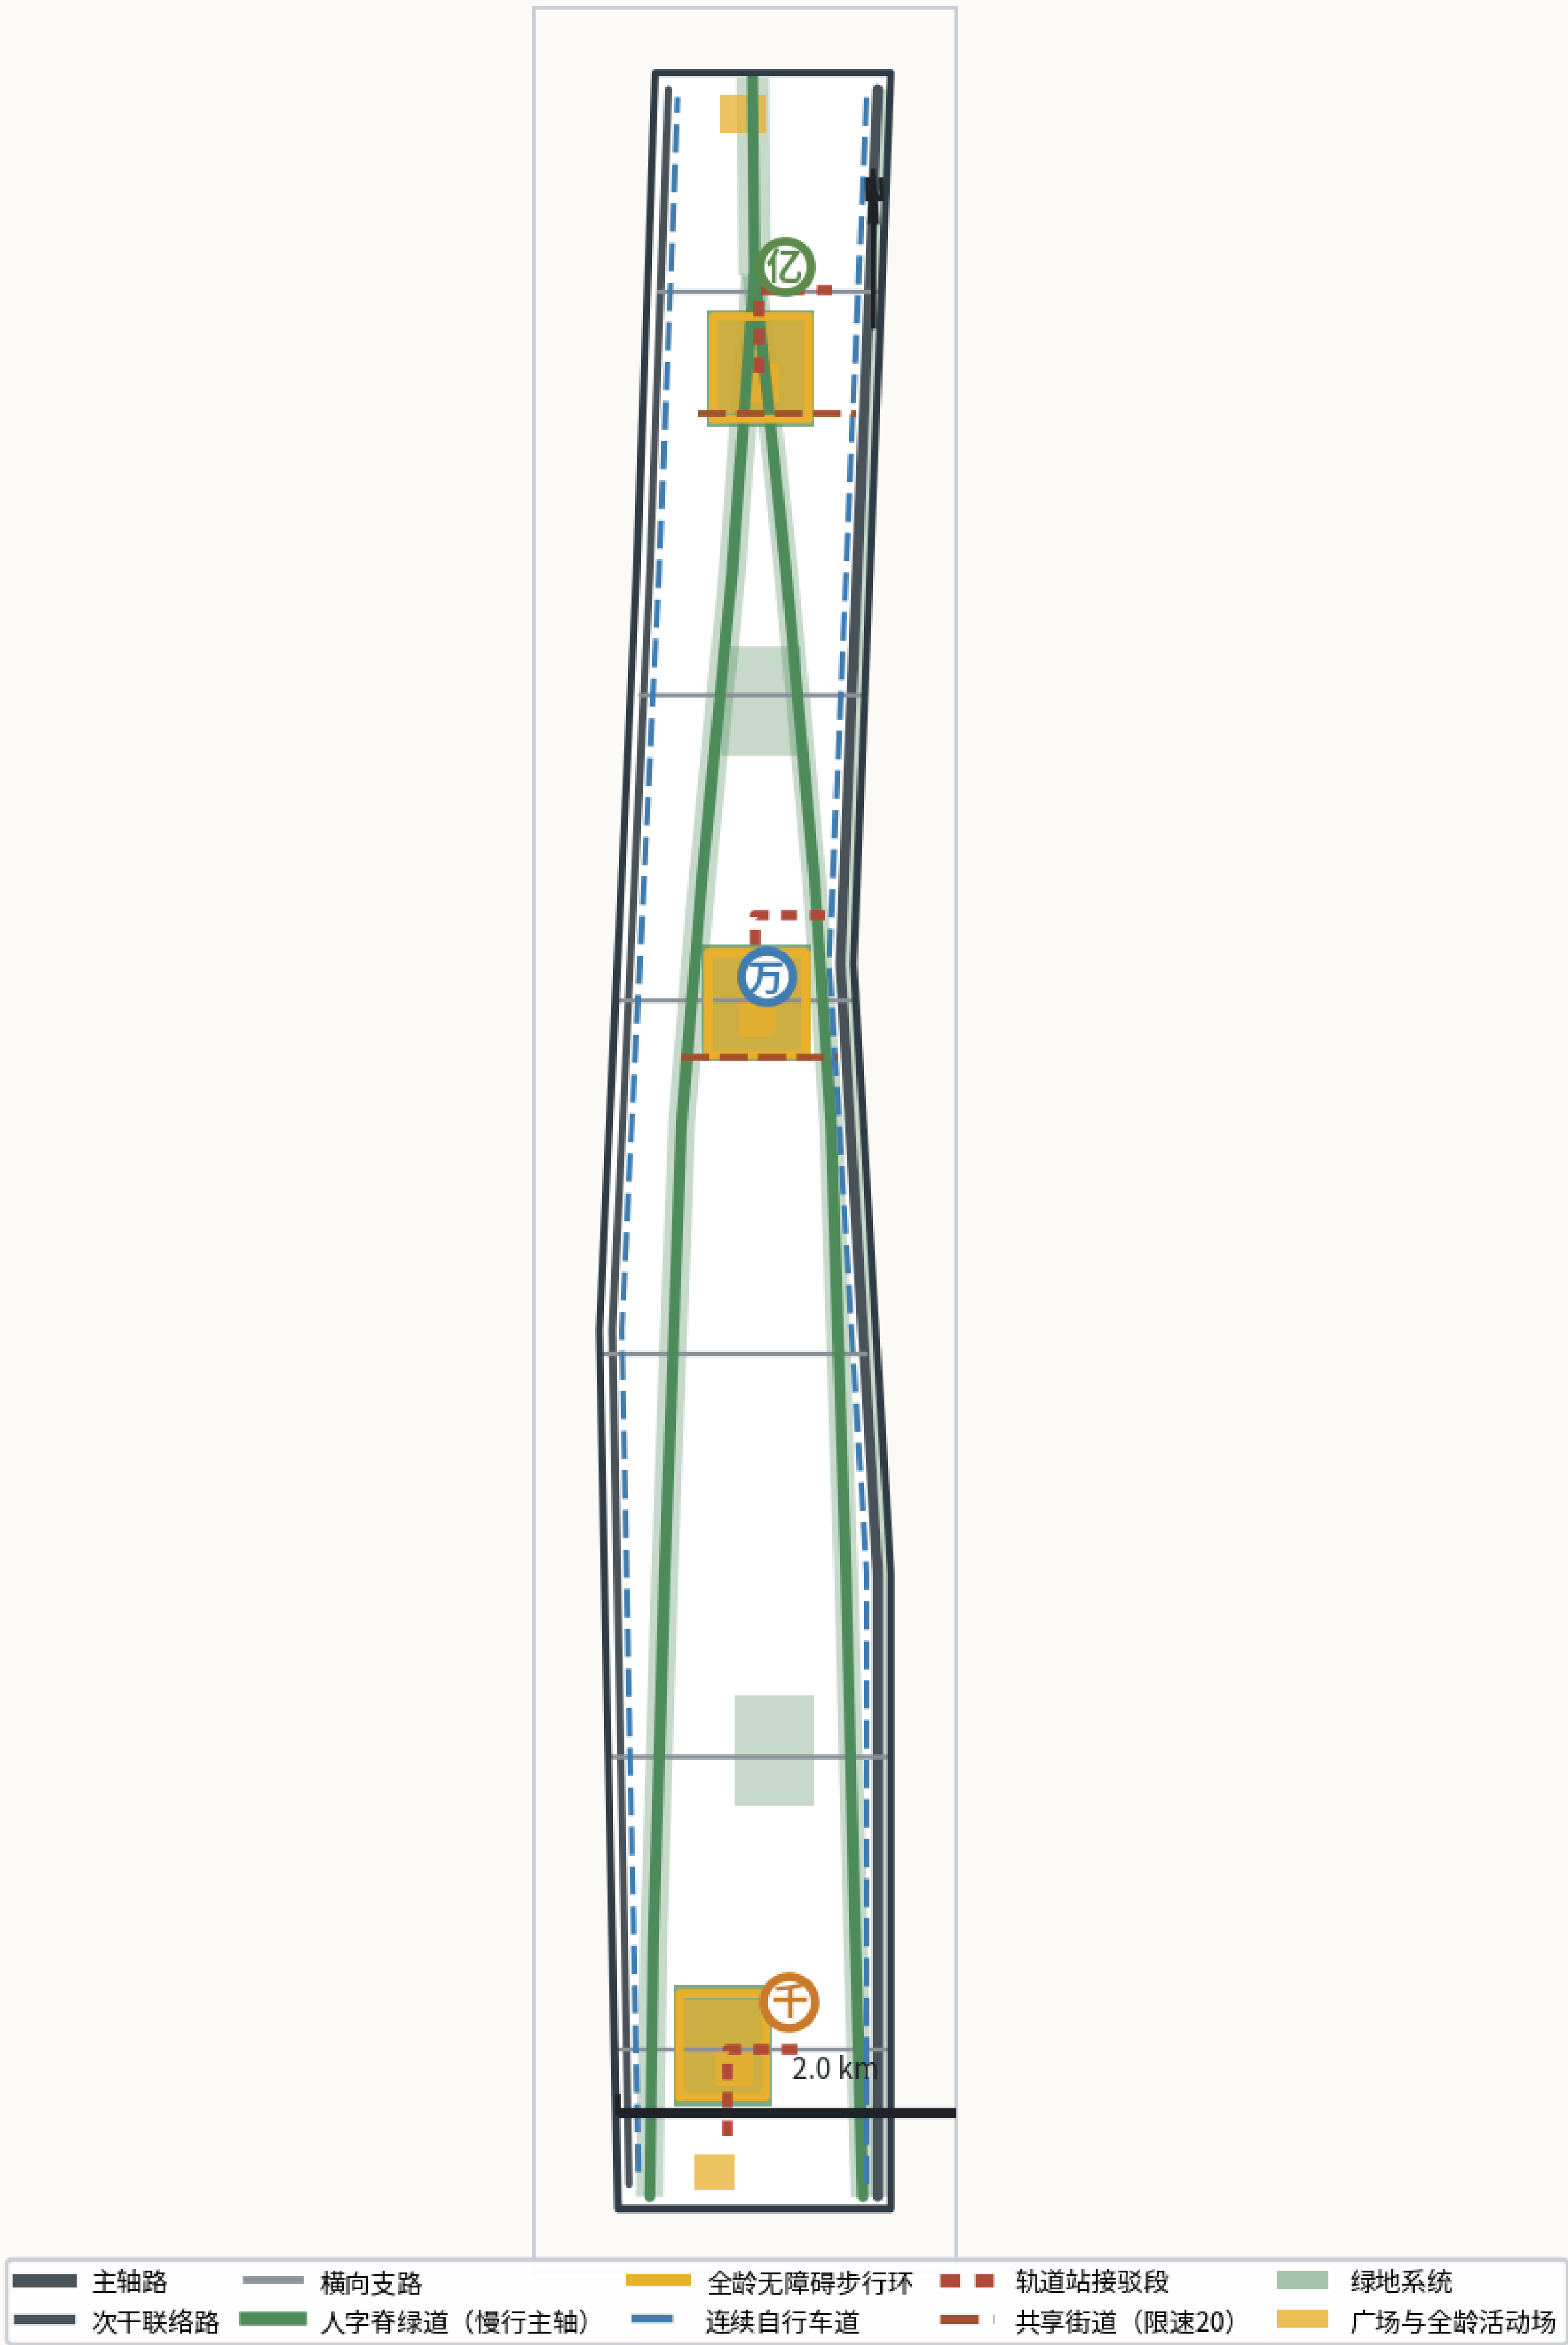

慢行优先不是口号，是长度比




慢行网络 44,912 m | 机动车路网 27,450 m

8-80 出行断面策略

8 岁 · 学径	不穿越主干道 · 抬升式过街 · 视线净空 · 限速 20
80 岁 · 每天一圈	三处全龄无障碍步行环，环长约 1.7~1.8 km
全龄 · 150 米法则	主要步行路径 150 米内可找到座椅与遮荫
接驳 · 三处枢纽	3 处轨道接驳：无高差 · 有遮蔽 · 有座椅
机器 · 让行原则	自动配送在学径与儿童活动区外侧减速让行

蓝绿与公共空间总量

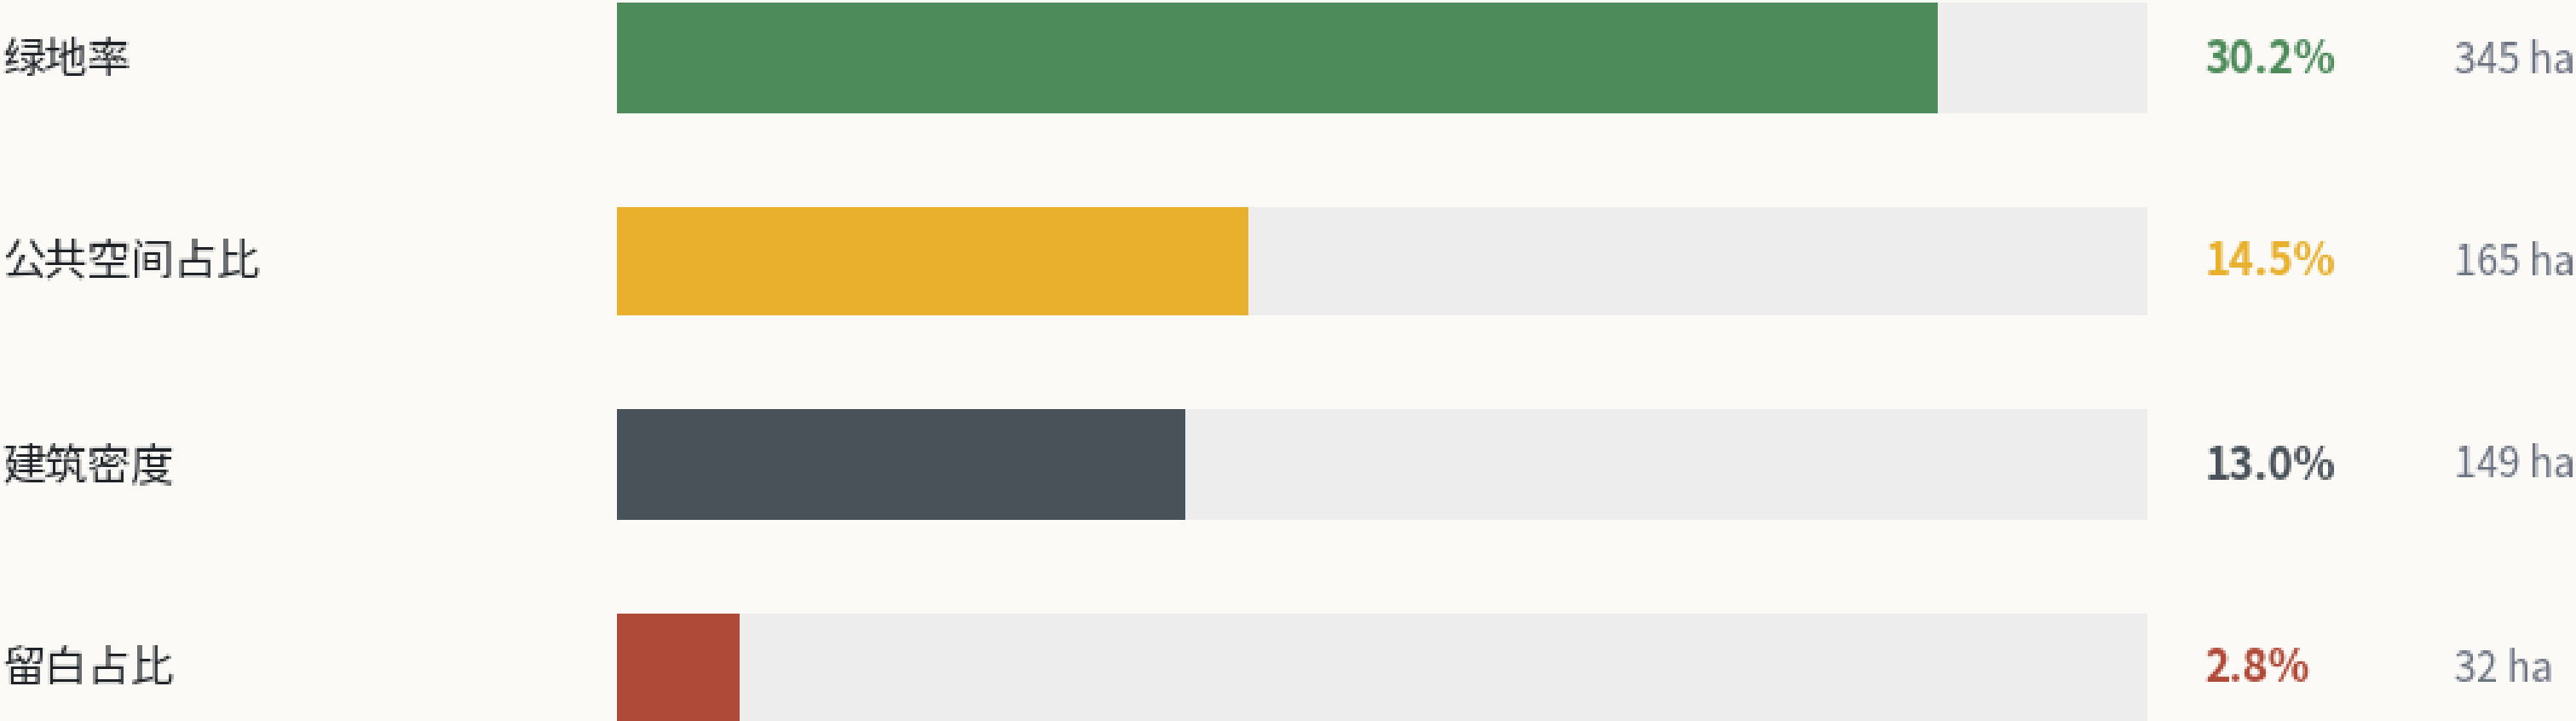


注：市政管廊、能源负荷与容量测算属专业范畴，本方案不给结论；300 米公园覆盖人口比例因缺官方人口数据标注为 unknown。

数据说明：本图基于临时粗略边界（official_boundary=false, geometry_role=provisional_constraint）生成，仅用于开源共创讨论与自检，不得作为法定红线、精确面积或审批依据；官方边界发布后需整体重算。面积与长度按 EPSG:4548 投影复算。来源：OFFICIAL-ANNOUNCEMENT / AGENT-TASKBOOK / SITE-PACKAGE / BOUNDARY-SOURCE。所有空间落地建议均为概念建议，可供专业团队深化研究。

图 01 · 人字号总体概念与证据链结构

REN-HAO 京张AI成长带 | 一脊 · 三园 · 三区 · 两翼 · 多留白 | 概念建议, 可供专业团队深化研究


总体设计范围 · 一脊三园三区结构 (临时边界)

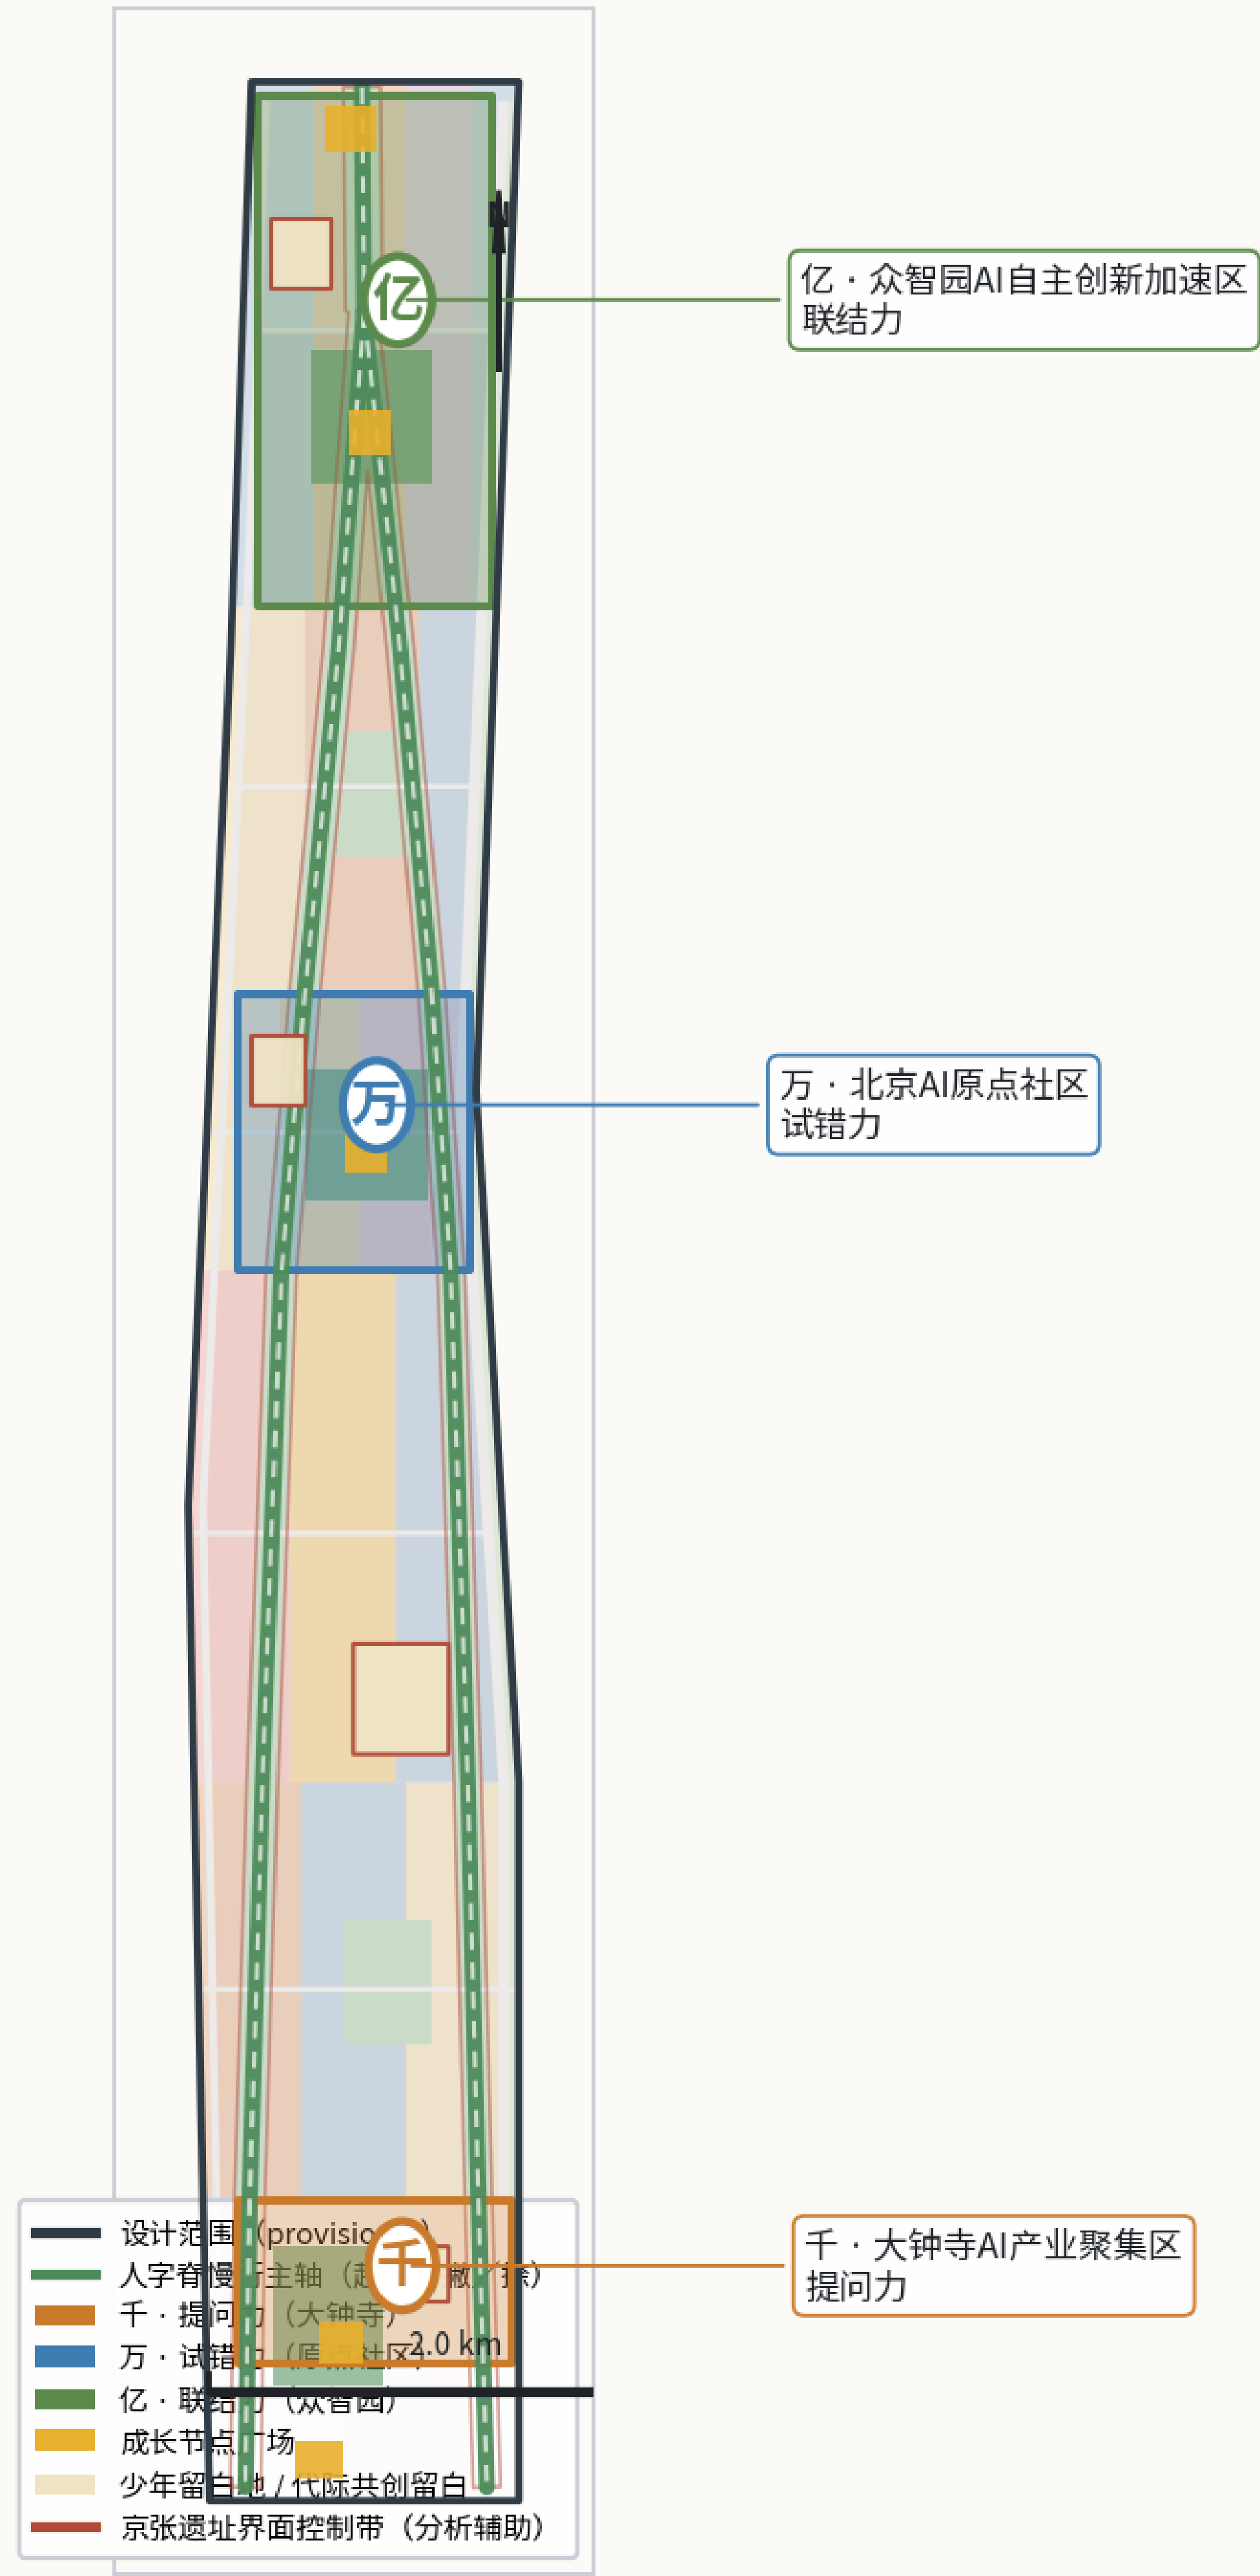

人字号 REN-HAO

命名三重含义

- 历史原型：青龙桥「人」字形展线，绕一点路也要上得去
- 价值锚点：AI 城市的中心不是算力，是人
- 代际契约：一撇少年向前，一捺长者托底，缺一笔站不住

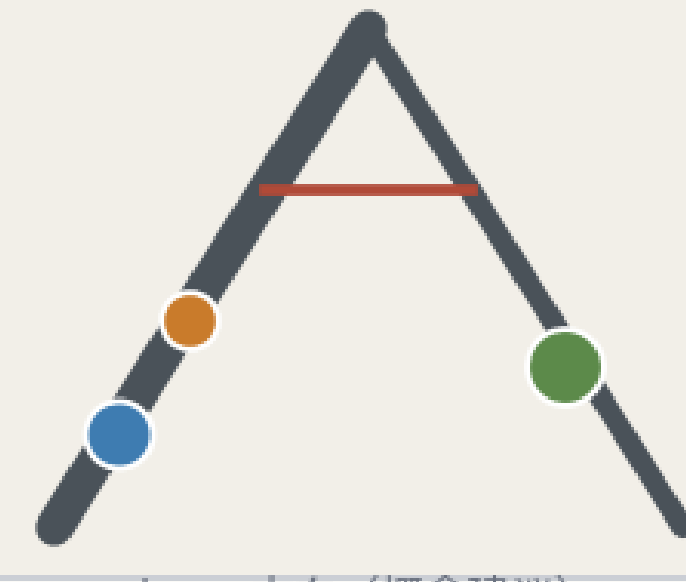

成长语法：千 · 万 · 亿

千 · 提问力	门户 · 提问的地方 好问题比标准答案值钱
万 · 试错力	客厅 · 试错的地方 做错一万次，也是在做
亿 · 联结力	工坊 · 一起干的地方 一个人想不出来，就找一亿个人

证据链：从一句结论回到一个字段

公告 / 任务书	OFFICIAL-ANNOUNCEMENT · AGENT-TASKBOOK
临时边界与站点包	BOUNDARY-SOURCE · KEY-AREA-SOURCE · SITE-PACKAGE
需求侧依据	FAMILY-AI-LITERACY-PROGRAM (家庭AI素养计划 · 三力模型)
结构化图层	geometry/*.geojson (9 层, 含 8-80 布尔字段)
可复算指标	metrics.json (27 项 known / 4 项 unknown)
三矩阵自证	compliance 23 条 · standard 6 条 · depth 15 条
可读成果	proposal.md · A3/A0 · visual/index.html
验收标准：让 8 岁的孩子和 80 岁的老人，都会为这个地方开心	

数据说明：本图基于临时粗略边界 (official_boundary=false, geometry_role=provisional_constraint) 生成，仅用于开源共创讨论与自检，不得作为法定红线、精确面积或审批依据；官方边界发布后需整体重算。面积与长度按 EPSG:4548 投影复算。来源：OFFICIAL-ANNOUNCEMENT / AGENT-TASKBOOK / SITE-PACKAGE / BOUNDARY-SOURCE。所有空间落地建议均为概念建议，可供专业团队深化研究。

指标复算 (临时边界, EPSG:4548)

设计范围	1.141e+07	m ²
重点区合计	3.693e+06	m ²
用地覆盖率	1	
绿地率	0.302	
公共空间占比	0.1445	
建筑密度	0.1303	
示意总规模	9.424e+06	m ²
慢行长度	4.491e+04	m
家庭AI素养站	11	处
少年学习场	19	处
共创空间	4	处
首层开放建筑	39	处
一期面积	1.121e+06	m ²

显示 unknown: floor_area_ratio / resident_population / population_within_300m_of_park_ratio / existing_building_retention_ratio, 原因: 缺少法定细分指标, 缺官方人口与人口分布, 缺现状建筑清单。
全部指标引用: [source: × 8] · [standard: × 4] · [depth: × 15] · [data: × 9 图层] · [metric: × 27 已知]。