
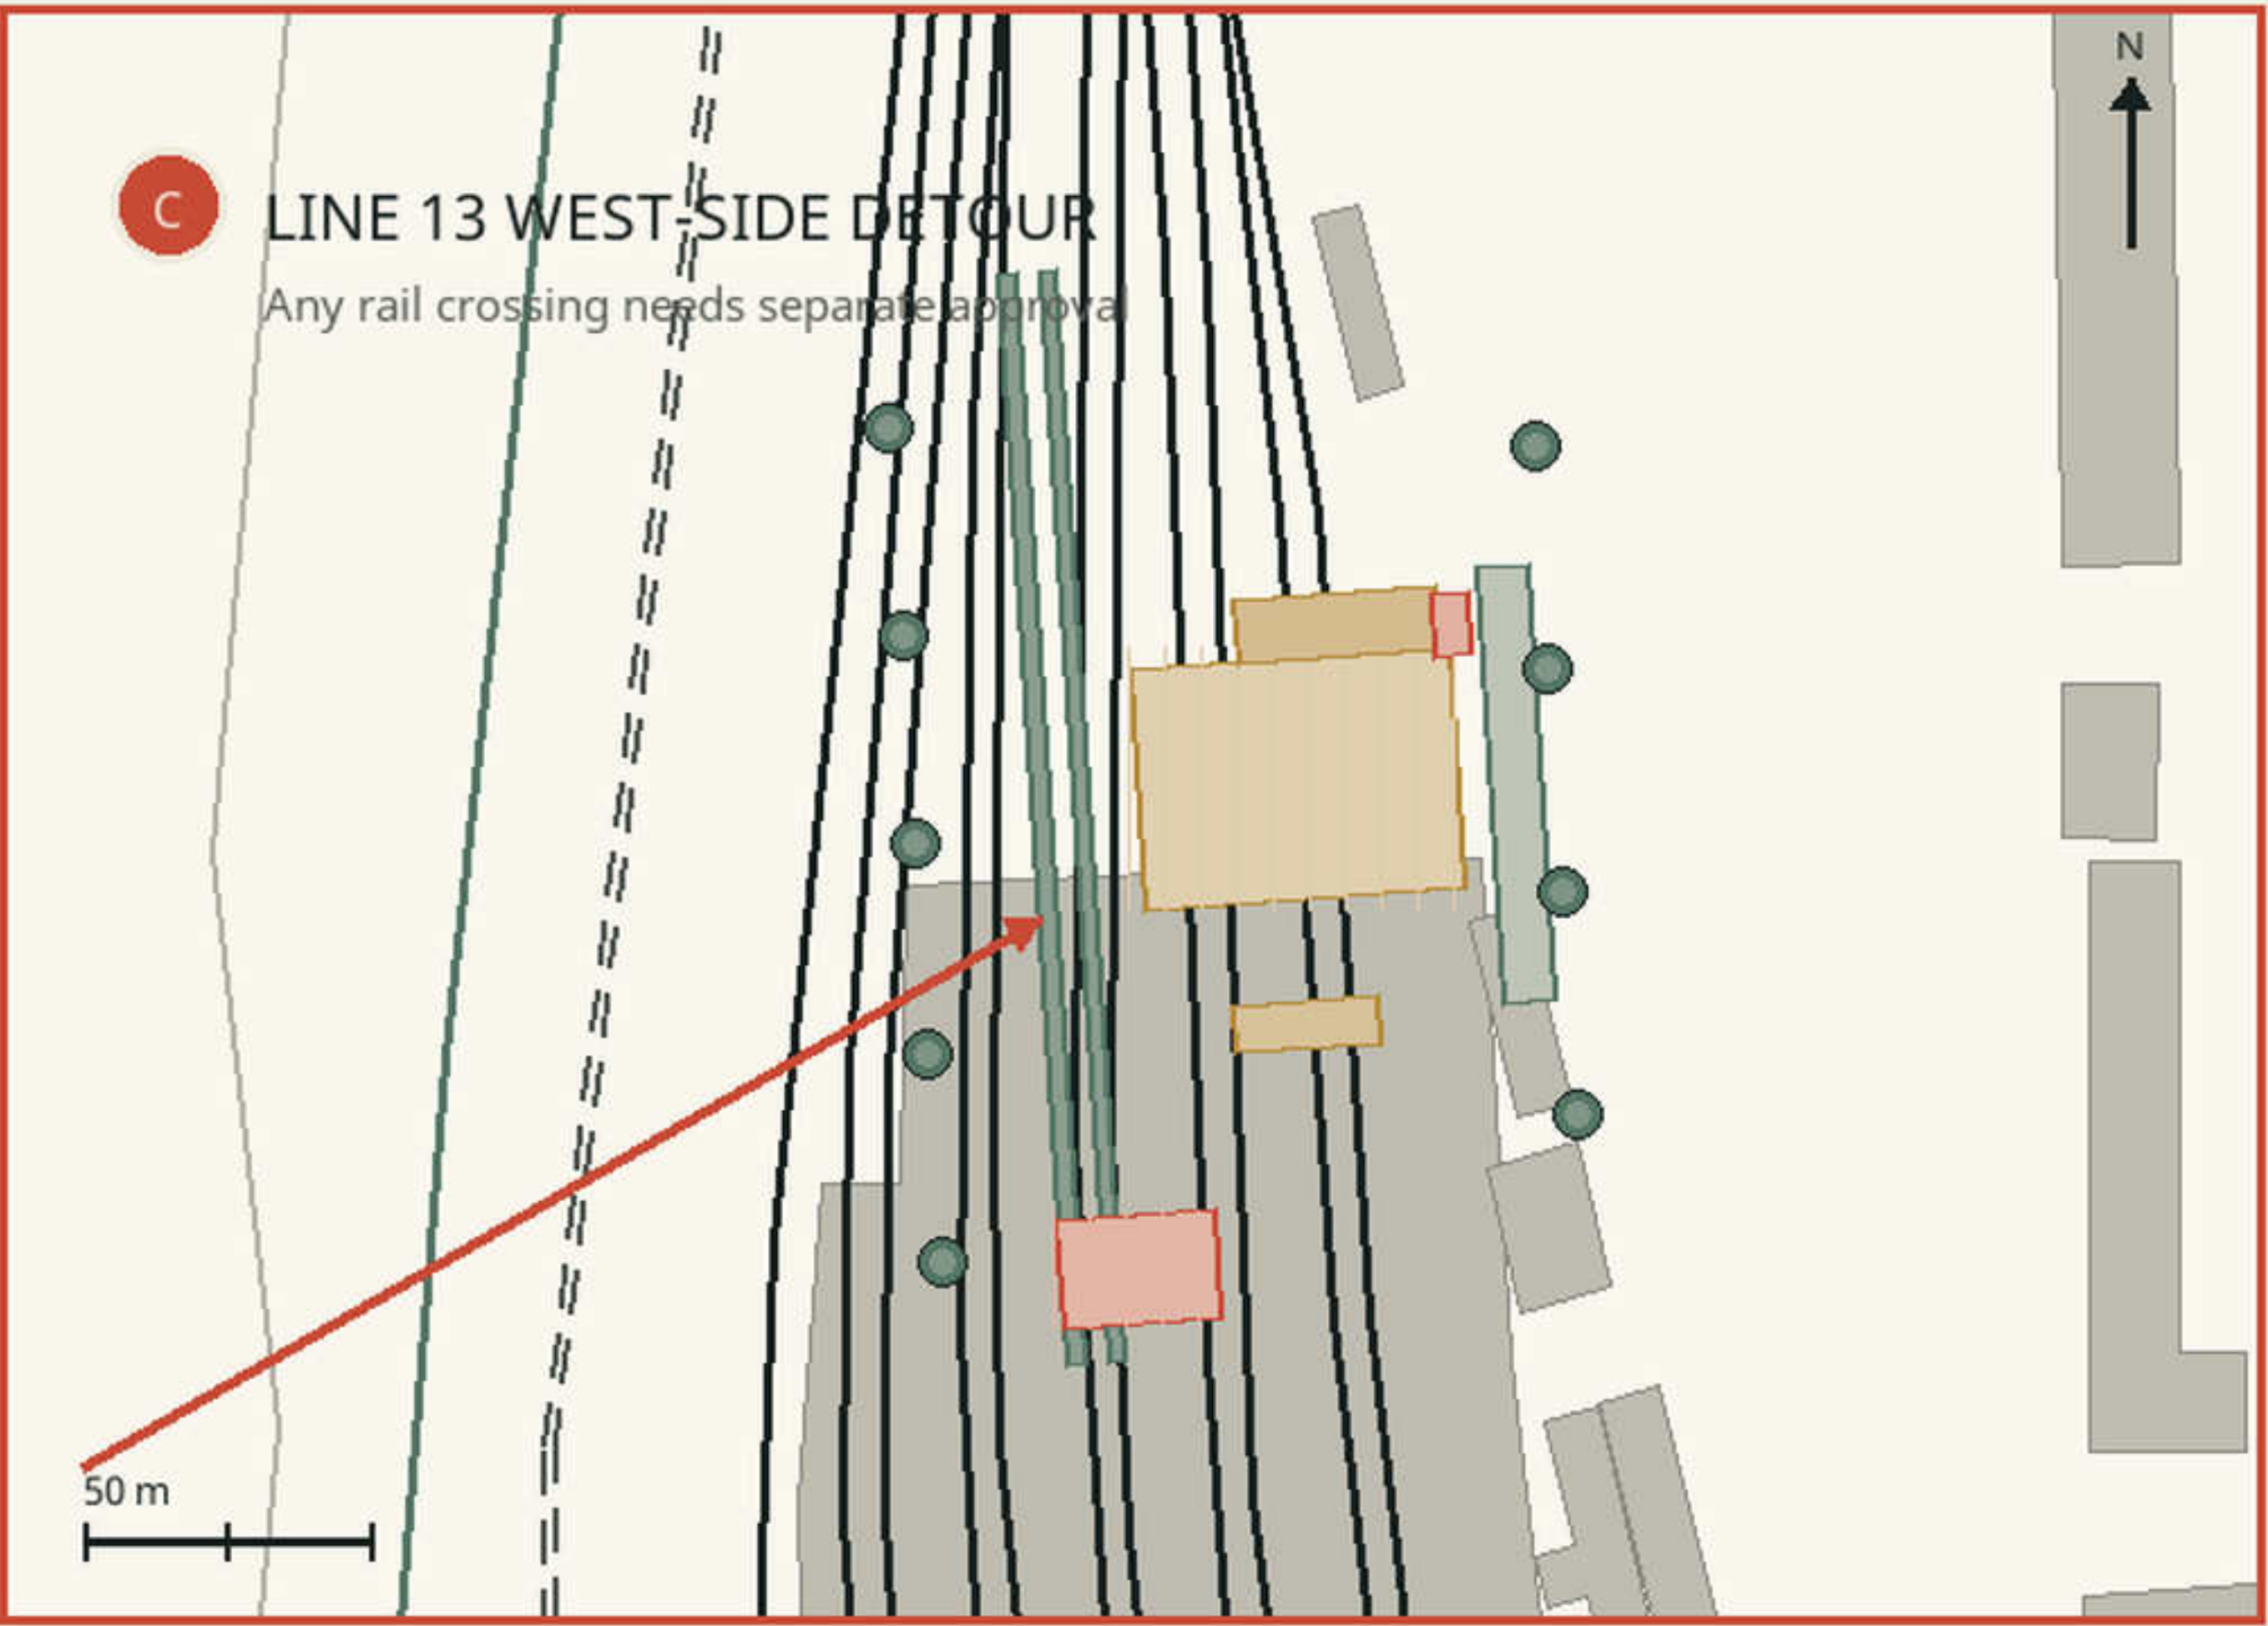
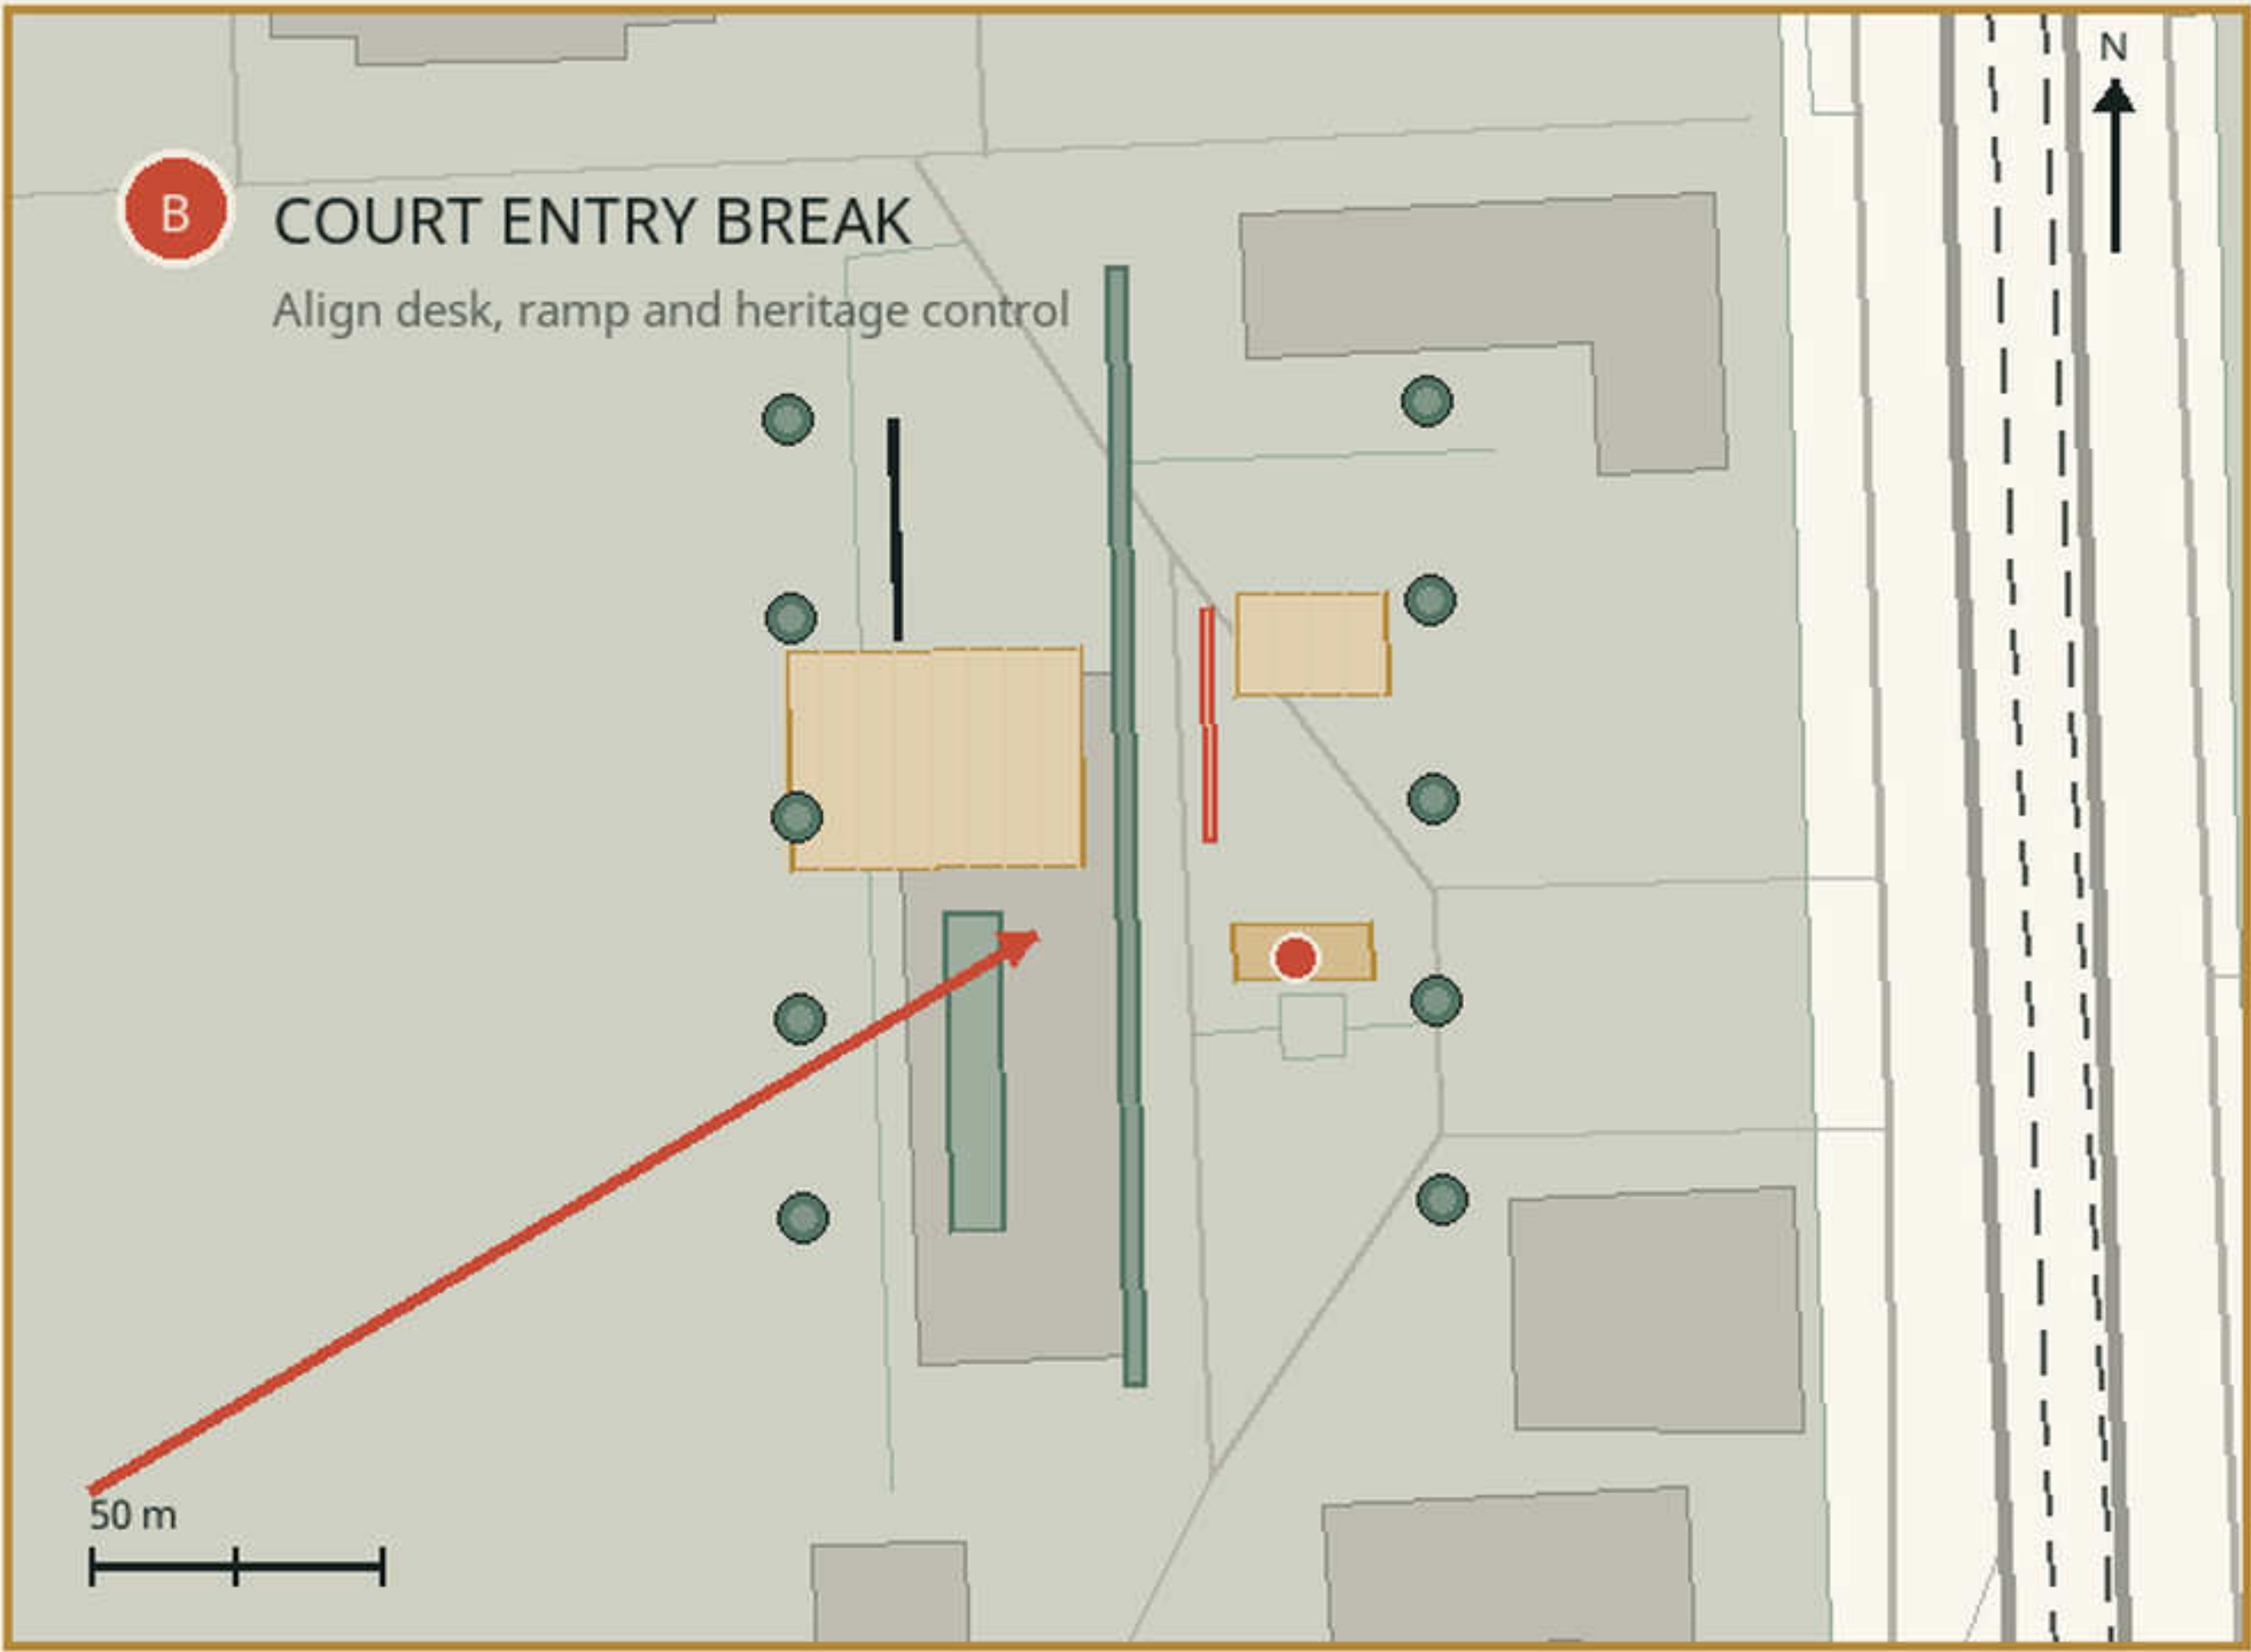


01 READ THE NINE KILOMETRES

Real context, public project status and three breaks on one drawing

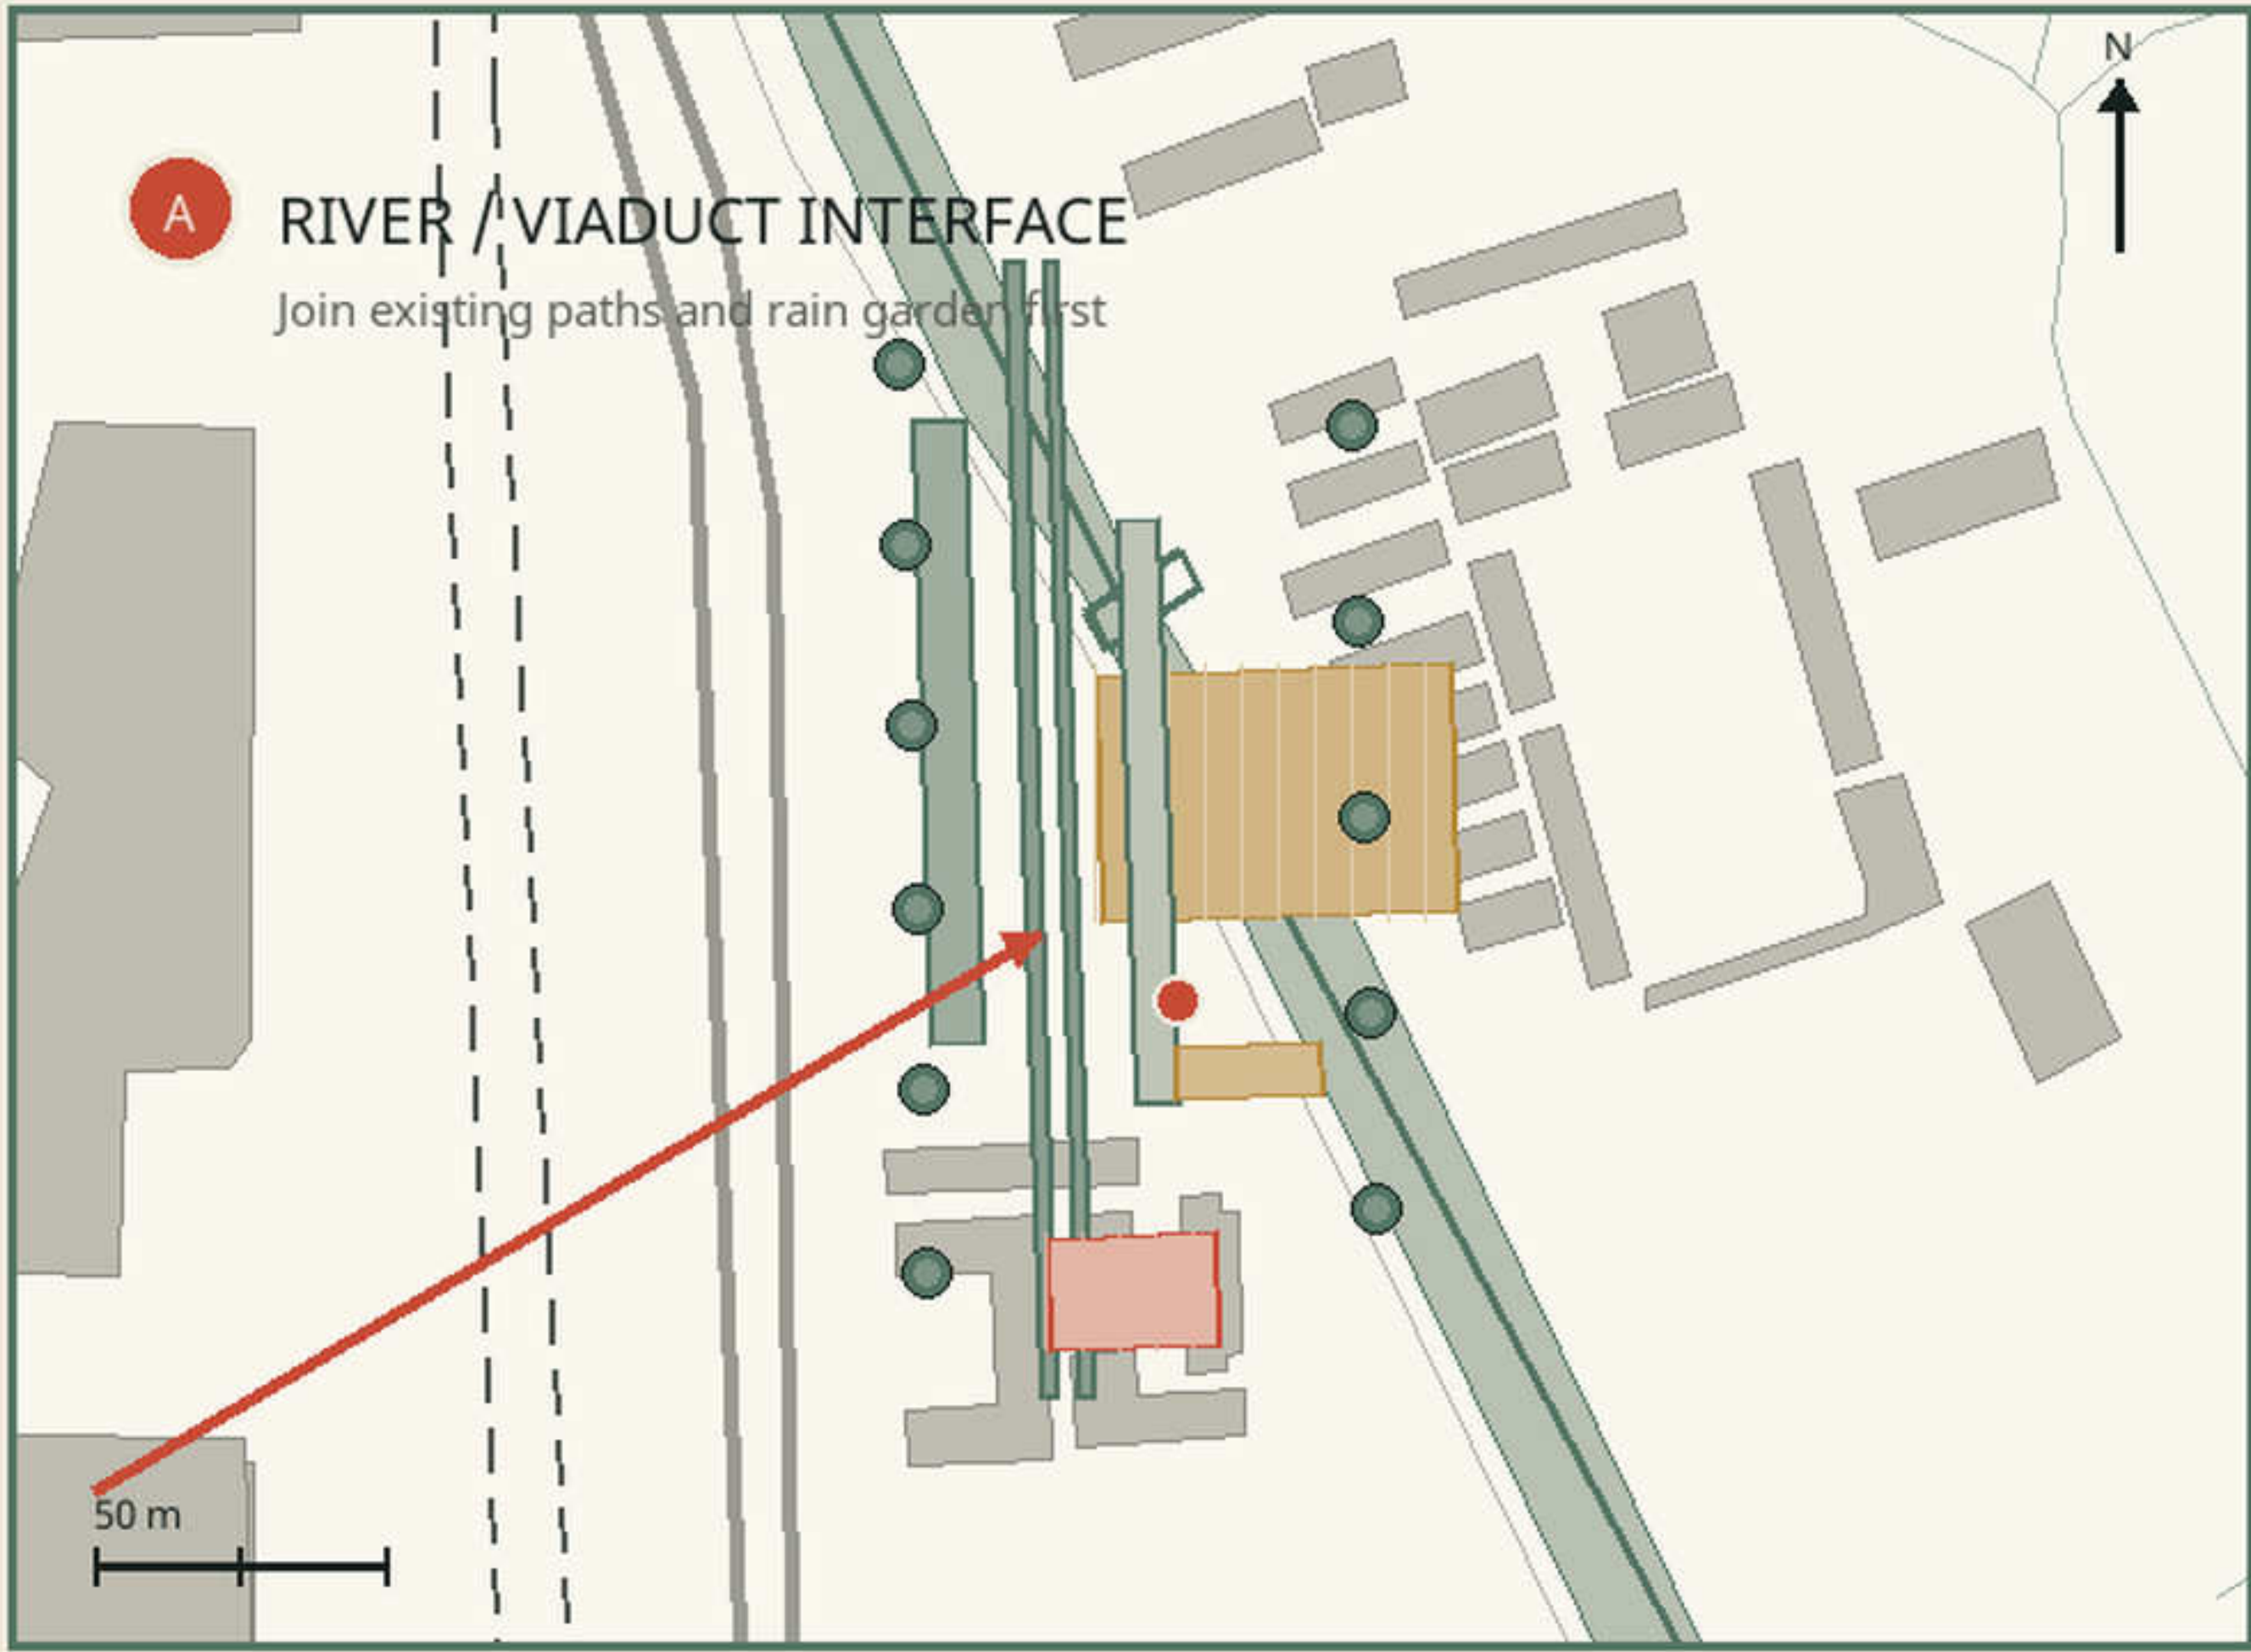

OSM context only | Concept boundaries require survey, ownership and approvals

STATUS CUT-OFF 2026-08 | PROVISIONAL / CONTEXT ONLY

BUILT
Phase I public reporting uses the 2.4 km and 16.8 ha definition.

UNDER WAY
Phase II and the project south of Qinghua East Road retain published status.







PROPOSED HERE
Only entrances, crossings, river access, and three courtyards are added.

APPROVAL NEEDED
Rail, heritage, water, and municipal interfaces are not shown as built.

03 THREE COURTYARDS IN DETAIL

Landscape plans at approx. 1:500 with matching AA / CC / EE sections

WALK CYCLE RAIN ENTRY / OBJECTS EXISTING EDGE

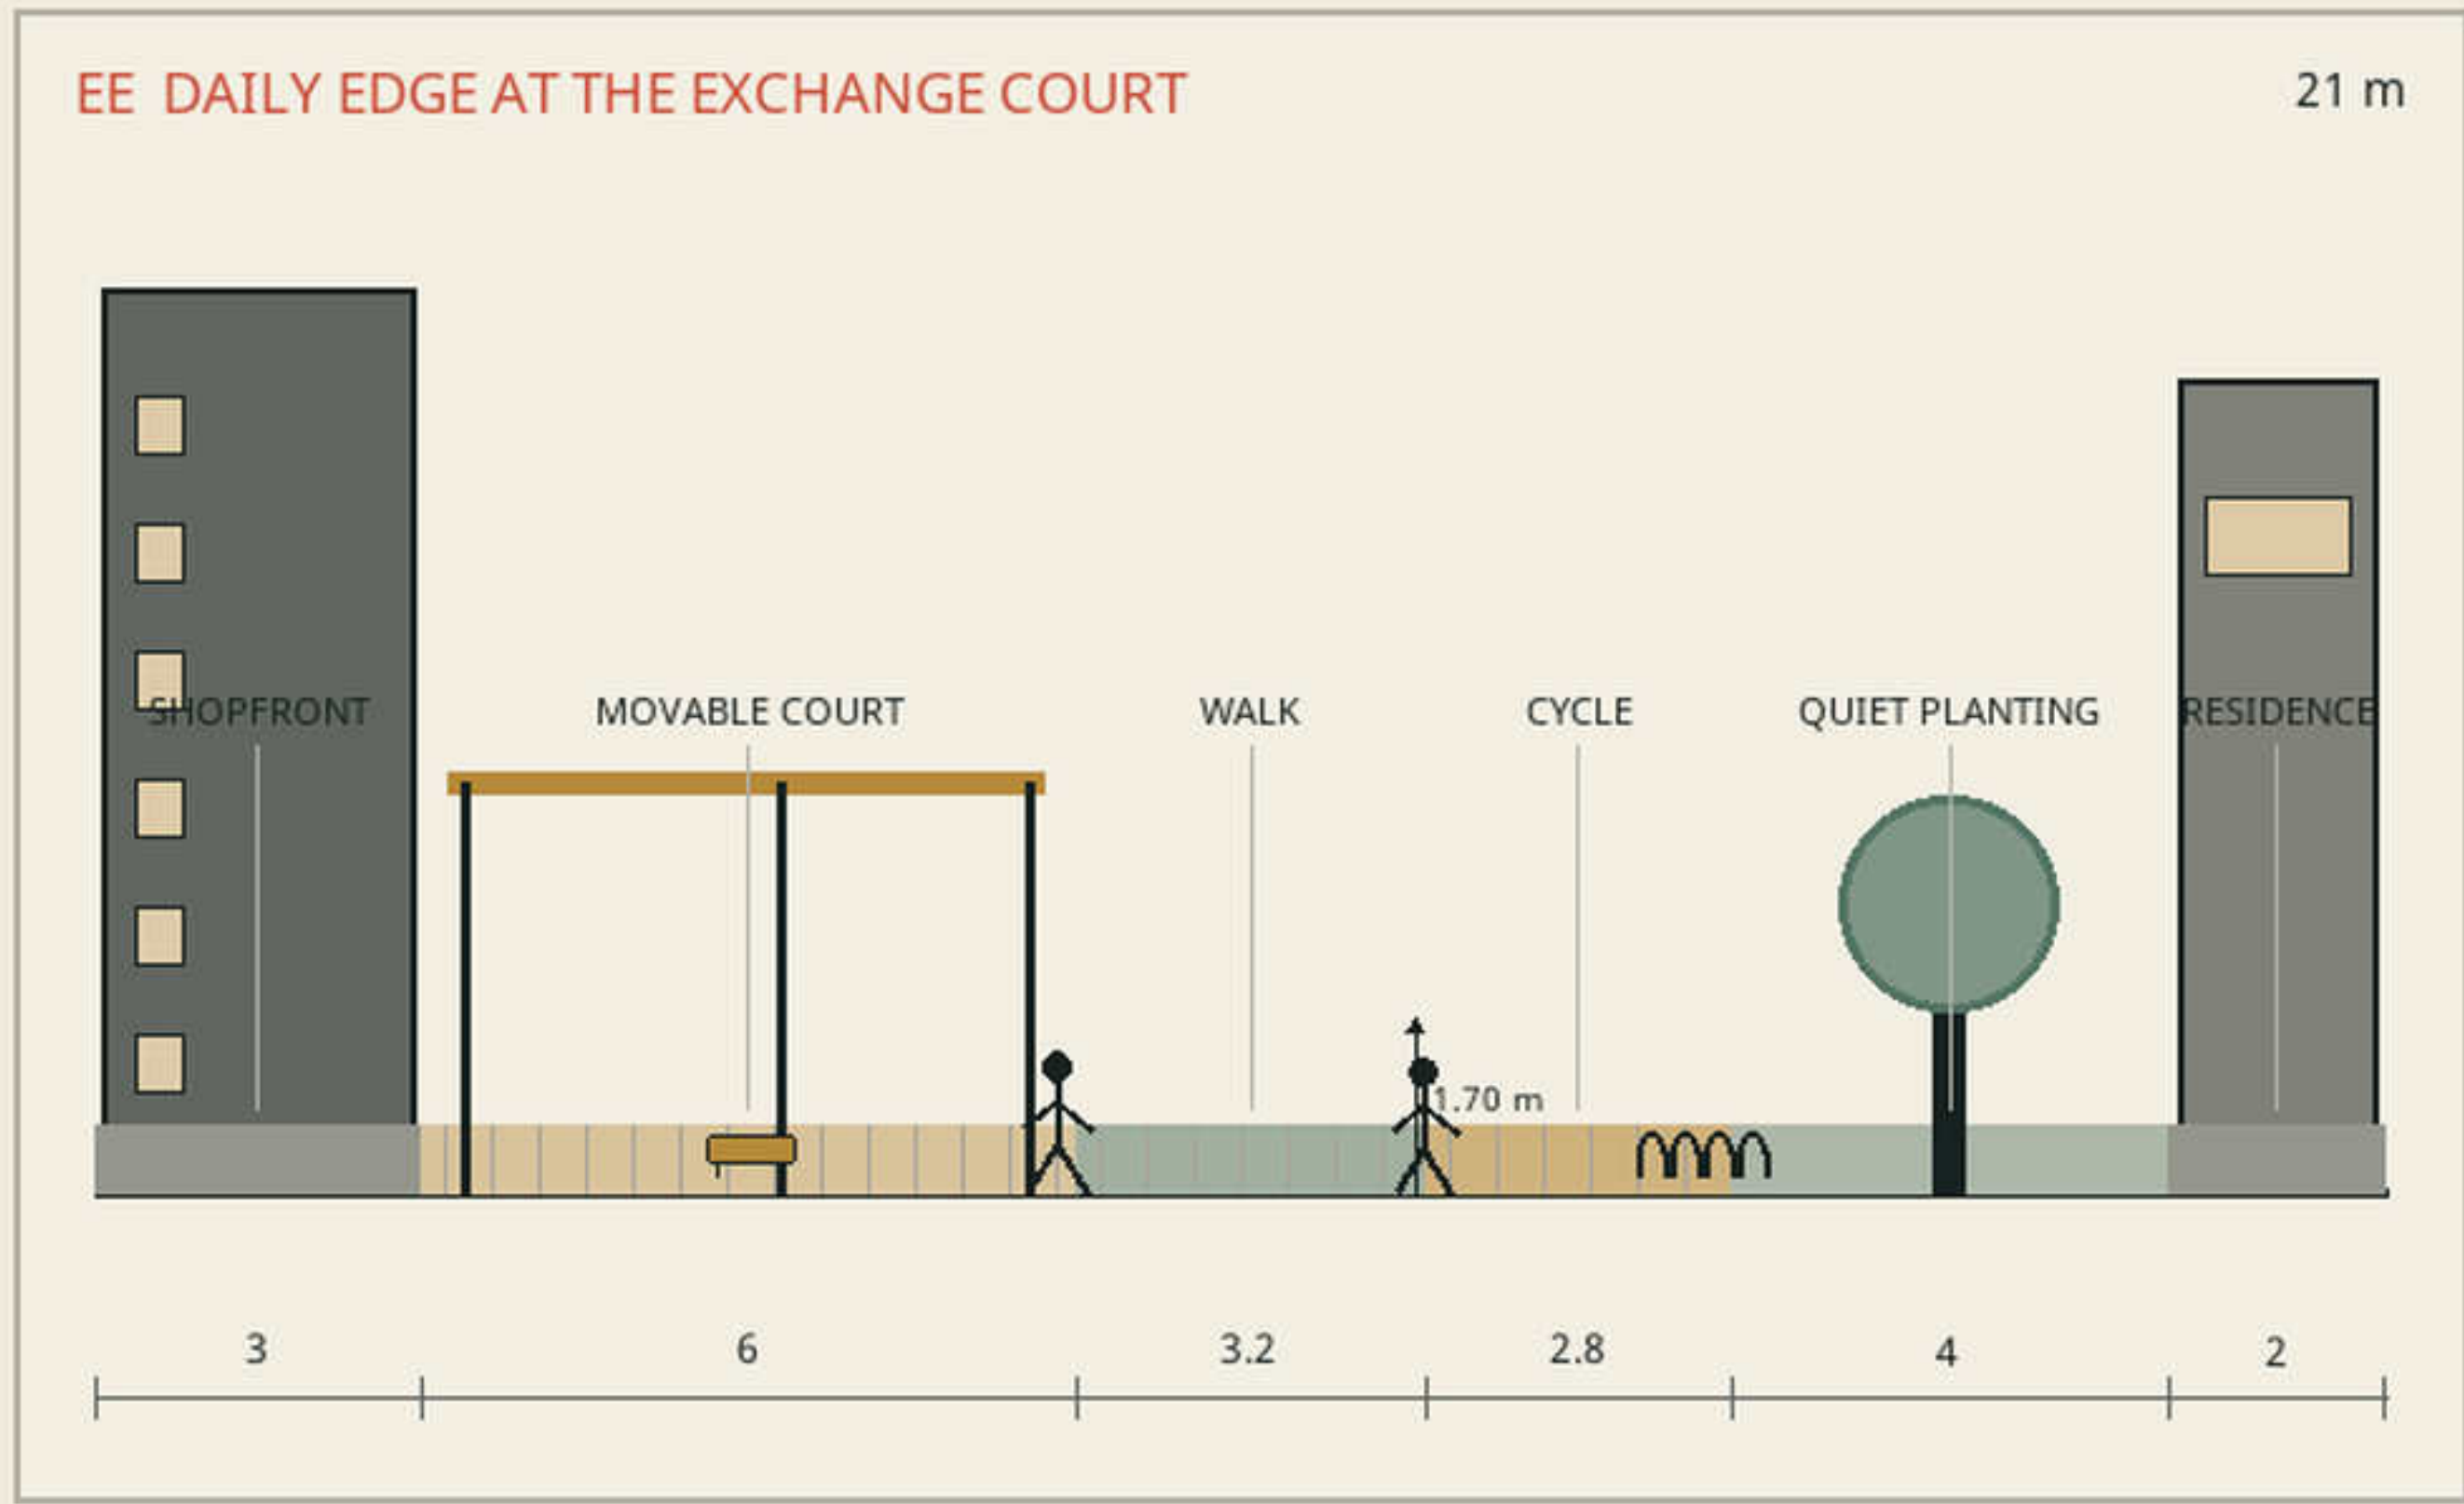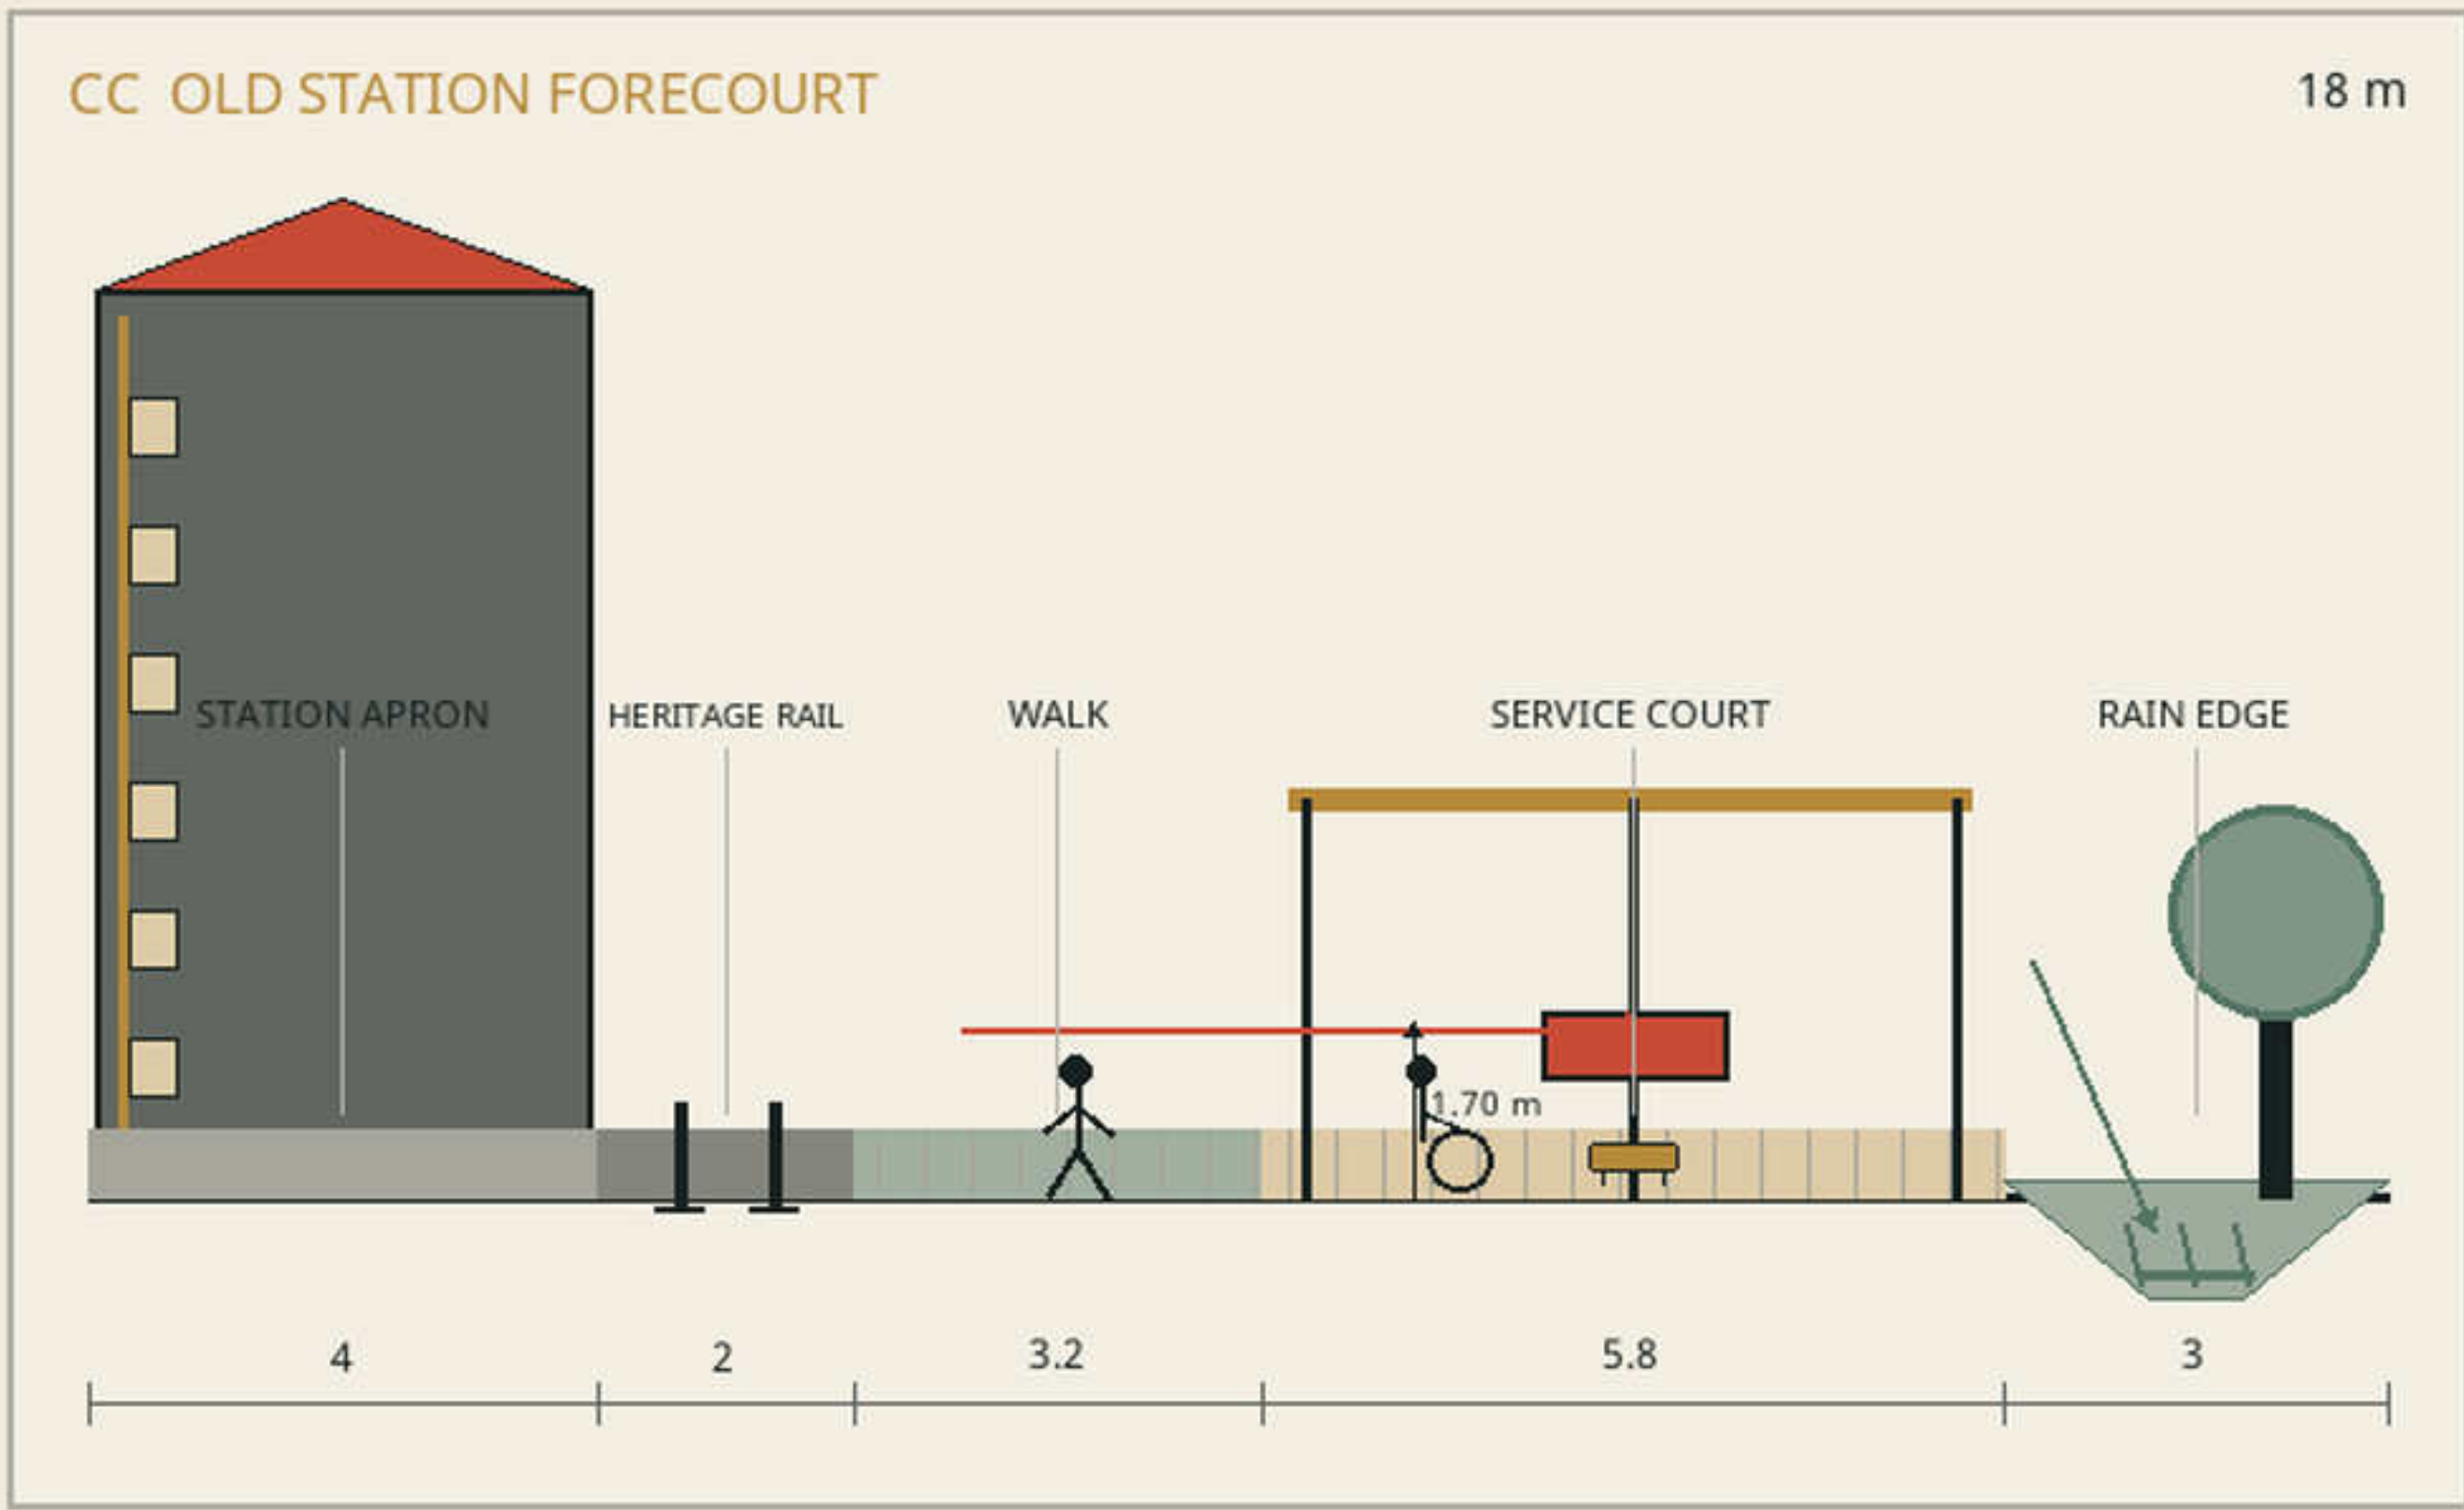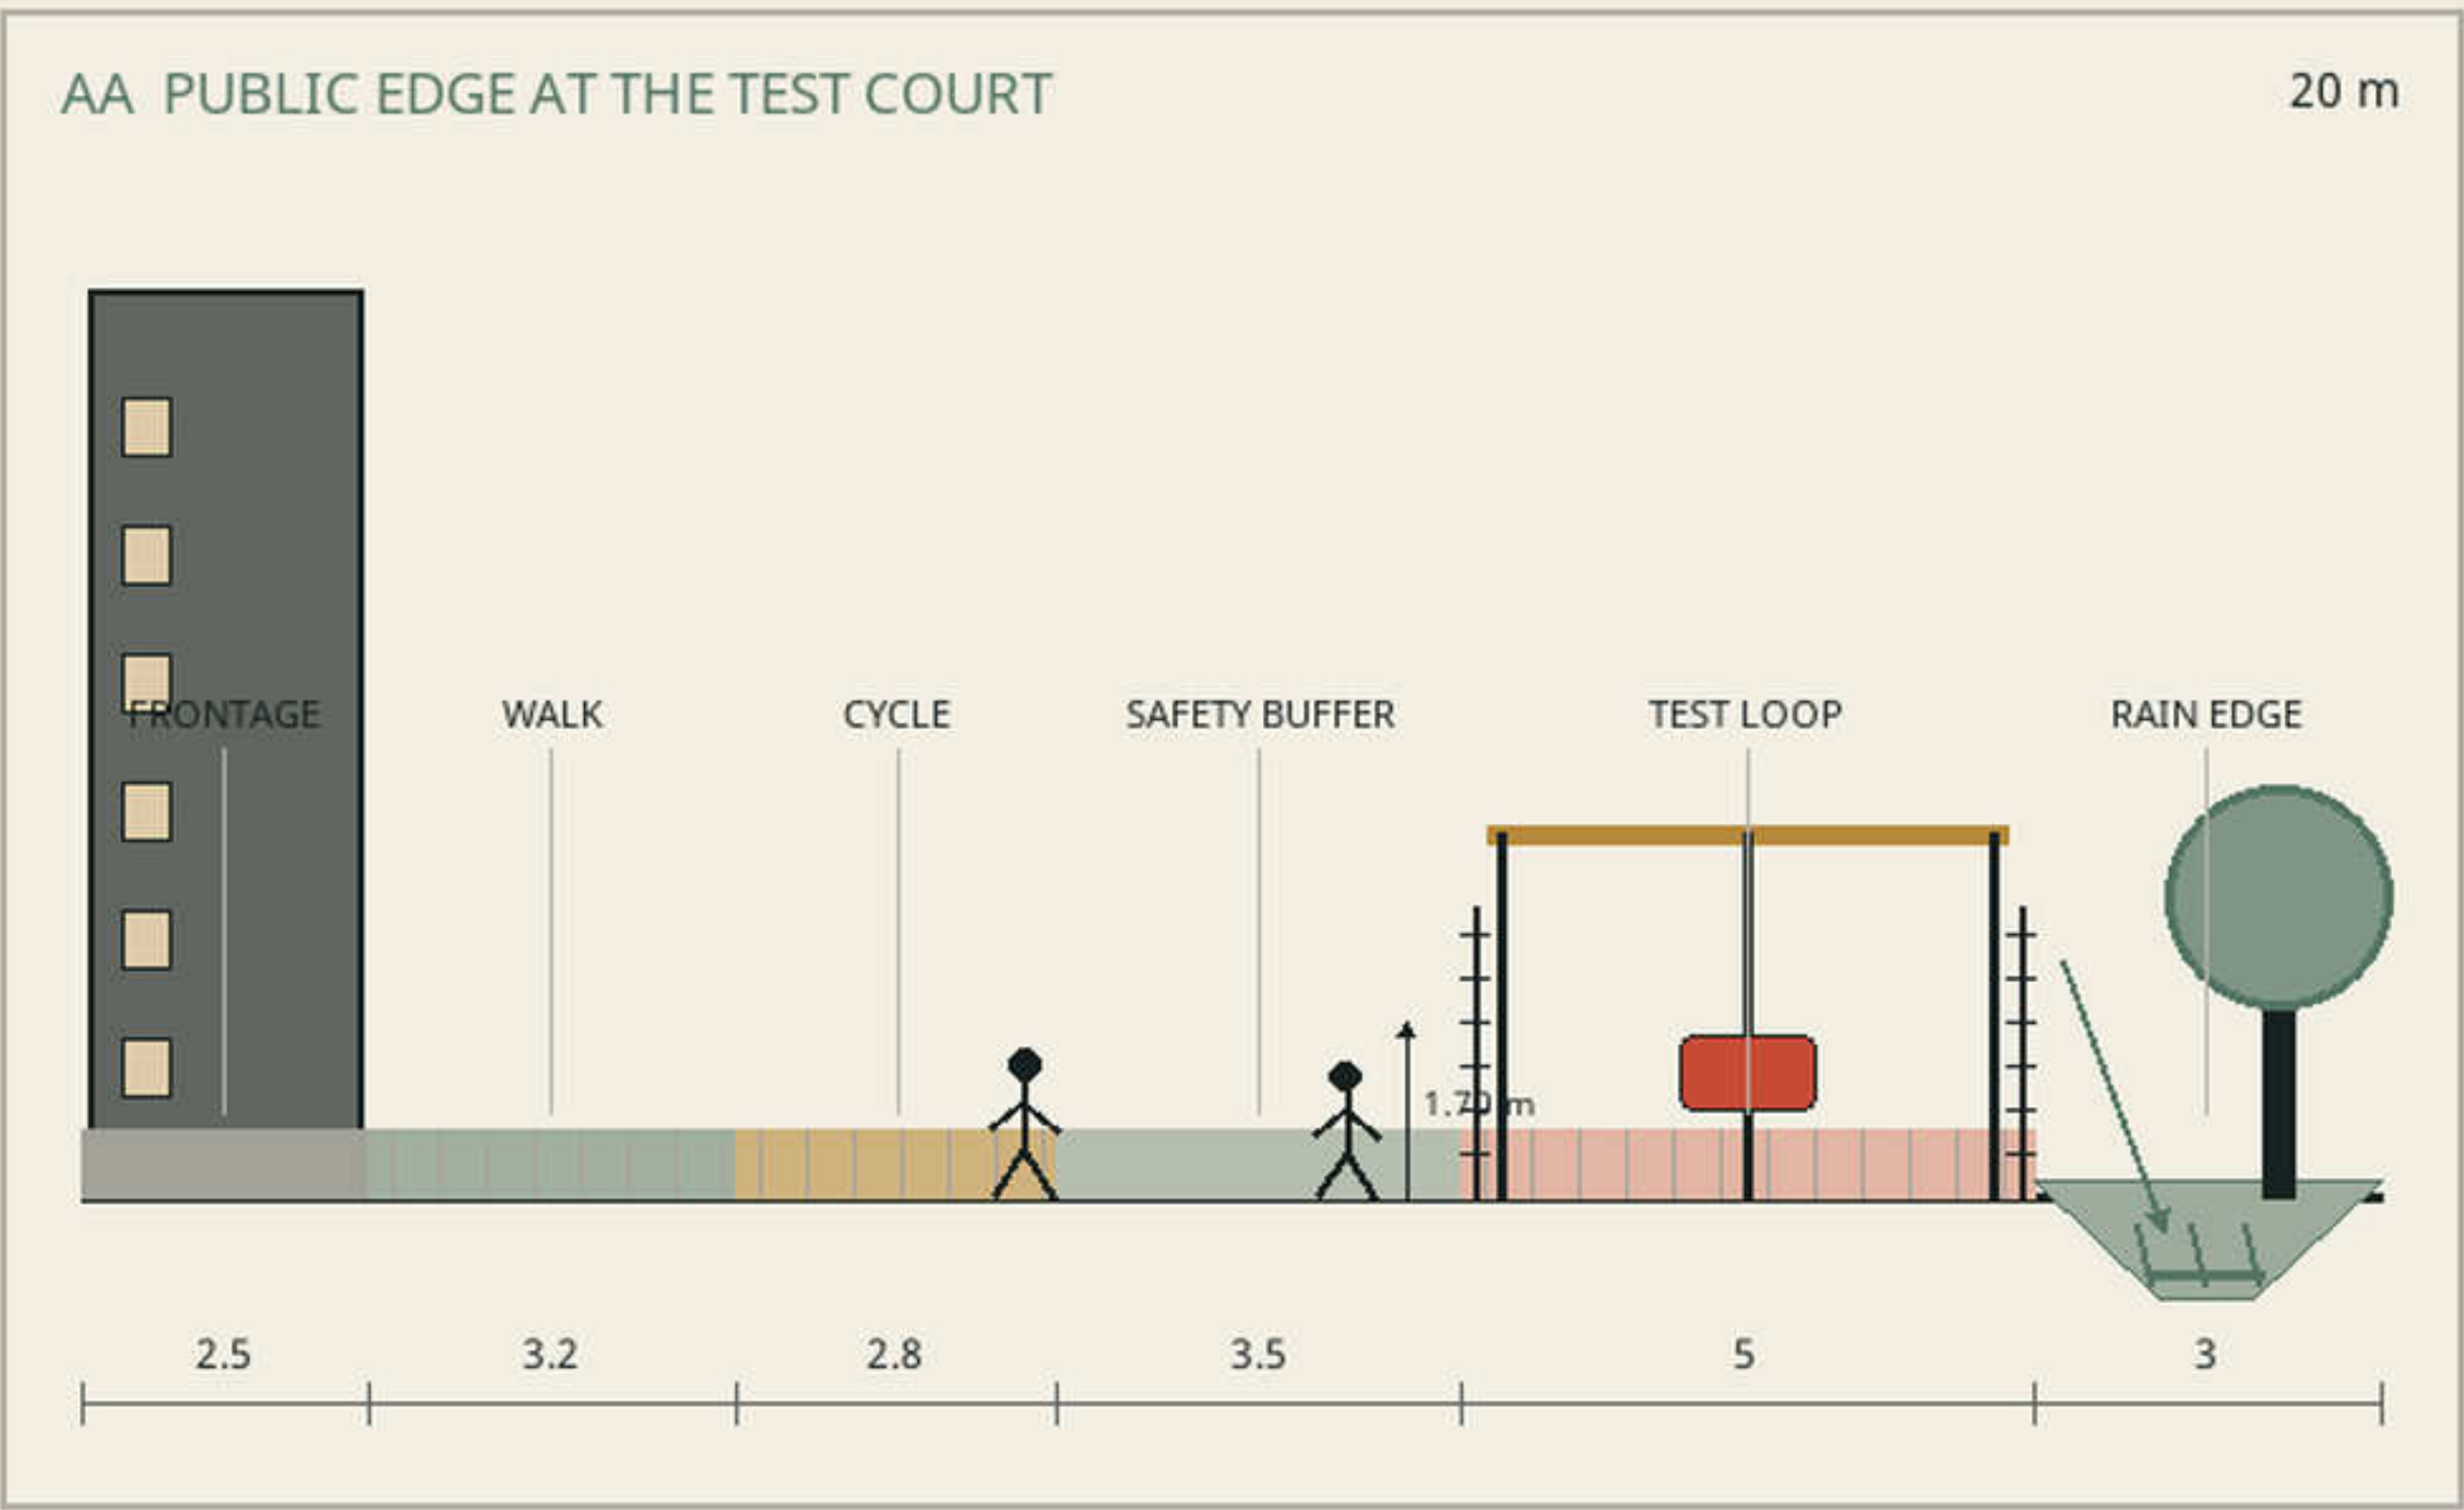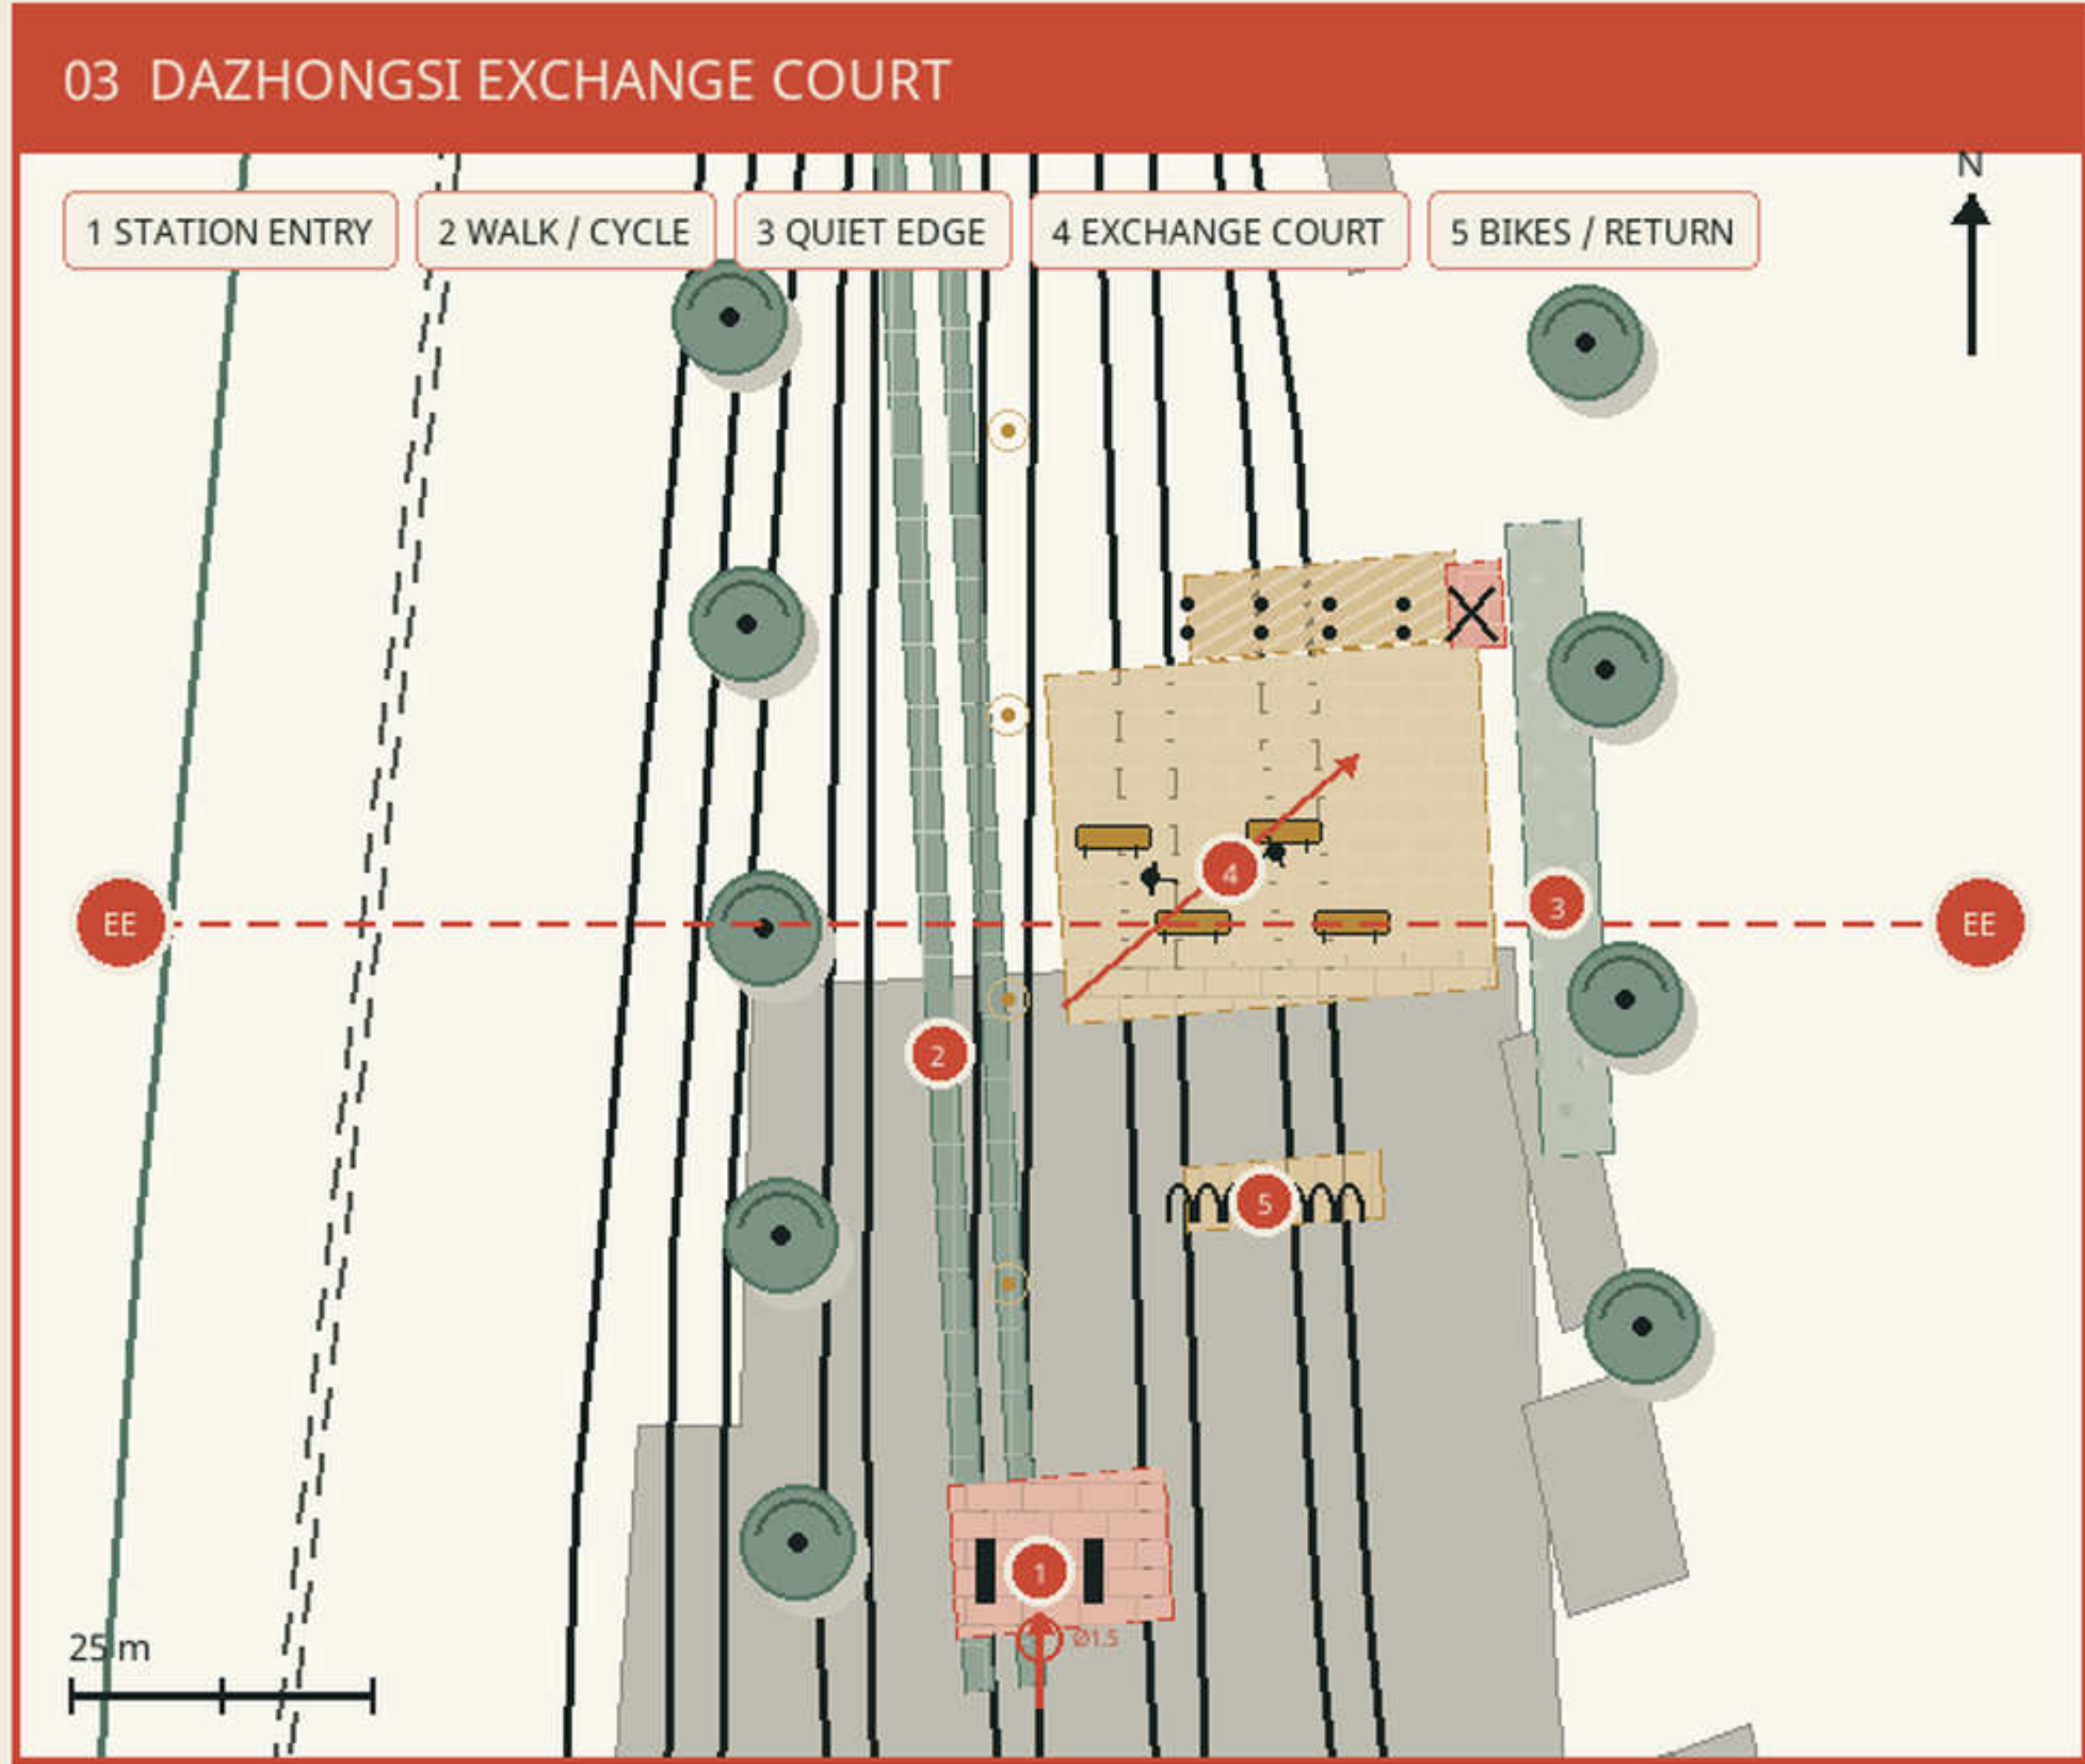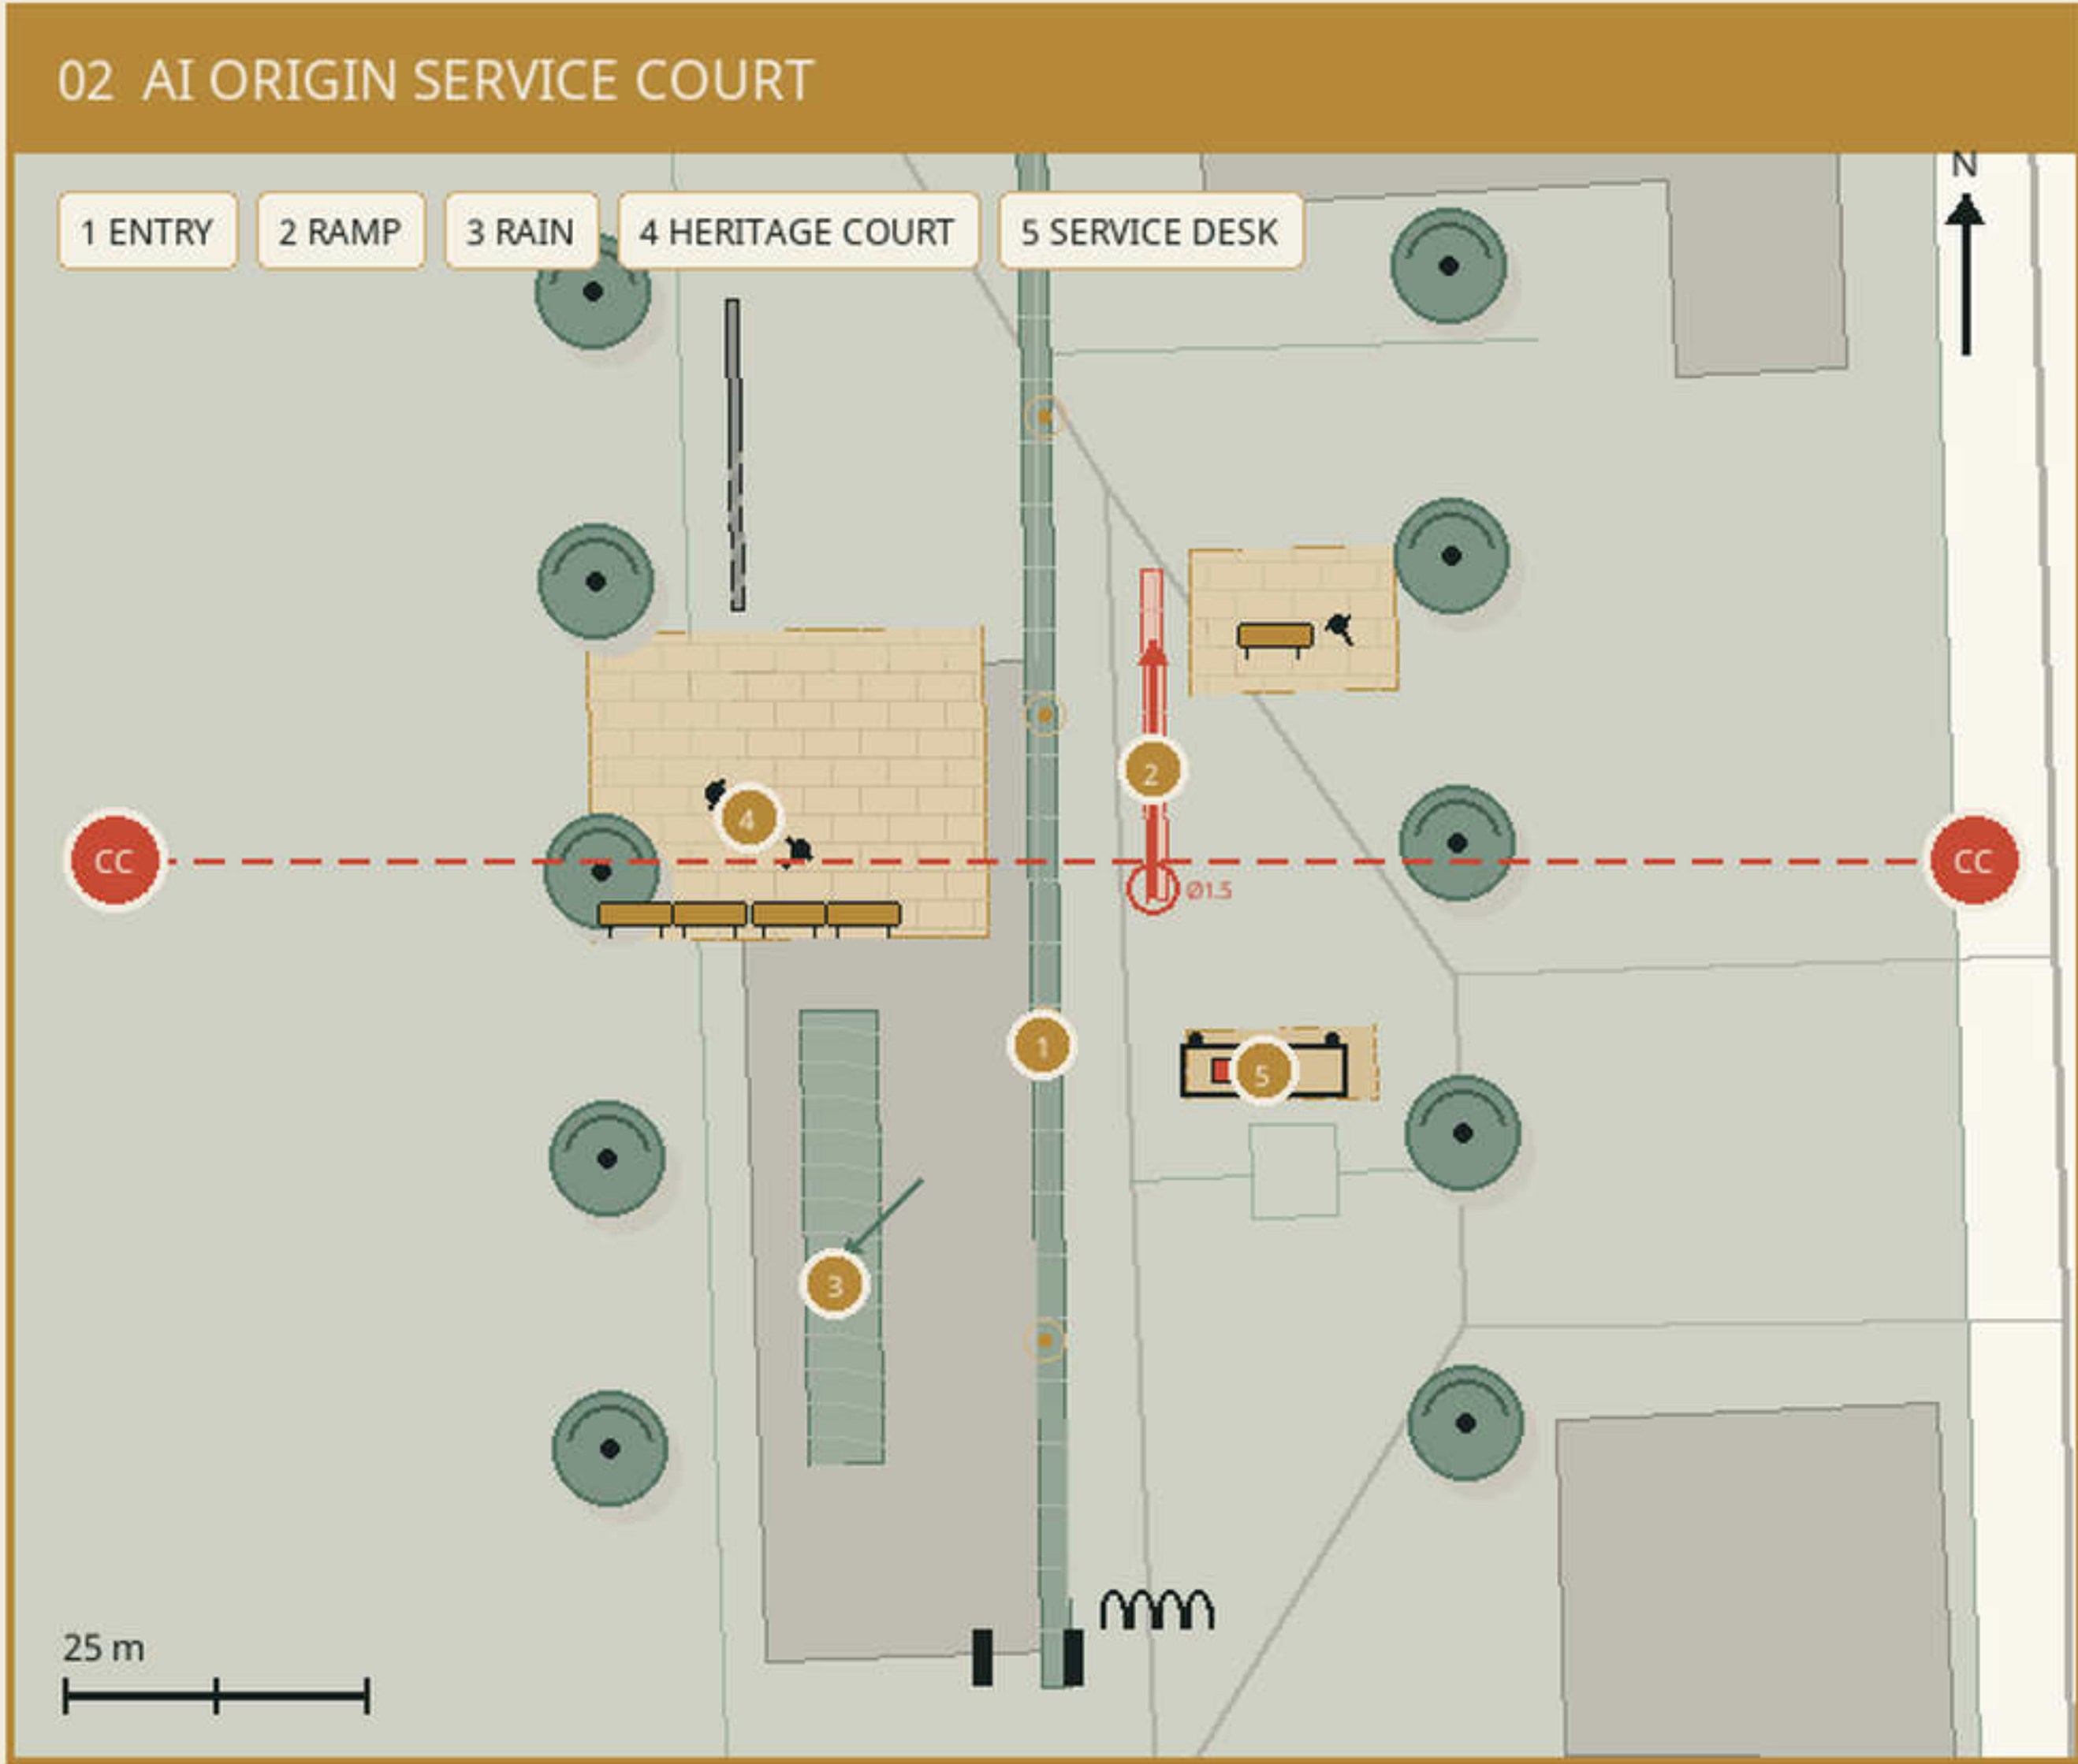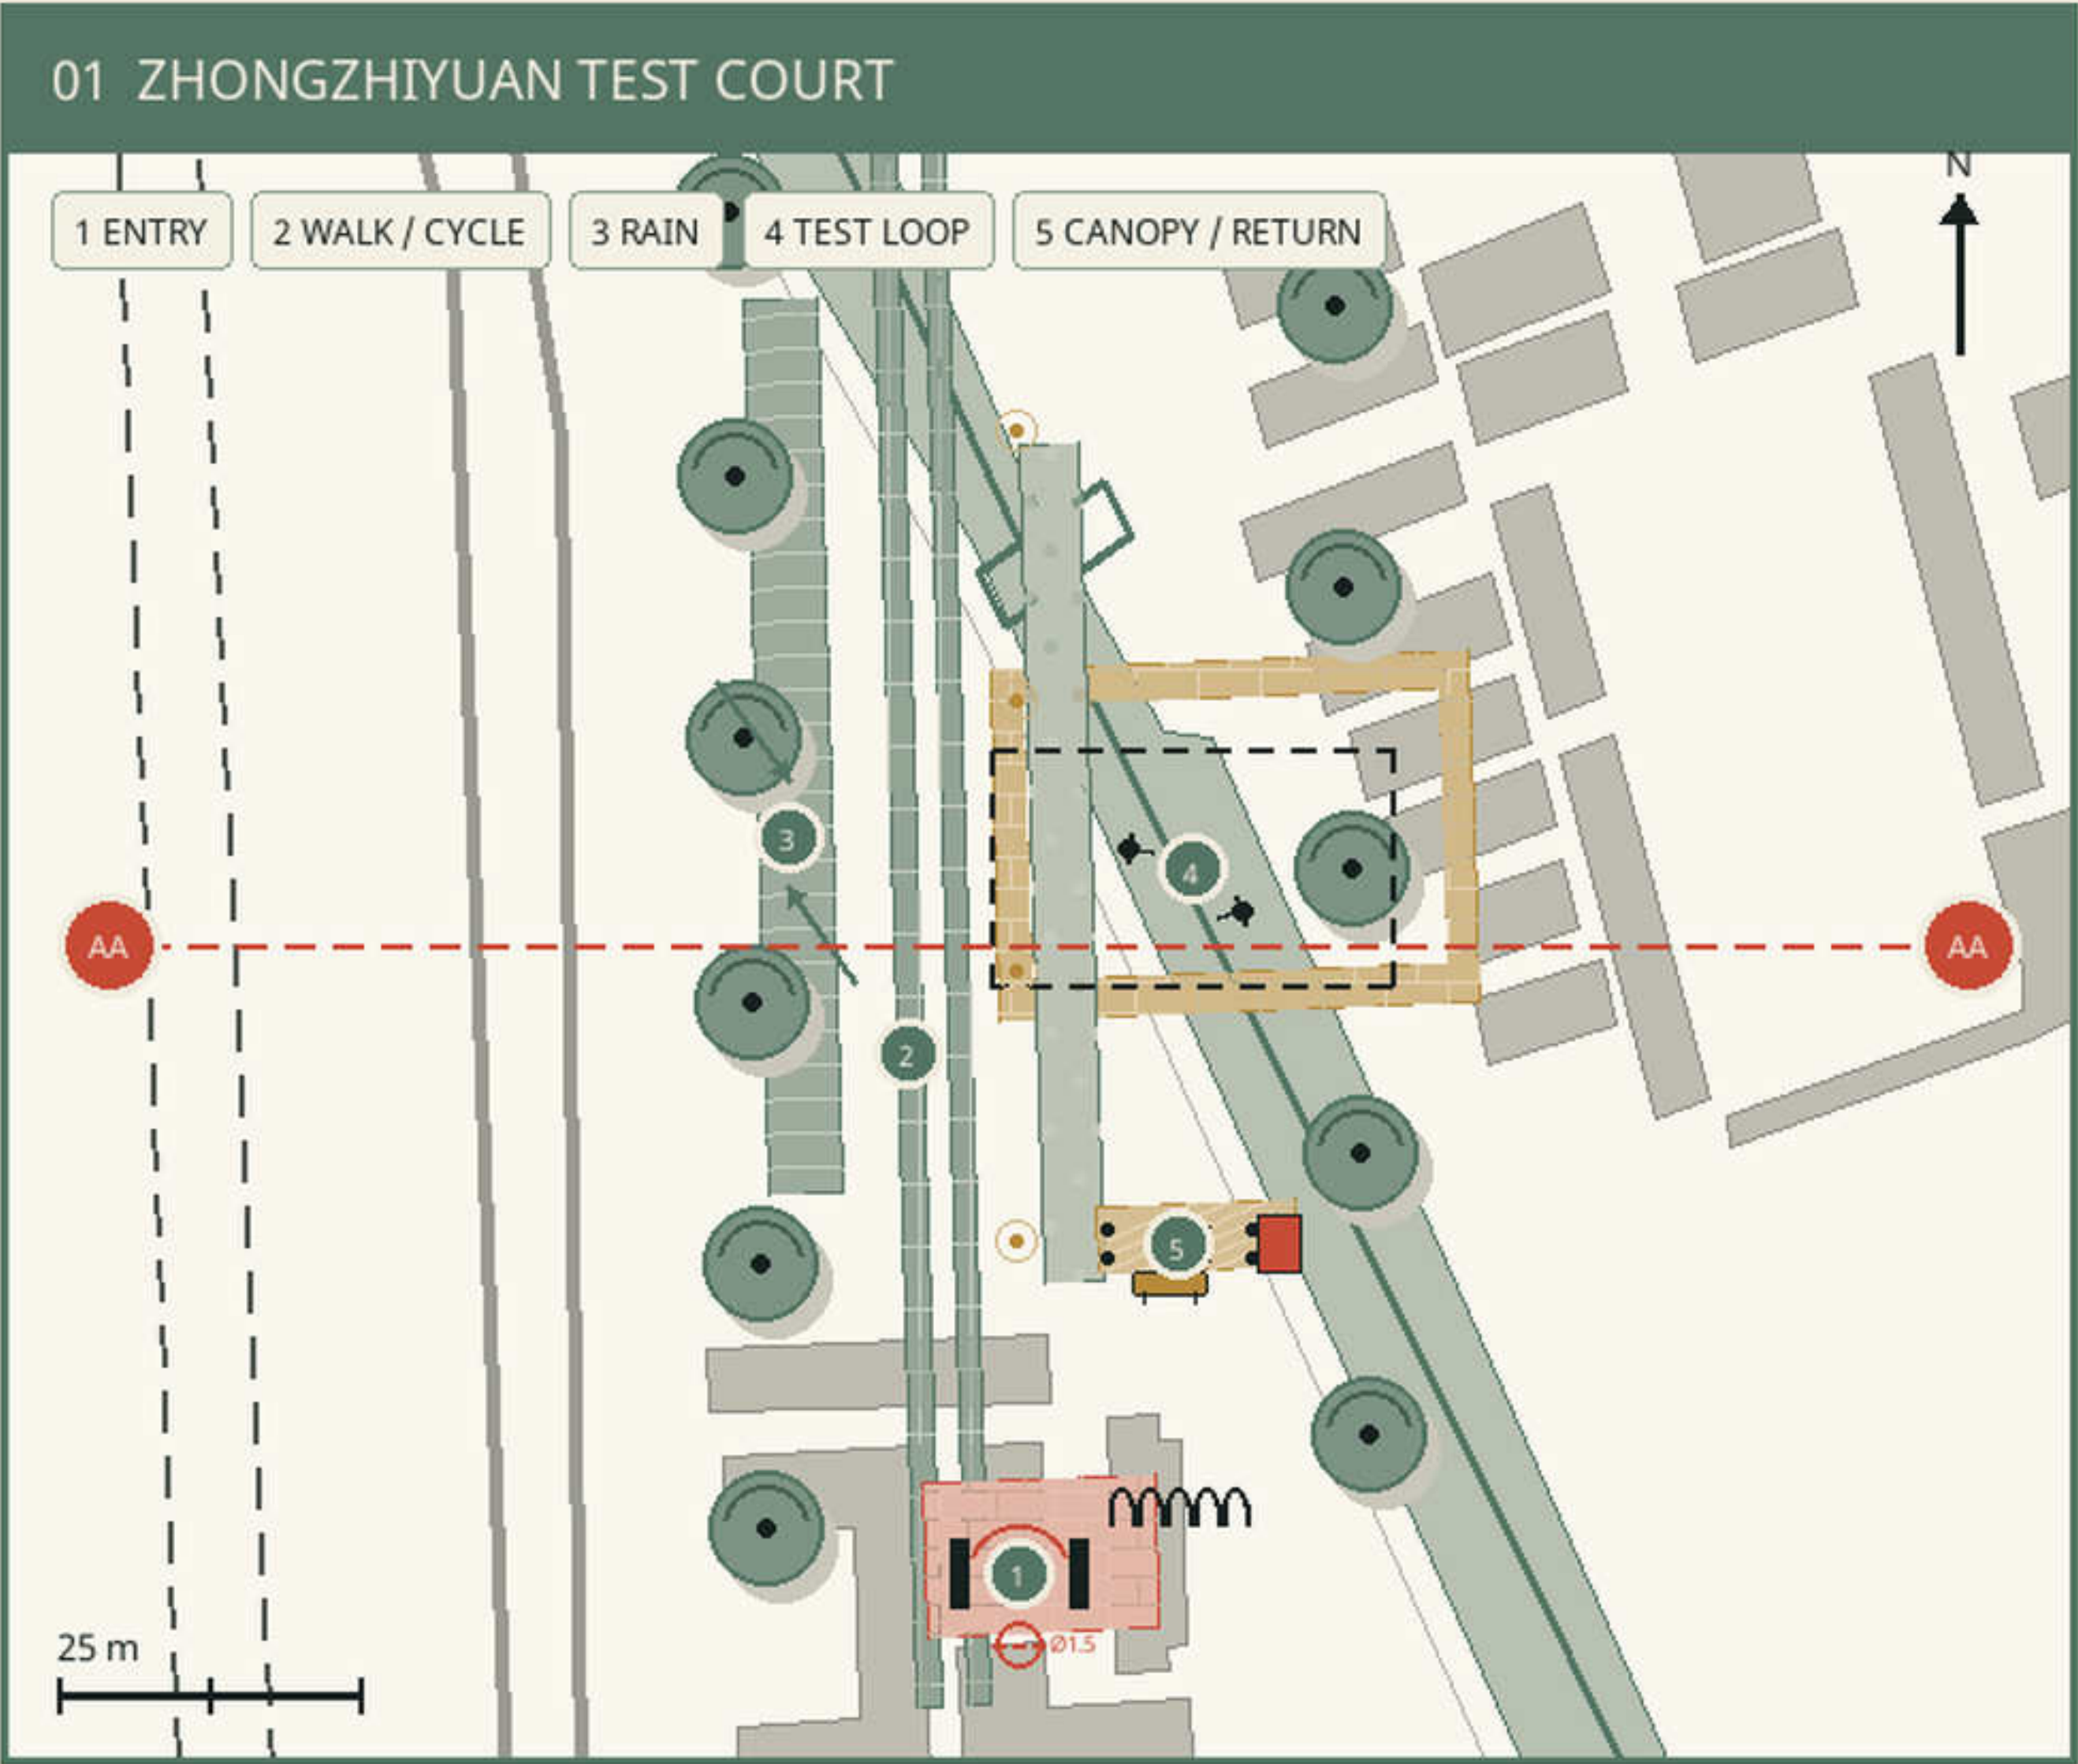

OSM context only | Concept boundaries require survey, ownership and approvals

approx. 1:500 | WORKING DIMENSIONS | CONCEPT DESIGN



ZHONGZHIYUAN / CONTAINED TEST - PUBLIC OUTER PATH



AILONG / A STAFFED STREET-SIDE SERVICE



DAZHONGSI / PEAK ACCESS - EVENING CLASSES

CONCEPT VIEW / NOT EVIDENCE OF EXISTING CONDITIONS

04 WALKING, CROSSINGS, RAIL AND WATER









Resolve breaks first; six measured sections set access and drainage

WALK / WATER

SLOW CYCLE

STEP-FREE CROSSING

RAIL / APPROVAL

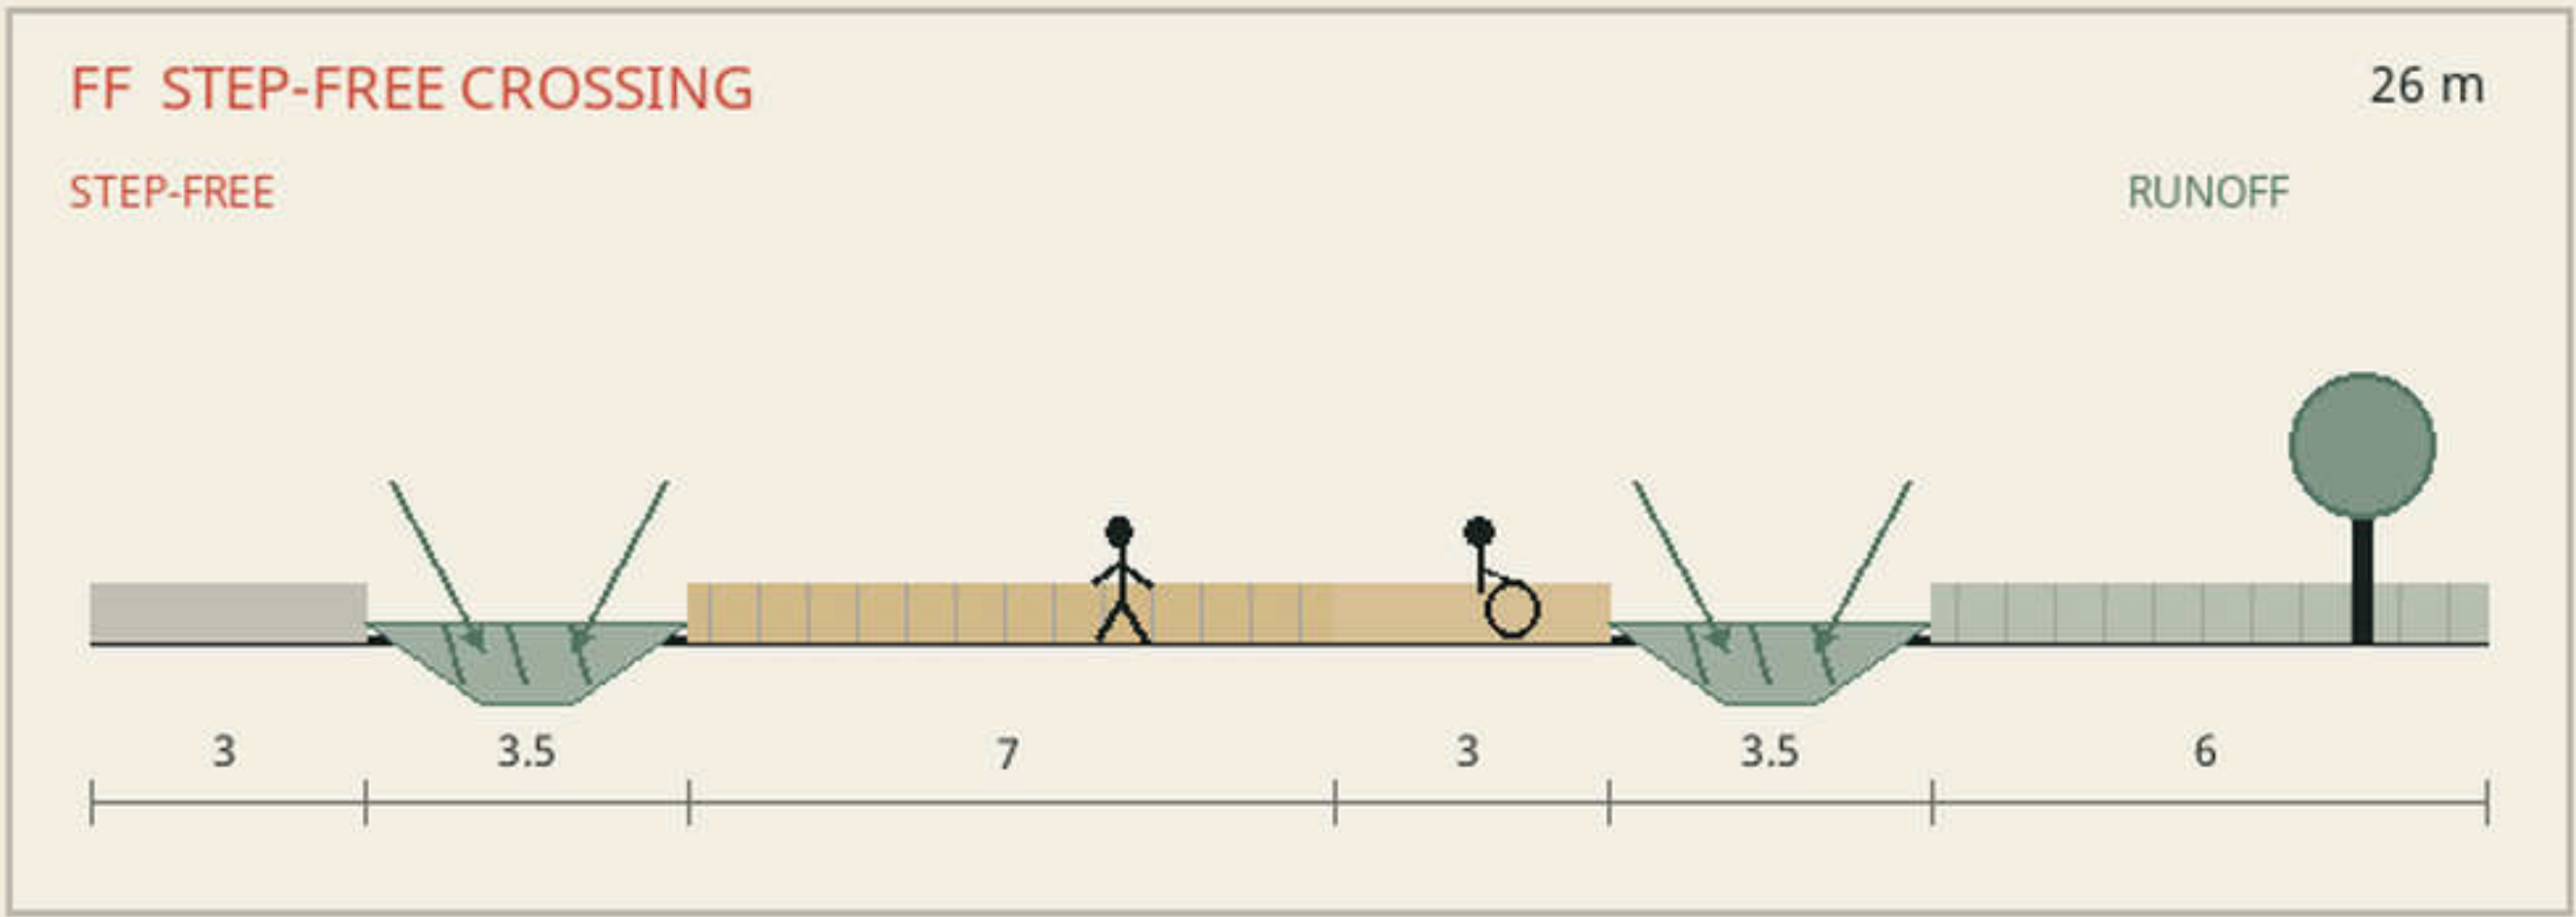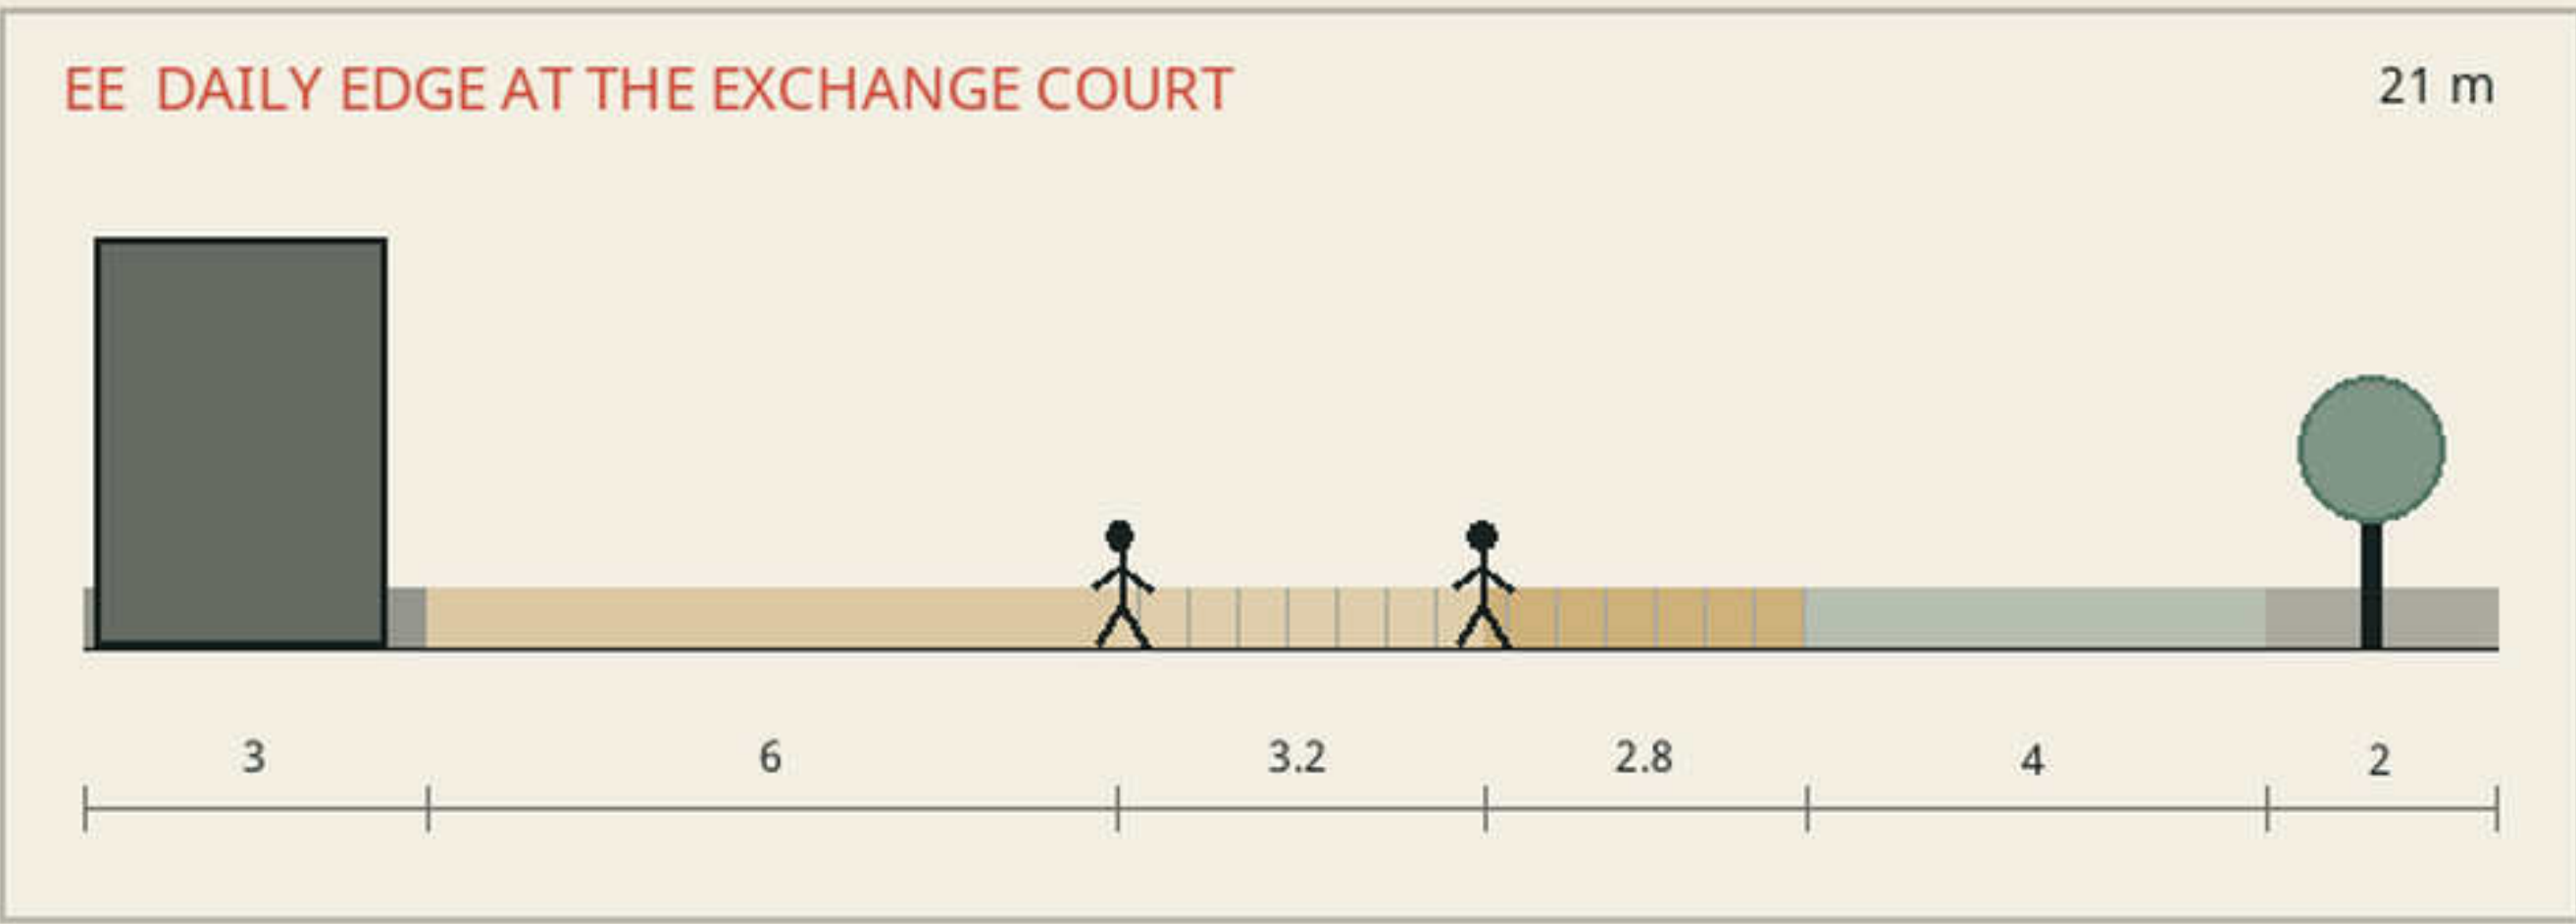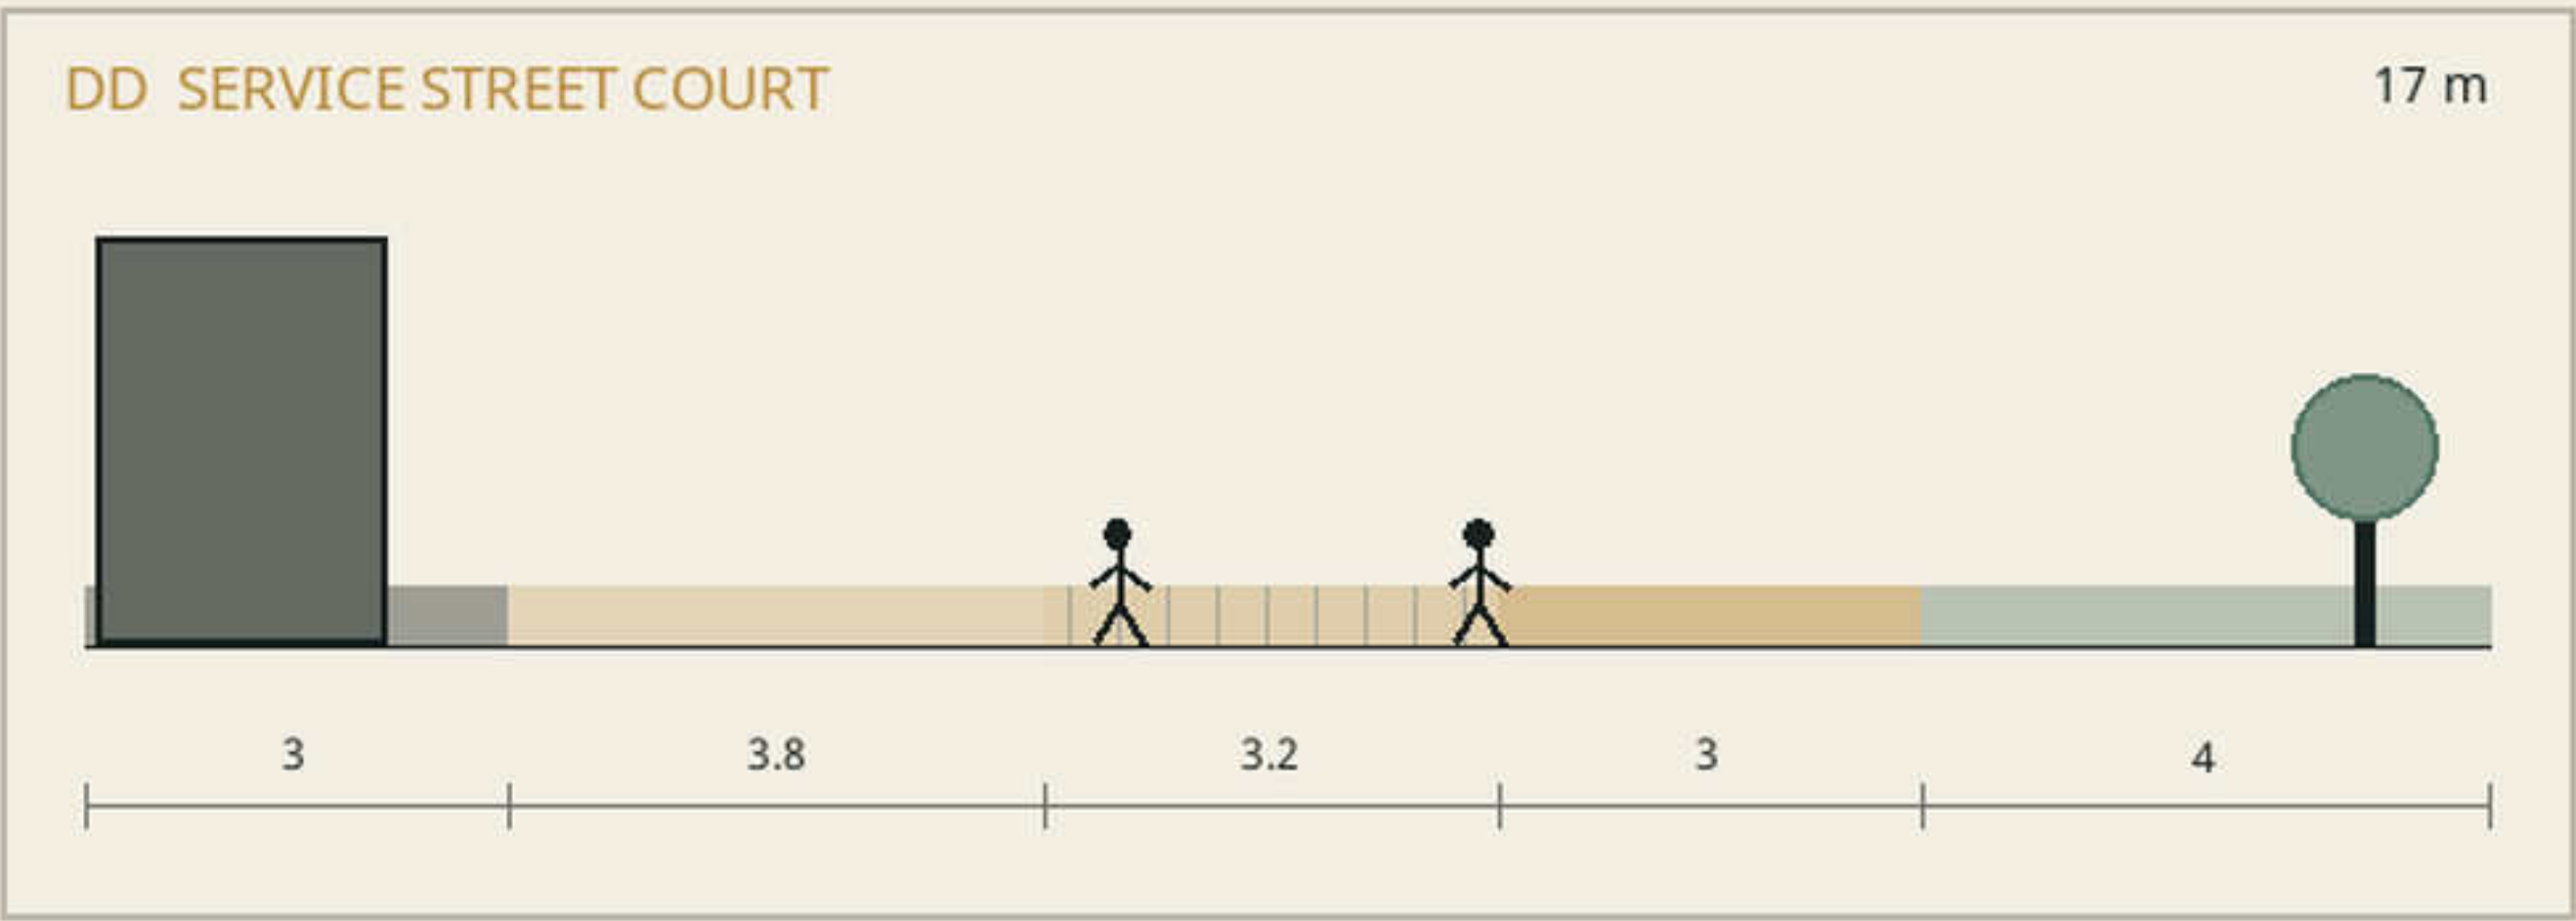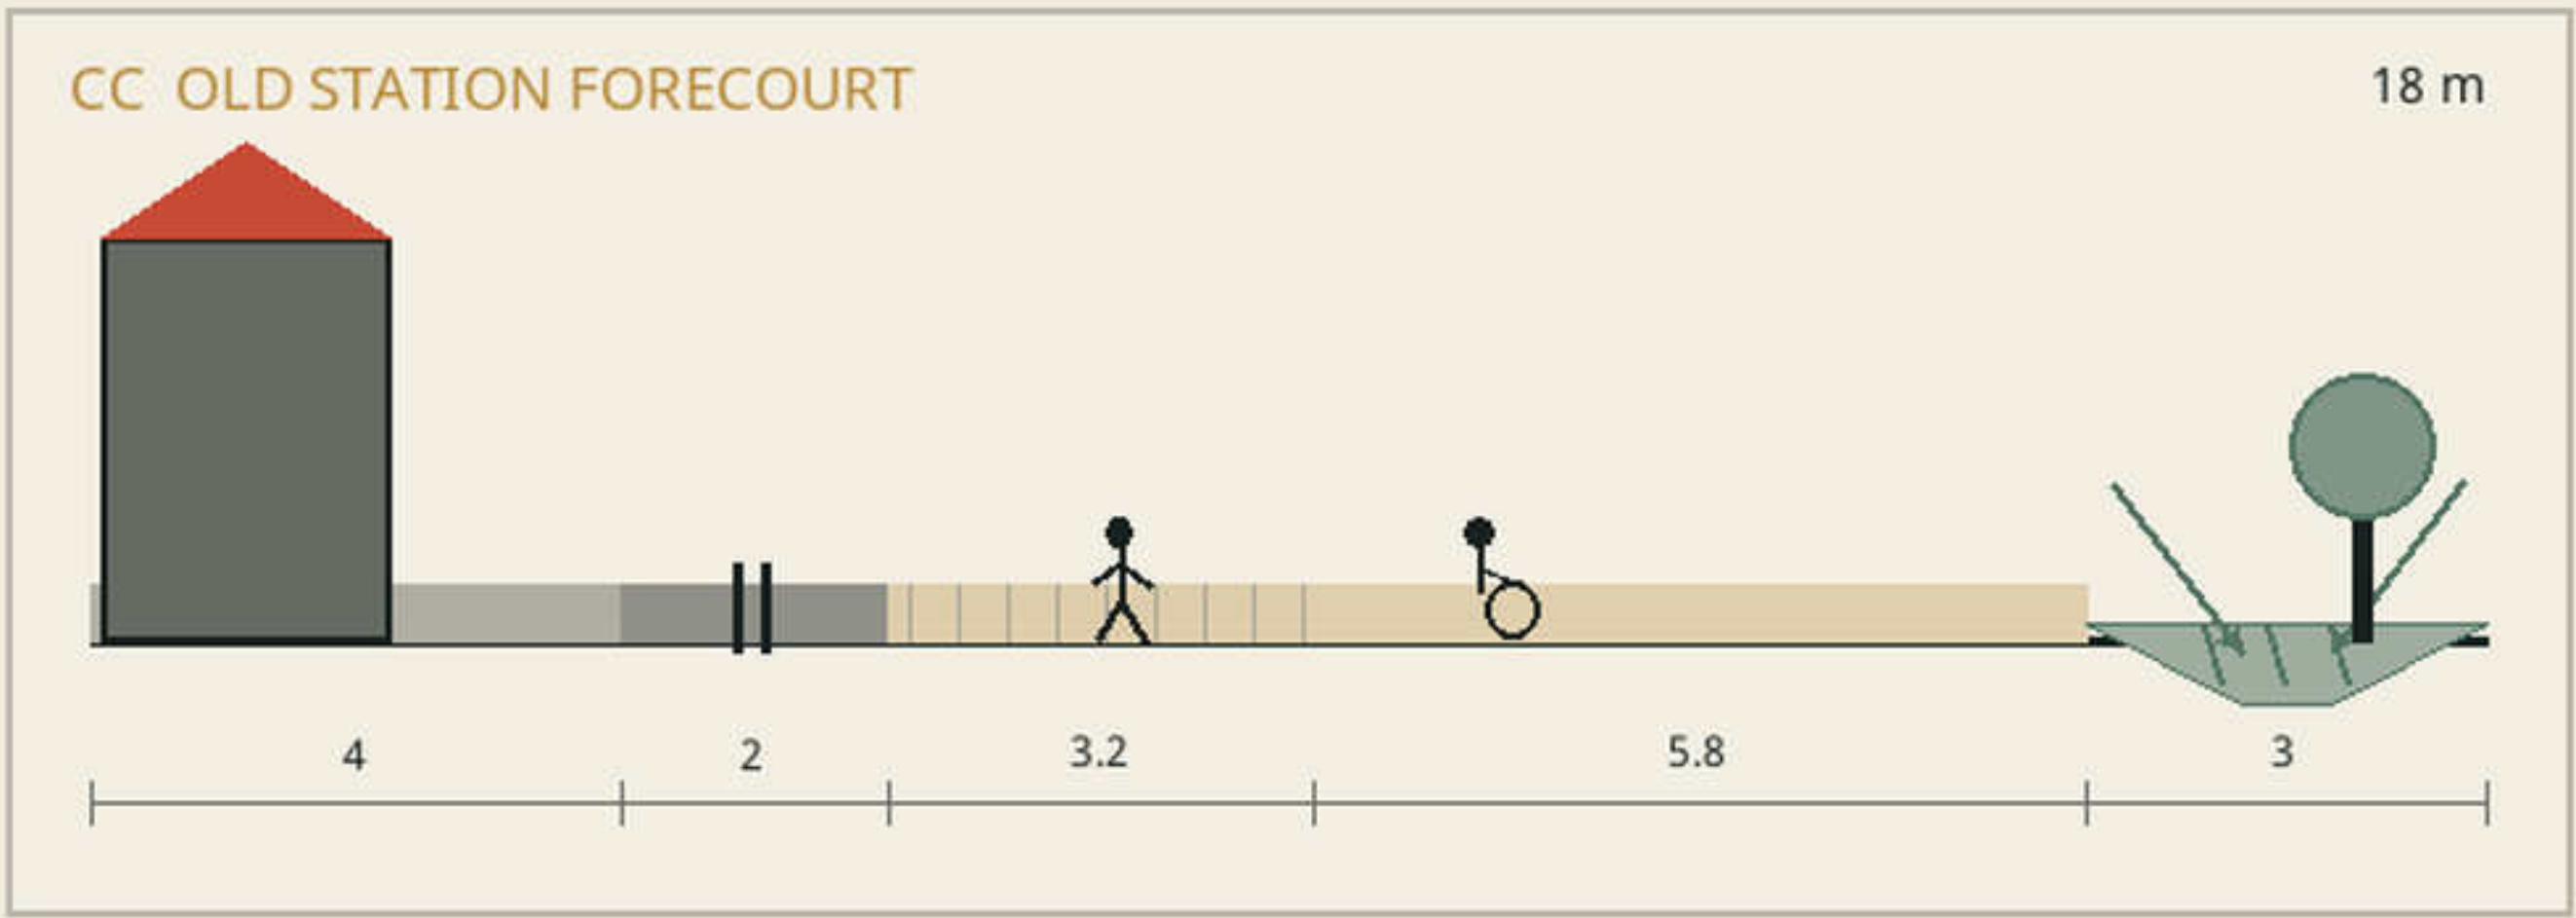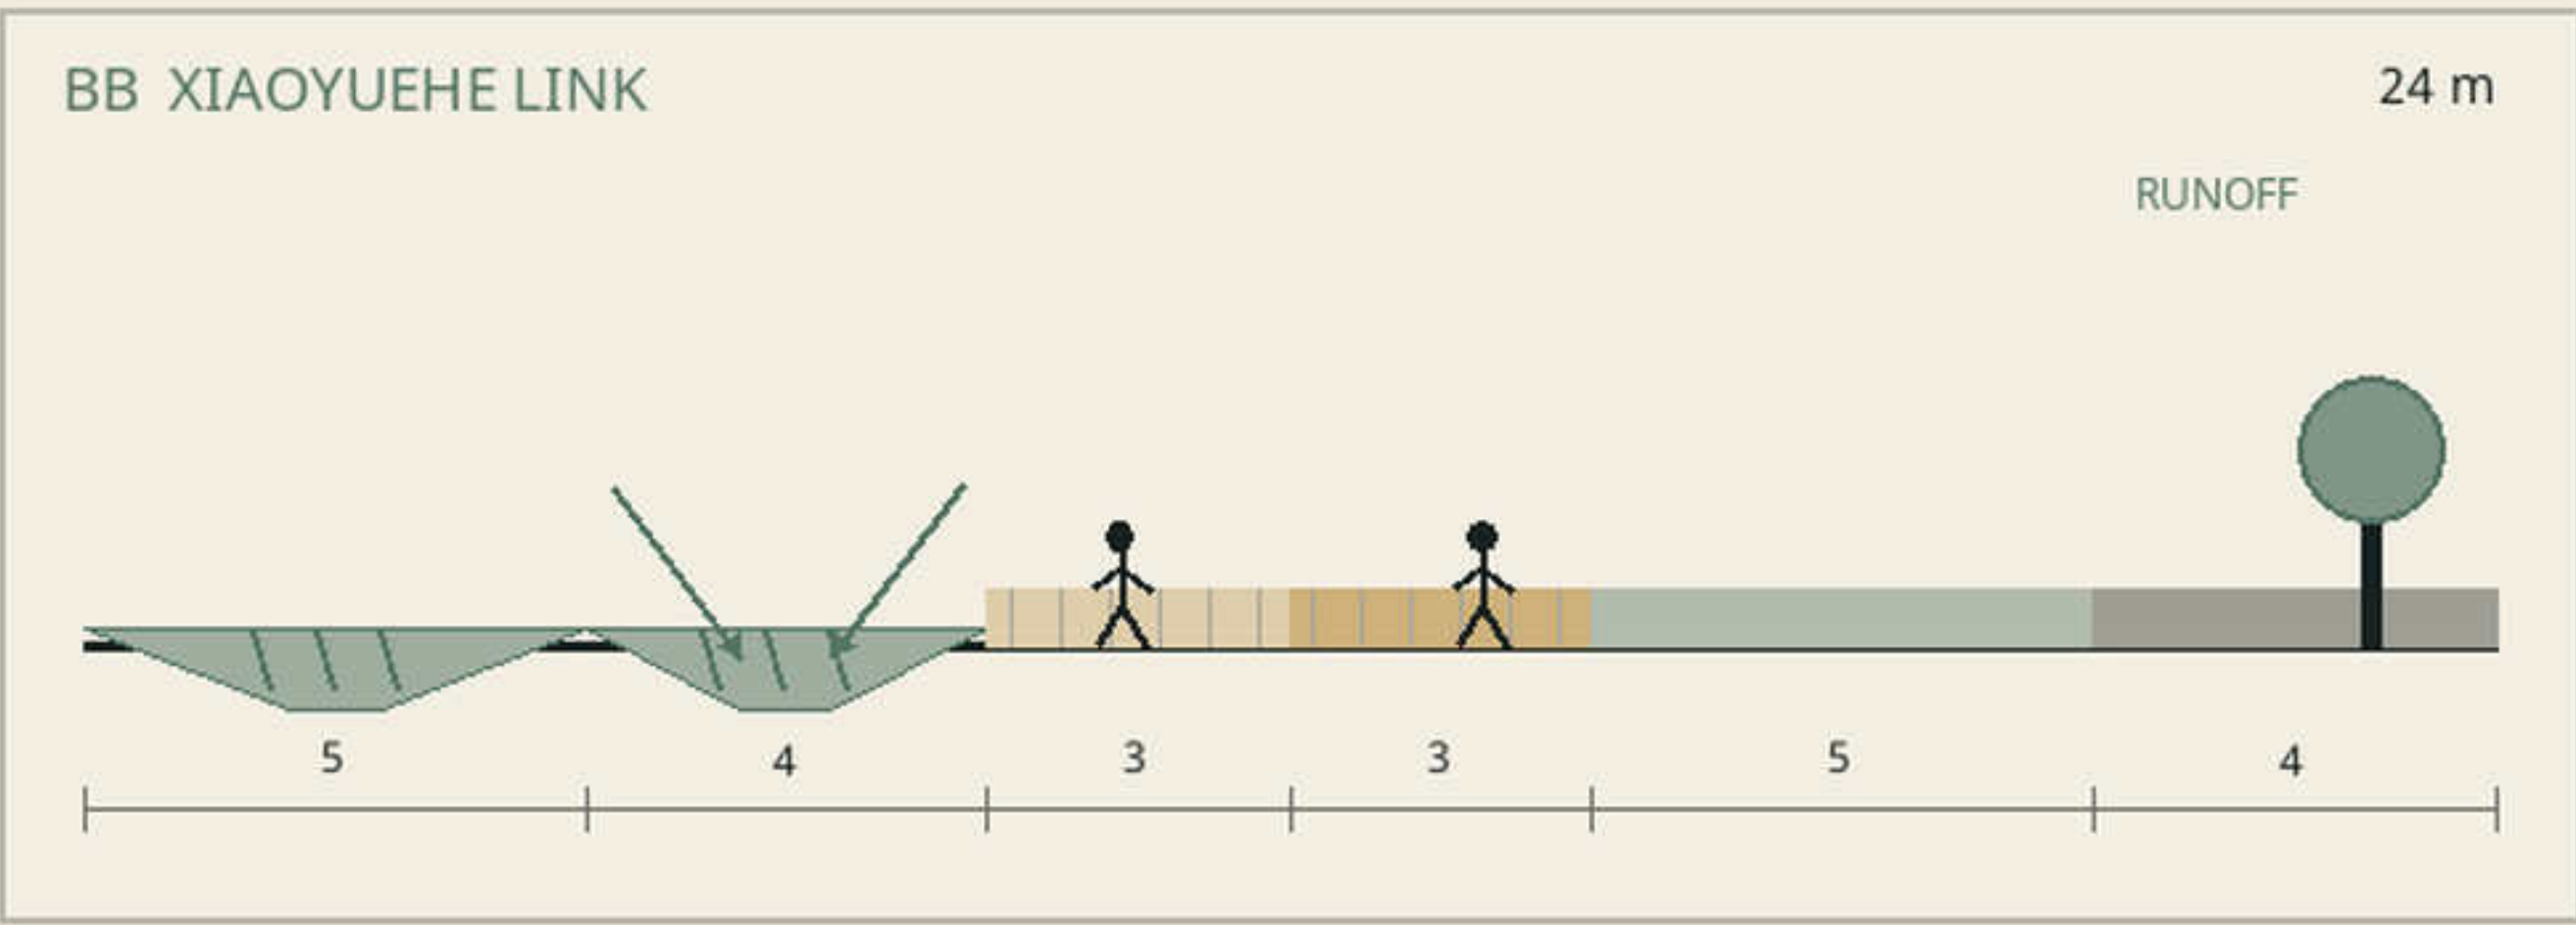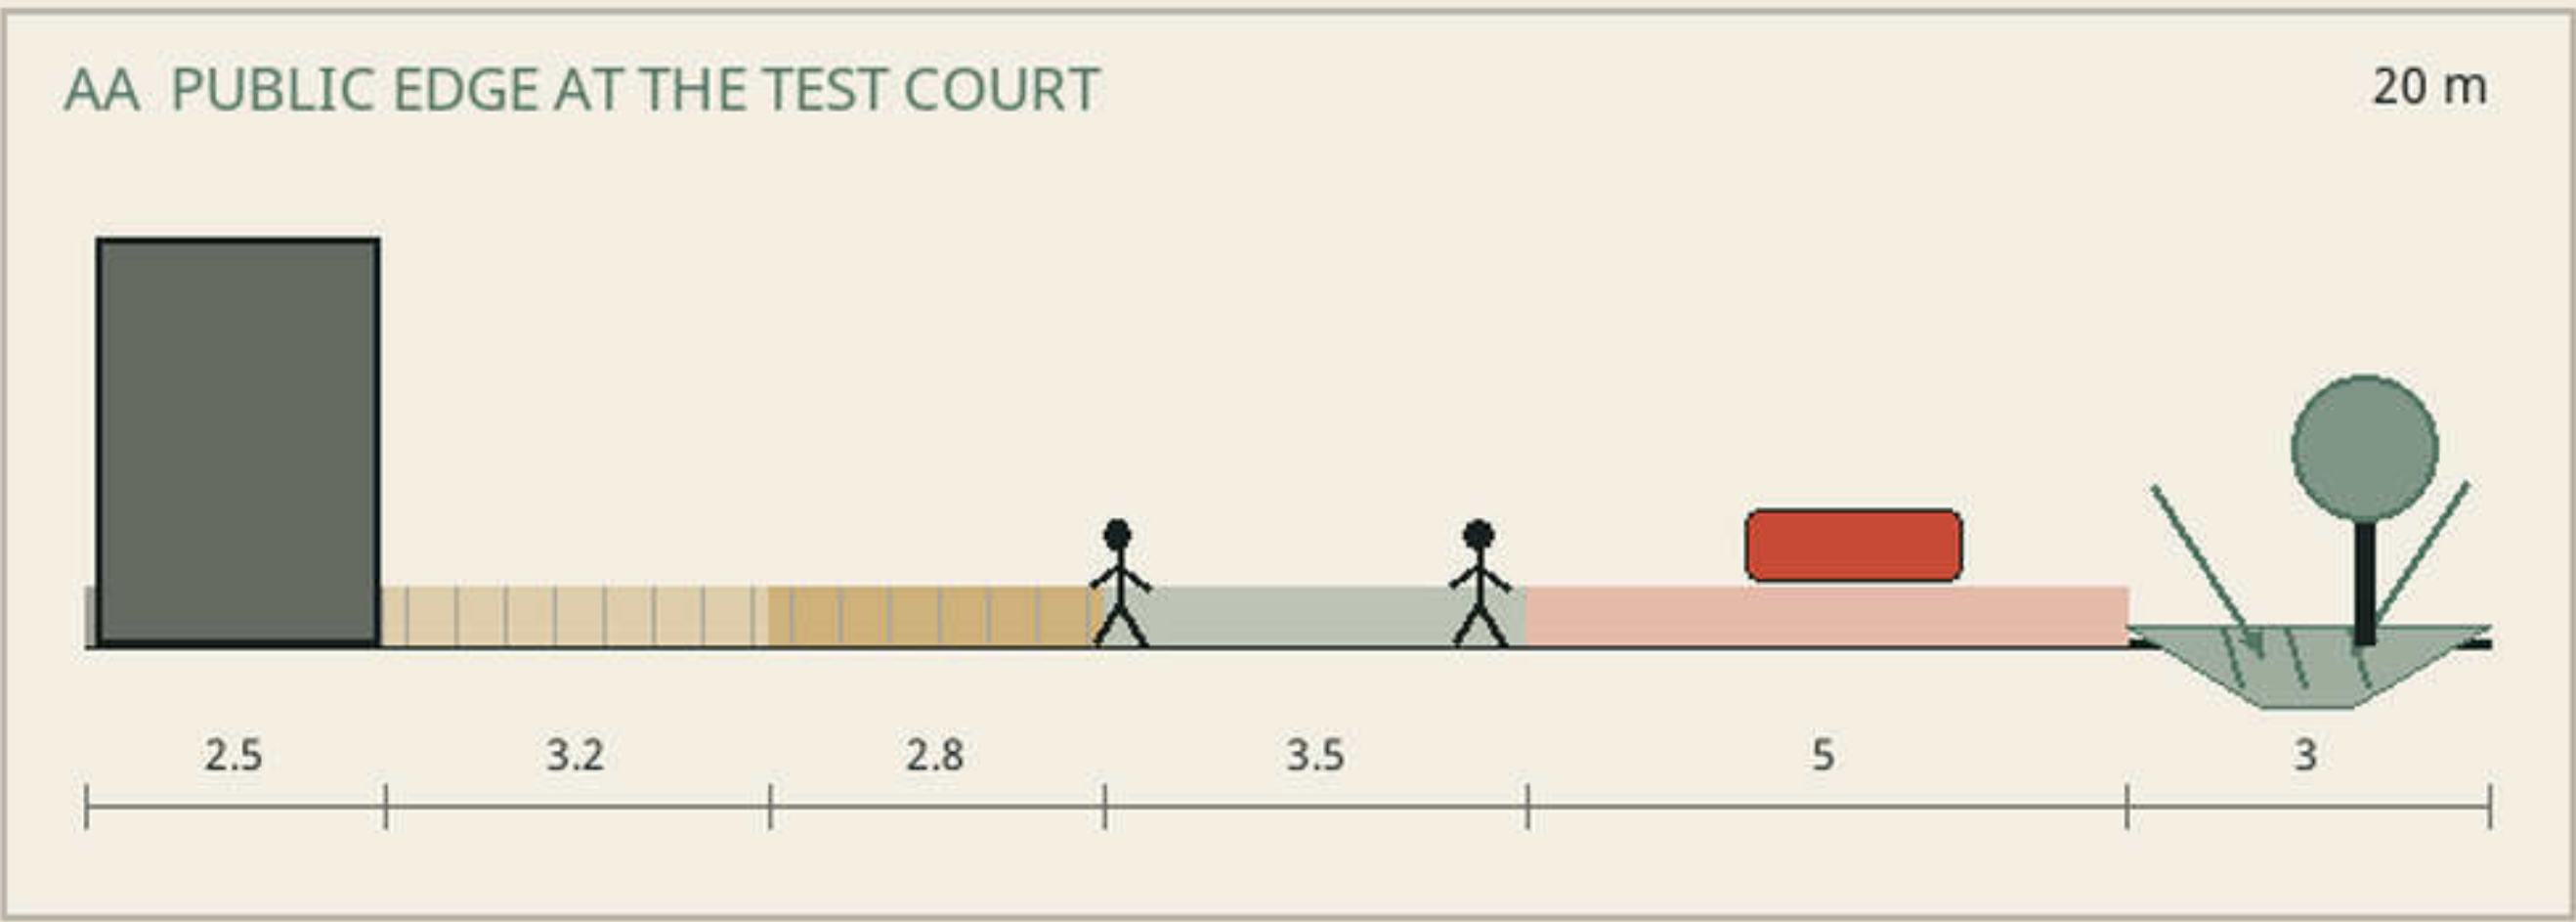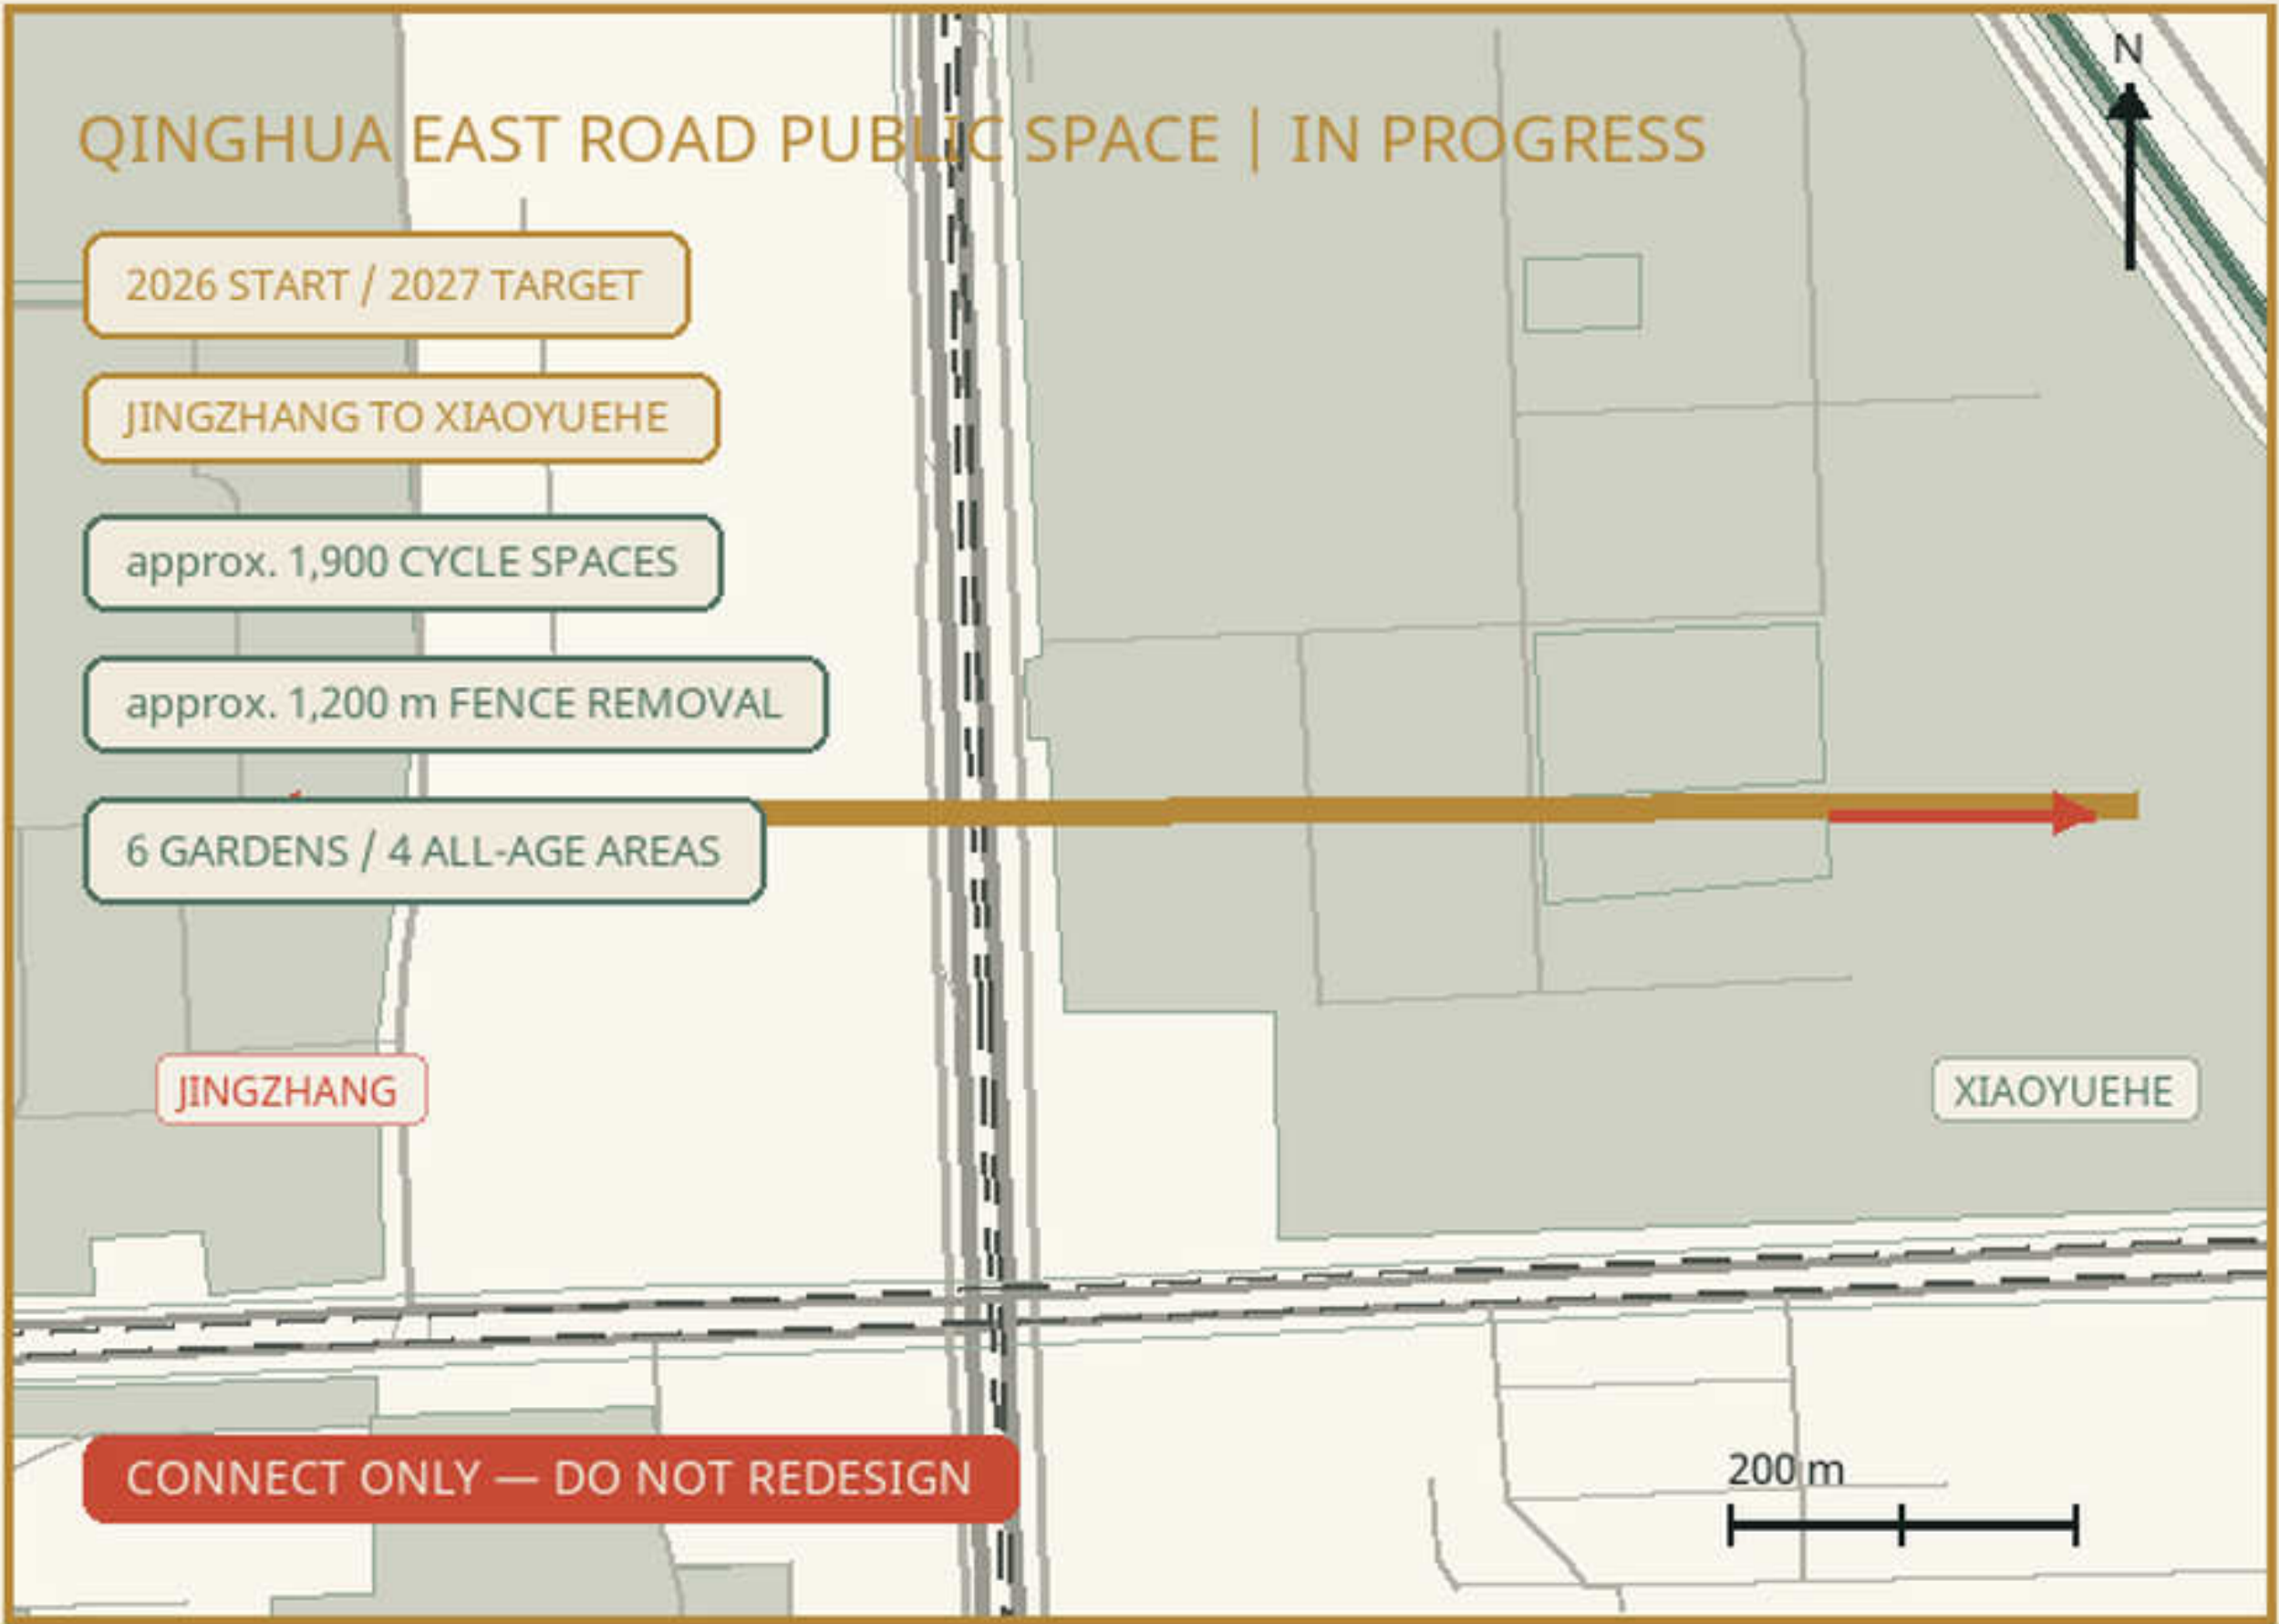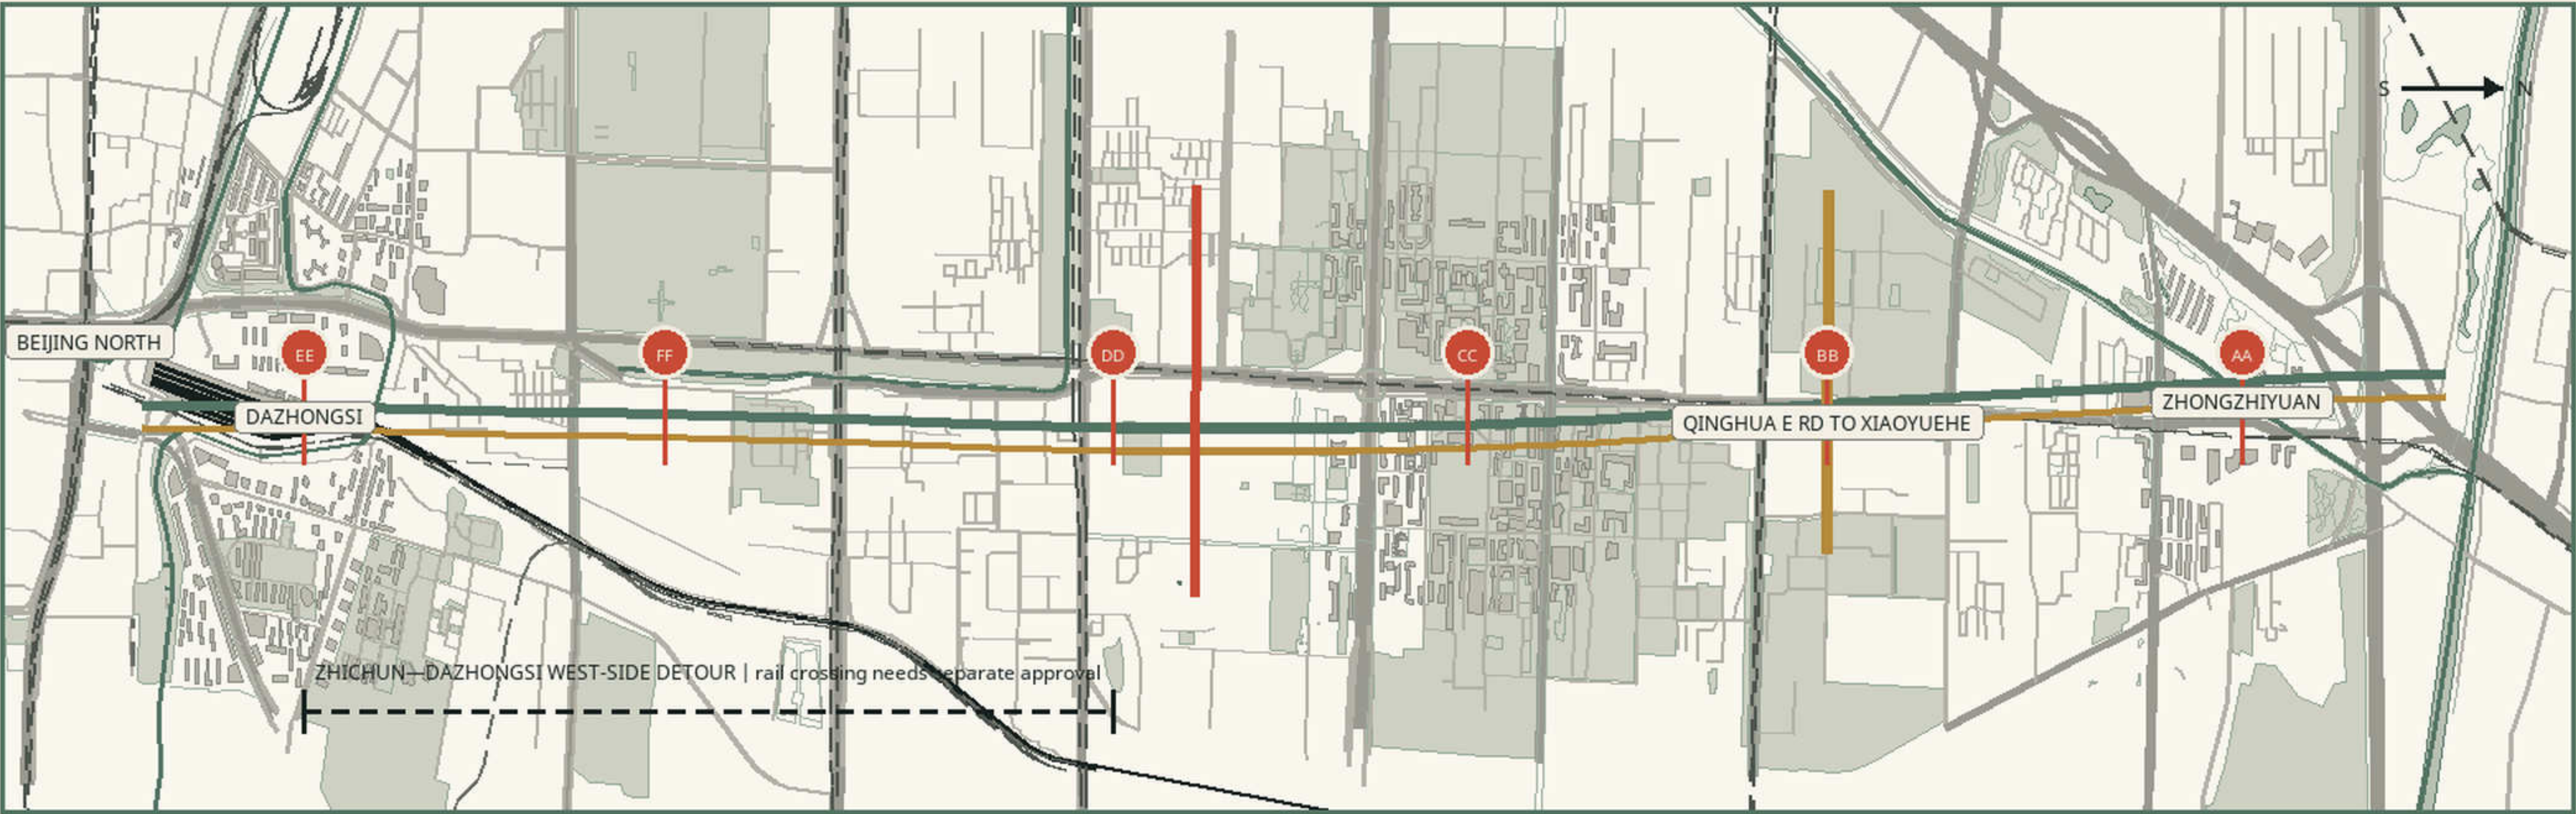

OSM context only | Concept boundaries require survey, ownership and approvals

WIDTHS IN METRES | DB11/T 1761-2020 WORKING LOGIC



3.2 m

Working width for the public path

2.8 m

Working width for the cycle lane

6.41 km

Xiaoyue River works; flood section remains unchanged




REVIEW

Line 13 crossing remains a problem location only

04

THE 300 M NODE, IN DETAIL

One set of dimensions across aerial, plan and section

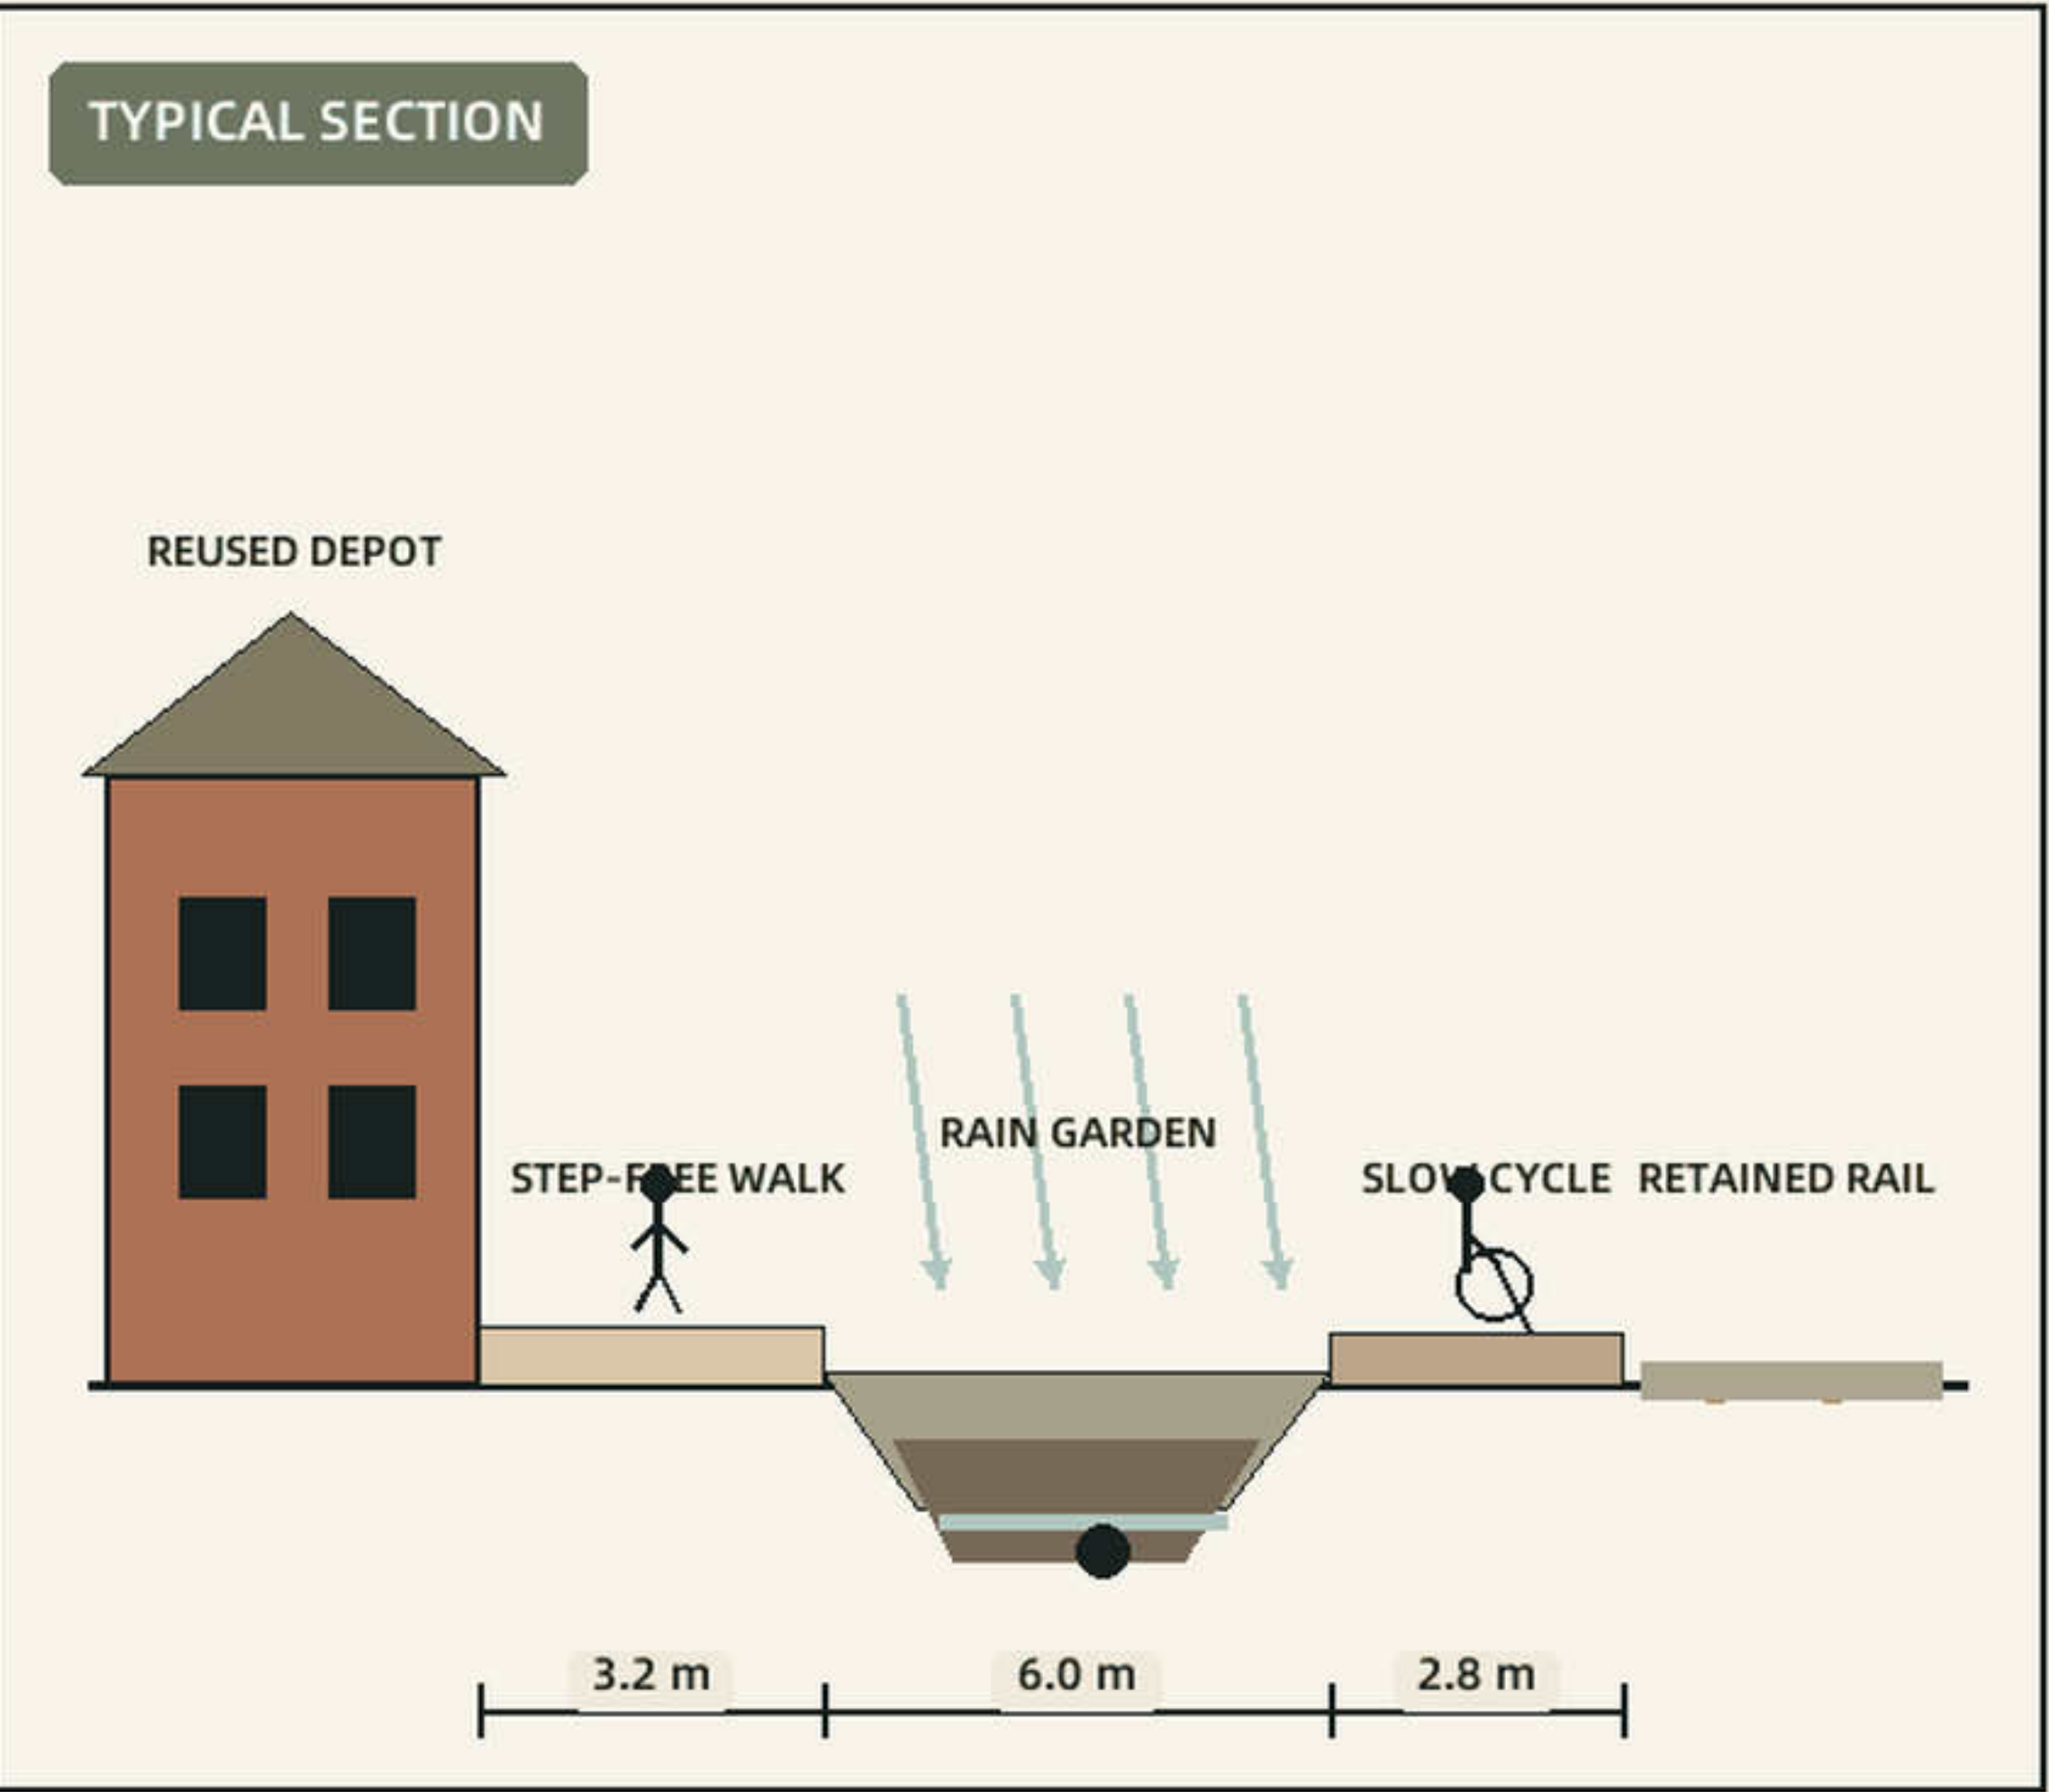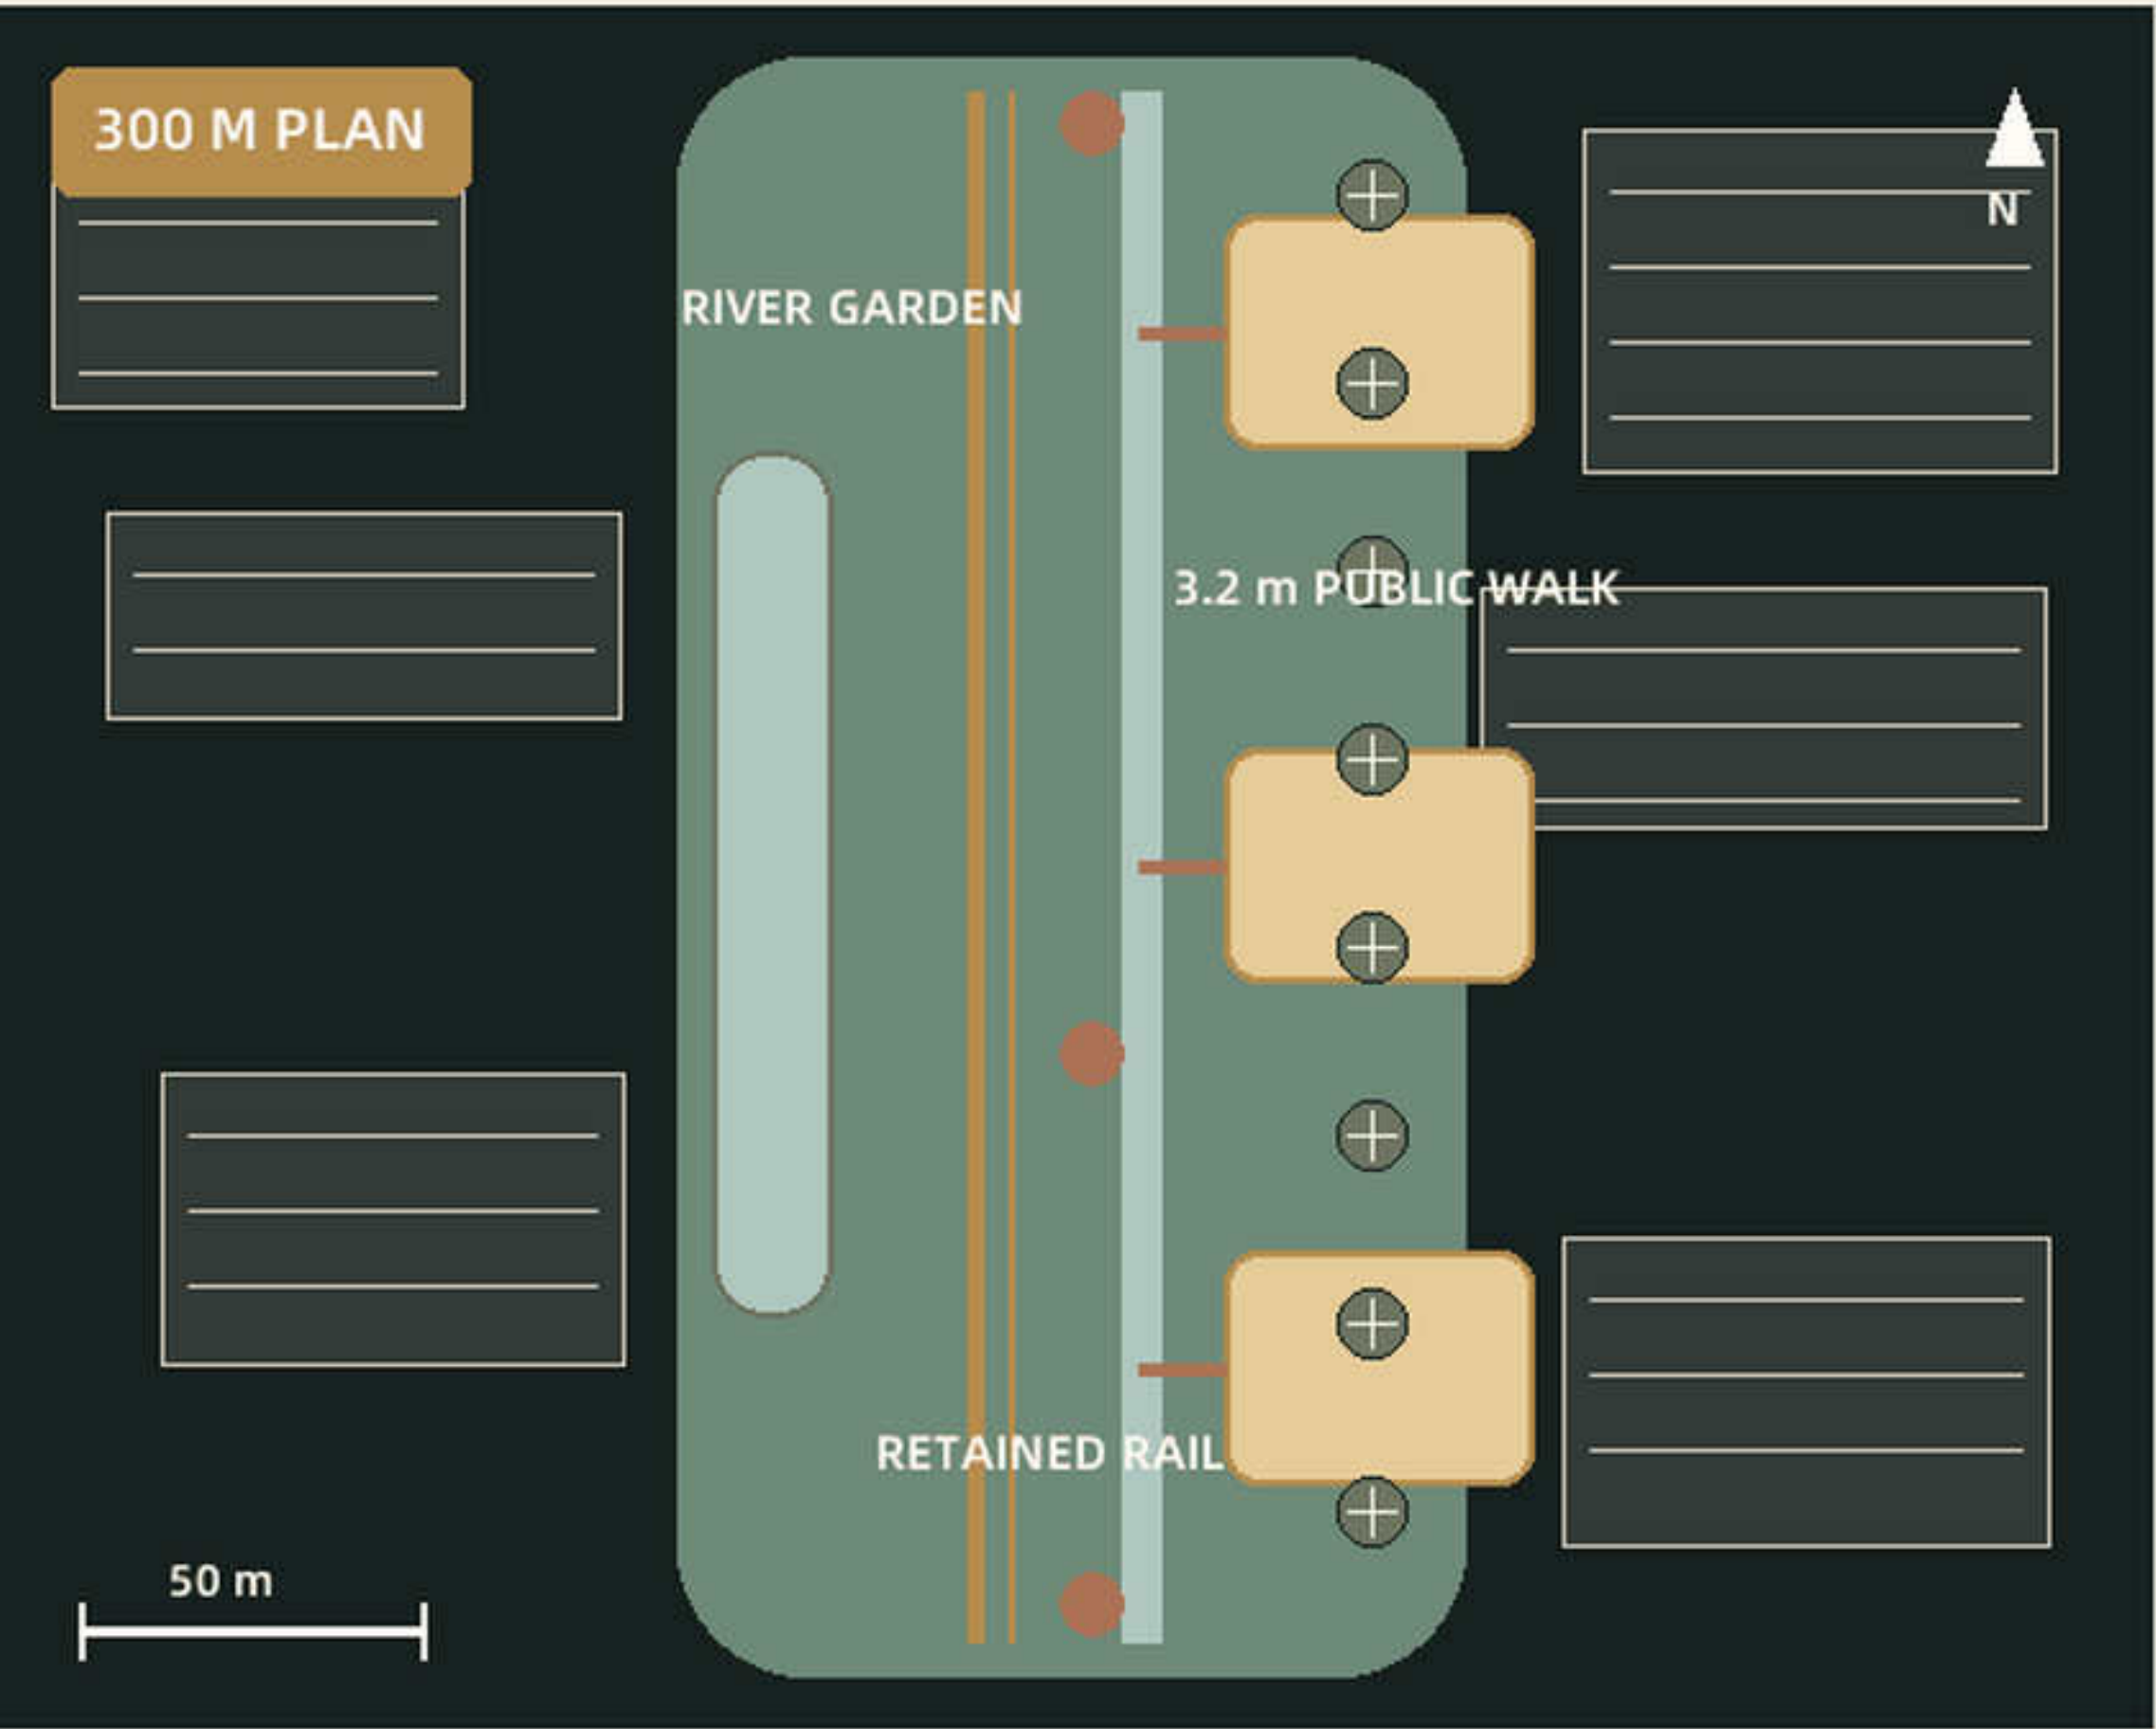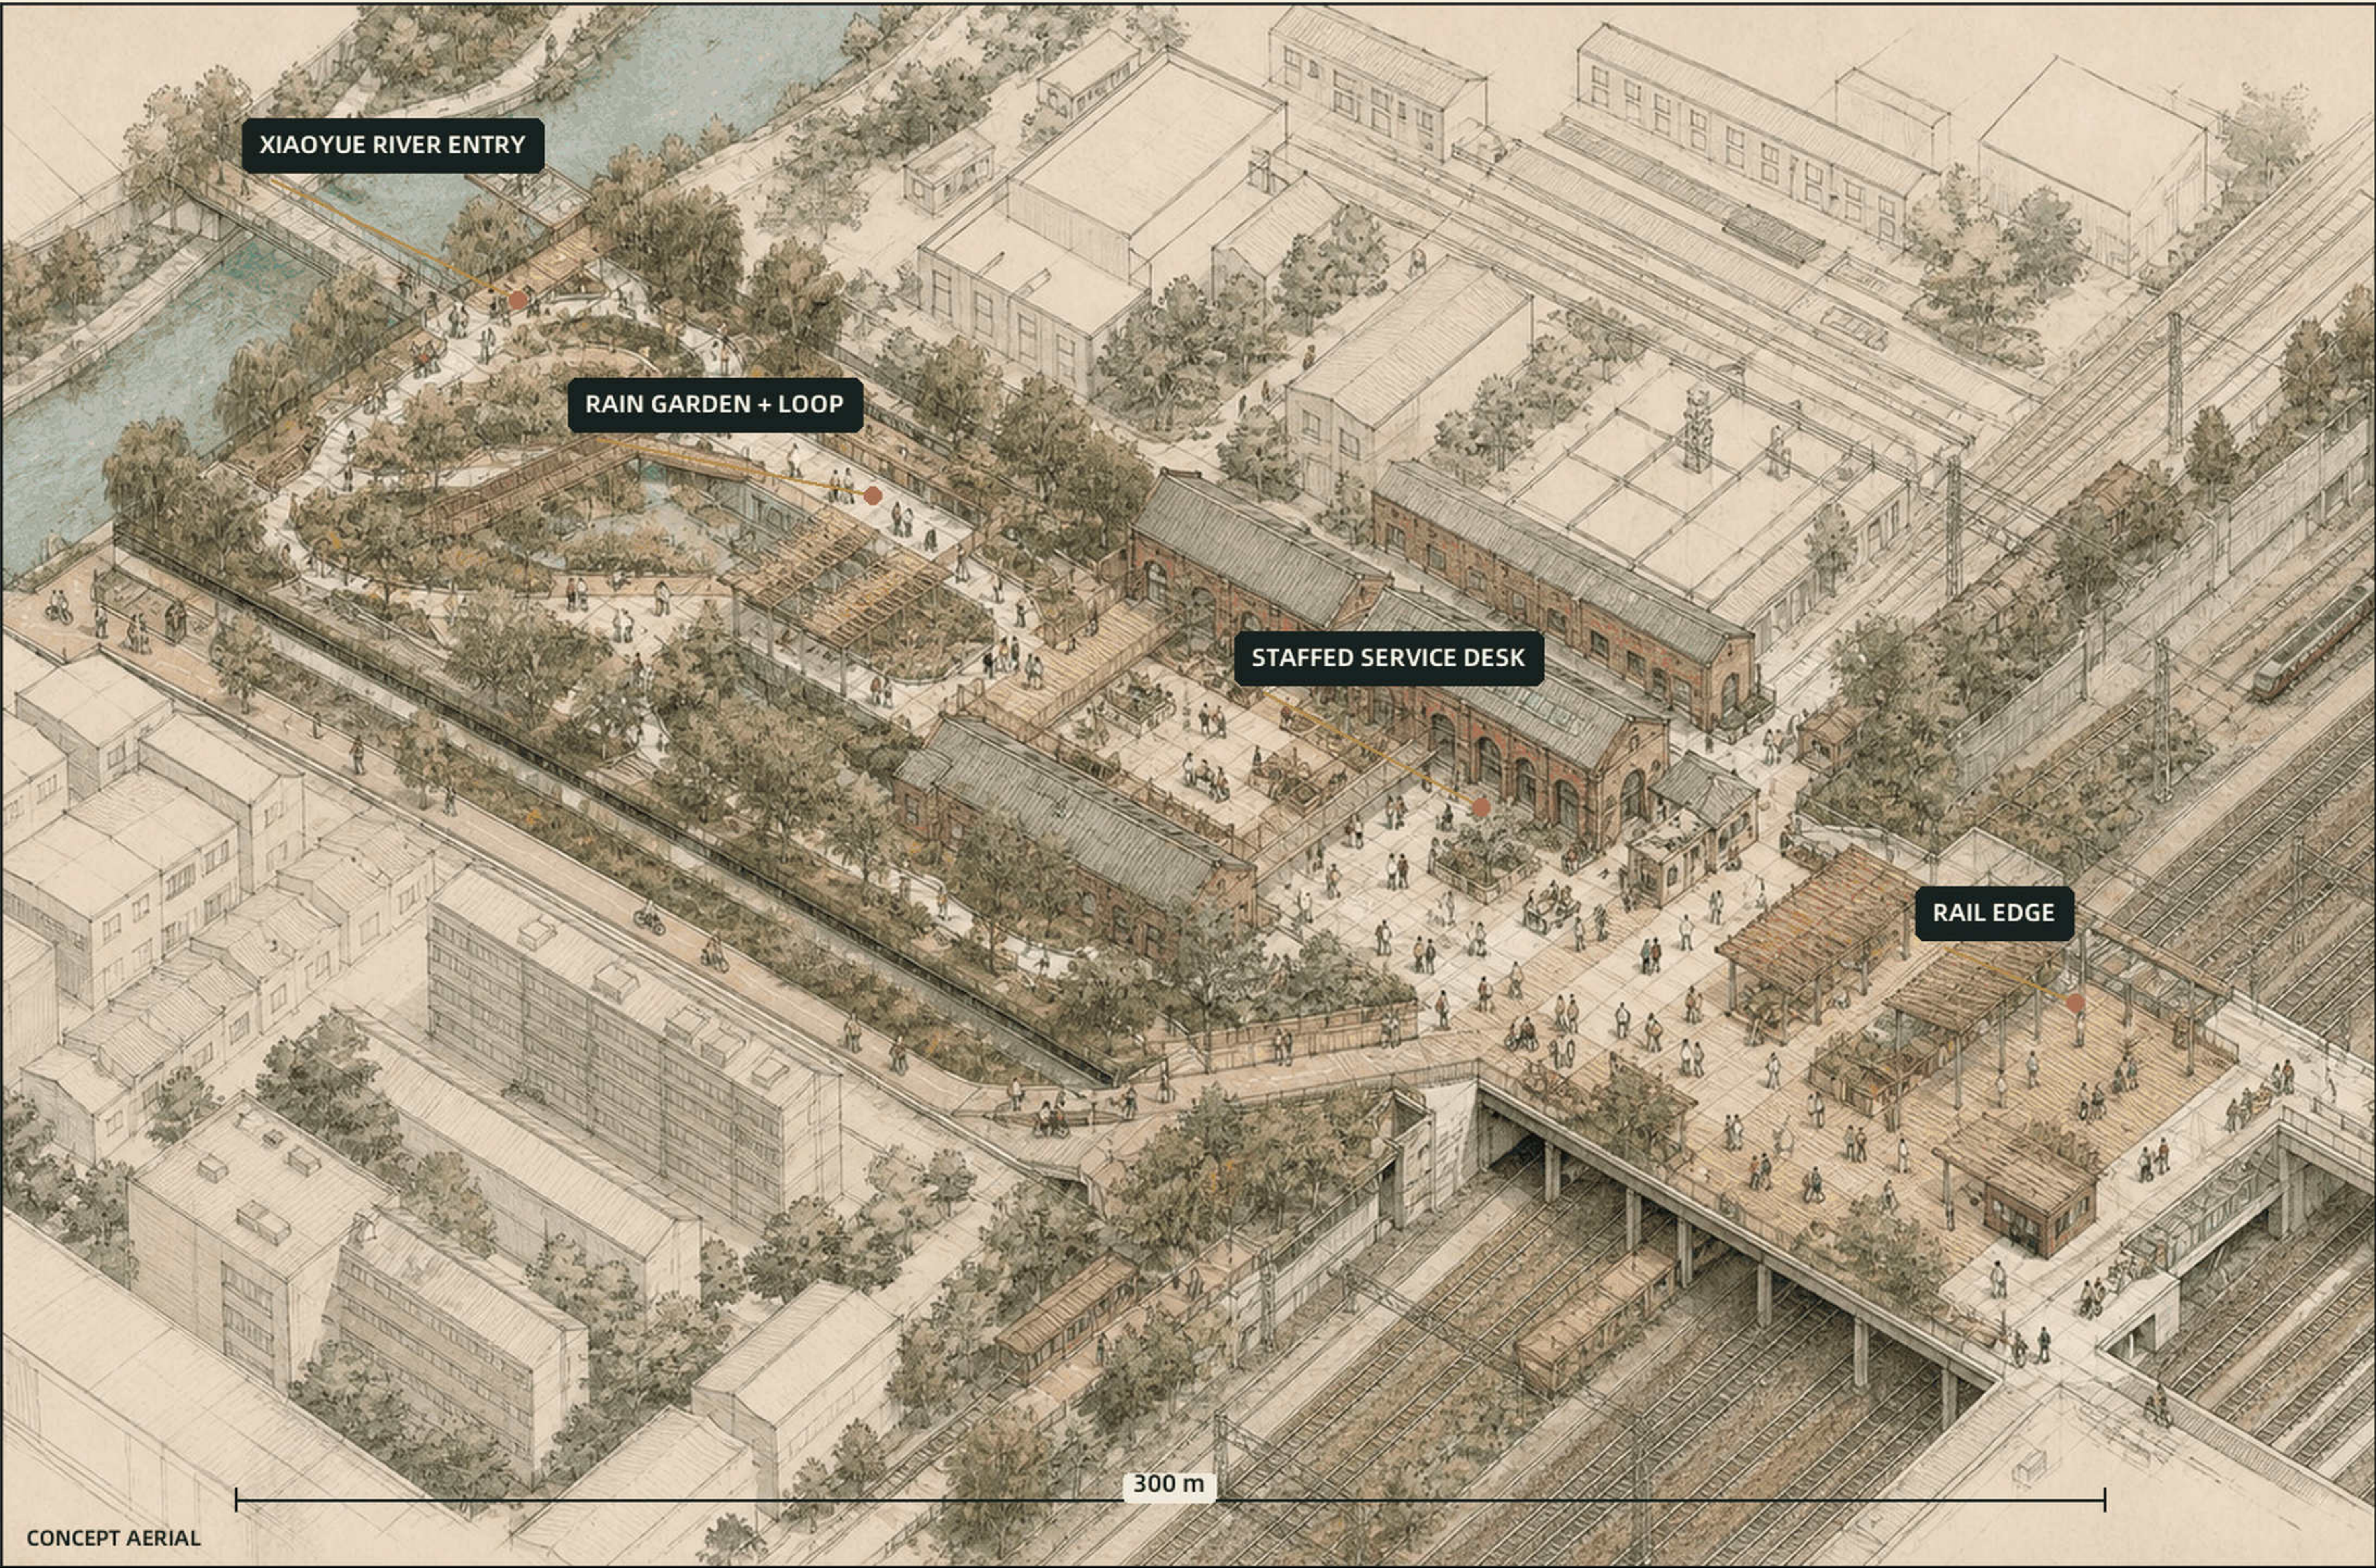

CONCEPT NODE | VERIFY OWNERSHIP, UTILITIES AND LEVELS BEFORE WORKS

OPEN-CITY-AI / HAIDIAN

PUBLIC FRONT
Entrance, ramp, and service desk face everyday users first.

SERVICE BACK
Equipment, maintenance, and deliveries use a separate door.

QUIET EDGE
Residential edges keep shade, seating, and low-level light only.

07

ONE DAY ON THE OPEN BELT

Four moments, four users, and a human fallback each time

07:35

XIAOYUE RIVER ENTRY

COMMUTER



ROUTE

Liudaokou → river gate → Xuezhijuan

HUMAN FALLBACK


Staff open the drain and hand-direct traffic after ponding

VISIBLE RESULT: THE GATE STAYS OPEN

12:10

AI ORIGIN

OLDER VISITOR

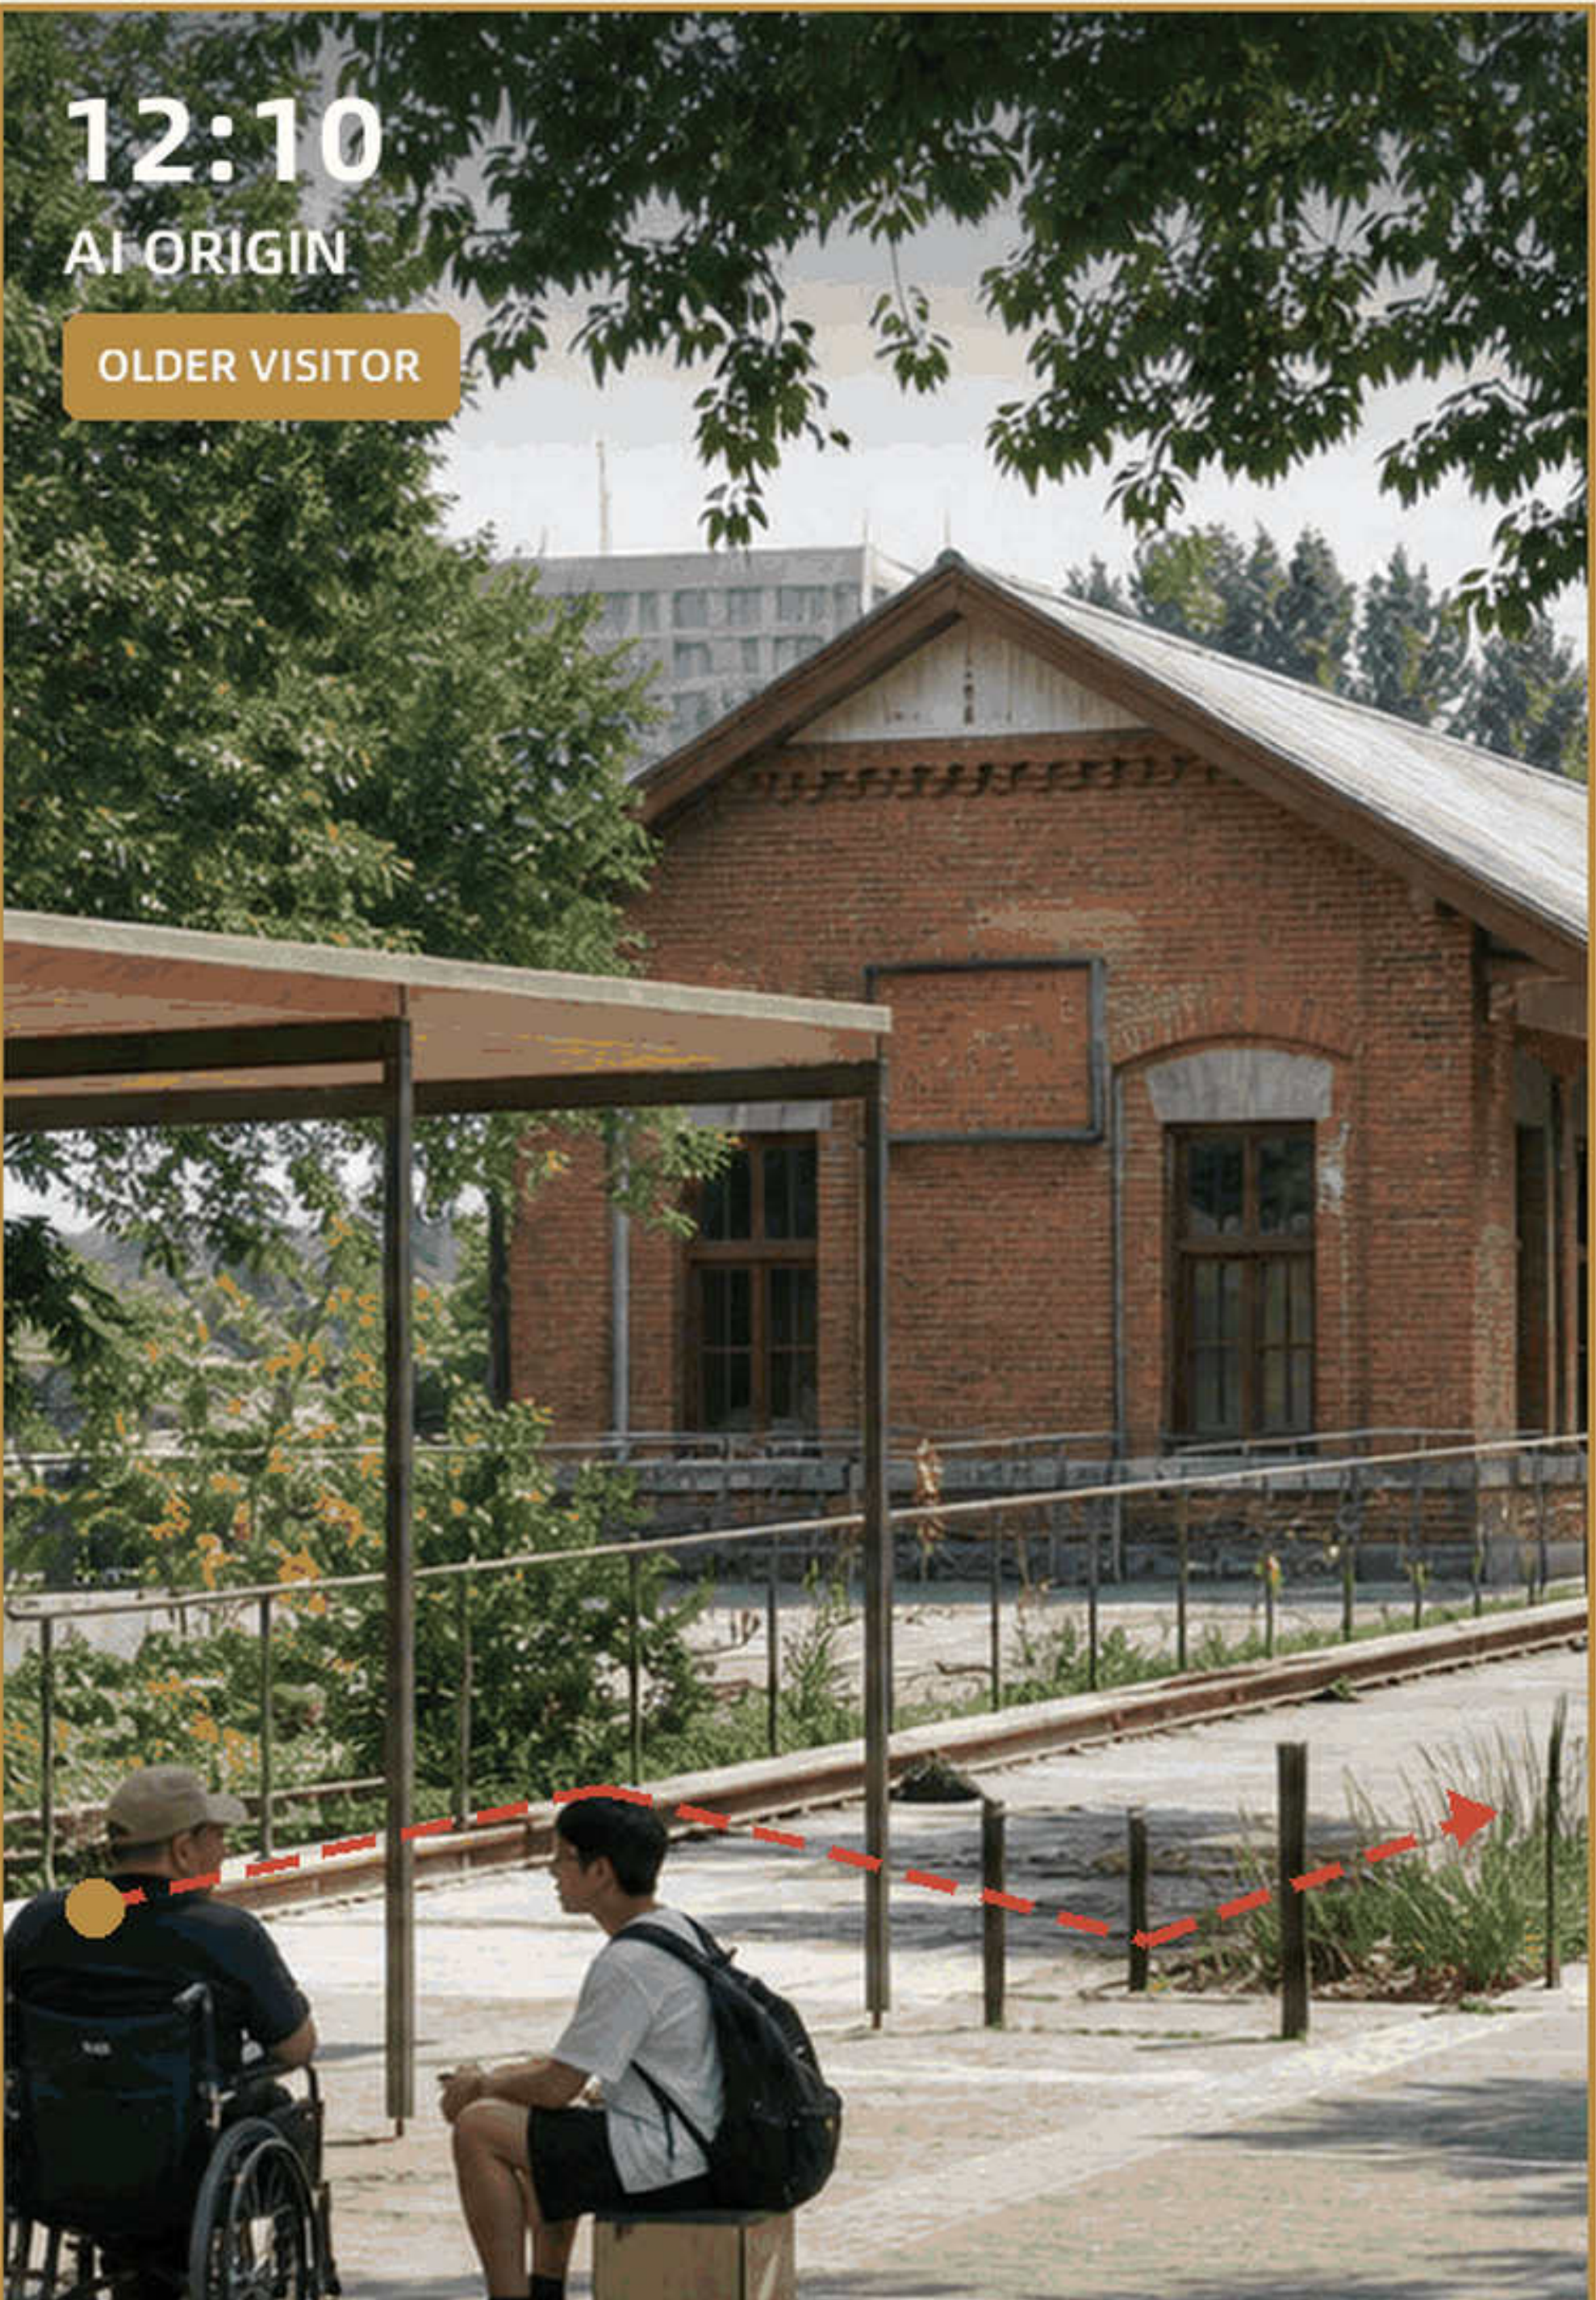

ROUTE

Shaded walk → service desk → quiet bay

HUMAN FALLBACK


The attendant completes the task without asking for a QR code

VISIBLE RESULT: A WHEELCHAIR CAN PARK BESIDE A FRIEND

16:35

ZHONGZHIYUAN

PARENT + CHILD

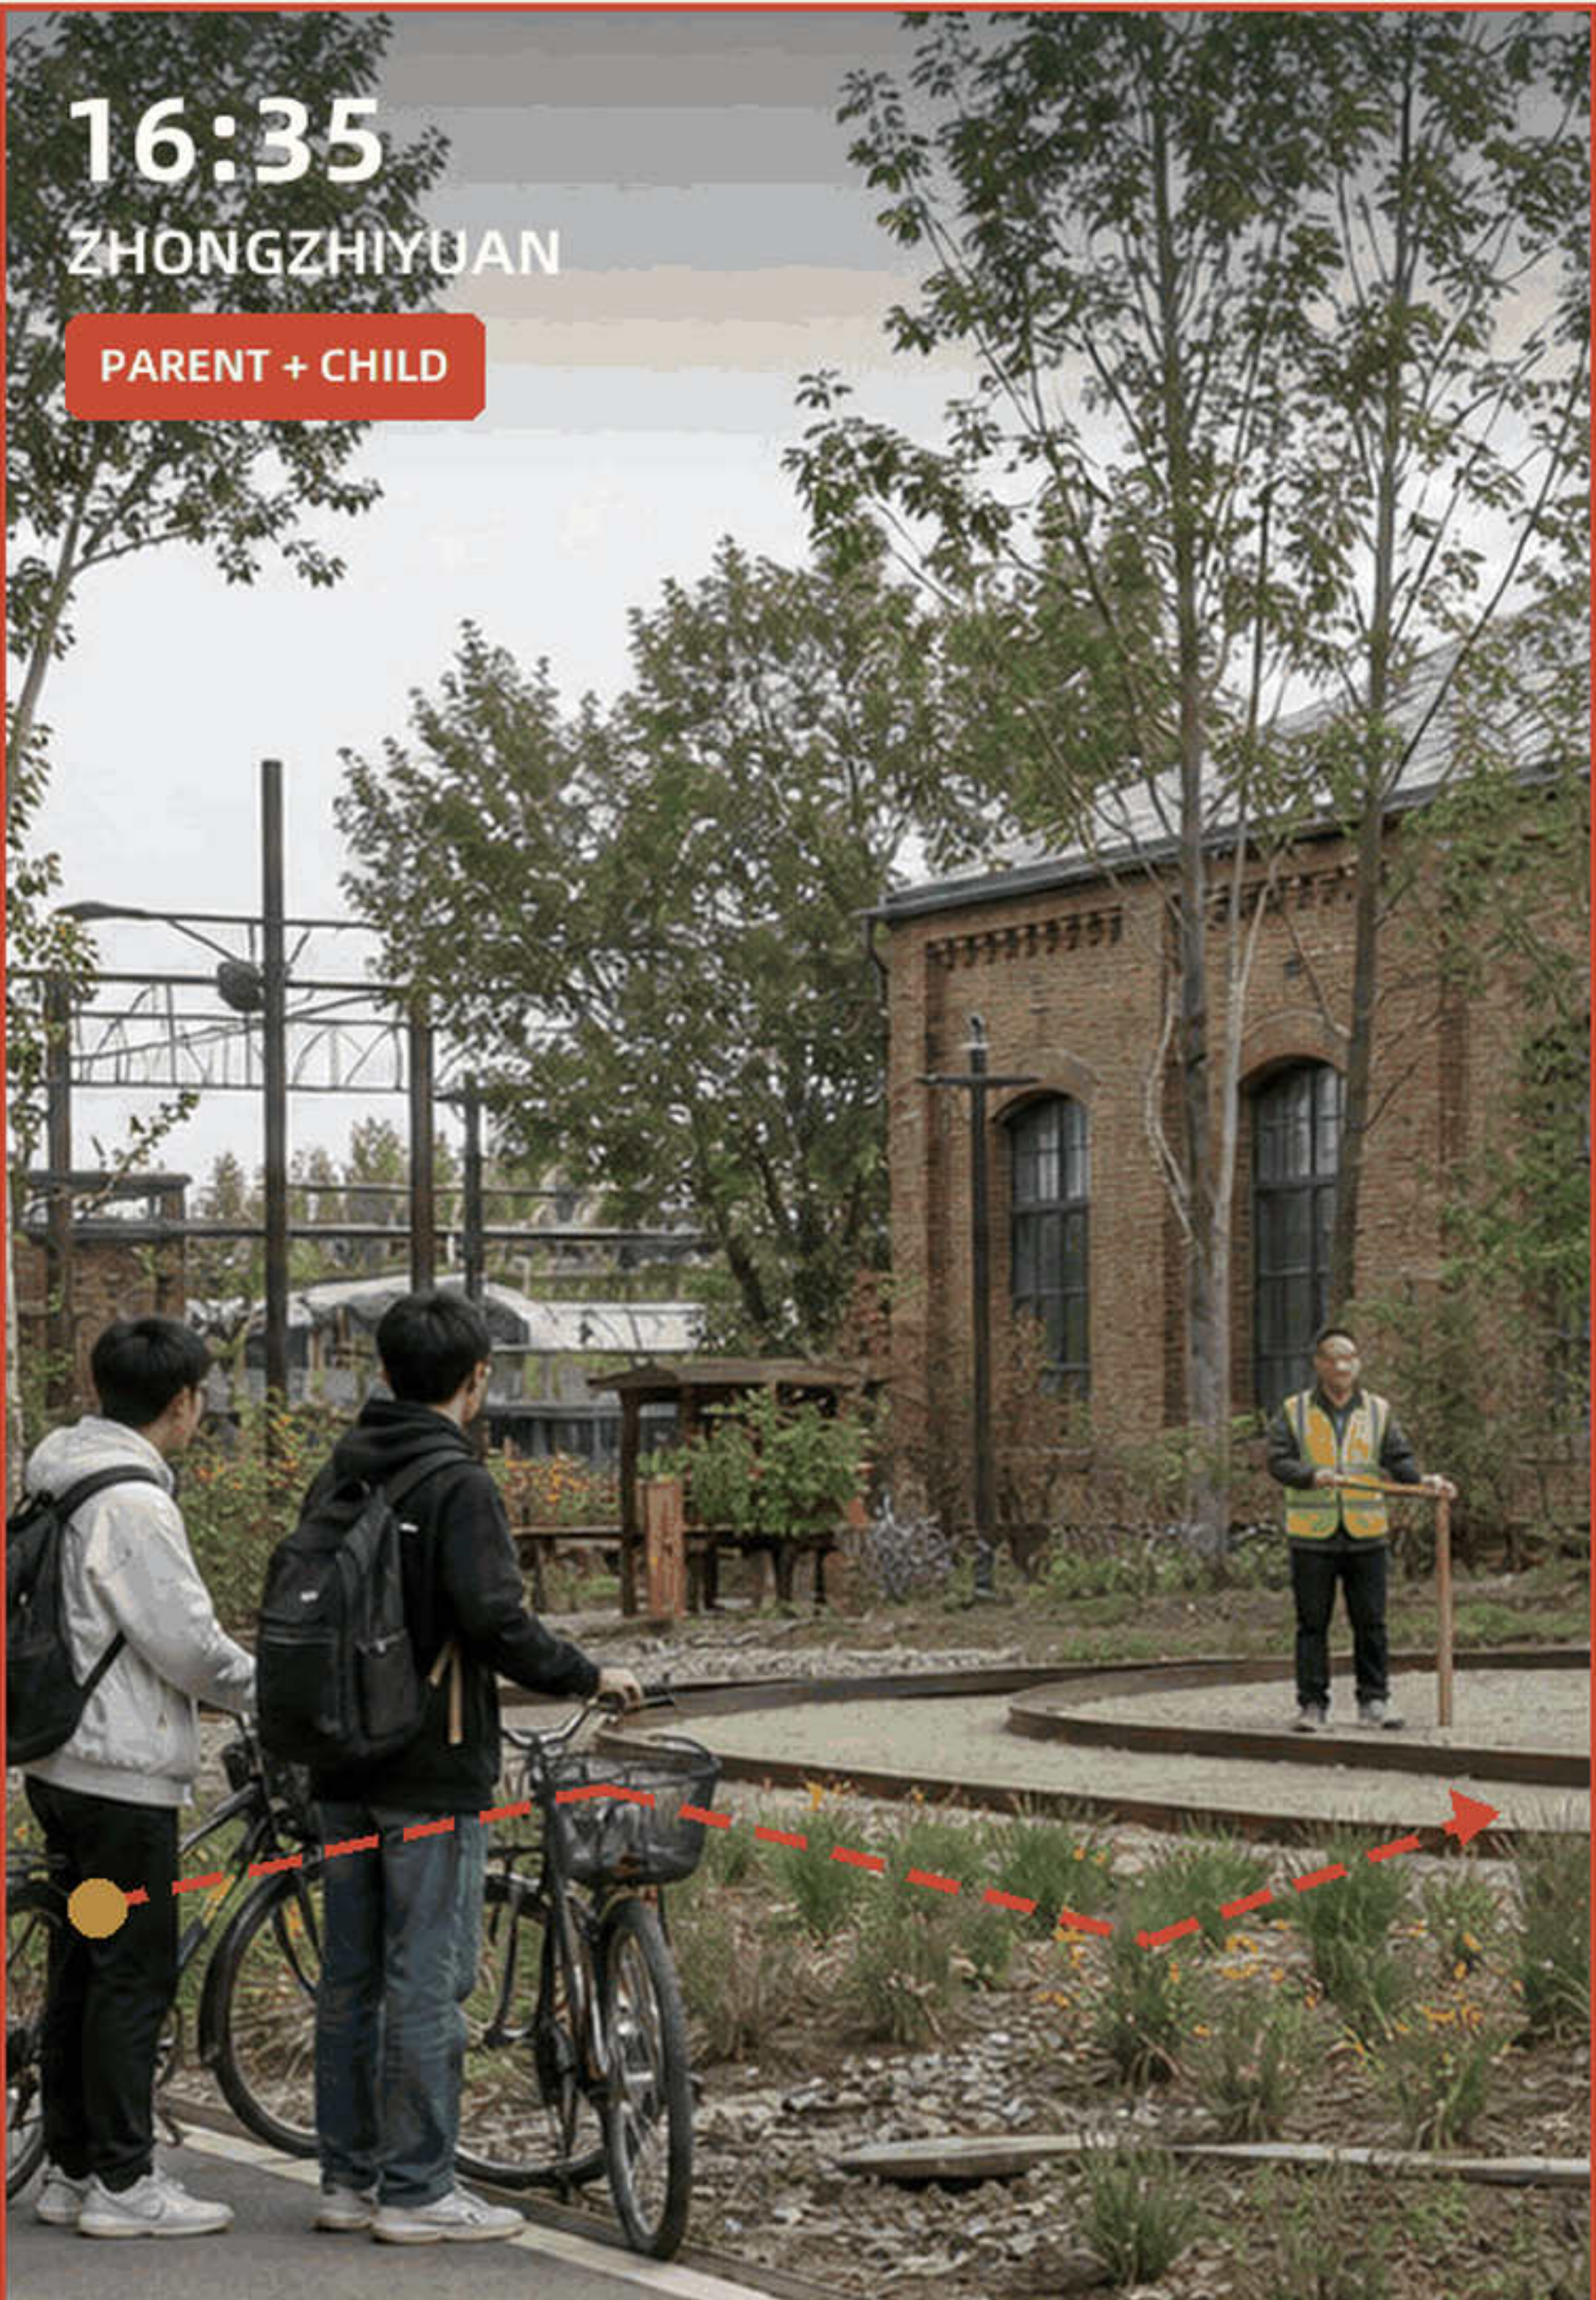

ROUTE

School gate → test loop → rain garden

HUMAN FALLBACK


Adults hand over at the buffer; staff can stop the test

VISIBLE RESULT: PLAY STAYS OFF THE CYCLE LANE

20:30

DAZHONGSI

NIGHT STEWARD

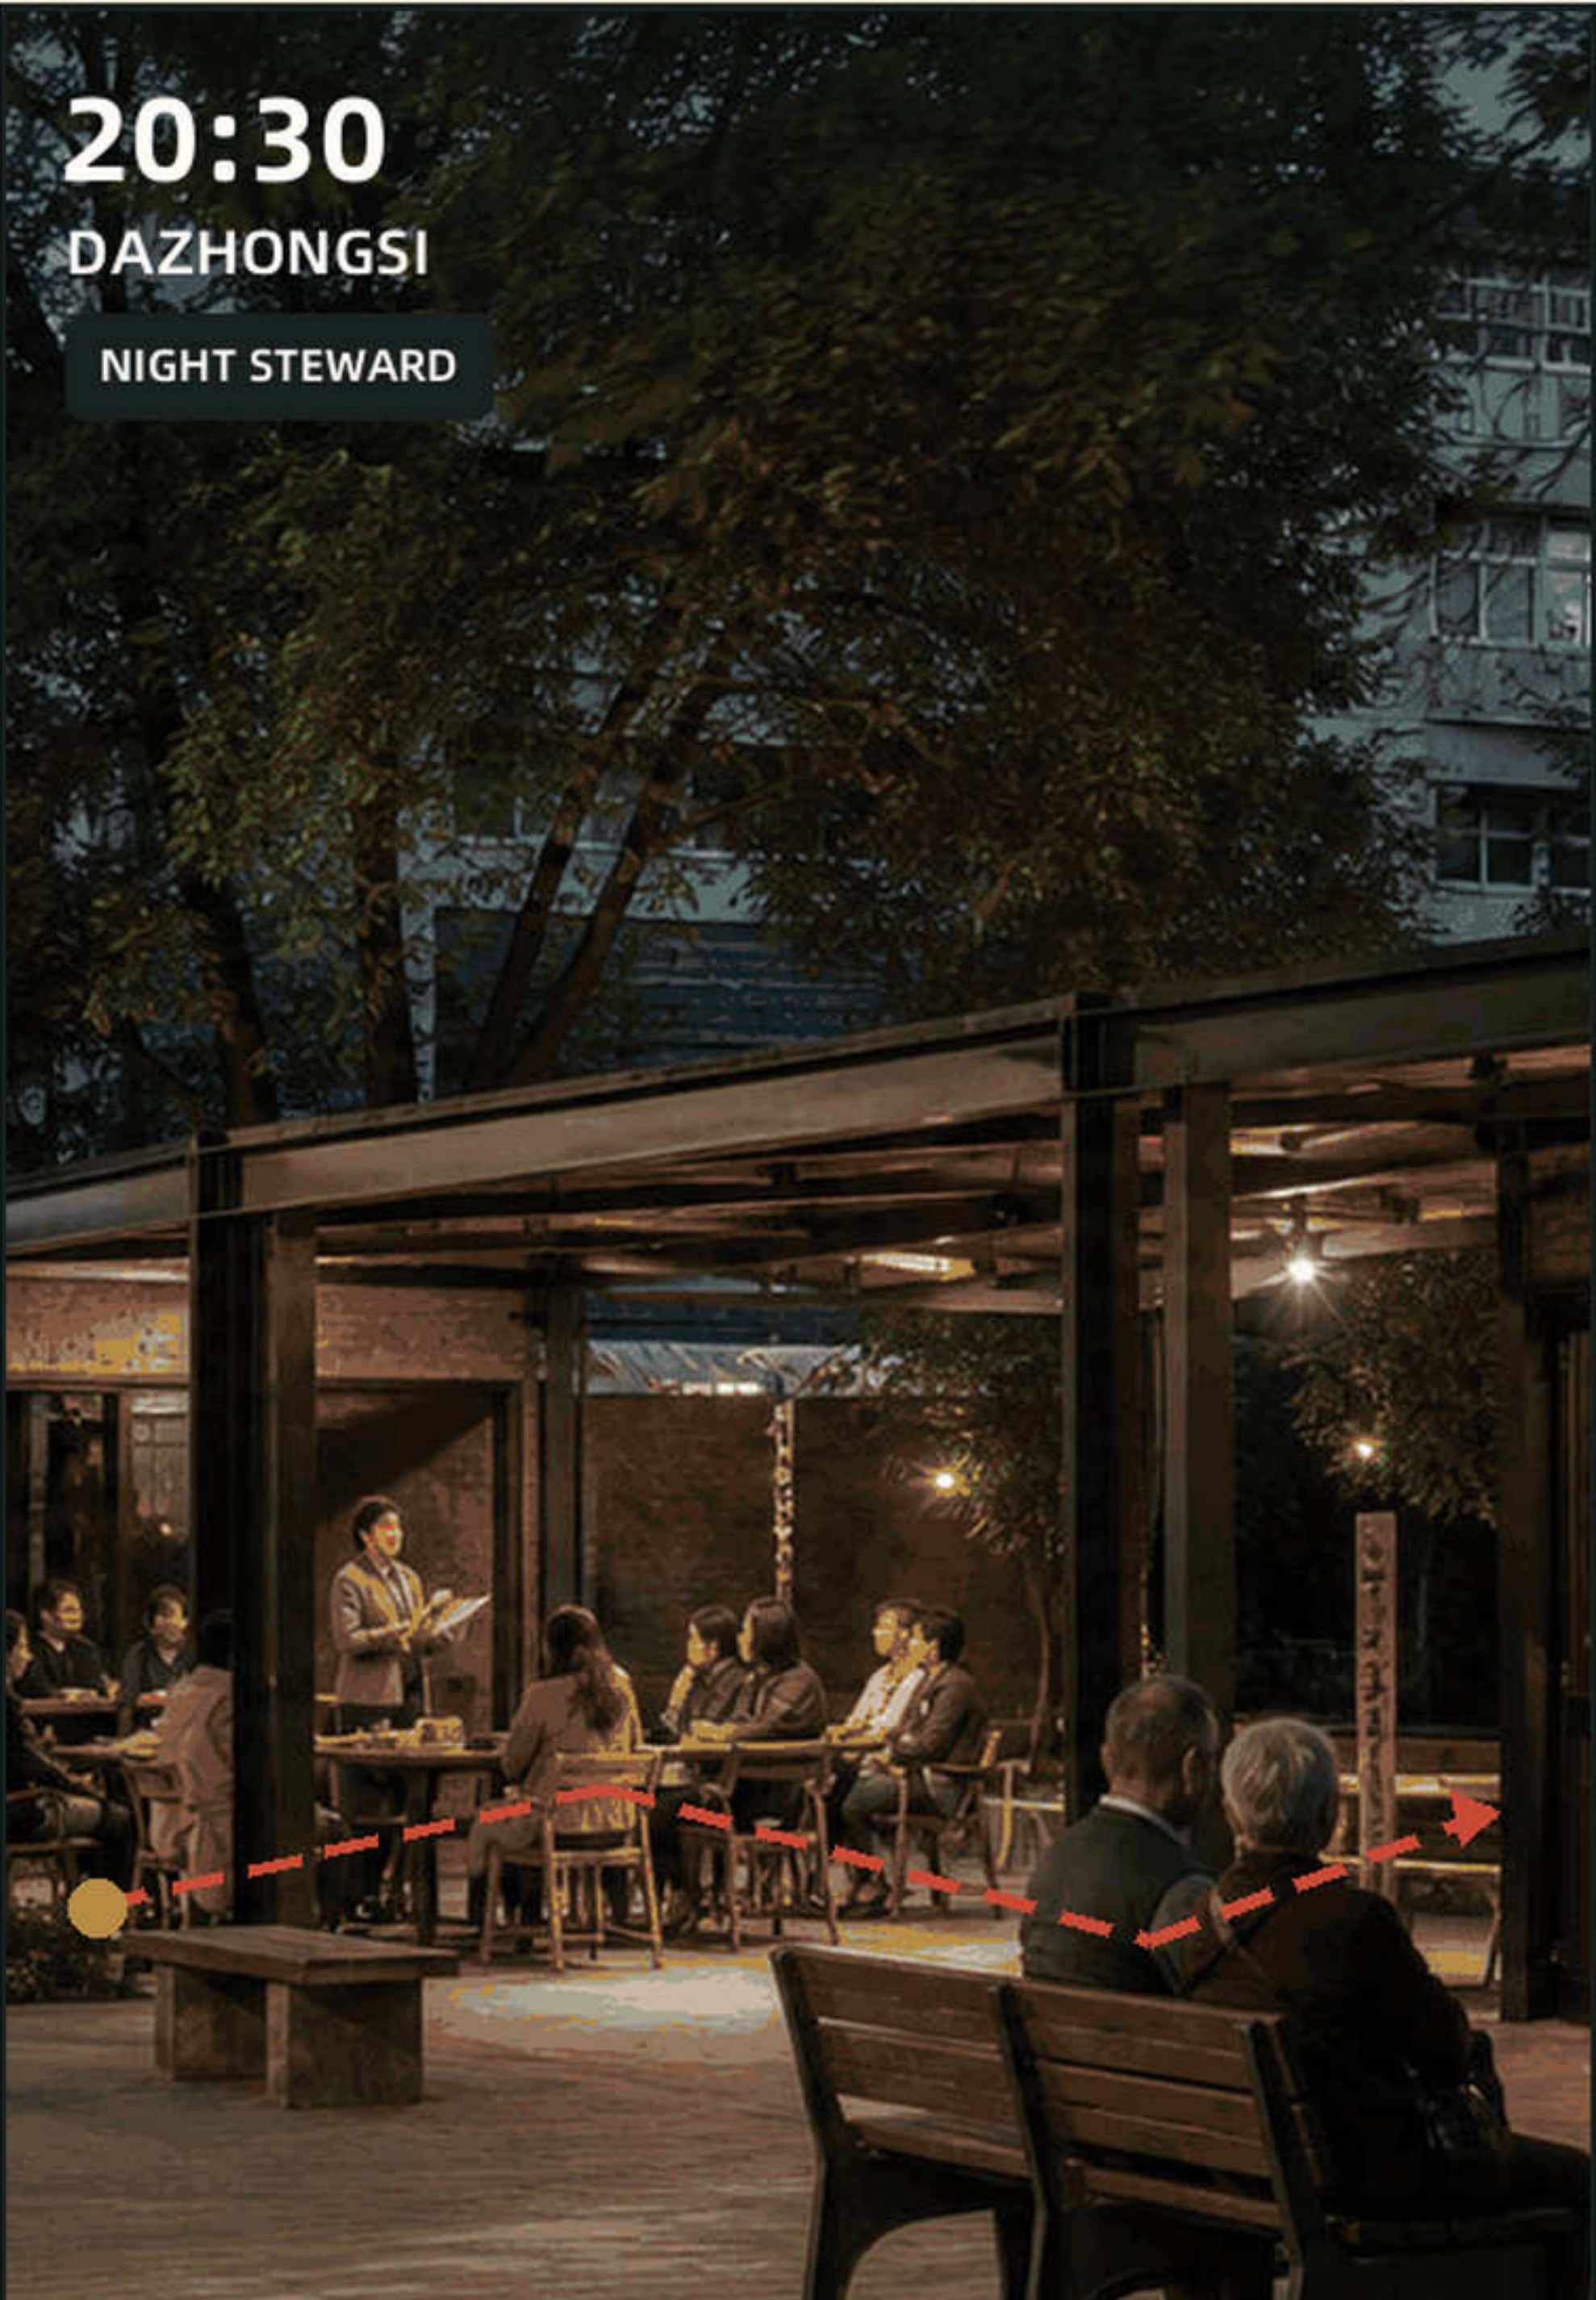

ROUTE

Metro → court → neighbourhood exit


HUMAN FALLBACK

The steward switches the lighting circuit by hand if it fails

VISIBLE RESULT: WARM LIGHT DOES NOT GLARE INTO HOMES

FIELD CHECK | ROUTES, STAFFING AND RESULTS CAN ALL BE VERIFIED ON SITE

OPEN-CITY-AI / HAIDIAN

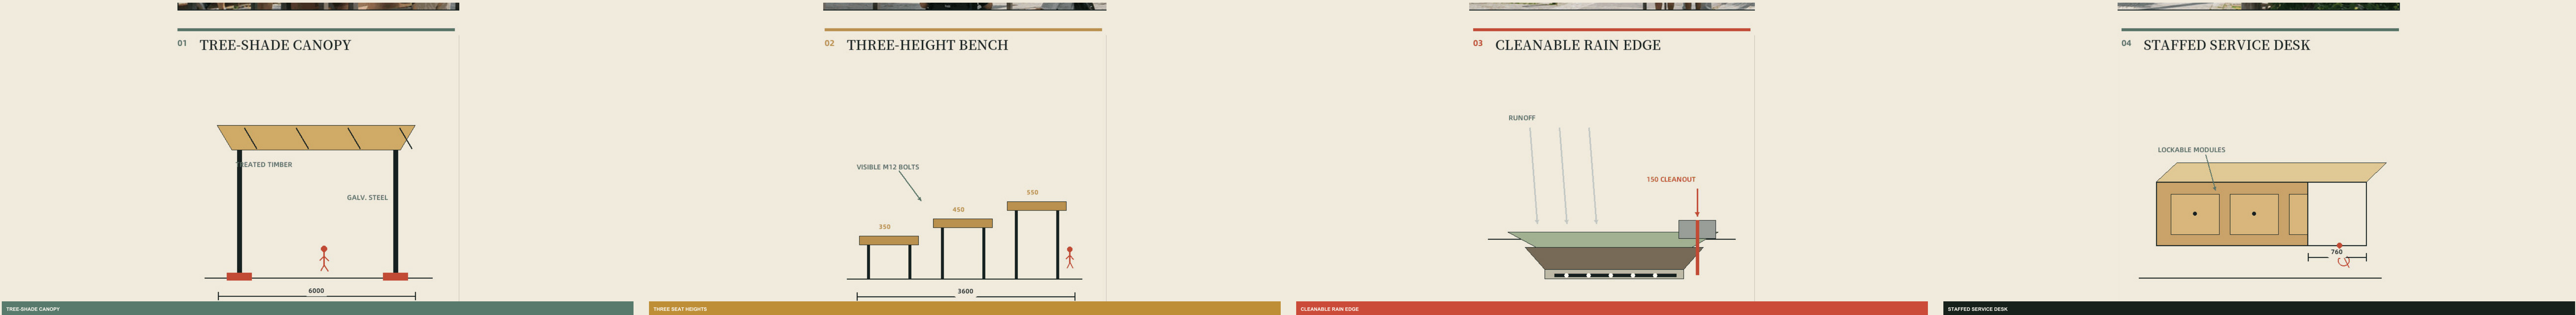

09

FIX THE BREAKS, THEN DECIDE WHAT STAYS


One real base, three cumulative steps; public works, proposal and approvals stay separate

BUILT

UNDER CONSTRUCTION

PROPOSAL

APPROVAL REQUIRED

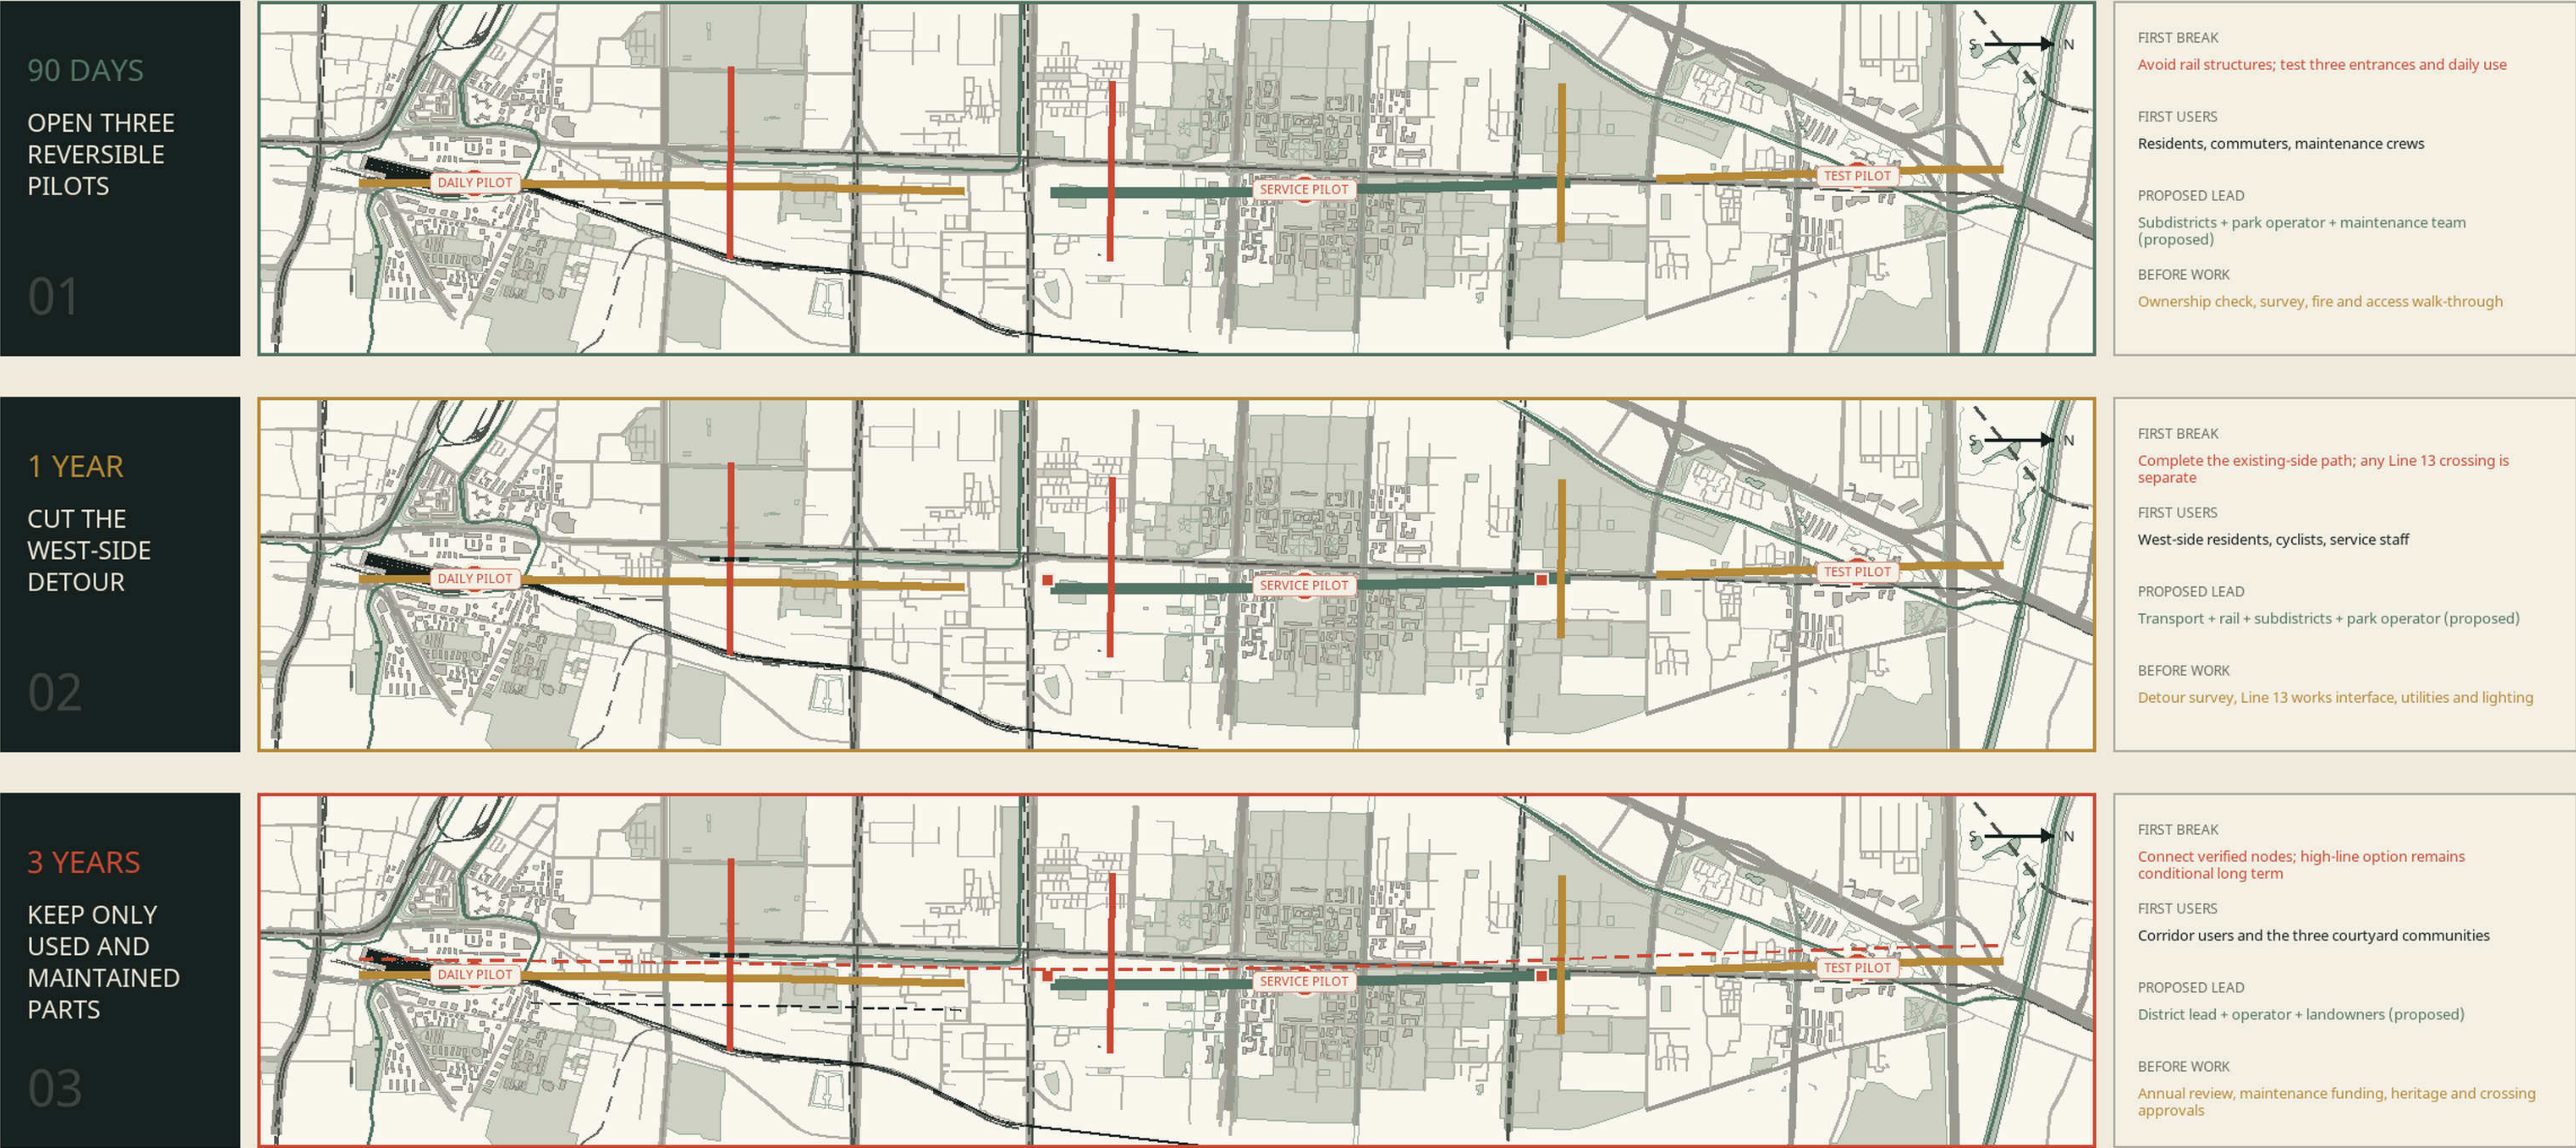

Red marks proposal additions only; black dash means heritage, rail or crossing approval is still required.

OSM context only | Concept boundaries require survey, ownership and approvals

EVIDENCE-GATED SEQUENCE | NOT A COMMITTED CONSTRUCTION SCHEDULE

90 DAYS

Three courtyard trials, entrance counts, conflict map, and repair records.

1 YEAR

Repair only measured crossings, rain-garden interfaces, and reading points.

3 YEARS

Recheck movement, shade, and maintenance before anything becomes permanent.

Four public checks placed in the real Zhichun Road-Dazhongsi context



MAP CONTEXT IS VERIFIED; LEVELS, TOILET AND SERVICES STILL NEED FIELD CHECKS

OPEN-CITY-AI / HAIDIAN



- **PRECEDENTS**
Inform method, never site facts