


京张1909 · AI创新带

总体方案 — 一轨两河三站 · 六轴多点

总览地图·用地结构与要素落位 (高德基底·北向上)

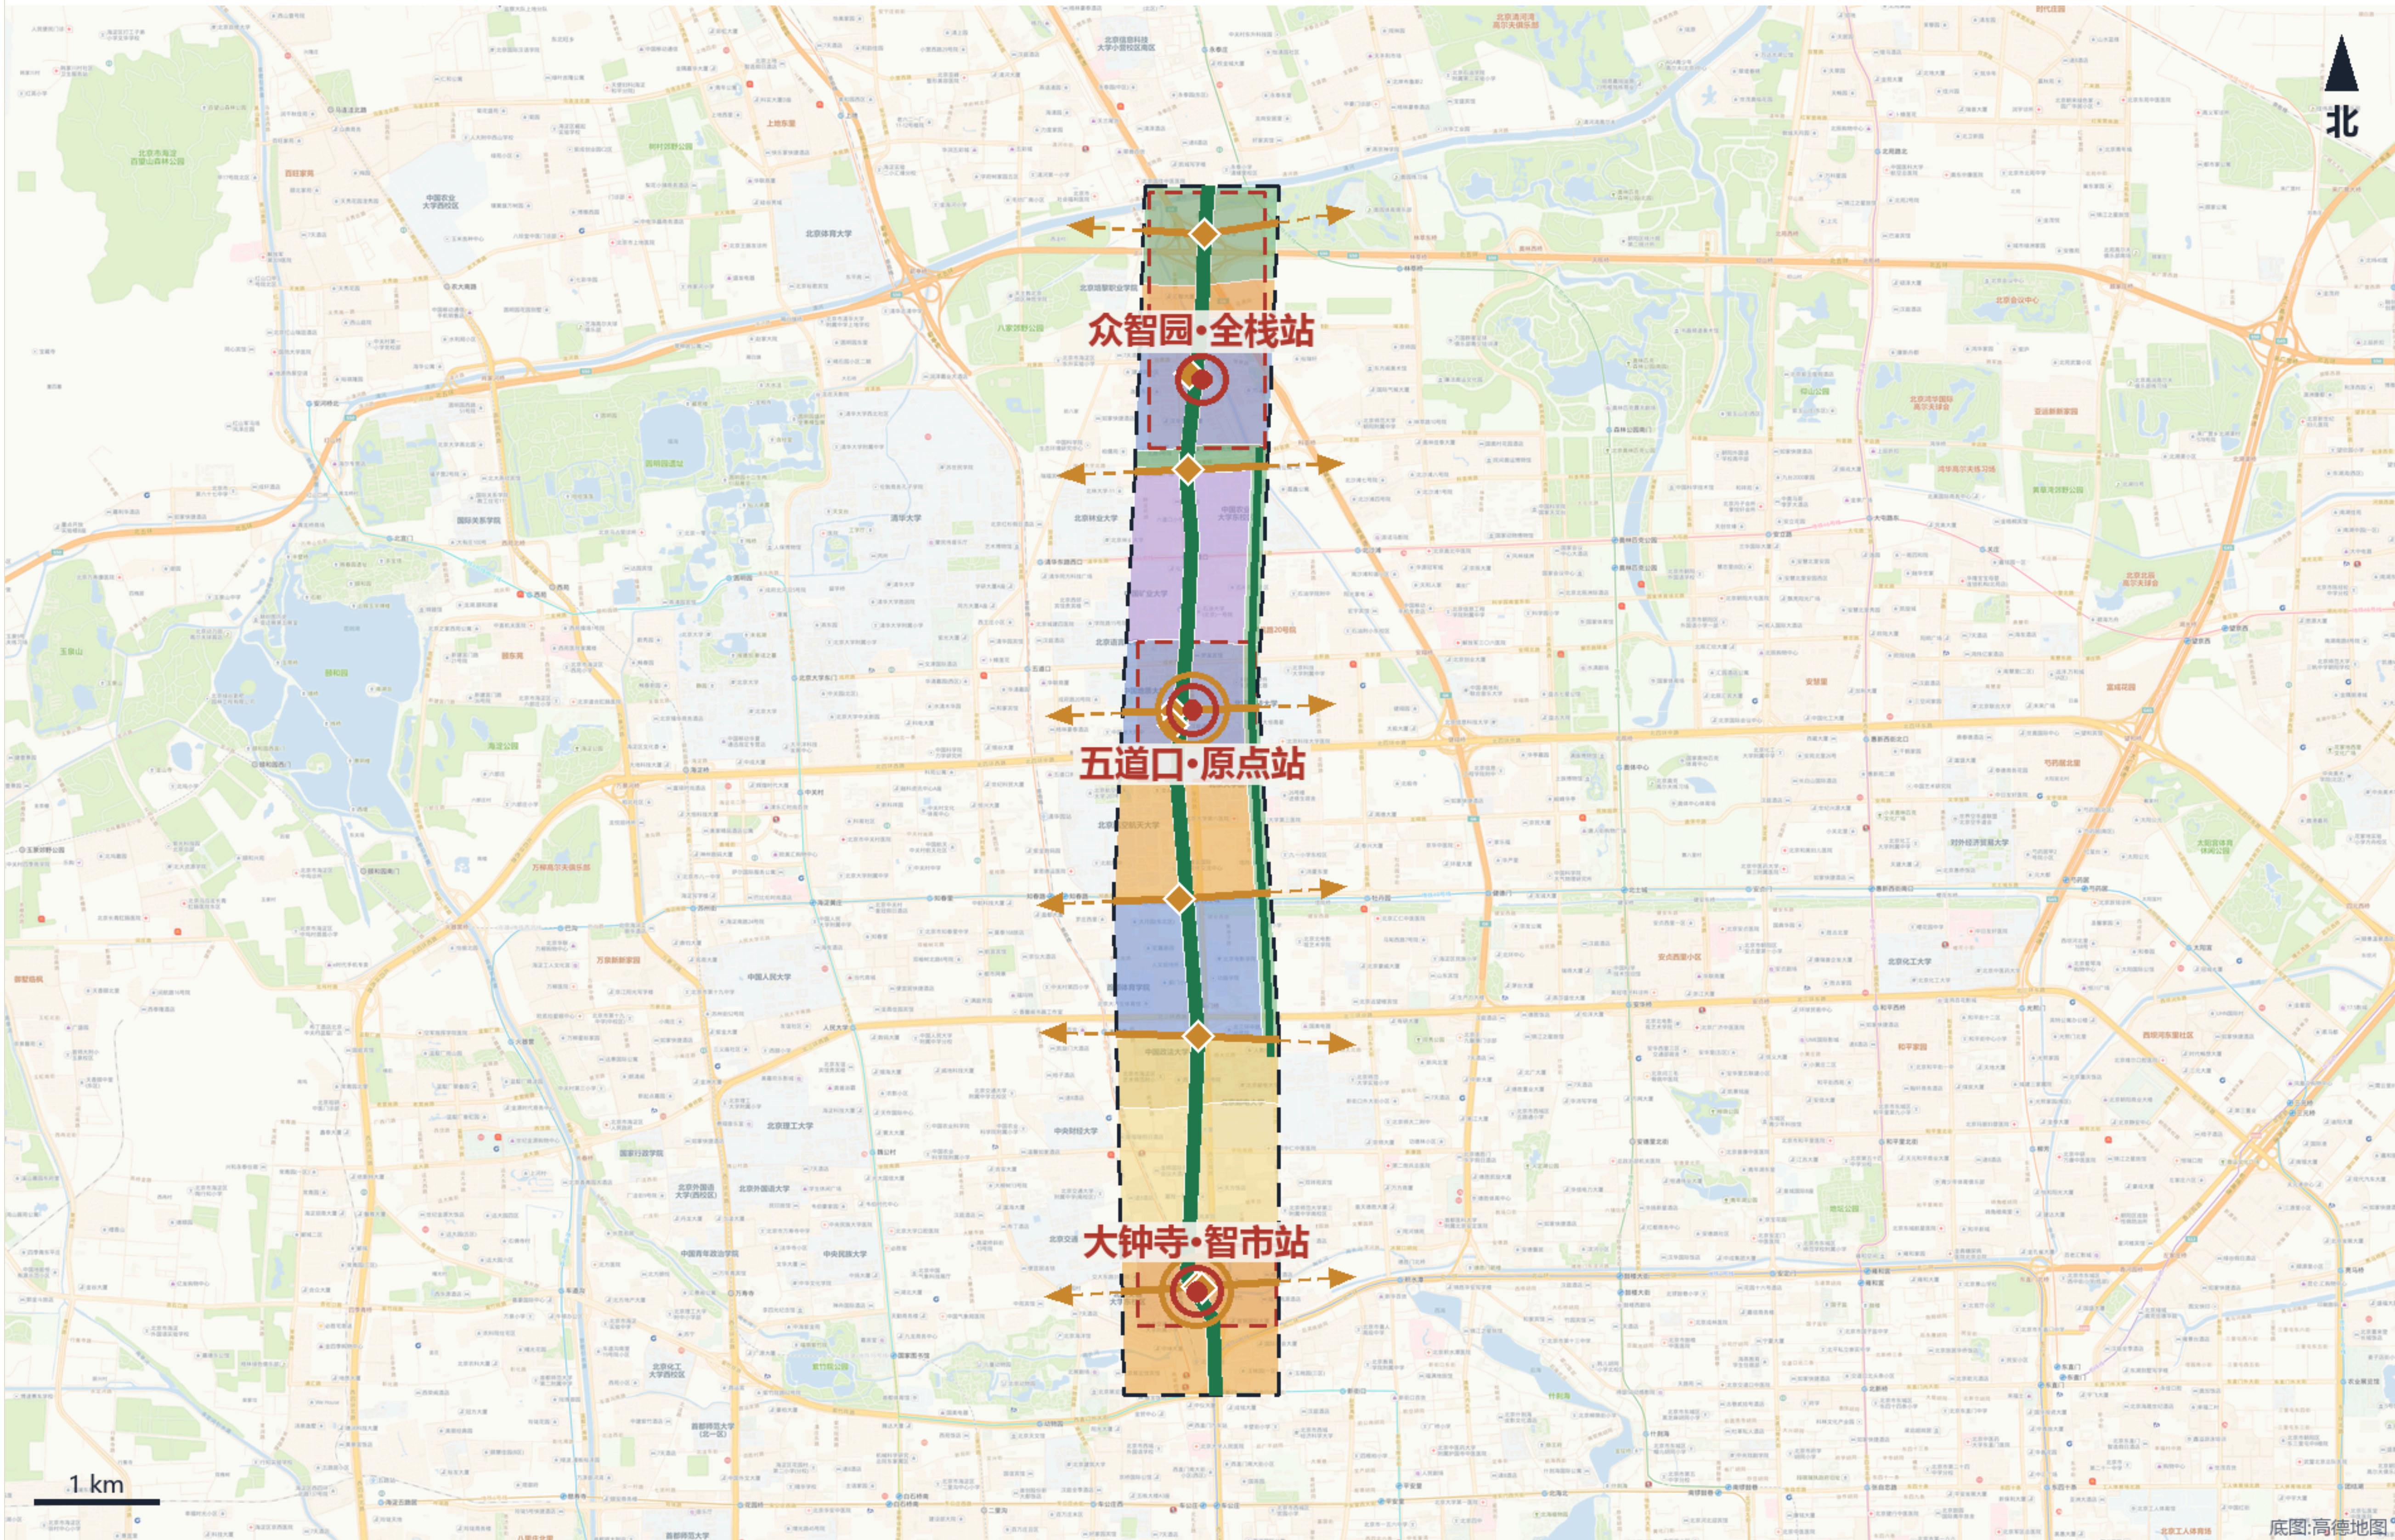

商业服务业 09 256 ha 居住 0701 132 ha 社区服务 0702 66 ha 科研 0802 306 ha 教育 0804 113 ha 公园绿地 1401 245 ha 防护绿地 1402 18 ha 广场 1403 5 ha 既有京张铁路线位 (遗产轨线脊) 现状主干路 重点区域 (临时约束) 站前广场与公共空间 示范更新建筑基底 蓝绿开敞空间

临时约束边界: 本册全部圈层与面积标注基于仓库登记的临时范型线, 仅供方案讨论与自检; 官方发布后整体重置。

一轨

京张遗产轨线慢行文化脊: 沿 1909 年线位设置约 9.8 公里、宽约 116 米遗产公园脊, 慢行、文化展示与 AI 场景复合轴 (控观 “一带” 核心段)。

六轴多点

六条东西缝合轴 (大钟寺/学院路/知春路/五道口/五环上苑/清河滨水) 响应控观 “南北贯通、东西连通”; 遗产脊与 9 条横向线路 18 处穿廊交点按 “一线一点” 设 9 处道岔广场, 对位控观 “多点” 体系。

两河

清河生态客厅 (北端约 83.4 公顷滨水界面) × 小月河场景连接绿廊 (场地内接驳段, 沿东边线内缩约 62 米, 河道本体在场地外), 衔接控观景观结构 “三带”。

三站

大钟寺·智市站、五道口·原点站、众智园·全栈站为接力折返点 (智市、原点承接控观 “两心”); 两翼 (中关村科技服务翼为西翼、小月河场景赋能翼为东翼) 自五道口分岔、向北汇合于众智园, 构成 “人” 字两翼。

核心指标

约 1,141.3 公顷

总体设计范围
公告约 11.4 平方公里, 临时边界复算一致

23.5%

绿地率 (复算)
green_space 图层开集 / 提交范围; 口径对照见正文

约 9.8 公里

遗产轨线慢行文化脊
串联三站与全部文化节点

63 个

用地单元
同一切割线平面切分, 无缝无重叠全覆盖

19 处

示范性更新建筑
新建 8 + 改造 9 + 保留 2; 拆除待现状调查

3 处 / 约 368.4 公顷

重点区域
众智园·原点社区 - 大钟寺 (临时范围)

分期实施

一期

约 748.9 公顷

三站首开区与遗产轨线指示范段

二期

约 167.6 公顷

原点社区从源与清河界面, 众智园概念先行区启动

三期

约 224.7 公顷

众智园全栈区与两河客厅全图建成

京张1909 · AI创新带

证据与运营 — 可复算、可审计、可迭代

AI+ 场景体系

编号	场景	空间载体	摘要
01	AI慢行导航	遗产轨线脊全线	可解释导航与低侵入传感识别断点与衔接节点，输出人工可复核建议
02	企业服务Copilot	三站服务驿站	政策检索、空间匹配与申报导航，结论附来源与置信度
03	公共安全与活动运营复核	站前广场群	人流与活动风险只微聚合预警，处置决定由人工作出
04	低速无人配送测试	原点社区内街	限定路线、限速、可回退的配送试点，数据分级开放
05	AI文化导览	1909记忆线路	多语导览讲述京张铁路与中关村创新史，史实经文献复核
06	AI健康服务导航	社区服务节点	连接周边医疗与健康资源，不提供诊断结论；医疗等公共服务场所保留现场指导与人工办理通道，传统服务与智能服务并行按图力发（2020）45号政策背景把握（其阶段性目标已到期，仅作参考设计参考）
07	安全治理沙盘（测试）	众智园实验楼	标准制定、可信评测与模型红队测试的可参观协作节点
08	数据算力驿站（测试）	三站公共服务点	分布式算力与低碳能源融合的新基建原型，供专业团队深化
09	开源发布厅	原点站广场	成果发布、代码贡献展示与小型路演
10	低碳运行监测（测试）	清河凉水客厅	雨洪、能耗与碳排放监测展示，指标口径公开
11	数据要素会客厅	大钟寺片区	以合规、授权、可审计为前提的数据流通城市界面
12	1909全球活动周路线	一带公共空间	开发者节、场景开放日与朝圣路线的年度运营组合

指标复算

提交范围面积	1,141.3 公顷
蓝绿开敞空间面积	267.9 公顷
蓝绿开敞空间占比	23.5%
公共空间面积	6.3 公顷
公共空间占比	0.6%
示范建筑基底面积	13.0 公顷
示范建筑基底占比（设计值）	1.1%
道路中心线总长	25,471 m
遗产轨线脊长度	9,800 m
一期面积	748.9 公顷
二期面积	167.6 公顷
三期面积	224.7 公顷
重点区域数量	3
用地单元数量	63

数据缺口（待正式数据补齐）：容积率、建筑高度上限、法定建筑密度、法定绿地率管控、退线控制 — 待正式数据补齐

任务覆盖与专业矩阵

- 公告任务 17/17 全覆盖
- 智能体任务 6/6 全覆盖
- 正式设计深度 15/15 完成
- 专业标准响应 9 条（含 3 条非强制新增标准）


来源分层

- SITE-PACKAGE** — 任务书、校毕、设计空间、限值、模式与临时边界等场地包材料。
- SOURCE-REGISTRY** — 区分 formal 可用、背景、临时与待审资料的登记册。
- PROCESSED-FACT-PACK** — 范围、任务、资料用途与缺资料清单的导航图，非新权威来源。
- BOUNDARY-SOURCE** — 提交总体设计范围（临时约束），仅用于生成、展示与临时自信。
- KEY-AREA-SOURCE** — 三处重点区域范围（临时约束），仅用于生成、展示与临时自信。
- OFFICIAL-ANNOUNCEMENT** — 公告 1.3/1.4/1.5 的任务、范围、面积、语言与成果最终主控依据。
- AGENT-TASKBOOK** — 十条共创原则、六项智能体任务、场景/品牌/运营要求与边界条款。
- GLOBAL-CASE-BACKGROUND** — 全球创新生态案例为背景研究（匹兹堡、伦敦国王十字、Kista、Kendall Square、深圳南山、杭州城西、慕尼黑 Werksviertel），仅作参考参照，不作为正式证据。
- KG-DRAFT-2024** — 《北京海淀区京张铁路遗址公园沿线（人工智能创新街区重点地区）HD00-1601等街区控制性详细规划（街区层面）（2022-2035年）（草案）》公示图则（北京市规划和自然资源委员会海淀分局，2024-12-20 公示）；空间结构“一带一轴、两心多点”、三大目标定位、规模控制（常住约36.4万人、城乡建设用地约1648.1公顷、建筑规模约2369.3万平方米）、九类主导功能分区、配套设施（公共服务298处等）、整体景观结构“三带六轴、多廊多中心”、交通体系（道路网密度约8.0公里/平方公里、绿色出行80%）等结构性衔接依据。
- KG-APPROVAL-2026** — 北京日报报道（2026-08-12）：市规划自然资源委于 2026-08-11 批复《北京海淀区京张铁路遗址公园沿线（人工智能创新街区重点地区）HD00—1601等街区控制性详细规划（街区层面）（2024年—2035年）》；范围东至新街口外大街、西至中关村大街、北至成府路、南至西直门外大街，共 9 个街区约 1668.2 公顷；以绿色公共空间建设引领区域城市更新，发展大模型、智能体、具身智能等新业态，构建生活圈与创新圈融合的一刻钟社区服务圈。

总体空间结构规划图 | 一轨两河三站 · 六轴多点（高德基底 · 北向上）

高德地图真实地理基底 × 提交 GeoJSON 结构要素 × 高德 POI 设施校核——对接街区控规“一带一轴、两心多点”，承接北京AI原点社区“创新策源、创业首选”定位

总体设计范围 11.4km²（临时约束）：一轨为干 · 三站接力 · 六轴缝合 · 多点激活

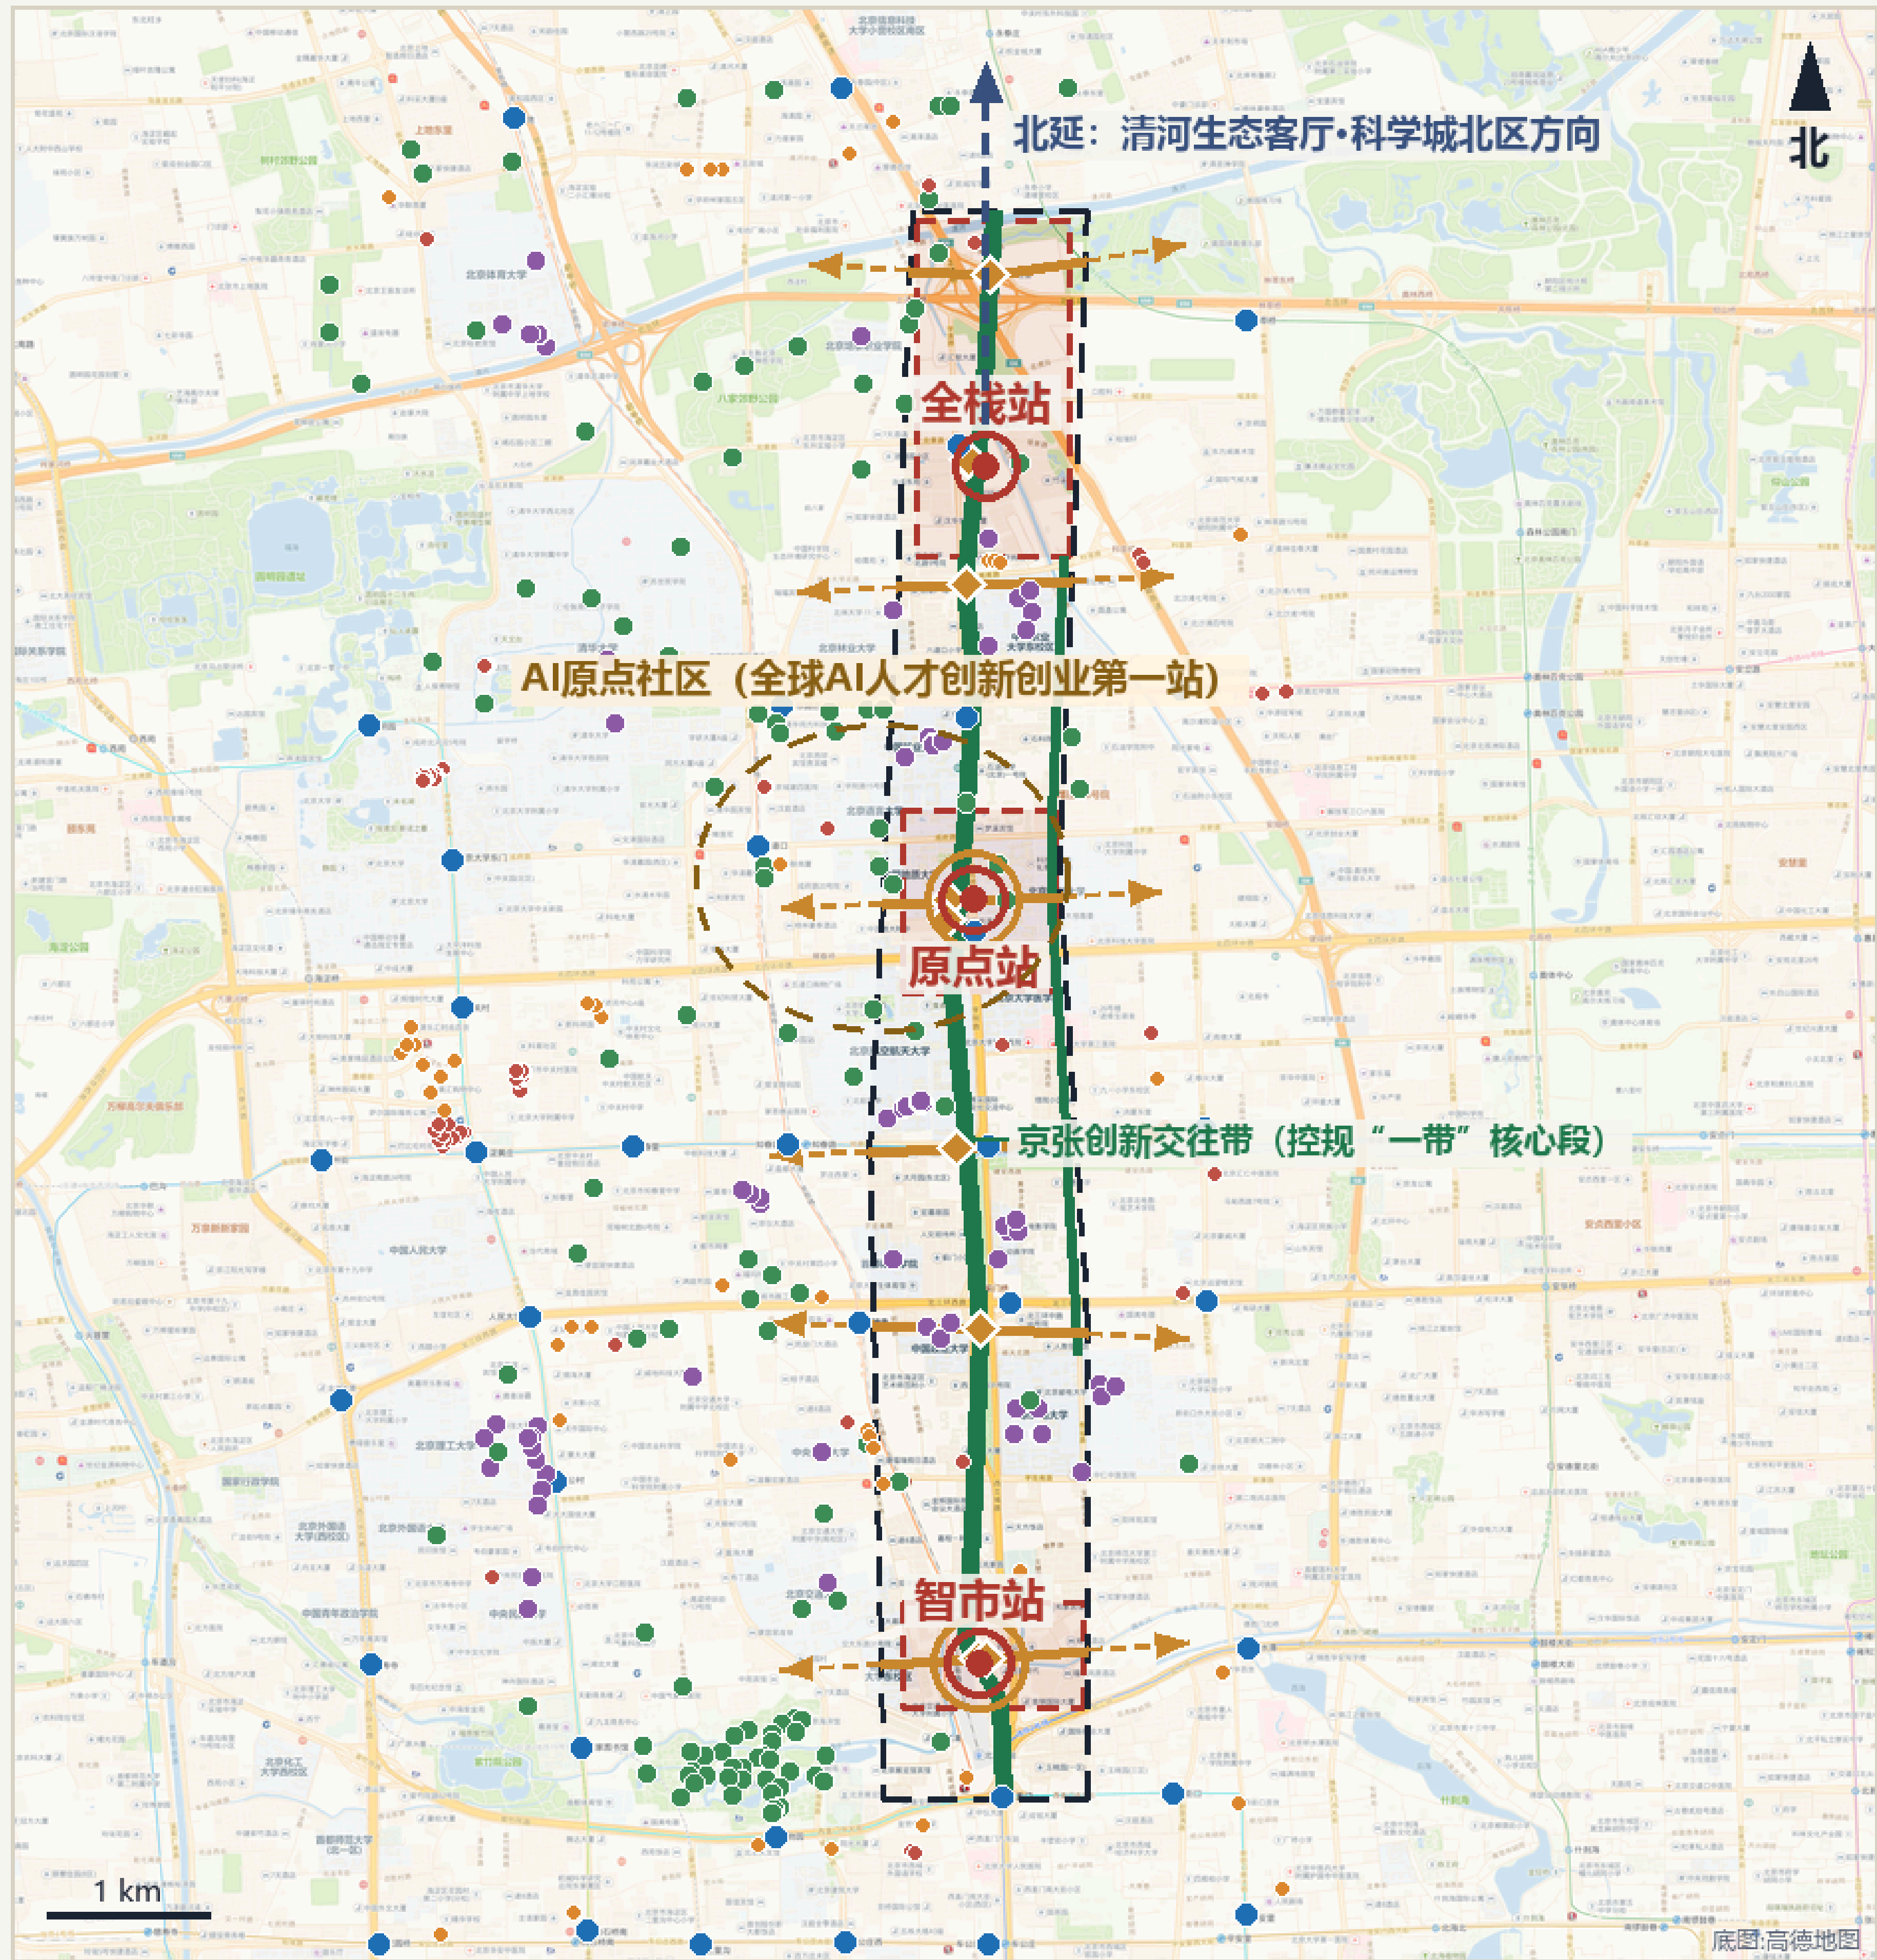

STRUCTURE / 结构要点

- 一轨：约9.8km遗产轨线慢行文化脊——控规“一带”（京张创新交往带）核心段空间骨架
- 两河：清河生态客厅×小月河场景连接绿廊（衔接景观“三带”）
- 三站：智市·原点·全栈接力折返点——承接控规“两心”，原点站对位北京AI原点社区
- 六轴：六条东西缝合轴，响应控规“南北贯通、东西连通”
- 多点：9处道岔广场节点网，对位控规“多点”体系

ALIGNMENT / 控规与AI原点社区对位

- 控规“一带一轴、两心多点”
 - 一轨三站 · 六轴多点（v1.5 起结构性衔接）
- 北京AI原点社区：“创新策源、创业首选”
 - 五道口·原点站承接——全球AI人才创新创业“第一站”的空间锚点
- “校区、园区、街区”融合·一刻钟活力生活圈
 - 原点站“校区—园区—街区”慢行缝合即其空间落位
- 大模型生态服务站“八找”全要素服务
 - 原点会客厅+开源协作中心功能策划与之呼应
- 北京市首批AI创新街区“一核多点”布局
 - 本案“一轨三站、多点成网”节点体系与之衔接

POI CHECK / 设施校核（高德）

- | | | |
|-----------|-----------|------------|
| ● 地铁站 37 | ● 高等院校 76 | ● 公园广场 121 |
| ● 综合医院 57 | ● 购物中心 48 | |

站点级设施分布与本方案“一刻钟服务圈”结构一致：轨道站点沿走廊与六轴均匀分布，高校群支撑五道口“校区—园区—街区”缝合。

LEGEND / 图例

- | | |
|------------------|--------------|
| □ 总体设计范围（临时） | □ 重点区域（临时） |
| — 遗产轨线脊（一轨） | — 东西缝合轴（六轴） |
| ◆ 道岔广场（多点） | ● 三站（两心+新中心） |
| ○ AI原点社区（运营口径示意） | |

底图：高德地图 webrd 瓦片（z15，GCJ02 墨卡托，2026-08 下载）；POI：高德开放平台周边检索（控规范围外包矩形内，地铁站 37、高校 76、公园广场 121、综合医院 57、购物中心 48）；结构要素由提交 GeoJSON 经 EPSG: