



REN-RAIL: Where AI Meets People


Centennial Jing-Zhang AI Innovation Belt — Overall Concept and Spatial Structure

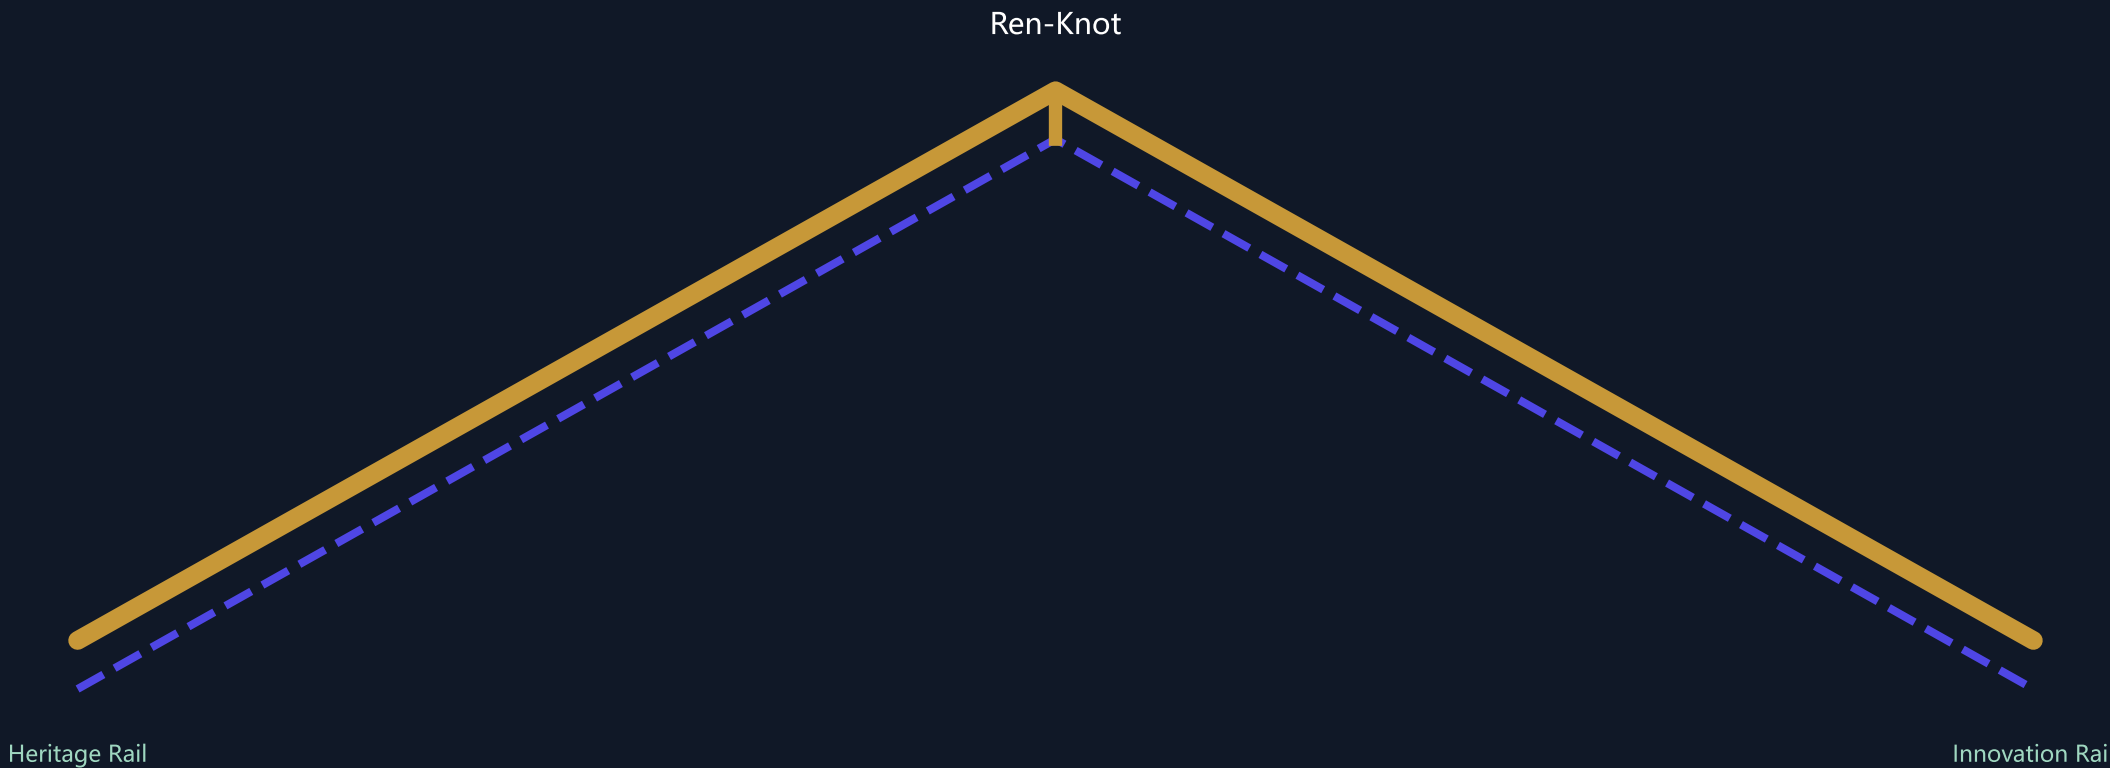

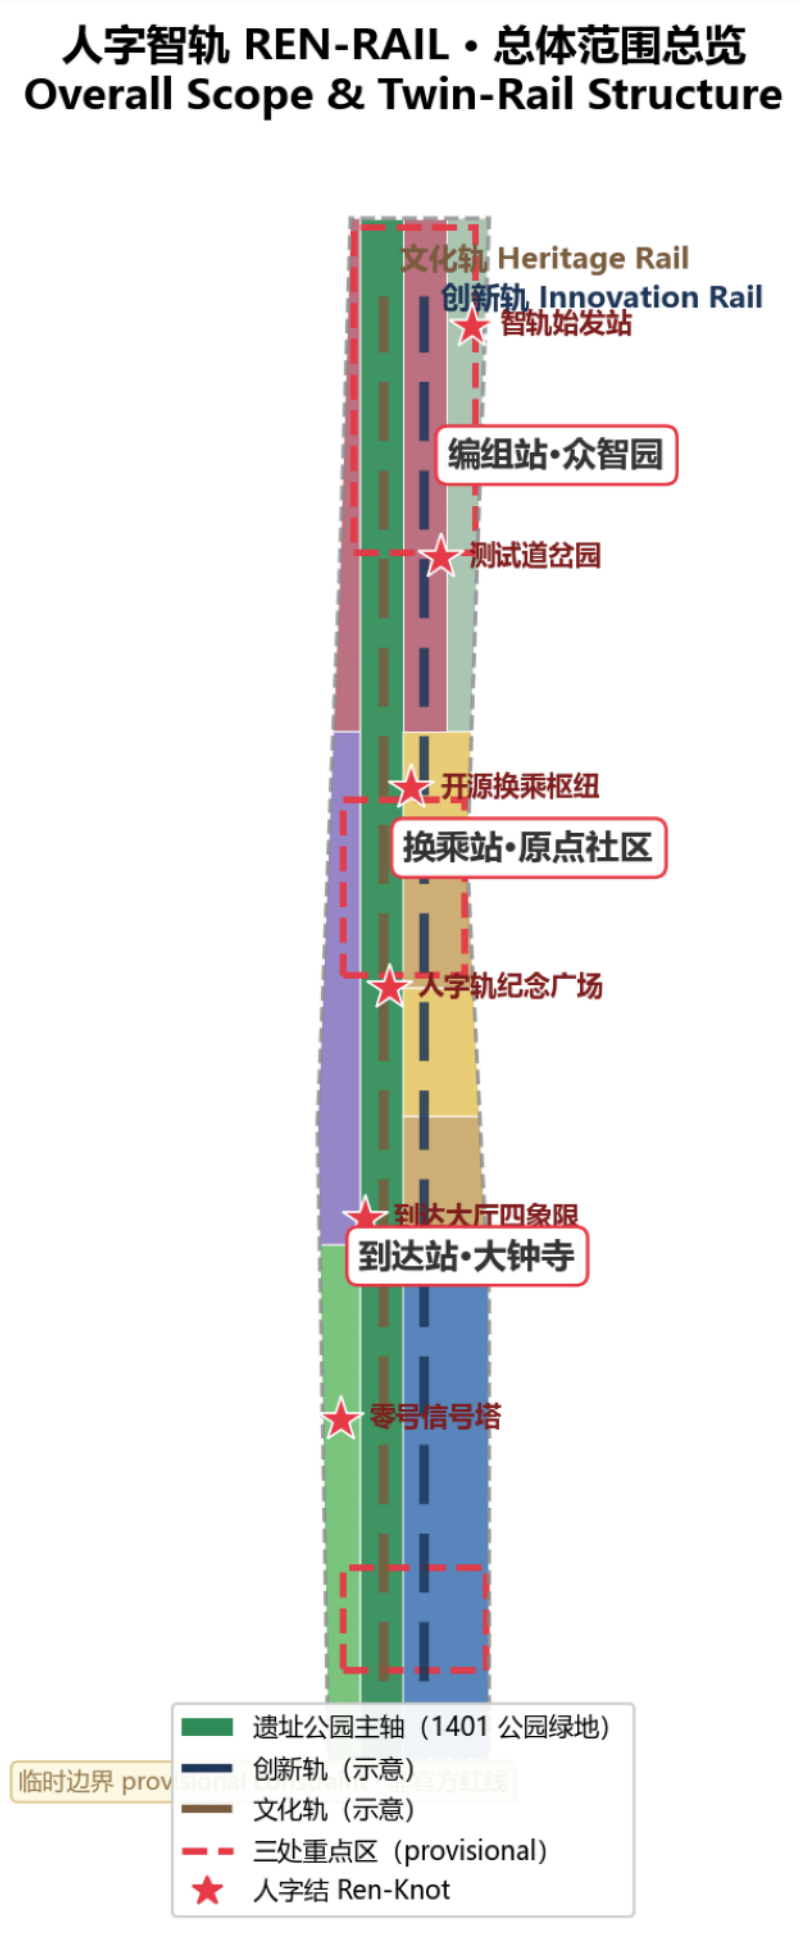

Coordinated research area 43.6 km² · Overall design area ~11.4 km² · Key detailed design area 368.4 ha


用地结构与建筑基底示意
Land-Use Structure & Indicative Building Footprints

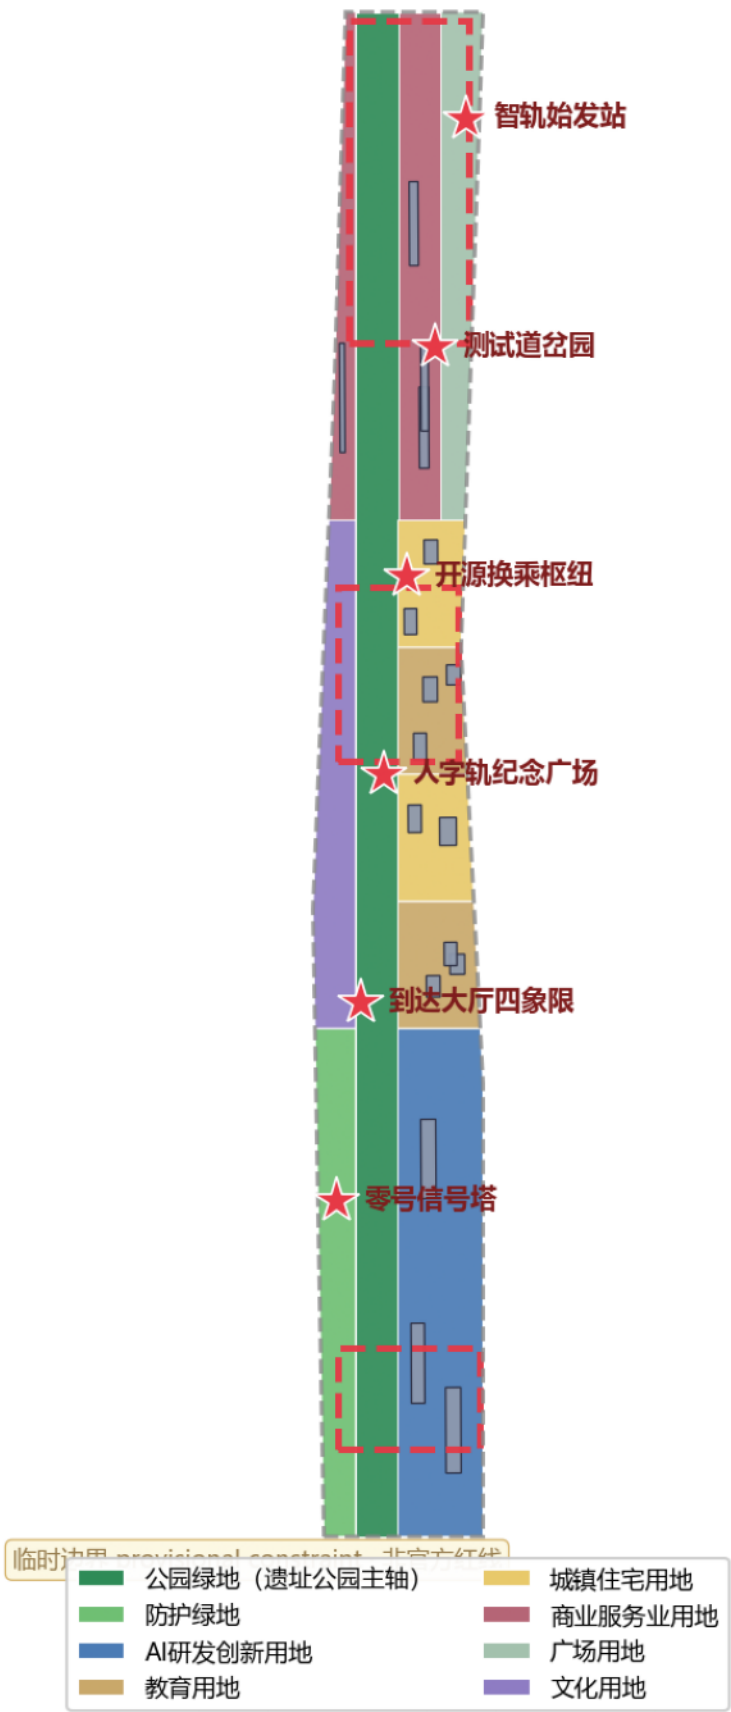

One belt, twin rails, six knots, four transversals · 1401 park green spine · 0802 AI R&D / 0804 education / 05 commercial / 1403 plaza


三处重点区域详细设计 (provisional 范围)
Three Key Detailed-Design Areas

编组站 · 众智园 AI 自主创新加速区
Marshalling Yard · Zhongzhiyuan

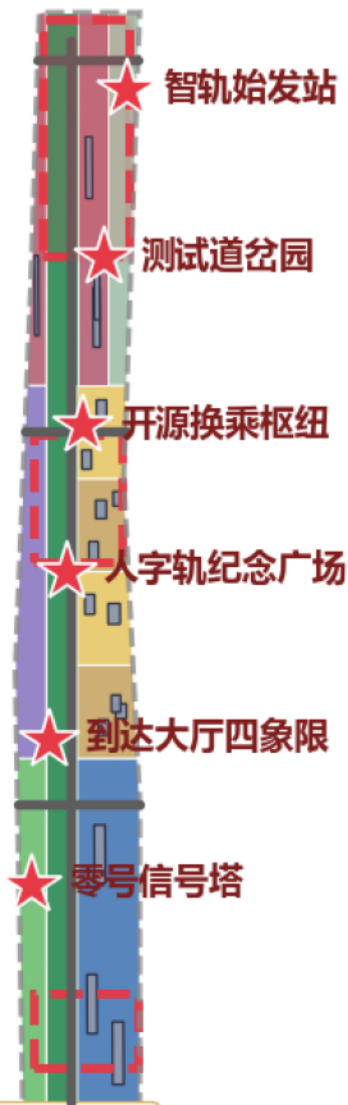


临时边界 provisional constraint · 非官方红线

换乘站 · 北京 AI 原点社区
Transfer Hub · Beijing AI Origin Community

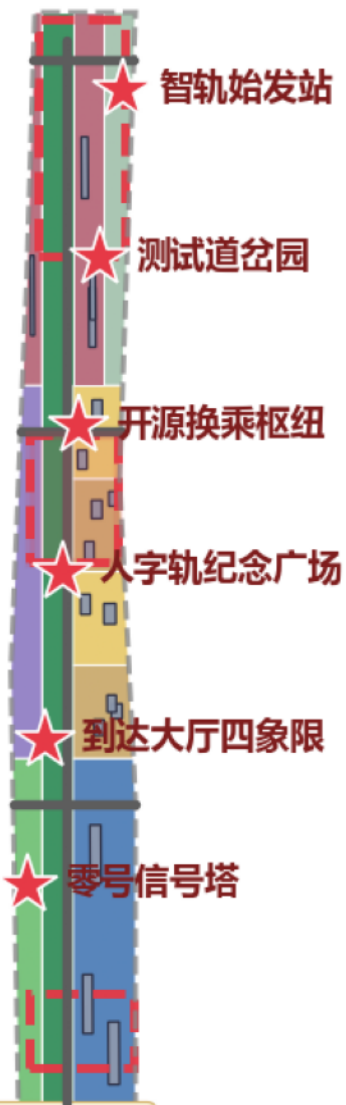

临时边界 provisional constraint · 非官方红线

到达站 · 大钟寺 AI 产业聚集区
Arrival Gate · Dazhongsi

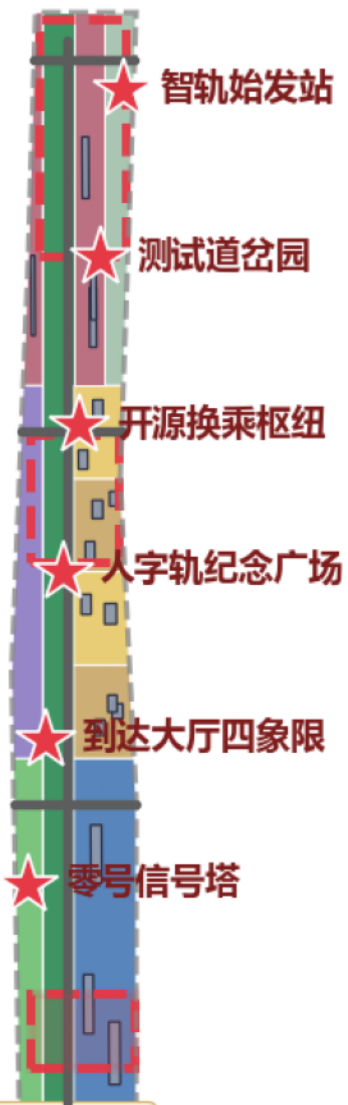


临时边界 provisional constraint · 非官方红线

Marshalling Yard (Zhongzhiyuan) ~192.1 ha / Transfer Hub (Origin Community) ~104.3 ha / Arrival Gate (Dazhongsi) ~72.0 ha


Conceptual drawings; spatial conclusions follow GeoJSON / metrics.json / compliance matrices.

交通缝合与蓝绿公共空间系统
Mobility Stitching & Blue-Green Public Space System

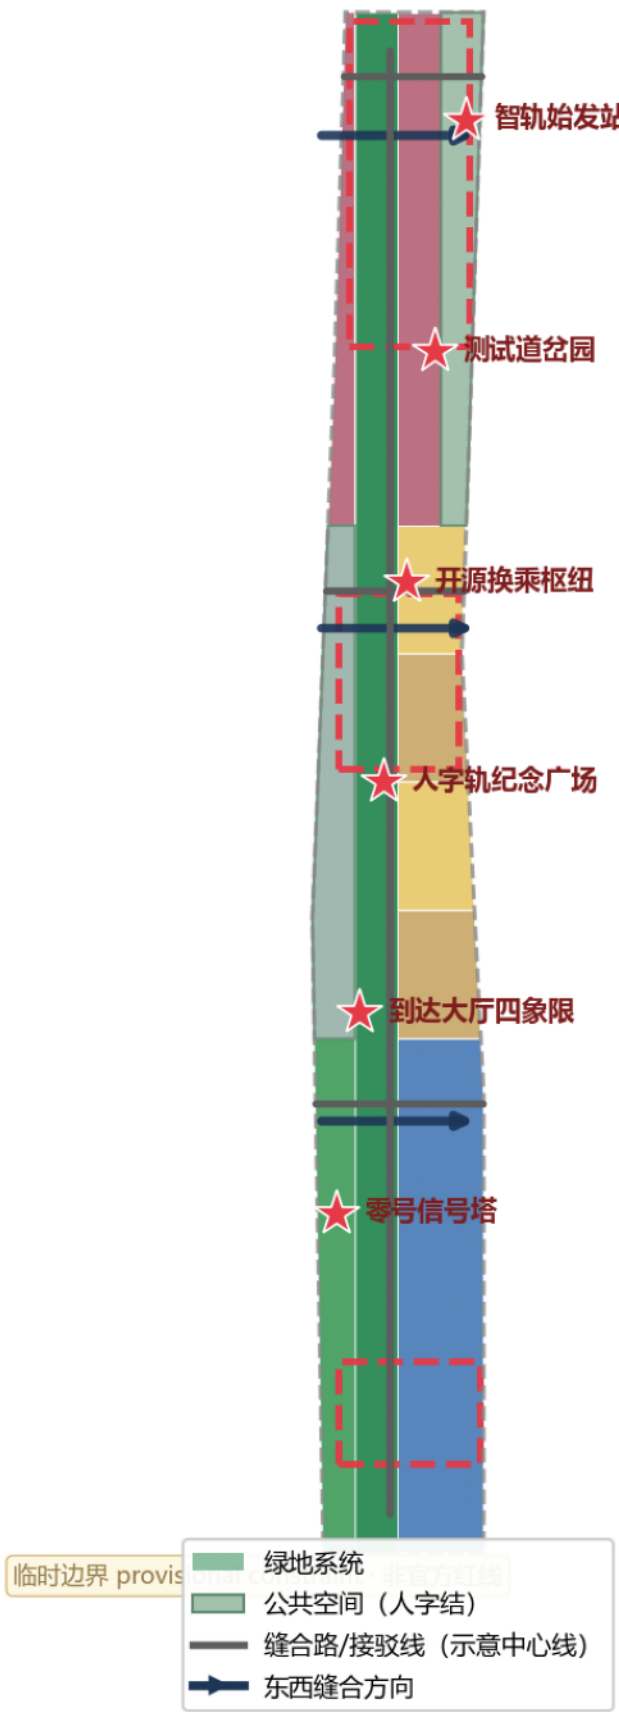


Four transversals + one longitudinal skeleton · Ren-Knot public-space system · green ratio 36.4% · public-space ratio 15.6%

核心比例指标 (EPSG:4548 复算)
Core Ratio Metrics (recalculated in EPSG:4548)

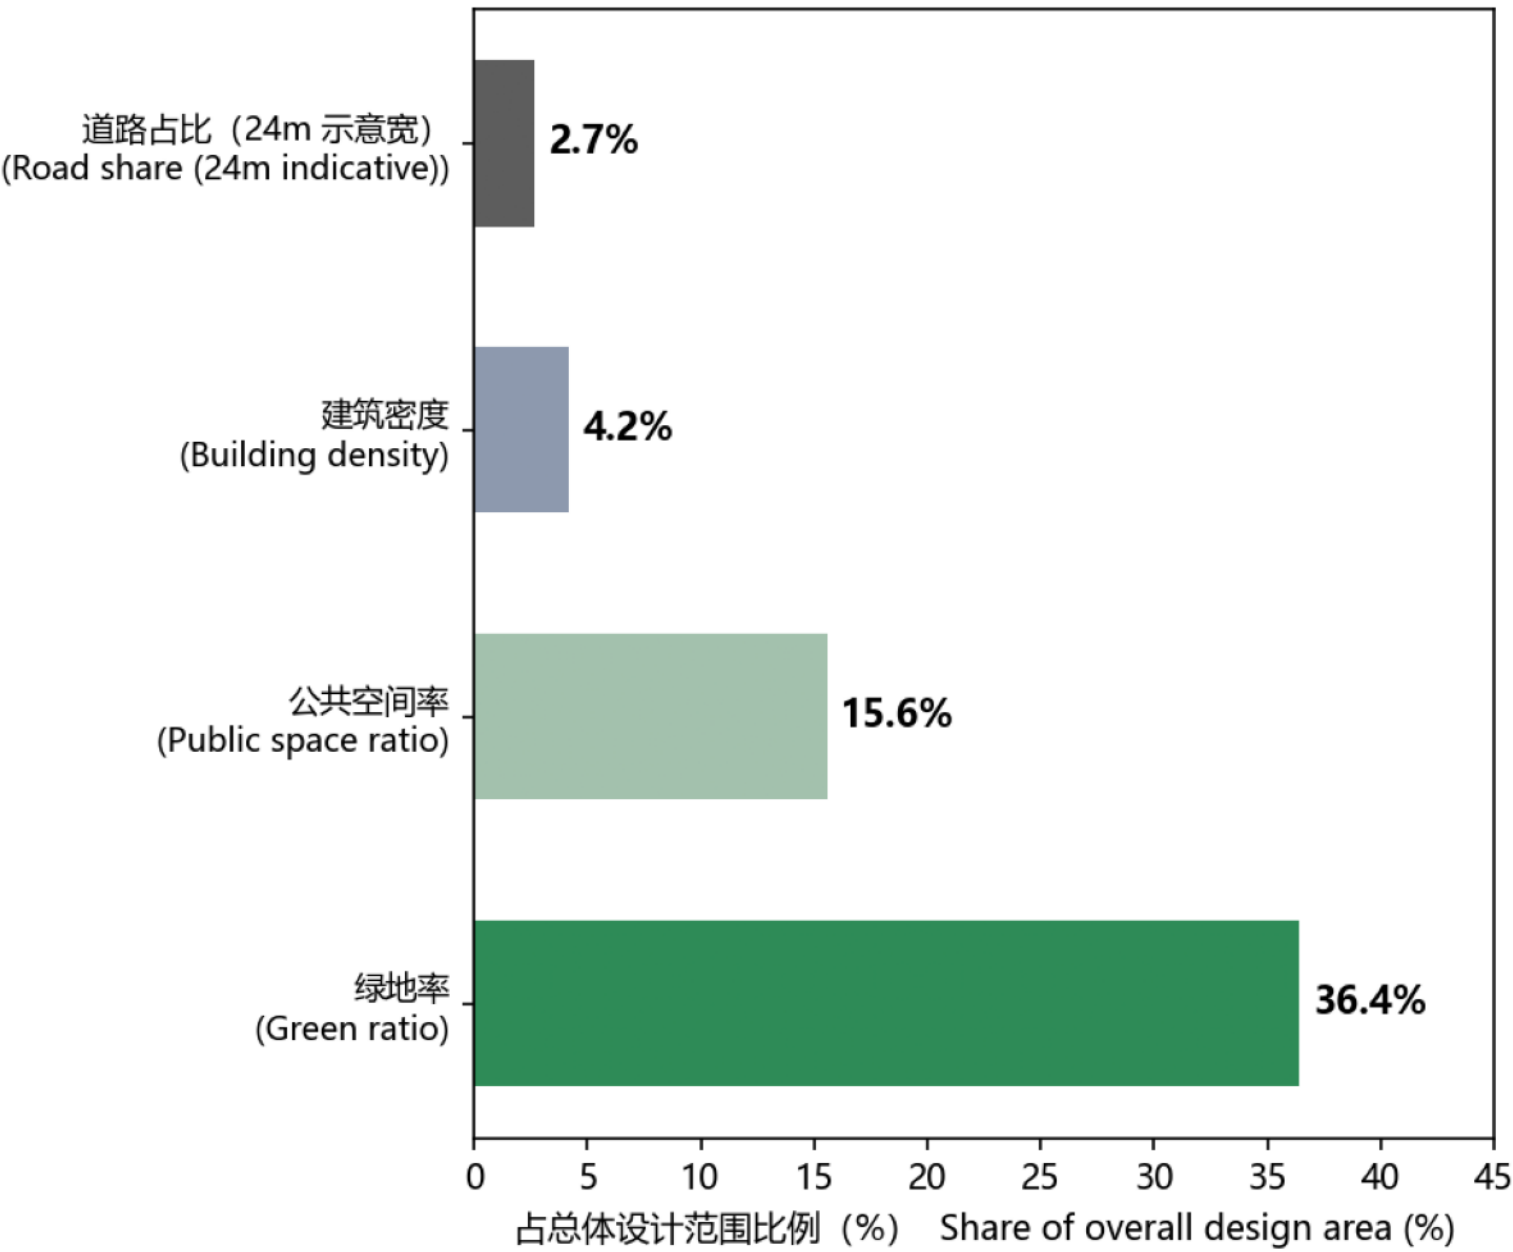

分期与重点区面积复算
Phasing & Key-Area Areas (recalculated)

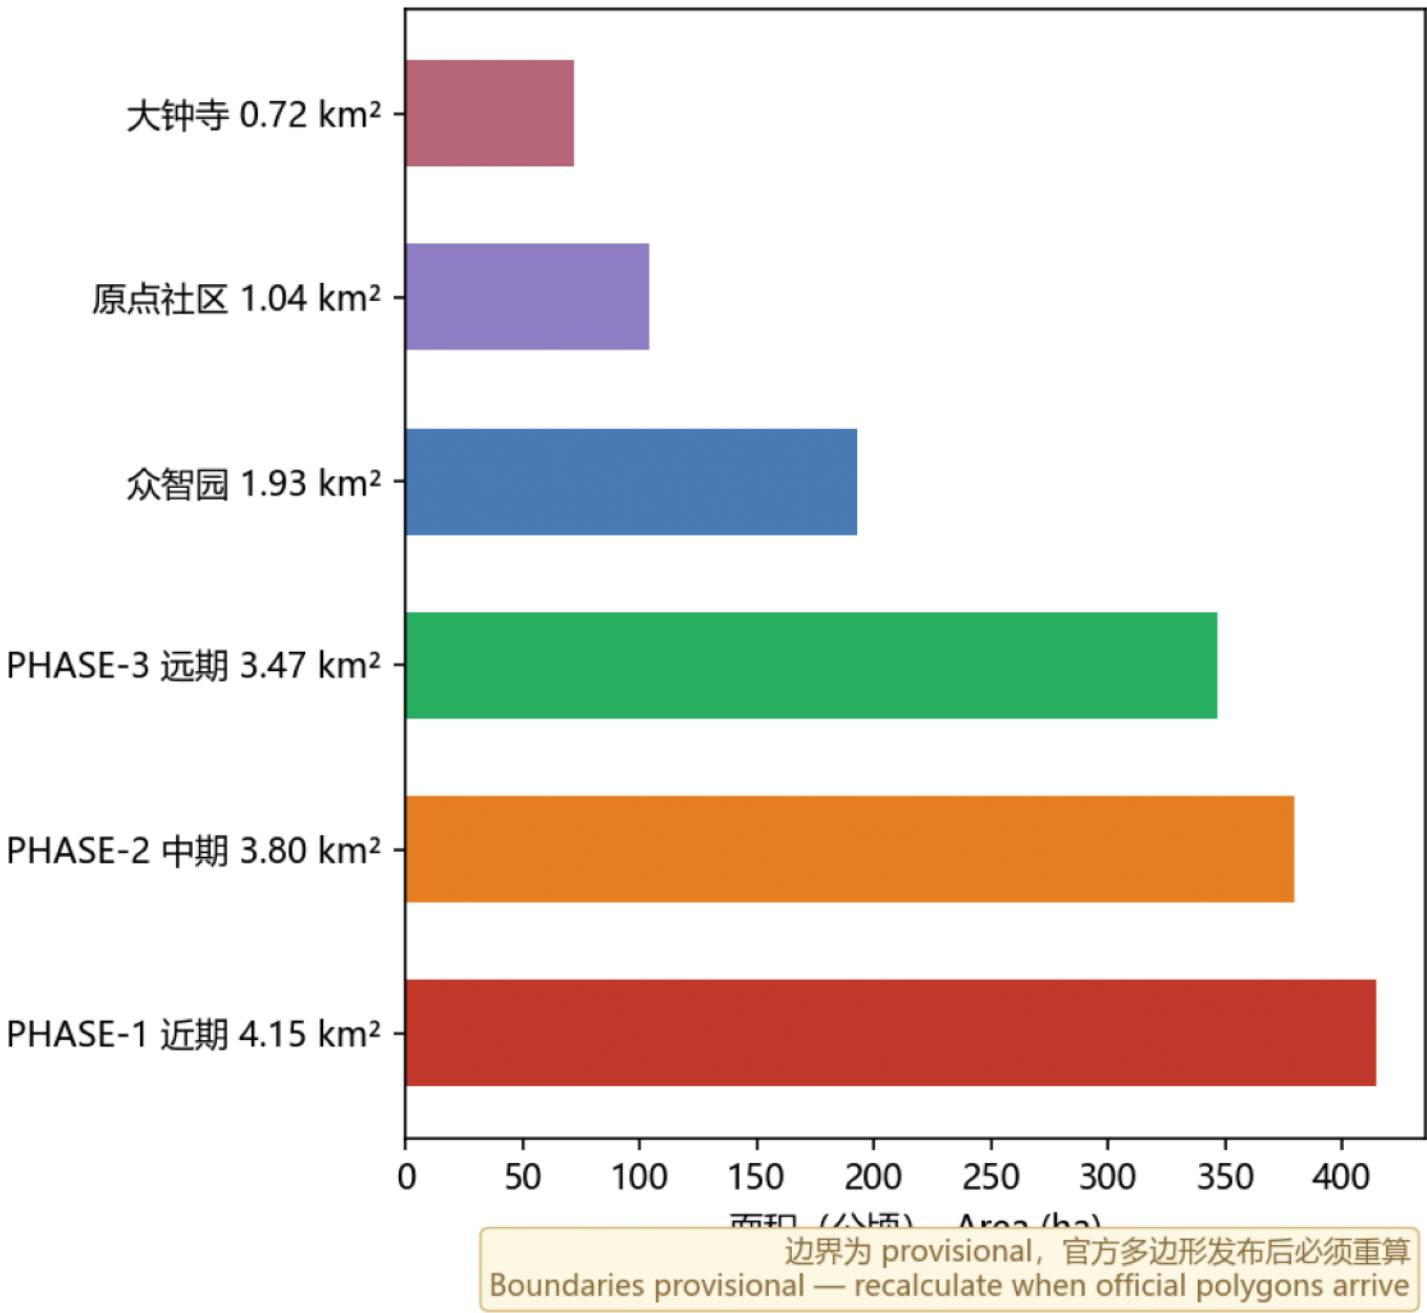

Site boundary area	site_area_sqm	11,412,825.386 m²
Green ratio	green_ratio	0.364
Public-space ratio	public_space_ratio	0.156
Building density ratio	building_density_ratio	0.042
Road centerline length	road_centerline_length_km	12.681 km
Floor area ratio (pending official limits)	floor_area_ratio	unknown

All spatial metrics recomputed from submitted geometry in EPSG:4548 (metrics.json, with confidence); control indicators stay status=unknown until official regulatory-plan data arrives.