



京张AI共生带 SIGMA LINK · 总体空间结构

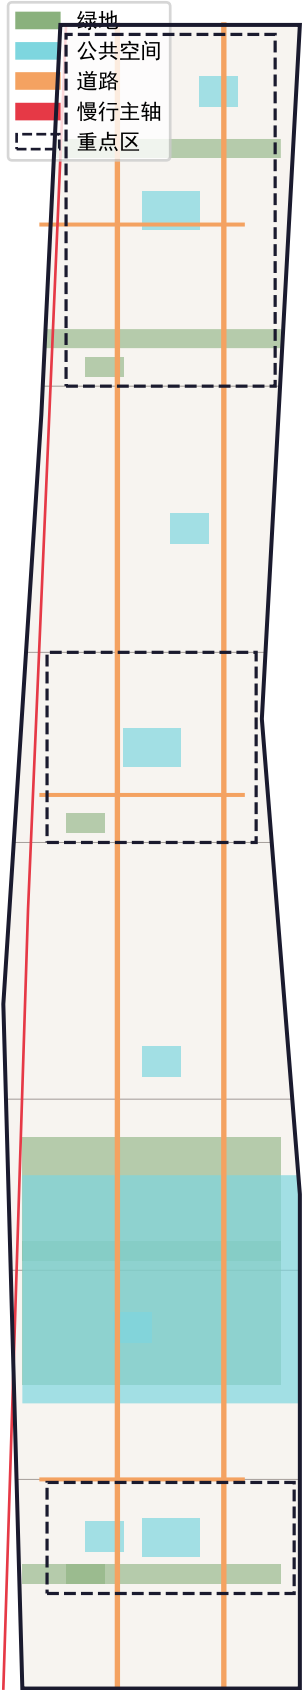


京张AI共生带 SIGMA LINK · 用地结构概念图

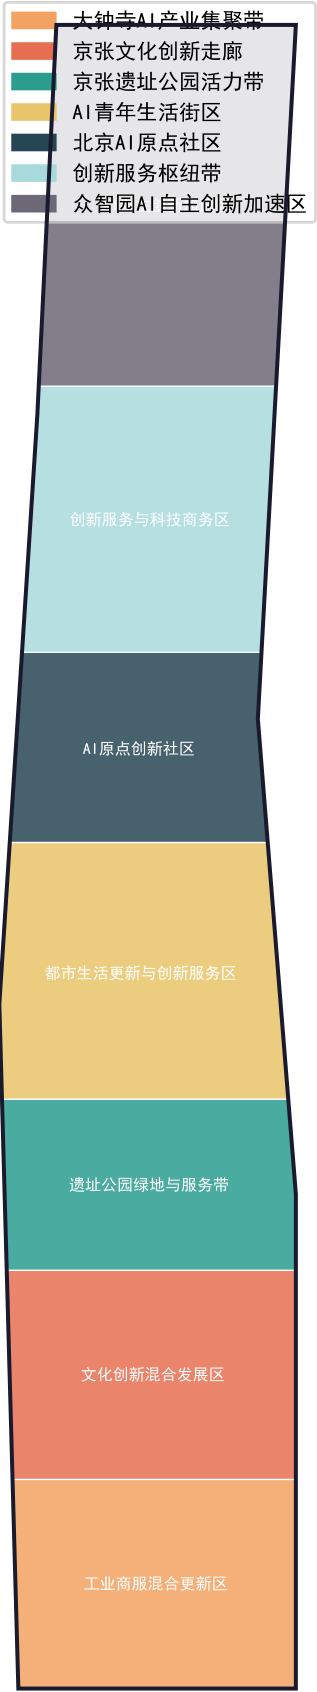


京张AI共生带 SIGMA LINK · 三处重点区域




京张AI共生带 SIGMA LINK · 交通慢行与蓝绿公共空间

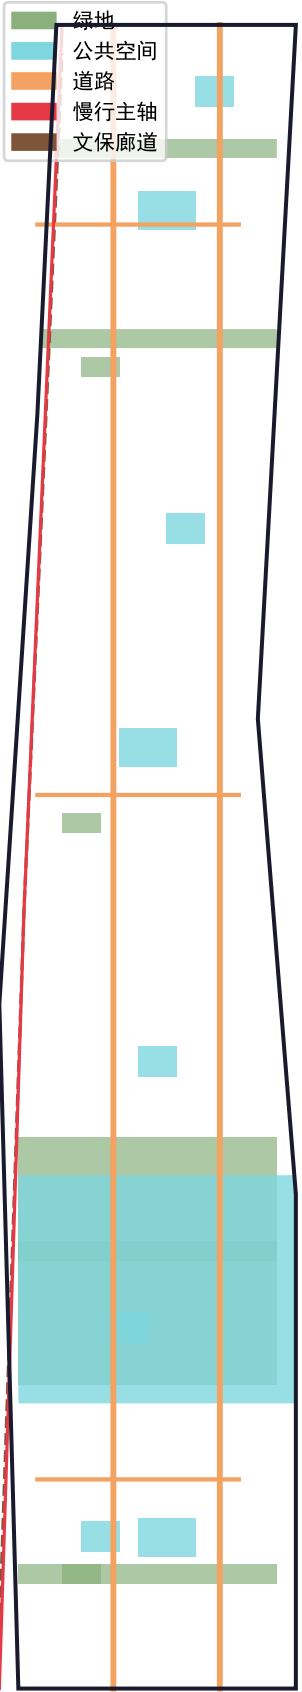

京张AI共生带 SIGMA LINK · 建筑与路网骨架

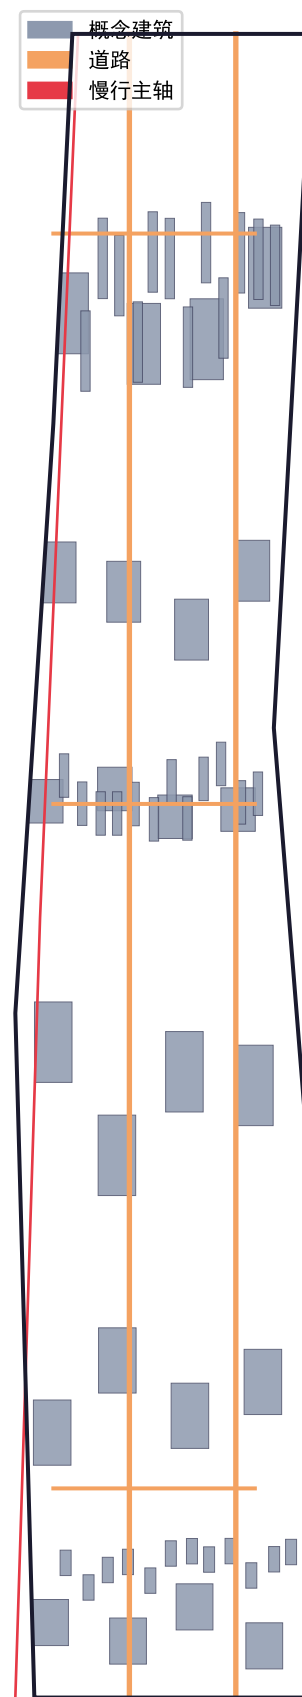

京张AI共生带 SIGMA LINK · 分期实施计划

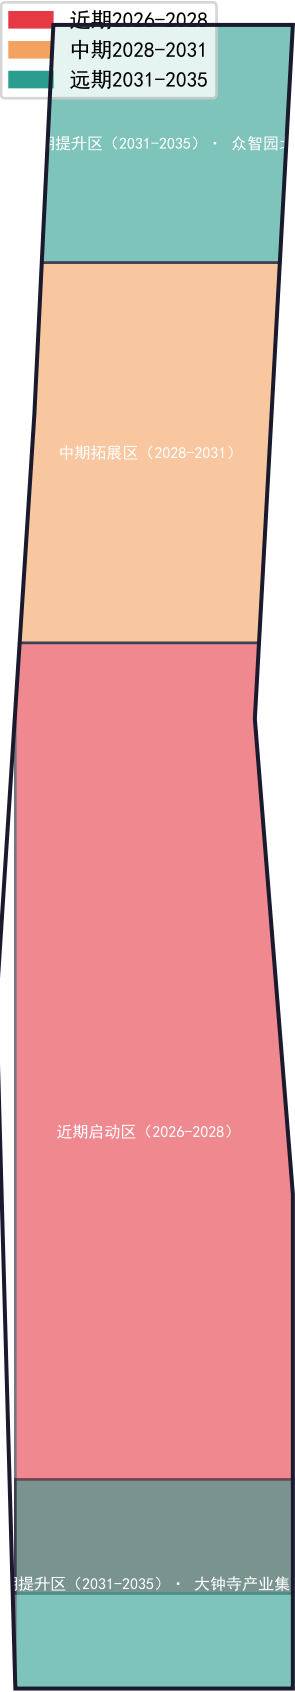

京张AI共生带 SIGMA LINK · 核心指标复算证据链

设计范围面积：11,412,825 m² （EPSG:4548投影）

绿地率：19.5% （2,223,005 m²）

公共空间率：17.4% （1,984,378 m²）

建筑密度：16.2% （1,845,160 m²）

路网总长：31.9 km （两纵三横一轴）

重点区：3处 / 368.4 ha

来源：geometry/*.geojson → EPSG:4548 投影复算
状态：provisional 粗略边界，官方 polygon 发布后需复算全部指标