


人字轨 · 智汇京张 — 以“人”为支点的百年京张AI创新带城市设计

1909年，京张铁路在青龙桥用“人”字形线路把一条爬不上去的陡坡变成两段爬得上去的折线。本方案把同样的智慧变成城市制度：一条遗址公园慢行主脊、一个原点支点、三段差异化爬坡（人—从—众）、两翼协同、十二处人字扣缝合口；每一段智能的爬坡，都经过一个可换向、可复核、可回退的“人”字支点。

图1 · 总体概念：人字轨 —— 以“人”为支点的智能带

一脊 · 一点 · 三段 · 两翼 · 十二扣

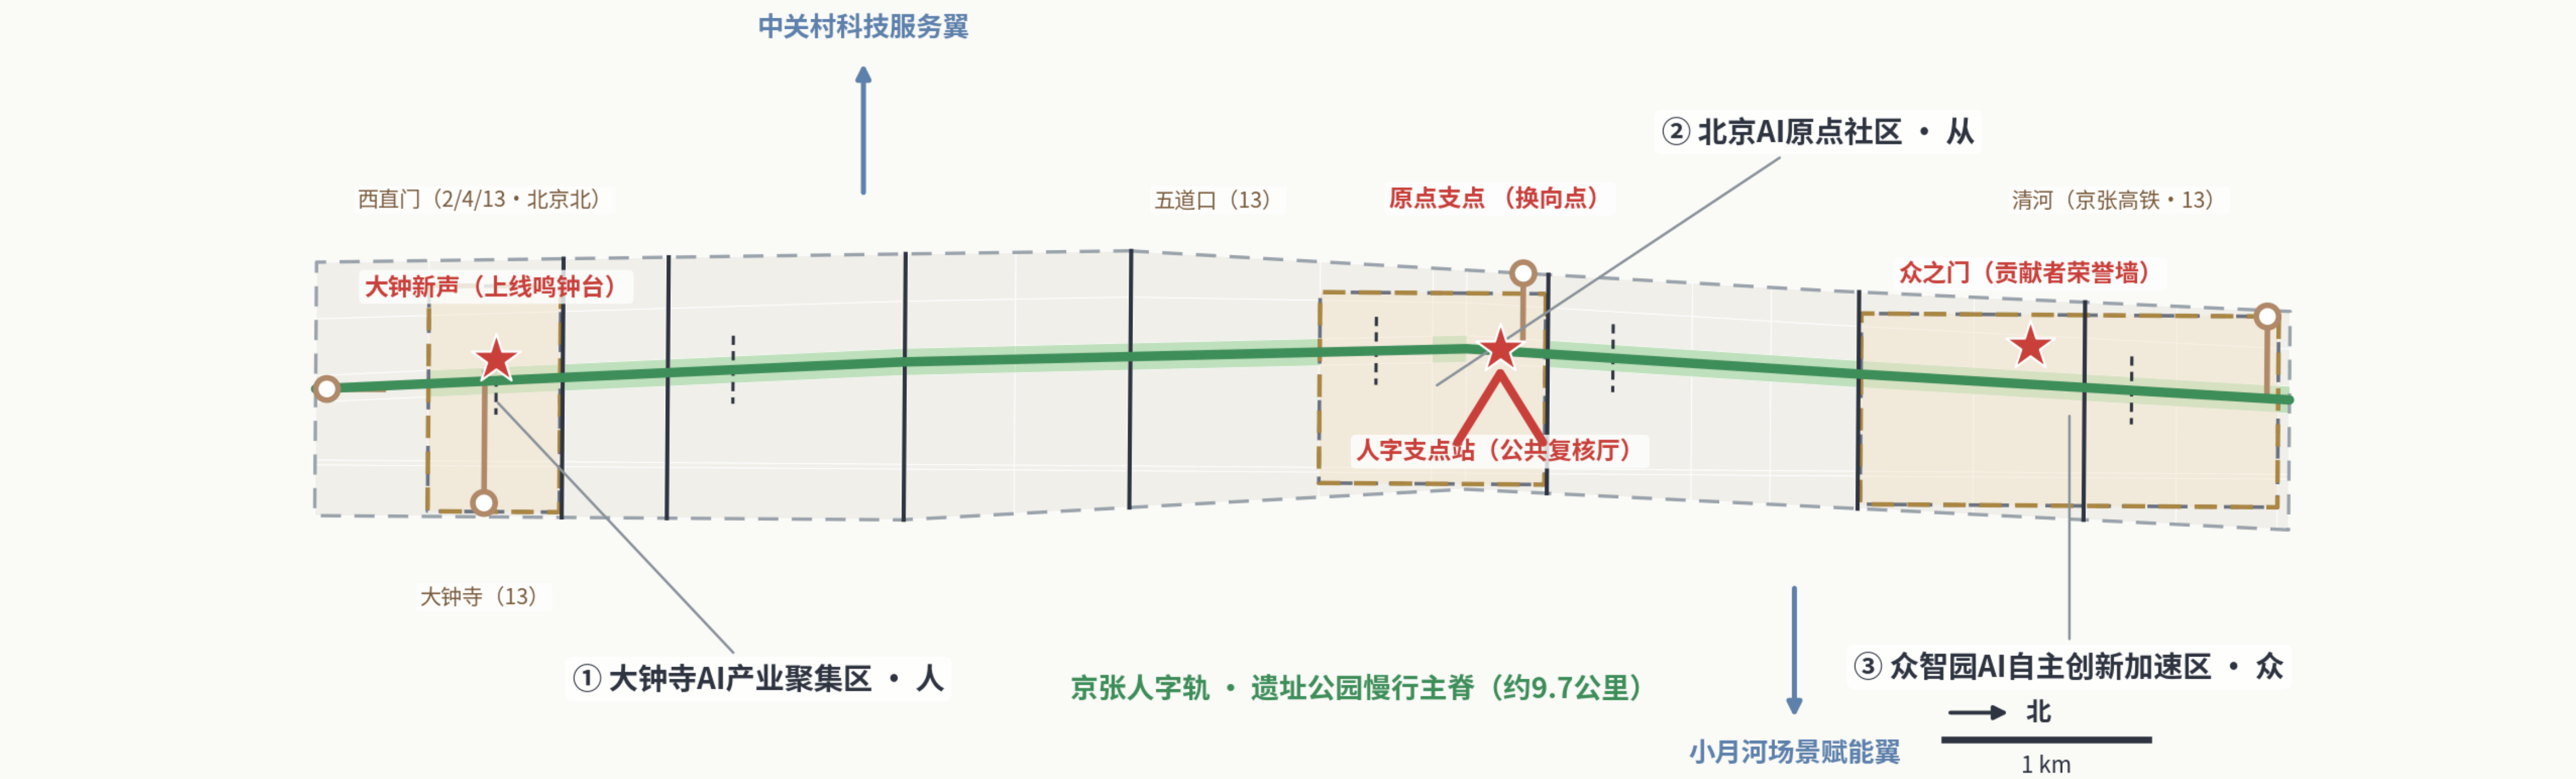

1909年，京张铁路用青龙桥“人”字形线路，把一条爬不上去的陡坡变成两段爬得上去的折线——换向的支点，正是工程为人留出的余地。本方案把这一智慧转译为AI创新带的空间与治理原型：每一段智能的爬坡，都经过一个可换向、可复核、可回退的“人”字支点。

命名系统：人→从→众（一人转译·结伴协作·众智加速）

边界状态：临时推定（provisional）·非官方红线·EPSG:4548复算·官方数据发布后整包重算
数据来源：本提交包 geometry/"_geojson 与 metrics.json（公告口径面积另行标注）



GiantGKL · rails-to-intelligence

图2 · 空间结构与用地布局：绿脊贯通的混合创新带

150个拓扑无缝用地单元 · 六带并置 · 官方控规条件待补齐

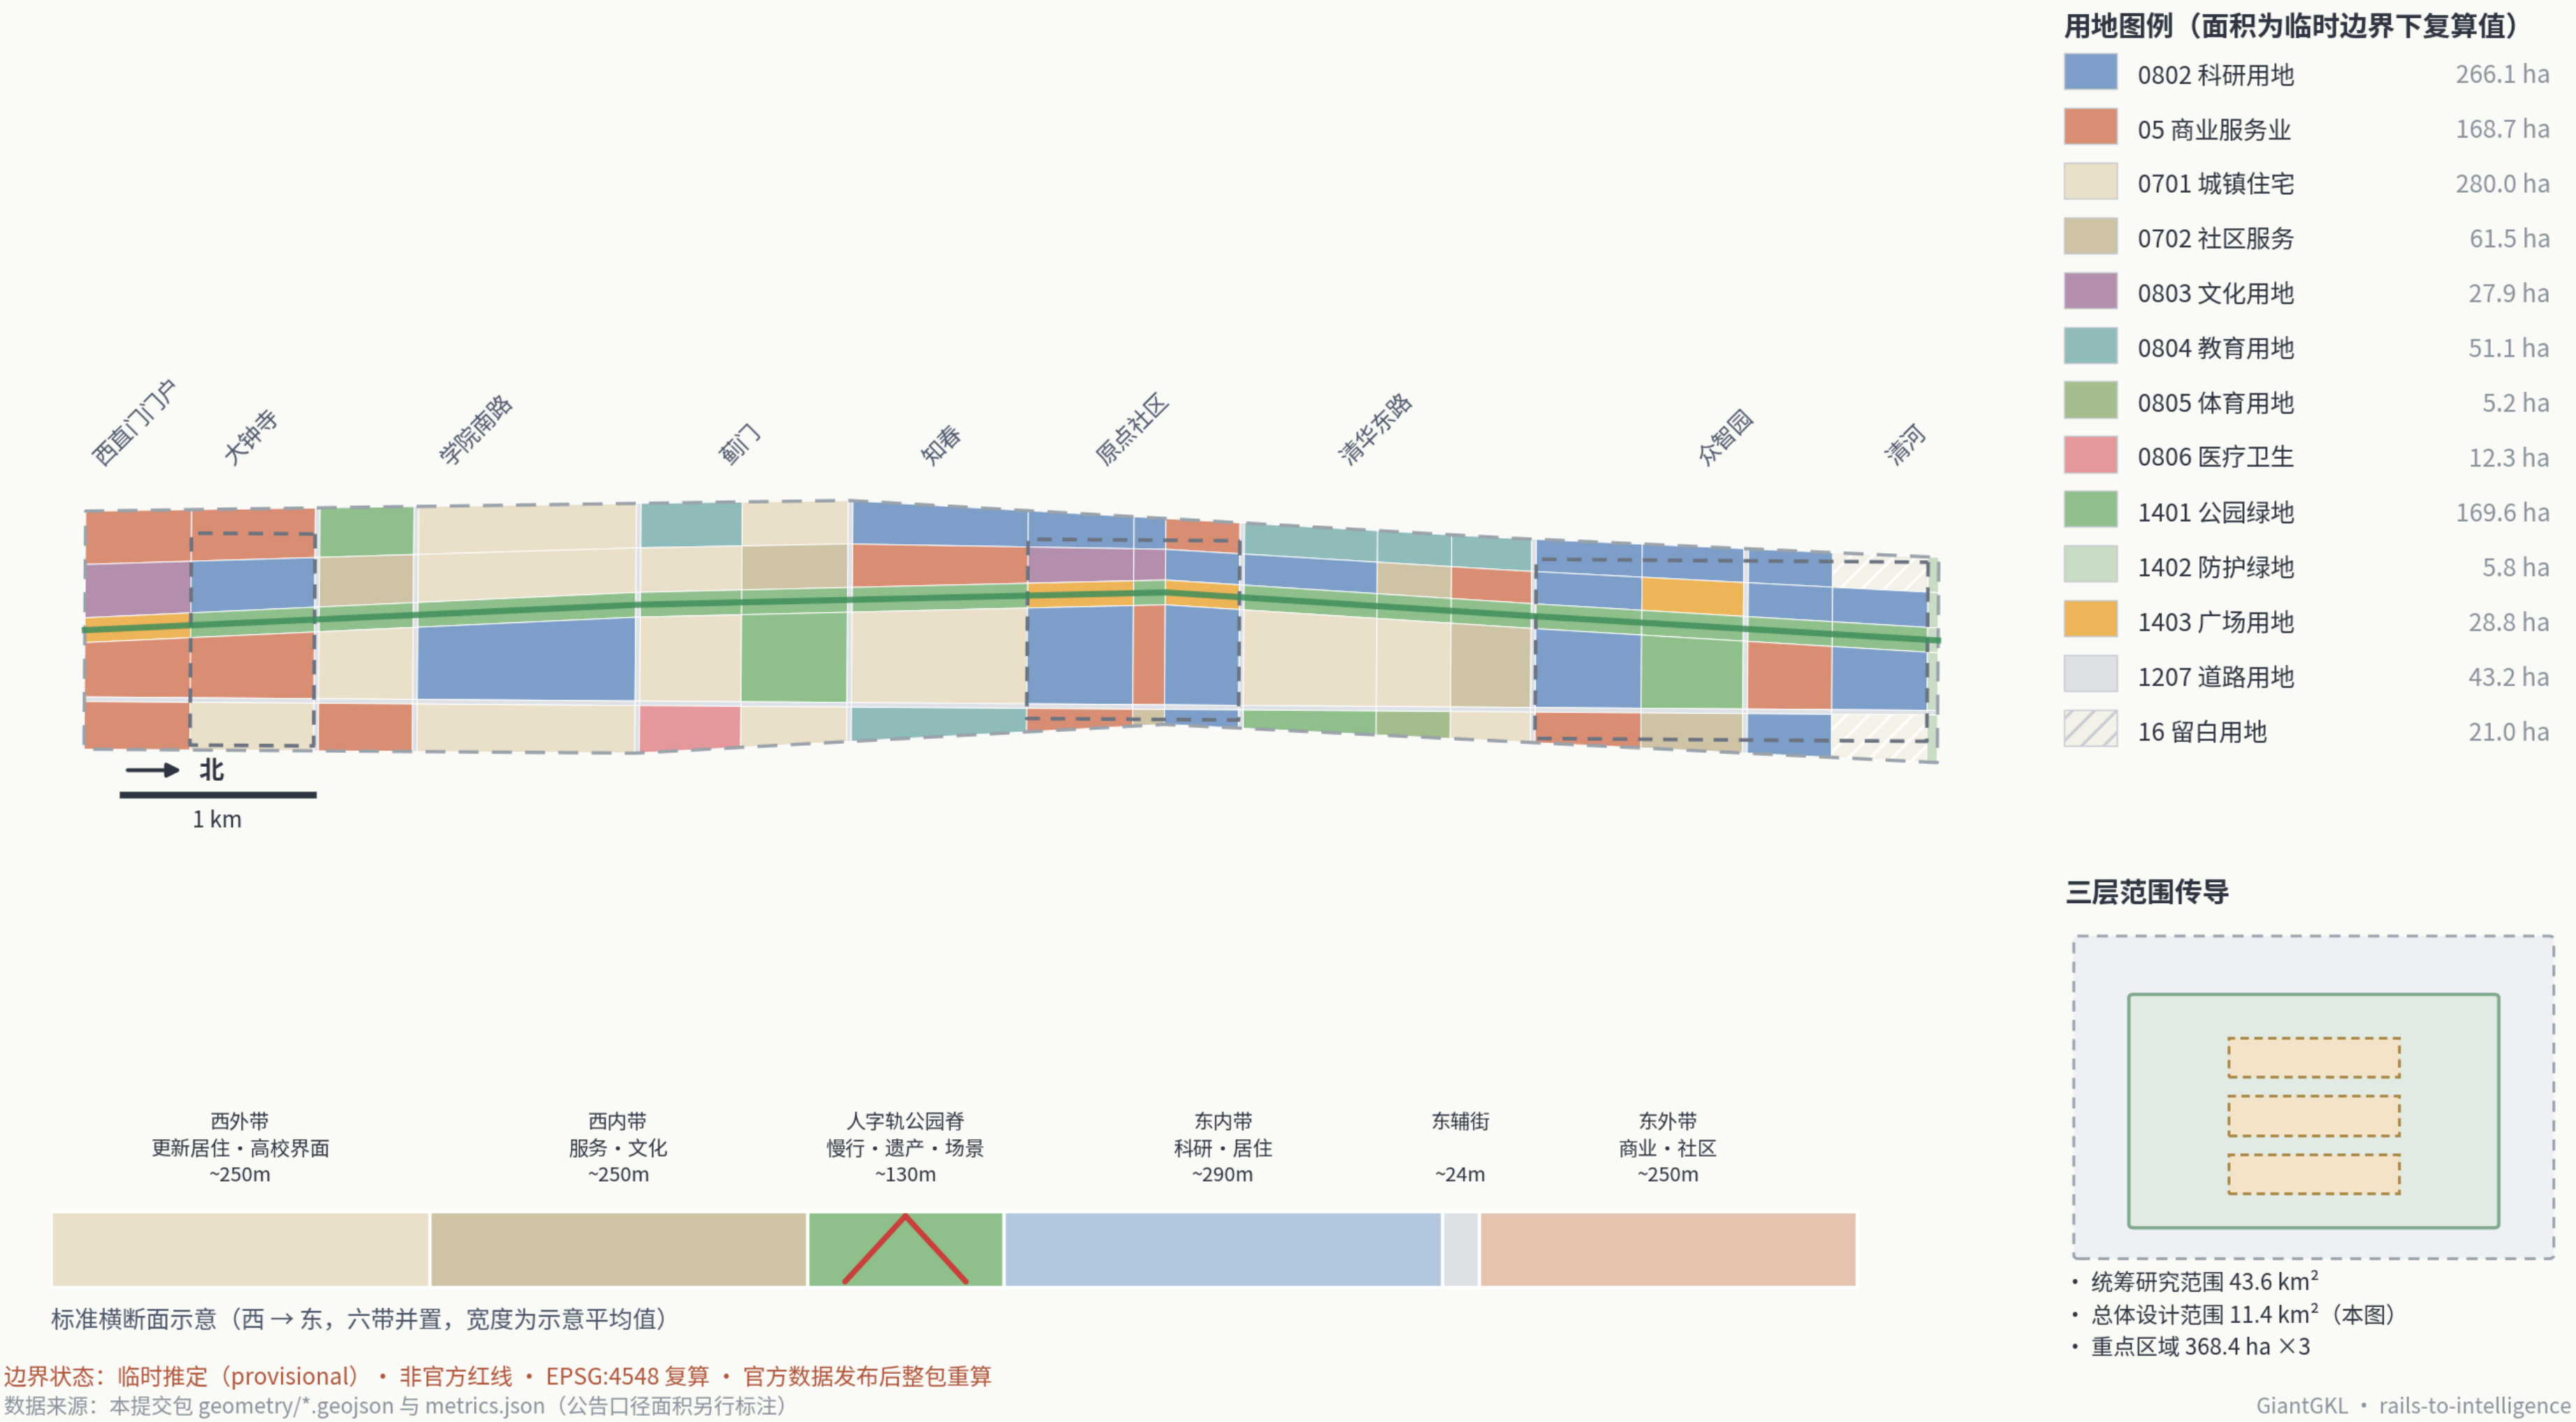


图3 · 三处重点区详细设计索引：人·从·众

同一条脊上的三种爬坡方式（临时矩形范围，官方边界待发布）

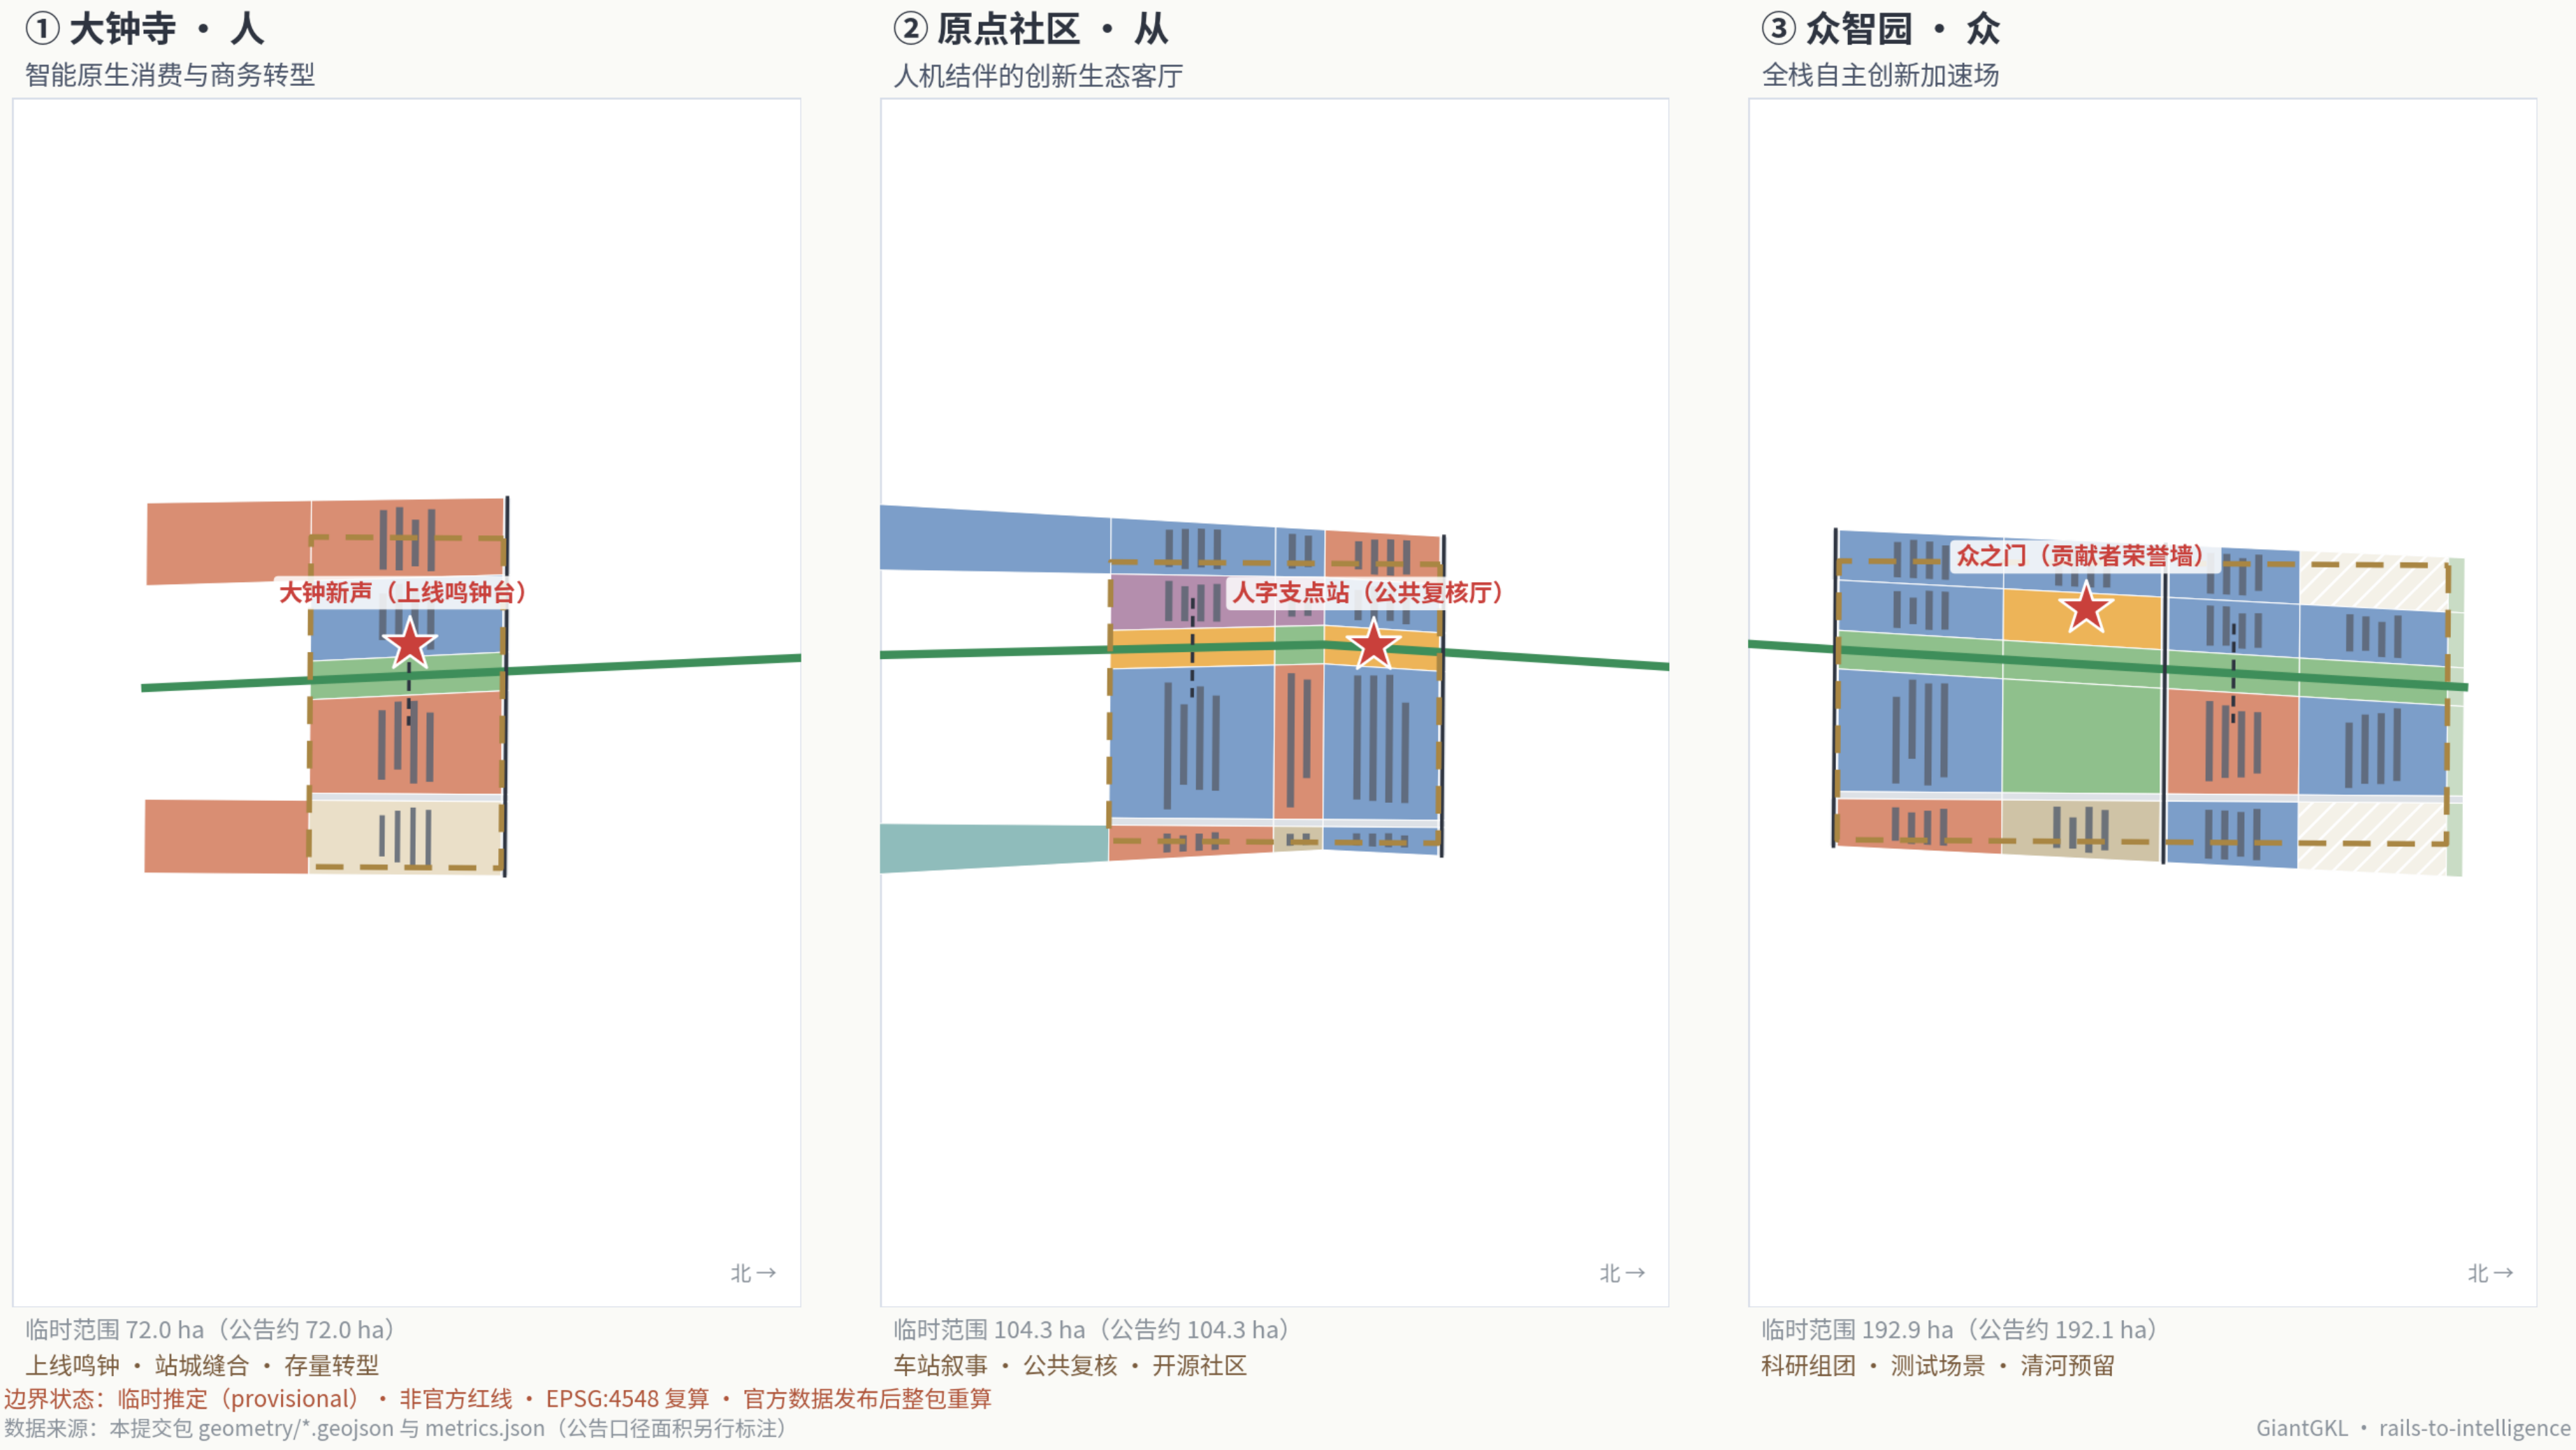


图4 · 交通慢行与蓝绿公共空间：十二扣缝合

百年铁路切开的东西两侧，用十二处人字扣重新缝合

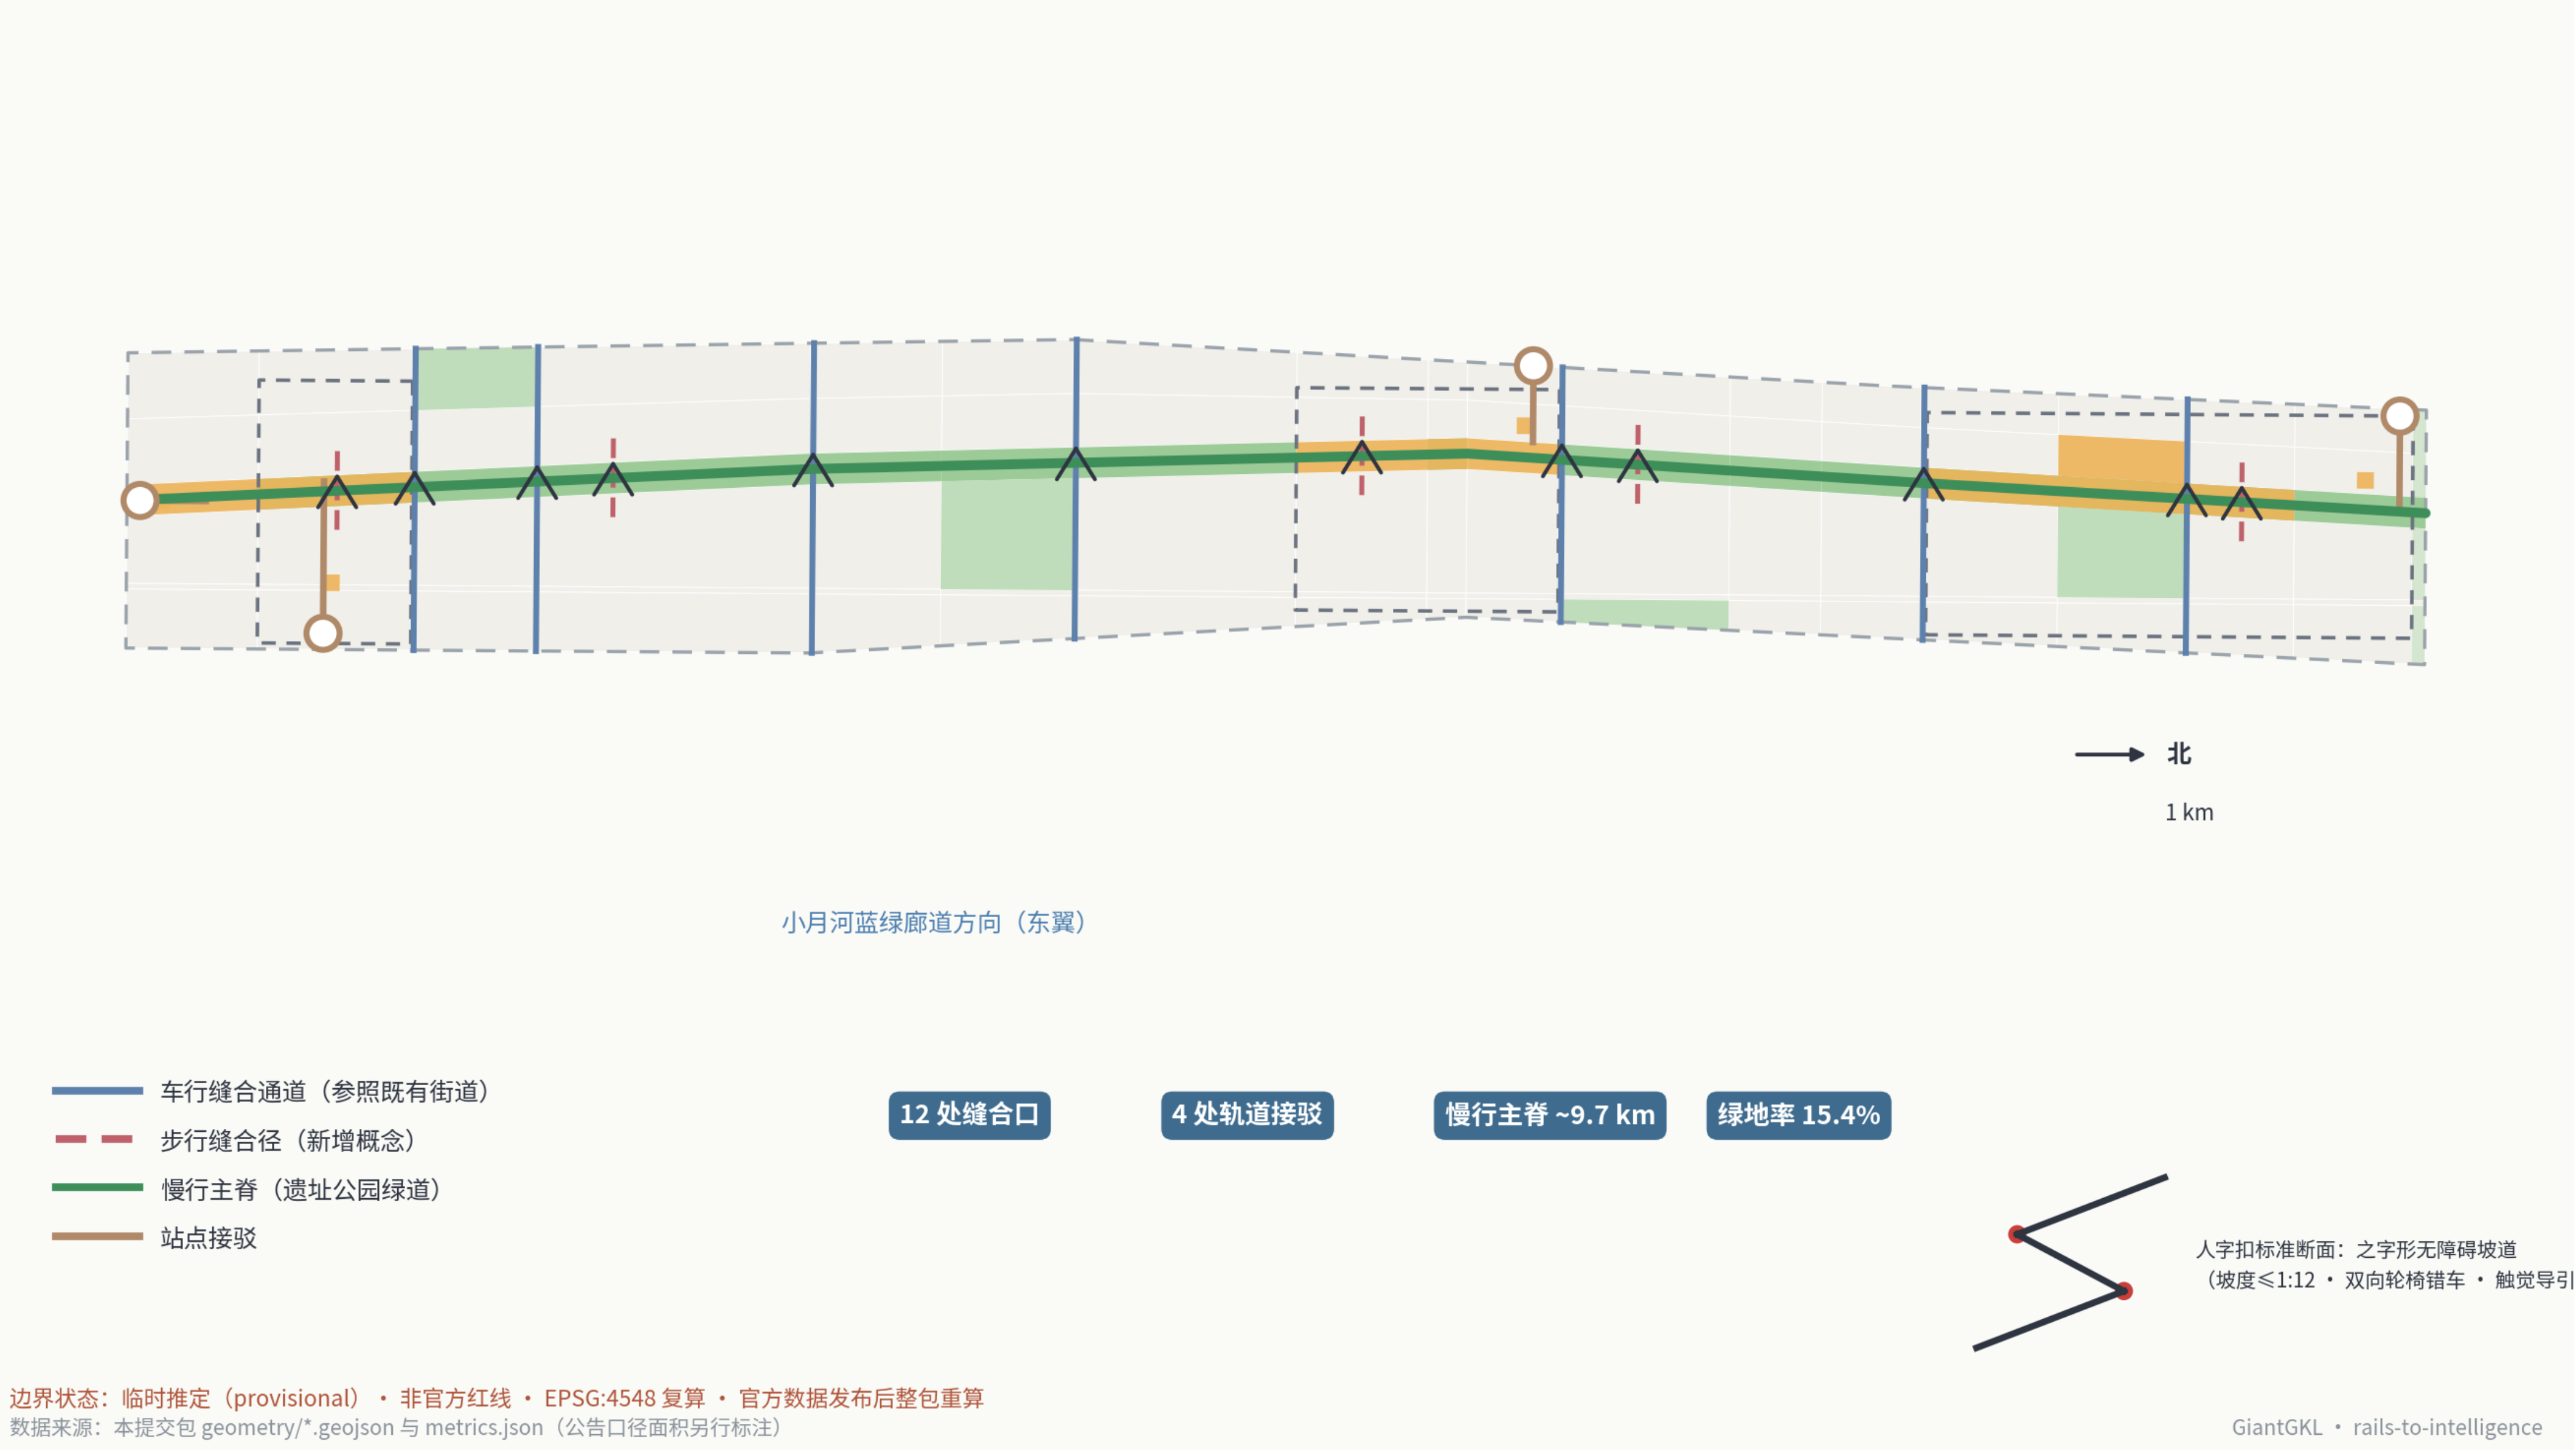



图5 · 指标复算与证据链：每个数字都能重算，缺什么写清楚

GeoJSON → EPSG:4548 → metrics.json → 图纸/HTML → 四道自检门

已复算指标（临时边界口径）

总体范围复算面积	官方口径约 1140 ha
1141.3 ha	
绿地率（概念体系）	公园脊+口袋公园+防护带
15.4%	
公共空间比例	广场+活力段+站前（叠加层）
5.4%	
道路用地比例	缝合通道+东辅街（非红线）
3.8%	
概念建筑体量	低置信设计量 · 非法定规模
646 万m ²	
容积率（法定）	无批准控规条件，不编造
待补齐	
建筑高度（法定）	航空/景观/文保约束未公开
待补齐	

证据链

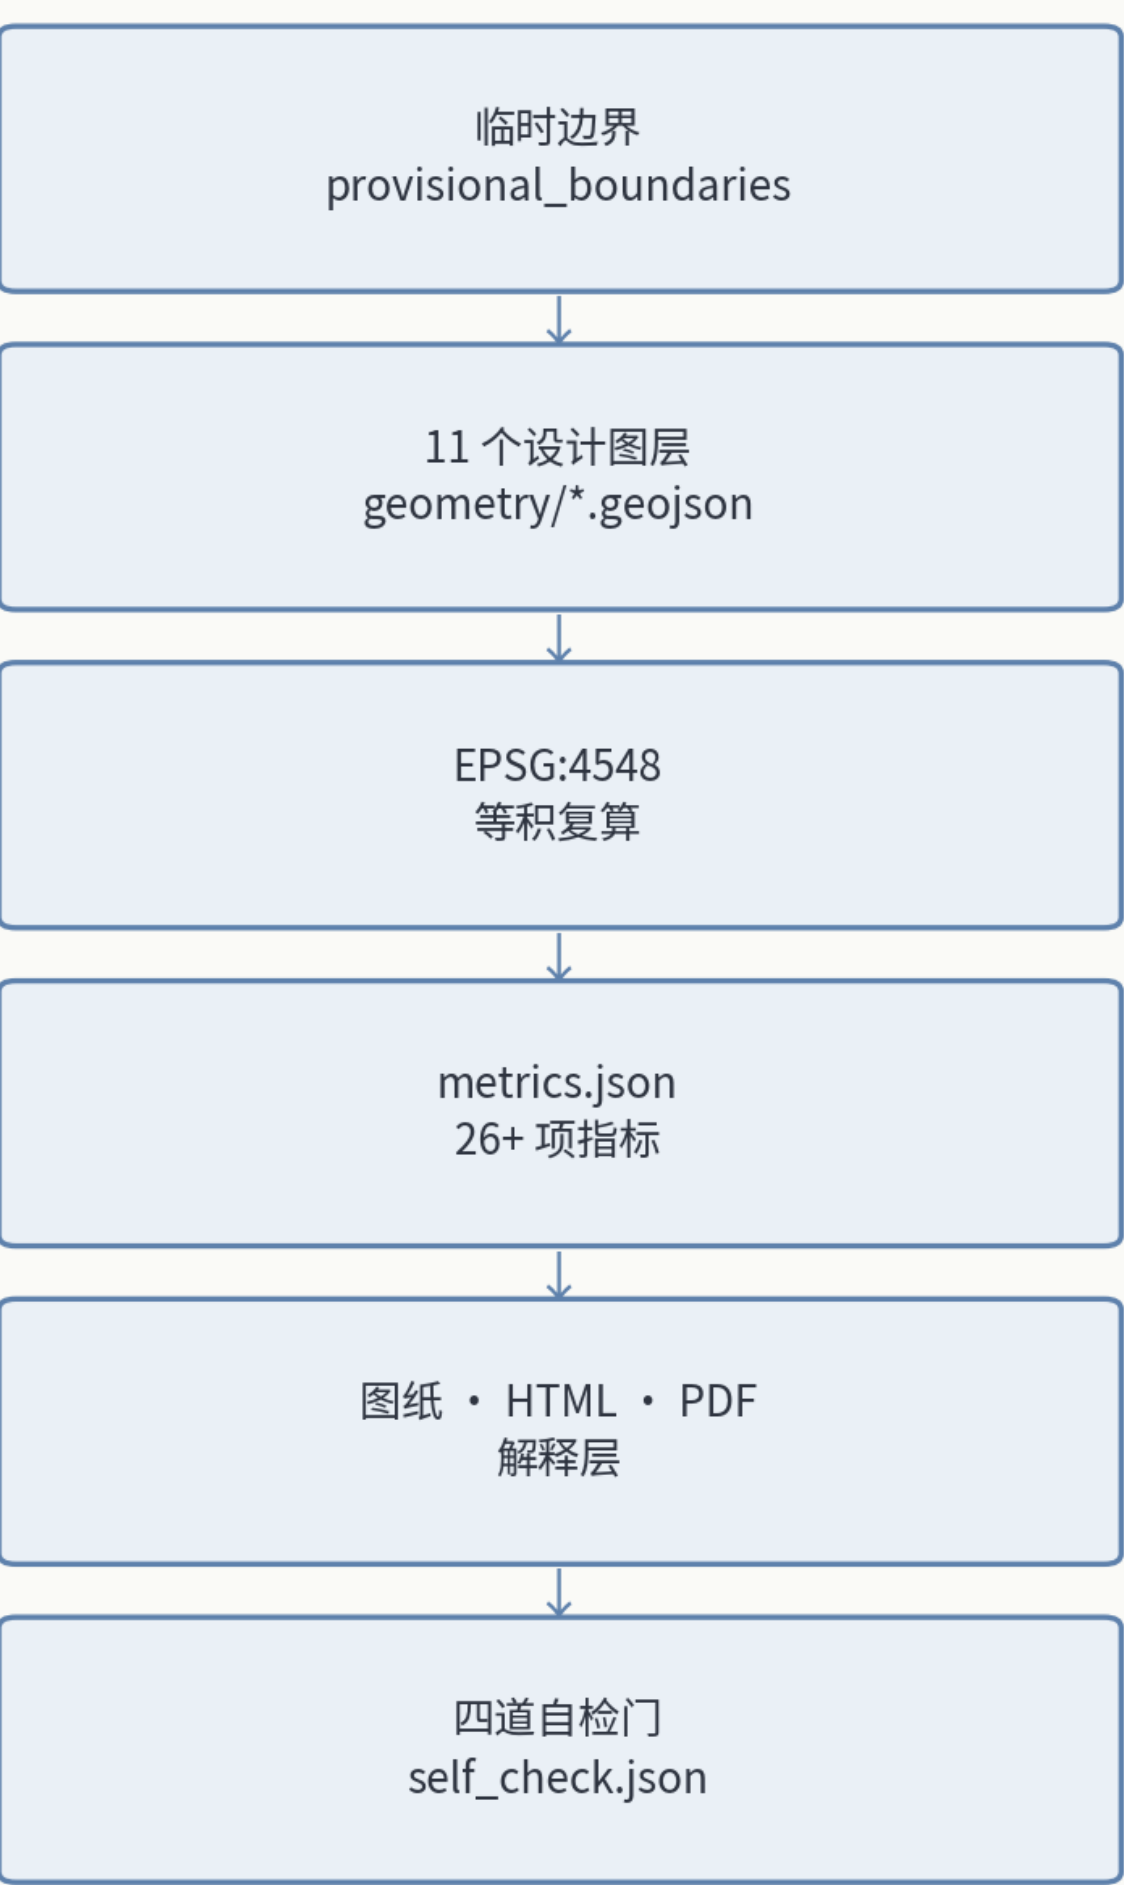

待正式数据补齐

- ☐ 官方三层范围与重点区 polygon
- ☐ 控规条件（容积率/高度/密度/绿地率/退线）
- ☐ 现状建筑轮廓、产权与拆改留底数
- ☐ 道路红线、轨道站点与市政承载数据
- ☐ 文保范围与建设控制地带 GIS 图层

官方数据发布后：整包重算全部图层与指标，不单独替换任何一个边界文件。

任务覆盖：公告 1.3/1.4/1.5 + agent.1-6 共 23 项 → compliance_matrix.json

23 / 23

边界状态：临时推定（provisional） · 非官方红线 · EPSG:4548 复算 · 官方数据发布后整包重算
数据来源：本提交包 geometry/*.geojson 与 metrics.json（公告口径面积另行标注）

GiantGKL · rails-to-intelligence

三处AI朝圣地标（自南向北）

- 大钟新声（上线鸣钟台）——每一项公共AI服务的上线与退出，鸣钟公示，市民听得见。
- 人字支点站（公共复核厅）——一带AI场景的用途、数据边界、复核记录与退出机制，市民查得到。
- 众之门（贡献者荣誉墙）——被社区采纳的贡献实时铭刻，包括本次开源征集的所有参与者。

坡度分级治理（G1/G2/G3）

- G1 可即时人工接管：导览、服务台、健康驿站等 8 类日常场景。
- G2 定期复核+一键降级：按需照明、长者陪伴等 2 类场景。
- G3 封闭测试段运行：低速微巴、机器人配送、共享试验场 3 类产业测试验证场景。
- 每张场景卡带“人字预案”：何时降级为人工、如何退出、谁来复核。

三期实施（概念建议）

- 近期 2026-2028 贯通与启动：公园脊贯通、十二处人字扣、支点广场与公共复核厅（约383.7公顷）。
- 中期 2029-2031 加速与转型：众智园科研组团、大钟寺消费转型、两处测试段（约293.6公顷）。
- 远期 2032-2035 成网与协同：居住服务带更新、两翼接口成熟、留白启用（约464.0公顷）。