

人字轨 · 智汇京张

以“人”为支点的百年京张AI创新带城市设计

1909年，京张铁路在青龙桥用“人”字形线路把一条爬不上去的陡坡变成两段爬得上去的折线。本方案把同样的智慧变成城市制度：一条遗址公园慢行主脊、一个原点支点、三段差异化爬坡（人一从一众）、两翼协同、十二处人字扣缝合口；每一段智能的爬坡，都经过一个可换向、可复核、可回退的“人”字支点。


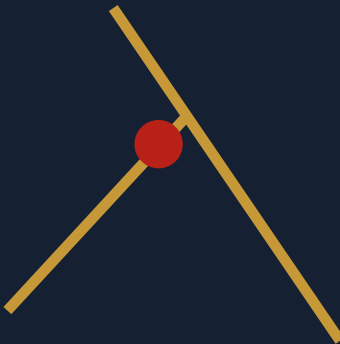


图1 · 总体概念：人字轨 —— 以“人”为支点的智能带

一脊 · 一点 · 三段 · 两翼 · 十二扣

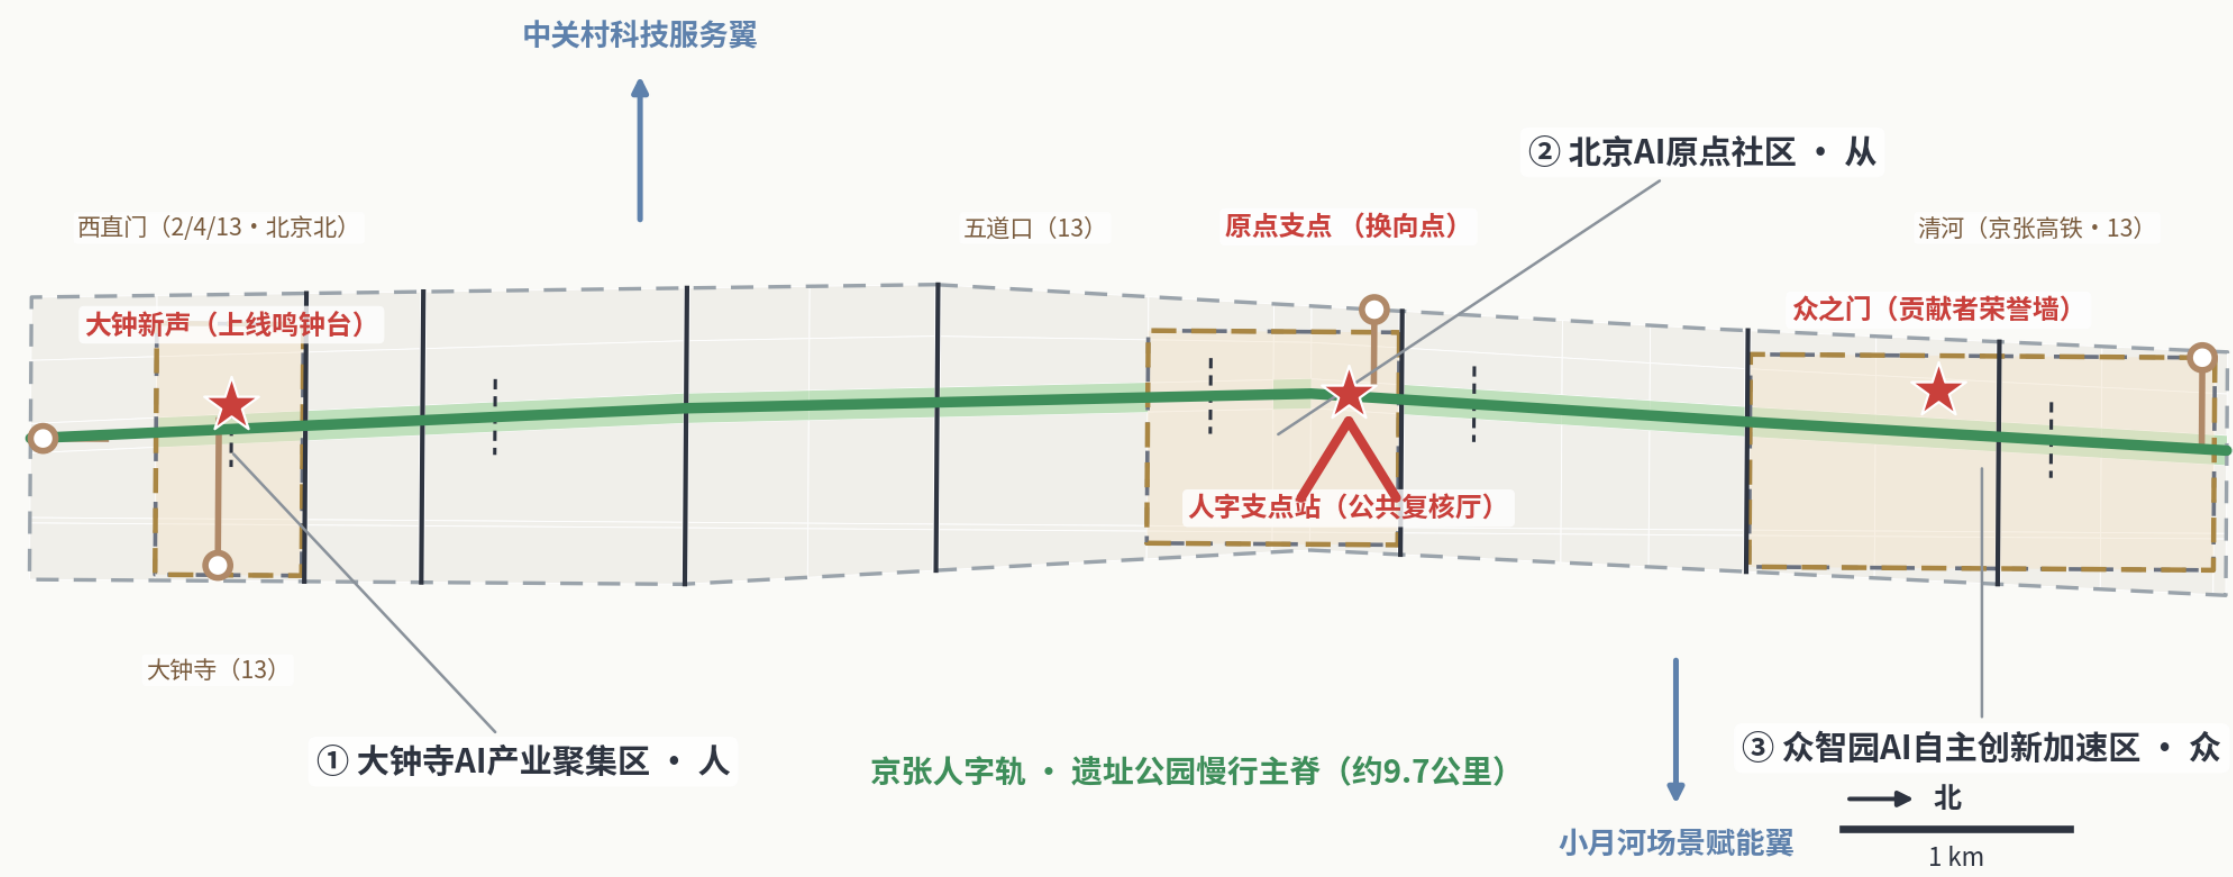

1909年，京张铁路用青龙桥“人”字形线路，把一条爬不上去的陡坡变成两段爬得上去的折线——换向的支点，正是工程为人留出的余地。本方案把这一智慧转译为AI创新带的空间与治理原型：每一段智能的爬坡，都经过一个可换向、可复核、可回退的“人”字支点。


命名系统：人 → 从 → 众 (一人转译 · 结伴协作 · 众智加速)

边界状态：临时推定 (provisional) · 非官方红线 · EPSG:4548 复算 · 官方数据发布后整包重算
数据来源：本提交包 geometry/*.geojson 与 metrics.json (公告口径面积另行标注)




图2 · 空间结构与用地布局：绿脊贯通的混合创新带

150 个拓扑无缝用地单元 · 六带并置 · 官方控规条件待补齐

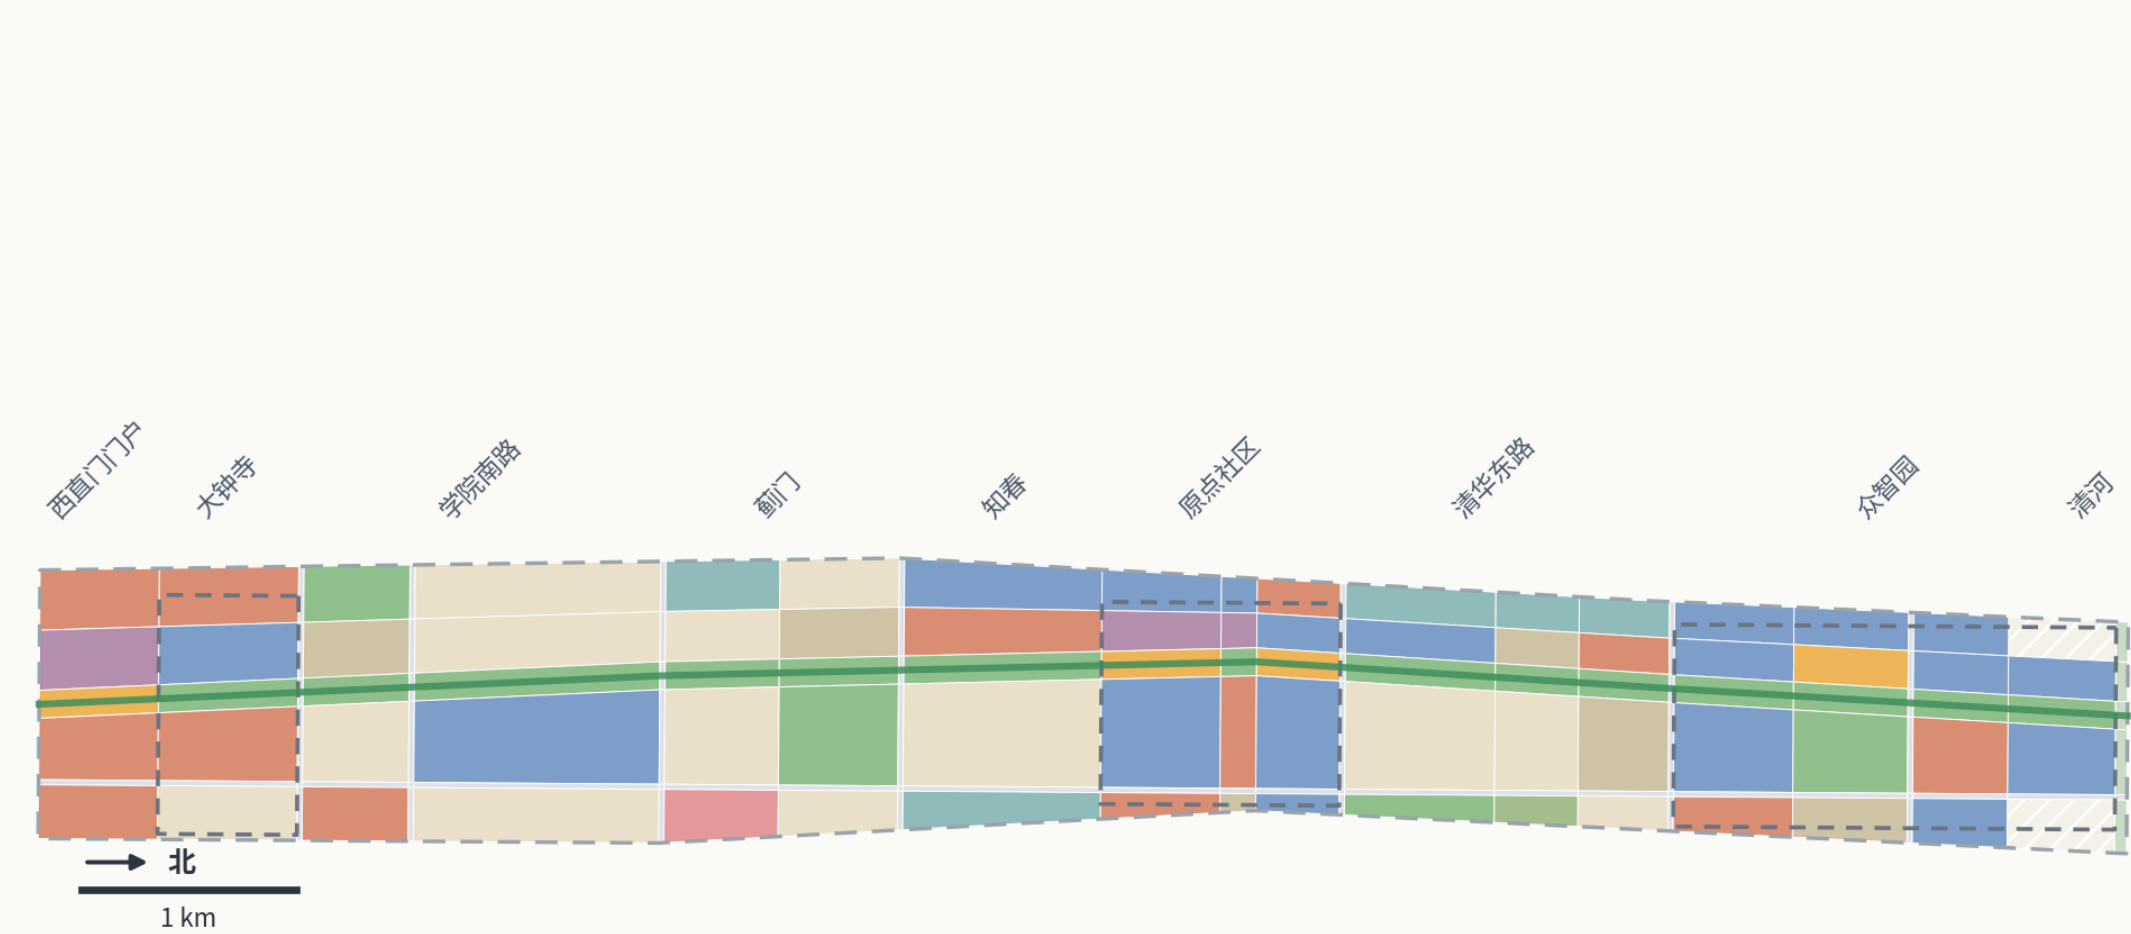

用地图例（面积为临时边界下复算值）


0802 科研用地	266.1 ha
05 商业服务业	168.7 ha
0701 城镇住宅	280.0 ha
0702 社区服务	61.5 ha
0803 文化用地	27.9 ha
0804 教育用地	51.1 ha
0805 体育用地	5.2 ha
0806 医疗卫生	12.3 ha
1401 公园绿地	169.6 ha
1402 防护绿地	5.8 ha
1403 广场用地	28.8 ha
1207 道路用地	43.2 ha
16 留白用地	21.0 ha

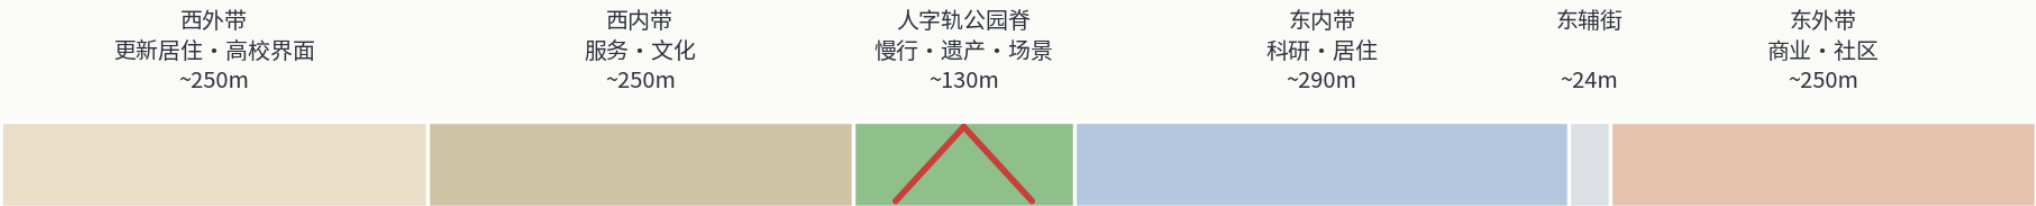

标准横断面示意（西 → 东，六带并置，宽度为示意平均值）

边界状态：临时推定（provisional） · 非官方红线 · EPSG:4548 复算 · 官方数据发布后整包重算
数据来源：本提交包 geometry/*.geojson 与 metrics.json （公告口径面积另行标注）

三层范围传导

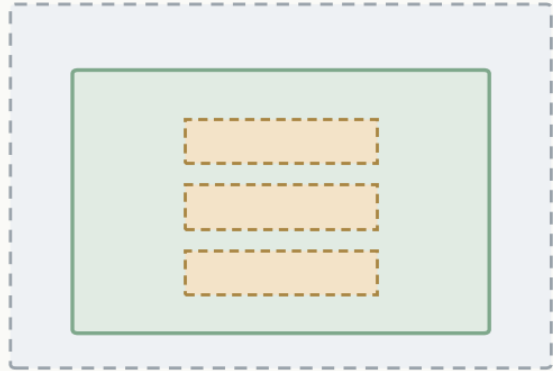


- 统筹研究范围 43.6 km²
- 总体设计范围 11.4 km²（本图）
- 重点区域 368.4 ha ×3

图3 · 三处重点区详细设计索引：人 · 从 · 众

同一条脊上的三种爬坡方式（临时矩形范围，官方边界待发布）

① 大钟寺 · 人

智能原生消费与商务转型

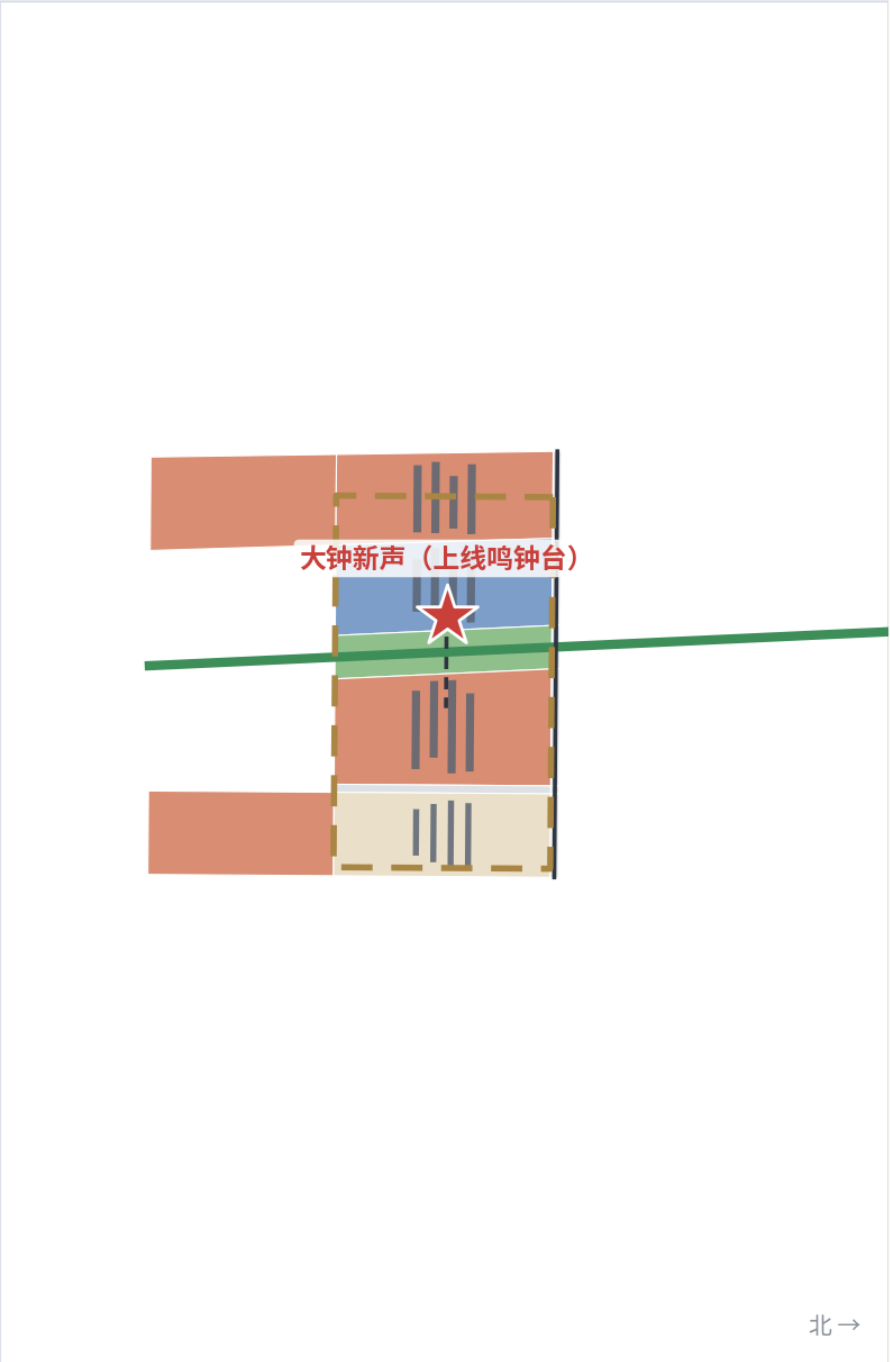

临时范围 72.0 ha（公告约 72.0 ha）


上线鸣钟 · 站城缝合 · 存量转型

边界状态：临时推定（provisional） · 非官方红线 · EPSG:4548 复算 · 官方数据发布后整包重算

数据来源：本提交包 geometry/*.geojson 与 metrics.json（公告口径面积另行标注）

② 原点社区 · 从

人机结伴的创新生态客厅

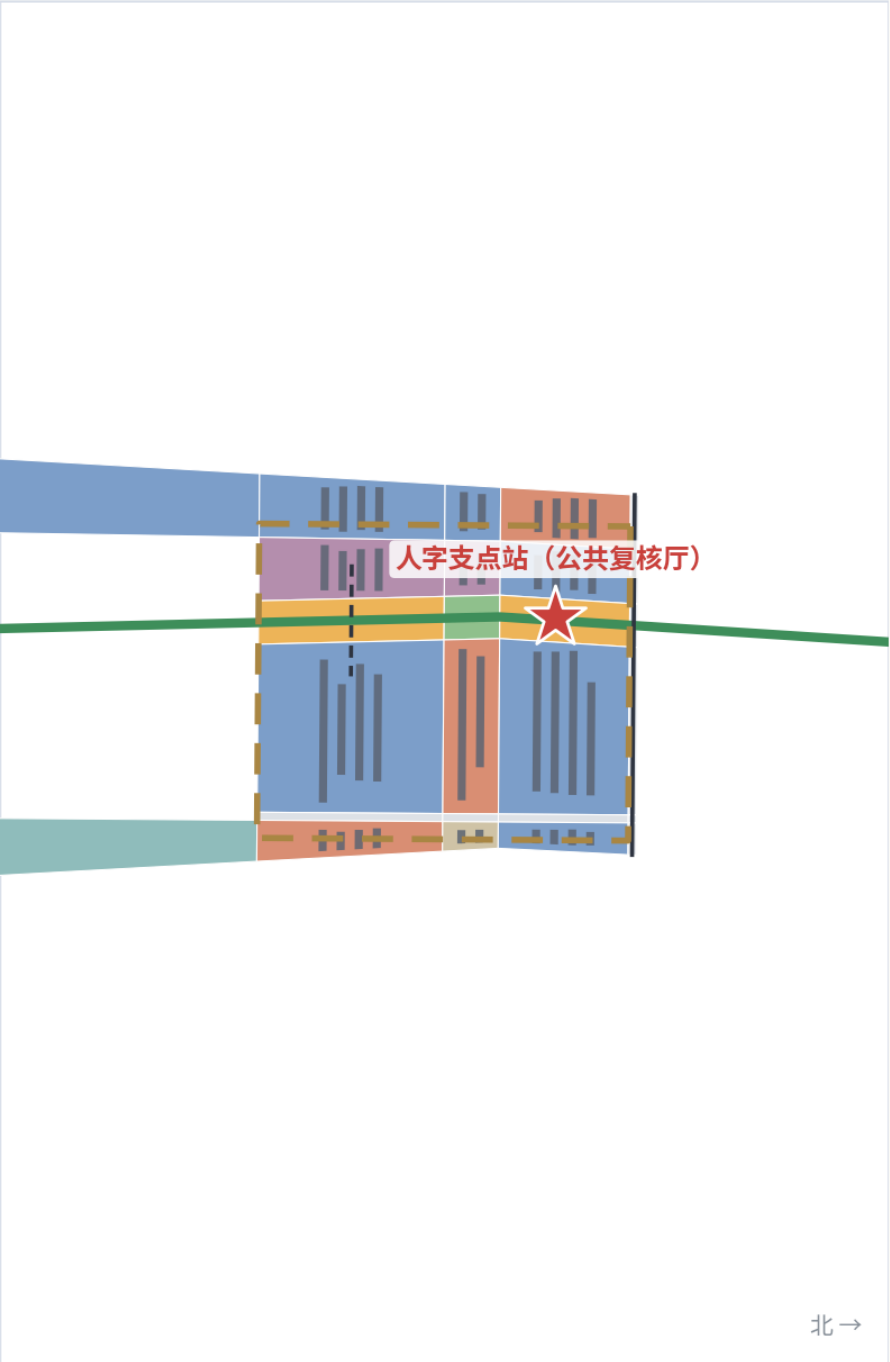


临时范围 104.3 ha（公告约 104.3 ha）

车站叙事 · 公共复核 · 开源社区

③ 众智园 · 众

全栈自主创新加速场

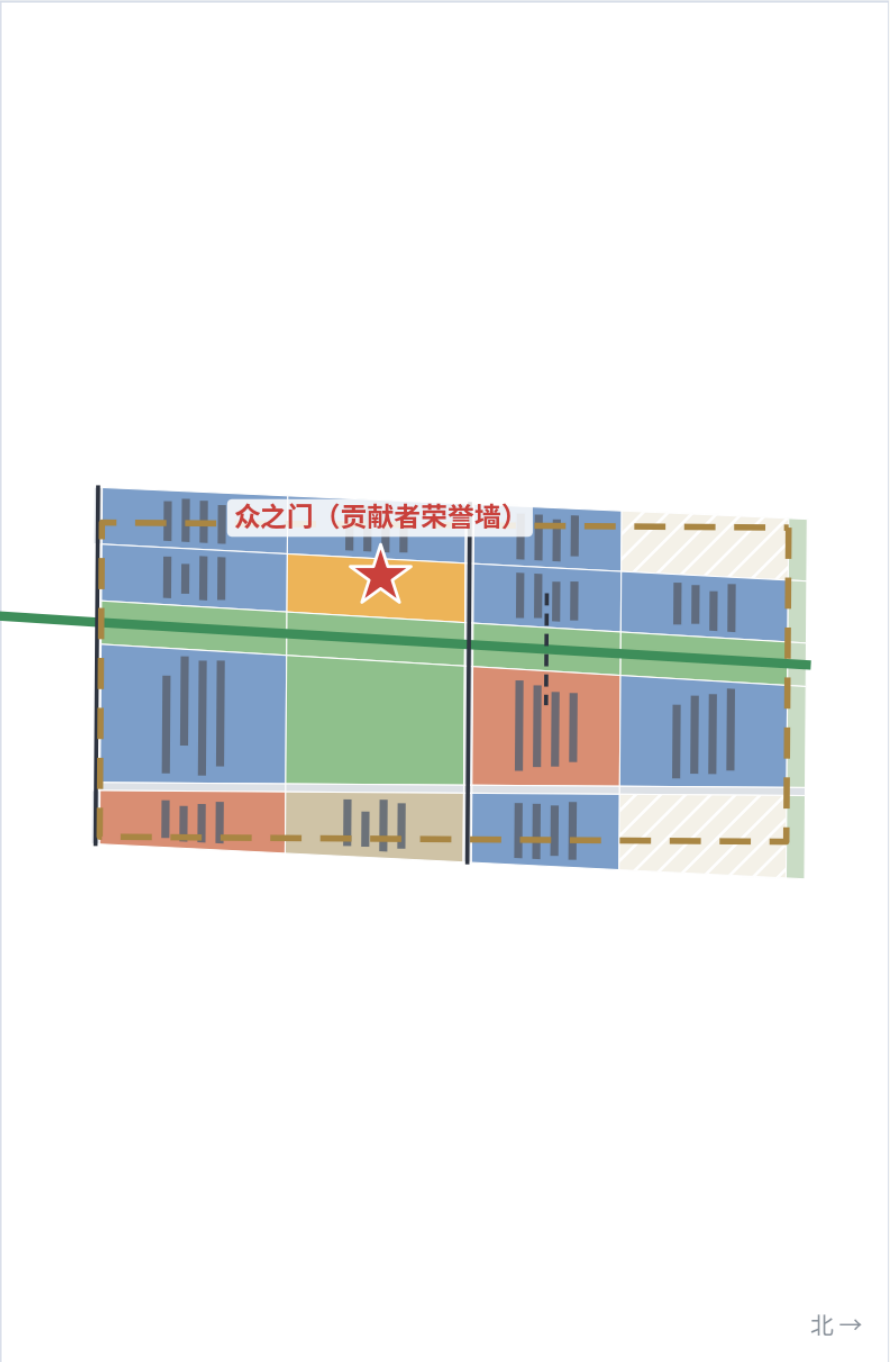


临时范围 192.9 ha（公告约 192.1 ha）

科研组团 · 测试场景 · 清河预留

图4 · 交通慢行与蓝绿公共空间：十二扣缝合

百年铁路切开的东西两侧，用十二处人字扣重新缝合

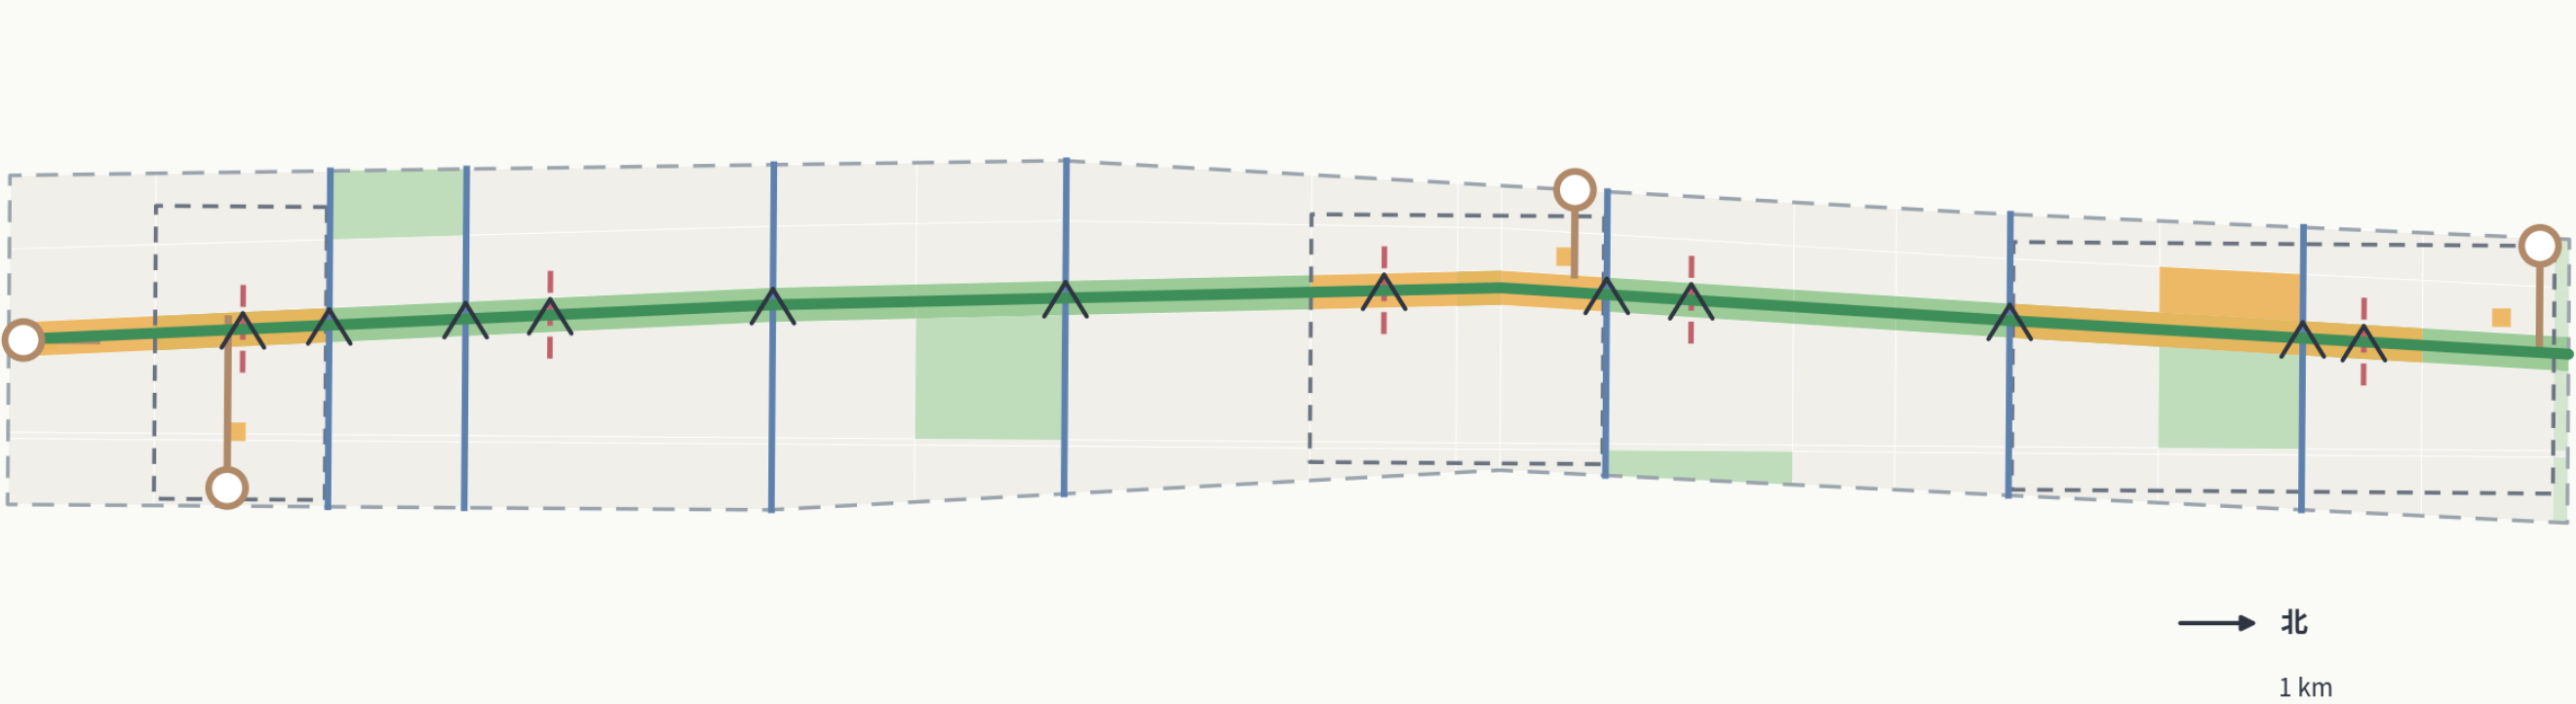

小月河蓝绿廊道方向（东翼）


- 车行缝合通道（参照既有街道）
- 步行缝合径（新增概念）
- 慢行主脊（遗址公园绿道）
- 站点接驳

12 处缝合口

4 处轨道接驳

慢行主脊 ~9.7 km

绿地率 15.4%

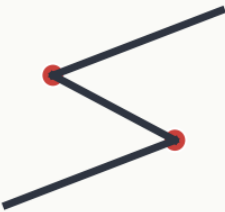

人字扣标准断面：之字形无障碍坡道
（坡度≤1:12 · 双向轮椅错车 · 触觉导引

边界状态：临时推定（provisional） · 非官方红线 · EPSG:4548 复算 · 官方数据发布后整包重算
数据来源：本提交包 geometry/*.geojson 与 metrics.json （公告口径面积另行标注）

GiantGKL · rails-to-intelligence


图5 • 指标复算与证据链：每个数字都能重算，缺什么写清楚

GeoJSON → EPSG:4548 → metrics.json → 图纸/HTML → 四道自检门

已复算指标（临时边界口径）

总体范围复算面积	官方口径约 1140 ha
1141.3 ha	
绿地率（概念体系）	公园脊+口袋公园+防护带
15.4%	
公共空间比例	广场+活力段+站前（叠加层）
5.4%	
道路用地比例	缝合通道+东辅街（非红线）
3.8%	
概念建筑体量	低置信设计量 • 非法定规模
646 万m²	
容积率（法定）	无批准控规条件，不编造
待补齐	
建筑高度（法定）	航空/景观/文保约束未公开
待补齐	

证据链

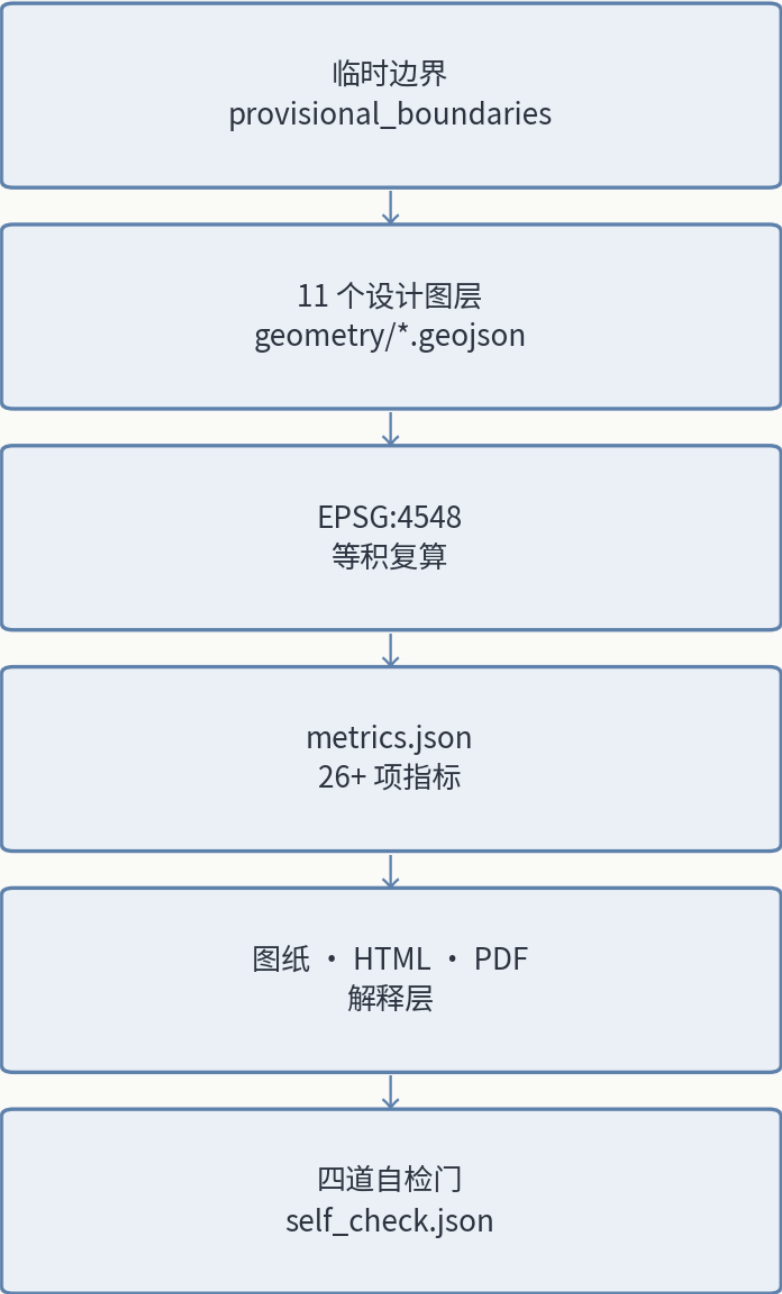

待正式数据补齐

- ☐ 官方三层范围与重点区 polygon
- ☐ 控规条件（容积率/高度/密度/绿地率/退线）
- ☐ 现状建筑轮廓、产权与拆改留底数
- ☐ 道路红线、轨道站点与市政承载数据
- ☐ 文保范围与建设控制地带 GIS 图层

官方数据发布后：整包重算全部图层与指标，不单独替换任何一个边界文件。

任务覆盖：公告 1.3/1.4/1.5 + agent.1-6 共 23 项 → compliance_matrix.json

23 / 23

边界状态：临时推定（provisional）• 非官方红线 • EPSG:4548 复算 • 官方数据发布后整包重算
数据来源：本提交包 geometry/*.geojson 与 metrics.json（公告口径面积另行标注）

核心复算指标

以“人”为支点的百年京张AI创新带城市设计

三处AI朝圣地标（自南向北）

- 大钟新声（上线鸣钟台）——每一项公共AI服务的上线与退出，鸣钟公示，市民听得见。
- 人字支点站（公共复核厅）——全带AI场景的用途、数据边界、复核记录与退出机制，市民查得到。
- 众之门（贡献者荣誉墙）——被社区采纳的贡献实时铭刻，包括本次开源征集的所有参与者。

坡度分级治理（G1/G2/G3）

- G1 可即时人工接管：导览、服务台、健康驿站等 8 类日常场景。
- G2 定期复核+一键降级：按需照明、长者陪伴等 2 类场景。
- G3 封闭测试段运行：低速微巴、机器人配送、共享试验场 3 类产业测试验证场景。
- 每张场景卡带“人字预案”：何时降级为人工、如何退出、谁来复核。

三期实施（概念建议）

- 近期 2026–2028 贯通与启动：公园脊贯通、十二处人字扣、支点广场与公共复核厅（约383.7公顷）。
- 中期 2029–2031 加速与转型：众智园科研组团、大钟寺消费转型、两处测试段（约293.6公顷）。
- 远期 2032–2035 成网与协同：居住服务带更新、两翼接口成熟、留白启用（约464.0公顷）。

核心复算指标

总体设计范围复算面积	1,141.3 ha	公告口径约1140公顷
三处重点区合计（临时）	369.3 ha	公告口径368.4公顷
绿地率（概念绿地体系）	15.4%	非法定绿地率
公共空间比例	5.3%	全部临脊布局
道路用地比例	3.8%	少修路、多缝合
概念建筑体量	约646万m²	149处示意体量，低置信度
缝合口 / 场景节点 / 地标	12 / 15 / 3	由图层直接清点
法定容积率 / 建筑高度	未知	待批准控规条件后重算

全部指标由本包 GeoJSON 在 EPSG:4548 下复算；法定容积率、建筑高度等待官方控规条件发布后重算。

本成果为面向开源征集的概念建议与参考方案，供专业团队深化研究；全部空间图层基于临时推定边界生成，不是官方红线；不构成法定规划结论、政府审定意见或实施承诺。结构化数据（GeoJSON/JSON）为权威口径，PDF 仅作展示。