


到站成邻 | 真实城市语境中的完整生活带

OSM 公开语境 × 可复算设计图层 | 北到达 · 中交换 · 南归属

01 / CONTEXT + OVERALL DESIGN

到站成邻 | 真实城市语境中的一条完整生活带

OSM 公开语境只用于看见道路、轨道、水系、建筑和站点；设计动作仍由可复算图层表达

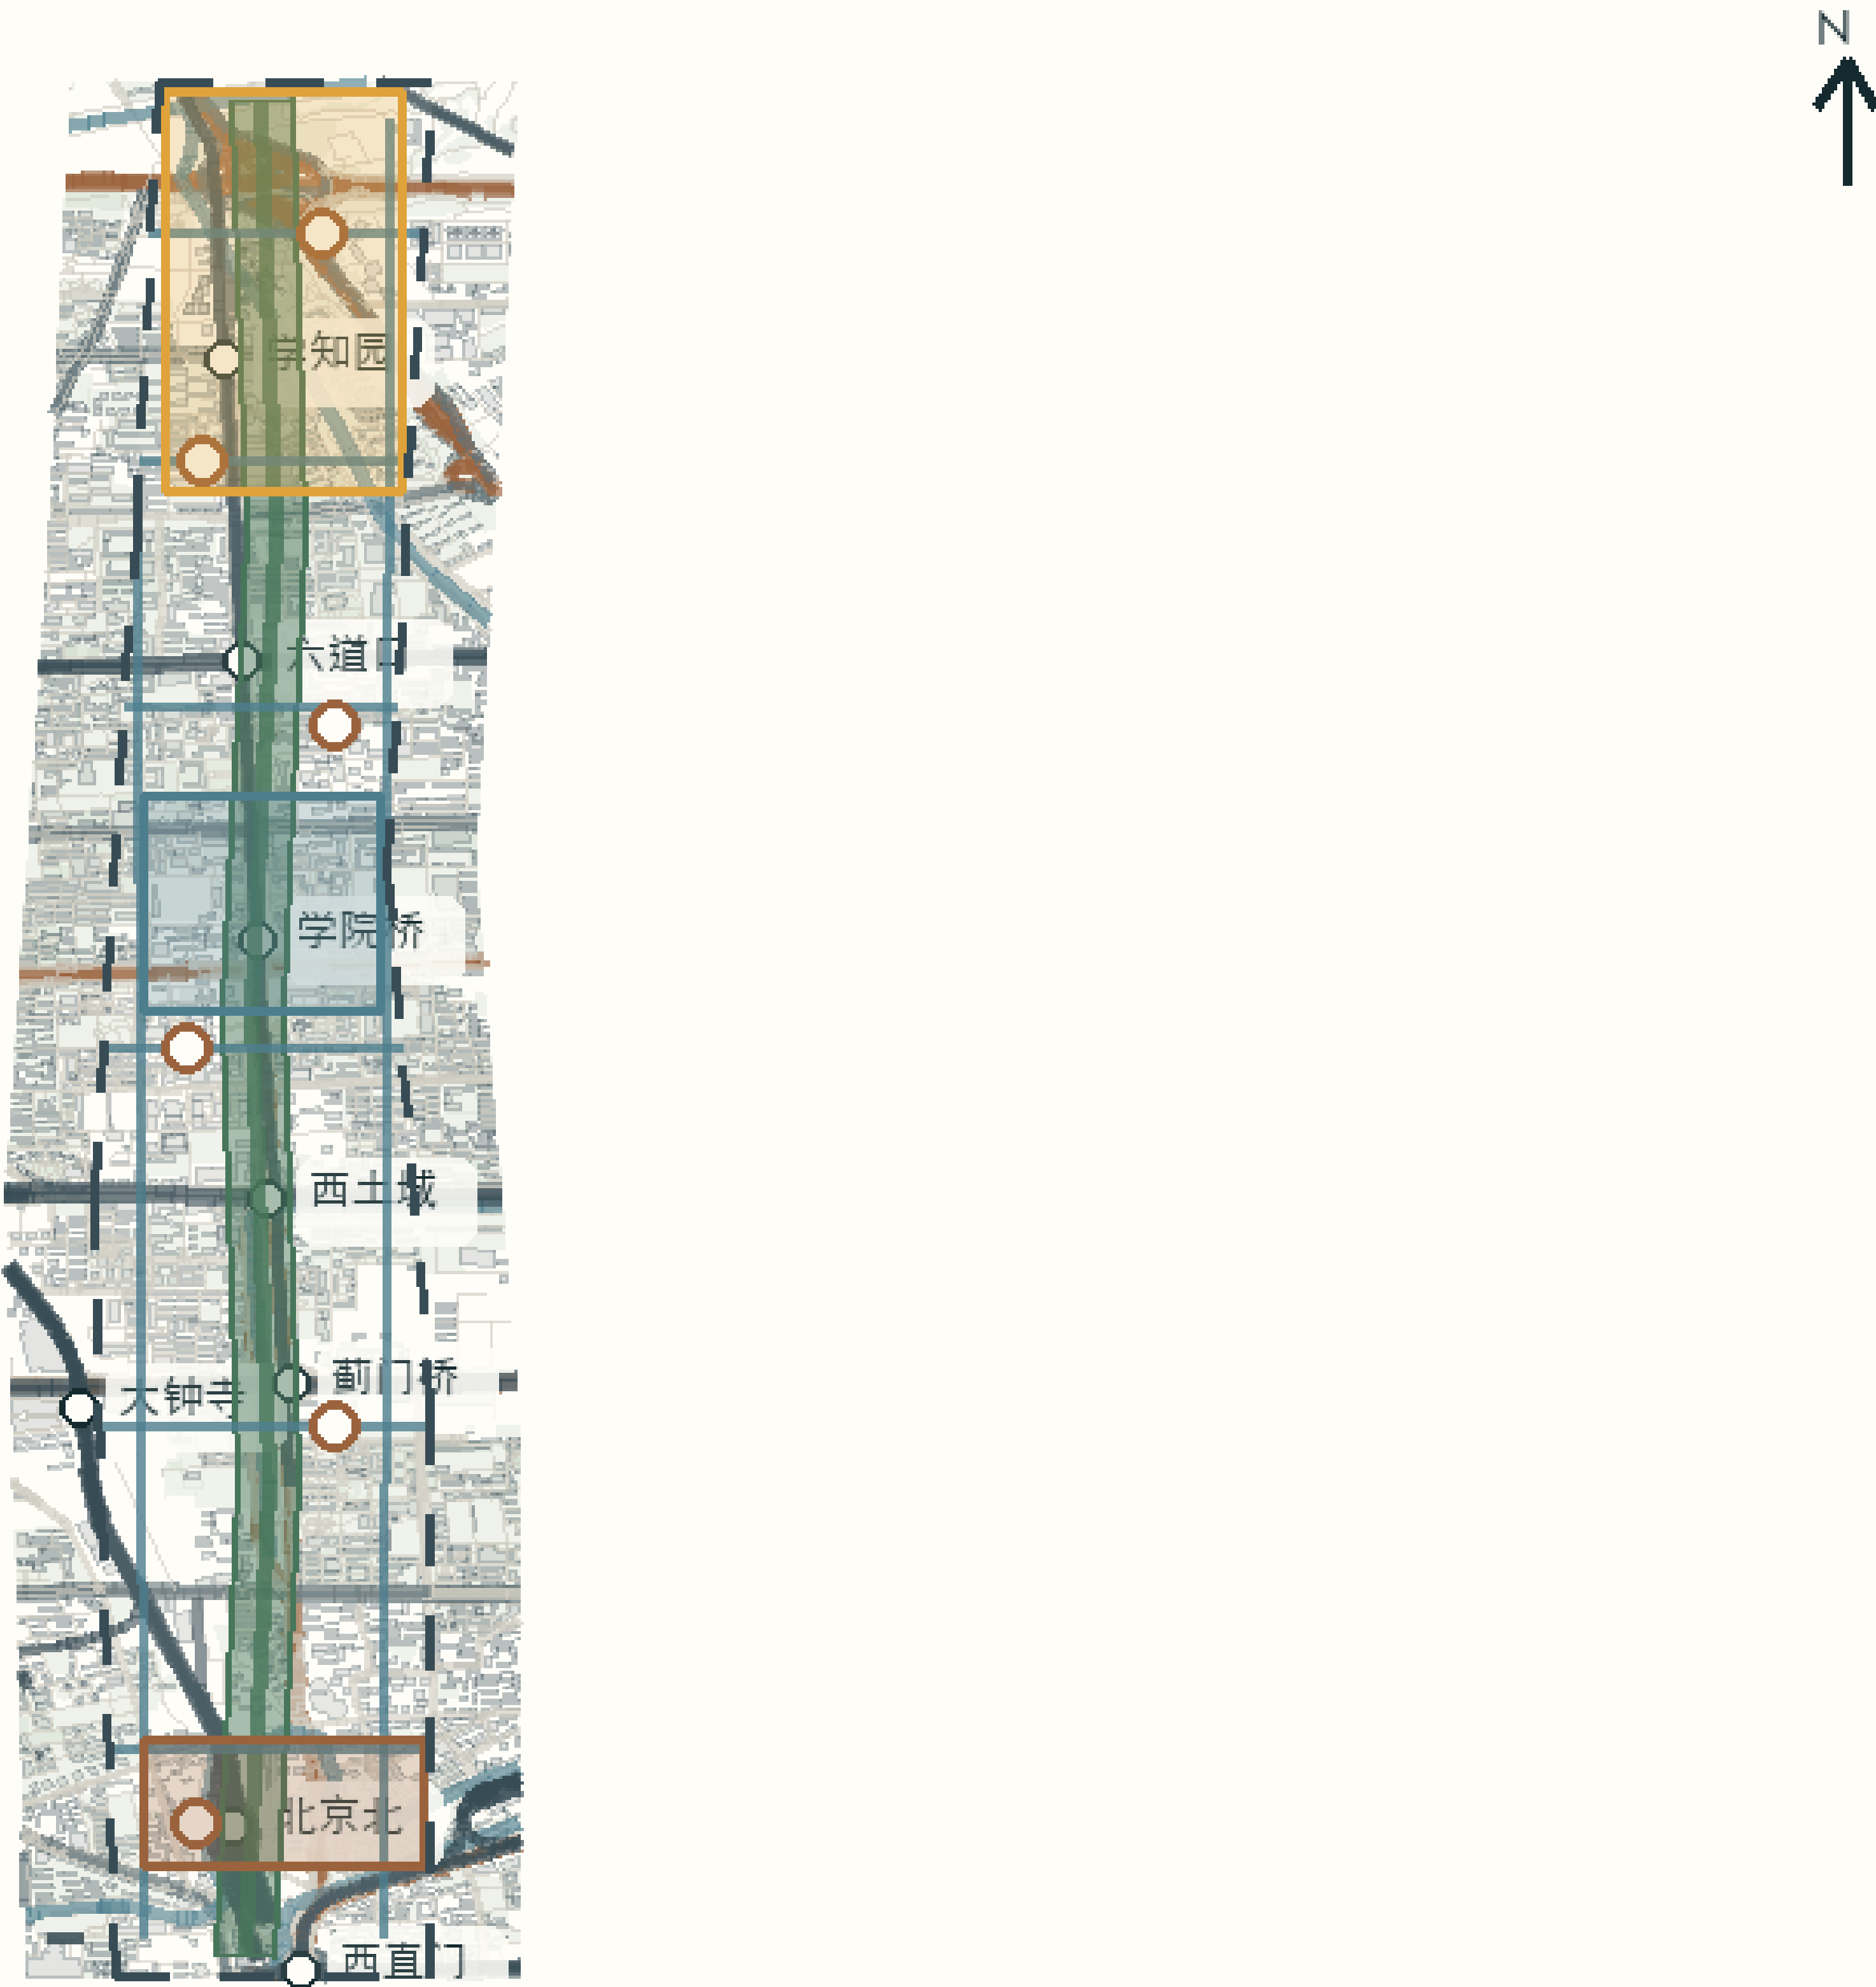

01 北 | 到达

众智园

开放研究首层 · 可信中试 · 协作庭

02 中 | 交换

AI 原点社区

第一周之家 · 完整生活 · 共生廊

03 南 | 归属

大钟寺—北京北

文化时间轴 · 应用院 · 城市门

设计骨架


绿脊 + 6条缝合 + 6处入院

© OpenStreetMap contributors (ODbL 1.0) , 2026-08-08 快照；仅作语境。虚线为 provisional geometry，非官方红线。

02 / SPATIAL STRUCTURE

一带 · 三段 · 两翼 · 多院

完整生活的空间结构：绿脊缝合，院落降尺度，两翼补功能

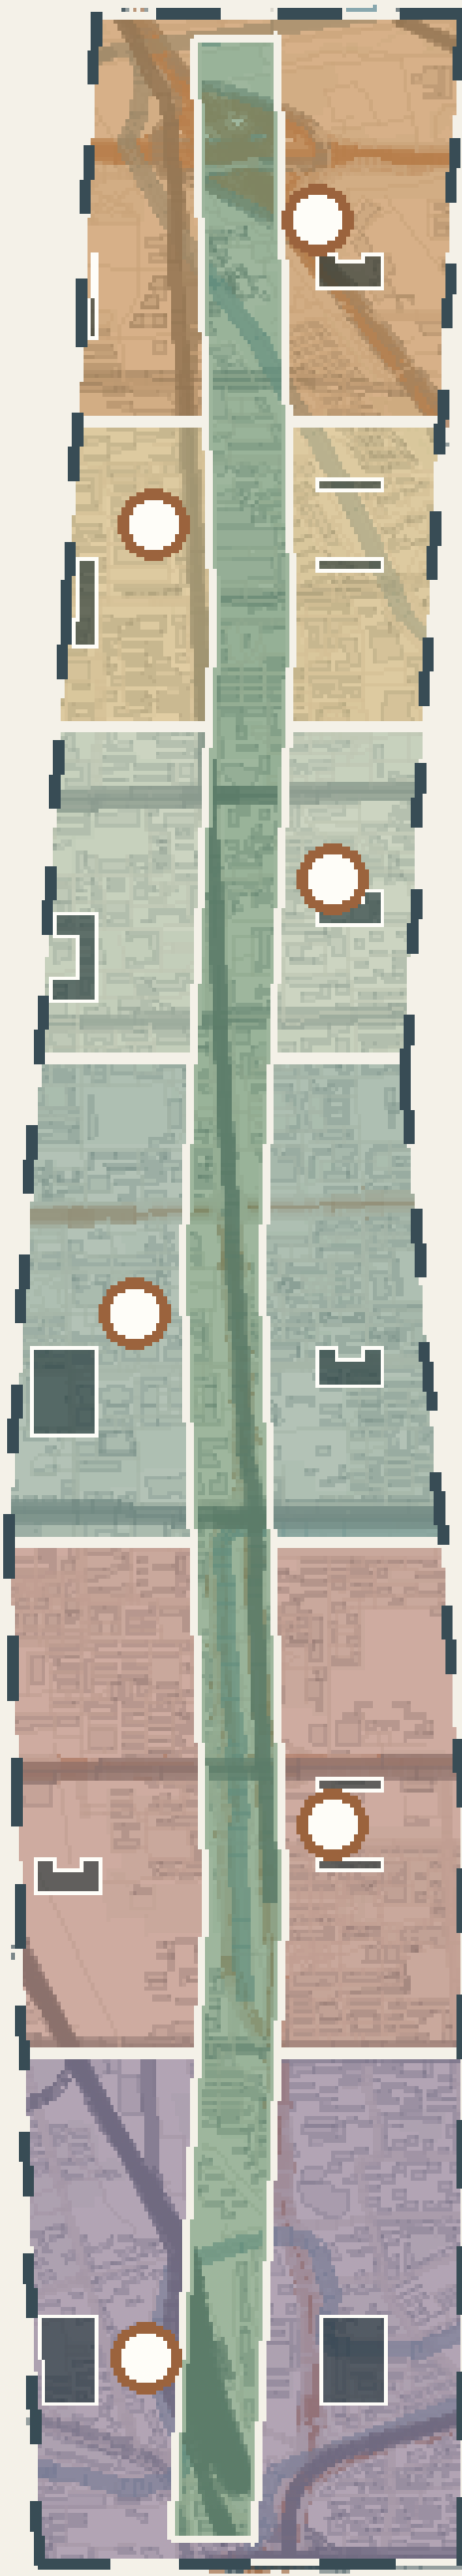

用地不是功能孤岛

- 0802 AI研发
- 0804 教育共学
- 0702 社区服务
- 0701 居住
- 05 商业服务
- 0803 文化
- 1401 公园绿地

北：研发到达门

中：完整生活核

南：文化城市门

中央绿脊 + 六条东西缝合

用地采用共同切线拓扑分割，union = 临时总体边界；分类为设计提案，不是已批控规。

重点区域 | 三处现场、三条剖面、三套首期动作

众智园可信中试 · AI 原点完整生活 · 大钟寺文化应用


03 / THREE KEY-AREA ATLAS

三处重点区 | 同一套专业问题，不同的空间回答

每处均表达现状语境、概念平面、典型剖面、首期动作与停止条件


01 众智园 | 可信中试场

基础设施切割与研发语境并存

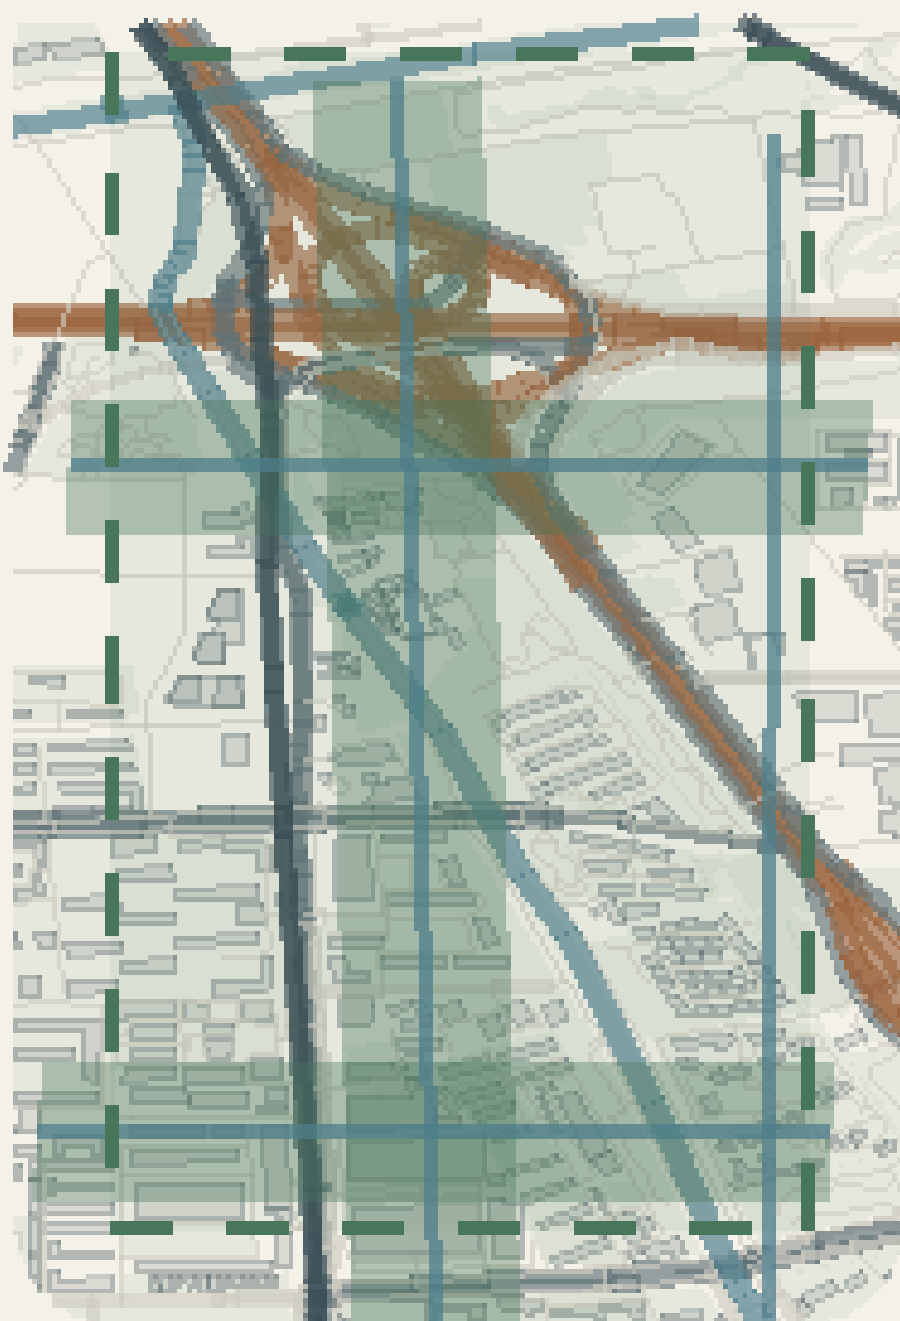

开放研究首层 · 协作庭 · 封闭验证机驿

概念剖面 | 林下公共界面—协作庭—后场机驿

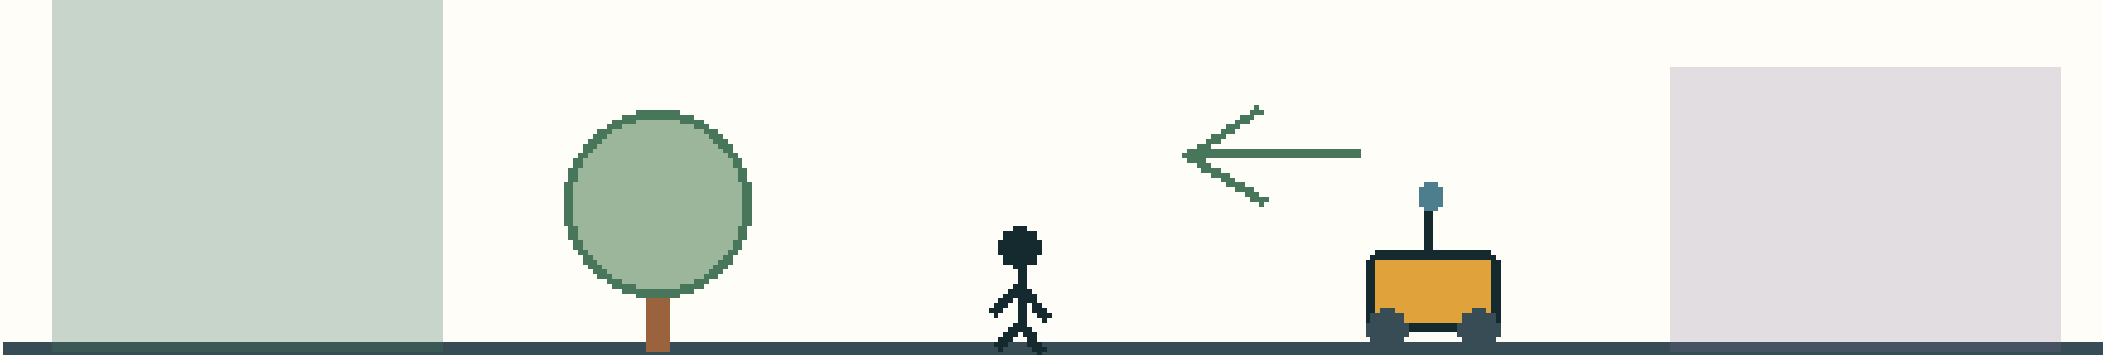


P5 / 先做轨道安全边界与场地许可审计

范围为 provisional；平面和尺寸待测绘、权属、消防与专项核验。

02 AI 原点 | 完整生活核

高校、社区与北四环高密交界

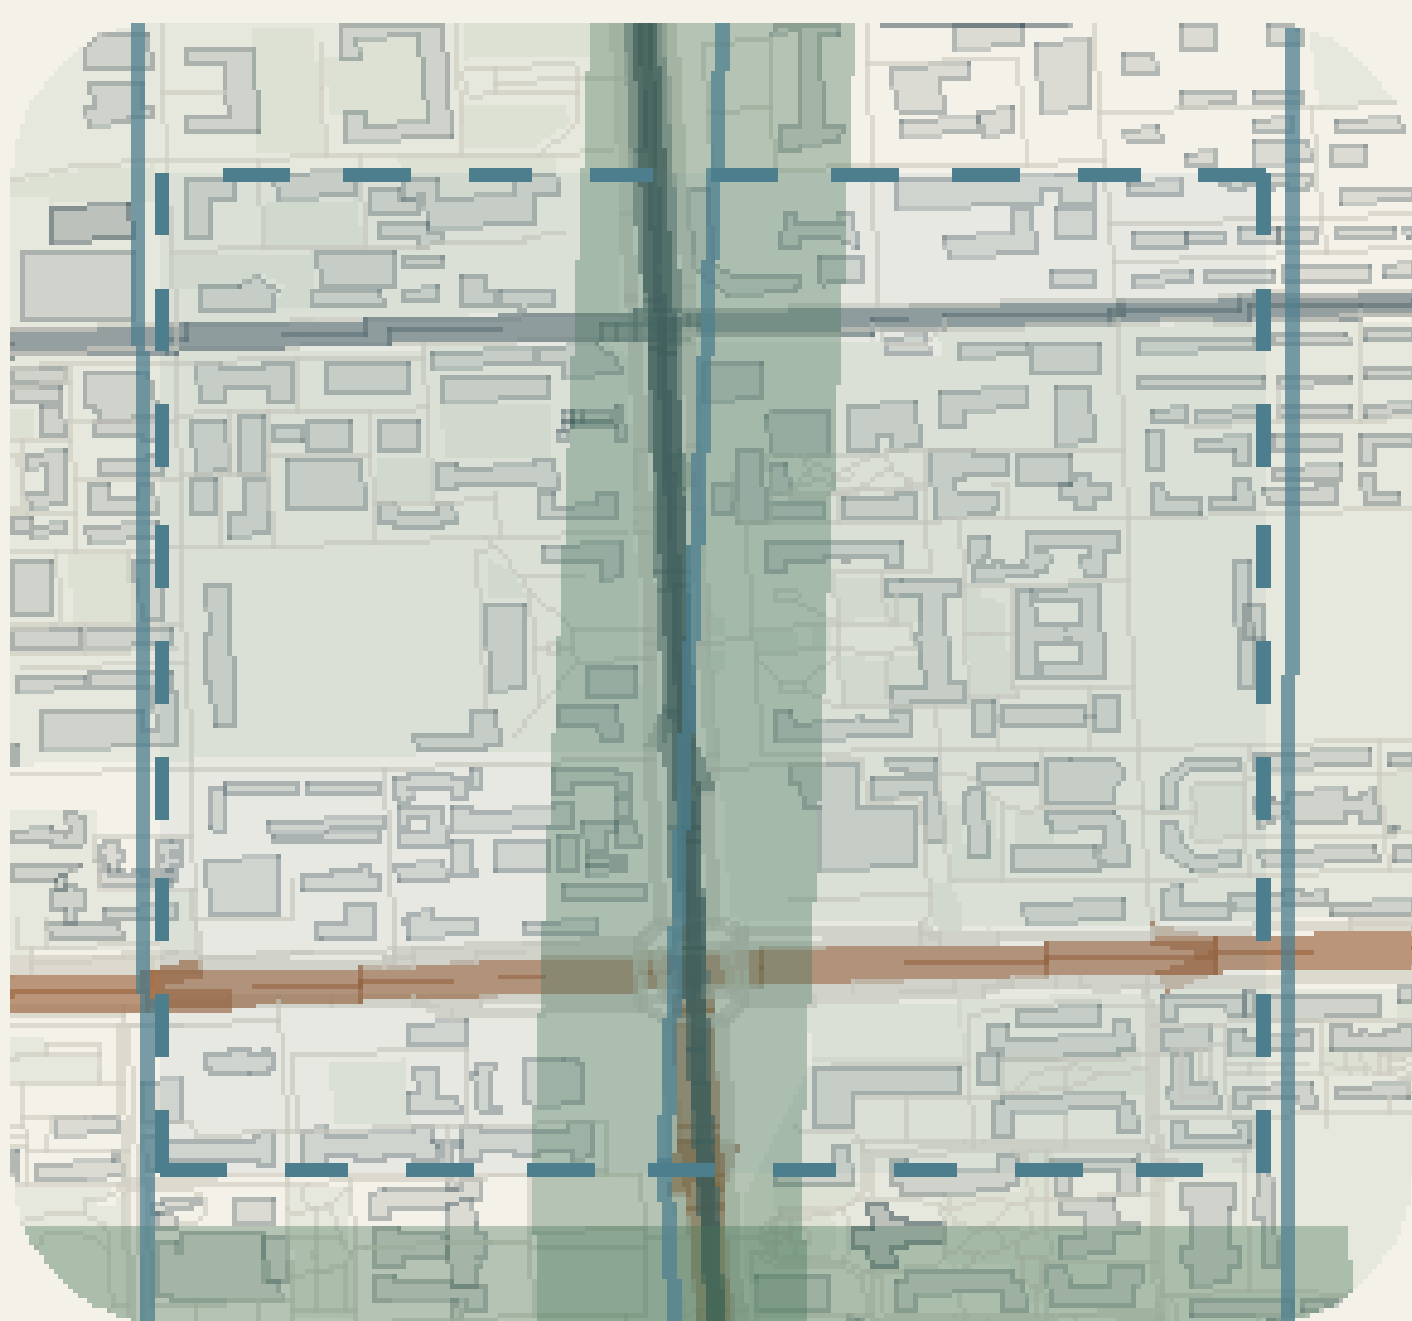

生活环 · 第一周之家 · 人优先共生廊

概念剖面 | 开放首层—入院—共生廊—社区服务




P4 / 先做百米生活环与无障碍共测

范围为 provisional；平面和尺寸待测绘、权属、消防与专项核验。


03 大钟寺 | 文化应用门

站城、产业与文保关系待核

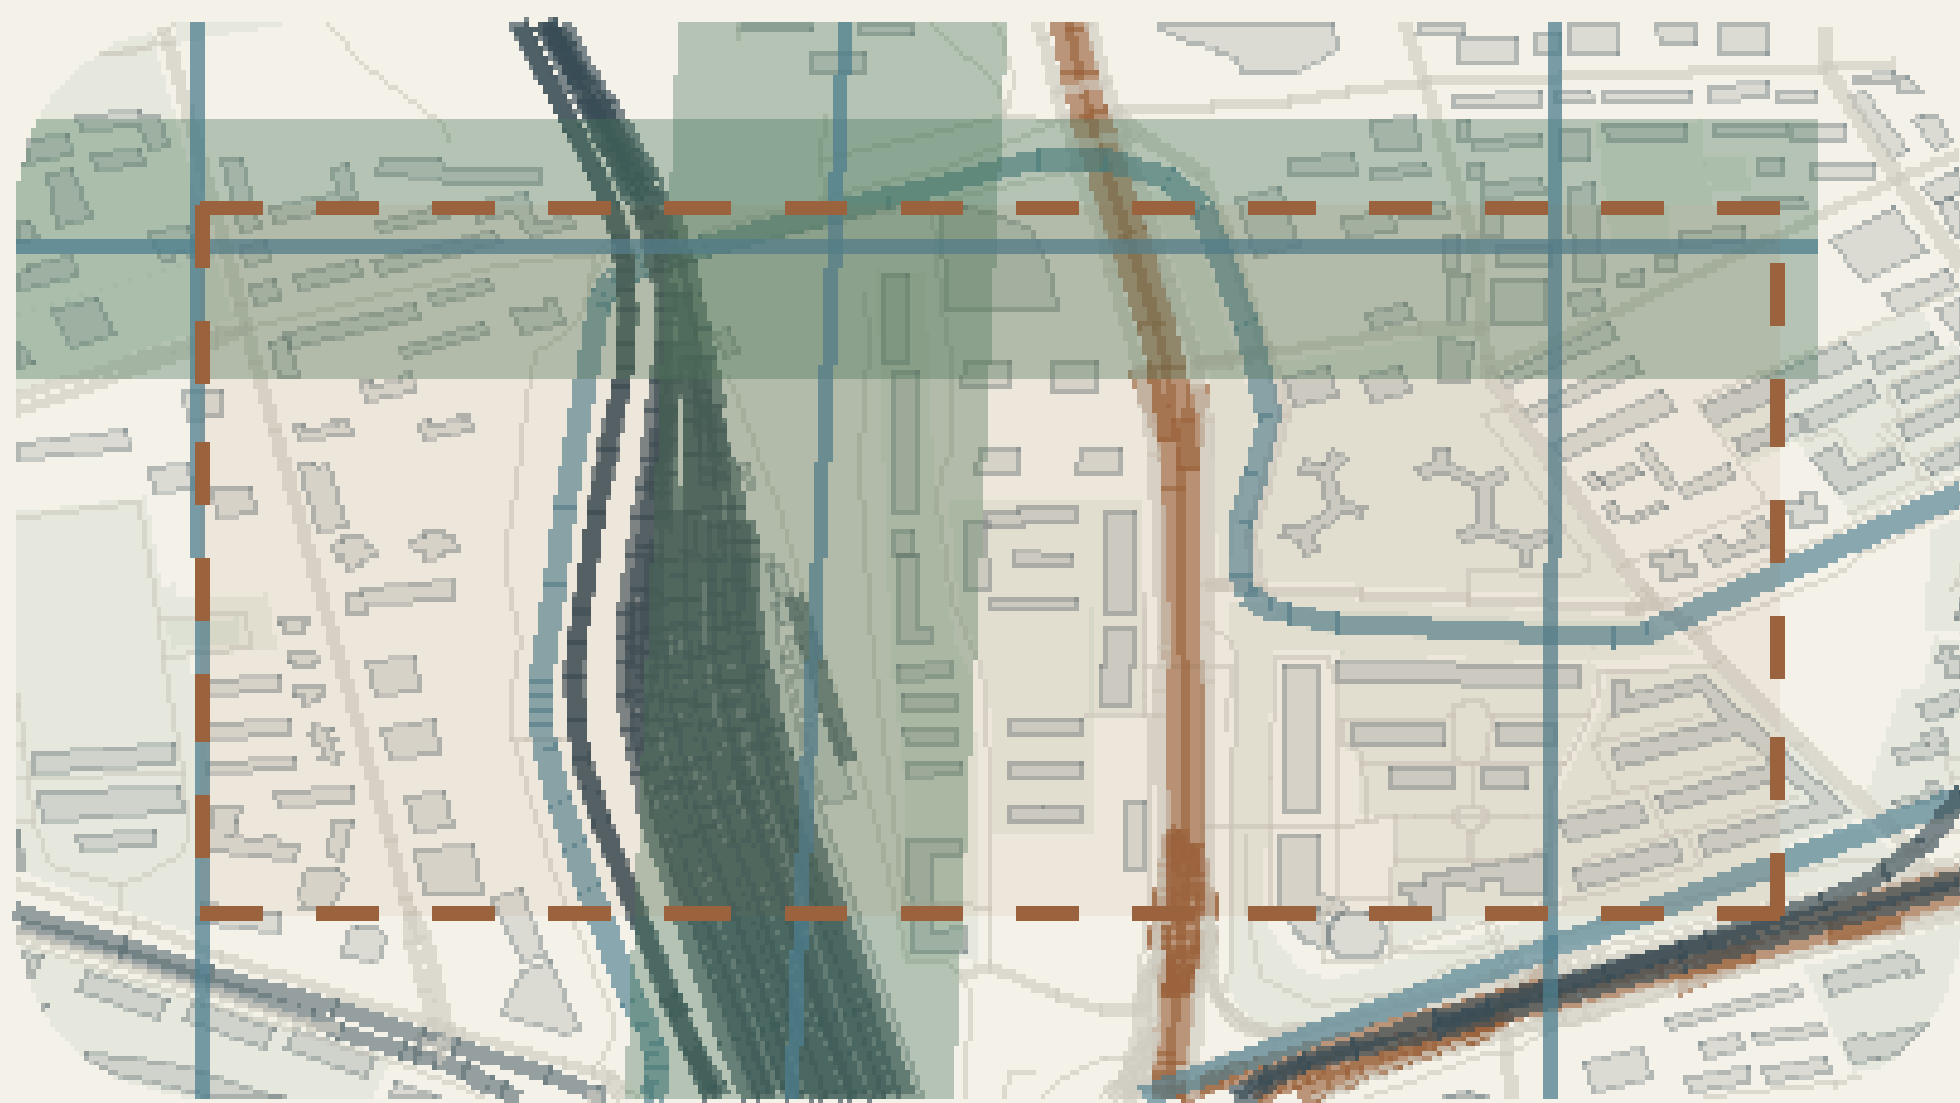

文化慢行 · 公开采用台 · 可退出展示

概念剖面 | 站口—文化门厅—应用院—后场服务

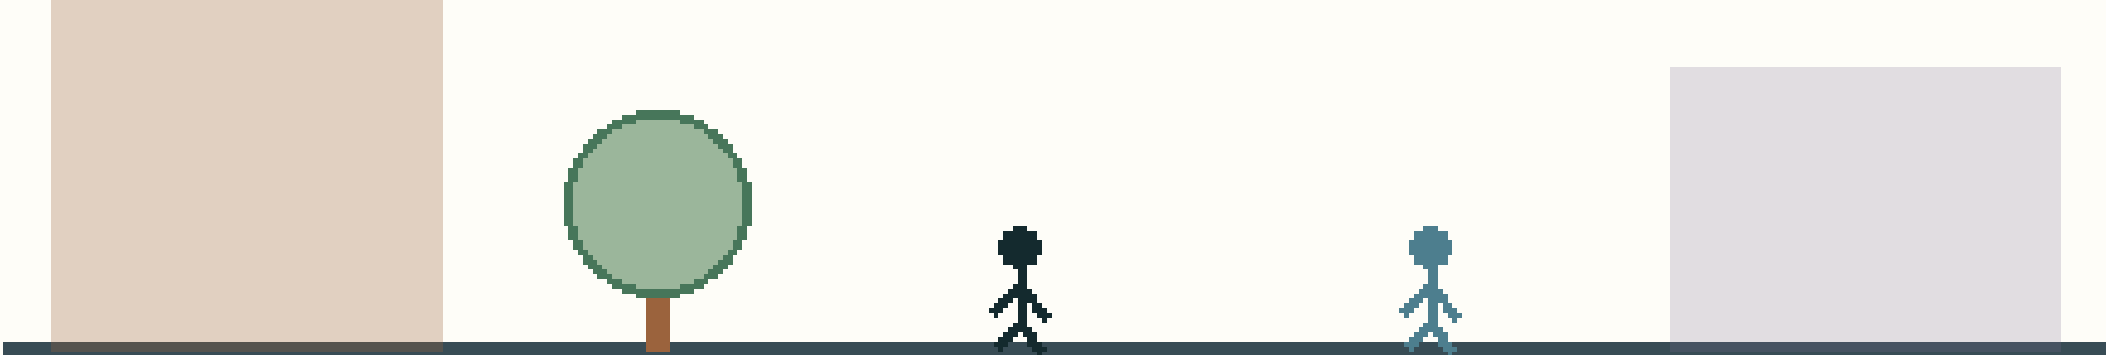

P6 / 边界文保冲突未解前不作工程落位

范围为 provisional；平面和尺寸待测绘、权属、消防与专项核验。

09 / HUMAN-AI-MACHINE TYPICAL SECTIONS

四条典型剖面 | 人和机器人共享城市，而不是各自被关起来

概念尺寸用于比较路权、界面与运行条件；入院—共生廊—协作庭—机驿保持连续通达

四类空间原型 | 概念宽度，待现场深化

A 入院 | 12-18m

照护 / 儿童 / 安静停留

树池 3m | 无目的停留 6m | 开放首层 3m

默认禁入

C 协作庭 | 24-36m

公众主动参与，监督、同意、急停与退出

观察边 5m | 协作区 12m | 缓冲 5m | 后场接口

B 共生廊 | 18-24m

人优先共享，成熟服务机器人进入日常

首层 4m | 步行 6m | 低速共享 4m | 绿化 4m

D 机驿 | 8-12m

补给、维护、货物交接和封闭验证

服务口 3m | 维护 4m | 充换电 3m | 防火分隔

连续梯度，不是空间隔离



共享路权矩阵

使用者	入院	共生廊	协作庭	机驿
居民 / 步行者 / 轮椅	●	●	●	△
儿童 / 照护使用者	●	●	△	—
日常服务机器人	—	●	△	●
试验 / 互动机器人	—	—	●	●
● 默认可用 △ 受邀 / 有人陪同 — 默认不进入				

共享运行必须同时满足

- 01

任务、路线与负责人可见
- 02

遇人主动减速、让行或暂停
- 03

公众可拒绝互动且服务不降级
- 04

工作人员可立即接管并公开事件
- 不让行、不可见、无法接管或进入入院 → 立即暂停。

10 / INDUSTRY VALIDATION SYSTEM

三类产业验证 | AI 创新不等于三种机器人展示

具身智能、公共服务智能体、空间智能各有现场、基线、测试、停止规则和开放输出



实施与运营 | 八个行动包和阶段门

可调查、可采购、可暂停；先补底数，再做可逆试点

11 / ACTION PACKAGES + DELIVERY GATES

八个行动包 | 把总体概念压到可调查、可采购、可暂停的工作面

每个行动包都有空间锚点、牵头者、依赖和阶段门；先补底数，再做可逆试点

ID	行动包	空间锚点	牵头	阶段	依赖 / 阶段门
P0	底图与现状审计	全带	规划/测绘	0	official边界、控规、权属；未齐不作工程量
P1	六条缝合廊实走	H1-H6	交通/社区	1	无障碍、过街、遮阴；路线未经复核不上线
P2	第一周之家	AI原点	街道/运营	1	人工窗口与纸质路径先运行
P3	共生廊与协作庭	原点/众智园	运营/安全	1	状态、让行、急停、接管任一失败即停
P4	百米完整生活环	AI原点	更新/社区	2	人口、消防、首层与服务缺口调查
P5	可信中试场	众智园	园区/第三方	2	环评、消防、测试许可与后场责任
P6	文化应用院	大钟寺	文保/运营	2	边界与文保冲突未解前不工程落位
P7	开放运营与年报	全带	多方理事会	3	公开指标、失败案例、维护预算和退出记录

三段实施

阶段0 | 补底数

边界、控规、现状、权属、文保与市政

阶段1 | 低后悔试点

P1-P3 | 可移动、可撤、有人值守

阶段2-3 | 永久化与运营

P4-P7 | 专项论证后再投资

资源账：空间 / 建设 / 运营 / 数据与算力 / 维护与退出。未说明维护和退出预算的项目不得进入永久建设。