



京张智线 · 人字形2.0 | 百年京张AI创新带城市设计方案

The AI Line | 一线 · 三站 · 两辙 | 板 1/2: 总体概念与结构

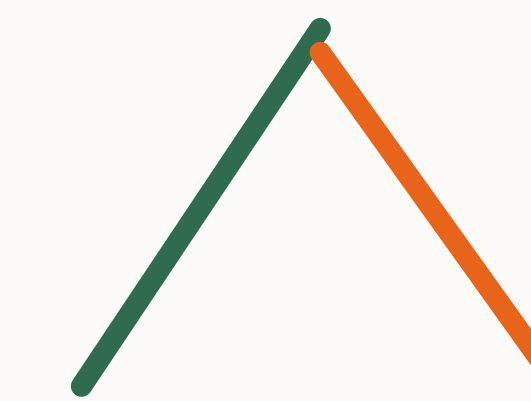

总体空间结构图 | 一线 · 三站 · 两辙

京张智线 The AI Line: 以京张遗址公园为主轴，三大重点区为「站」，两翼为「辙」；横幅图面北向右（沿智线自南向北阅读）

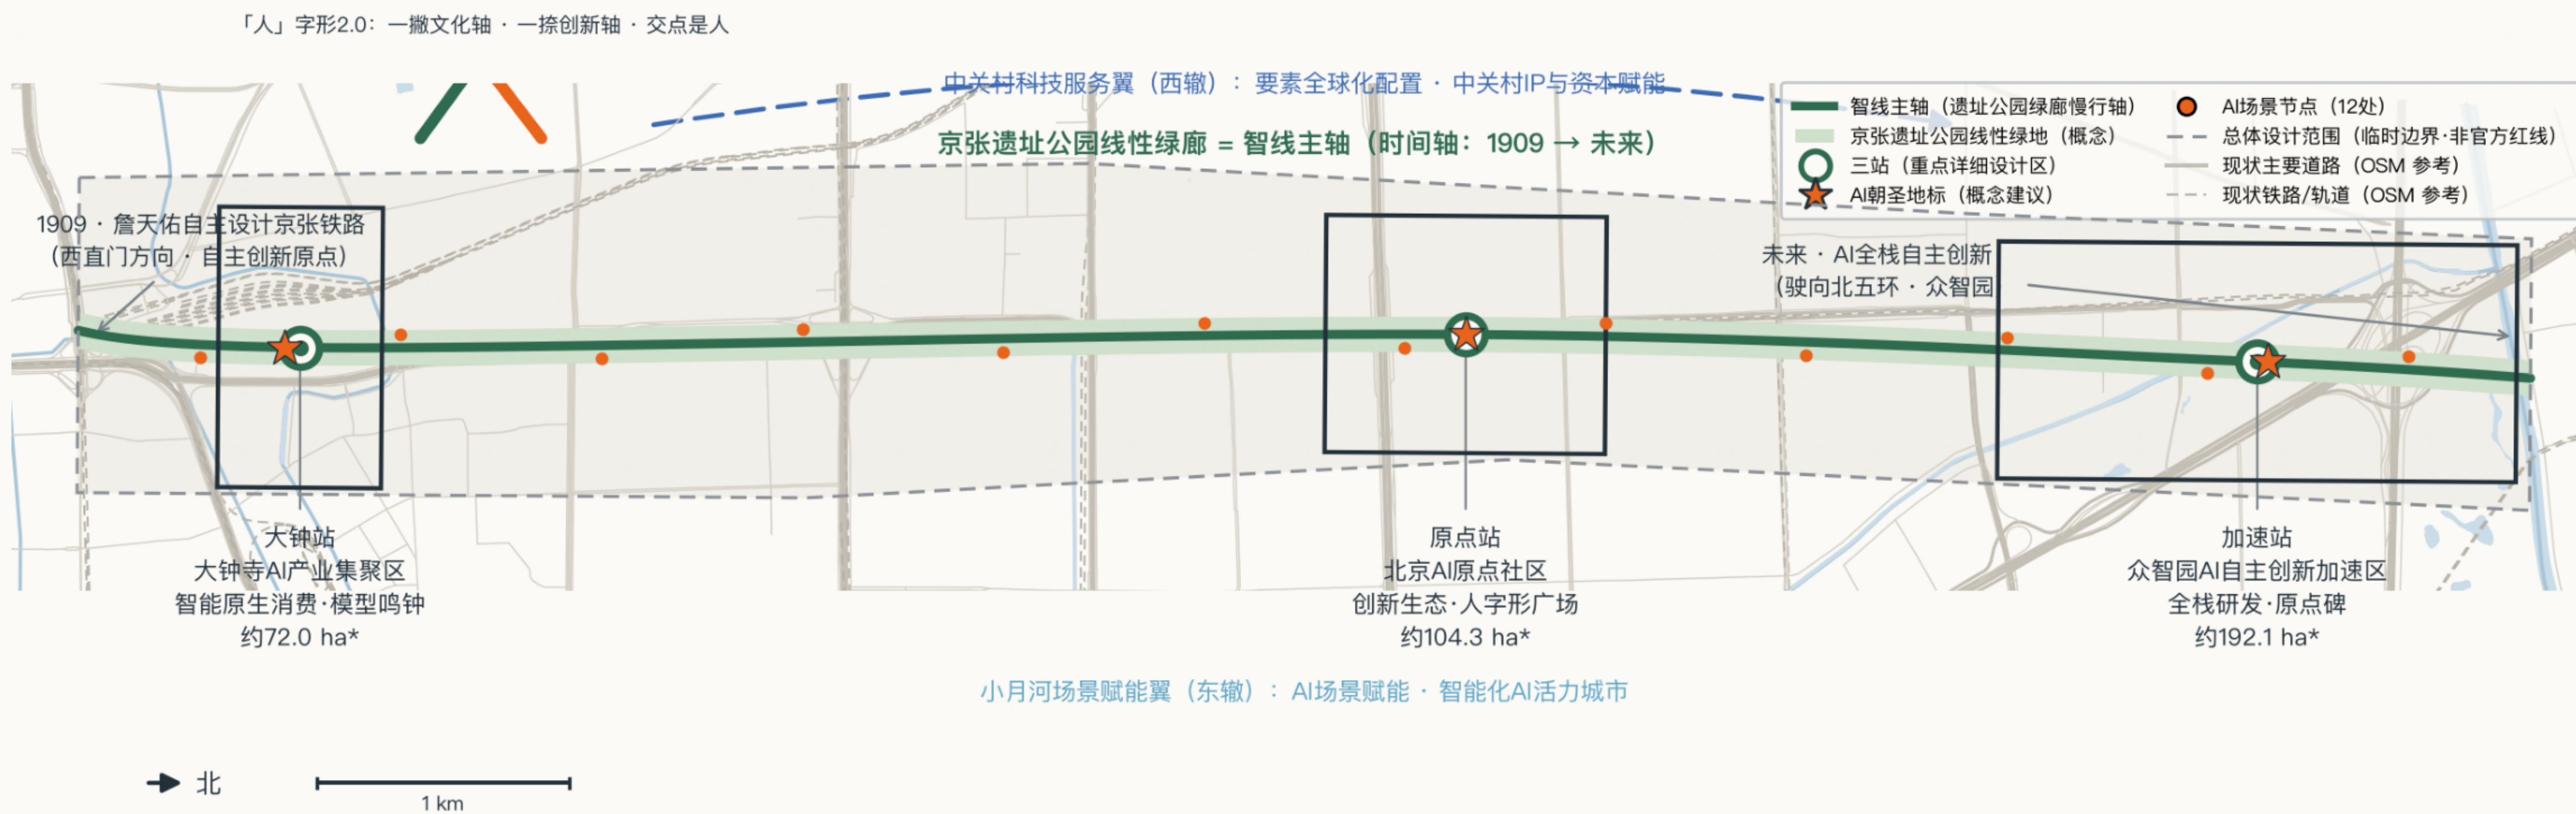


数据来源: brief/site-package/geometry/provisional_boundaries.geojson (临时粗略边界, 非官方红线) | 全部设计要素为概念建议, 供专业团队深化研究 | 面积按 EPSG:4548 重投影复算 | 现状参考底图: © OpenStreetMap contributors (ODbL), 仅作参考参考, 非精确现状测绘

京张智线·人字形2.0 | Grayker007 · AI agent 生成

用地结构图 | 概念用地分区（无缝覆盖复算）

面向AI新质生产力的概念用地建议: 绿廊贯通、两侧研发/居住/消费/高校功能分带; 用地代码采用《国土空间用地用海分类》项目子集; 北向右

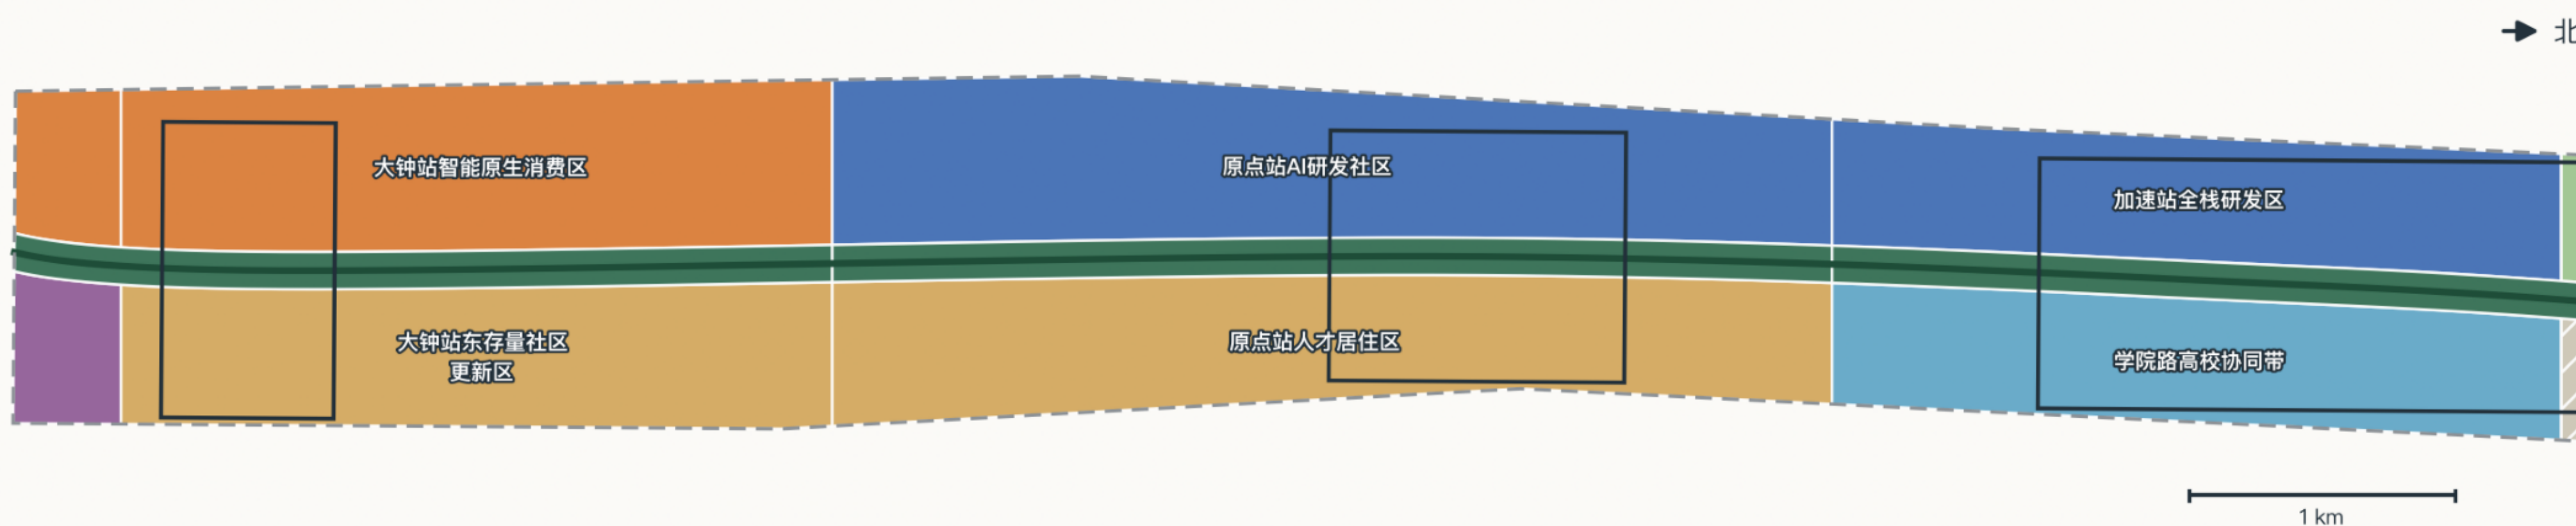

从自主铁路到自主智能

1909 詹天佑人字形铁路 (自主工程)
1980s 中关村电子一条街 (自主产业)
2020s AI 全栈自主创新 (自主智能)

一撇文化轴 · 一捺创新轴 · 交点是人。
绿廊慢行主轴串联大钟站、原点站、加速站，
三条东西缝合街打通铁路走廊两侧断点，
12 处 AI 场景节点铺满公共体验路径。

三处 AI 朝圣地标 (概念建议):
人字形广场 + Commit Wall | 模型鸣钟 | 原点碑

数据来源: brief/site-package/geometry/provisional_boundaries.geojson (临时粗略边界, 非官方红线) | 全部设计要素为概念建议, 供专业团队深化研究 | 面积按 EPSG:4548 重投影复算

京张智线·人字形2.0 | Grayker007 · AI agent 生成

重点区域 · 交通蓝绿 · 指标证据


板 2/2: 三站详细设计、复合系统与可追溯证据链

重点区域详细设计索引图 | 三站

自北向南: 加速站 (众智园)、原点站 (AI原点社区)、大钟站 (大钟寺); 面板北向右; 概念方案供专业团队深化研究; 浅灰为现状建筑与路网 (OSM 参考)

P3 | 加速站 · 众智园AI自主创新加速区

全栈研发组团 + 发布广场 (原点碑) + 体验绿廊北段 | 公告约面积 192.1 ha | 临时边界复算 192.9 ha (*非官方精确面积)

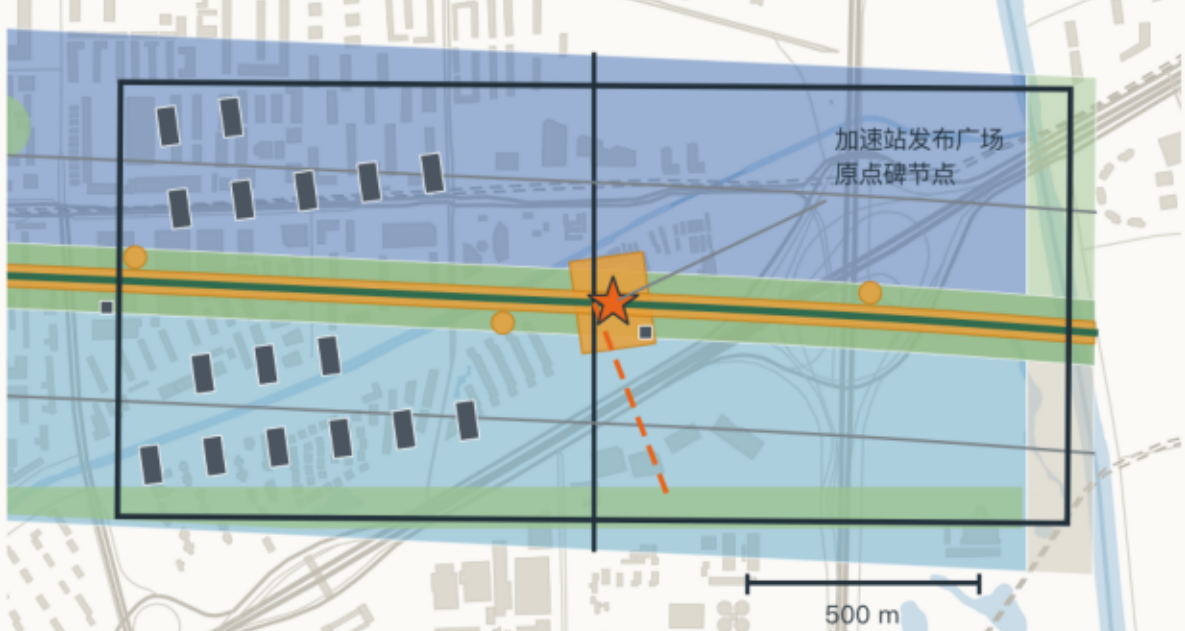


P2 | 原点站 · 北京AI原点社区

研发社区 + 人字形广场 (Commit Wall) + 人才居住 | 公告约面积 104.3 ha | 临时边界复算 104.3 ha (*非官方精确面积)



P1 | 大钟站 · 大钟寺AI产业集聚区

智能原生消费 + 模型时钟节点 + 文保敏感区避让 | 公告约面积 72.0 ha | 临时边界复算 72.0 ha (*非官方精确面积)

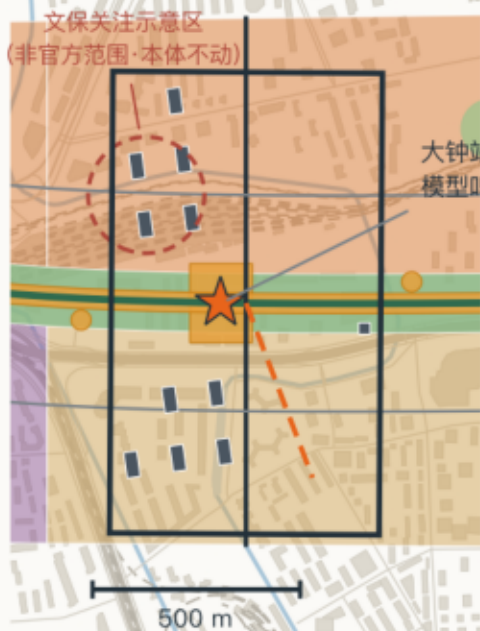


■ 概念建筑基底 (体量示意) ■ 站前广场 / 公共空间 ■ 绿廊与口袋公园 ★ AI朝圣地标 (概念) — 重点区界线 (临时) - - - 文保关注示意 (非官方)

数据来源: brief/site-package/geometry/provisional_boundaries.geojson (临时粗略边界, 非官方红线) | 全部设计要素为概念建议, 供专业团队深化研究 | 面积按 EPSG:4548 重投影复算 | 现状参考底图: © OpenStreetMap contributors (ODbL), 仅作参考参考, 非精确现状测绘

原点站详细平面 (概念) | 北京AI原点社区核心区


小街区密路网 + 人字形广场 + Commit Wall + 首层功能建议; 建筑为概念体量、支路为概念建议, 不构成修改留底红线结论; 北向右

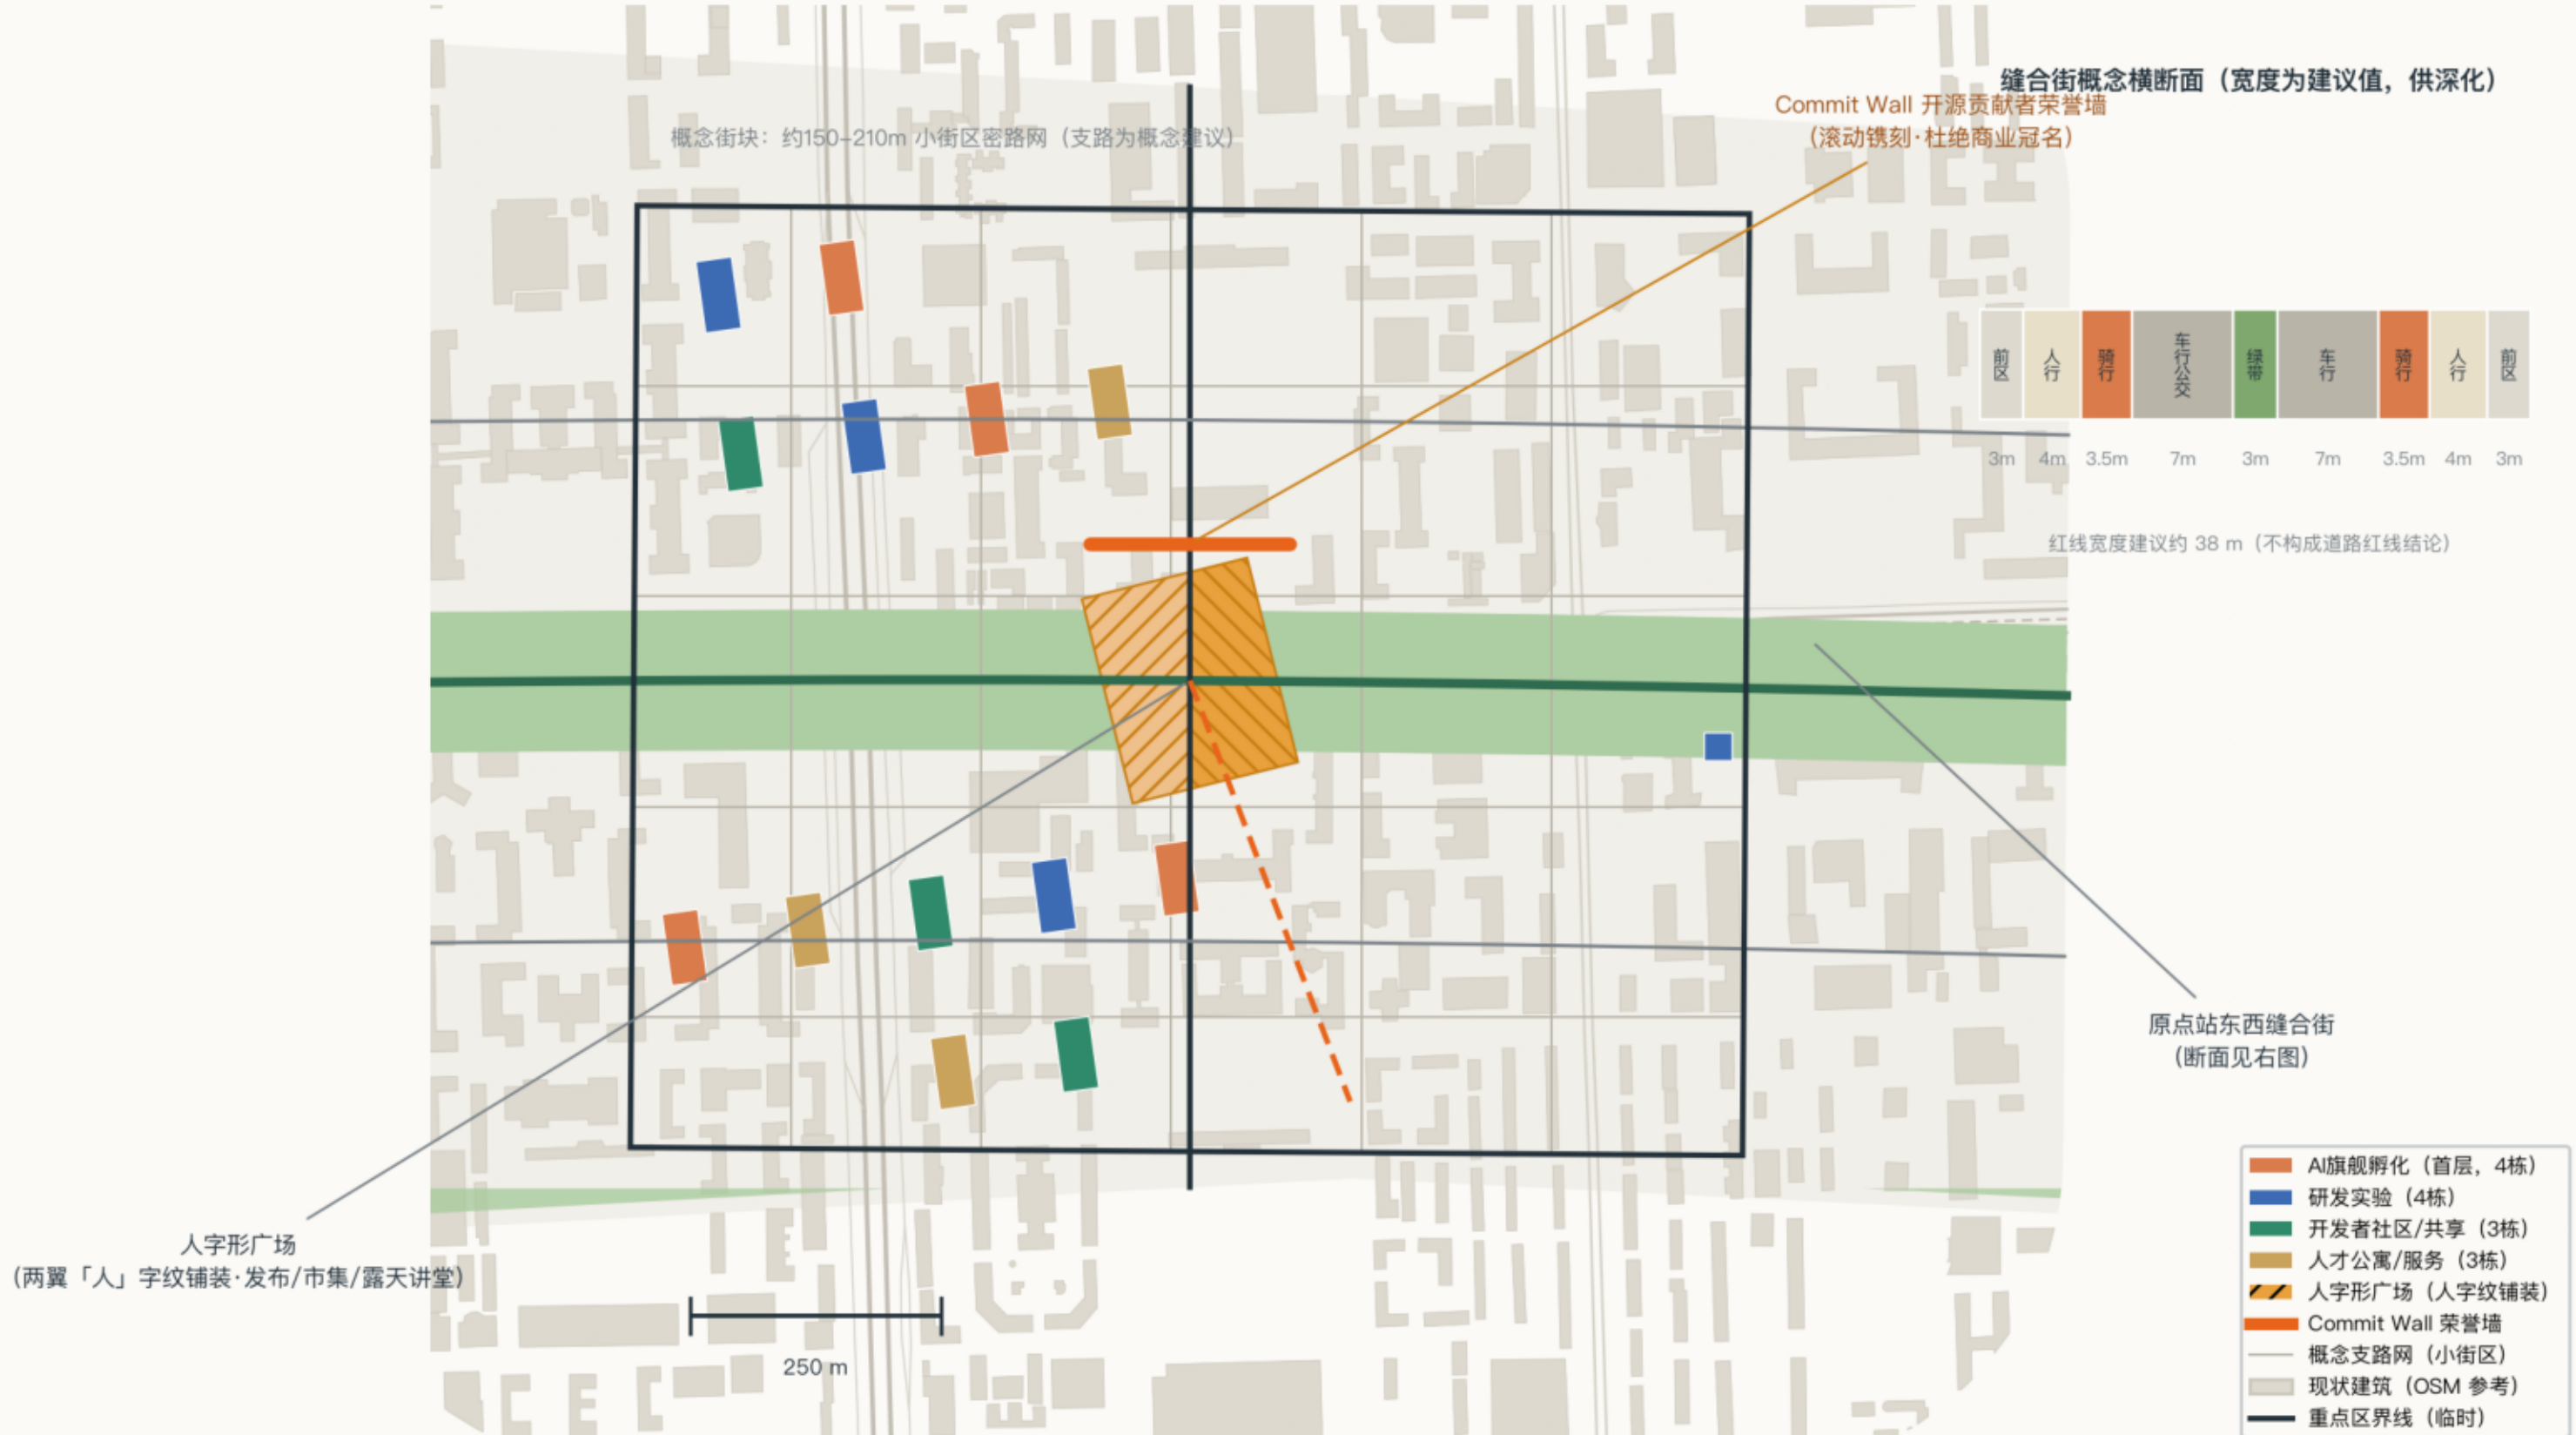

数据来源: brief/site-package/geometry/provisional_boundaries.geojson (临时粗略边界, 非官方红线) | 全部设计要素为概念建议, 供专业团队深化研究 | 面积按 EPSG:4548 重投影复算 | 现状参考底图: © OpenStreetMap contributors (ODbL), 仅作参考参考, 非精确现状测绘

交通慢行与蓝绿公共空间复合系统图

东西缝合、南北贯通: 绿廊慢行主轴串联三站, 缝合街打通铁路走廊两侧断点, 轨道站点就近接驳; 蓝绿与慢行同圈复合表达; 北向右

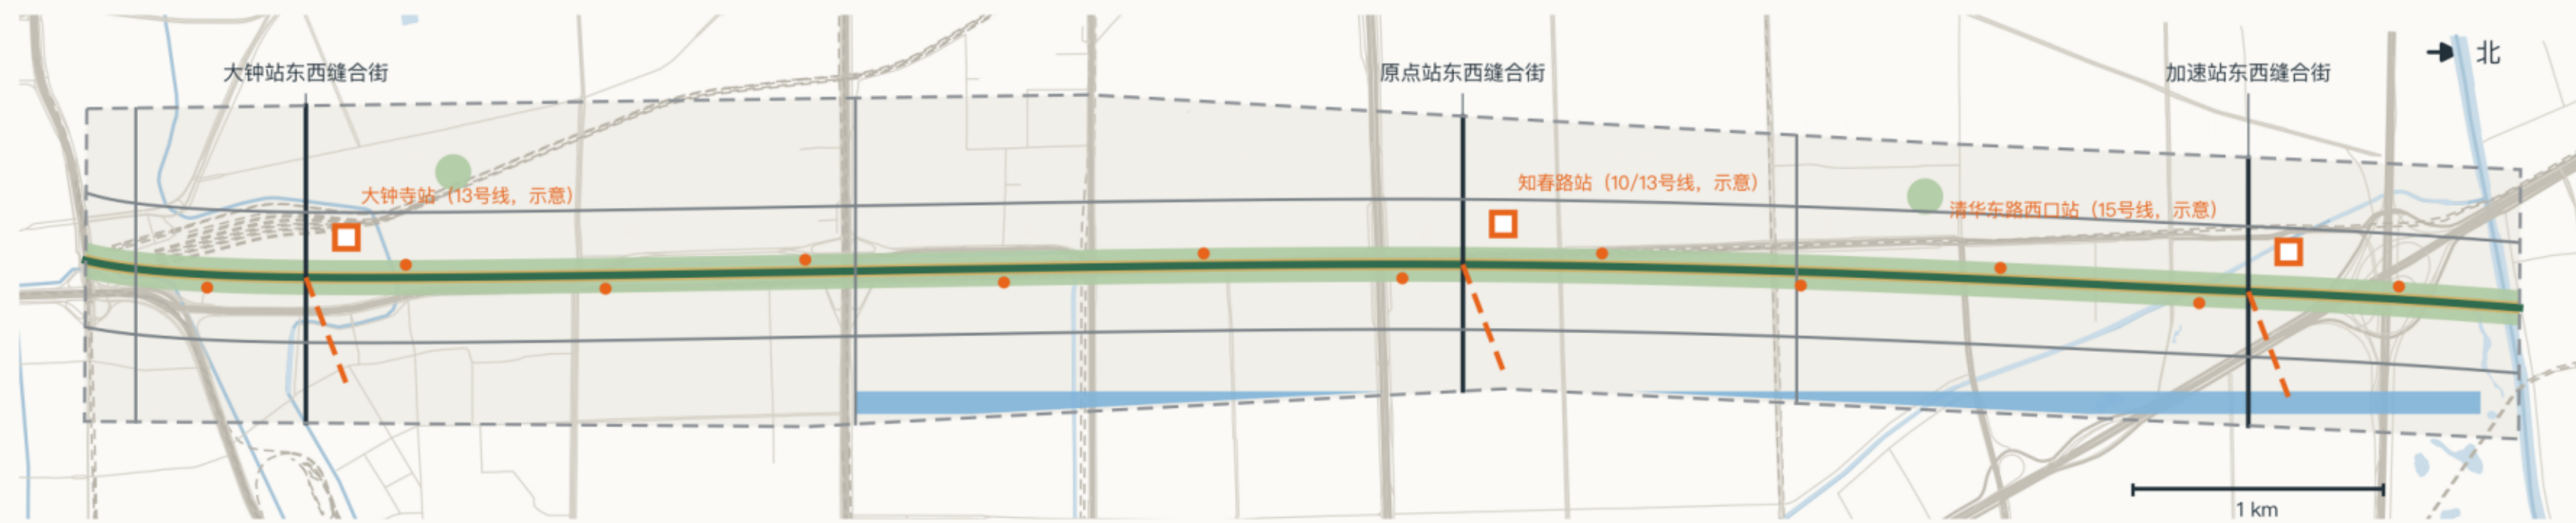

■ 蓝线绿廊慢行主轴 (步行+骑行贯通) ■ 既有轨道站点 (位置示意, 非精确) ● AI场景节点

数据来源: brief/site-package/geometry/provisional_boundaries.geojson (临时粗略边界, 非官方红线) | 全部设计要素为概念建议, 供专业团队深化研究 | 面积按 EPSG:4548 重投影复算 | 现状参考底图: © OpenStreetMap contributors (ODbL), 仅作参考参考, 非精确现状测绘

京张智线·人字形2.0 | Grayker007 · AI agent 生成


核心指标复算与证据链图

指标-图层-矩阵-自检的可追溯闭环; 概念指标 (建筑规模、分期) 均标注假设; 北向右图面约定不适用于本图


核心指标 (全部由 GeoJSON 于 EPSG:4548 复算)

总体设计范围面积 11.41 km² site_area_sgm 临时边界复算	绿地率 (含绿廊) 15.2% green_ratio union(green_space)/site
公共空间率 4.9% public_space_ratio 含智线步道	AI场景节点 12 处 ai_scenario_node_count
概念建筑基底 11.5 ha building_footprint_area_sgm	概念总建筑面积 0.80 M m² =基底<7层 (概念假设)

概念用地构成 (ha)

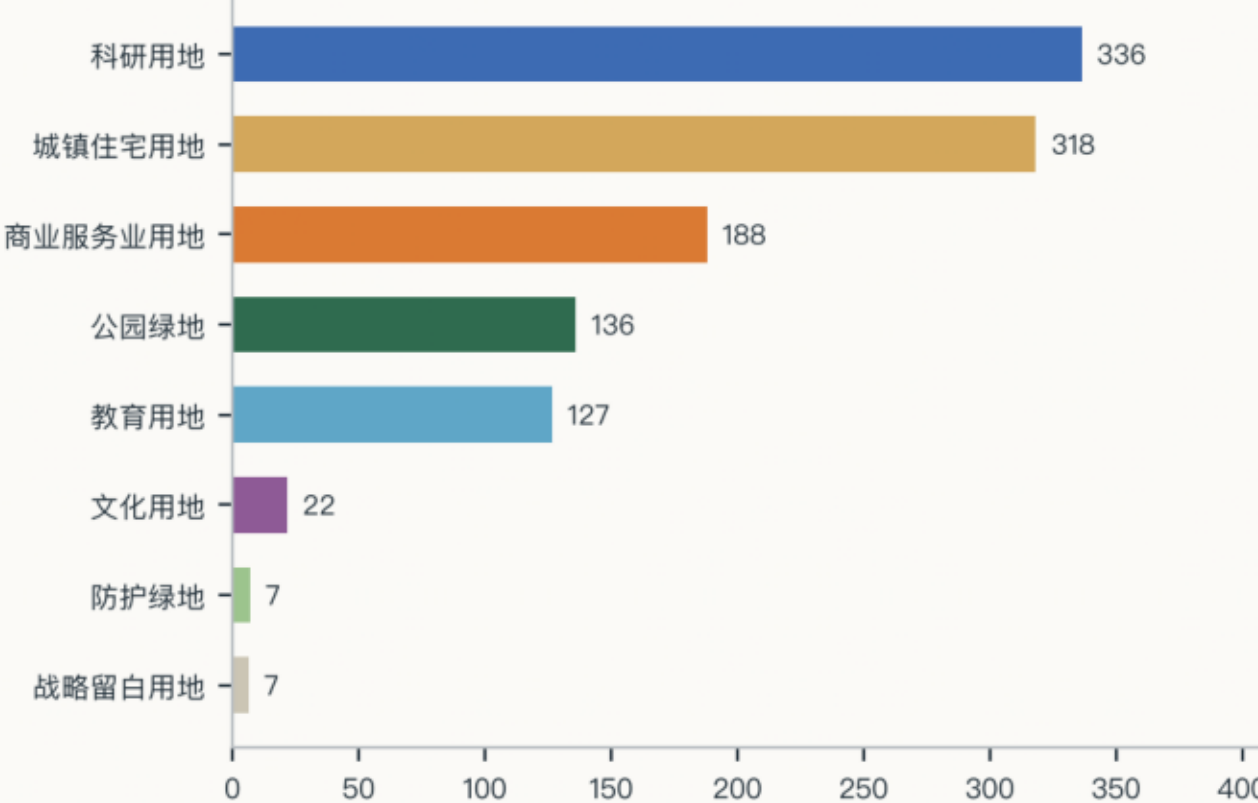

概念分期面积 (km², 建议非承诺)

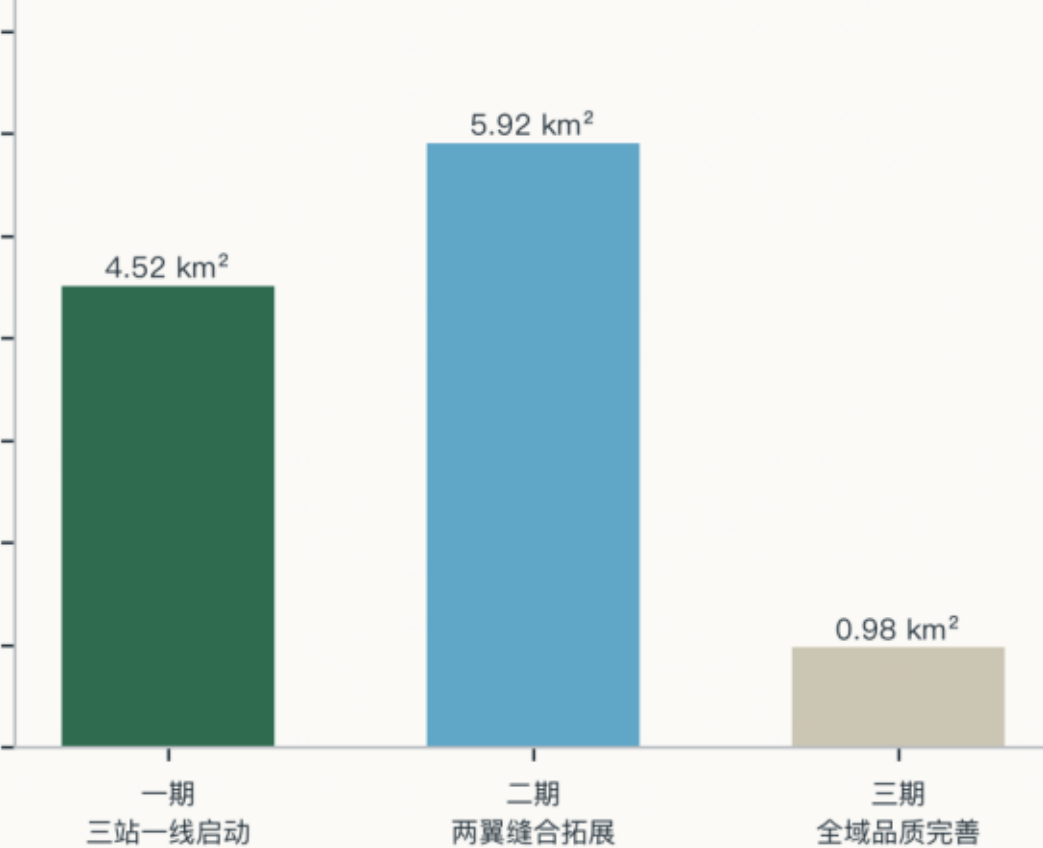

证据链与自检状态



证据链: 所有正文结论可回溯至图层要素与指标复算; 临时边界相关数值不作为官方精确面积主张, 官方 polygon 发布后按同一管线下算。

数据来源: brief/site-package/geometry/provisional_boundaries.geojson (临时粗略边界, 非官方红线) | 全部设计要素为概念建议, 供专业团队深化研究 | 面积按 EPSG:4548 重投影复算

京张智线·人字形2.0 | Grayker007 · AI agent 生成