


京张智脊·总体概念与三层范围框架

一脊三核两翼多点 | 百年京张文化带 / 都市AI生活体验带 / AI融合创新带

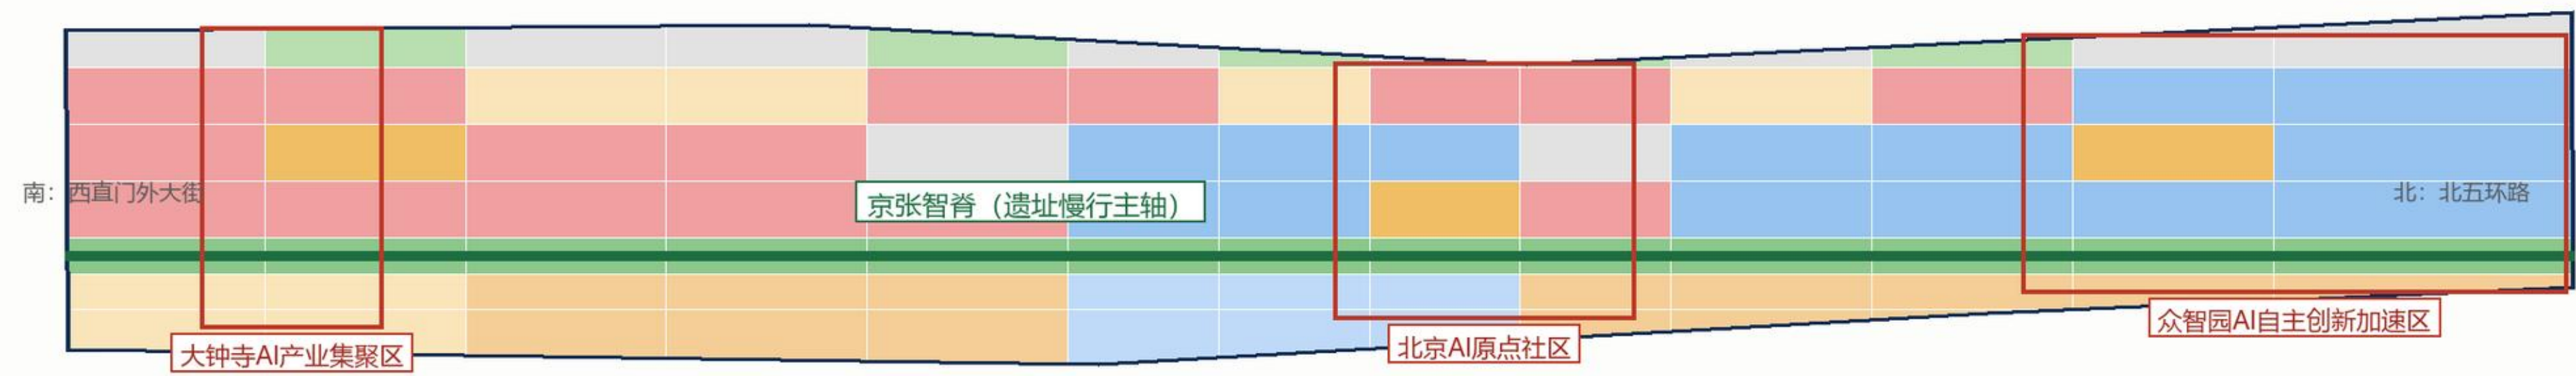

三层范围工作框架

统筹研究范围 43.6 km<sup>2</sup>  
AI产业生态与未来城市形态研究

总体设计范围 11.4 km<sup>2</sup>  
控规深度城市设计（本地图落图范围）

重点区域 368.4 ha（3处）  
规划综合实施方案深度详细设计

命名体系与视觉识别方向

智脊 Spine（主轴）→ 智核 Cores（三处重点区）→ 智廊 Corridors（两翼联系）→ 智场 Arenas（场景节点）

主色：铁轨青铜绿 × 神经网络靛蓝；图形母题：人字形轨徽（致敬詹天佑人字形线路）


两翼协同回路：中关村科技服务翼（要素配置/IP/资本）×  
小月河场景赋能翼（场景/活力城市）——概念性协同，不新增红线

图例 Legend

智脊绿道主轴  
重点详细设计区（临时边界）  
总体设计范围（临时边界）

用地结构总图（概念性拓扑无缝分区·90 单元）

国土空间用地用海分类代码 | 与 geometry/land\_use.geojson 一致

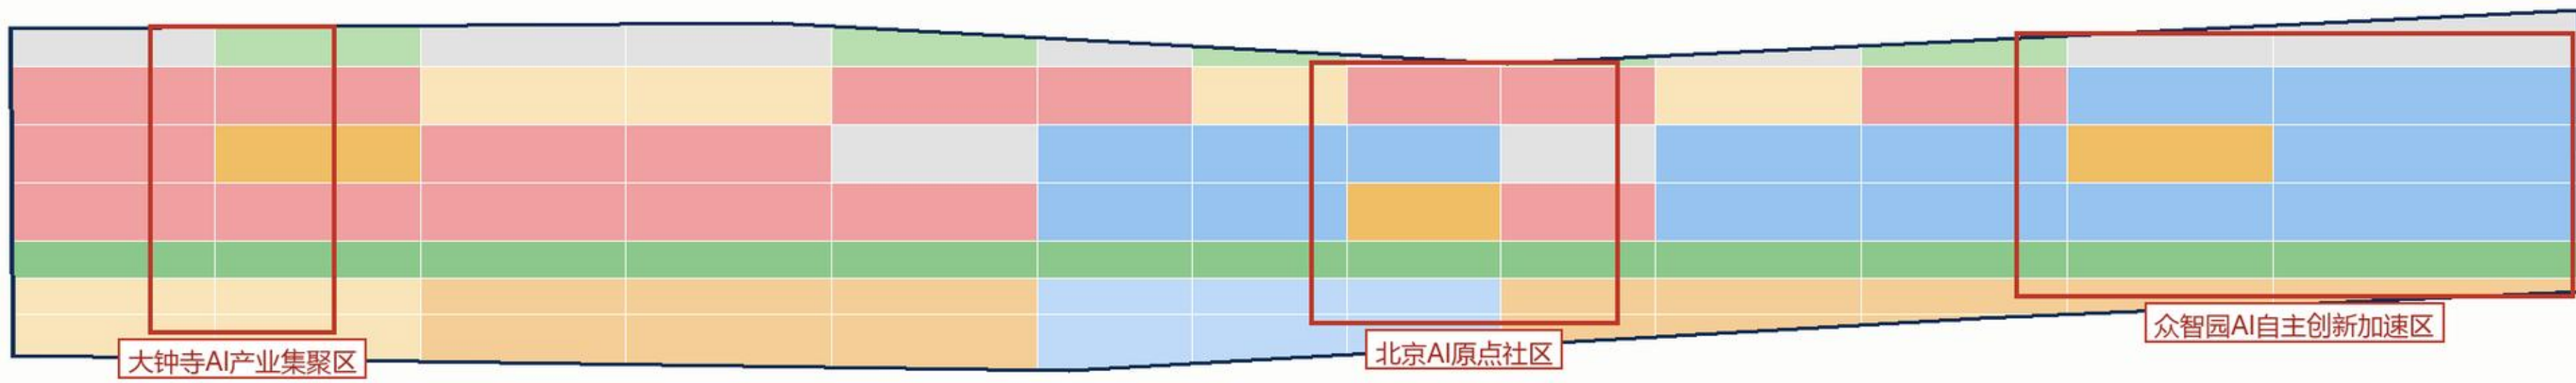

图例（面积 / 占比）

05 商业服务 · 256.3 ha · 22.5%

0802 科研 · 243.4 ha · 21.3%

0701 城镇住宅 · 142.6 ha · 12.5%

1401 公园绿地 · 133.5 ha · 11.7%

16 留白 · 114.0 ha · 10.0%

0702 社区服务 · 112.4 ha · 9.9%

0804 教育 · 54.9 ha · 4.8%

1403 广场 · 47.0 ha · 4.1%

1402 防护绿地 · 37.0 ha · 3.2%

相邻单元共享切割线坐标，union 等于提交边界；概念建议，待正式控规条件确认后复算。

资料来源：北京市规自委海淀分局征集公告（2026-05-09）与维护者临时边界（provisional constraint，非正式红线）；由 GeoJSON/指标复算生成（EPSG:4548）。

资料来源：北京市规自委海淀分局征集公告（2026-05-09）与维护者临时边界（provisional constraint，非正式红线）；由 GeoJSON/指标复算生成（EPSG:4548）。




意向效果图（AI生成，仅供参考）

意向效果图（AI生成，仅供参考）

核心指标复算与证据链

known 指标可由 geometry/geojson 在 EPSG:4548 下复算；unknown 指标待正式控规条件补齐

用地面积构成 (ha)

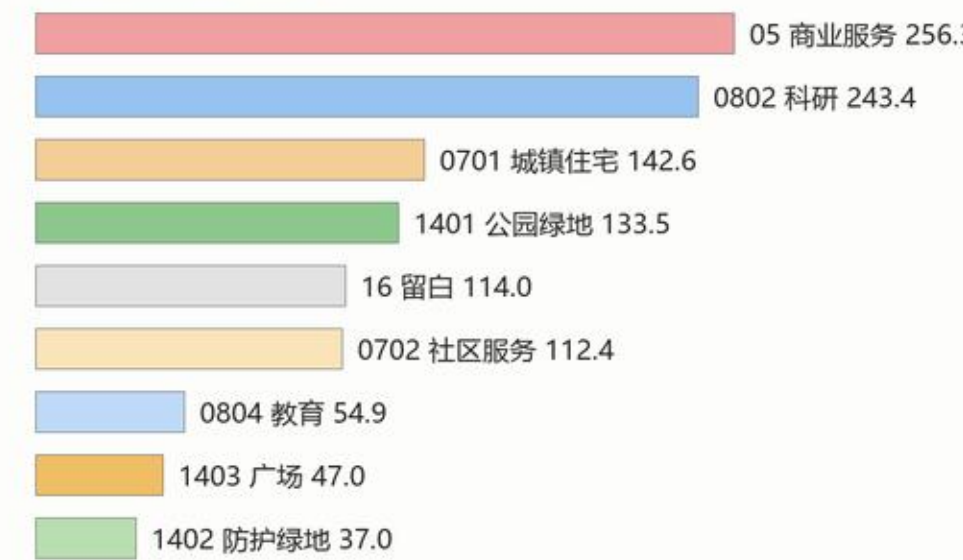

结构比例与概念分期

绿地率 14.9%

公共空间占比 7.5%

建筑密度(概念) 9.6%

概念分期面积 (ha)



证据链：指标 → 复算公式 → 来源文件 → 状态

|                             |                               |                                |         |
|-----------------------------|-------------------------------|--------------------------------|---------|
| site_area_sqm               | polygon_area(site_boundary)   | geometry/site_boundary.geojson | known   |
| green_ratio                 | green_space_area / site_area  | geometry/green_space.geojson   | known   |
| public_space_ratio          | public_space_area / site_area | geometry/public_space.geojson  | known   |
| building_footprint_area_sqm | sum(polygon_area(buildings))  | geometry/buildings.geojson     | known   |
| road_centerline_length_m    | sum(line_length(roads))       | geometry/roads.geojson         | known   |
| key_area_count              | count(key_areas)              | geometry/key_areas.geojson     | known   |
| floor_area_ratio            | unknown                       | 待正式控规条件                        | unknown |

|                                                |         |
|------------------------------------------------|---------|
| geometry/site_boundary.geojson                 | known   |
| geometry/green_space.geojson                   | known   |
| geometry/public_space.geojson                  | known   |
| geometry/buildings.geojson                     | known   |
| geometry/roads.geojson                         | known   |
| geometry/key_areas.geojson                     | known   |
| brief/site-package/ranges/planning_limits.json | unknown |

资料来源：北京市规自委海淀分局征集公告（2026-05-09）与维护者临时边界（provisional constraint，非正式红线）；由 GeoJSON/指标复算生成（EPSG:4548）。

总体概念：以京张遗址公园为历史与公共空间主轴，串联众智园、AI原点社区、大钟寺三处创新锚点，形成 ‘一脊三核两翼多点’ 的空间组织。用地为拓扑无缝概念分区（复算自 geometry/land\_use.geojson），全部指标可在 EPSG:4548 下复算。




三处重点区域详细设计索引

众智园 192.1 ha | 原点社区 104.3 ha | 大钟寺 72.0 ha（公告值；临时边界复算接近）

众智园AI自主创新加速区


花园型全栈自主创新街区

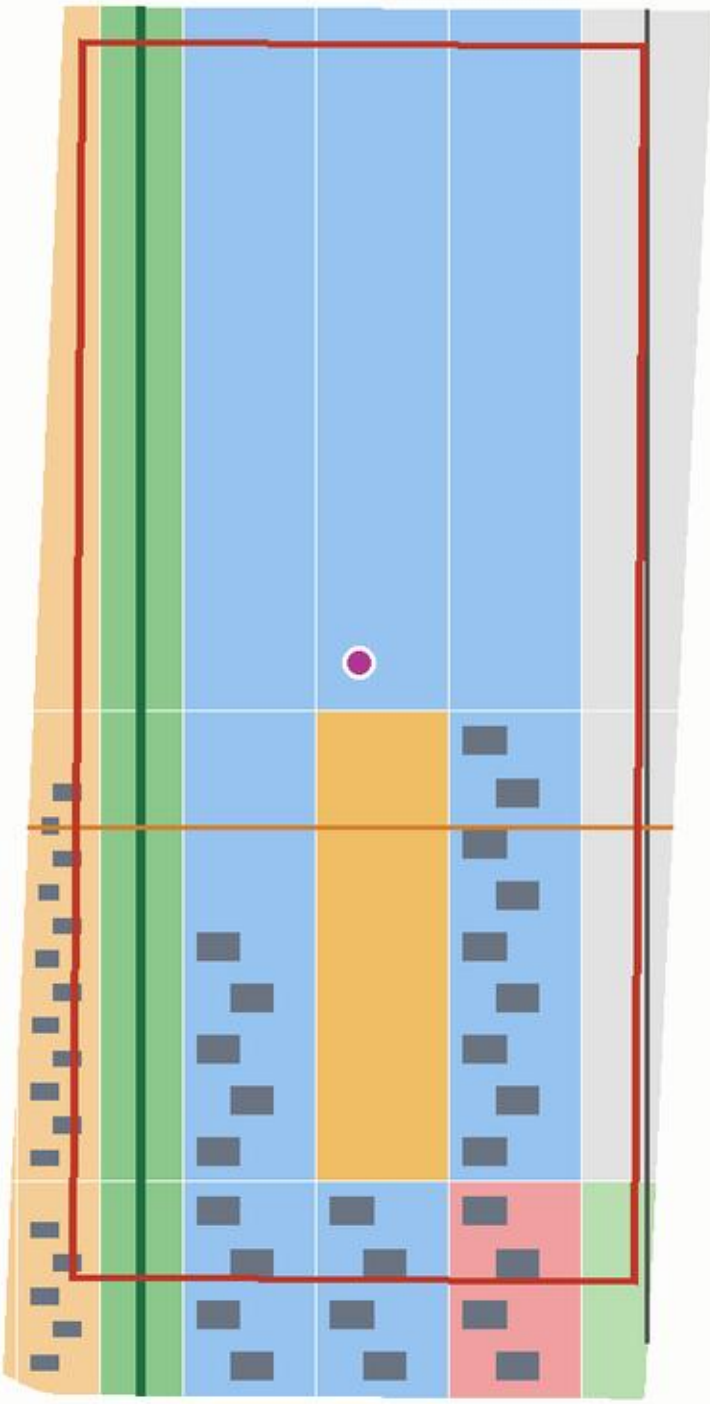

清河界面·众智广场（AI治理展示）·  
院落式研发单元·低碳开放测试场

北京AI原点社区


近校型成果转化与人才社区

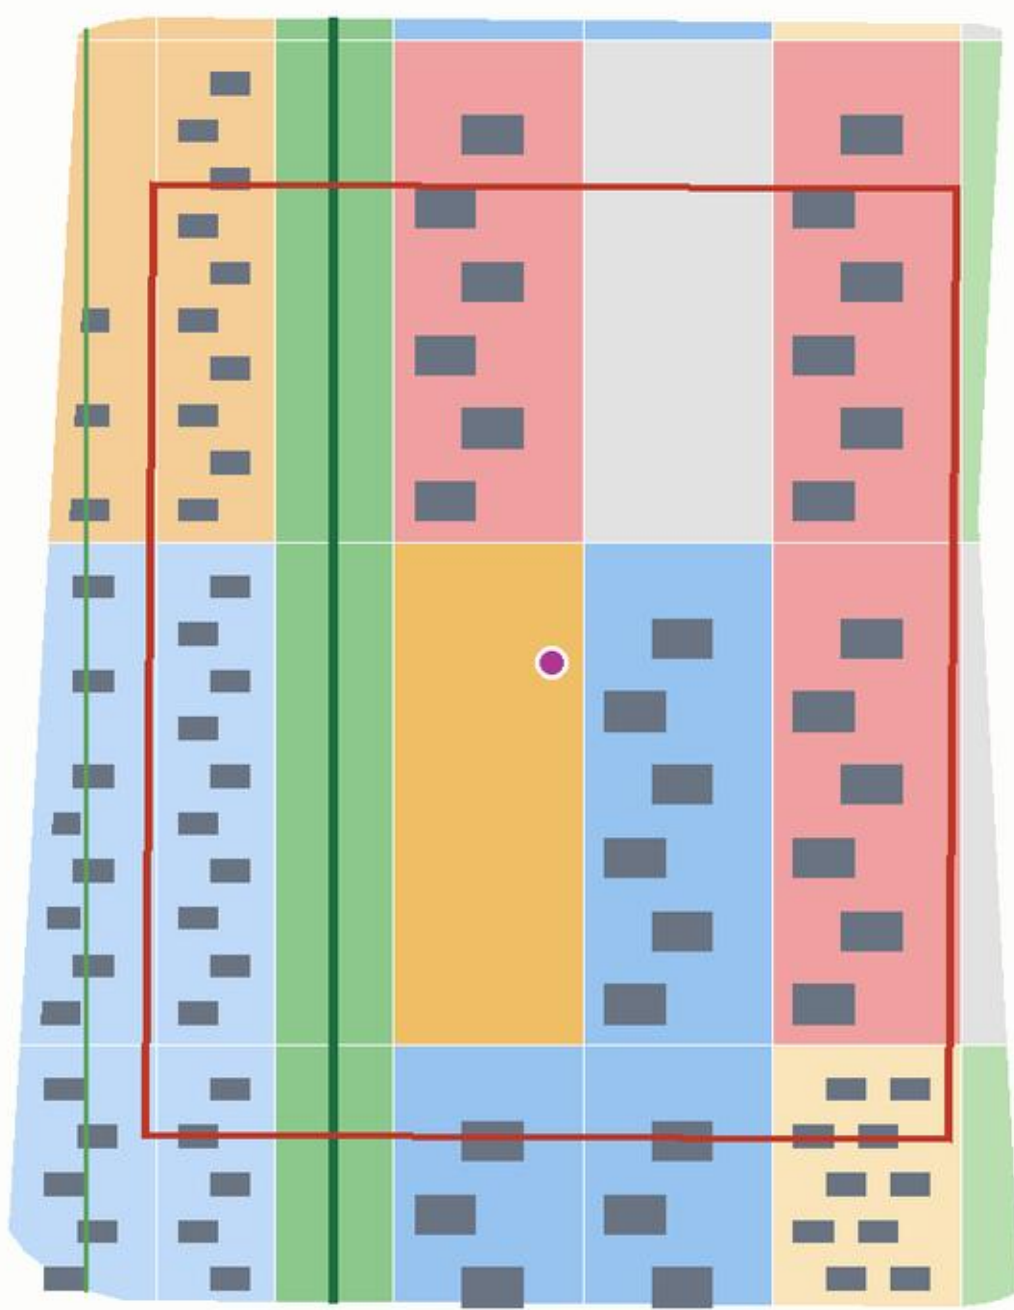

原点广场（开源发布）·校区-园区慢行缝合  
·成果转化街·人才服务

大钟寺AI产业集聚区

城市型智能经济与国际交往街区

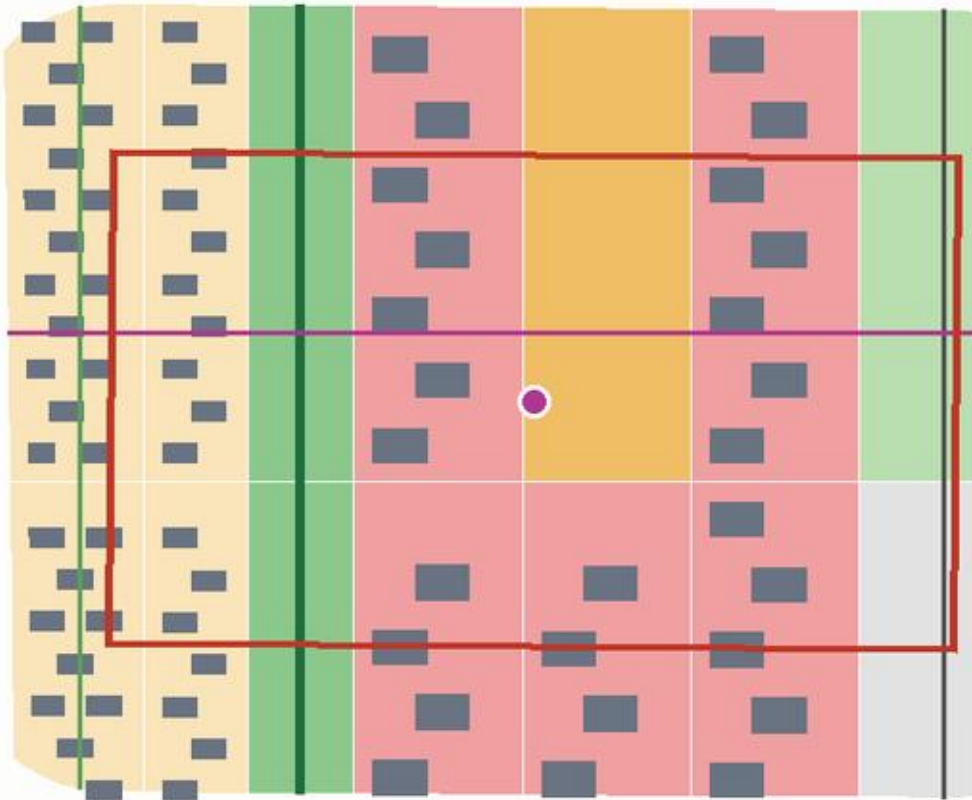


钟寺广场（国际路演）·站点一体化·  
四象限步行连通·数据要素会客厅

资料来源：北京市规自委海淀分局征集公告（2026-05-09）与维护者临时边界（provisional constraint，非正式红线）；由 GeoJSON/指标复算生成（EPSG:4548）。

交通慢行 × 蓝绿公共空间复合系统

一脊两环多联：遗址慢行主轴 + 东西翼循环 + 三处站点/片区缝合廊

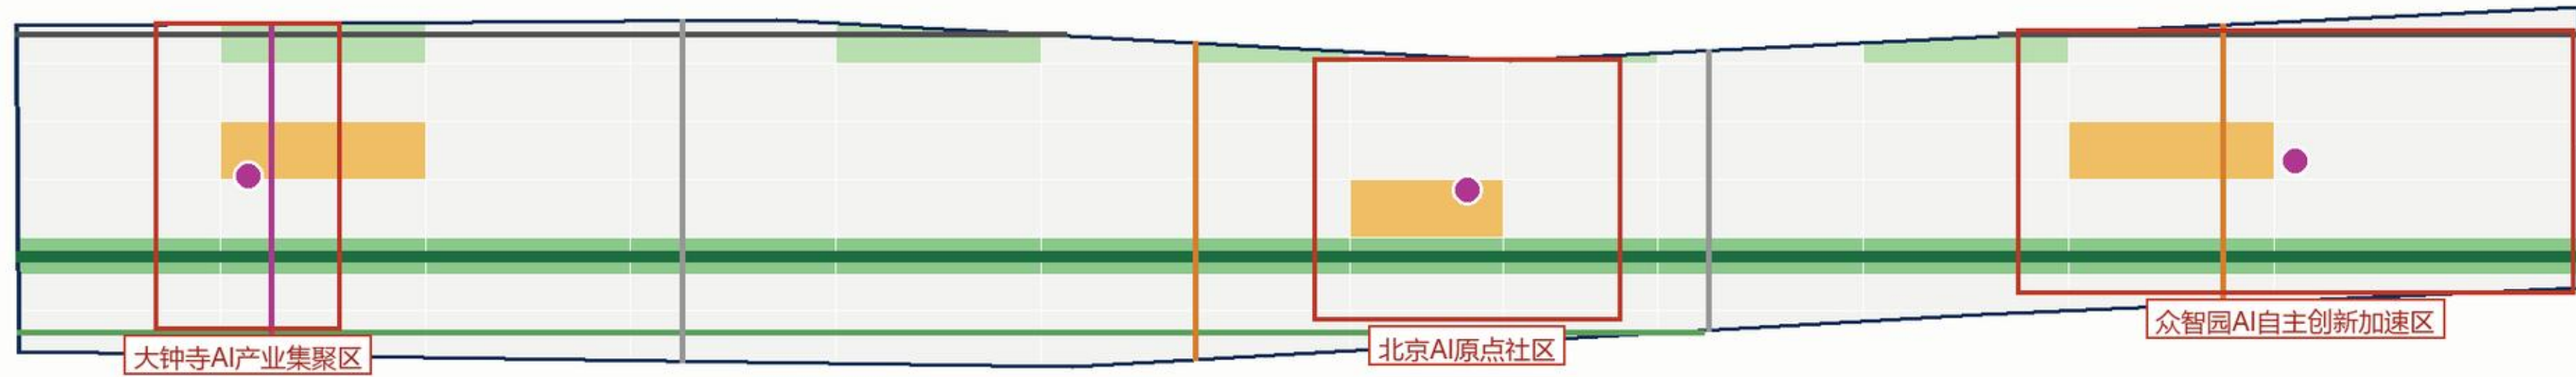

图例 Legend


智脊绿道主轴  
西翼骑行廊  
东翼次干路  
微循环支路

步行缝合廊  
轨道接驳  
公园绿地  
防护绿带

广场/公共节点  
站点/片区节点

慢行/道路中心线总长 28.2 km  
绿地率 14.9%  
公共空间占比 7.5%  
全部道路为概念中心线，不涉及红线判断

资料来源：北京市规自委海淀分局征集公告（2026-05-09）与维护者临时边界（provisional constraint，非正式红线）；由 GeoJSON/指标复算生成（EPSG:4548）。

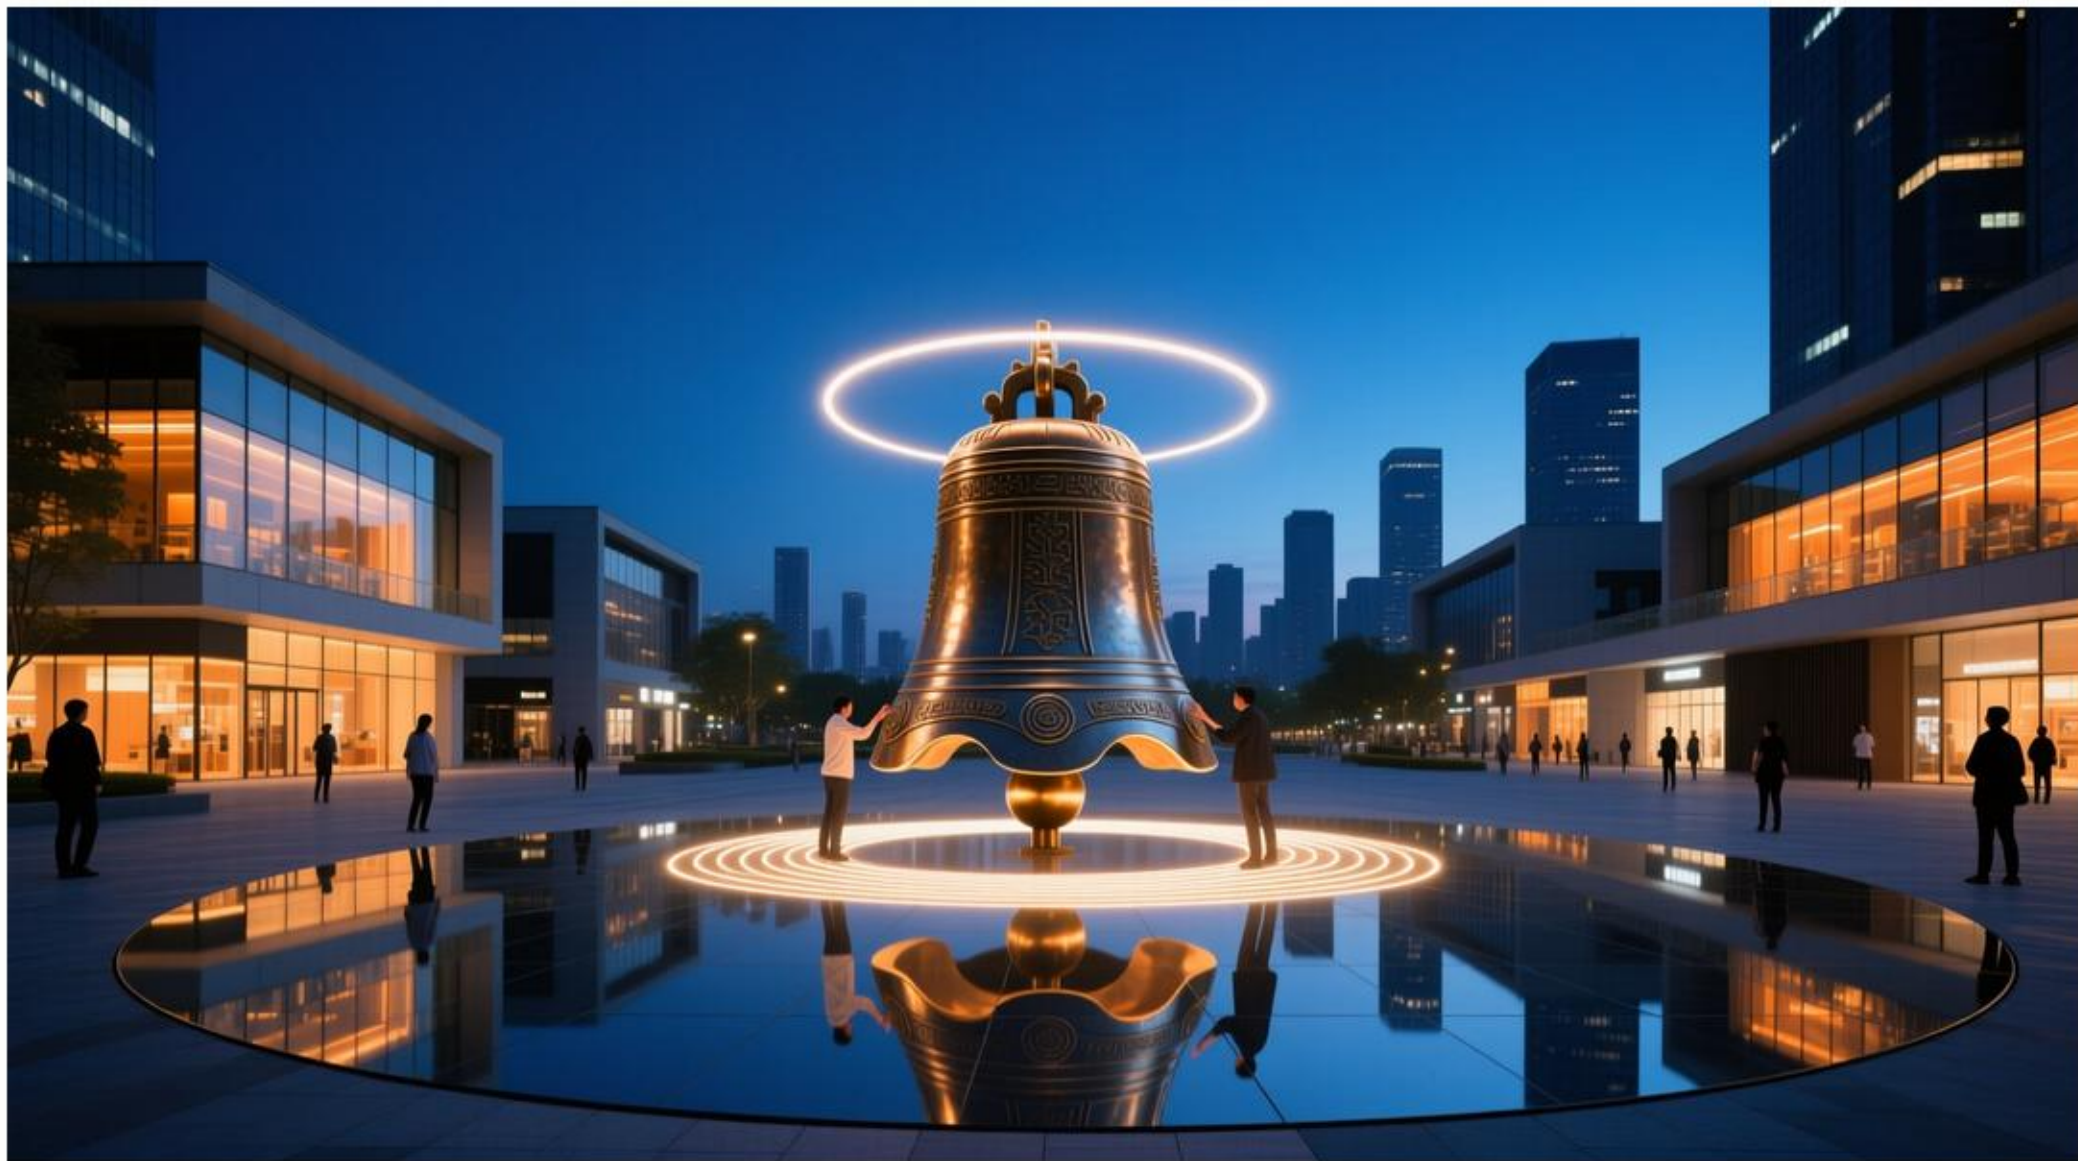

AI 场景卡 Scenario Cards

01 开源发布厅

北京AI原点社区 | 高校/开源社区/初创的成果发布与小型路演；不采集个  
人行轨迹

04 AI慢行导航

京张遗址公园活力带 | 可解释导视与低侵入传感识别慢行断点

07 近校成果转化街

原点社区 | 孵化、法务、知识产权与投融资服务街

10 全球AI活动周路线

一带公共空间 | 遗址文化-开源社区-产业展示-国际路演步行路线

02 安全治理沙盒

众智园 | 标准制定、安全评测、模型红队测试的可参观协作节点

05 国际路演客厅

大钟寺 | 智能体/智能终端/内容消费企业的展示与国际交流

08 数据要素会客厅

大钟寺 | 合规授权可审计的数据要素流通城市界面

11 遗址公园夜光跑道

遗址公园 | 夜间活力与安全照明分级管理的运动场景

03 端侧算力驿站

总体范围节点 | 与公共服务和低碳能源结合的新型基础设施原型

06 清河低碳创新廊

众智园临清河界面 | 绿色空间、雨洪、骑行与AI展示复合

09 AI生活服务样板街

社区商业交汇处 | 医疗教育法律生活服务的AI+小尺度样板

12 无障碍AI导览

全带 | 多语种无障碍导览，保留人工服务兜底（无障碍环境建设法第39条边  
界）