


总体区位与双轨骨架 · 百年京张 AI 创新带

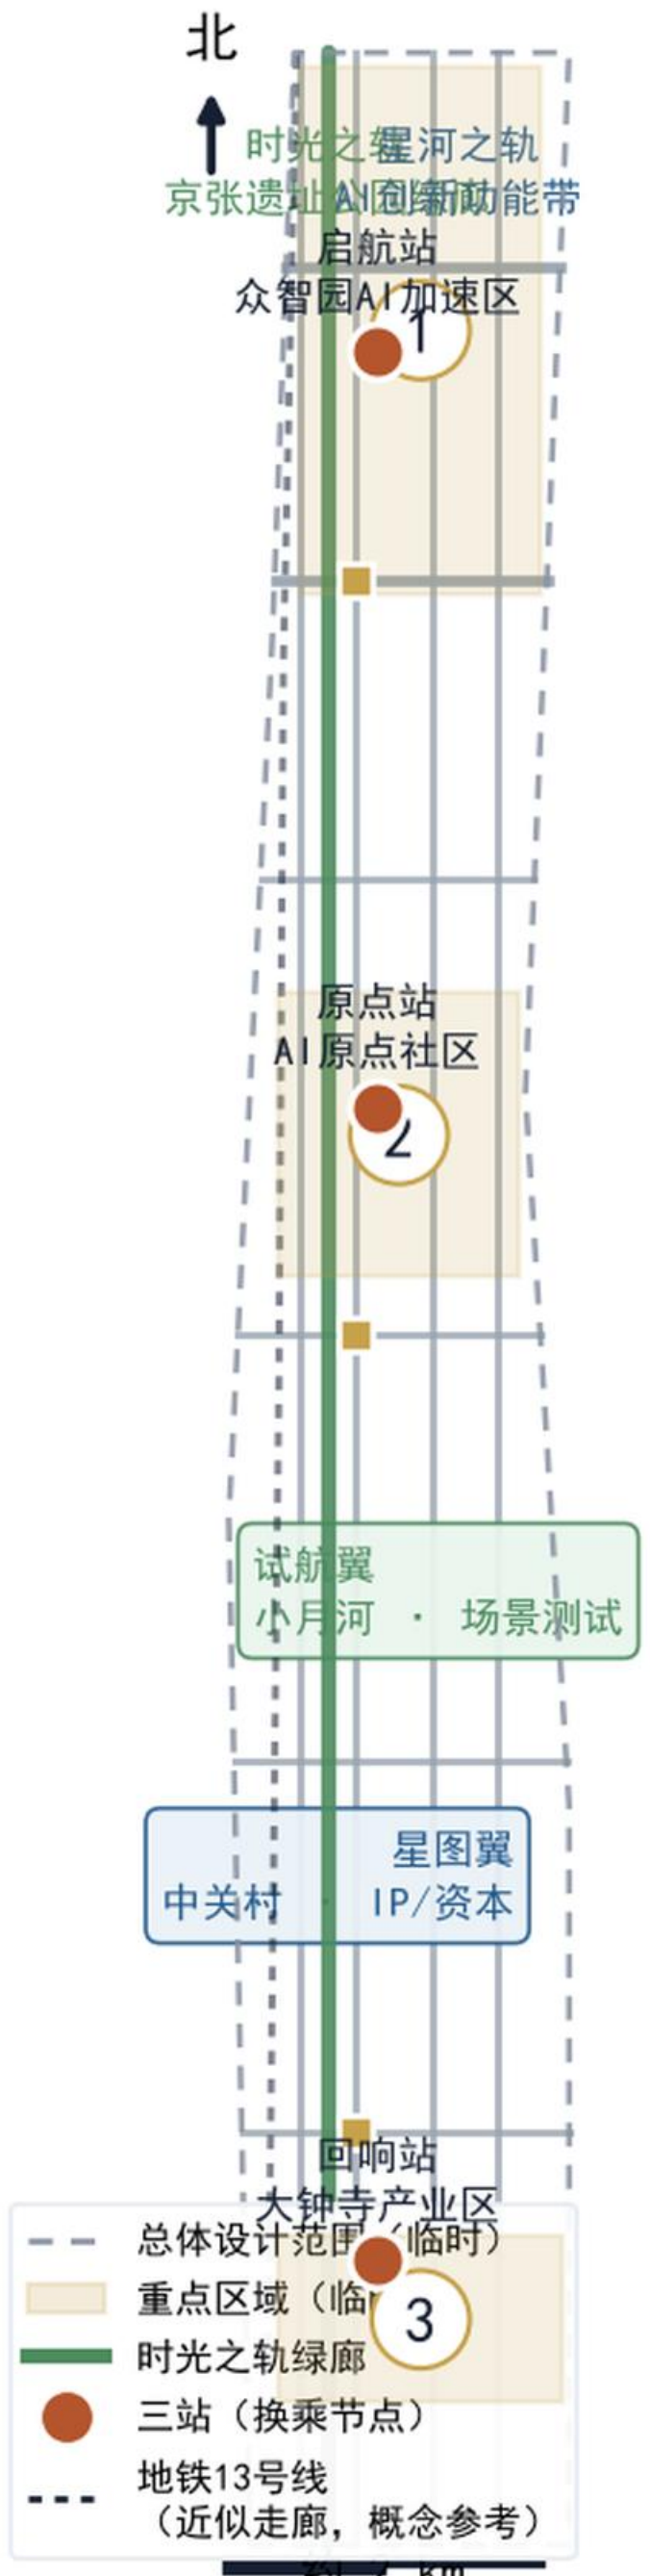

换乘节点

注意：边界为临时约束范围（provisional constraint），非官方红线；官方边界发布后复算。

来源：provisional site boundary + key areas（仓库临时几何）、open-city-ai/haidian 公开任务书与公开报道。

双轨 · 京张

时光之轨 × 星河之轨 · 从 0 到 1，回声无穷



0 → 1 → ∞

自众智启航，回大学原点，成全球回响

启航站（研发）→ 原点站（转化）→ 回响站（落地）

→ 试航翼（验证）→ 星图翼（资本/IP 指引）→ 反馈研发

与海淀分区规划「两心聚一核」同构：时光之轨承三山五园文化绿心，星河之轨承中关村科学城科技智芯；呼应「智慧平行城市」与9公里京张遗址公园（2026-08 二期竣工）、地铁 13/12 号线换乘枢纽。

双轨：时光之轨（京张遗址公园文化慢行主轴）× 星河之轨（AI创新功能带）。

三站：启航站（研发）→ 原点站（转化）→ 回响站（落地）；

两翼：星图翼（IP/资本）· 试航翼（场景测试）；交汇：换乘节点。

命名明线当代、暗线历史：启碇/津梁/觉生/司南/道生为文化注脚。

与海淀分区规划「两心聚一核」同构；呼应9公里京张遗址公园与13/12号线换乘。

Logo方向：双轨之间嵌入「人」字折线，圆形换乘符号收束；



色彩：锈红（铁路之史）· 墨色（大地铁轨）· 星蓝（AI之光）。

品牌：京张双轨节 Twin Tracks Festival（概念）。

用地结构：中央绿廊（1401 约17.0%）、西翼社区（0701/0702）、中轴创新（0802/0804/05/0803）、东翼服务、道路 1207 约22.8%。建筑基底约222.8万㎡（密度约19.5%）；小街区密路网复合底商。拆改留：保留/织补/嵌入/腾退置换四类概念分类。

待正式数据补齐：控规容积率、建筑高度、建筑密度、绿地率、权属与拆改信息；官方边界发布后全量复算。


用地结构：三站两翼与双轨走廊

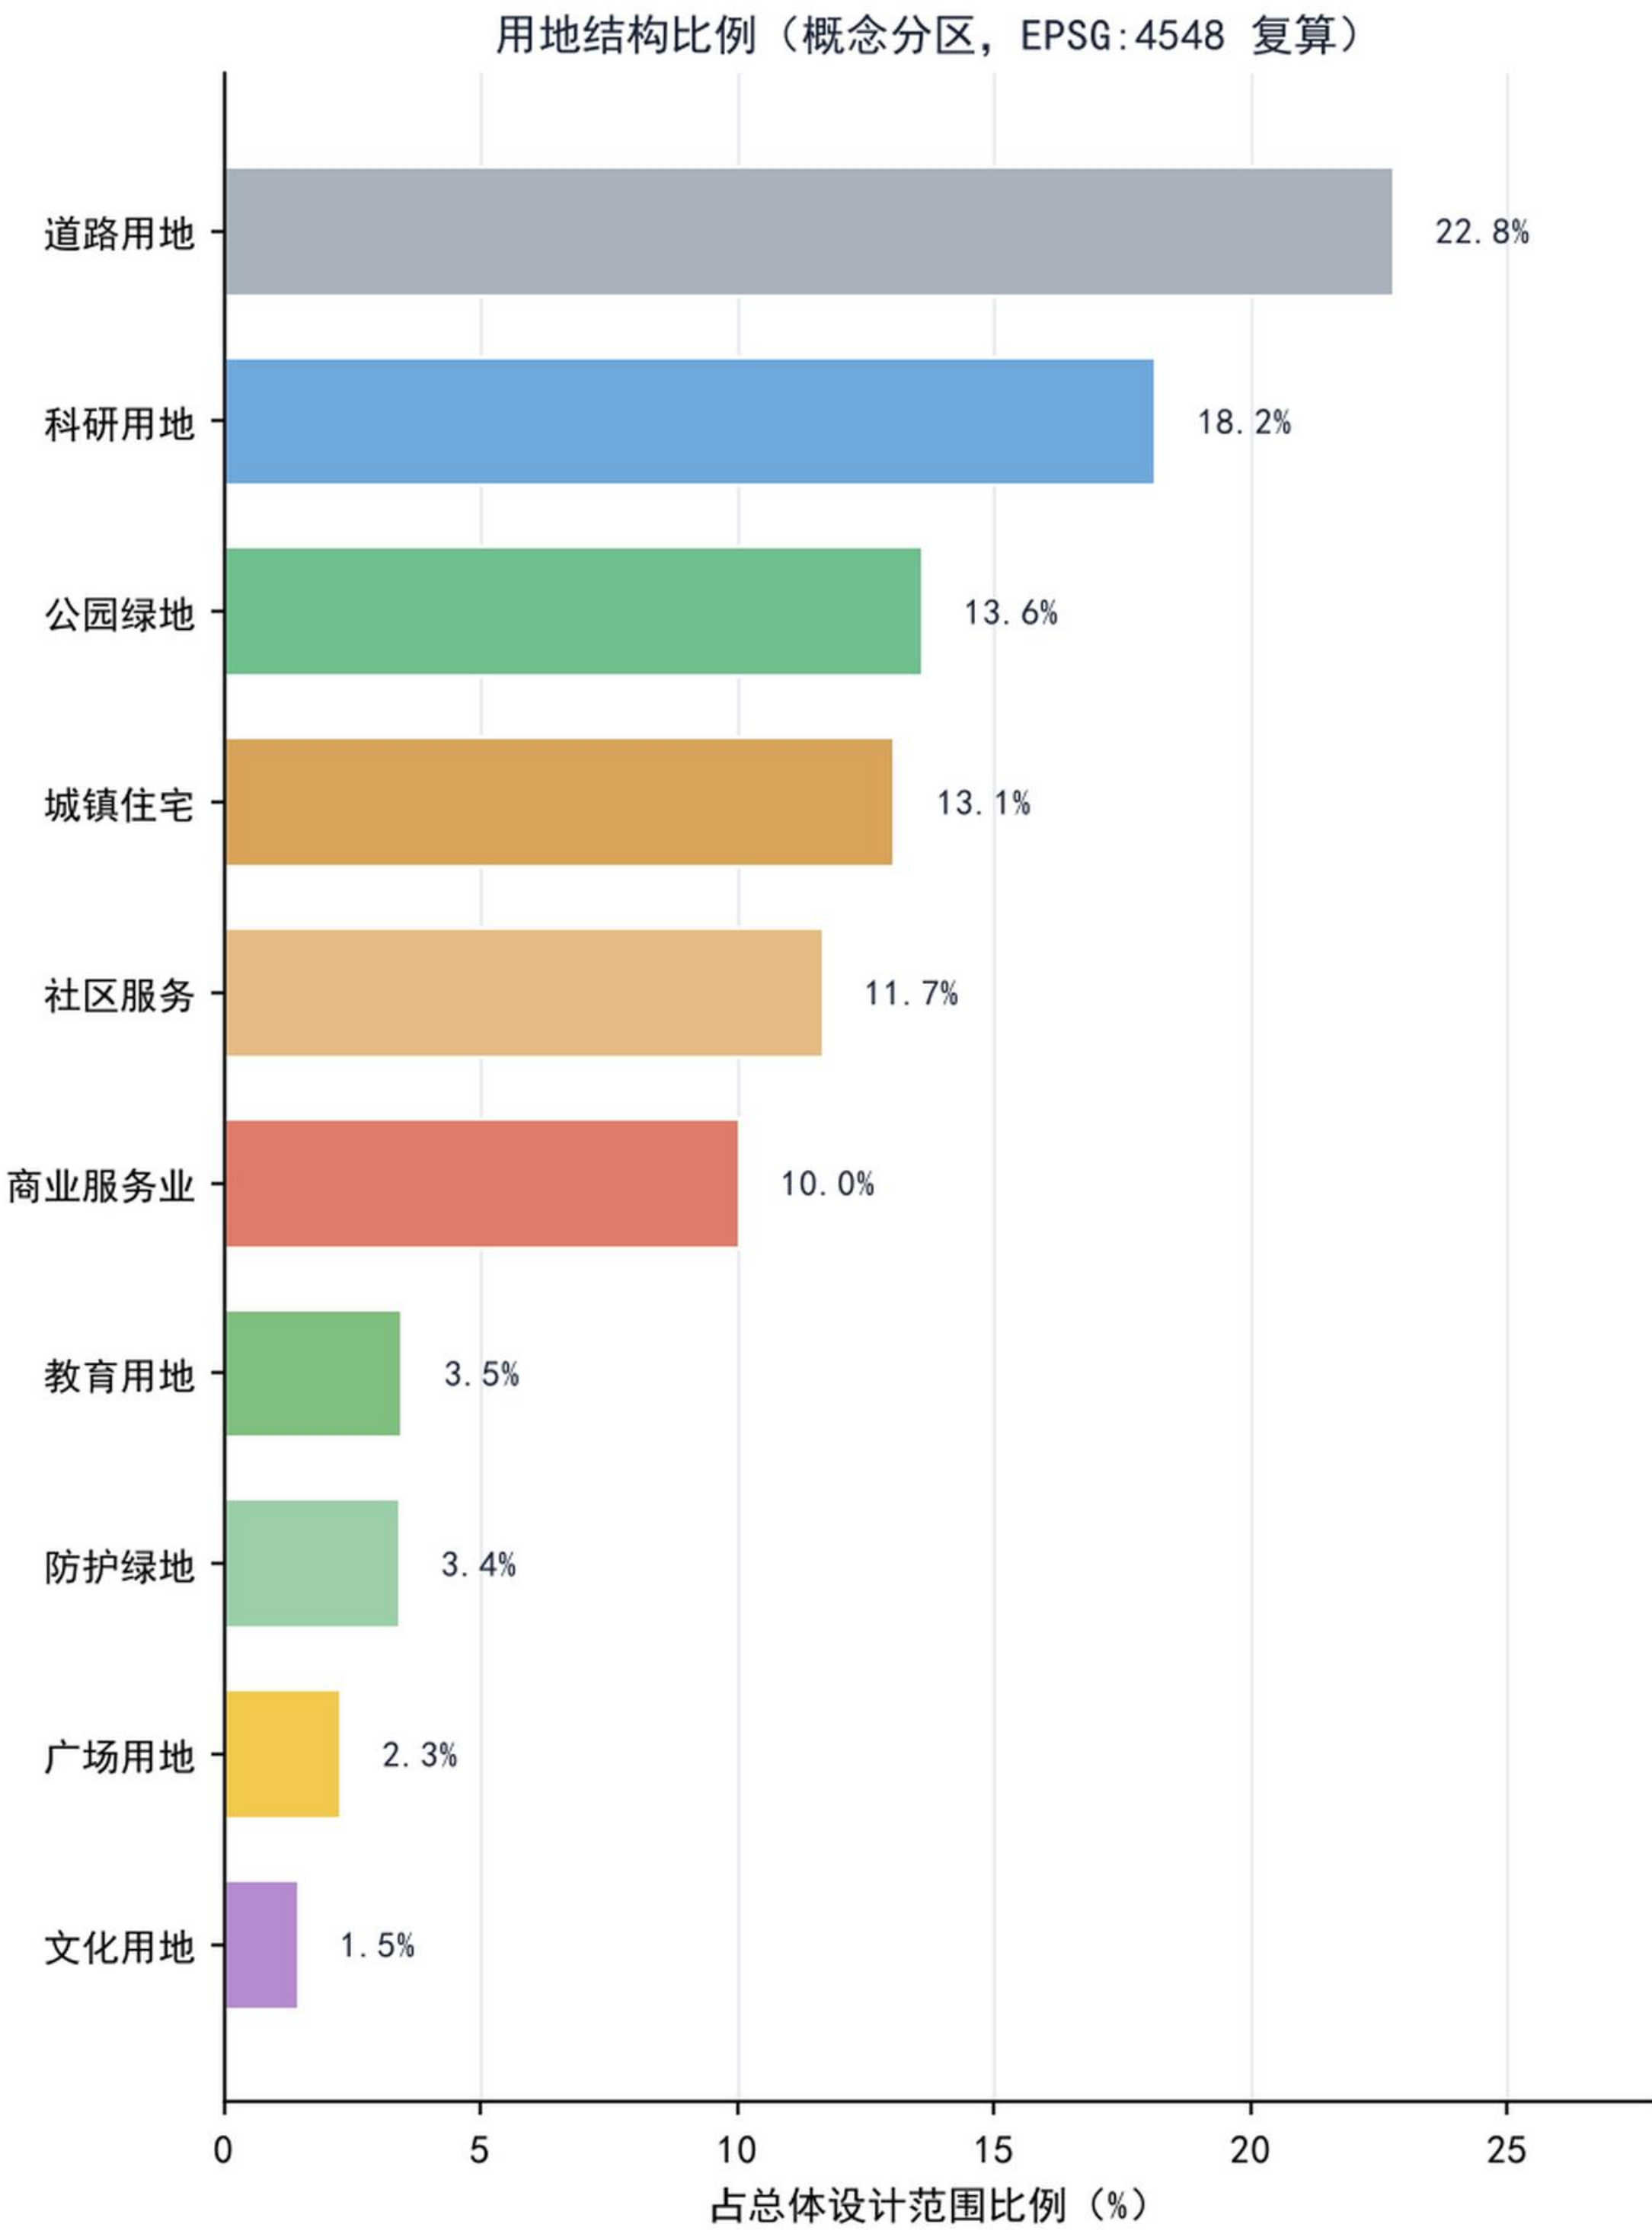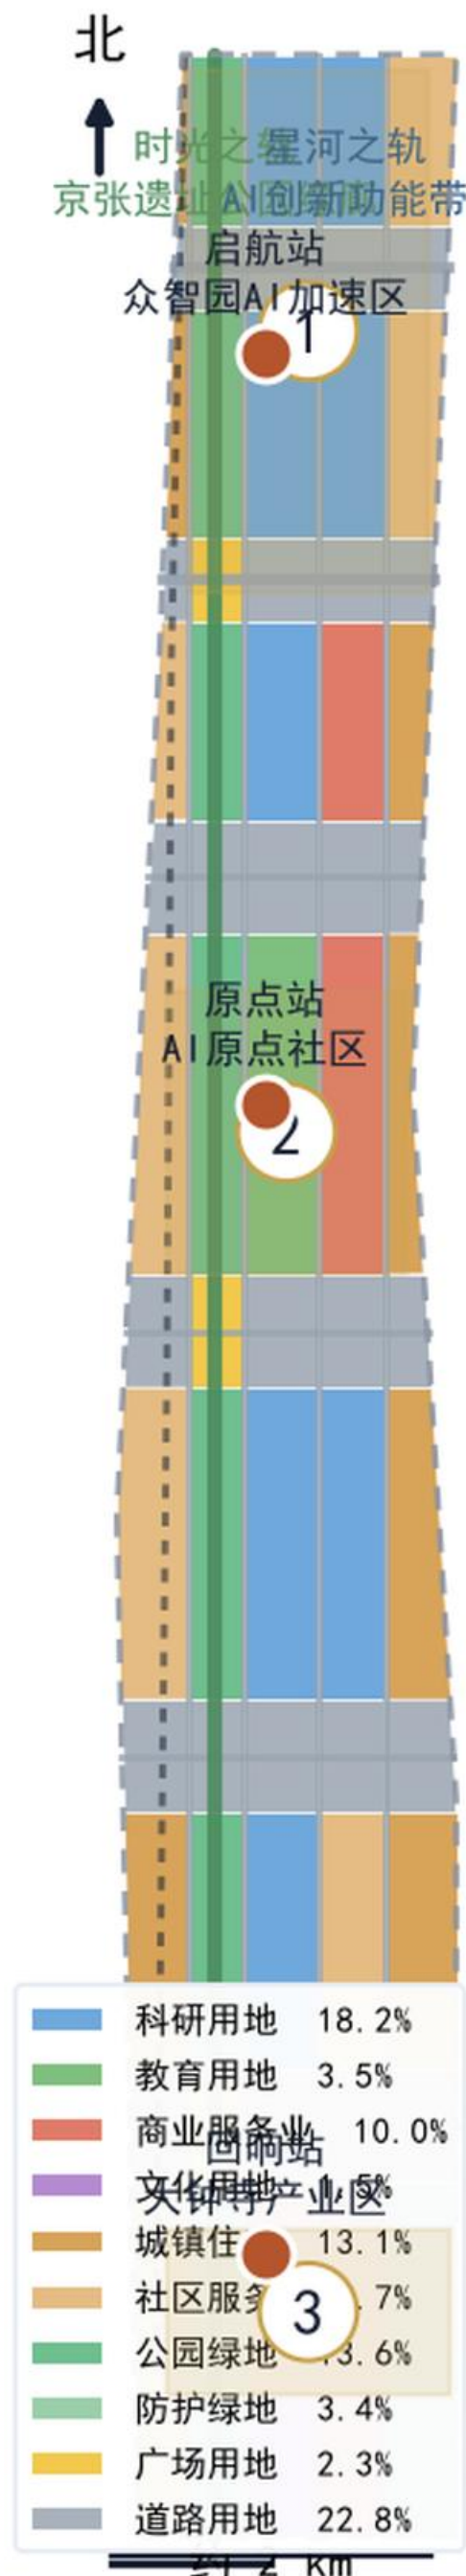

三站两翼，启航站（0802 全栈研发）→ 原点站（0804 源头教育、05 转化服务）→ 众智园AI加速区（0803 场景测试）；中轴创新（0802/0804/05/0803）、东翼服务、道路 1207 约22.8%。建筑基底约222.8万㎡（密度约19.5%）；小街区密路网复合底商。拆改留：保留/织补/嵌入/腾退置换四类概念分类。

注意：全部边界为临时约束范围（provisional constraint）；本方案为概念建议，不构成法定规划结论。

三大重点区域详细设计索引

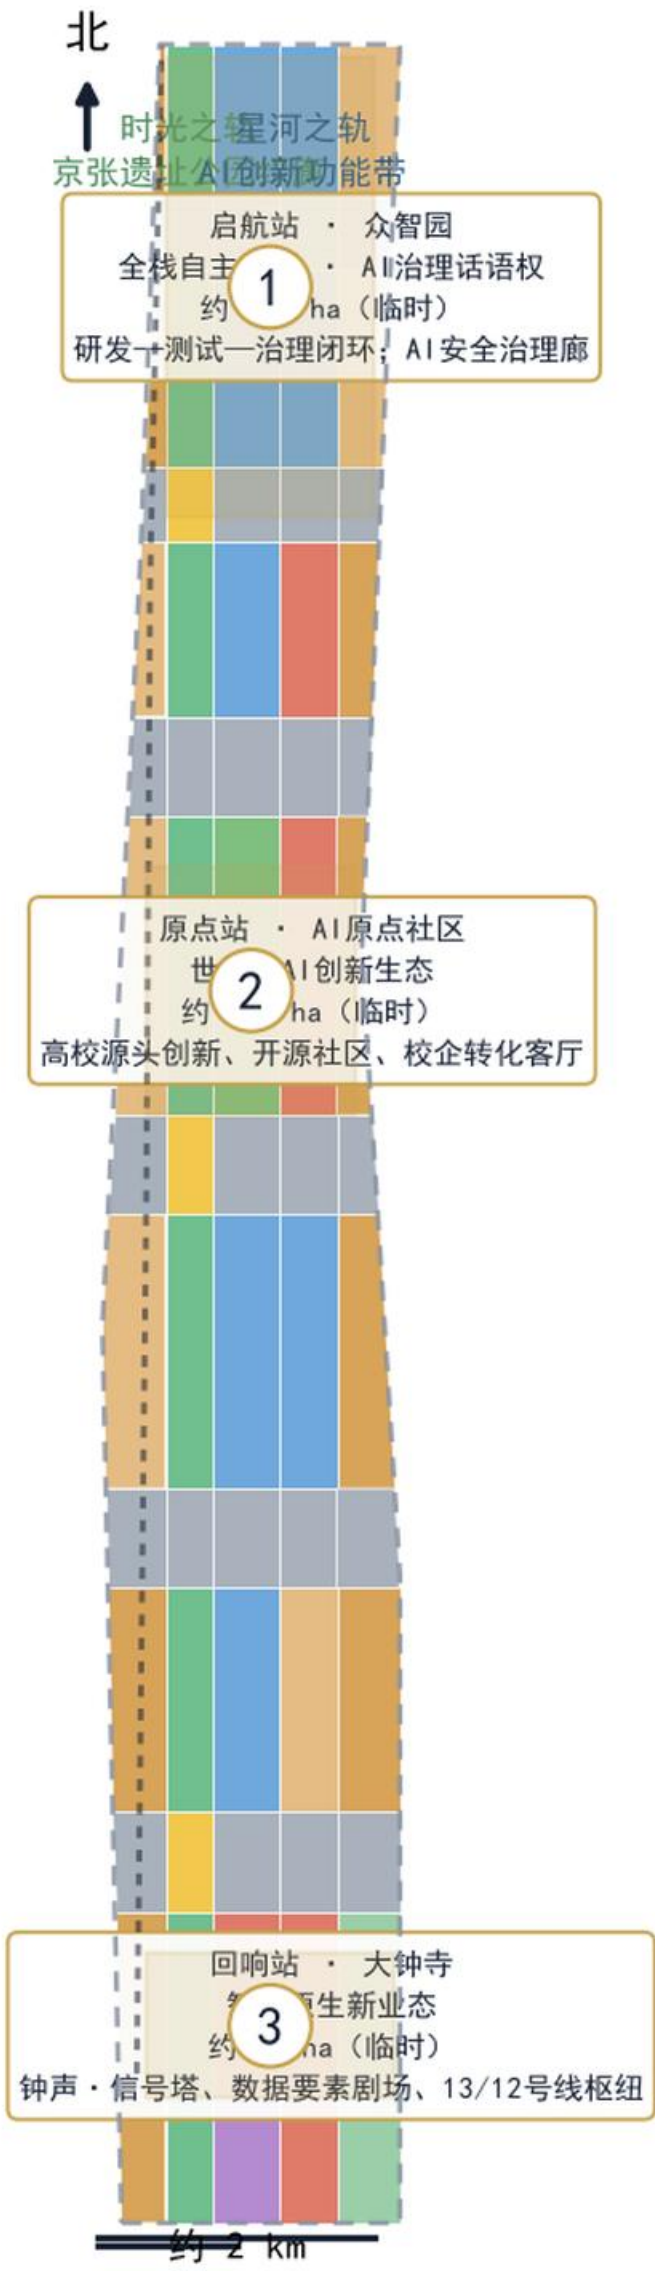

1 启航站 · 众智园

全栈自主创新 · AI治理话语权

面积：193 ha（临时复算） / 公告约 192.1 ha

研发—测试—治理闭环；AI安全治理廊

2 原点站 · AI原点社区

世界级AI创新生态

面积：104 ha（临时复算） / 公告约 104.3 ha

高校源头创新、开源社区、校企转化客厅

3 回响站 · 大钟寺

智能原生新业态


面积：72 ha（临时复算） / 公告约 72.0 ha

钟声 · 信号塔、数据要素剧场、13/12号线枢纽

三个重点区均为临时约束范围（provisional constraint），仅作方向性设计；
官方 KEY_AREA 多边形发布后需重算面积并替换详细设计范围。

来源：provisional site boundary + key areas（仓库临时几何）、open-city-ai/haidian 公开任务书与公开报道。

交通慢行与蓝绿公共空间复合系统

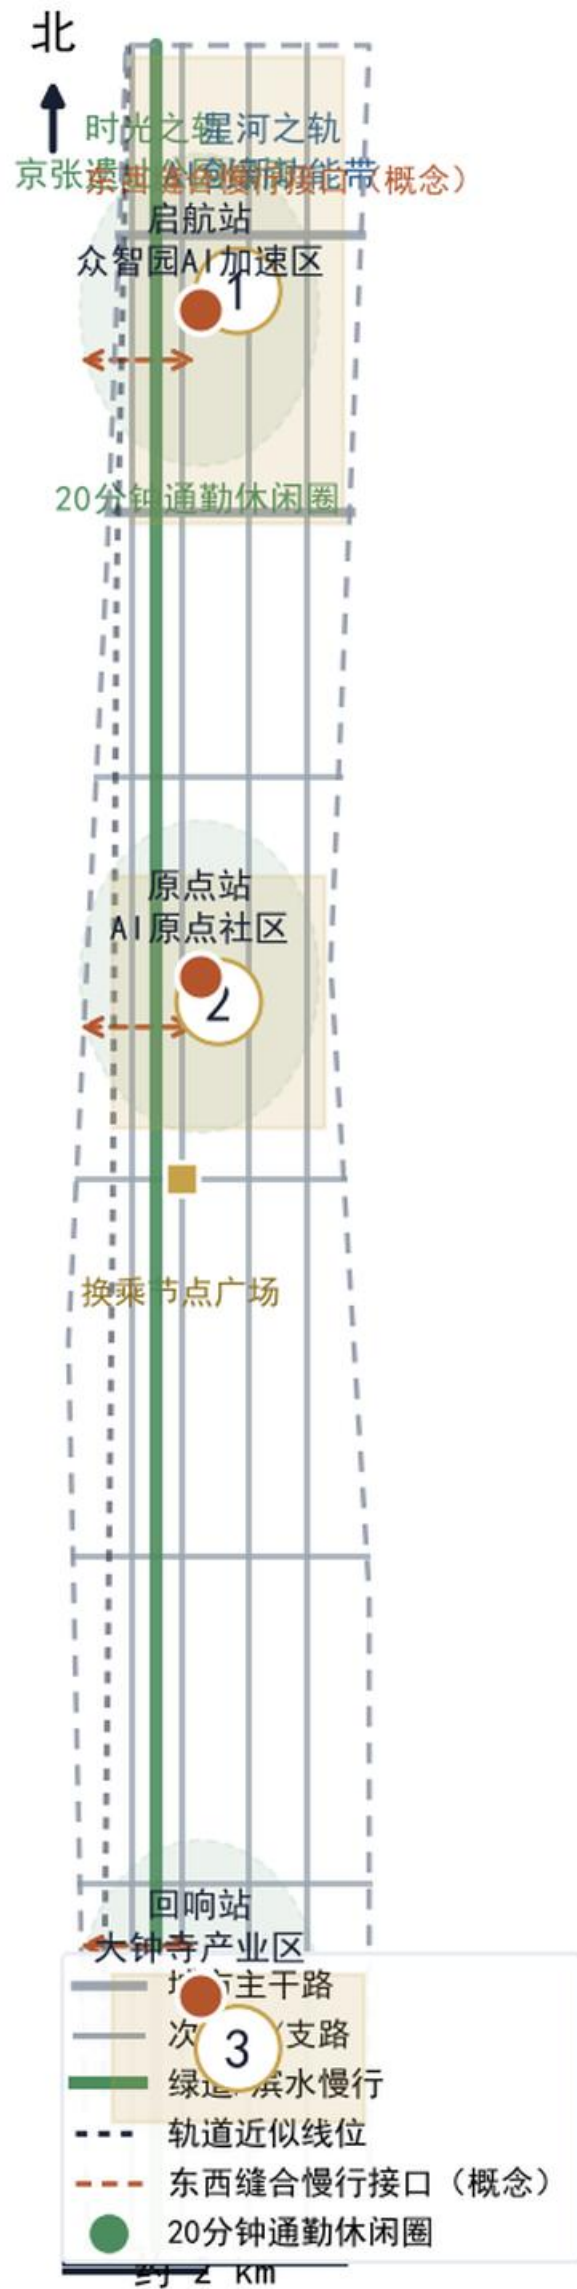

南北贯通

时光之轨绿道串联三站；星河之轨以研发—转化—落地分段组织功能连续性

东西缝合

沿公园设置跨轨慢行接口与「缝线」公共空间，缝合高校产业与西侧社区（概念建议）

轨道接驳

回响站利用大钟寺 13/12 号线换乘枢纽；原点站衔接五道口/清华东路轨道站点

慢行断点

城市智能体沙盒与「慢行断点诊断」场景用于识别步行骑行断点，需人工复核


蓝绿系统

京张绿廊 + 小月河蓝带 + 三道一绿慢行系统；换乘节点广场兼作活动与展示场

注意：边界为临时约束范围（provisional constraint），非官方红线；官方边界发布后复算。

来源：provisional site boundary + key areas（仓库临时几何）、open-city-ai/haidian 公开任务书与公开报道。

核心指标复算与证据链

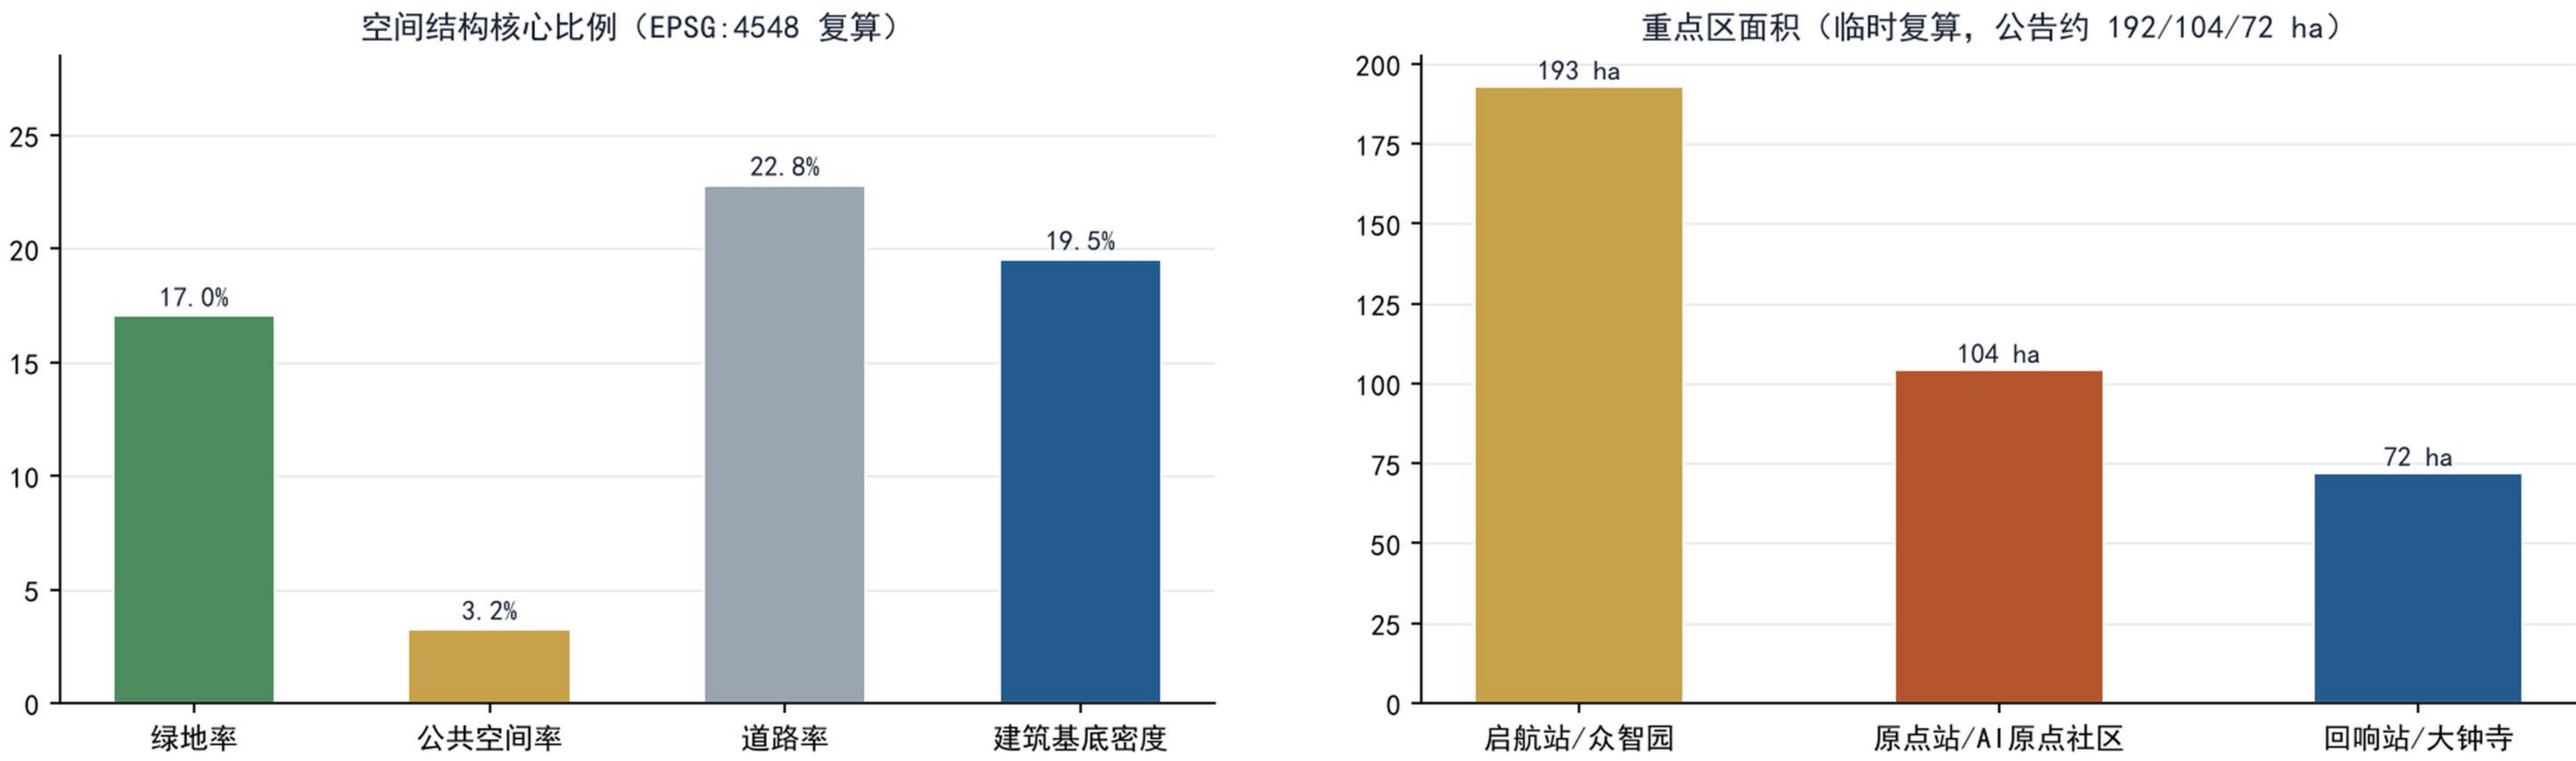

分期：一期启航站·众智园与北段绿廊（近期）；
二期原点站·AI原点社区与中段（中期）；
三期回响站·大钟寺与南段（远期）。
更新项目：绿廊激活、站城一体、社区织补、数字叠加四类。


运营：京张双轨节（开发者周/场景开放日/开源发布/国际共创营）；
开发者社区「贡献→展示→荣誉」闭环；沙盒按季度开放+人工复核。
指标：11,412,825m²（临时边界），绿地率17.0%，公共空间率3.2%。

指标	复算值	公式	置信度
site_area_sqm	11,412,825 m2	<code>polygon_area(site_boundary, EPSG:4548)</code>	medium
green_ratio	17.0%	<code>green_area / site_area</code>	medium
public_space_ratio	3.2%	<code>public_area / site_area</code>	medium
building_density	19.5%	<code>footprint / site_area</code>	medium
floor_area_ratio	待正式控规条件	<code>total_floor_area / site_area</code>	unknown

证据链：geometry/* .geojson → EPSG:4548 投影复算 → metrics.json → 本图与 visual/index.html。
总面积、容积率、建筑高度等法定指标缺官方控规条件，一律标注「待正式数据补齐」，不编造。

来源：provisional site boundary + key areas（仓库临时几何）、open-city-ai/haidian 公开任务书与公开报道。

交通慢行与蓝绿公共空间复合系统

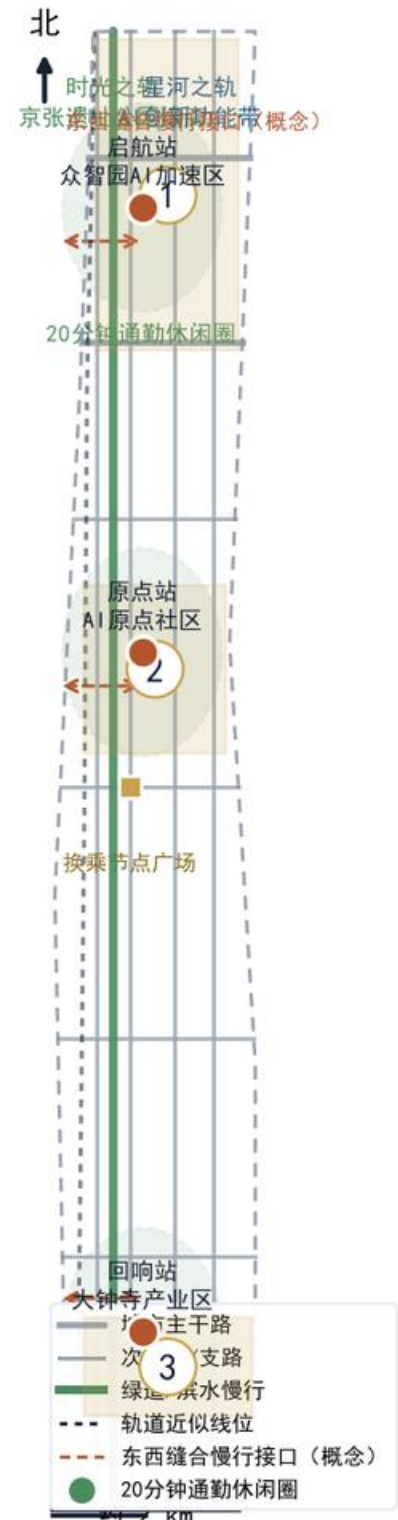

南北贯通
时光之轨绿道串联三站；蓝带之轨以研发—转化—落地分段组织功能连续性
东西缝合
沿公园设置跨轨慢行接口与「缝合」公共空间，缝合高校产业与西侧社区（概念建议）
轨道接驳
回响站利用大钟寺 13/12 号线换乘枢纽；原点站衔接五道口/清华东路轨道站点
慢行断点
城市智能体沙盒与「慢行断点诊断」场景用于识别步行骑行断点，需人工复核
蓝绿系统
京张绿廊 + 小月河蓝带 + 三道一绿慢行系统；换乘节点广场展作活动与展示场

注意：边界为临时约束范围（provisional constraint），非官方红线；官方边界发布后复算。
来源：provisional site boundary + key areas（仓库临时几何）、open-city-ai/haidian 公开任务书与公开报道。