


AI Life • AI Creation • AI Axis — Centennial Jing-Zhang AI Innovation Belt — Concept Plan

01 Design concept & overall structure

The Jing-Zhang railway heritage green spine works as the north-south AI axis, chaining three themed districts: AI Creation (Zhongzhiyuan), AI Axis (AI Origin Community), AI Life (Dazhongsi), with two wings linking campus innovation and legacy retail upgrades.

总览：AI生活•AI创造•AI极轴 空间结构 | Overall structure: AI Life • AI Creation • AI Axis

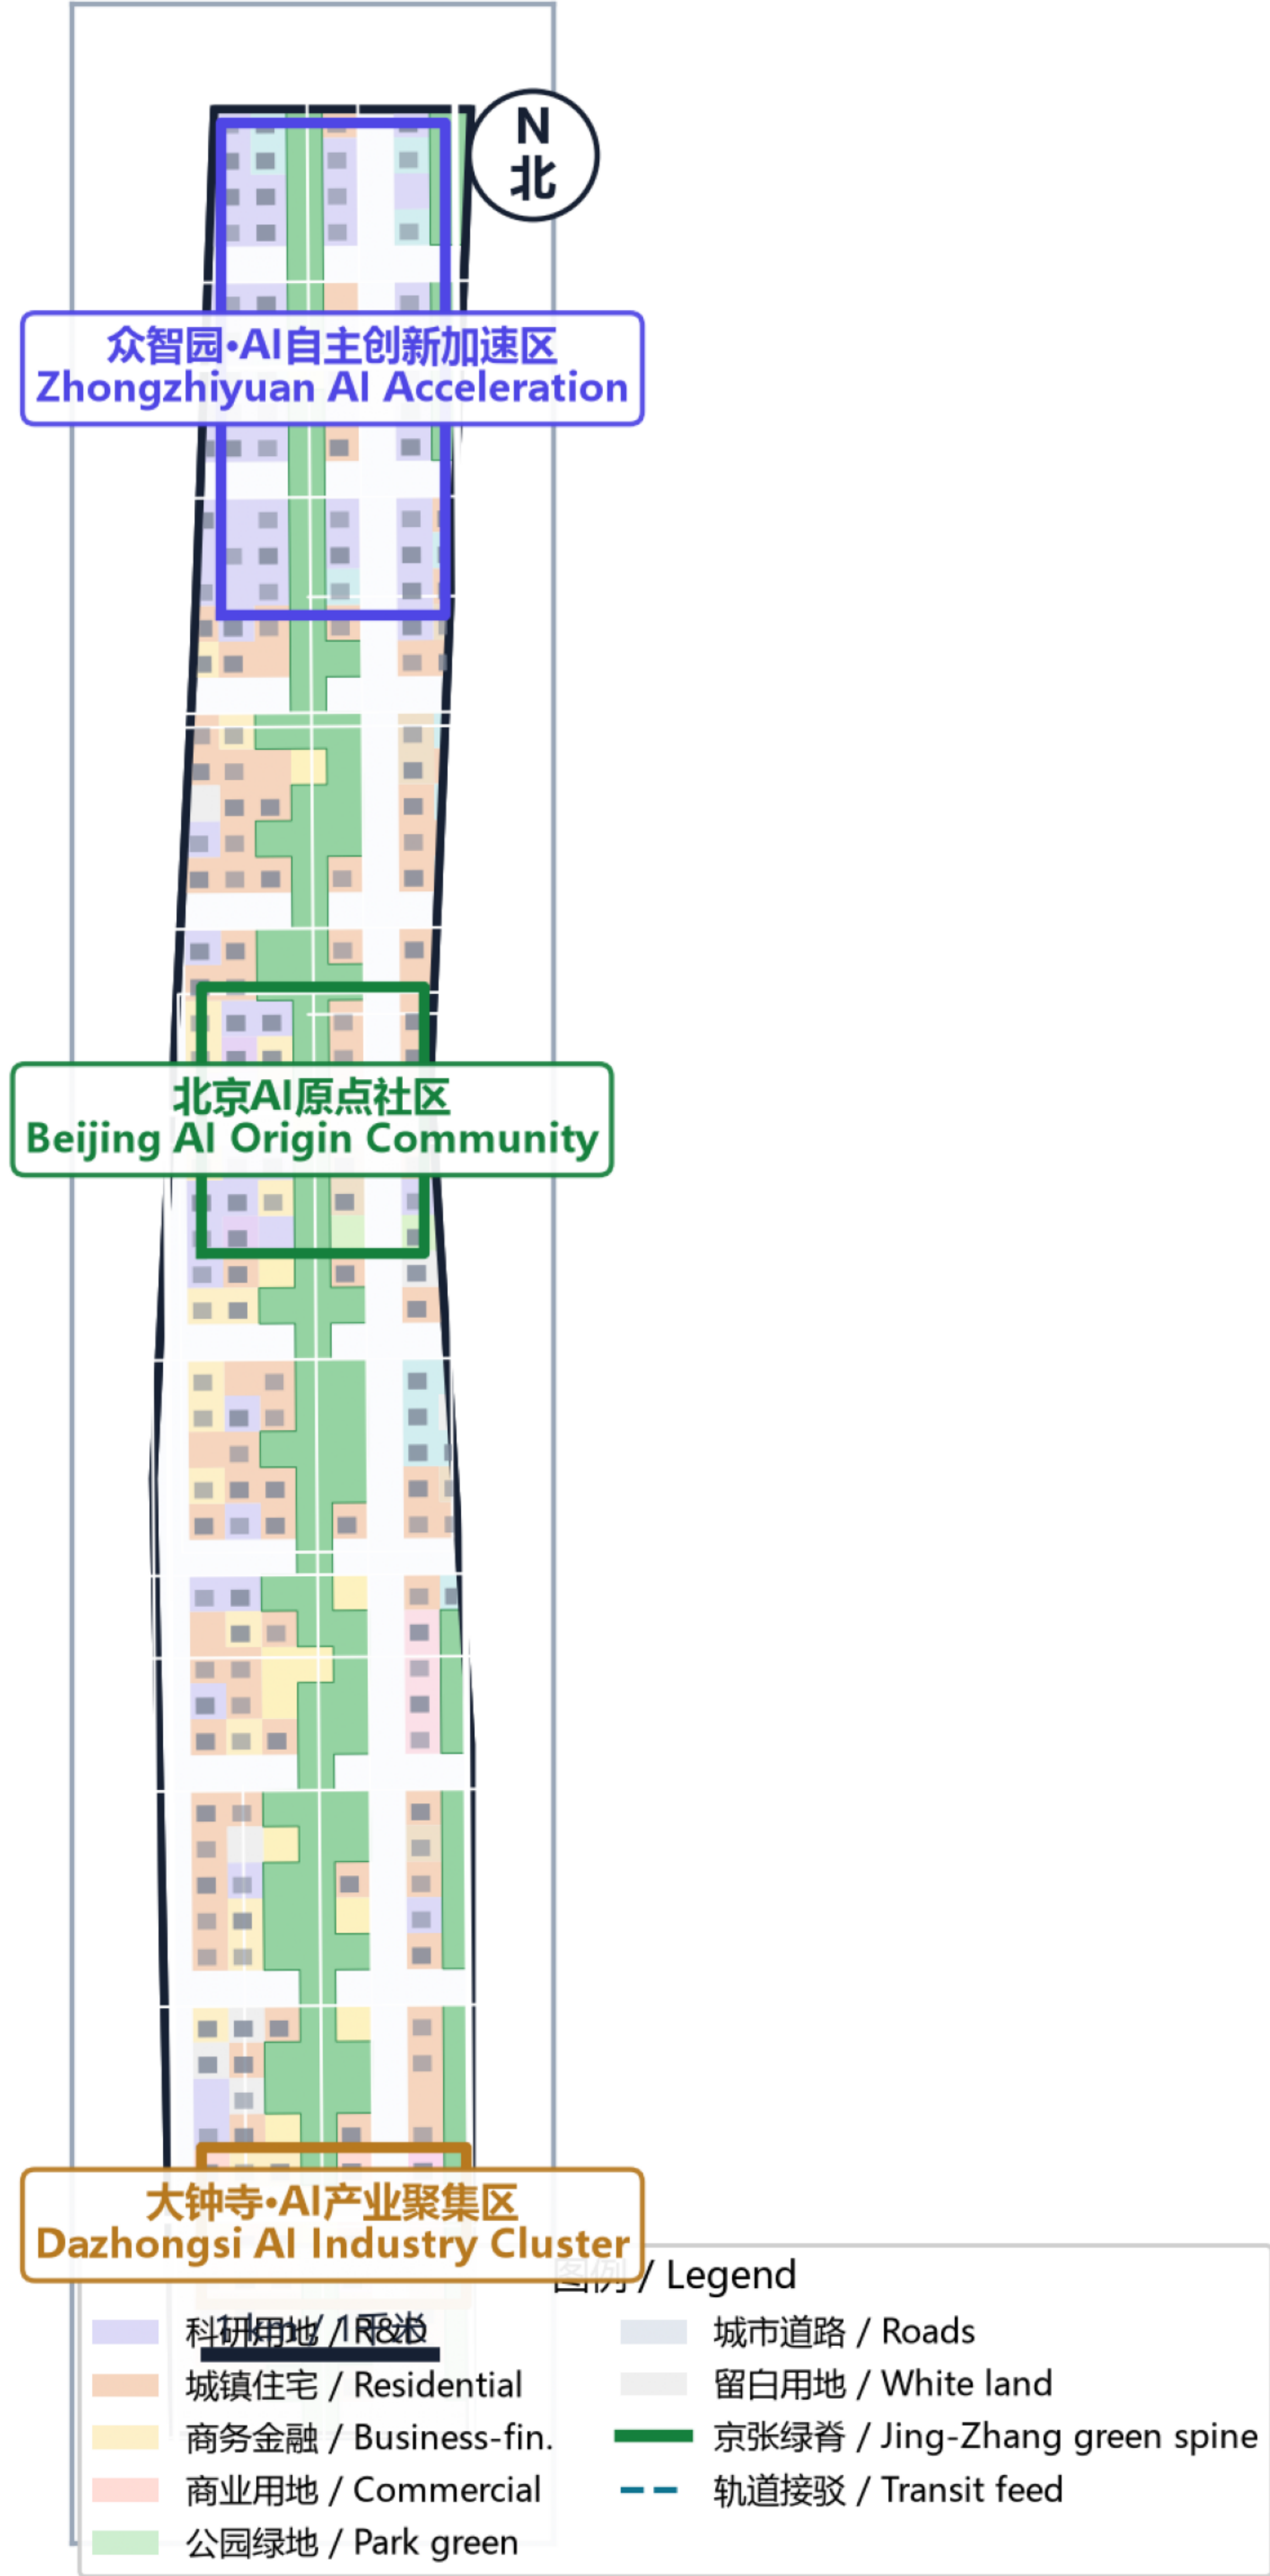

基于临时边界（provisional boundary）的概念方案图，正式红线发布后须更新 | Concept plan on provisional boundary; update upon official redline release

AI Life • AI Creation • AI Axis — Centennial Jing-Zhang AI Innovation Belt — Concept Plan

03 Three key detailed-design areas

Zhongzhiyuan: garden-style innovation quarter. AI Origin Community: campus-adjacent transformation quarter. Dazhongsi: urban intelligent-economy quarter.

三大重点区域详细设计概念 / Three key detailed-design areas

众智园·AI自主创新加速区
Zhongzhiyuan AI Acceleration




193 ha · provisional

北京AI原点社区
Beijing AI Origin Community



104 ha · provisional

大钟寺·AI产业聚集区
Dazhongsi AI Industry Cluster

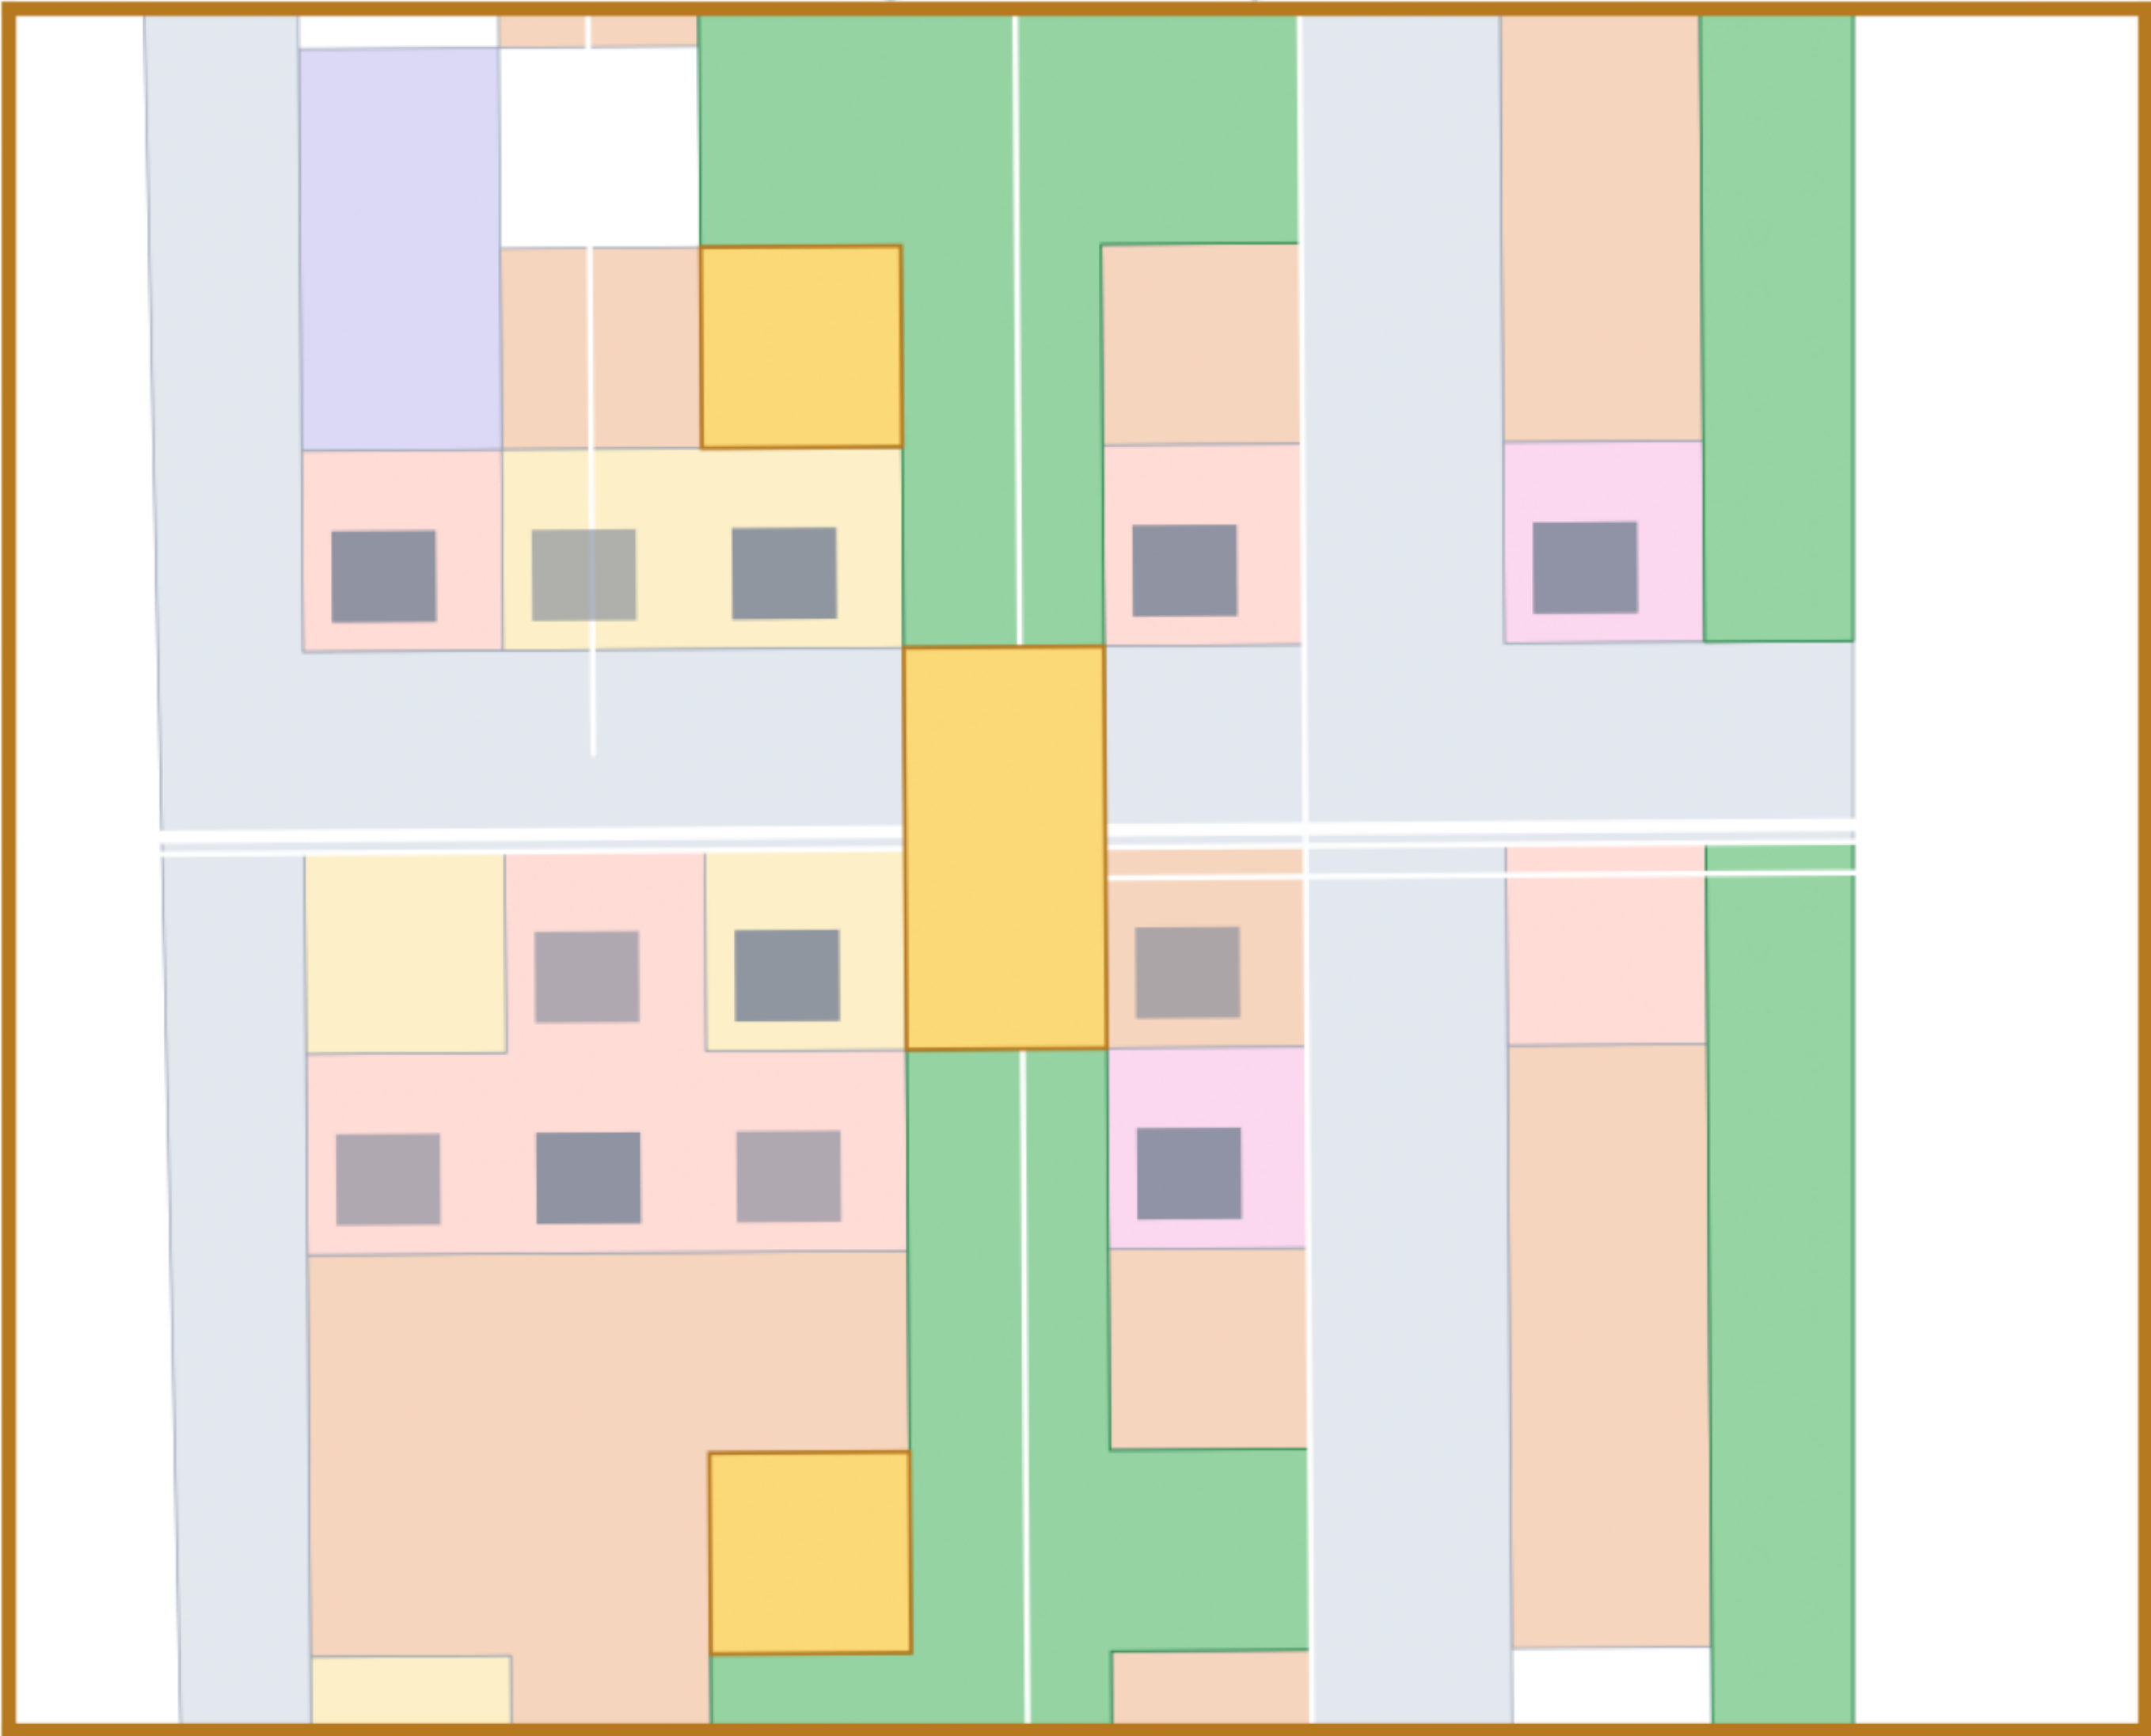

72 ha · provisional


概念深度：结构分区与更新方向；正式控规条件发布后深化 | Concept depth; deepen after statutory controls

AI Life • AI Creation • AI Axis — Centennial Jing-Zhang AI Innovation Belt — Concept Plan


04 Mobility & blue-green network

The green spine runs north-south, slow-mobility loops stitch the three districts, transit feeds bind stations to blocks, and arterial/collector grids carry vehicles.

交通慢行与蓝绿网络 | Mobility & blue-green network

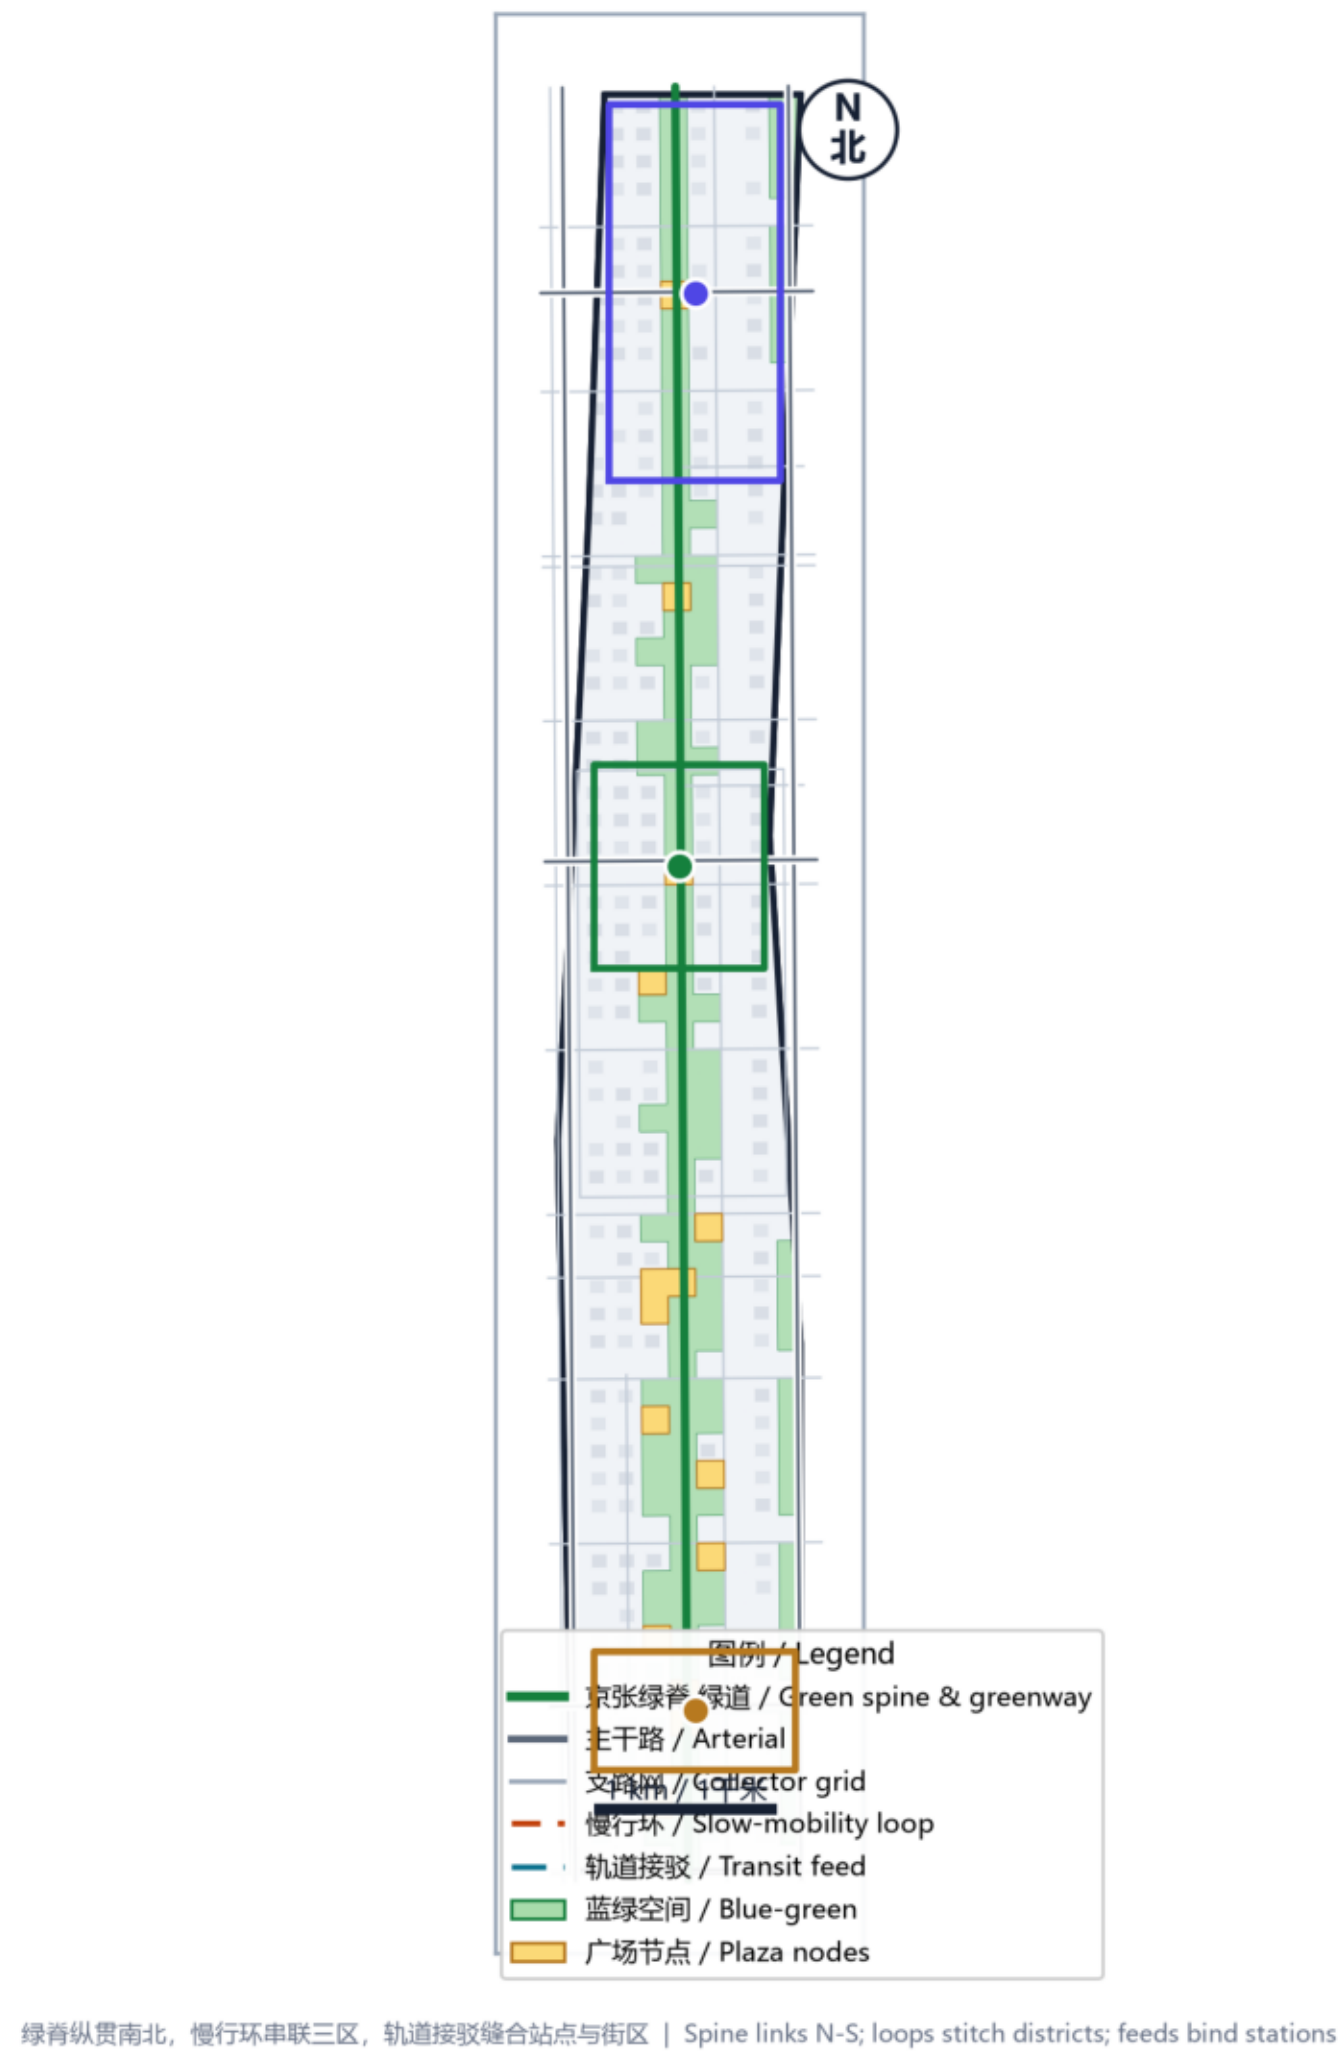

用地结构与概念分区 | Land-use structure & concept partition

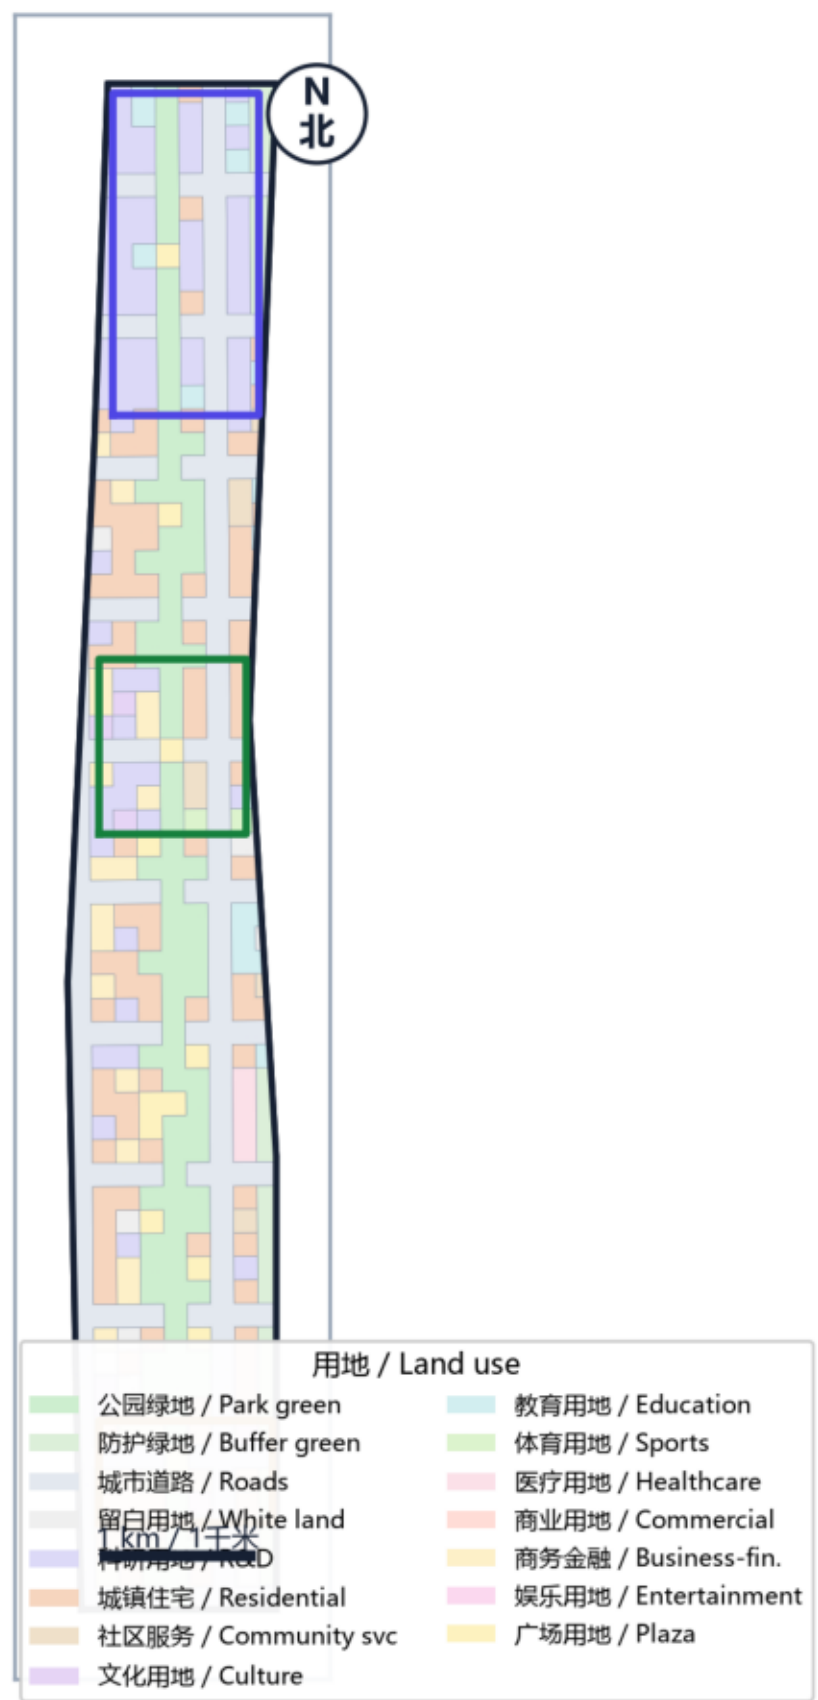


用地平衡表 / Land-use balance

代码 Code	用地 Land use	面积(ha) Area
1207	城市道路 / Roads	347.0
1401	公园绿地 / Park green	211.0
0701	城镇住宅 / Residential	203.2
0802	科研用地 / R&D	149.2
0902	商务金融 / Business-fin.	51.1
1402	防护绿地 / Buffer green	50.3
1403	广场用地 / Plaza	33.8
0804	教育用地 / Education	25.4
16	空白用地 / White land	16.6
0901	商业用地 / Commercial	15.8
0702	社区服务 / Community svc	13.3
0806	医疗用地 / Healthcare	9.0
0803	文化用地 / Culture	6.8
0805	体育用地 / Sports	4.5
0903	娱乐用地 / Entertainment	4.5
合计 / Total		1,141.3


三大重点区域 / Three key areas

面积按 EPSG:4548 投影计算，基于临时边界 | Areas computed in EPSG:4548 on provisional boundary
- 含数据/面积于数据附加属性 (193 ha)


核心规模指标 / Core scale metrics

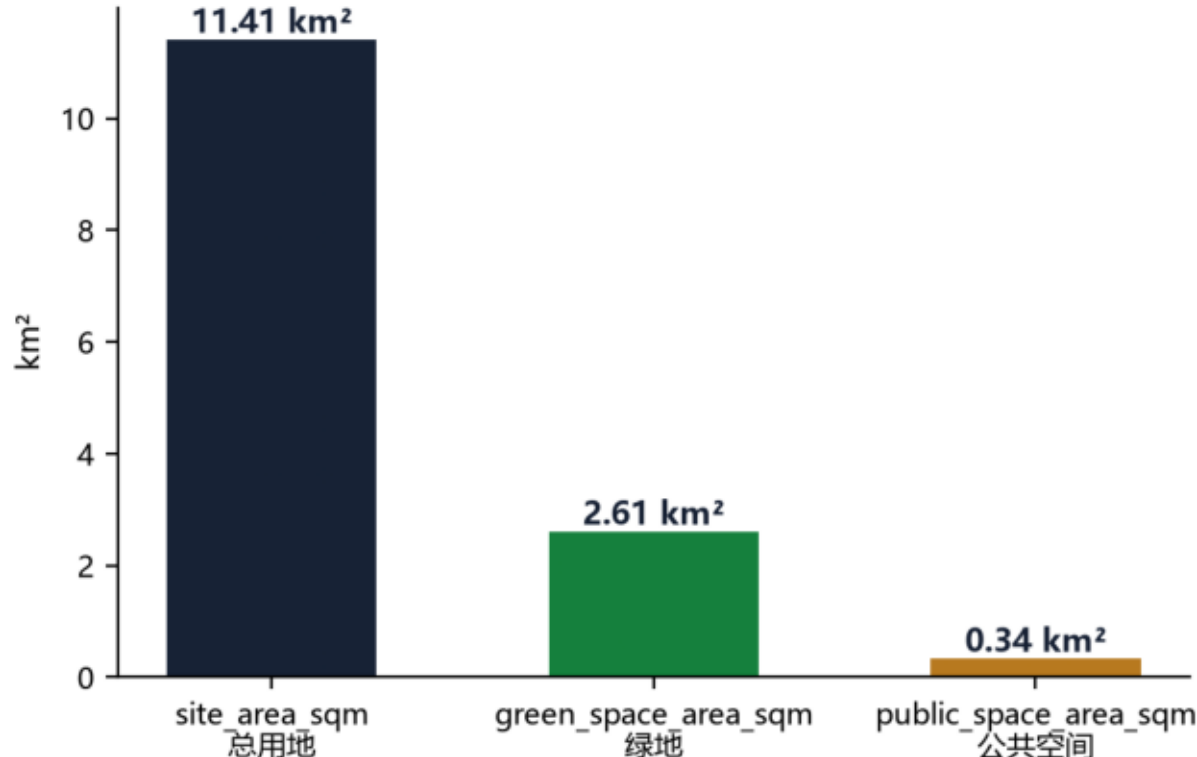

核心比率指标 (%) / Core ratios (%)

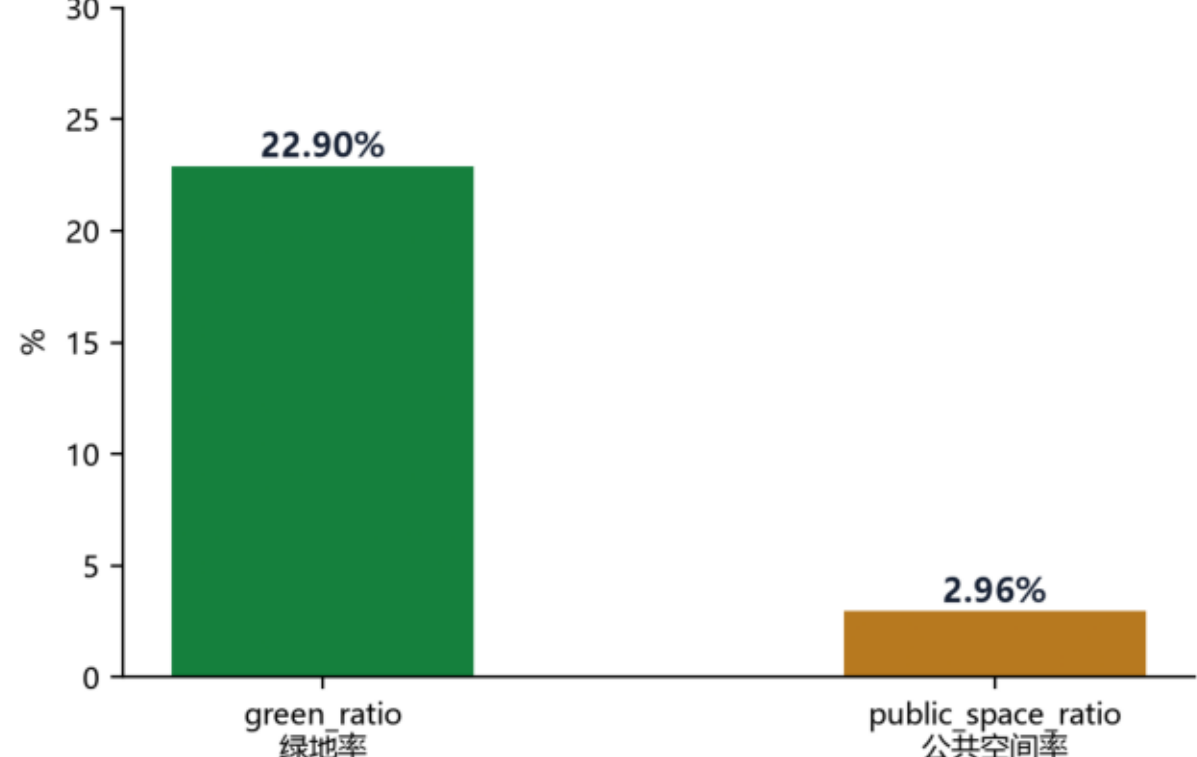

用地构成 TOP8 (ha) / Land-use top-8 (ha)

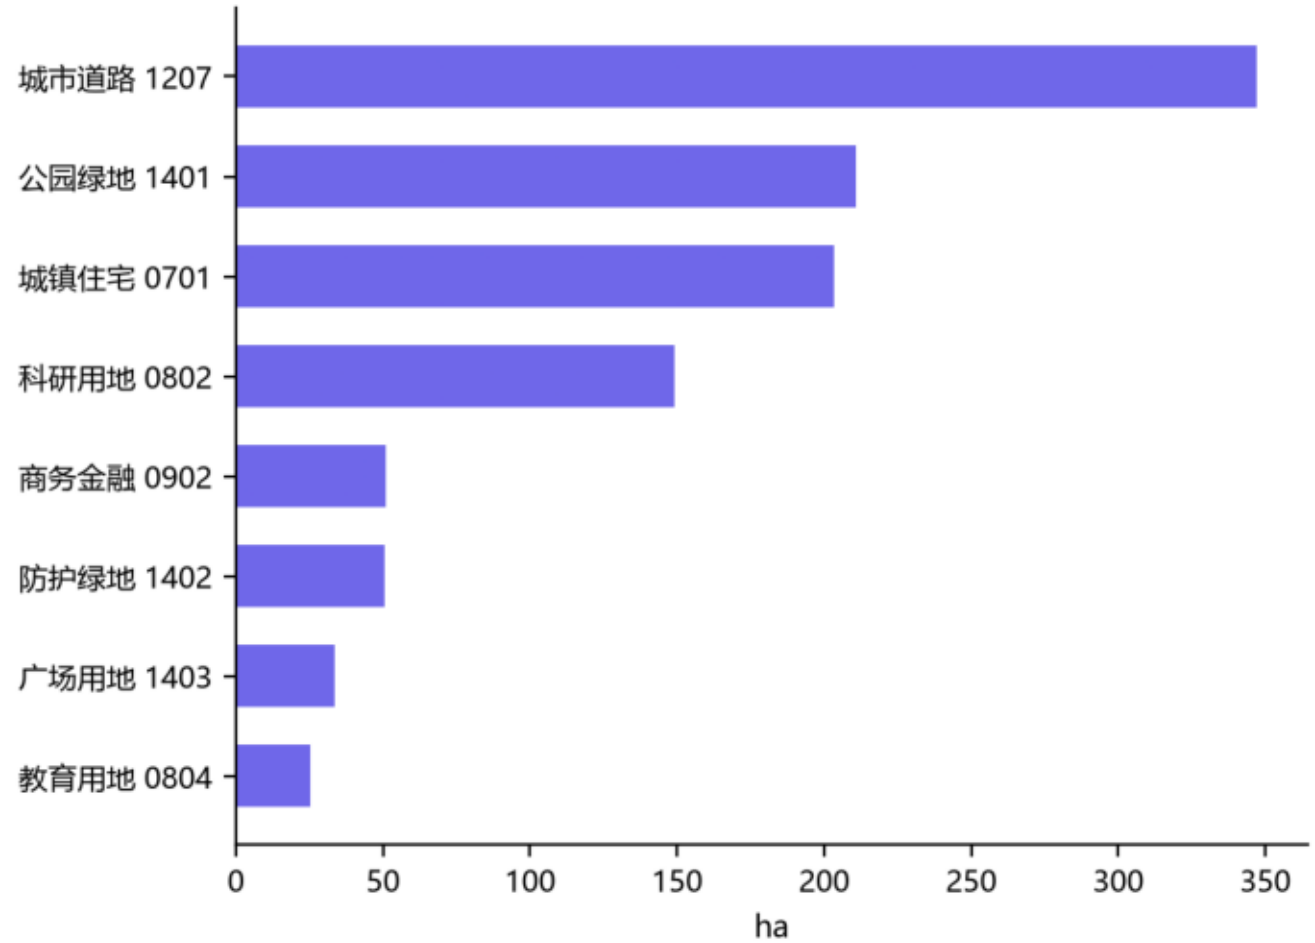

指标证据链 / Metric evidence chain

site_area_sqm	11,412,825.4 sqm	geometry/site_boundary.geojson
green_space_area_sqm	2,613,312.1 sqm	geometry/green_space.geojson
green_ratio	0.22898	green / site @EPSG:4548
public_space_area_sqm	37,500.0 sqm	geometry/public_space.geojson
public_space_ratio	0.029572	public / site @EPSG:4548
key_area_count	3	geometry/key_areas.geojson

全部指标可由提交几何在 EPSG:4548 下复算；基于临时边界，置信度 low

指标与 metrics.json 一致；三大核心视觉指标可在 visual/index.html 复核 | Values mirror metrics.json; three core visual metrics restated in visual page