


京张智脊 · 总体空间结构图 一脊三核 · 两翼多点 · 蓝绿慢行复合环

概念方案 CONCEPT

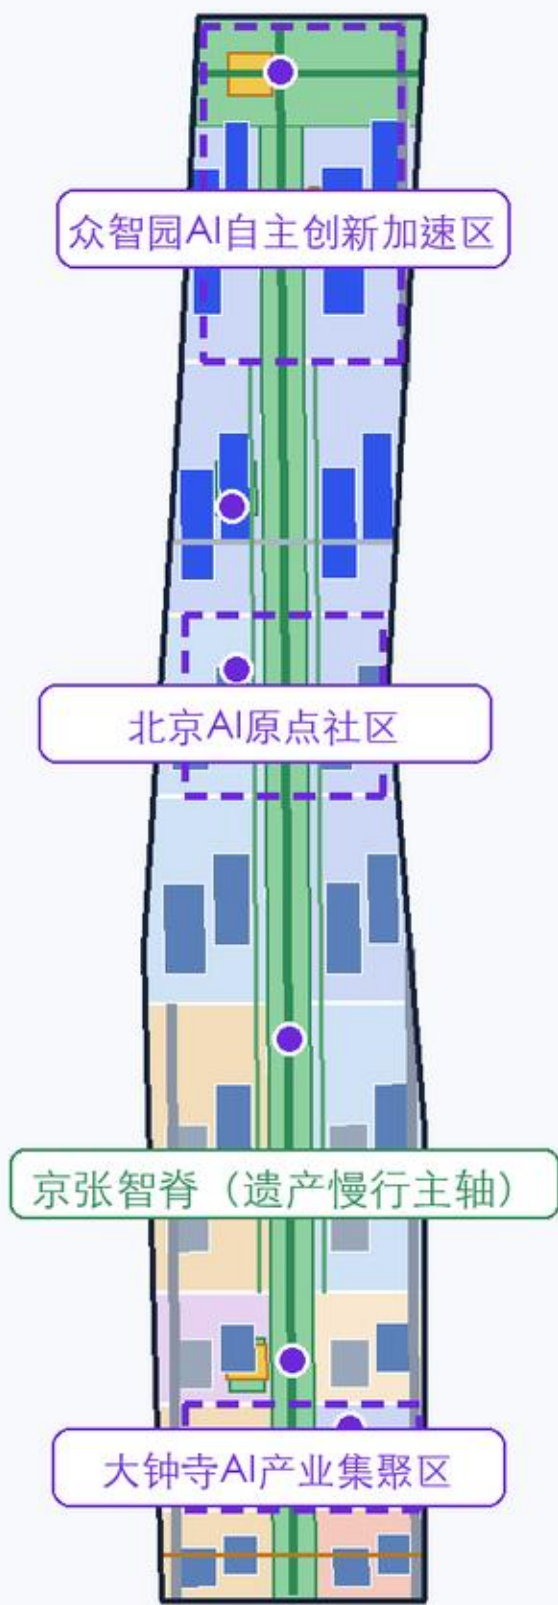

图例 Legend

- 科研/AI研发用地
- 商业服务业用地
- 教育用地
- 居住用地
- 文化用地
- 智脊绿廊与滨水绿带
- 公共空间节点
- 新建概念建筑
- 改造概念建筑
- 保留建筑基底
- AI场景节点


空间结构 Structure

- 一脊：京张遗址公园智脊主轴
- 三核：众智园 · AI原点 · 大钟寺
- 两翼：中关村科技服务翼 · 小月河场景赋能翼
- 多点：10处AI场景节点与6处公共客厅

来源：提交包 geometry/*.*.geojson (EPSG:4548 复算)；边界与重点区为维护者临时粗略多边形，非官方红线 | 绘图：刘霖峰 × AI 2026-08

用地结构与三层范围图 无缝用地分区 · 国土空间分类口径

控规深度城市设计

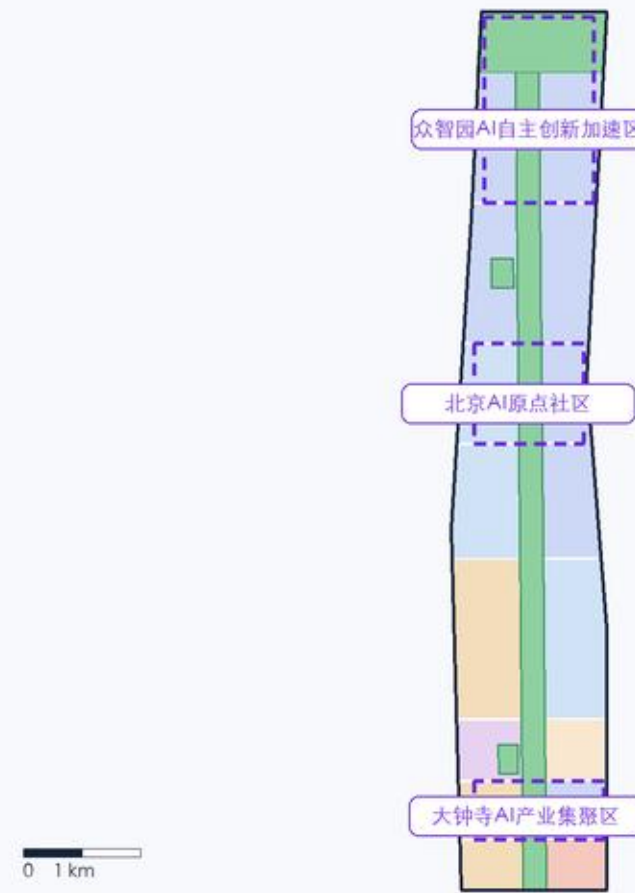

用地构成 (EPSG:4548 复算)	
科研用地 0802	454.8万㎡
教育用地 0804	223.7万㎡
公园绿地 1401	189.4万㎡
居住用地 0701	167.5万㎡
文化用地 0803	38.1万㎡
社区服务 0702	36.5万㎡
商业服务 05	29.2万㎡

三层范围 Three scopes

统筹研究范围 43.6 km²

产业生态与未来城市形态研究

总体设计范围 11.4 km²

控规深度城市设计 (本图范围)

重点区域范围 368.4 ha

三处重点片区详细设计

用地代码依据《国土空间调查、规划、用途管制用地用海分类指南》；分区由提交边界无缝派生，无重叠无缺口 | 临时边界，面积以官方数据发布后重算为准

三处重点区域详细设计索引图 众智园 · AI原点社区 · 大钟寺

综合实施方案深度

众智园AI自主创新加速区


公告约 192.1 公顷 · 临时多边形



- 花园型全栈自主创新街区
- 国家平台 · 标准治理 · 安全评测展示
- 清河文化界面与低碳创新交往
- 五环路一体化对外交通优化方向

北京AI原点社区

公告约 104.3 公顷 · 临时多边形

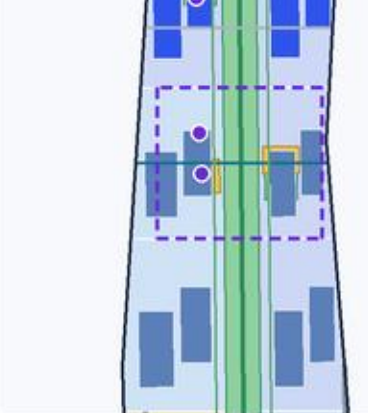

- 近郊型成果转化与人才社区
- 开源体系 · 成果发布 · 人才特区服务
- 校区园区街区慢行缝合
- 五道口/清华东路西口站一体化

大钟寺AI产业集聚区

公告约 72.0 公顷 · 临时多边形



- 城市型智能经济与国际交往街区
- 智能体 · 智能终端 · 内容消费新业态
- 大钟寺站四象限步行连通
- 规划绿地复合利用与商业服务提升

三处重点区均为临时粗略多边形 (provisional_constraint)，仅用于概念设计讨论；详细设计结论待官方片区范围发布后复核 | 证据：geometry/key_areas.geojson

设计判断 Design statements

- 以遗址公园为公共主轴组织AI创新带：科研用地约40%，绿地率约22.8%，公共空间比例约2.6%（临时边界内概念复算）。
- 三核分工：众智园=全栈自主与治理，原点社区=成果转化与人才，大钟寺=智能经济与国际交往。
- 全部空间结论为概念建议；官方边界与控规条件发布后重算深化。

交通慢行与蓝绿公共空间复合系统图

南北贯通 · 东西缝合 · 站点一体

系统规划



图例 Legend

- 智脊遗产慢行主轴（绿道）
- 轨道站点联络慢行道
- 东西骑行通勤廊
- 现状主干路走廊
- 清河 / 小月河蓝线（临时示意）
- 轨道站点与文保节点
- 蓝绿公共空间网络
- 公共客厅与广场

设计策略 Strategy

慢行断点缝合：跨环路、站前与桥下节点优先
四象限步行连通：大钟寺站路口一体化
蓝绿复合：清河滨水+遗址公园+口袋公园
静态交通：非机动车停放与接驳秩序优化
AI+交通：可解释导视与低侵入传感辅助诊断

道路为概念中心线（非道路红线）；慢行系统与蓝绿网络指标见 metrics.json：slow_mobility_spine_length_m / green_ratio / public_space_ratio

核心指标复算与证据链图

几何 → 指标 → 矩阵 → 自检

可复核 AUDITABLE

site_area_sqm

11,412,825 m²

总体设计范围 ≈11.4 km²

green_ratio

22.8%

绿地率（概念，临时边界内）

public_space_ratio

2.6%

公共空间比例（广场客厅）

building_footprint_area_sqm

283 万 m²

概念建筑基底合计

concept_total_floor_area_sqm

1914 万 m²

概念总建筑规模（低置信）

floor_area_ratio

待正式数据补齐

容积率：官方控制条件缺失

重点区面积：临时多边形 vs 公告值（ha）

众智园 192.9 / 192.1

AI原点 104.3 / 104.3

大钟寺 72.0 / 72.0

偏差 <0.5%，满足面积校核；仍以官方片区范围为准

分期面积（EPSG:4548）

近期 2026-28 239 万 m²

中期 2028-31 510 万 m²

远期 2031-35 392 万 m²

证据链与自检状态 Evidence & self-check

geometry/*.geojson 9 个图层 · 无缝用地分区 · 投影复算

metrics.json 32 项指标 · 公式/来源/置信度齐备

compliance_matrix.json 公告 1.3-1.5 + agent.1-6 全覆盖

standard_matrix.json 5 项强制专业标准全部响应

design_depth_matrix.json 15 项设计深度项全部 complete

self_check.json 四门框自检：确定性/空间/视觉/专业

所有 known 指标均可从提交包 GeoJSON 在 EPSG:4548 下复算；unknown 指标在 assumptions.json 中登记待补条件 | 数值与 visual/index.html 的 data-metric 完全一致

实施路径 Implementation pathway

- 近期（2026-28）：智脊慢行断点缝合、清华园车站记忆广场、大钟寺四象限连通概念方案（约239万 m²）。
- 中期（2028-31）：成果转化街与开源发布厅、站点接驳优化、端侧算力驿站试点（约510万 m²）。
- 远期（2031-35）：清河创新界面与滨水客厅、全球AI活动周路线滚动运营（约392万 m²）。
- 运营：一周一节一坛一月度 + 六方共治委员会 + 场景开放申请制（均为概念建议）。