

01 总体概念与空间结构


一轴· 三核· 两翼 —— 从铁路原点到 AI 原点

主名称：京张智创带；概念名：原点带 / The Origin Belt；Logo 方向为“同心圆原点 O”——外圈是京张铁路“人字形”轮迹抽象，内点是 AI 的“原点”。三大定位：世界级 AI 自主创新策源地、AI 新质生产力城市形态样板、全球 AI 人才向往的高品质城区。五大功能：创新策源、场景验证、人才生活、文化体验、全球交往。三区两翼协同四路：A1 全栈自主创新加速（北）、A2 近校转化与人才社区（中）、A3 智能经济与国际交往（南）；中关村科技服务翼（西）、小月河场景赋能翼（东）。

描述	面积	核心问题	方案目标
核算研究范围	43.6 km²	AI 产业生态与未来城市形态	高校策源—开源协作—生态转化—场景验证—国际传播
总体设计范围	11.4 km²	城市更新、产业空间、交通市政与风貌	一轴三核两翼 + 12 类用地无缝分区
重点区域	368.4 公顷	三处片区详细设计	众智园/AI 原点社区/大钟寺分别定位

京张智创带 · 从铁路原点到 AI 原点 —— 总体概念图

一轴（京张遗址公园活力带）· 三核（众智园 / AI 原点社区 / 大钟寺）· 两翼（中关村科技服务翼 / 小月河场景赋能翼）

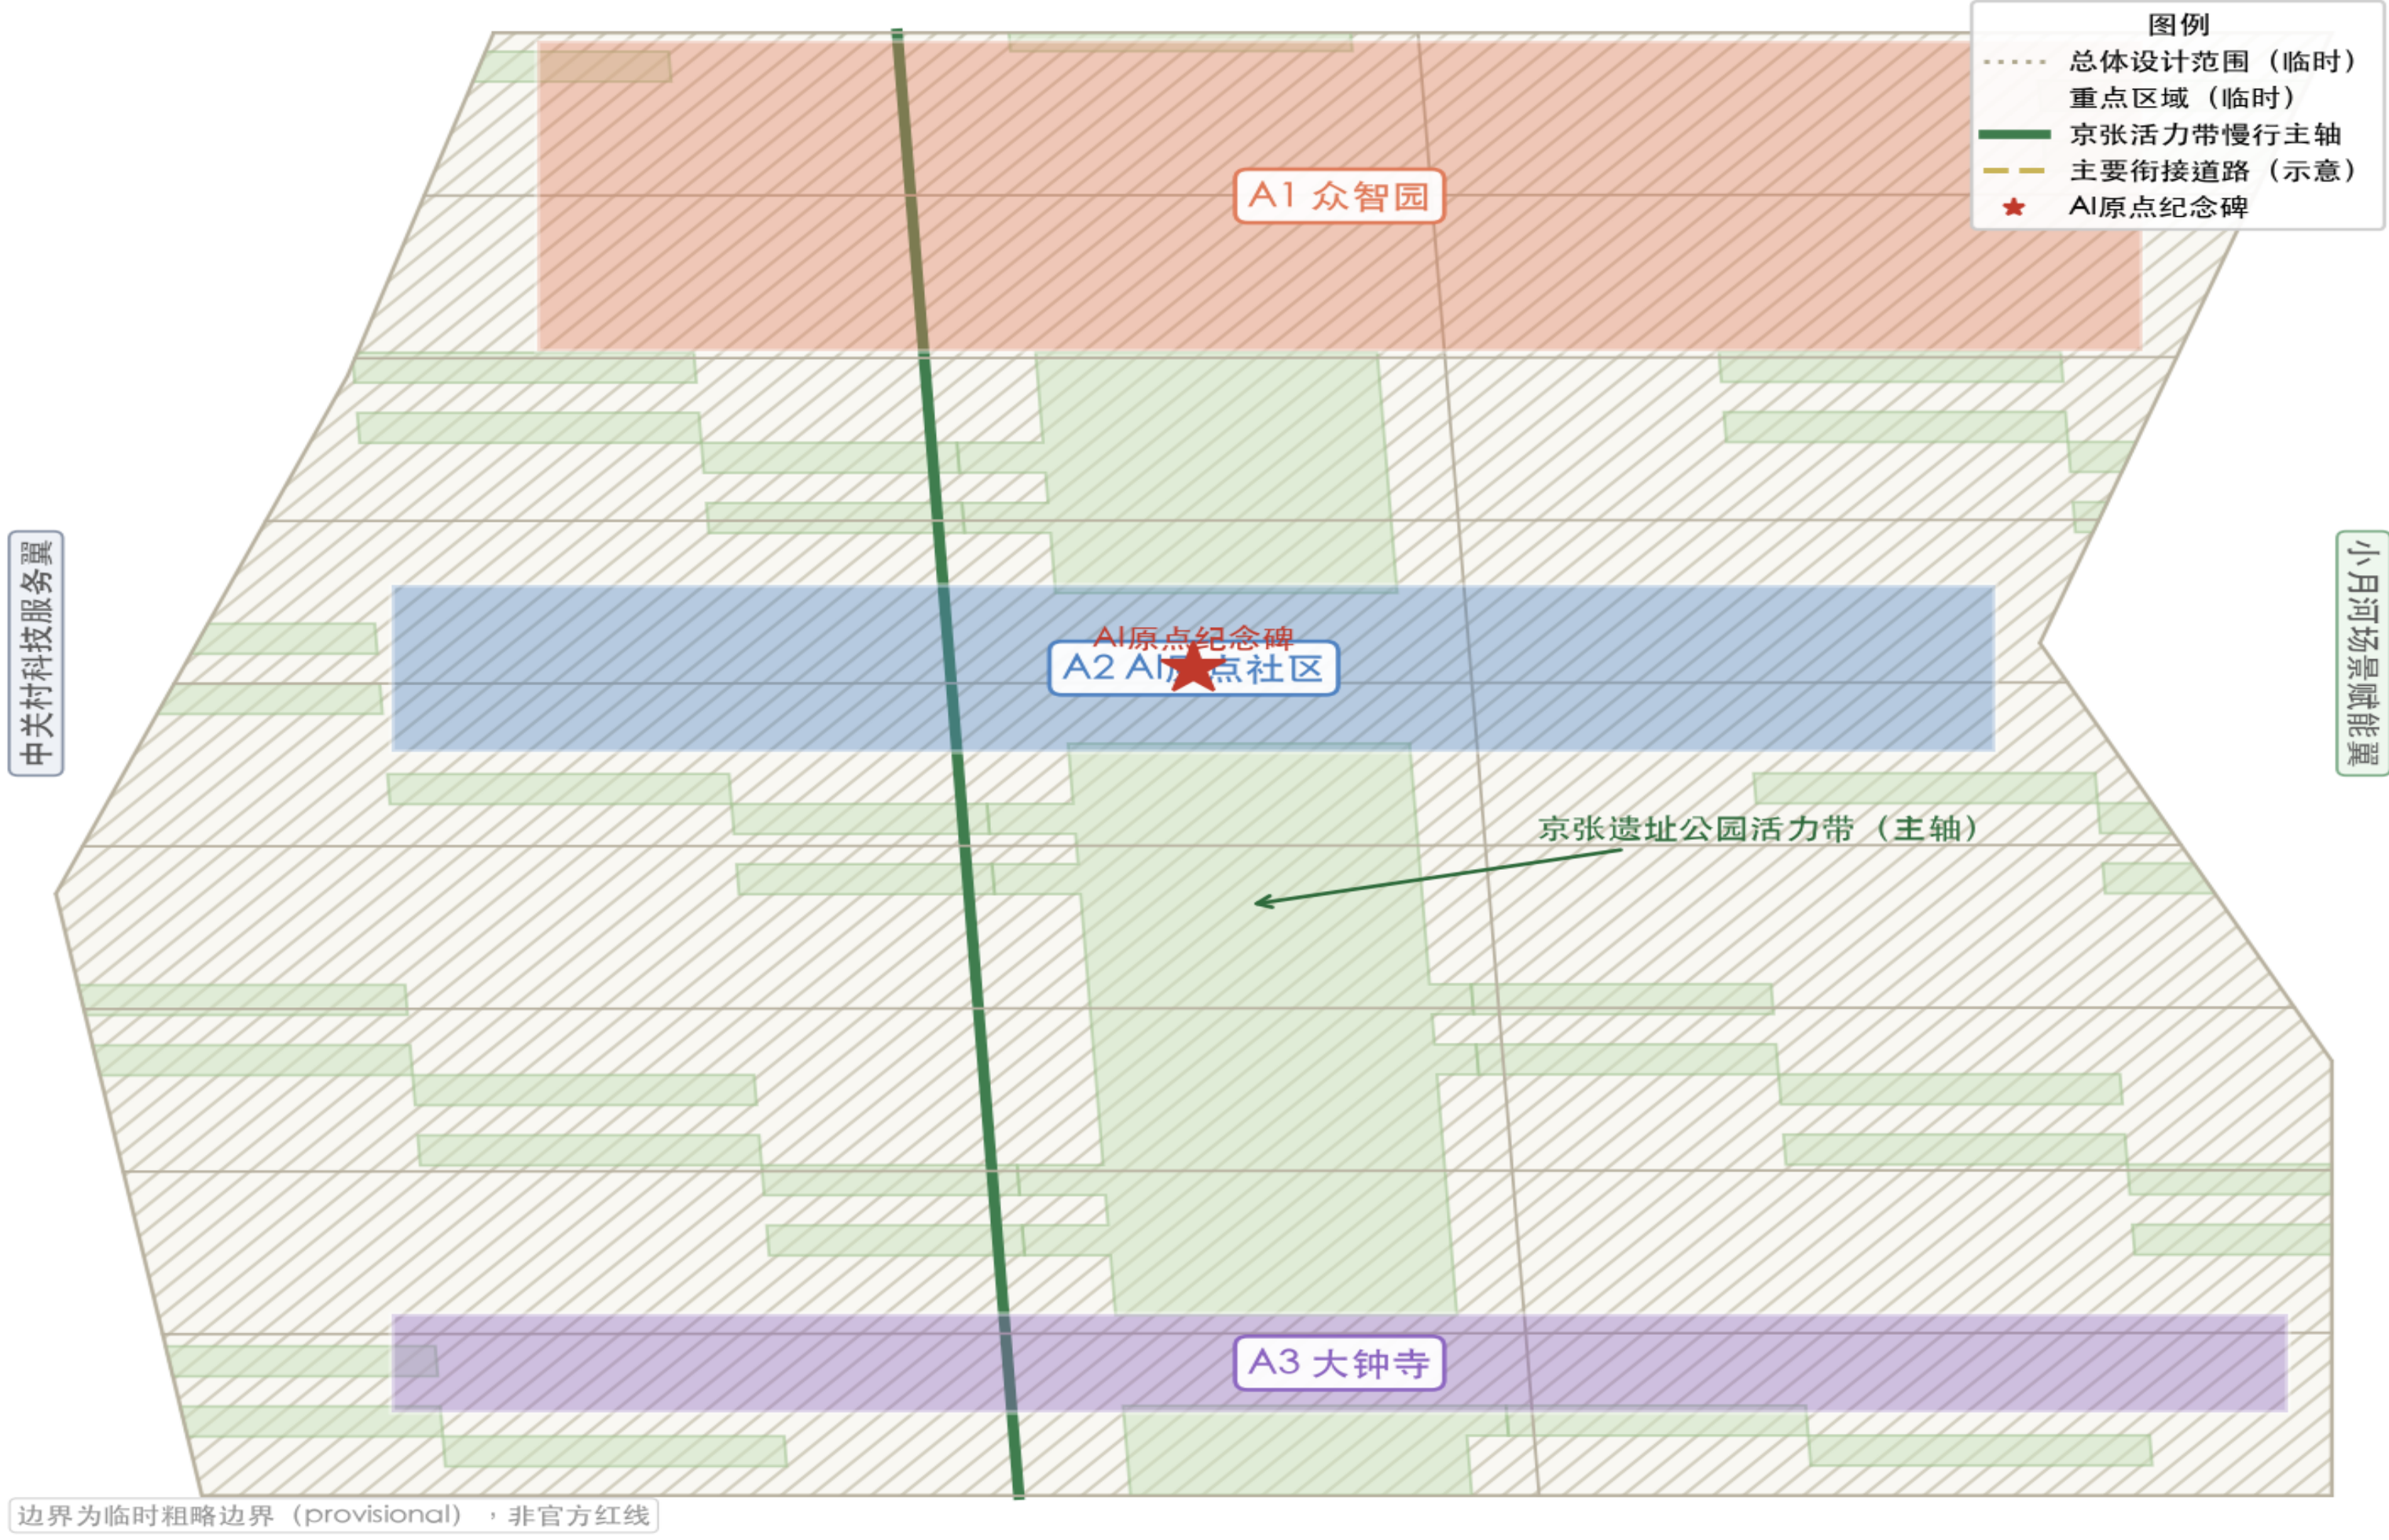

来源：本方案 geometry/*.geojson (provisional_boundaries 派生)；EPSG:4326 展示；边界精度见 proposal.mxd


02 用地布局与城市更新

12 类用地无缝覆盖 · 8 个更新项目 · 拆改留策略

用地依照国土空间用地分类表达，分区闭合无缝（gap=0），面积在 EPSG:4548 复算，北投（众智图）科研与文化展示为主；中投（AI 原点社区）科研—教育—居住混合承载团校孵化与人才生活；南投（大钟寺）商业商务承载智慧经济与国际交往。城市更新以“小尺度、渐进式、街区织补”为原则，形成 8 个更新项目（见分期表），容积率、建筑密度等控制指标在官方条件缺类后记为待确认，仅提供示意建筑基底用于结构与密度研究。

用地布局与空间结构图（控规深度示意）

12 类用地无缝覆盖总体设计范围（gap=0）；三核锚点 + 活力带主轴 + 东西缝合廊道组织空间结构

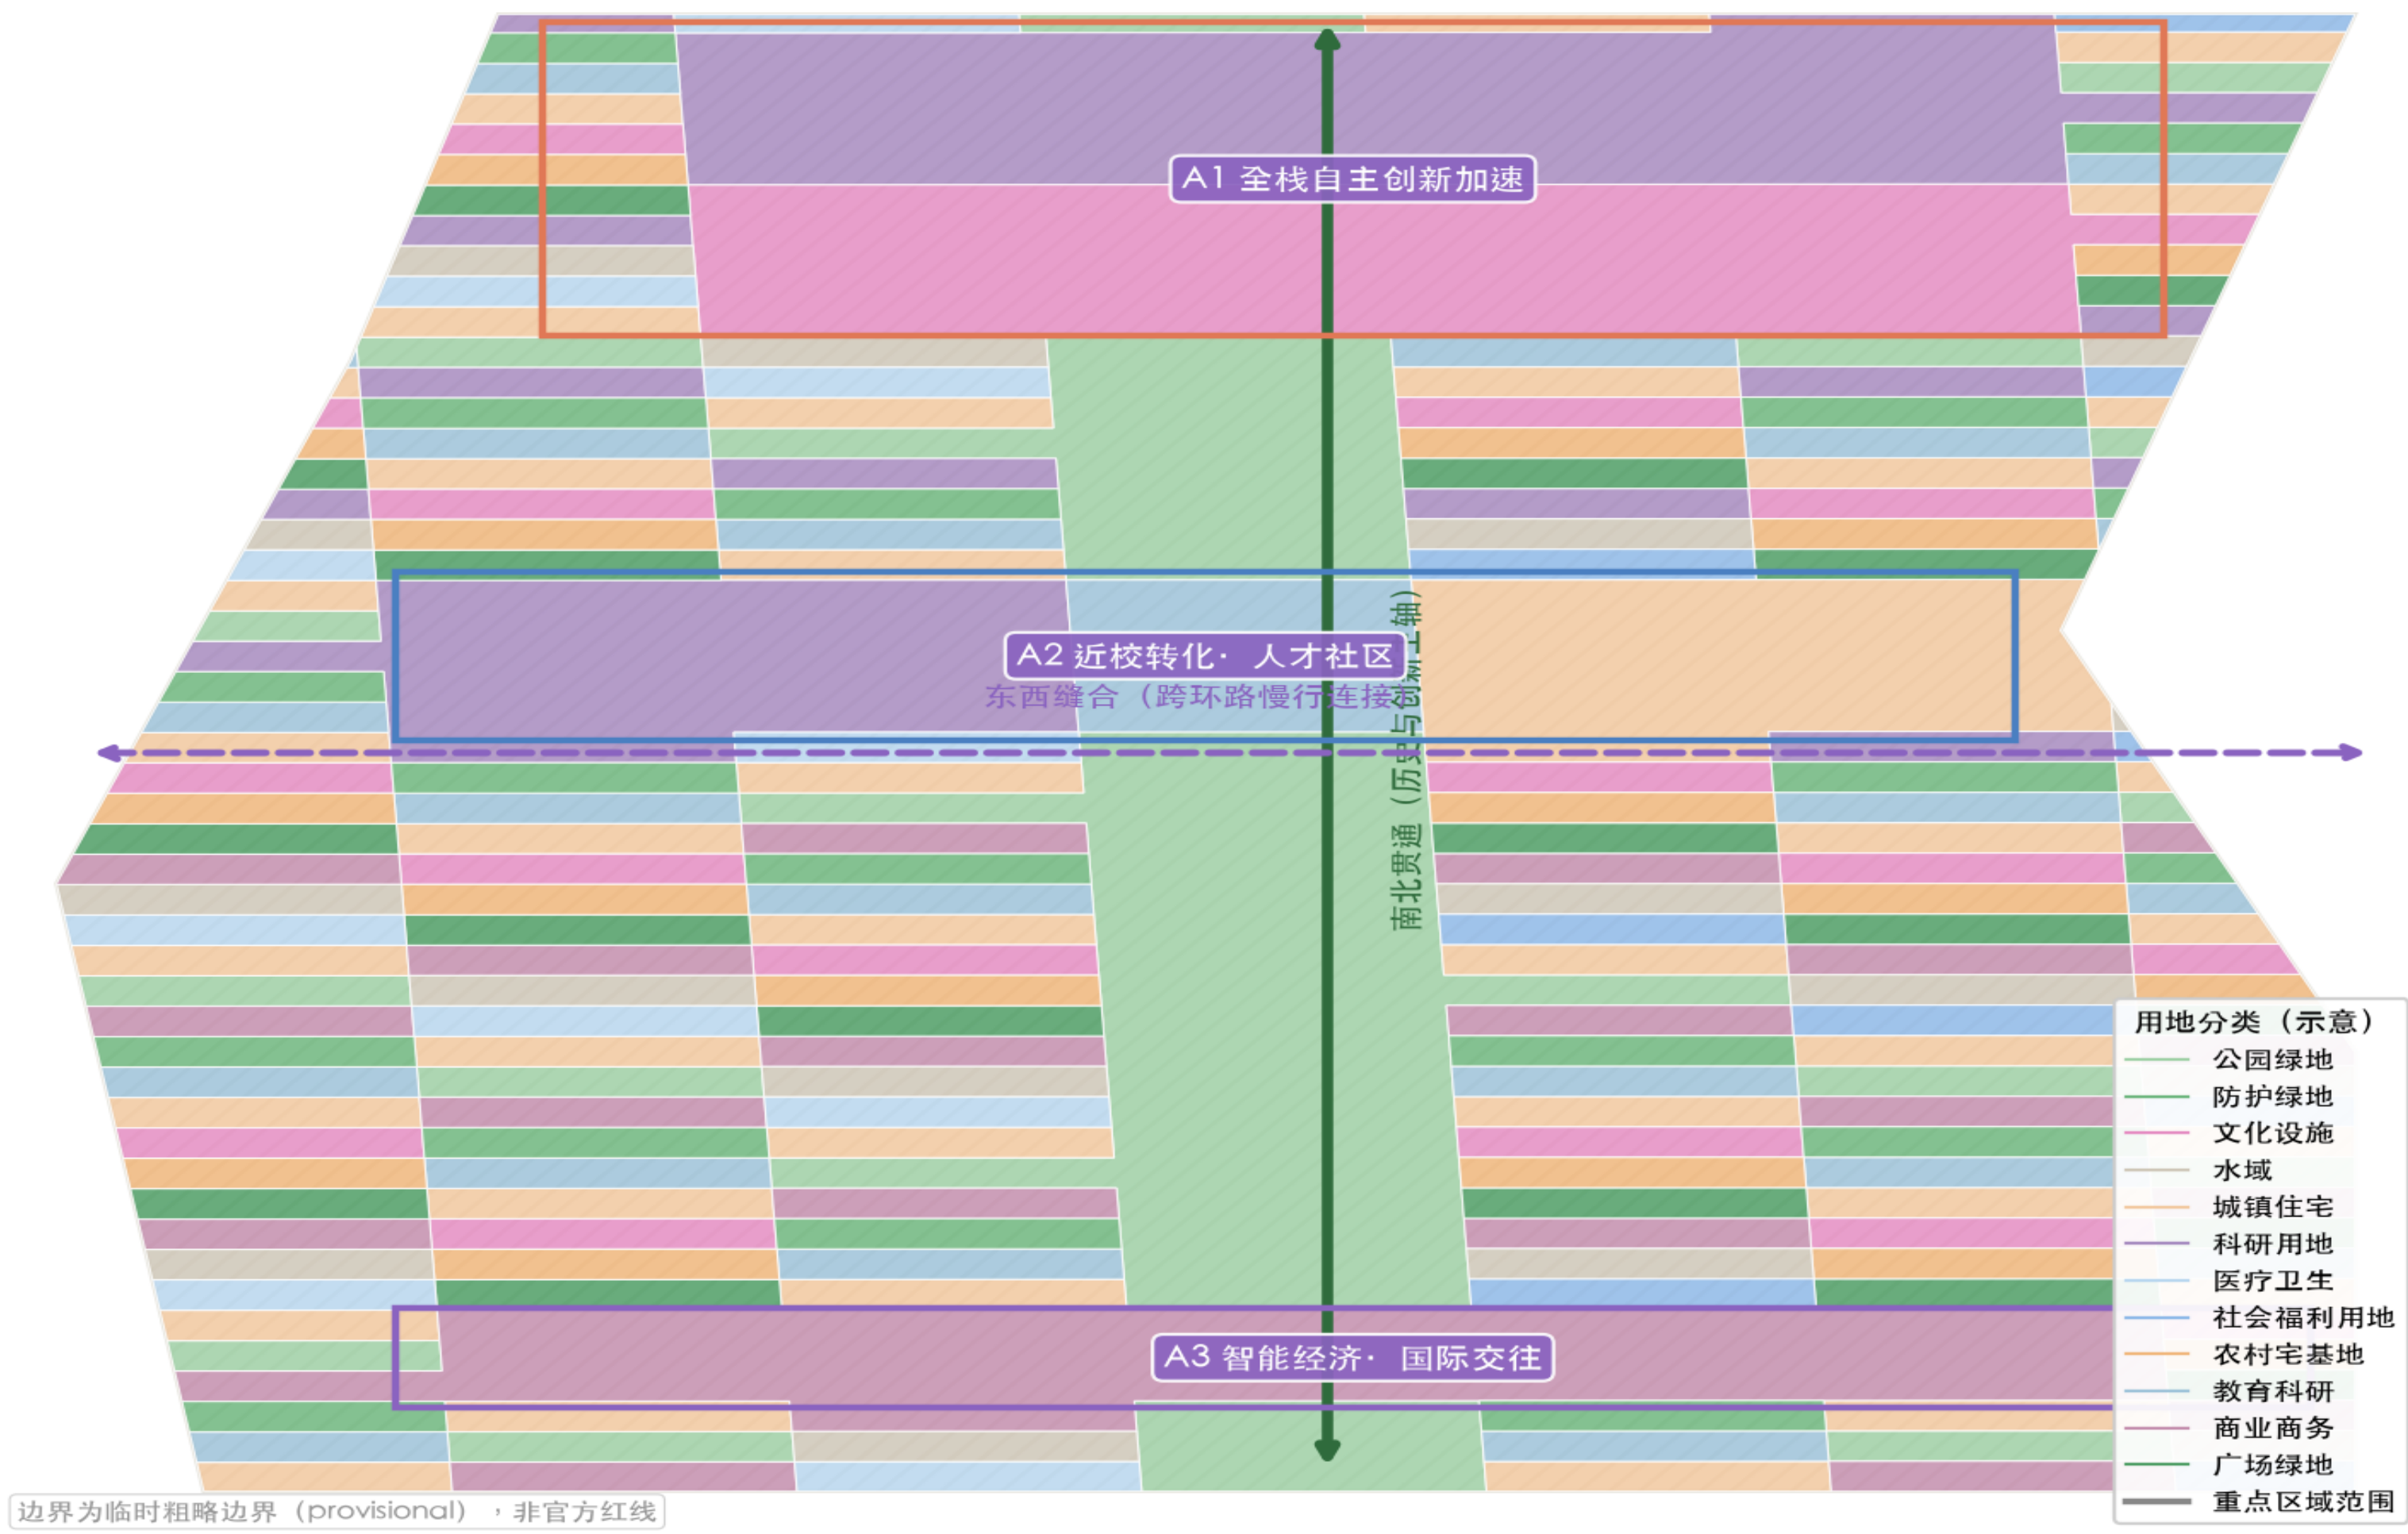

来源：geometry/land_use.geojson（12 分区，EPSG:4548 面积复算）；用地分类依据《国土空间调查、规划、用途管制用地用海分类指南》


03 交通、轨道、市政与 AI 新基建

慢行主轴 * 东西缝合 * 轨道接驳 * AI 场景节点

以活力带慢行主轴*0 条东西缝合连接带*外围衔接环路组织路网 · 重点解决京张遗址公园上跨北五环慢行断点 · 大钟寺站西侧步行连续 · 五道口/清华东路西口校线接驳 · 线网传统市政与 AI 产业服务设施 · 创新服务平台 · 分布式能源与碳测算力 · 铁路遗址走向与小月河/清河水系以示意线标注（非官方线位/蓝线） ·

交通慢行与蓝绿公共空间复合系统图

慢行主轴贯通 · 东西缝合连接 · 轨道接驳 · AI 场景节点（低速、可监管、可复核试点）

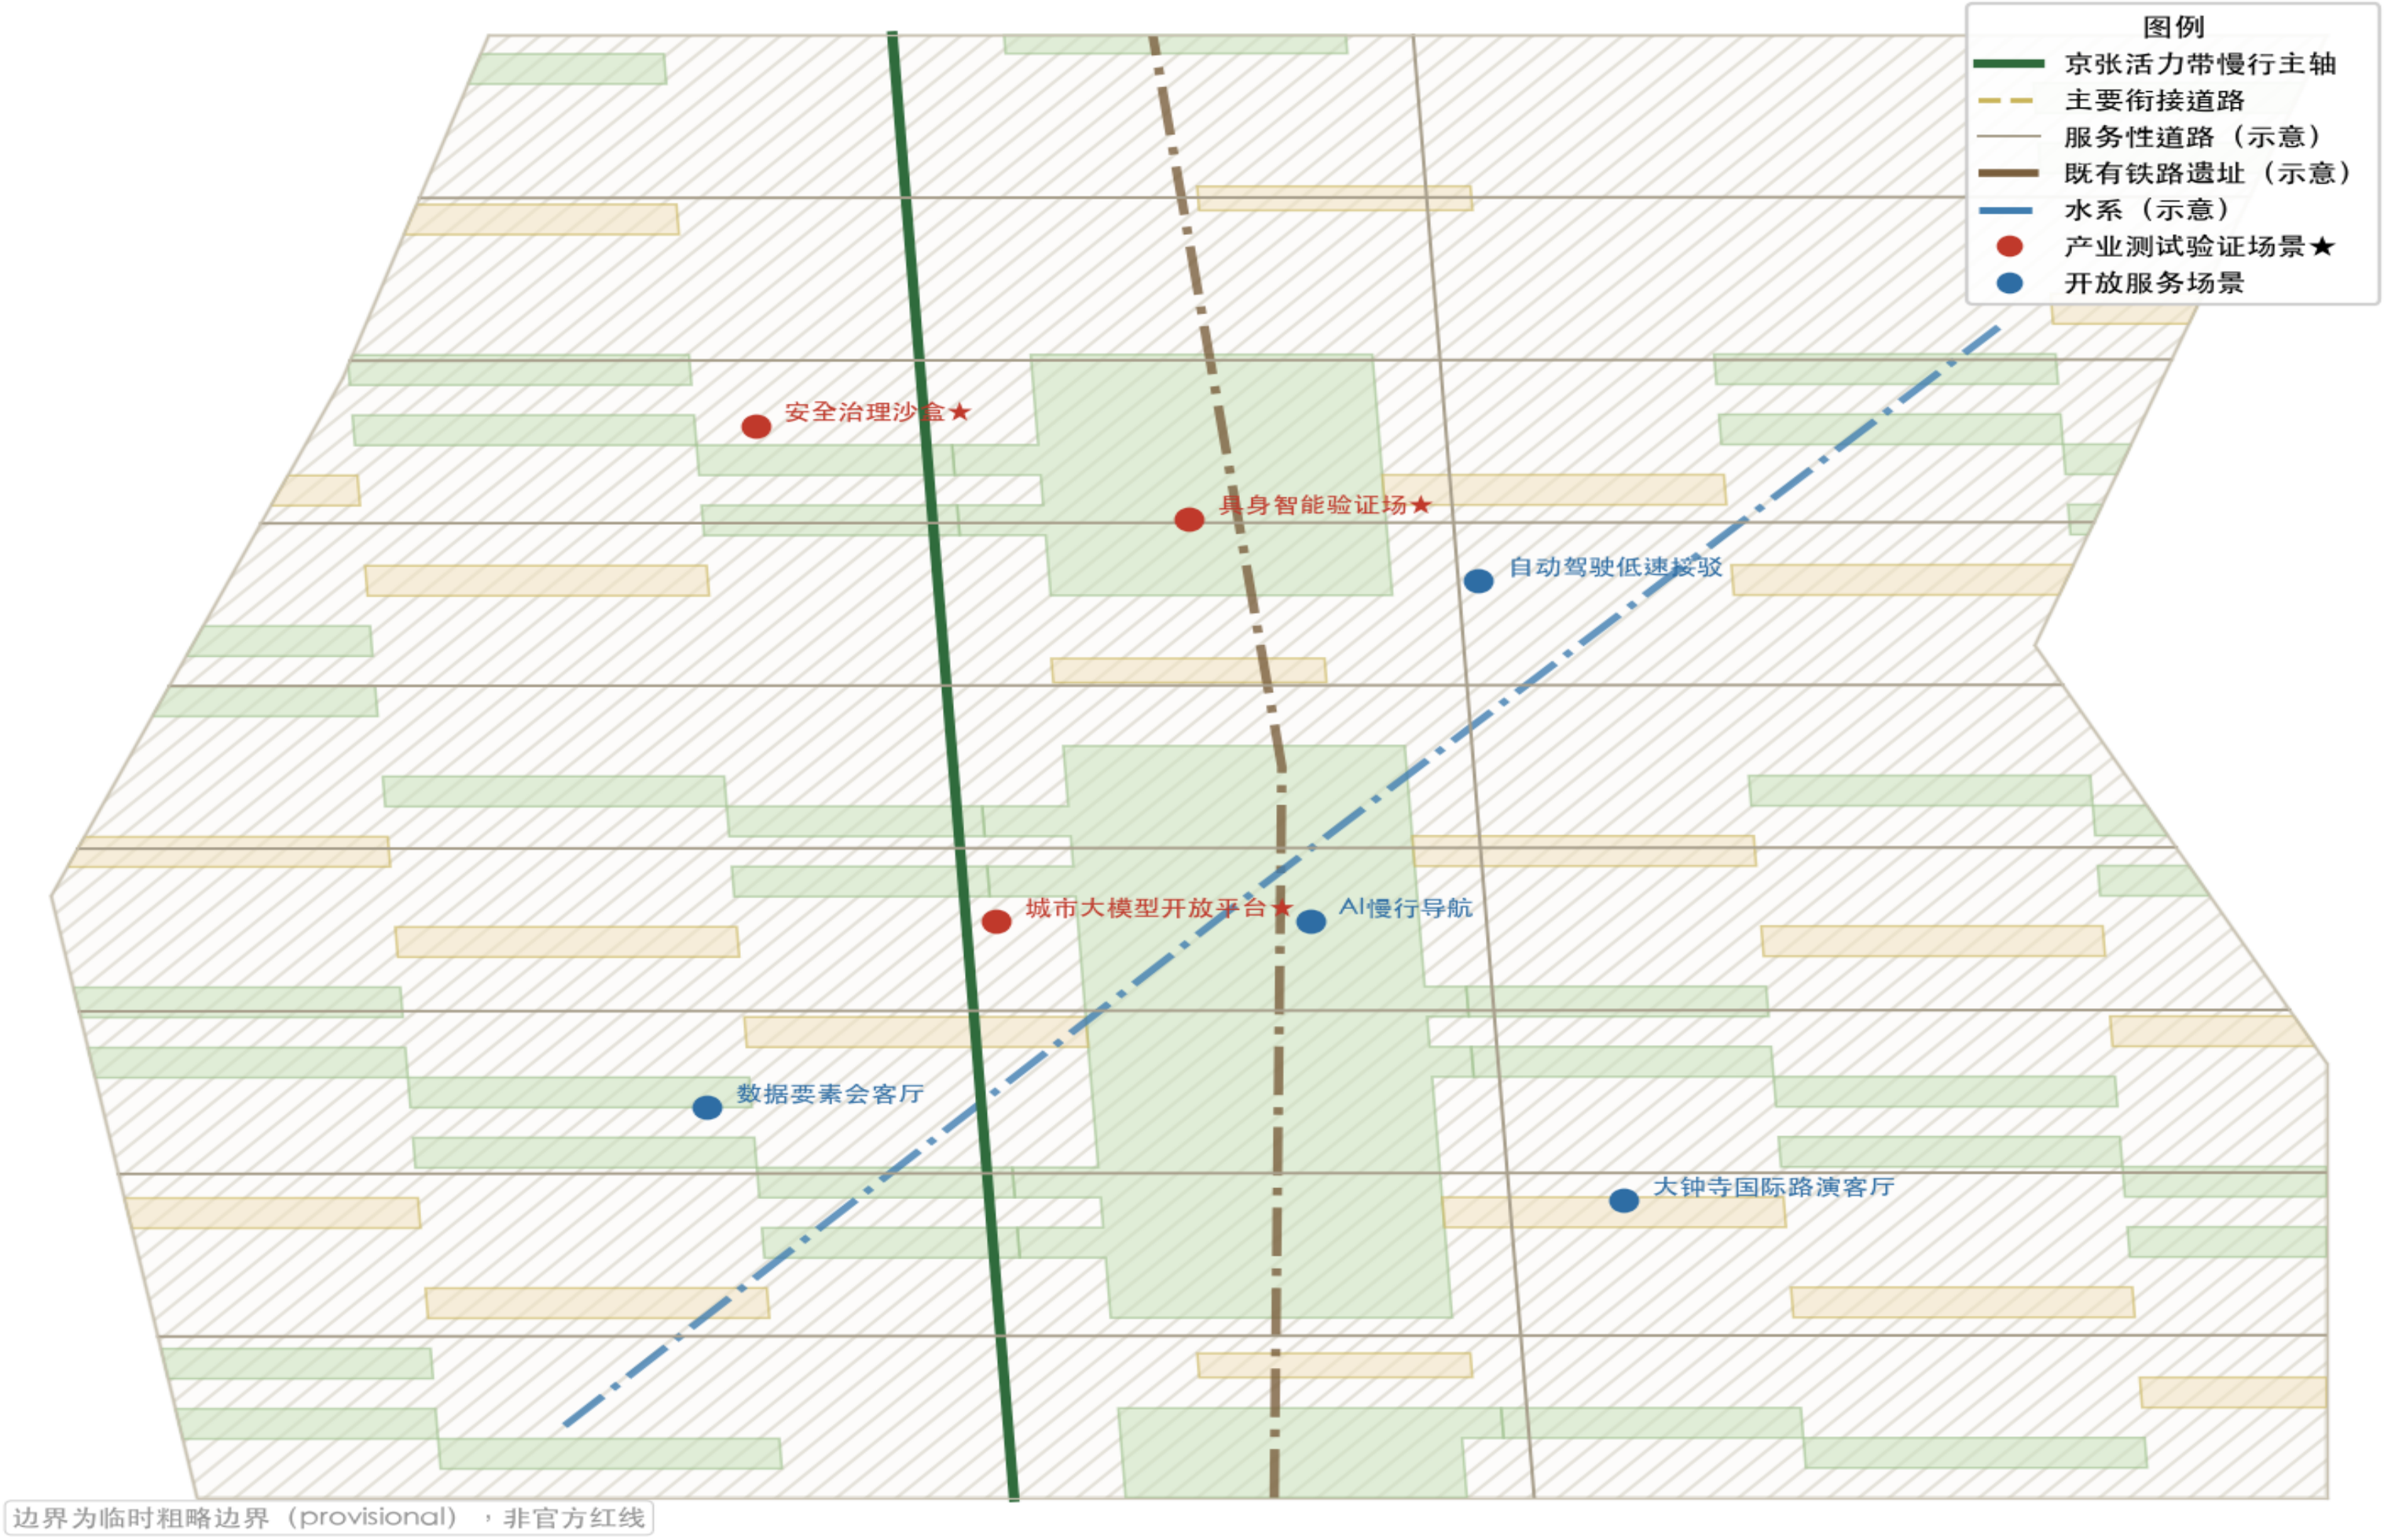

来源：geometry/roads.geojson、green_space.geojson、public_space.geojson、constraints.geojson；铁路/水系为示意线，非官方线位

04 蓝绿空间、公共空间与城市风貌

京张遗址公园活力带 · 三重文化叙事 · 朝圣地标


以京张遗址公园活力带为主轴线，串联白桦公园与防护绿地网络，南北贯通、东西缝合，城市风貌融合京张铁路历史文化、中关村创新文化、AI 新文化三重文化；“京张黄+原点红+芯图绿”基调；“原点◎”导视符号体系，国际传播主题叙事：“From the railway that proved a nation could build its own, to the AI that proves it can create its own.”

AI 朝圣地标（3 个）：① AI 原点纪念碑（A2，原创开源类数字 GitHub 署名）；② 黄天佑—世纪对话广场（活力带）；③ 城市智能体验馆（众智园）。

重点片区	定位	空间功能	AI 产业与运营场景
A1 众智园 (约192.1公顷)	全栈自主创新·花园街区	清河智能创新界面·产业展示与对外交通	自主模型测试·标准工作坊·安全治理沙盒·具身智能验证场
A2 4维点社区 (约104.3公顷)	近校成果转化·人才社区	校区—街区—街区慢行融合·开源发布厅	AI原点纪念碑·人才特区
A3 大钟寺 (约72.0公顷)	城市智能经济·国际交往	大钟寺站四家限步行连通·商业服务更新	智能终端与内容消费·数据要素会客厅·国际路演

三处重点区域详细设计（规划综合实施方案深度示意）

三核定位差异 · 空间联系 · 项目抓手 · 风险条件（全部为概念建议）

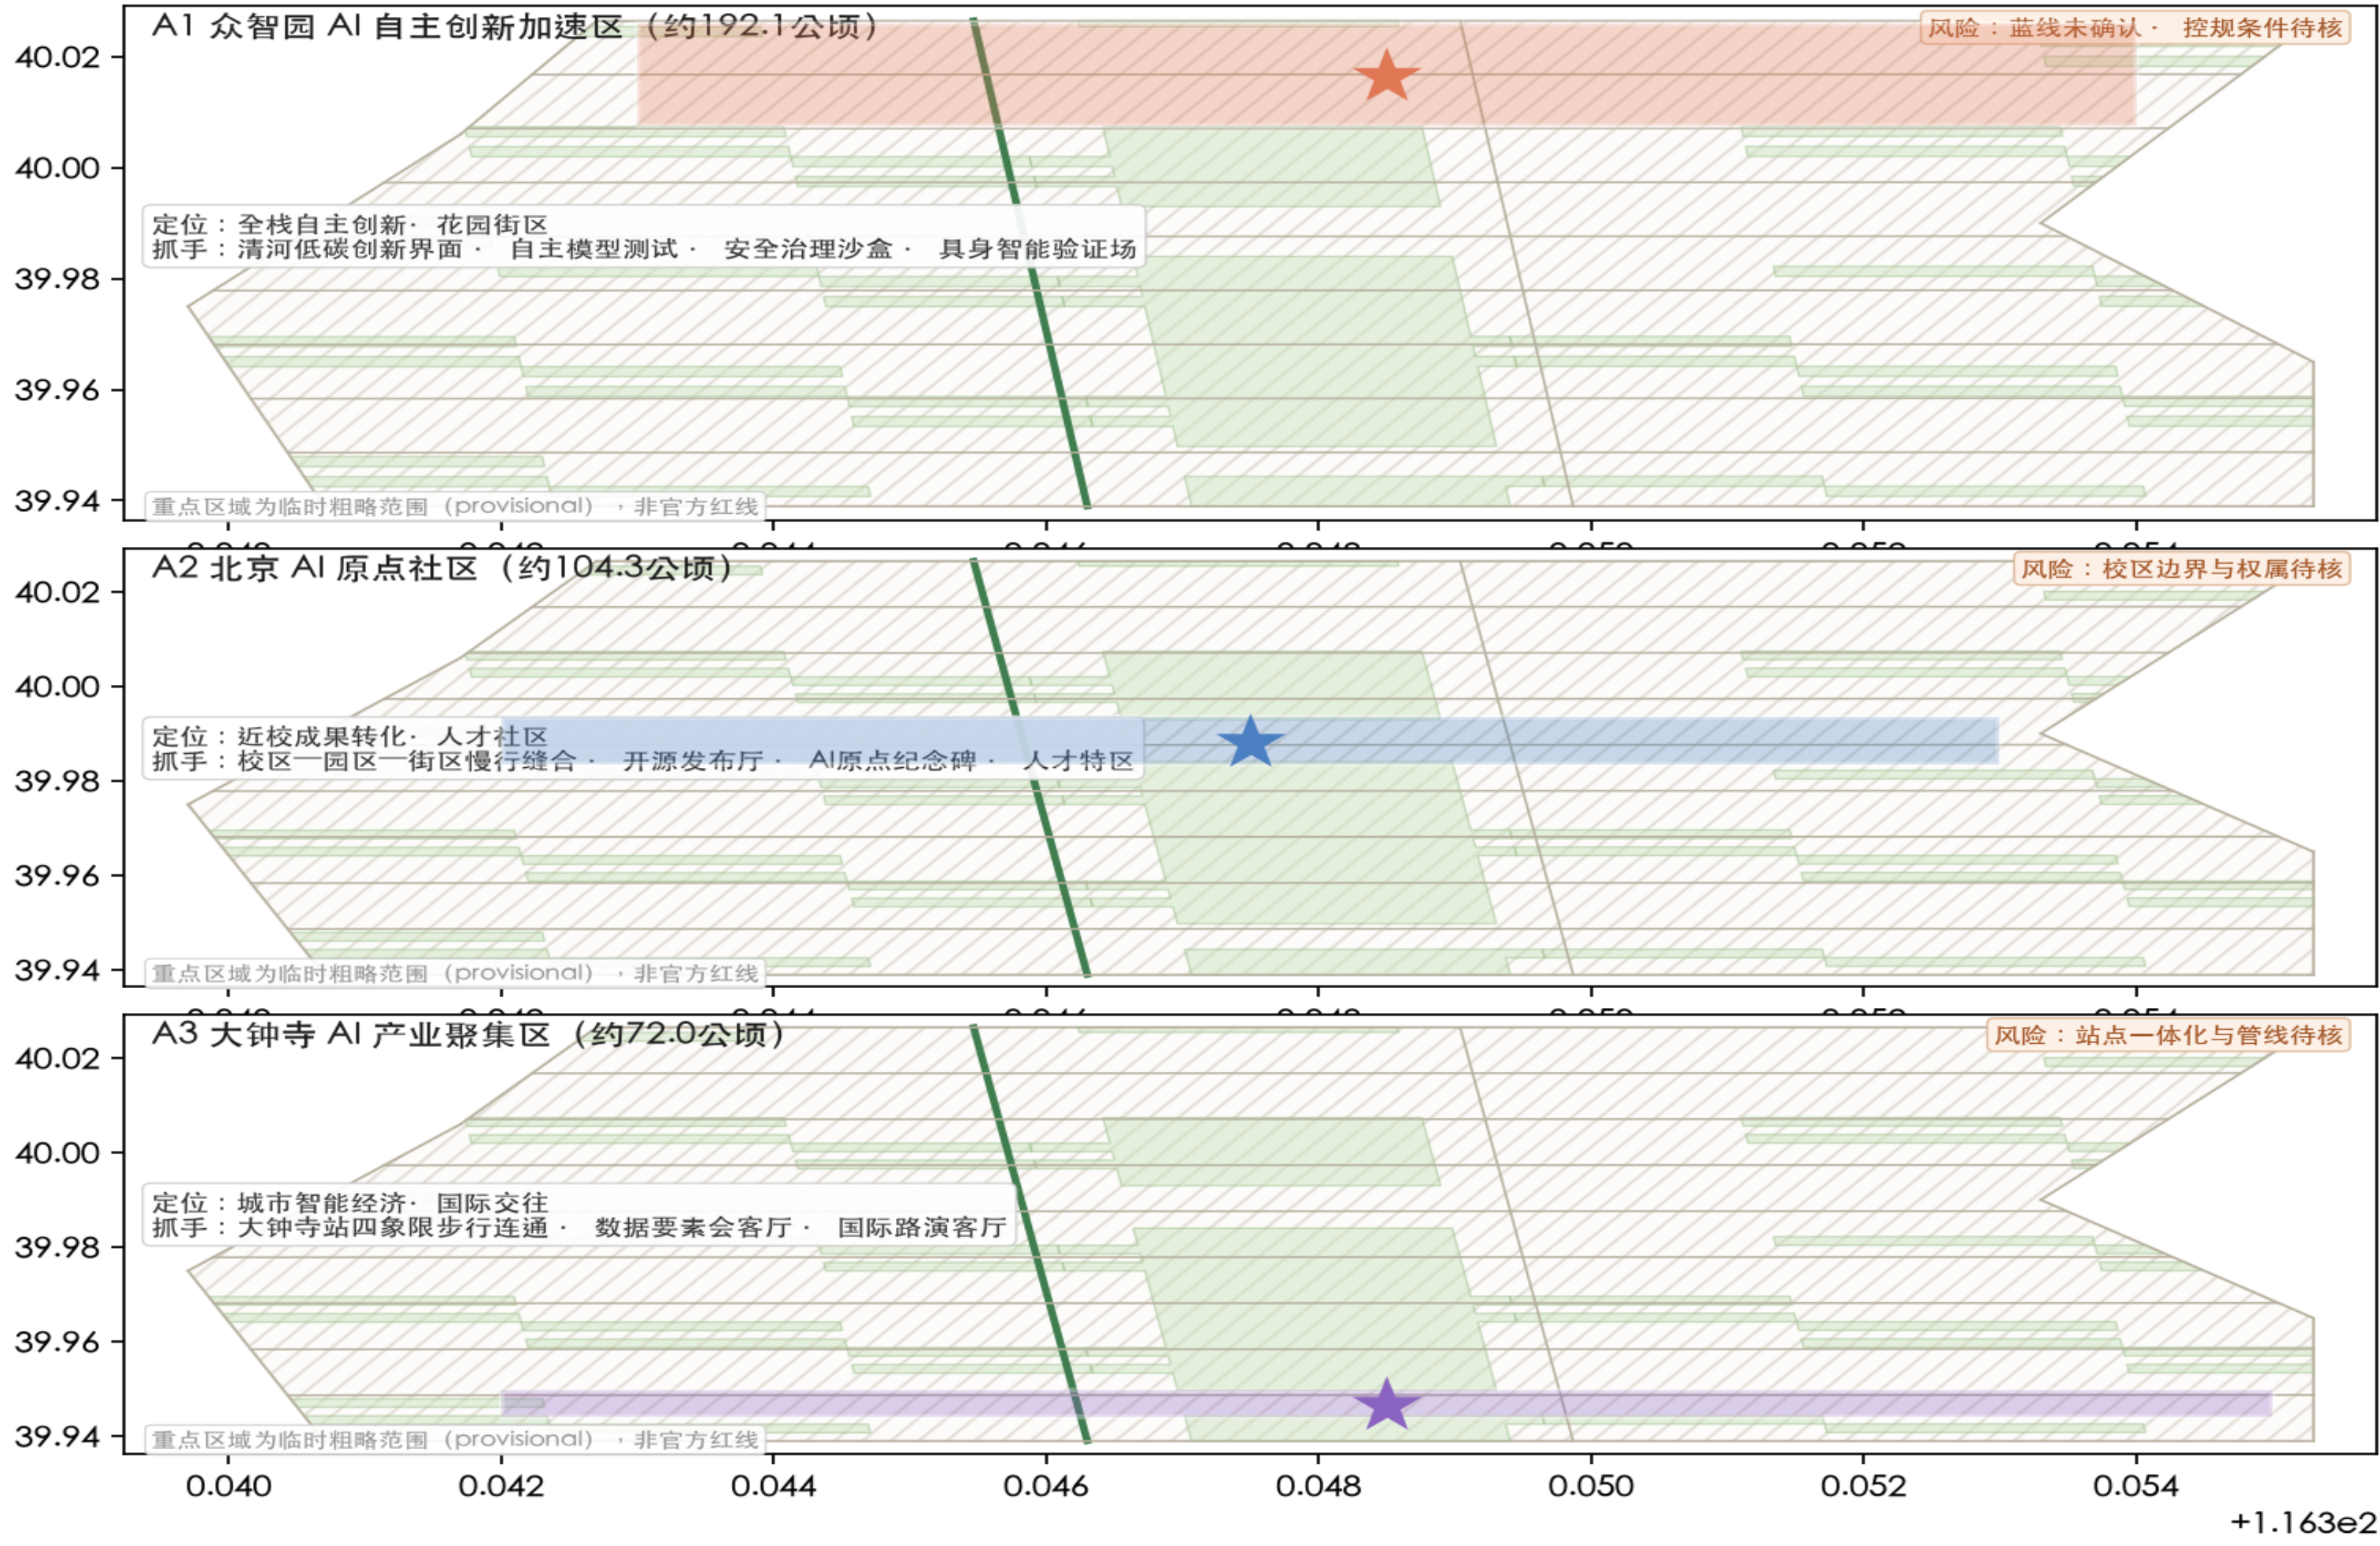

来源：geometry/key_areas.geojson (PROV-KEY-001/002/003)；边界为临时粗略范围

06 AI 场景、分期实施与运营

12 张场景卡 · 三阶段实施 · 全球活动体系

场景卡 12 张（含 3 个产业测试验证场景：安全治理沙盘、具身智能验证场、城市大模型开放平台） · 用户画像 6 类 · 分期：近期[2026-2028]三核强点与活力带断点缝合→中期[2029-2032]成片更新与站城一体→远期[2033-2035]金带贯通与全球场景运营 ·

长期运营（Agent-G）：年度京张 AI 开源节/城市智能体挑战赛/AI 挑战赛；开发者社区运营机制（以本次 GitHub 开源征集为种子）；场景开放运营平台（场景即服务）；国际路演客厅*人才落地通道的指引转化机制 ·

核心指标复算与证据链

所有 known 指标可由 geometry/*.geojson 在 EPSG:4548 复算；unknown 指标给出原因与前置条件

总体设计范围面积（复算）

11,412,825

m²

公告面积（官方声明）

11,400,000

m²

绿地率（设计建议）

0.210

比值

公共空间比例（设计建议）

0.057

比值

建筑基底面积（示意）

780,765

m²

容积率（待控规）

待官方确认

官方控规条件缺失 → unknown

geometry/*.geojson

EPSG:4548 复算

metrics.json

visual/index.html
(data-metric)

self_check.json

自检状态：PASS

指标与合规：known 指标均可由 GeoJSON 在 EPSG:4548 复算；合规矩阵覆盖公告 1.3/1.4/1.5 与 agent1-6；标准矩阵覆盖全部强制专业标准；设计深度核心项全部 complete · 所有空闲落地建议均为概念建议 ·

边界说明：本方案使用临时模糊边界（provisional） · 非官方红线；官方模糊边界发布后需统一复算 ·