



01 MASTERPLAN ATLAS

Nine kilometres folded into three urban plans: built works, public plans and this proposal


01 NORTH Zhongzhiyuan + Xiaoyuehe

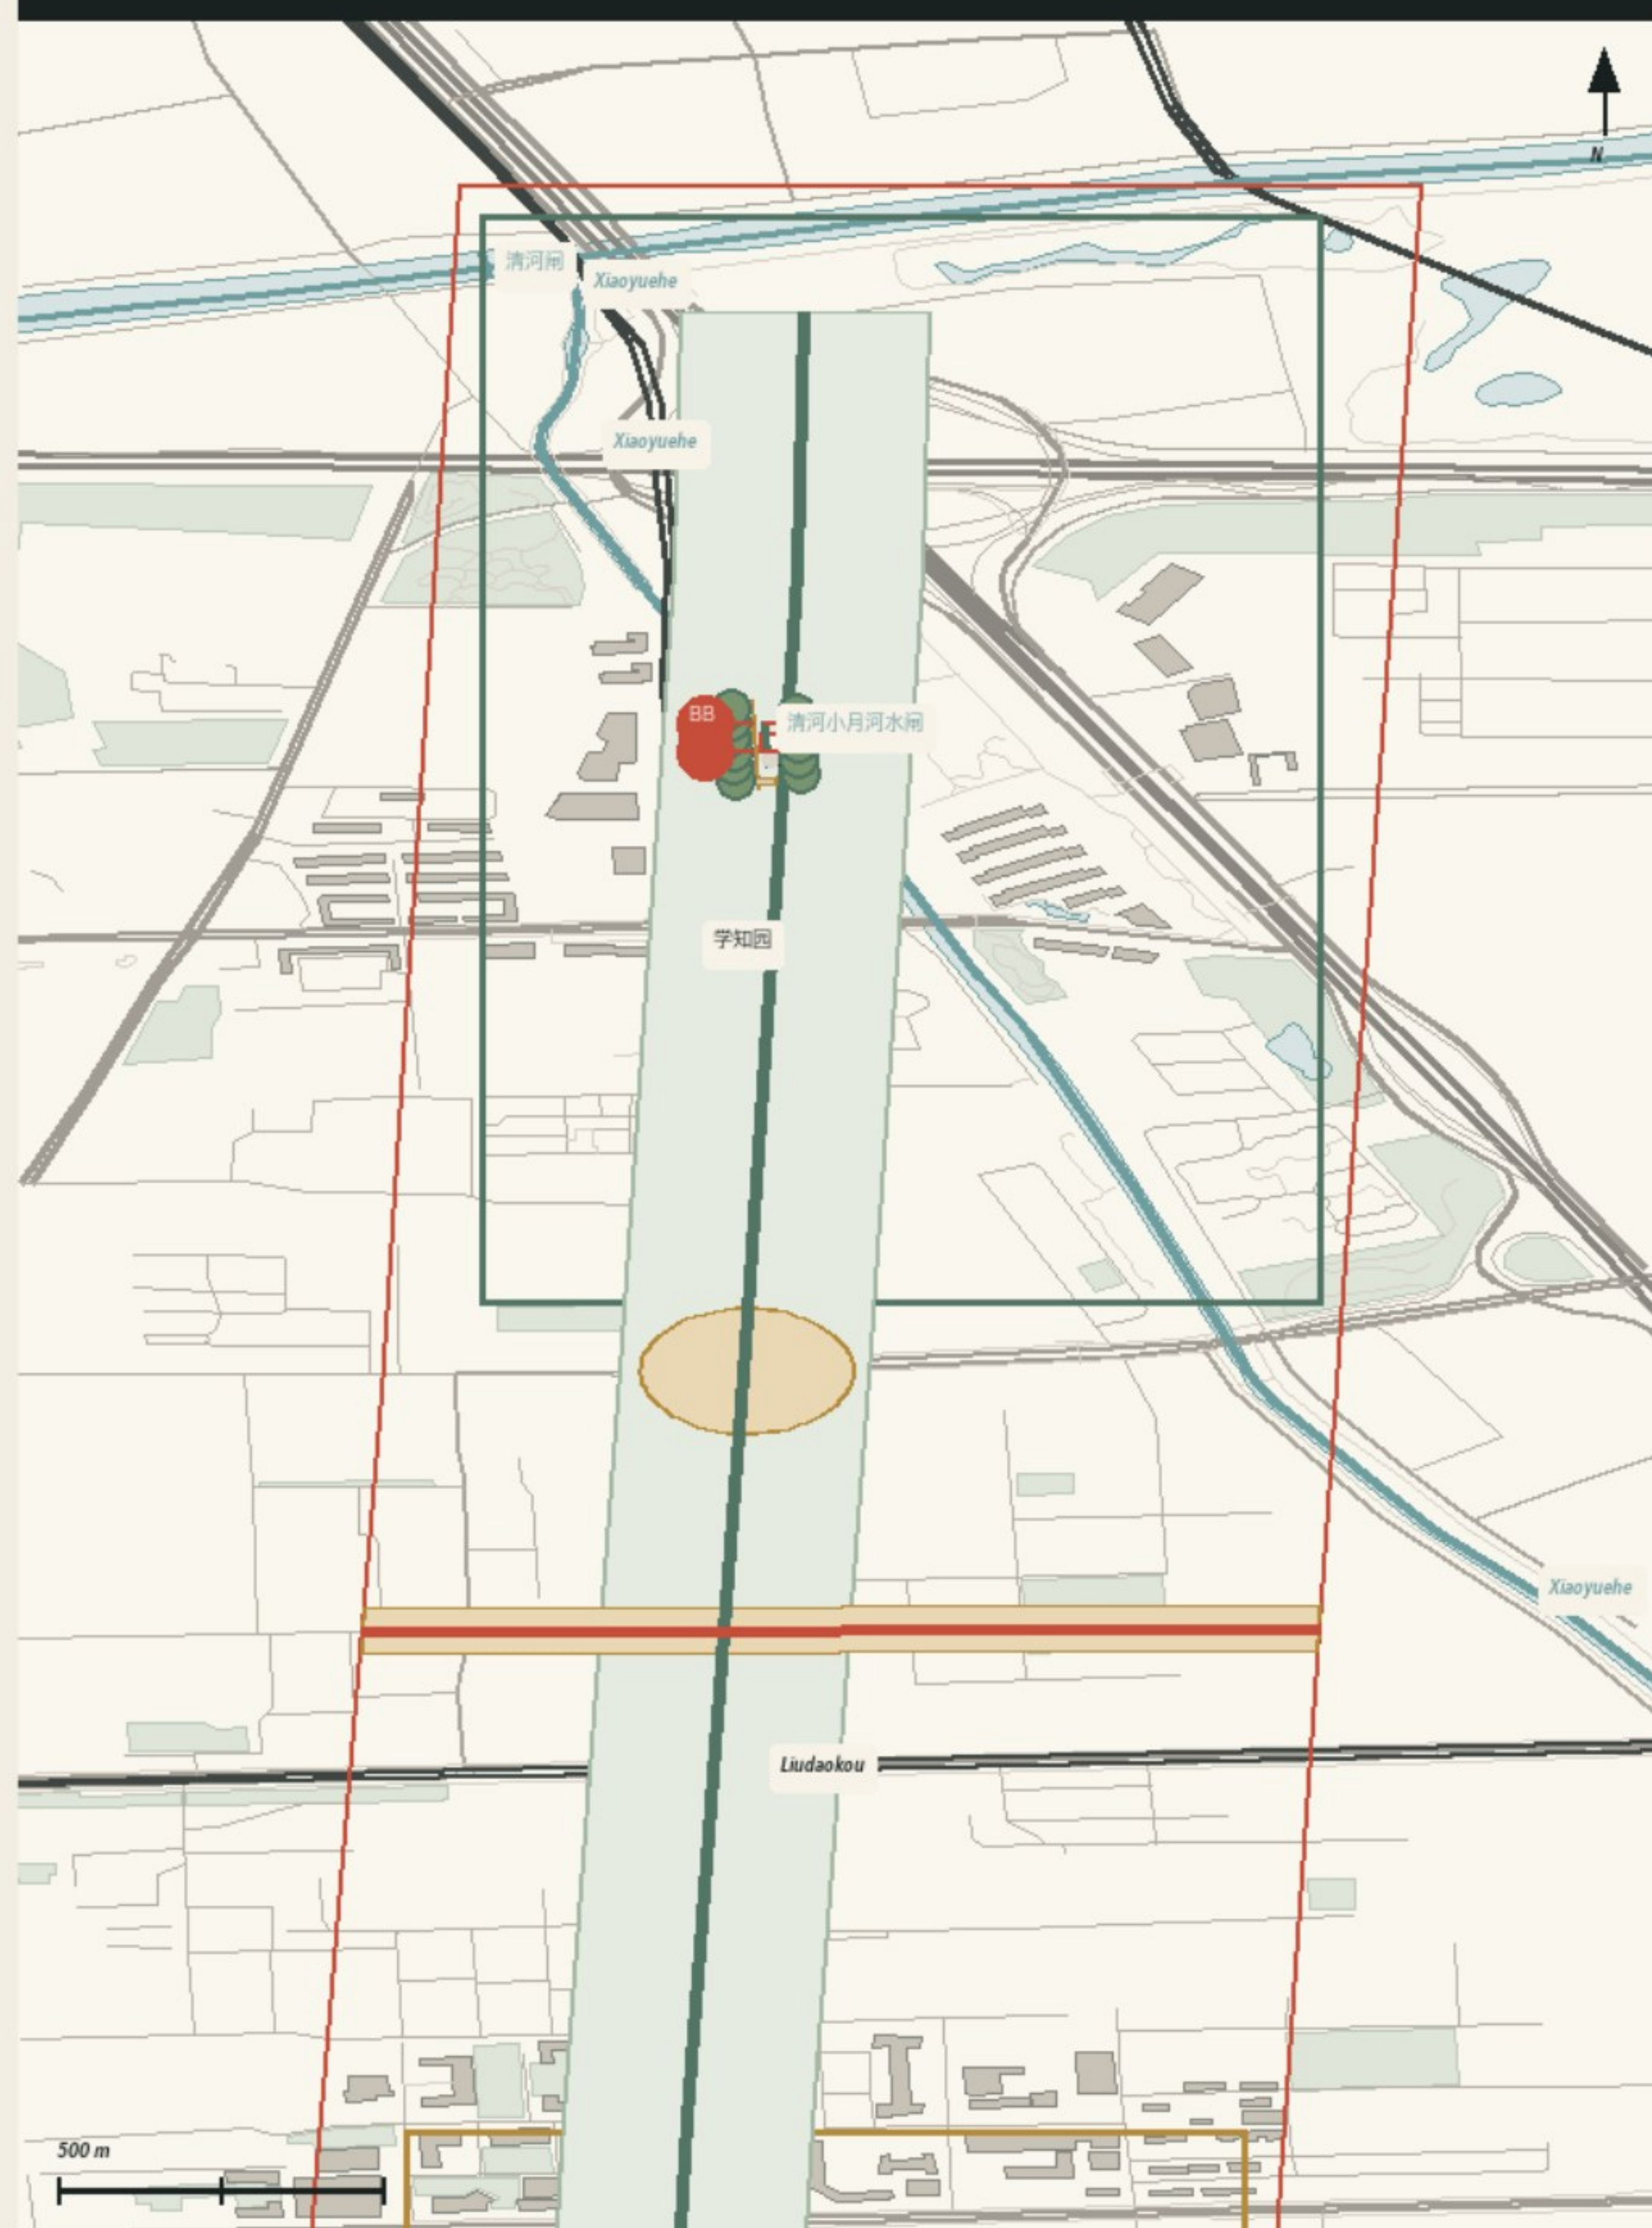

02 CENTRE AI Origin + Xueyuan Bridge

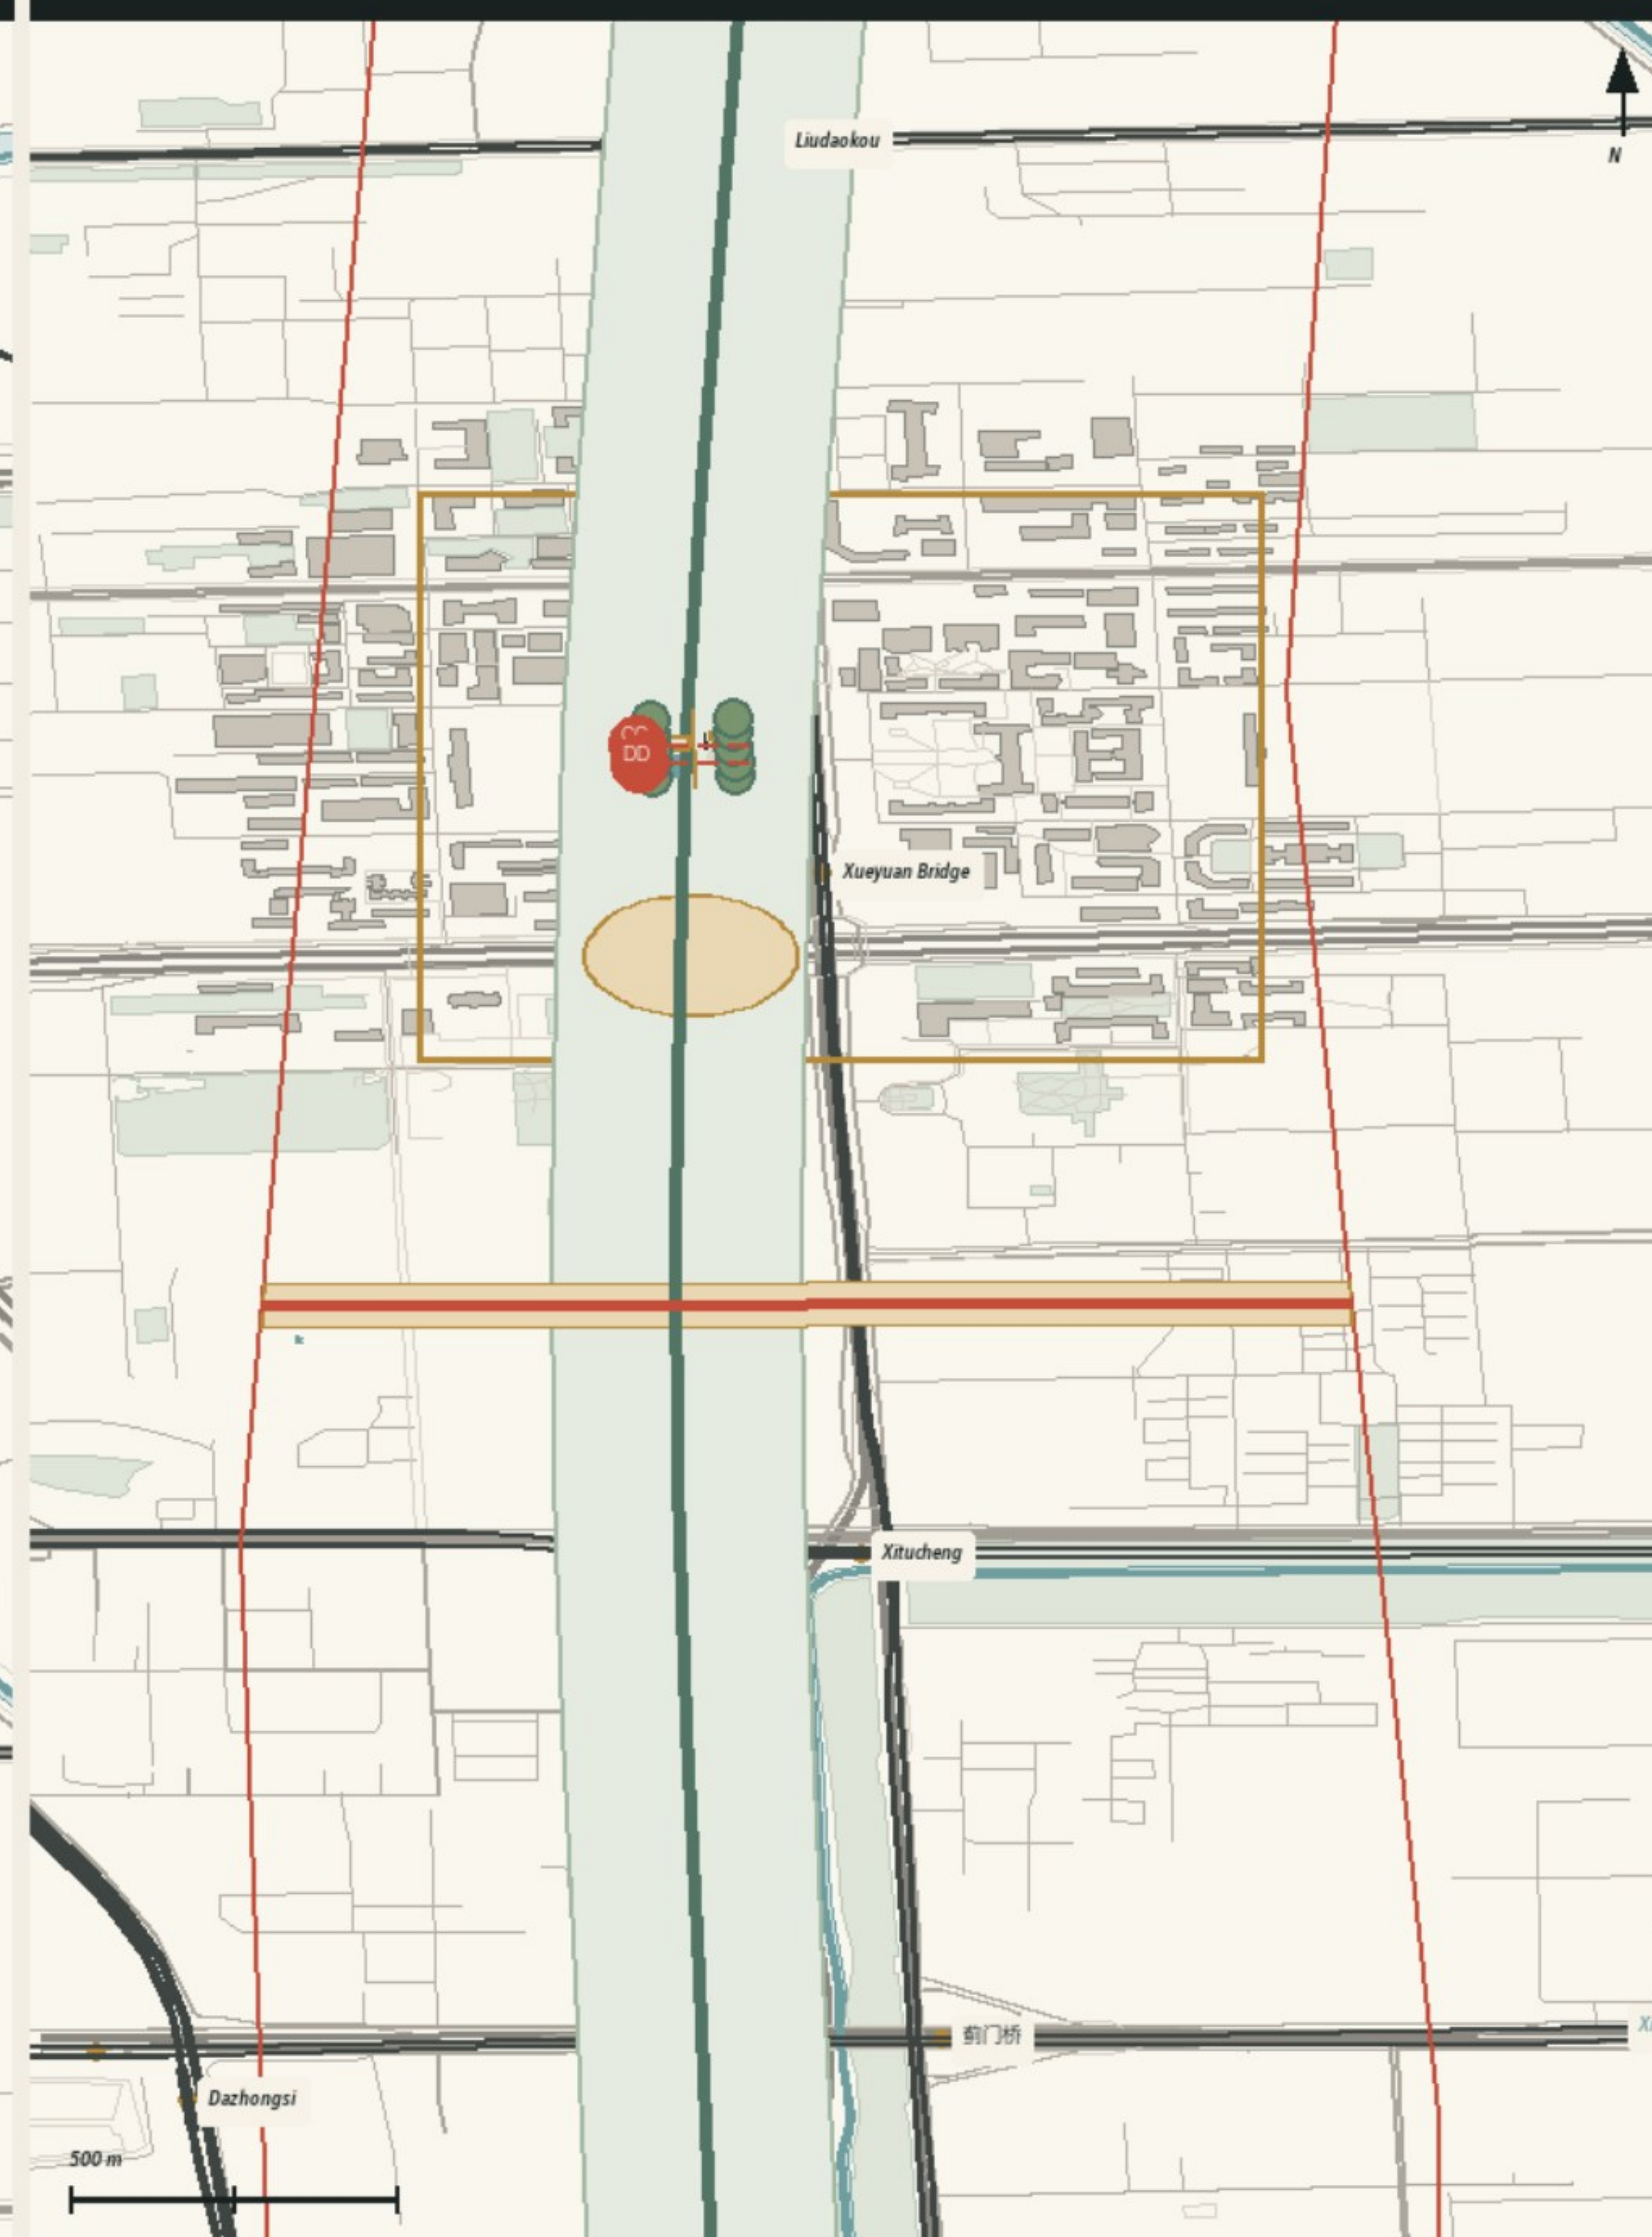

03 SOUTH Dazhongsi + Jiaotong University

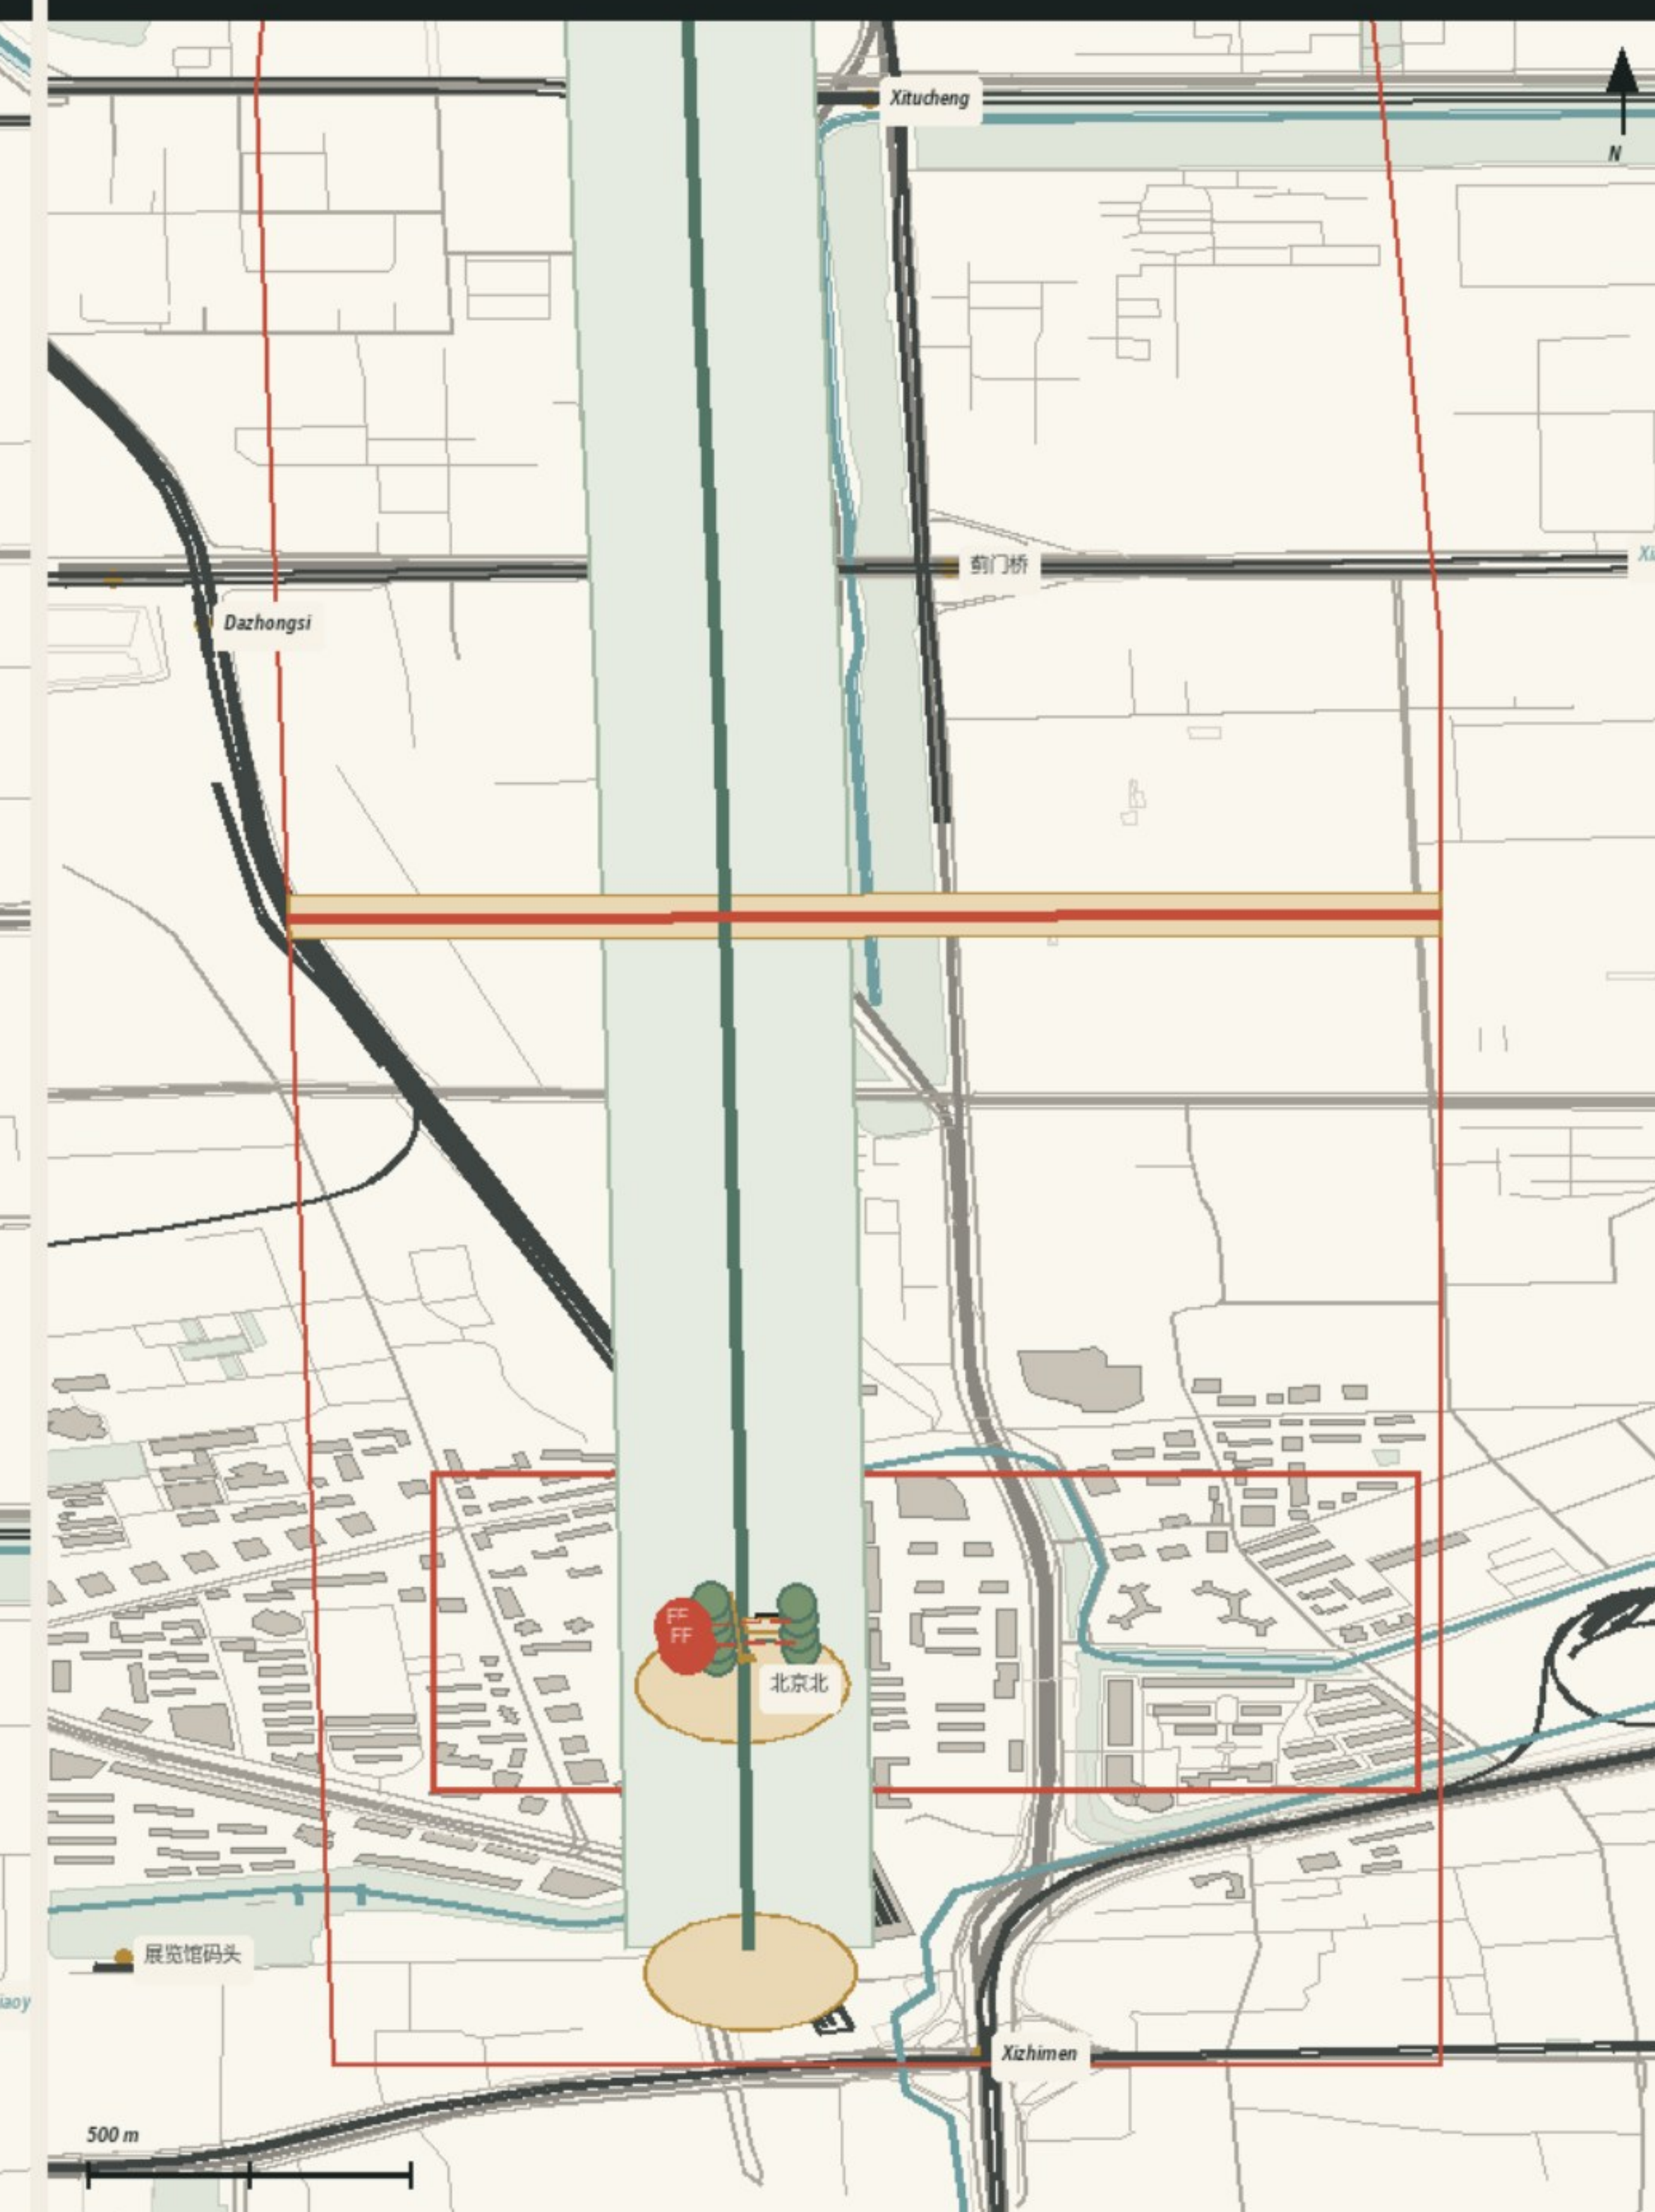

CONCEPT DESIGN PROVISIONAL BOUNDARY OSM FOR CONTEXT ONLY


© OpenStreetMap contributors ODbL 1.0




03 THREE KEY AREAS

Plans, cut lines and everyday edges at the same scale


01 Zhongzhiyuan Test Court

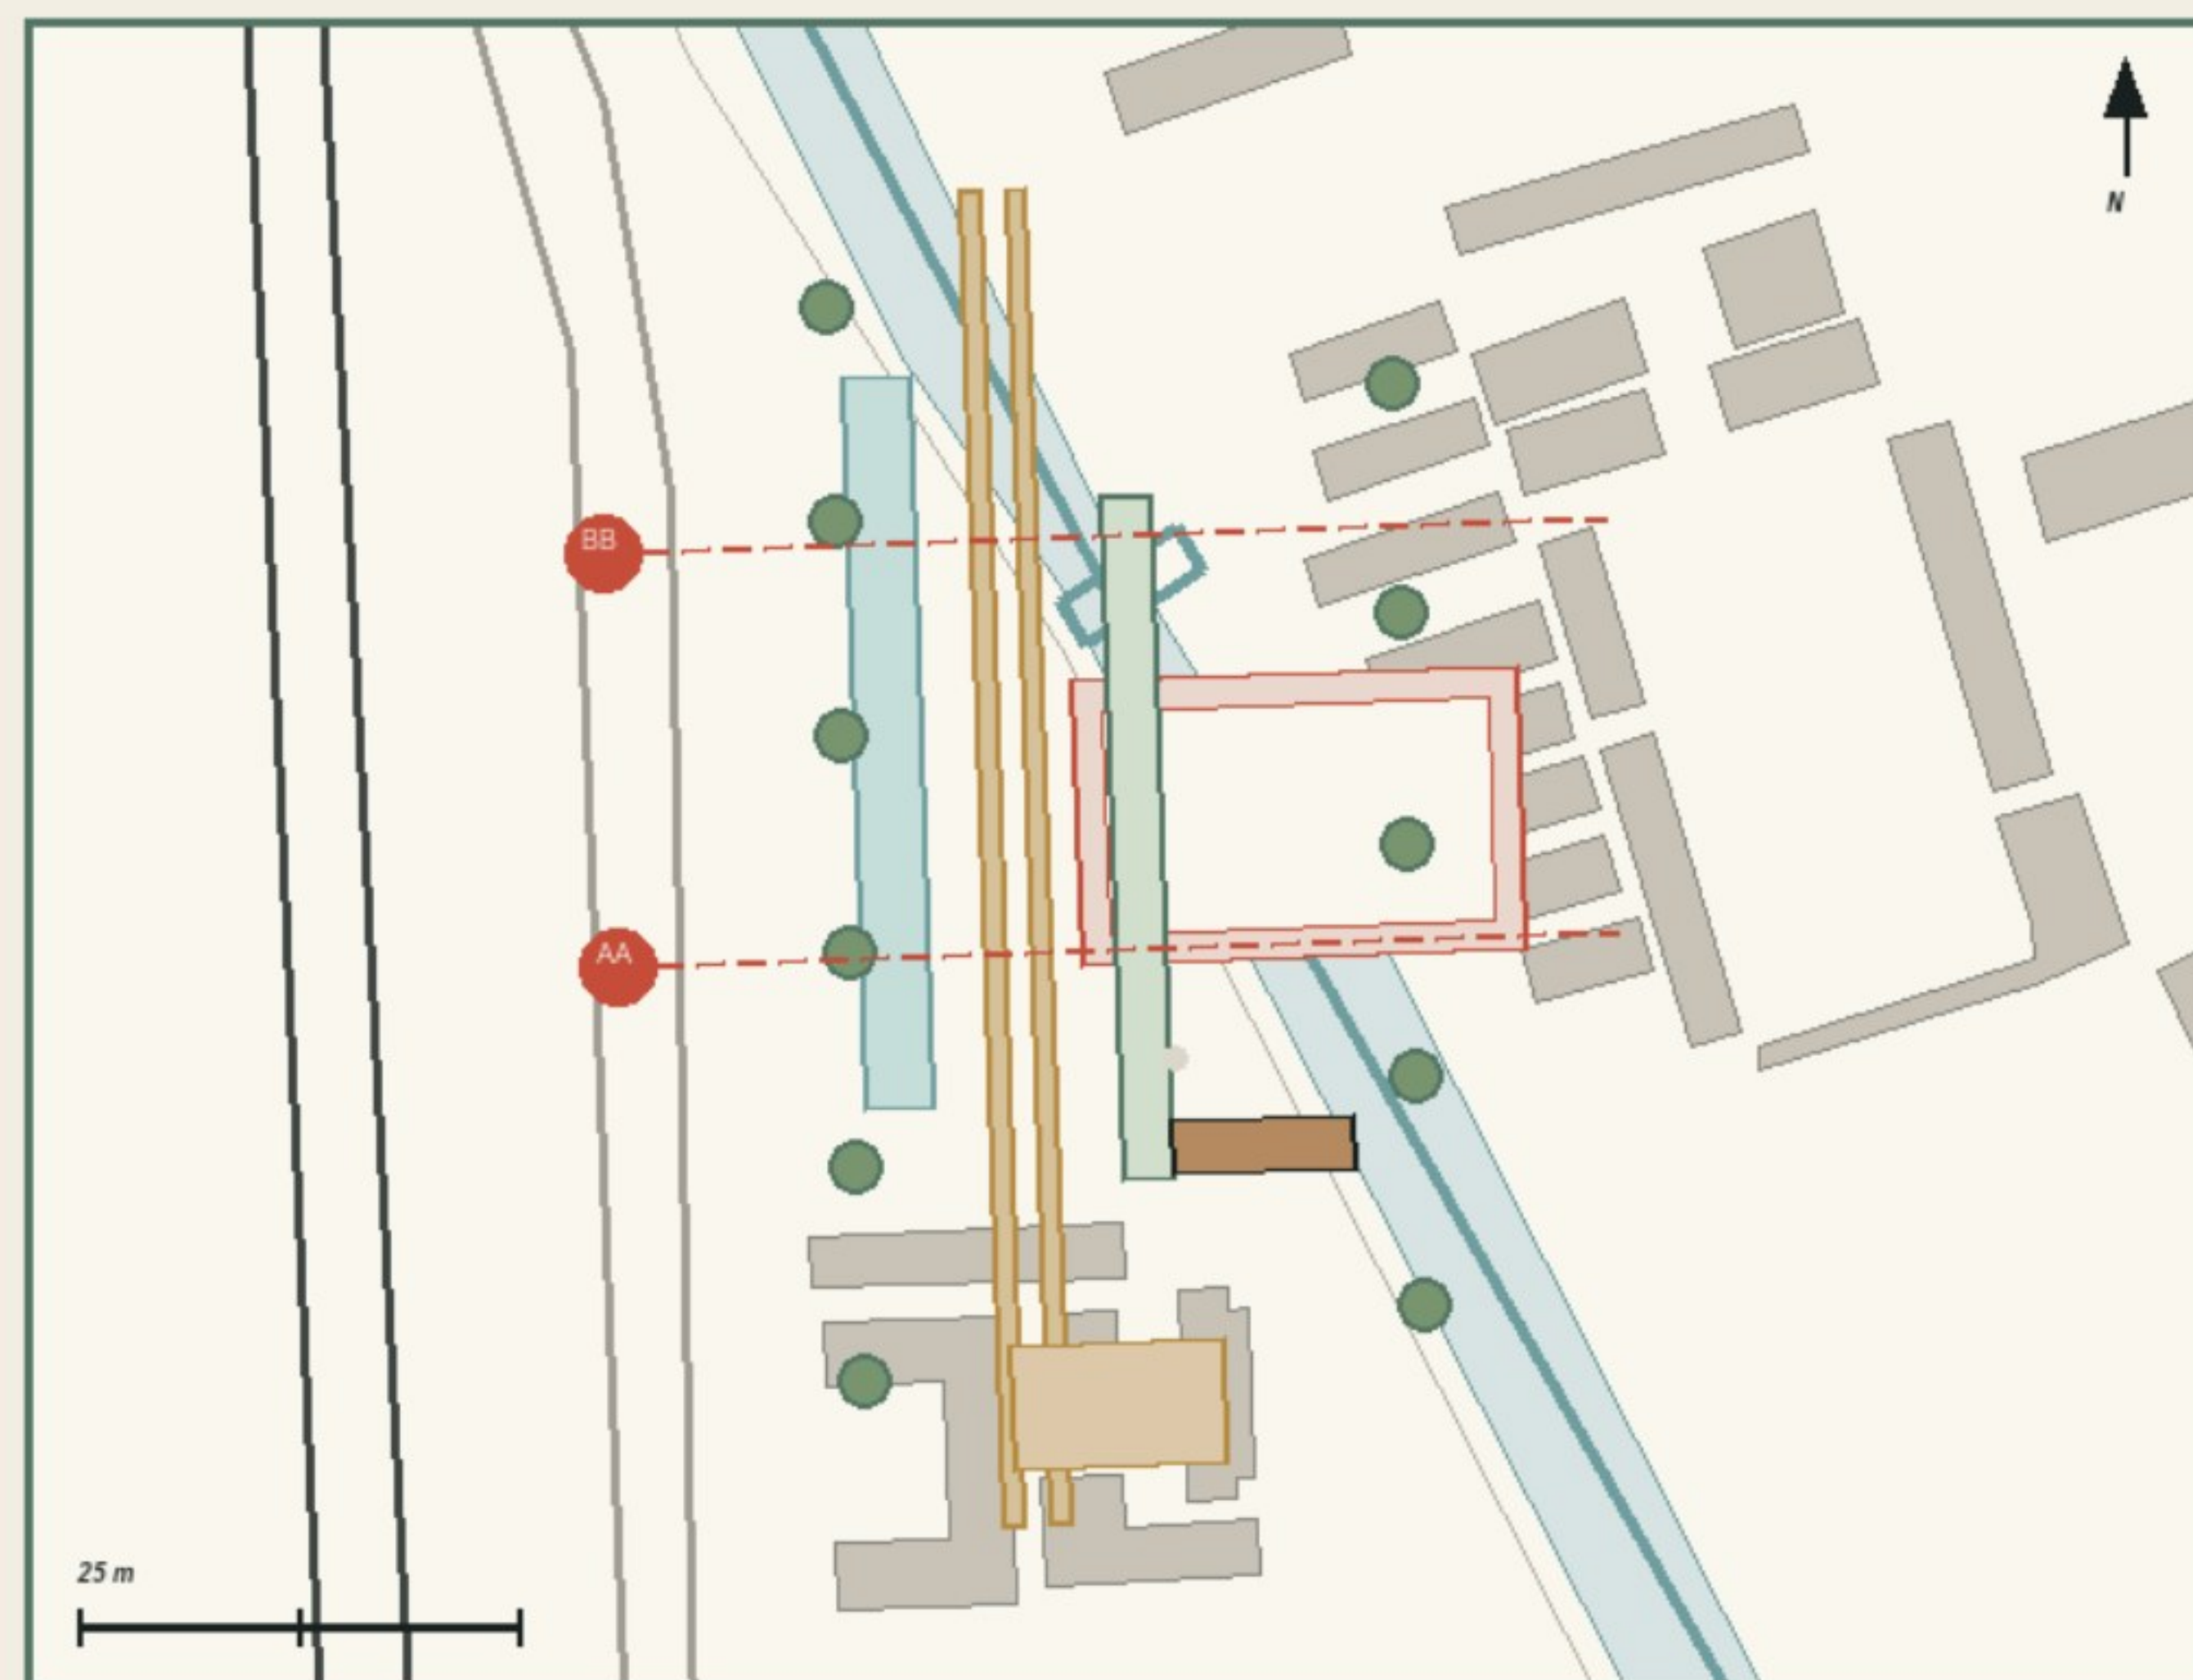


AA Public edge at the test court

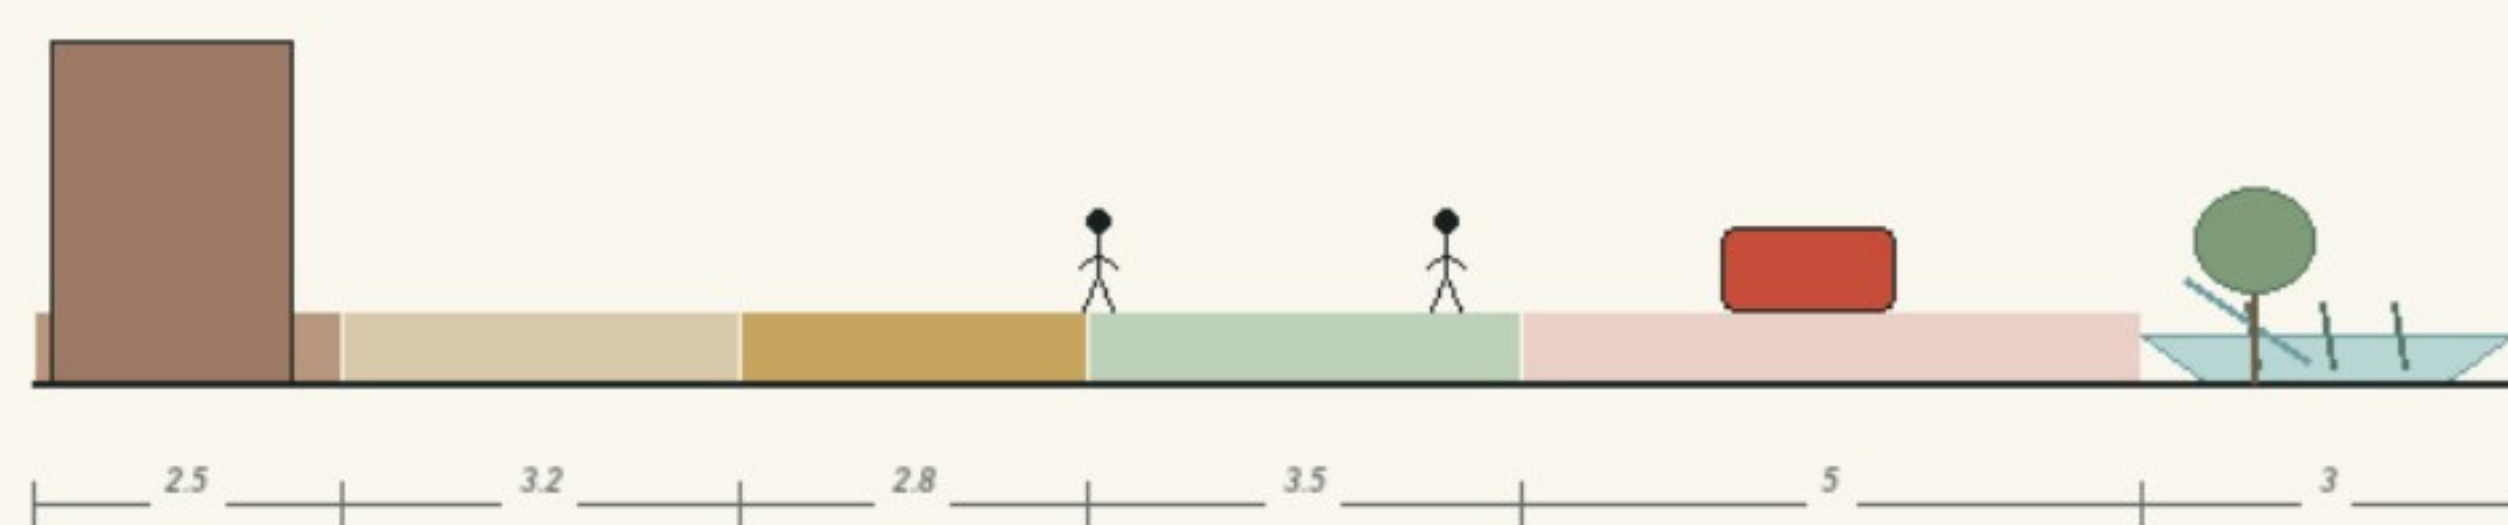


BB Xiaoyuehe link

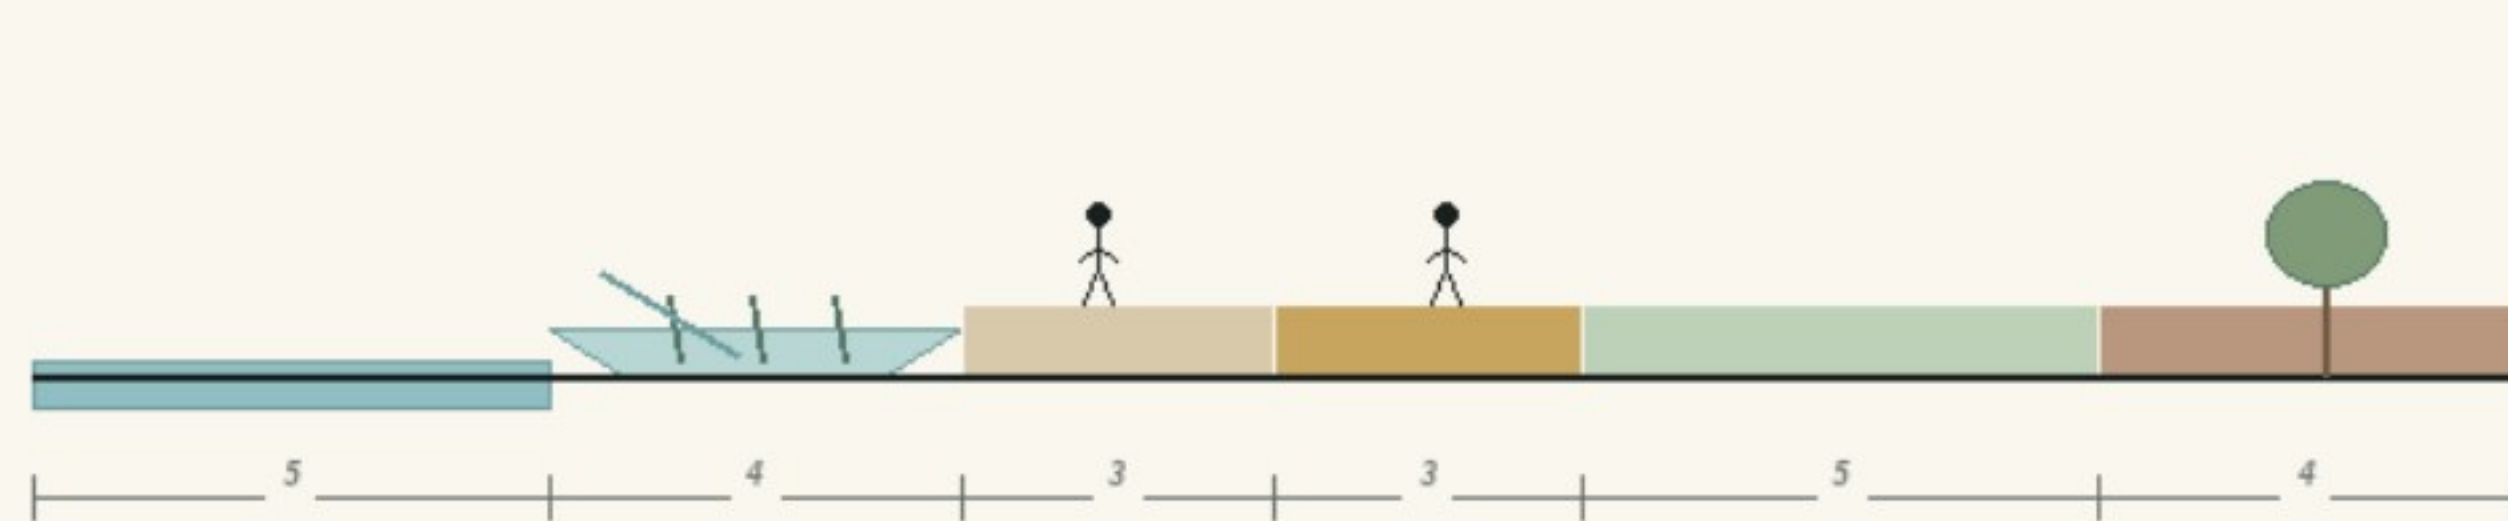


02 AI Origin Service Court

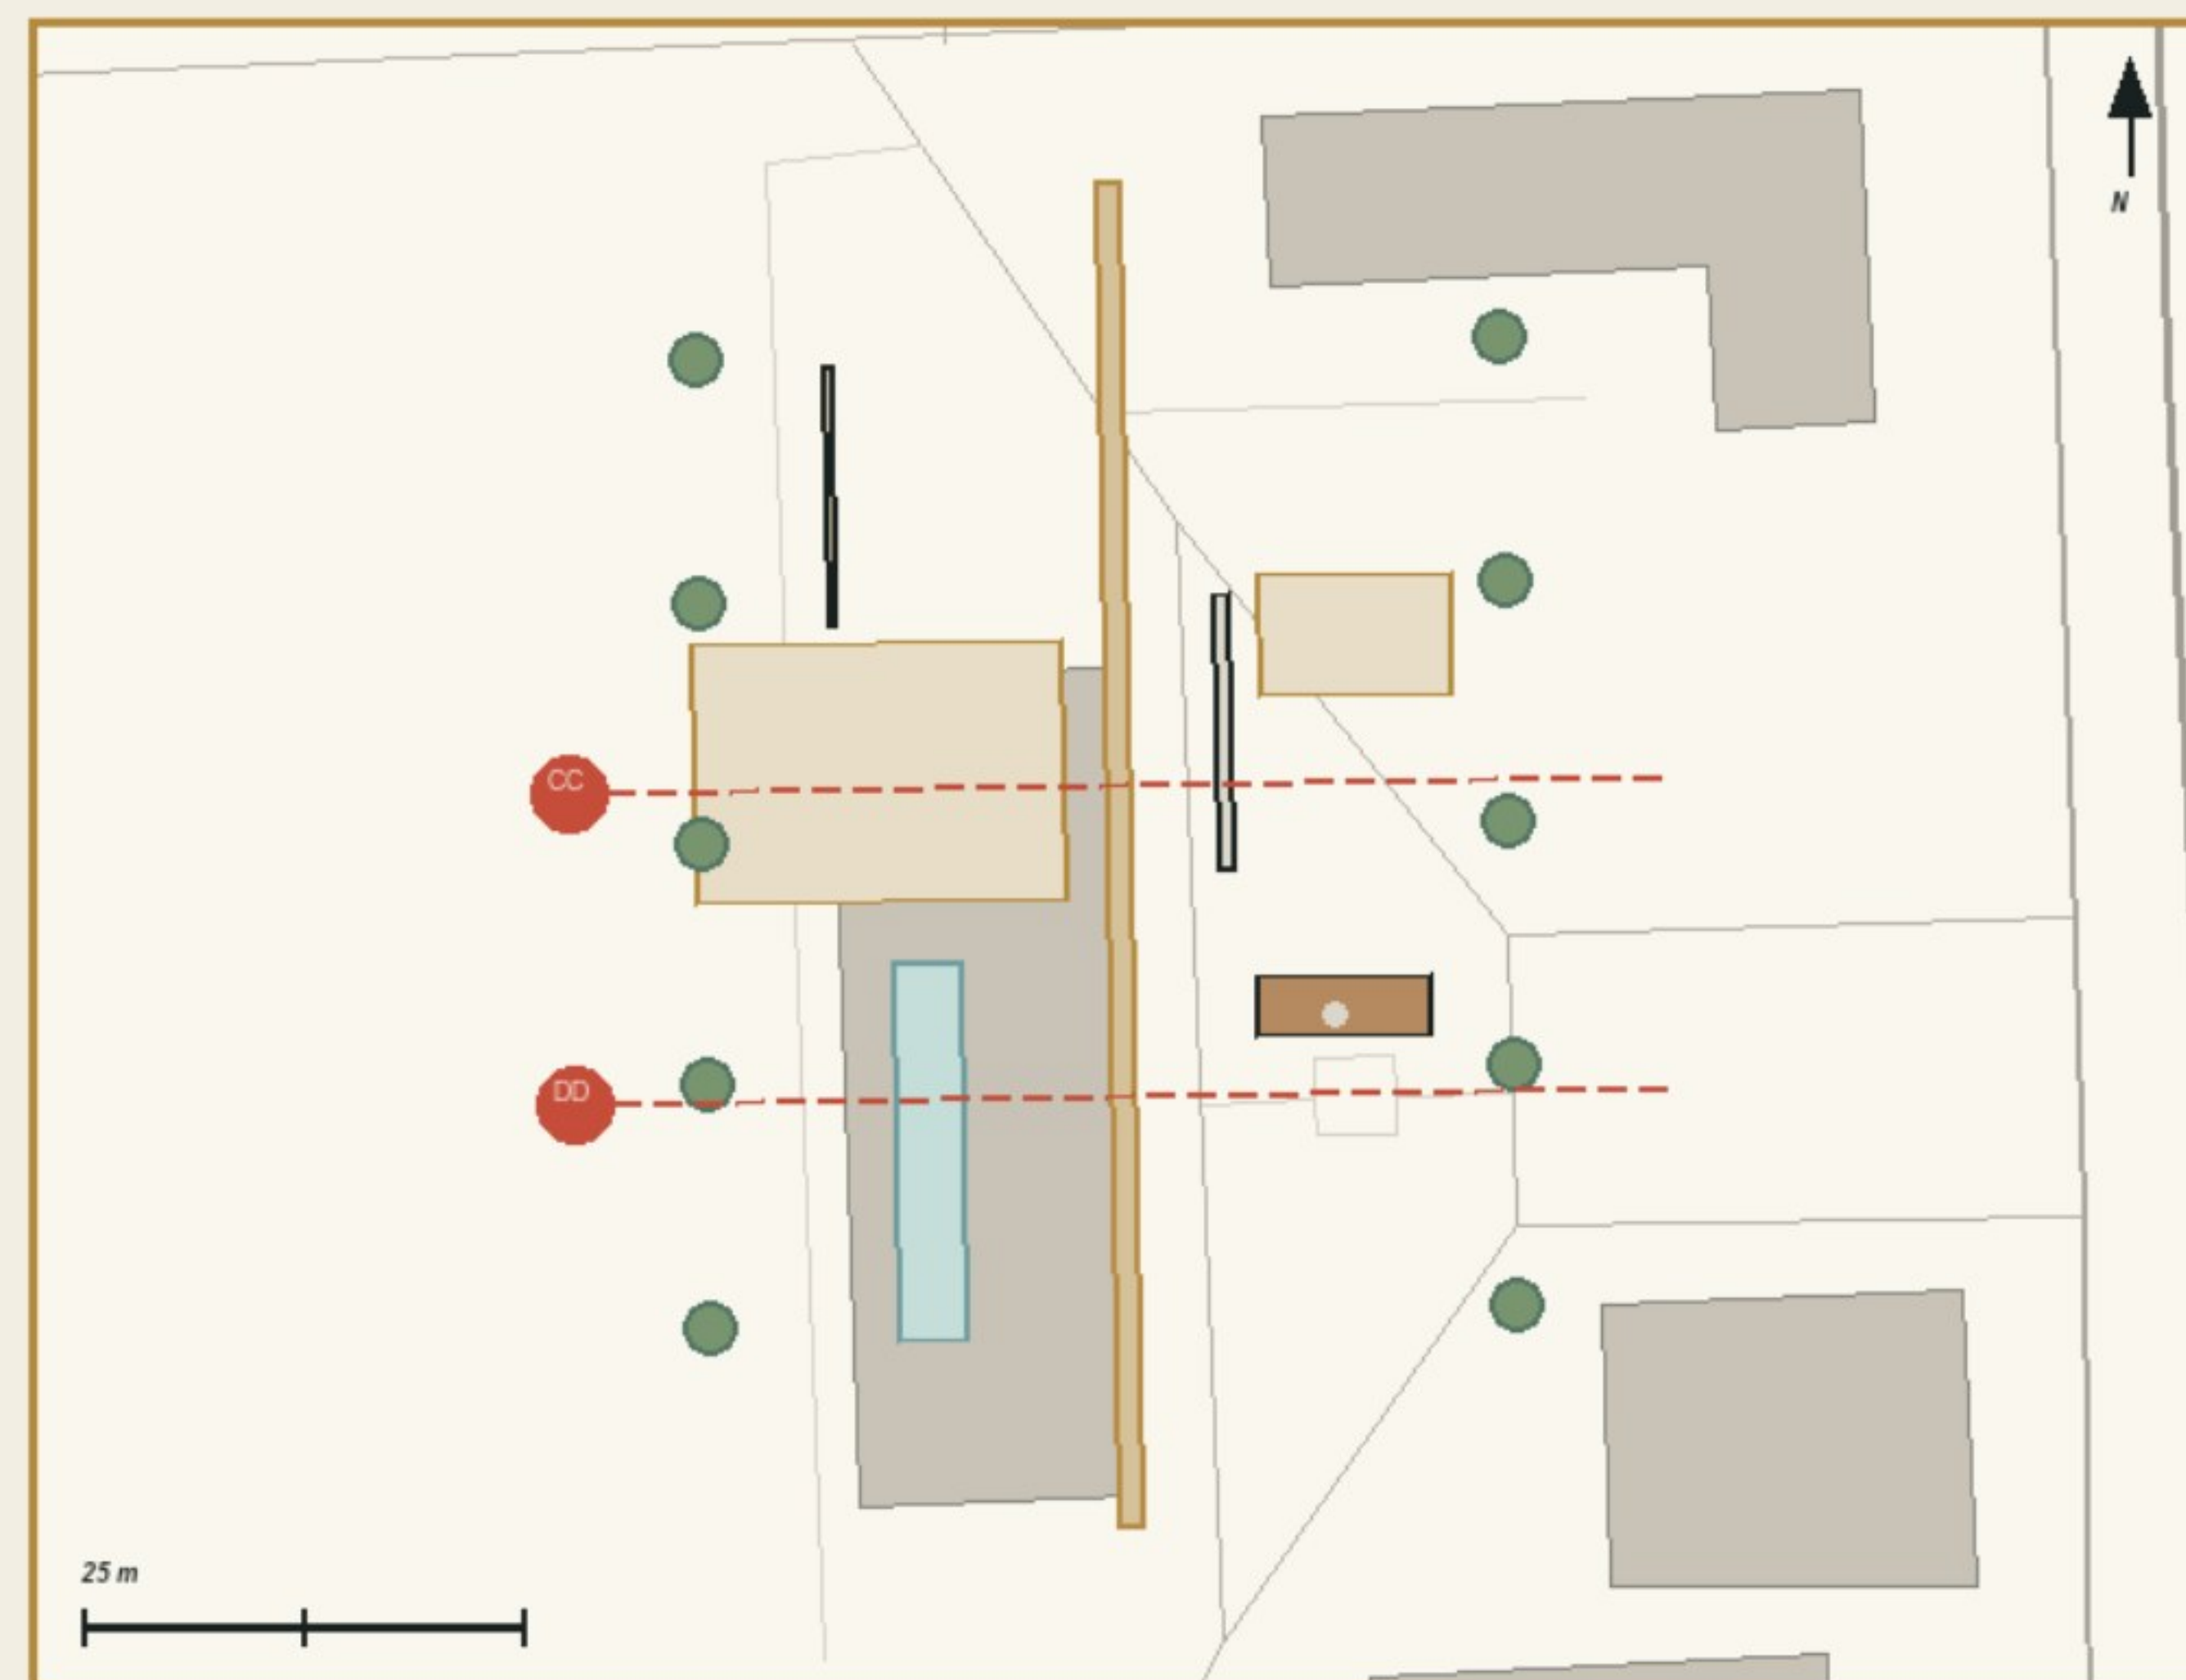


CC Old forecourt

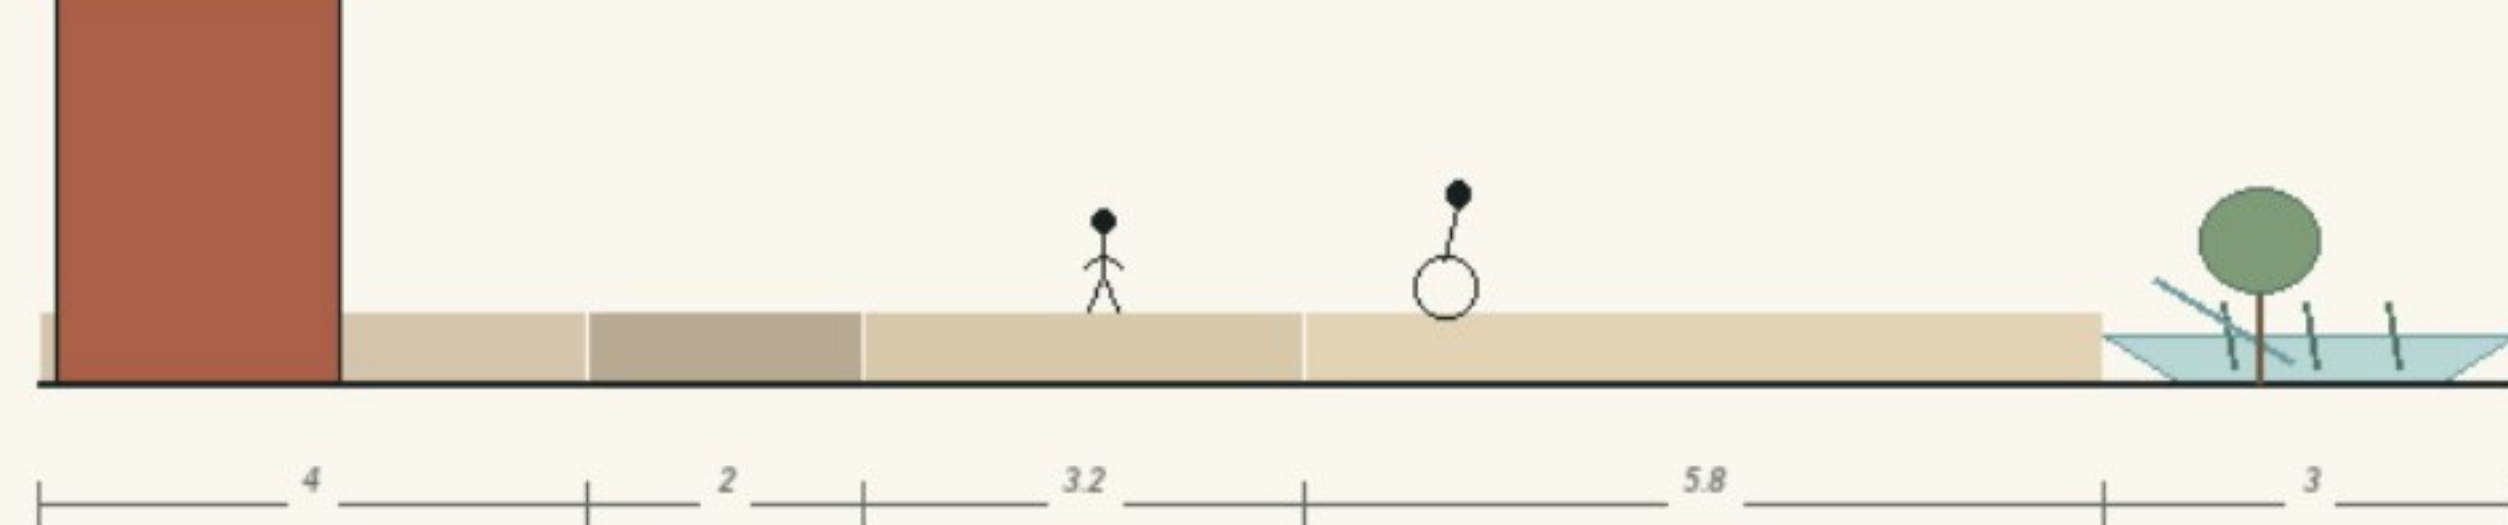


DD Service street court

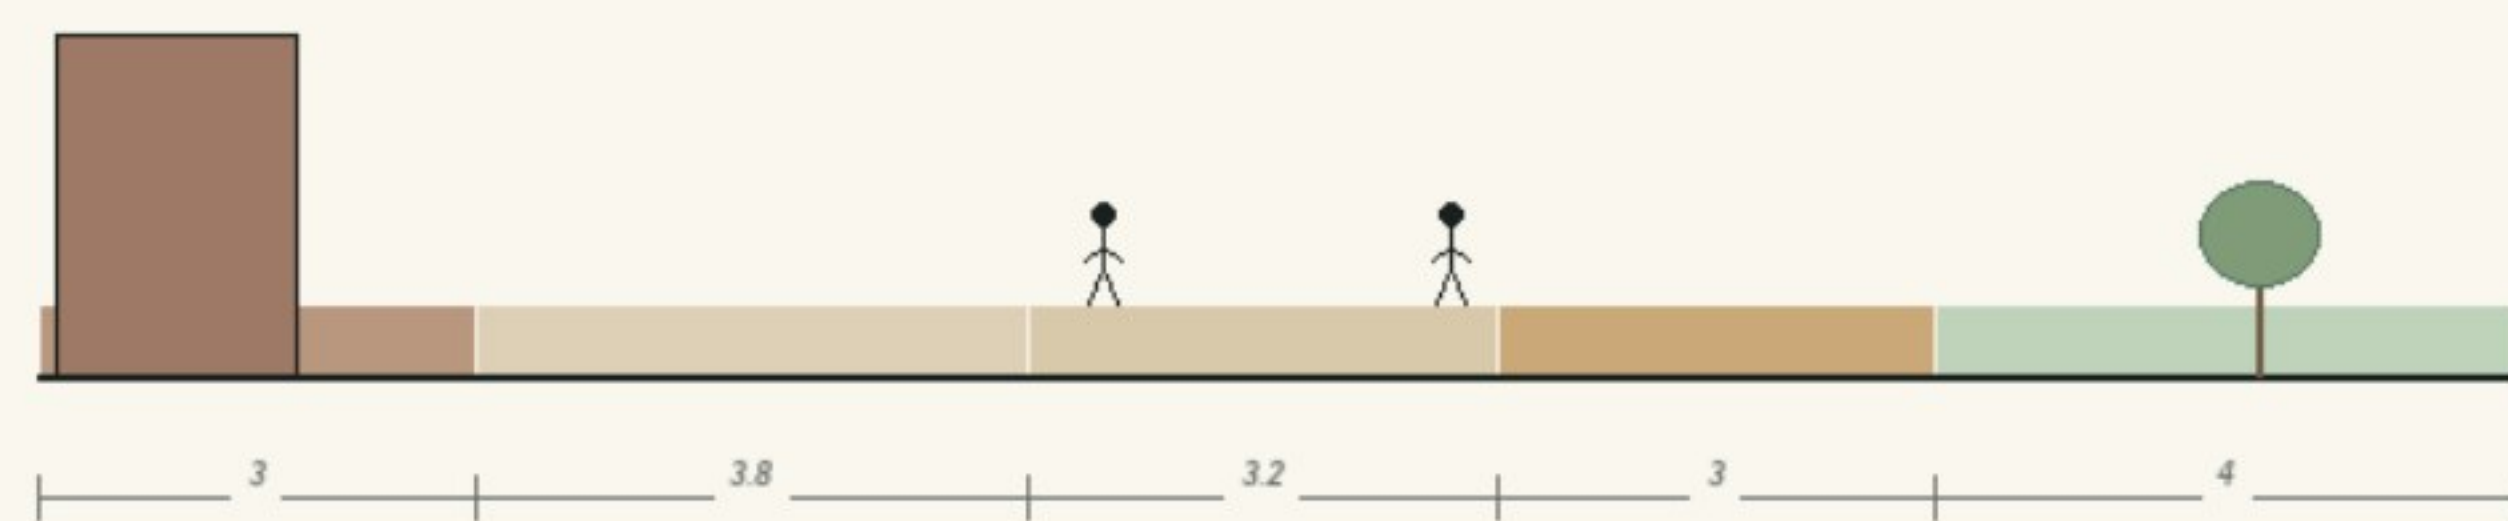


03 Dazhongsi Exchange Court

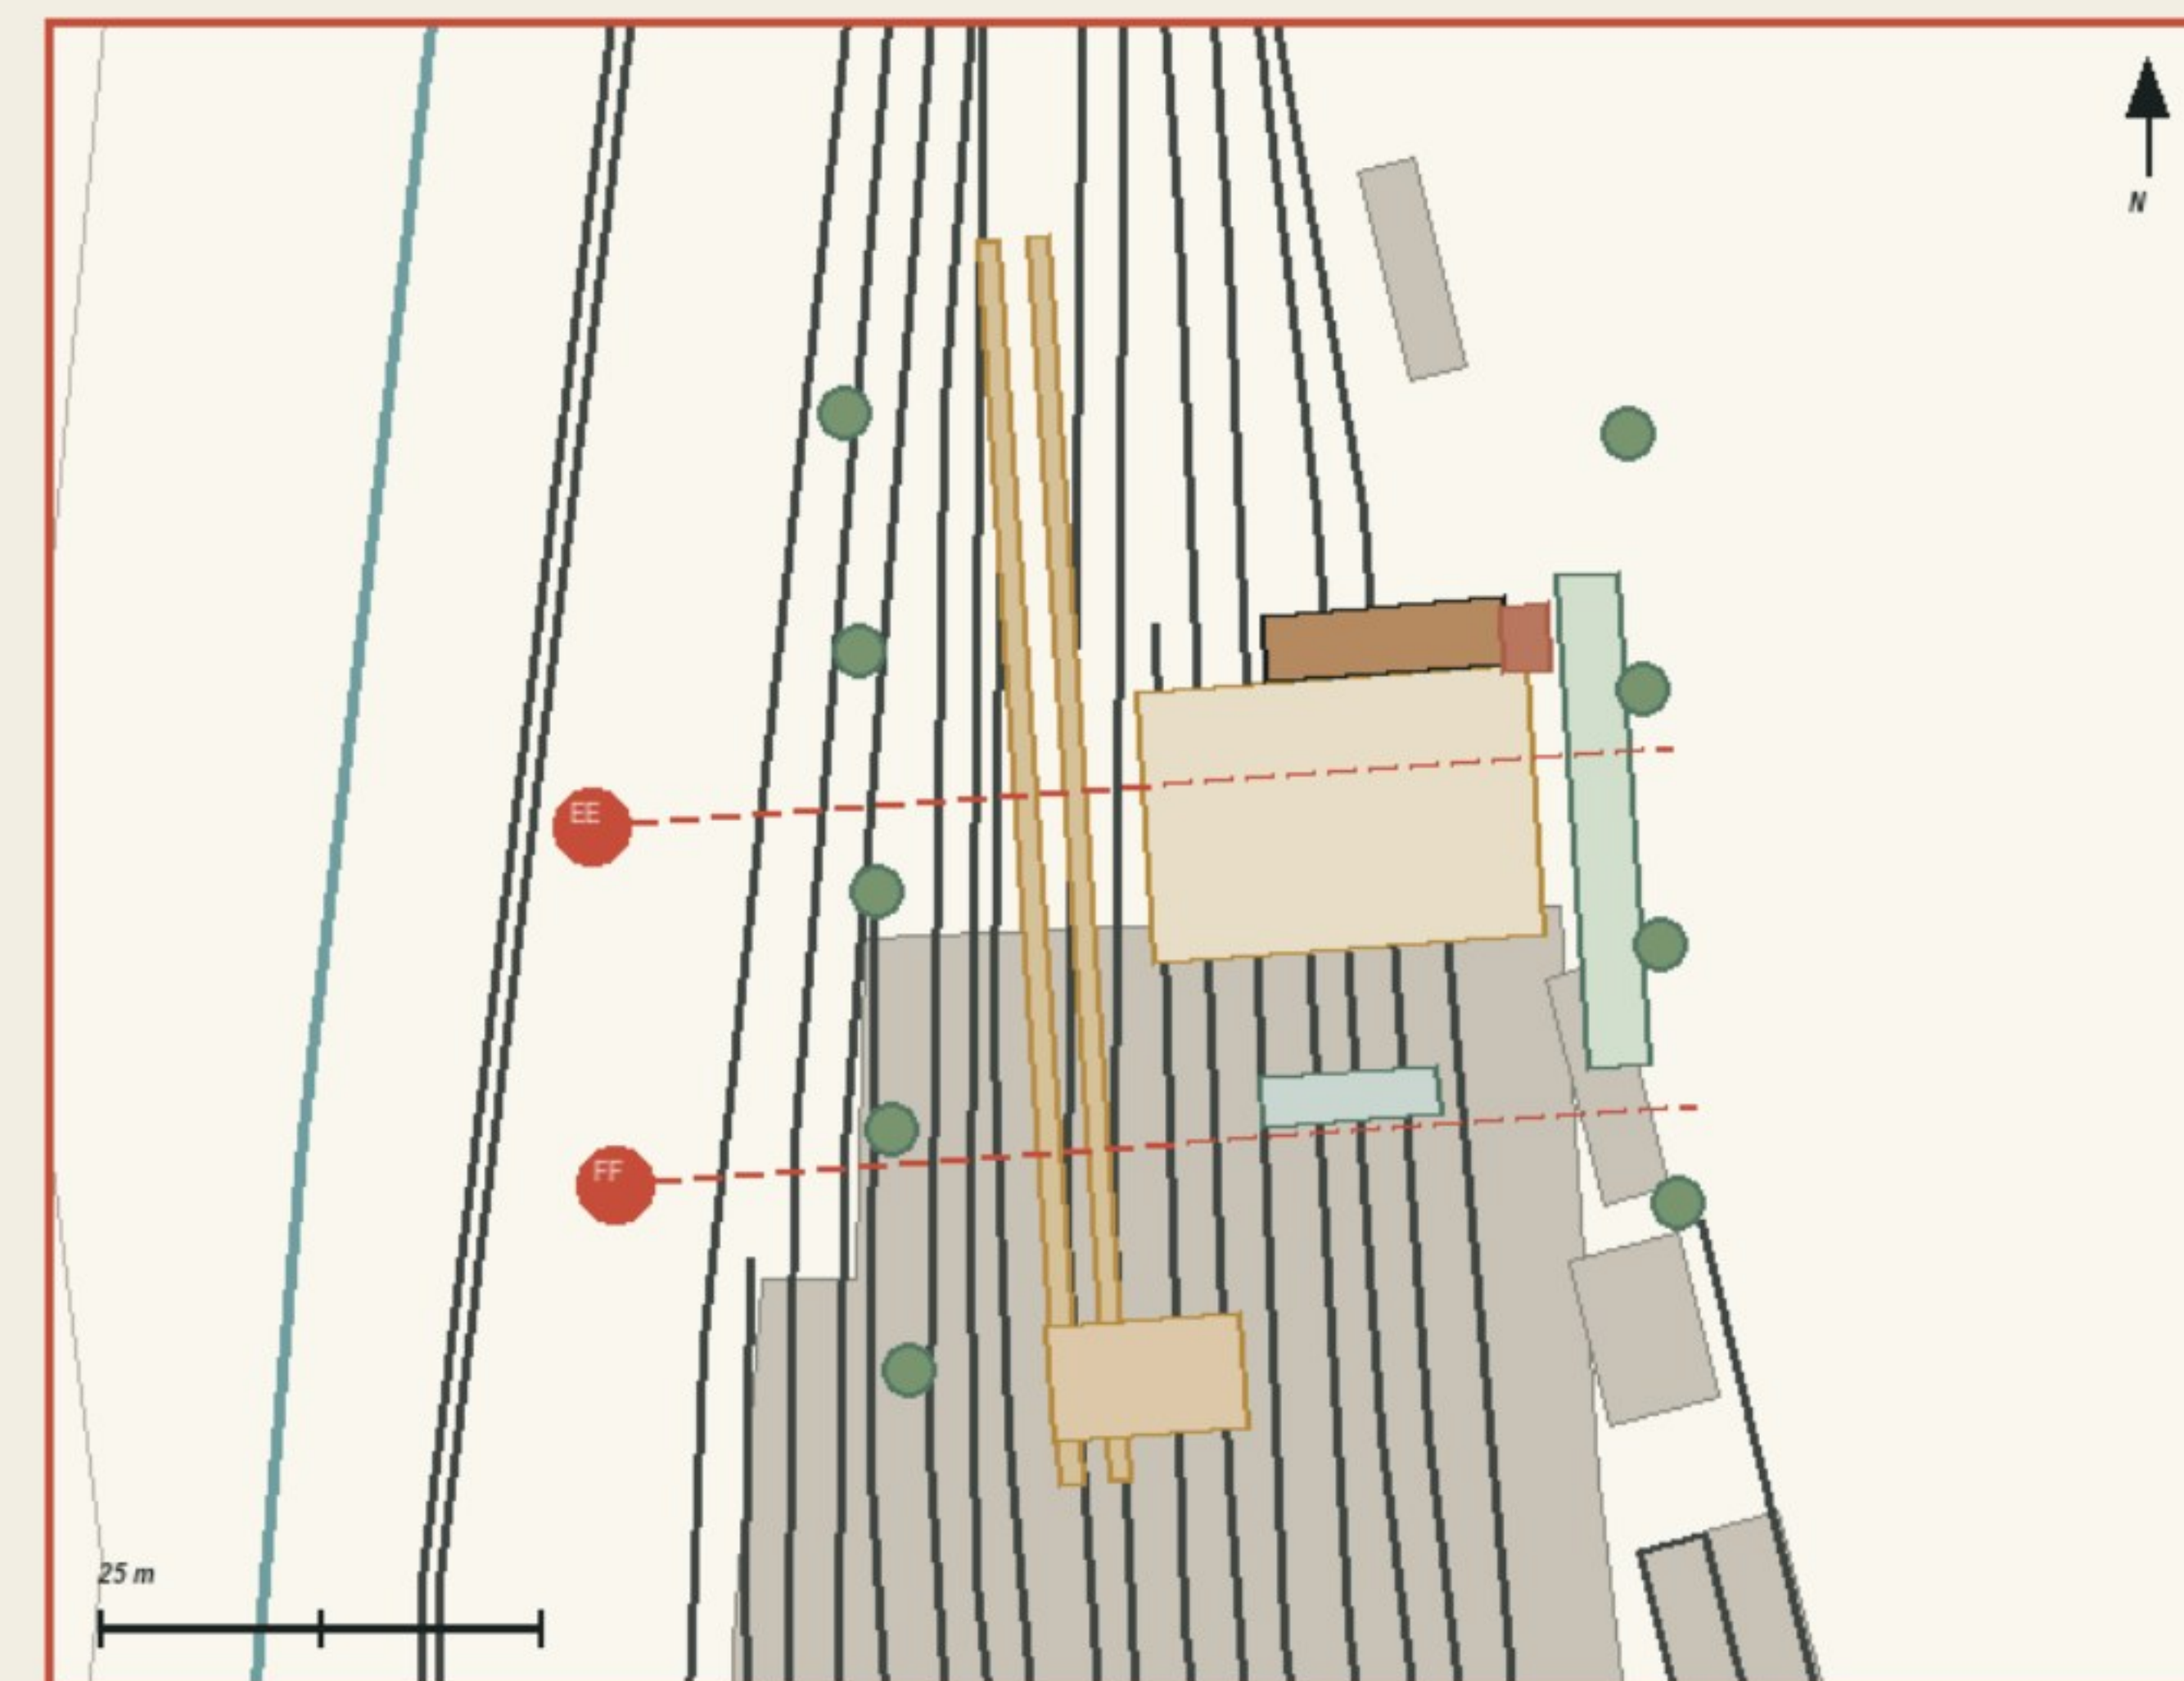

EE Daily edge at the exchange court

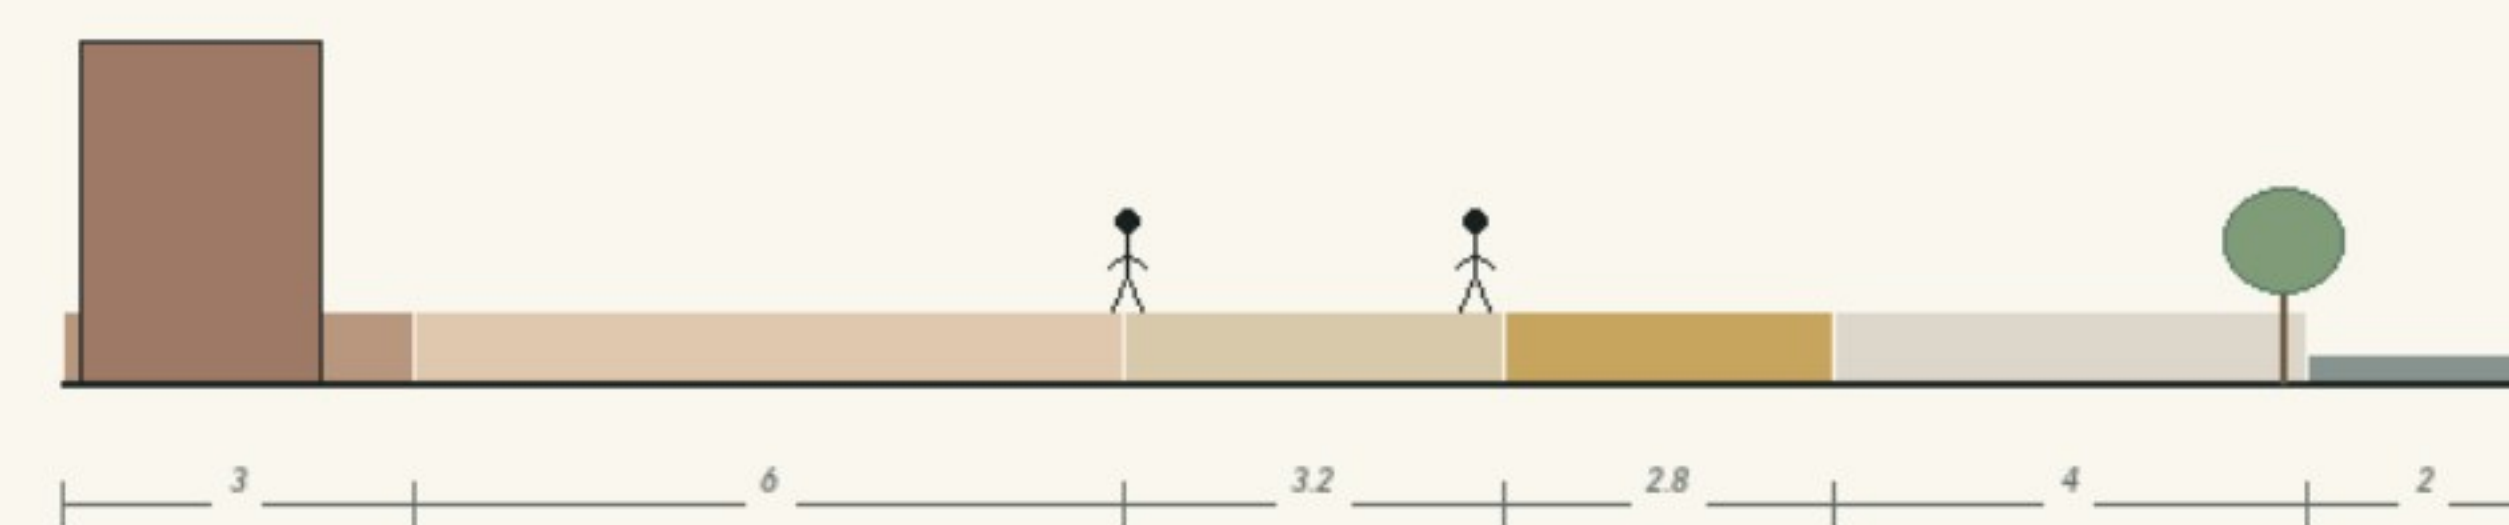

FF Step-free crossing

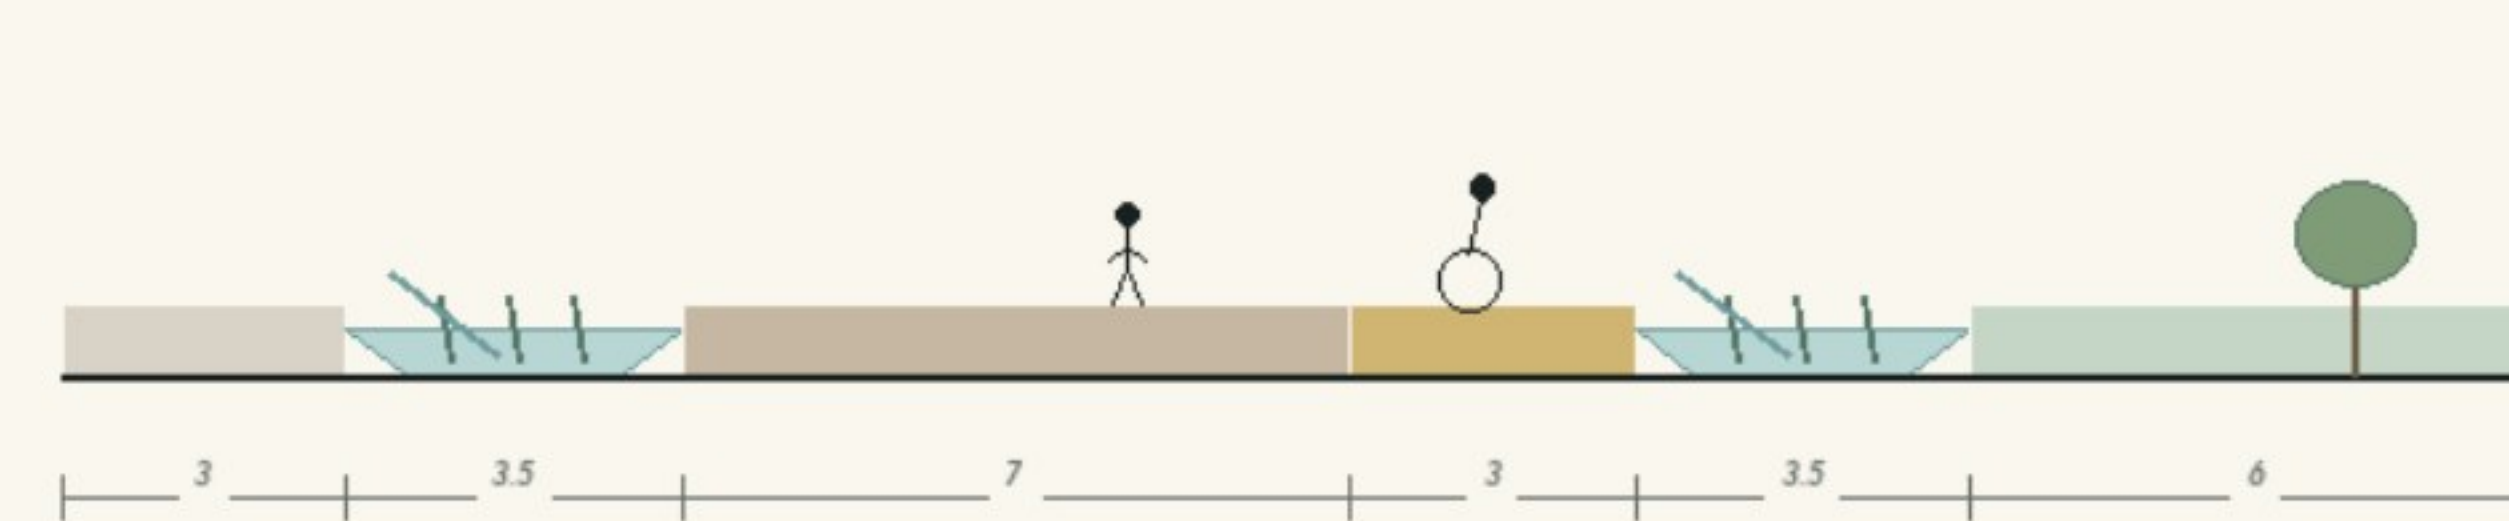

PUBLIC WALK SLOW CYCLE RAIN GARDEN REVERSIBLE TEST EDGE

CONCEPT DESIGN PROVISIONAL BOUNDARY OSM FOR CONTEXT ONLY

Working dimensions Concept design 1:200 section logic




08 REVERSIBLE / REPAIRABLE / REPLACEABLE

Eight field-ready components: assembly, material layers and maintenance

JINGZHANG OPEN BELT
FIELD KIT / 08

C01 SHADE CANOPY

P1 / PILOT

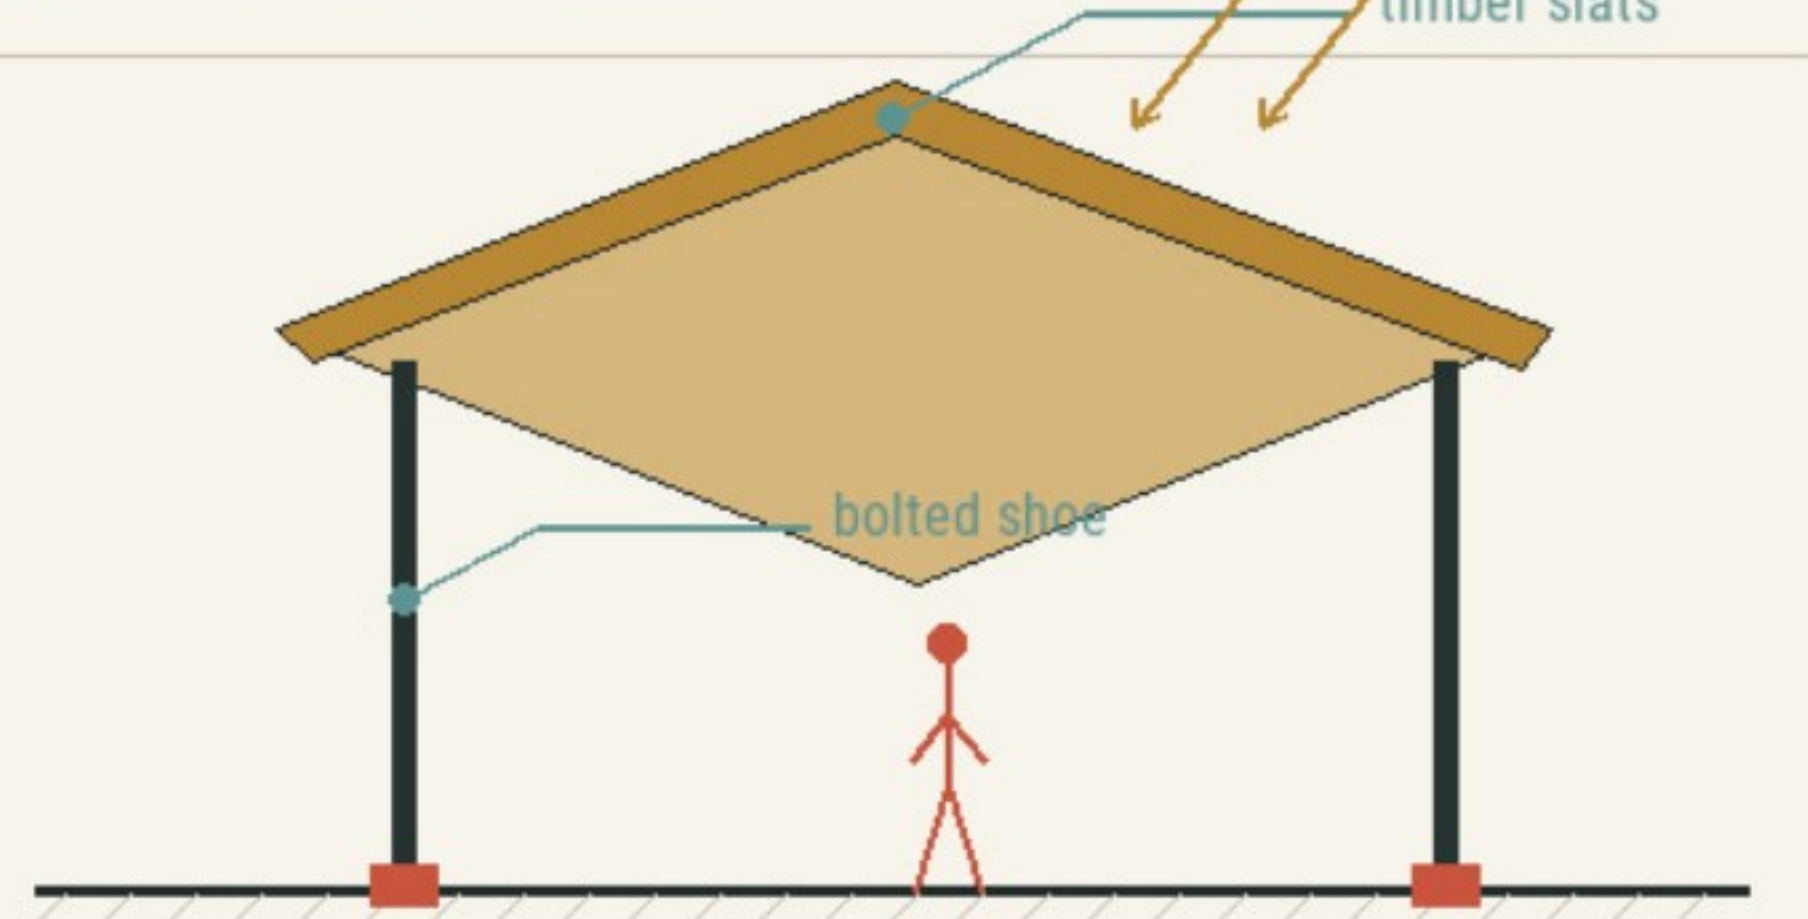


Four-point footing; roof and shoes replace independently

■ steel ■ timber

6 x 3 x 3.2 m

C02 THREE-HEIGHT BENCH

P1 / PILOT

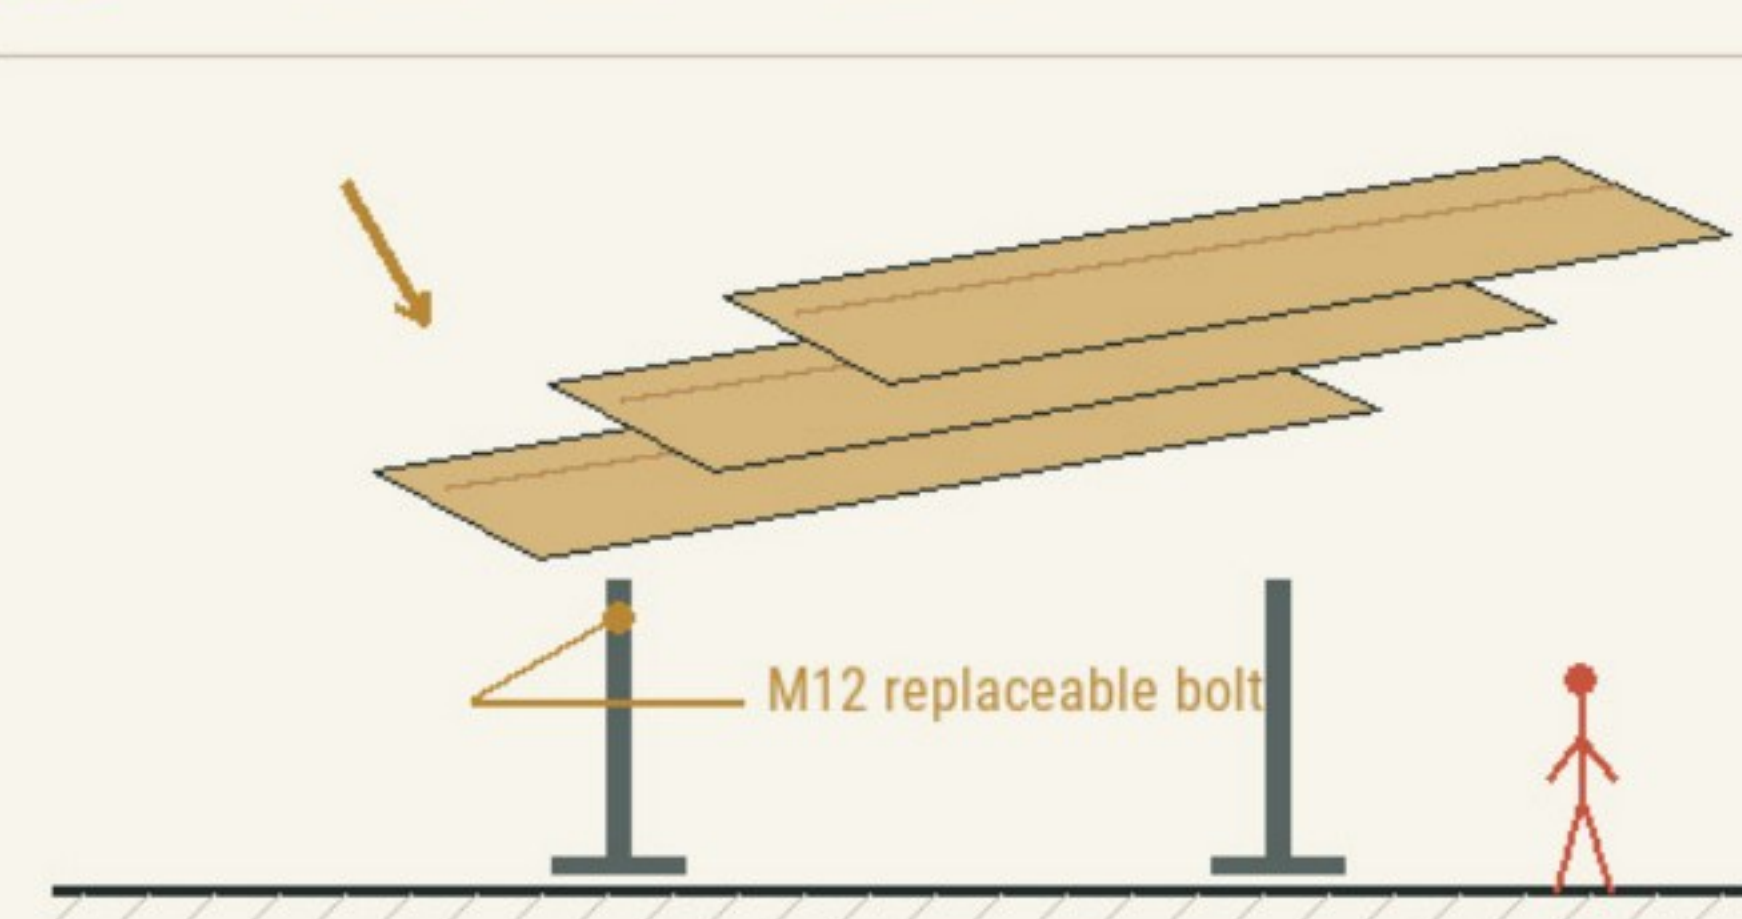


One galvanized frame; worn boards change by segment

■ zinc ■ boards

3.6 x .7 x .55 m

C03 RAIN-GARDEN EDGE

P1 / WET

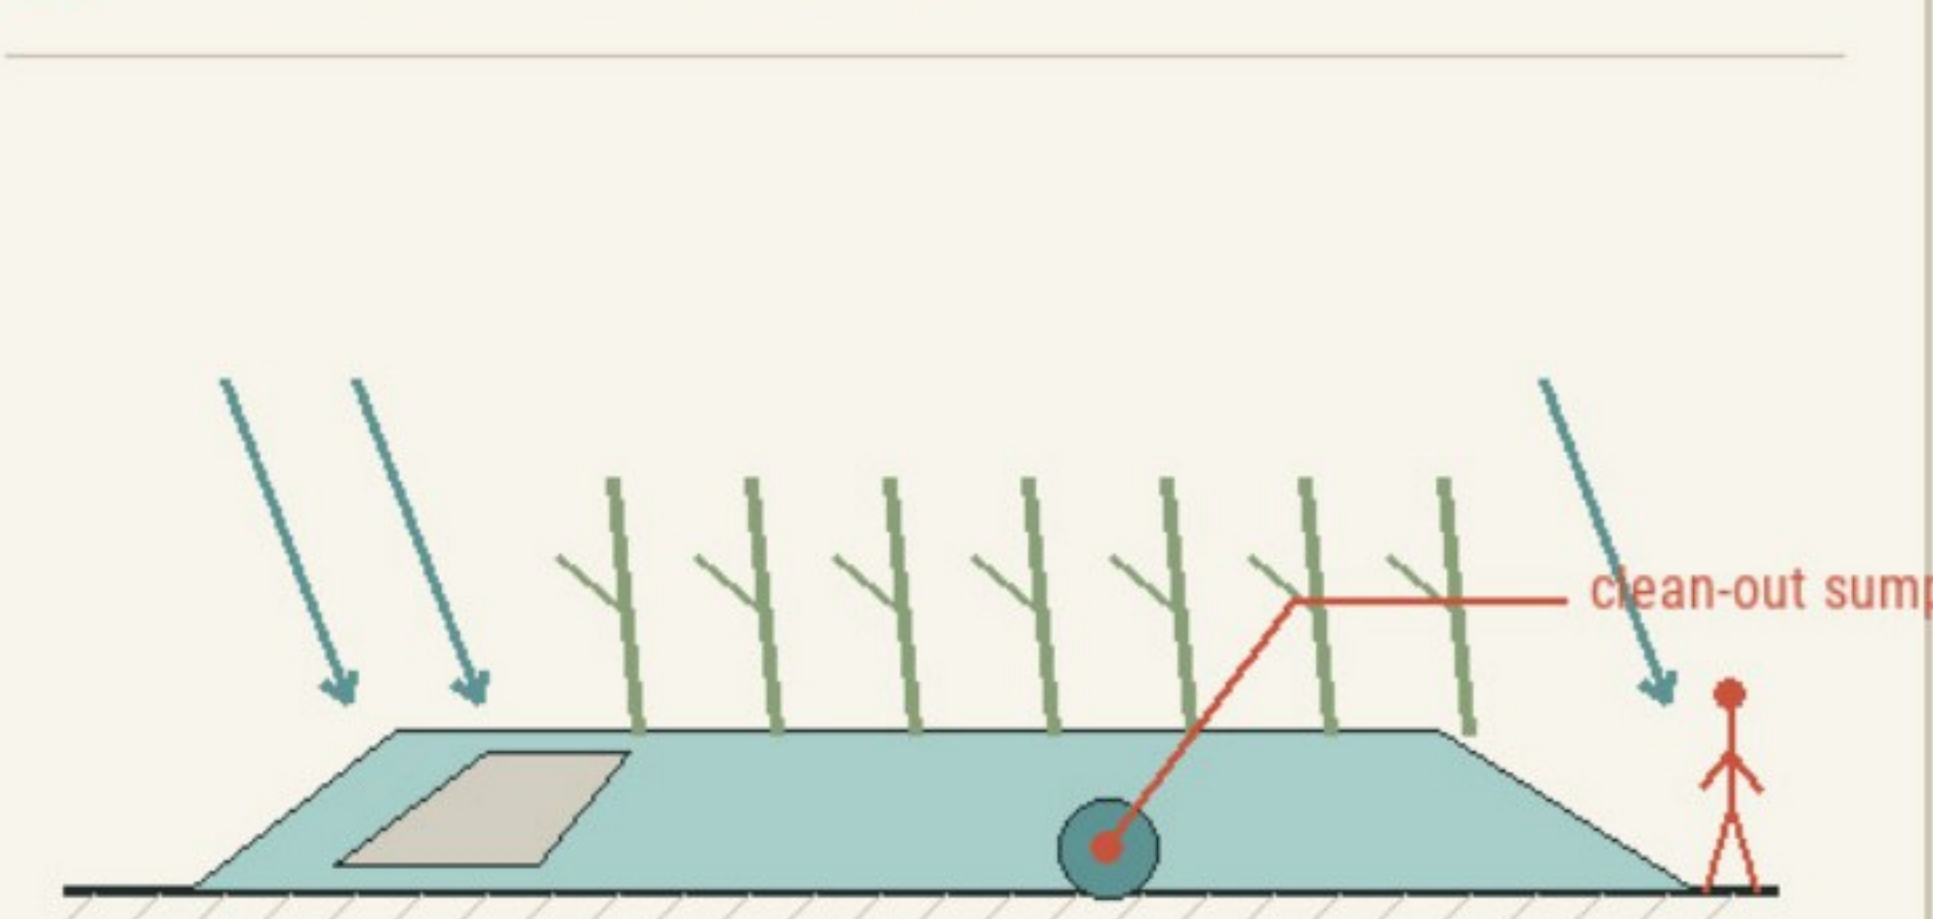


Open curb feeds planting; sump stays on service side

■ aggregate ■ plants

6 x 2.4 x .45 m

C04 HERITAGE READING RAIL

P2 / FIXED

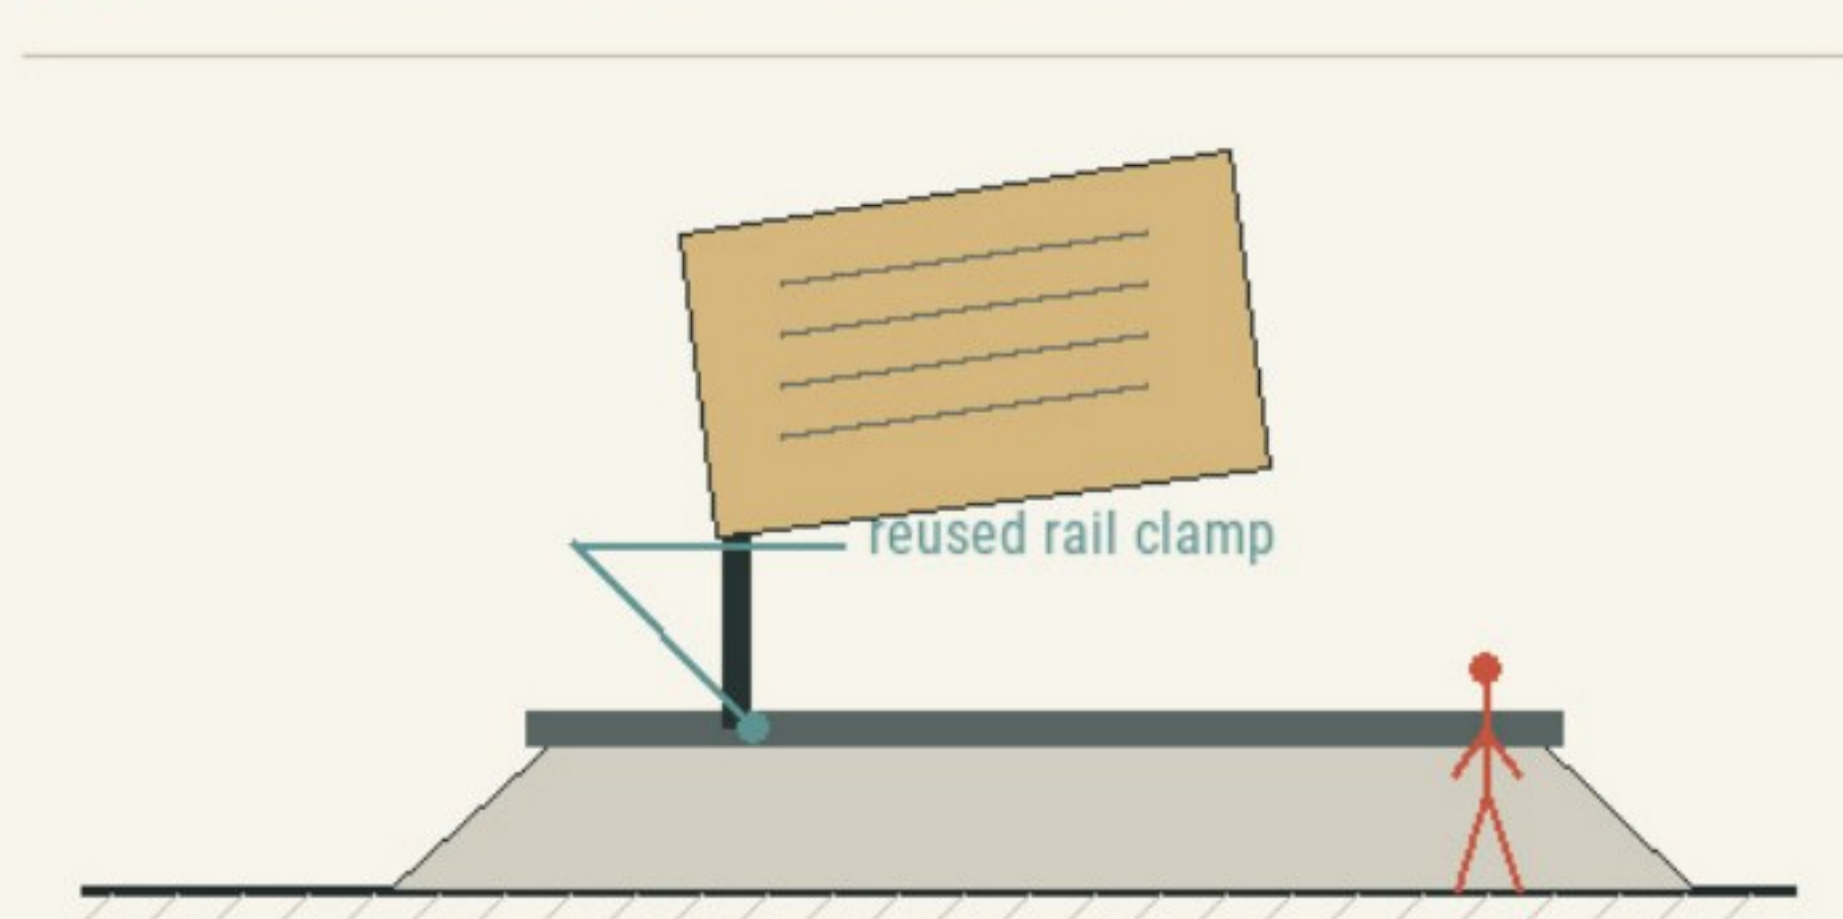


Reused rail base; non-digital panel updates in place

■ rail ■ panel

2.4 x .45 x 1.15 m

C05 STAFFED SERVICE TABLE

P1 / EVENT

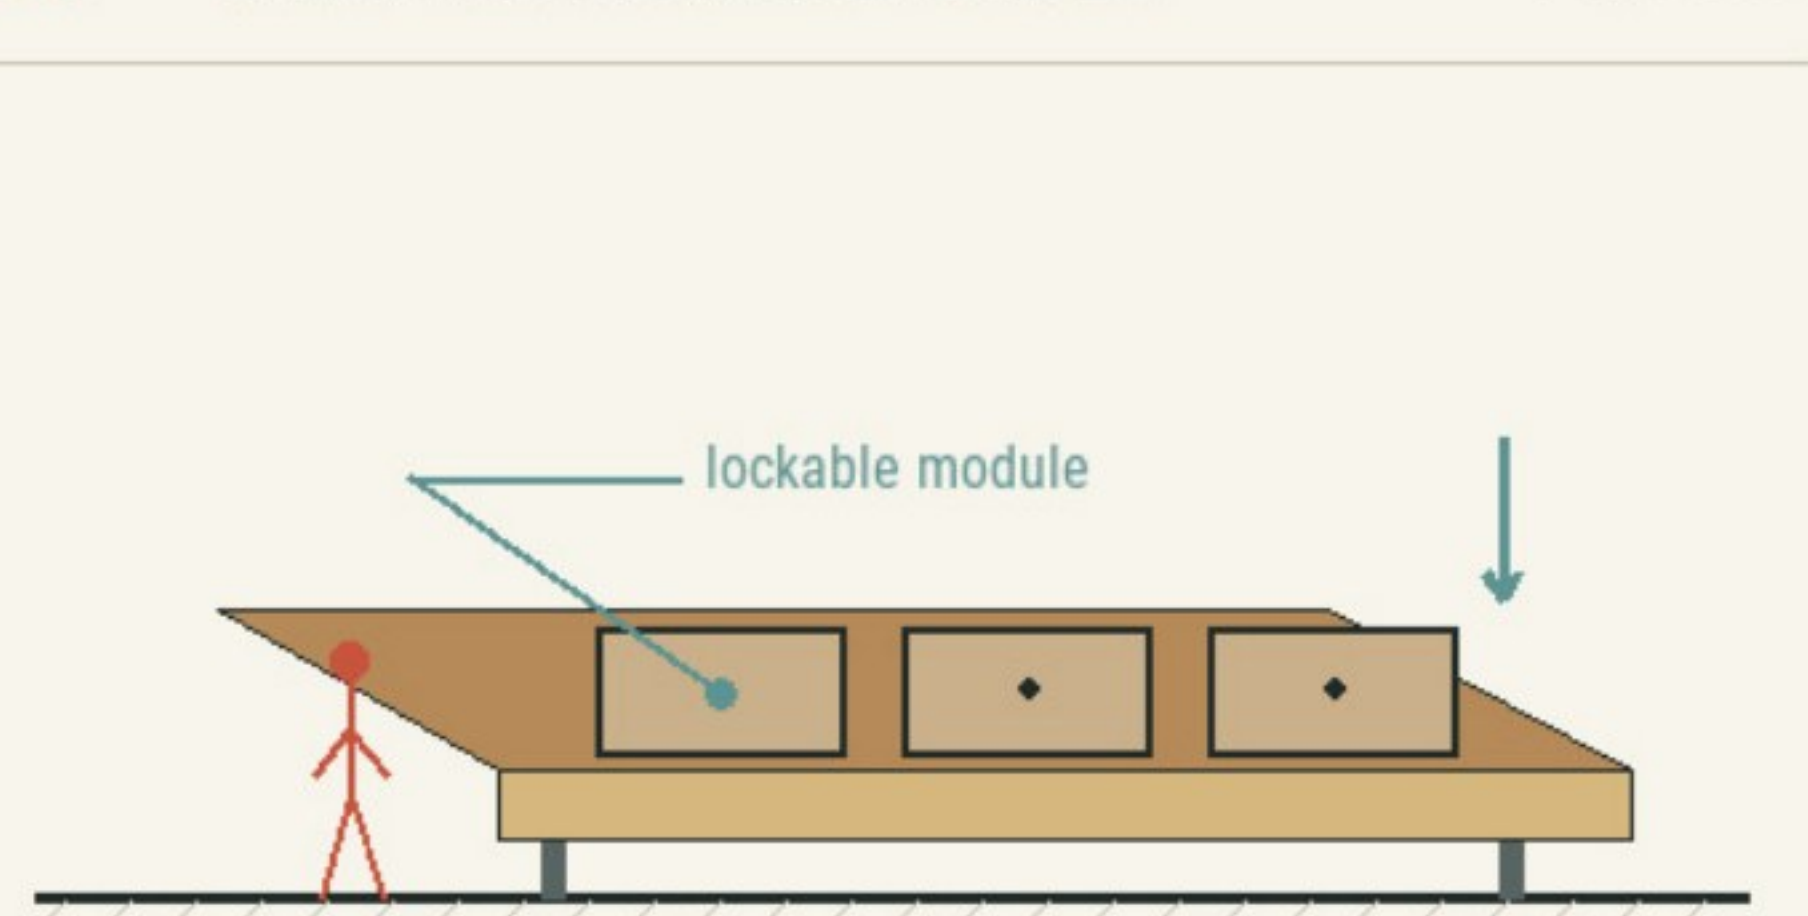


Lockable drawers; modules and stools move separately

■ steel ■ module

2.4 x .8 x .75 m

C06 VISIBLE TEST EDGE

P0 / QUICK

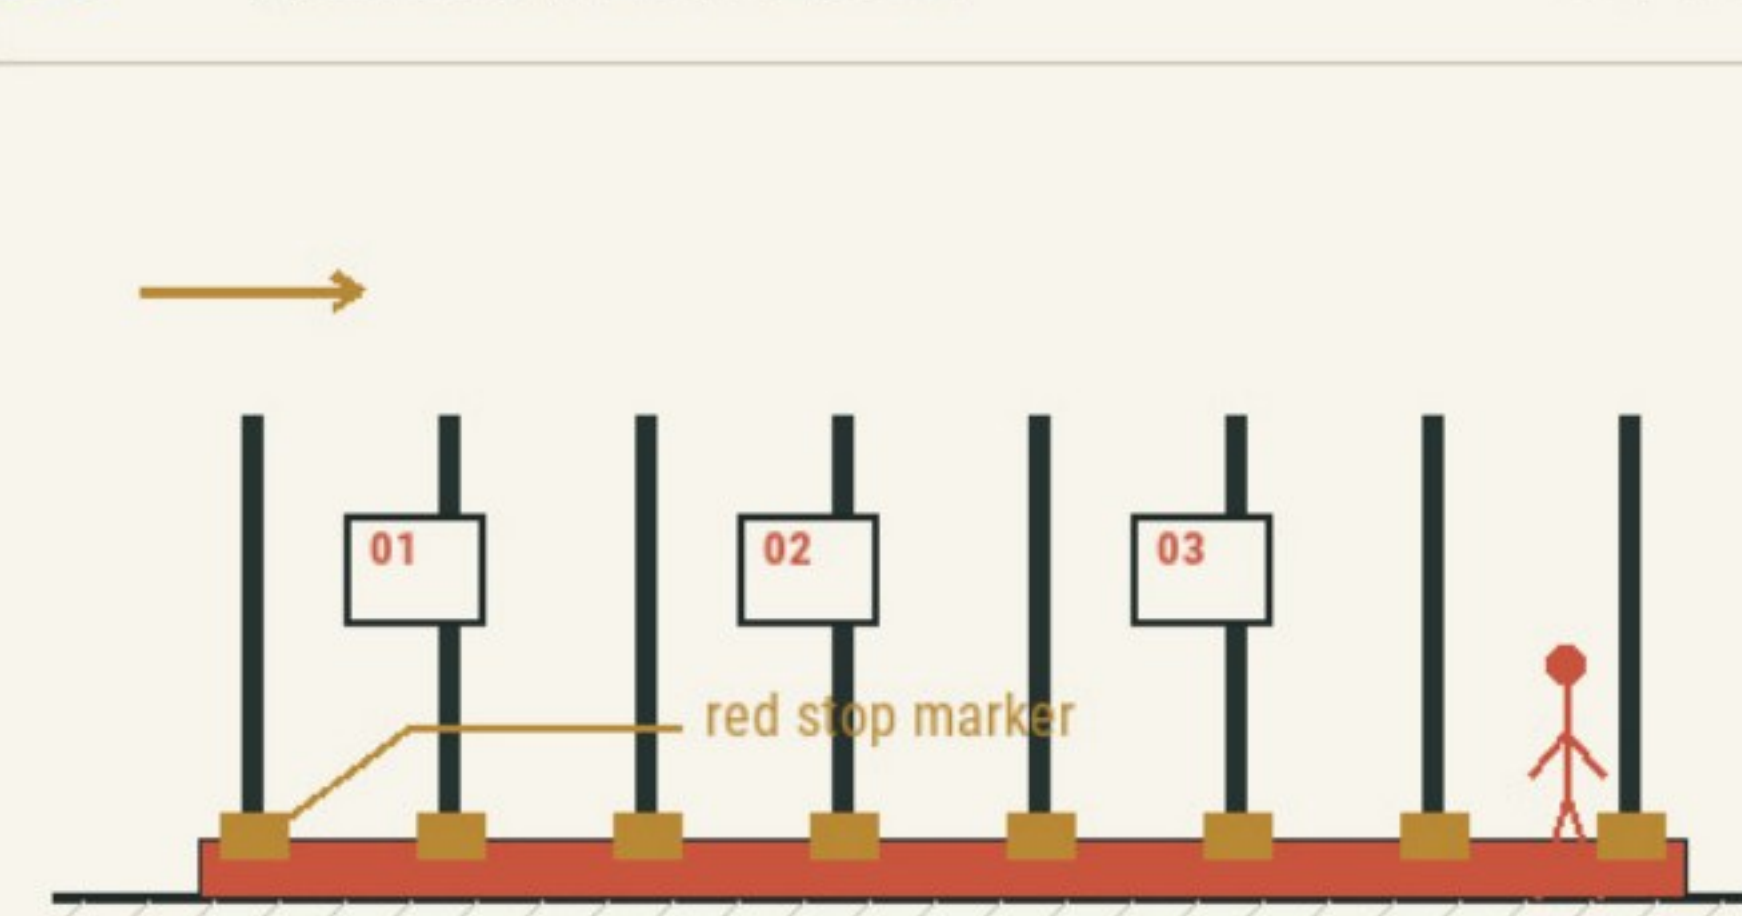


Keeps views open; red stop marks the test boundary

■ steel ■ red mark

4 x .25 x .9 m

C07 STAFF CALL POST

P1 / STAFF

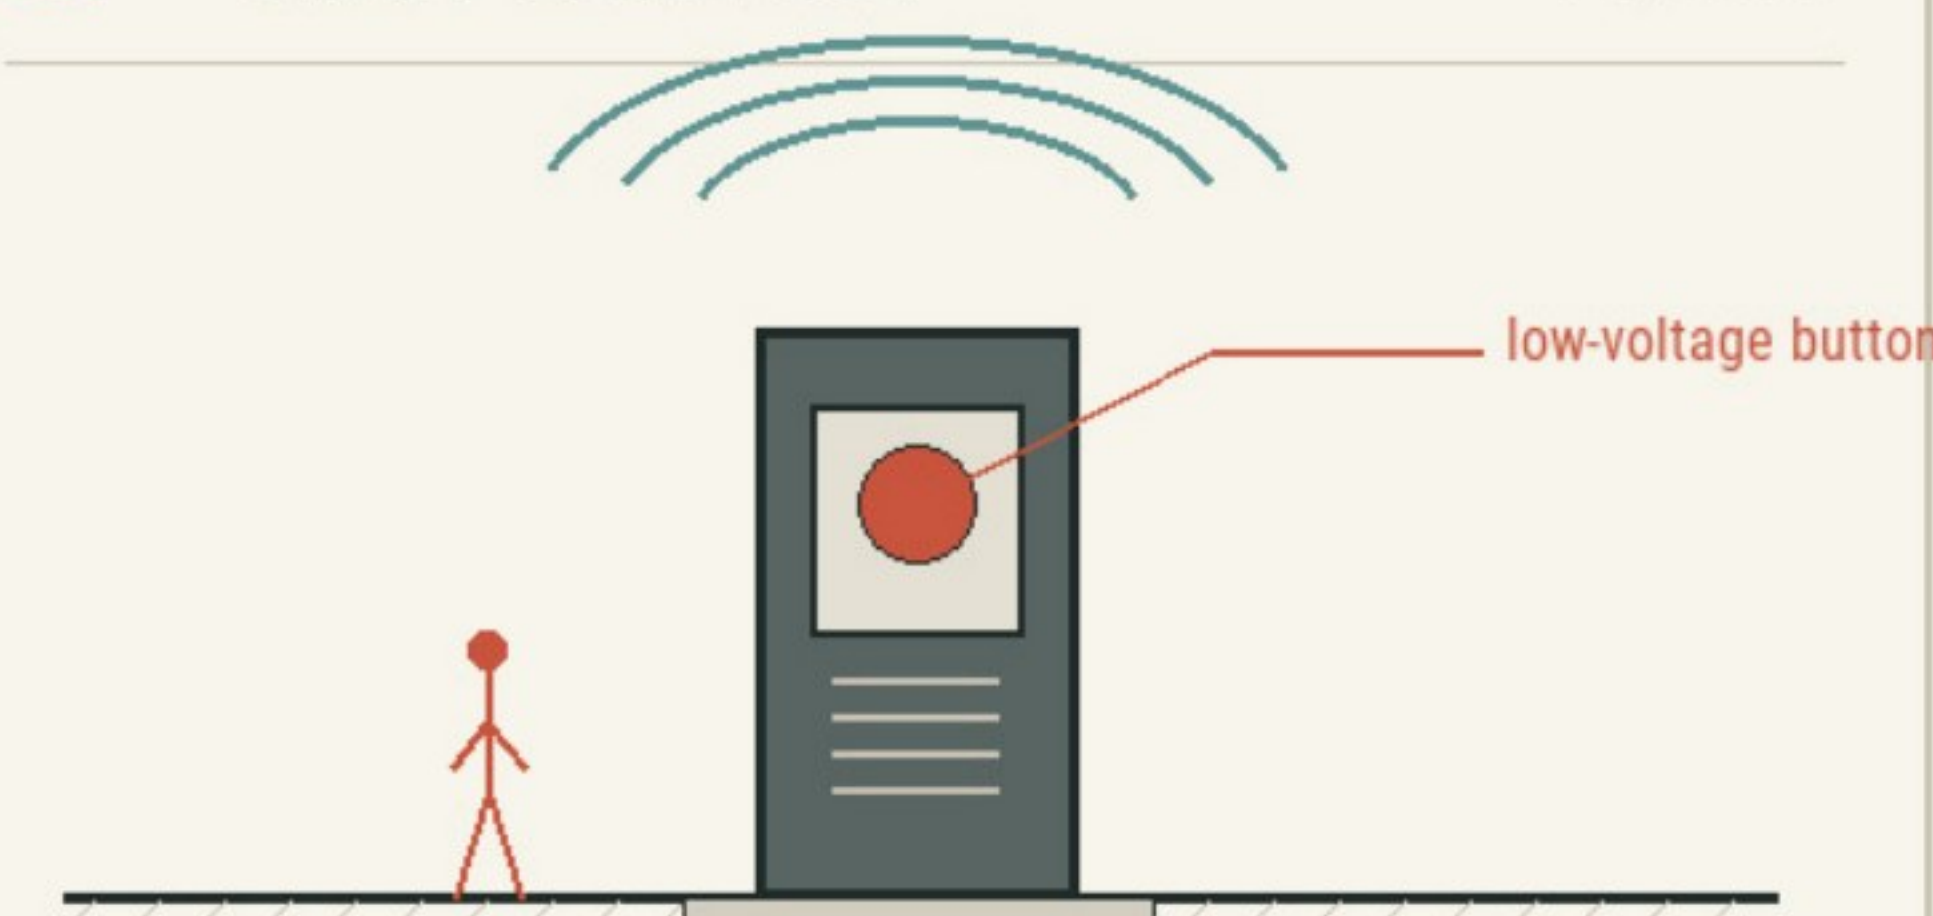

Tactile marker and low-voltage call to staffed point

■ steel ■ button

.35 x .35 x 1.35 m

C08 SHIELDED NIGHT LIGHT

P1 / NIGHT




Warm light stays on path; head swaps, timer circuit

■ steel ■ warm light


.35 x .35 x 3.6 m

MOVEMENT, WATER AND SIX SECTIONS


Join public routes and crossings before placing tests and services

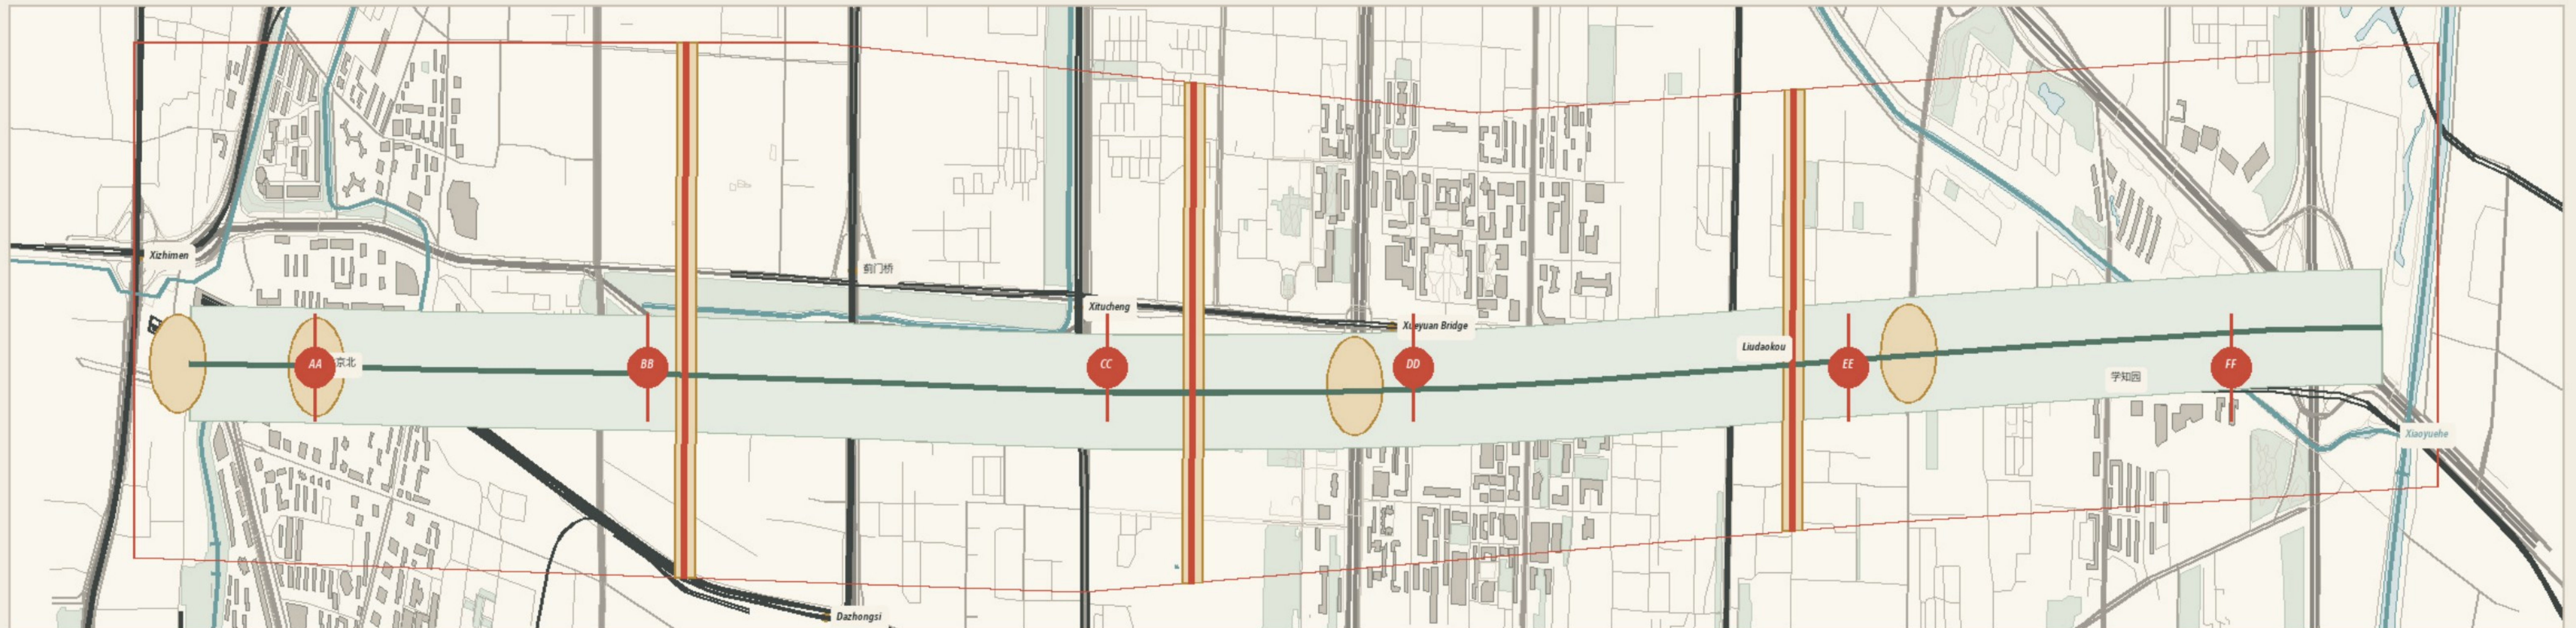


AA Public edge at the test court

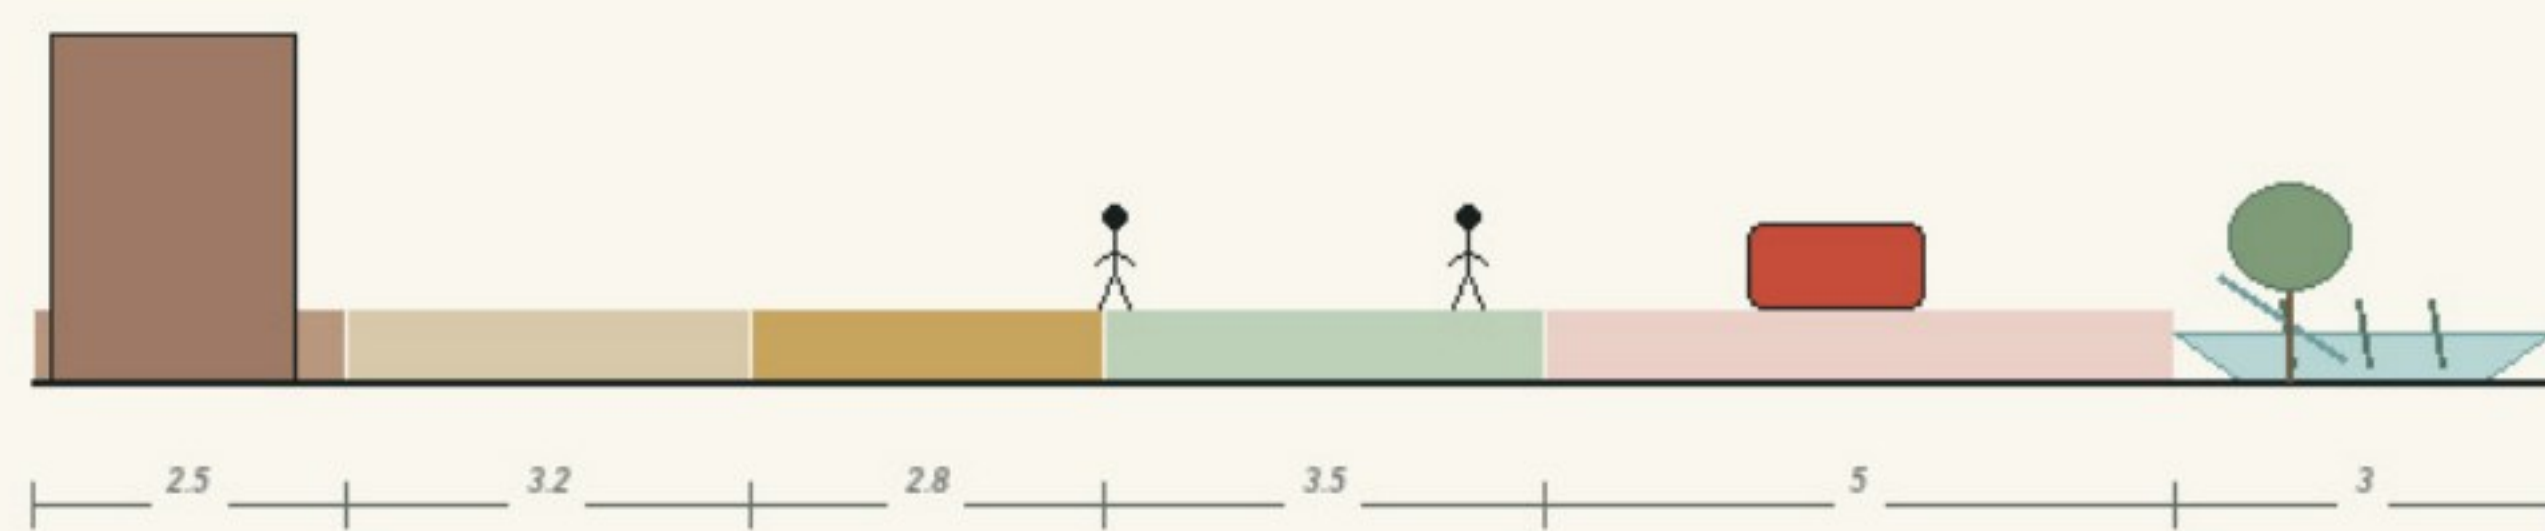


BB Xiaoyuehe link

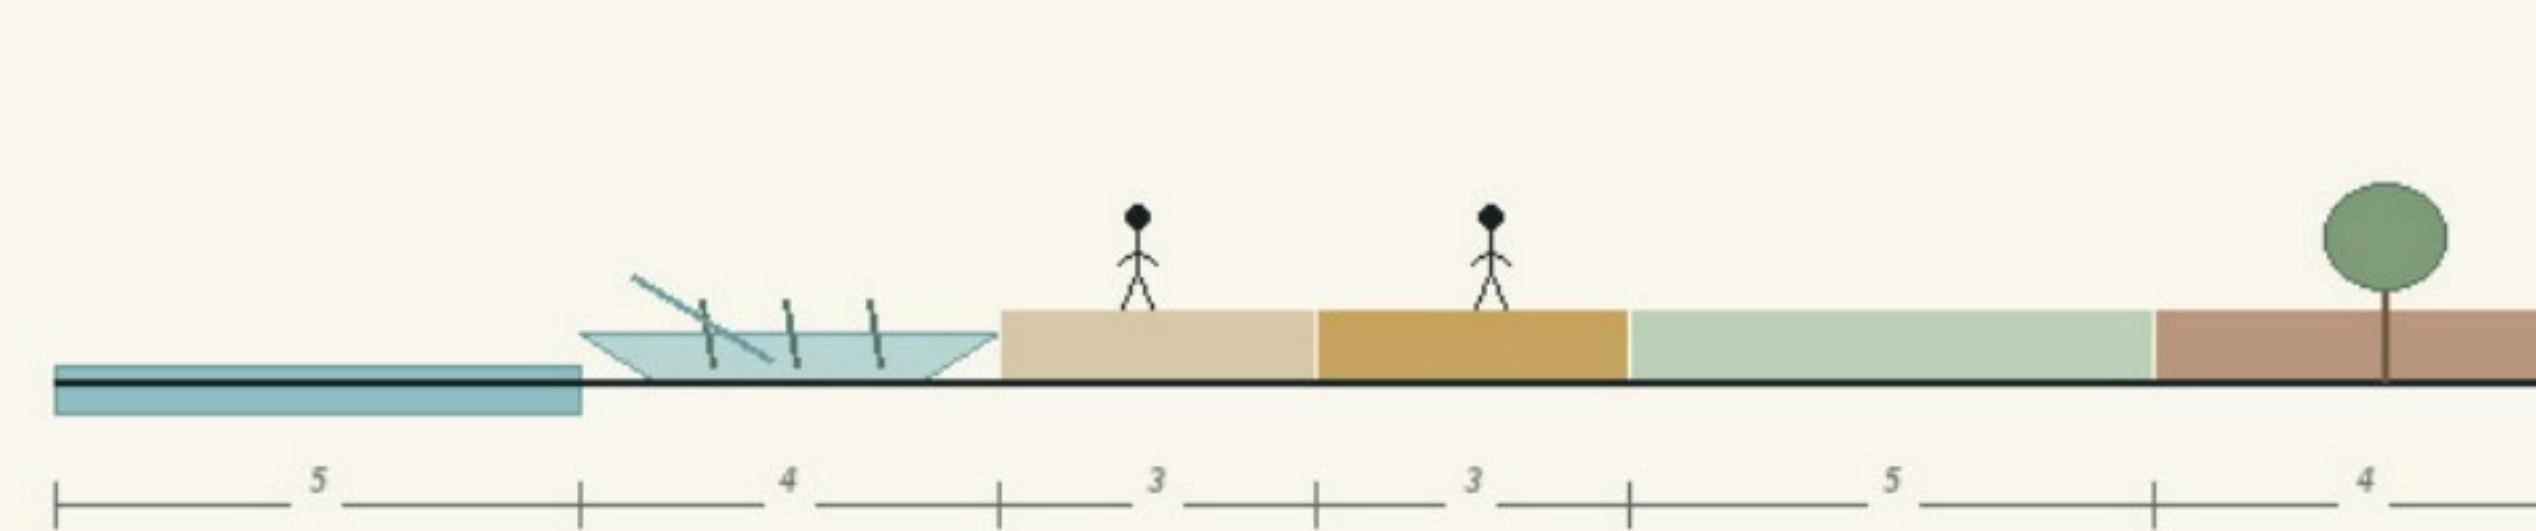


CC Old station forecourt

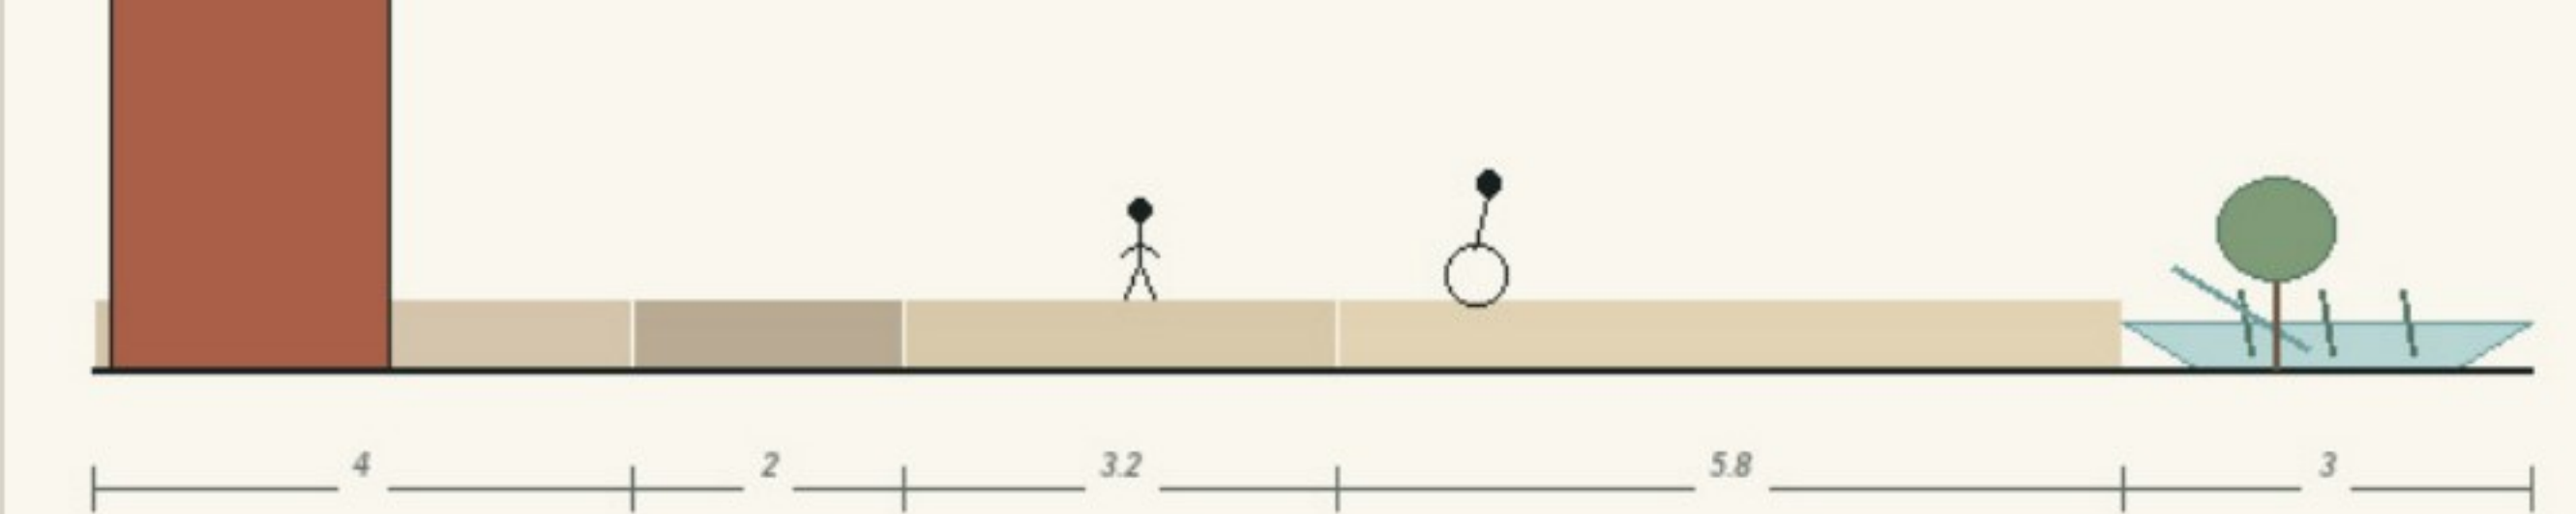


DD Service street court

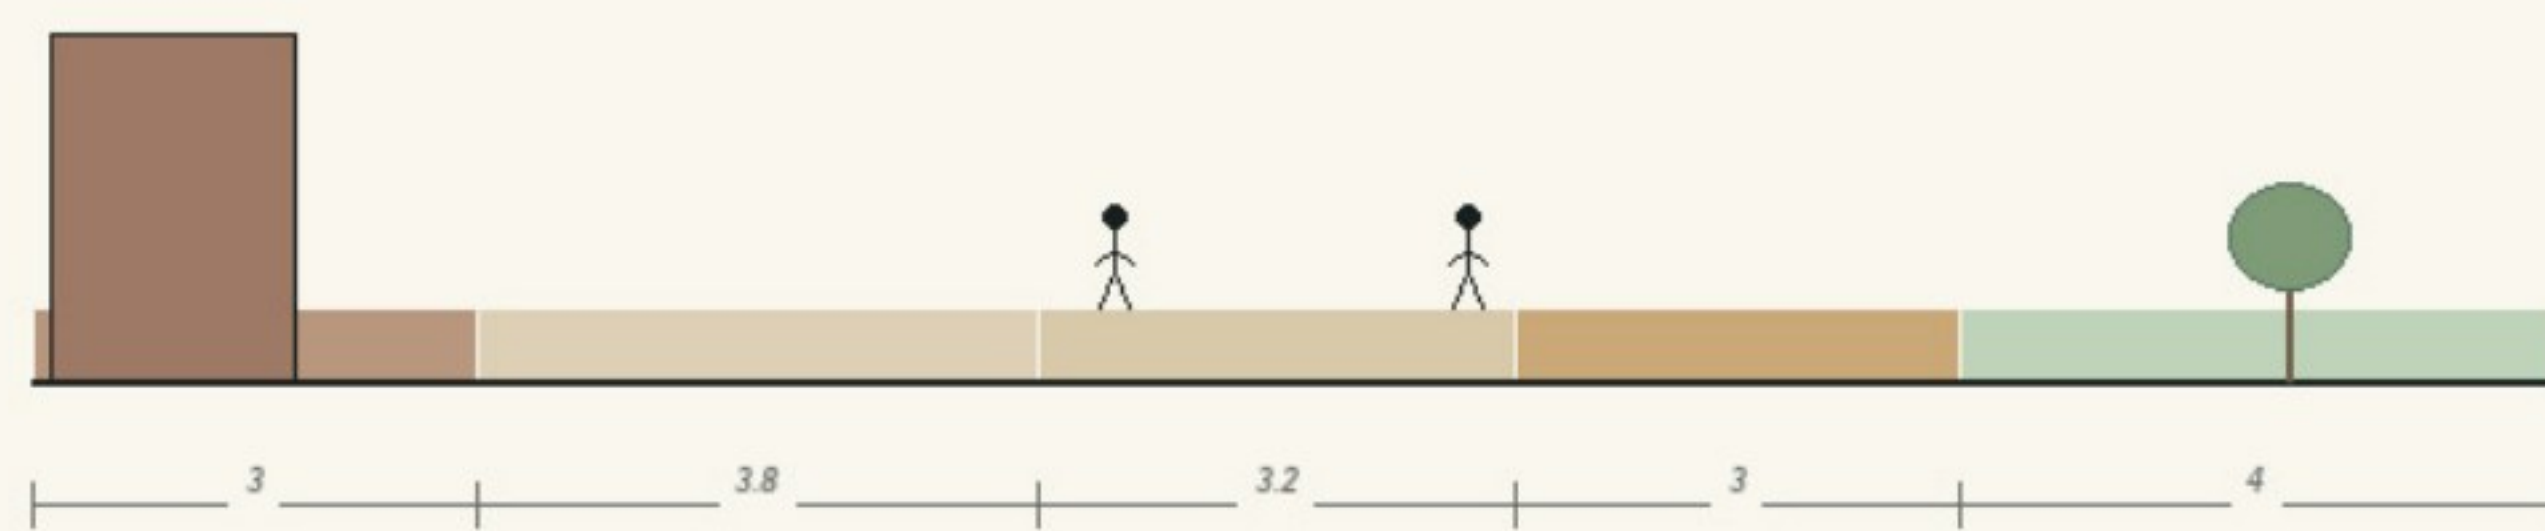

EE Daily edge at the exchange court

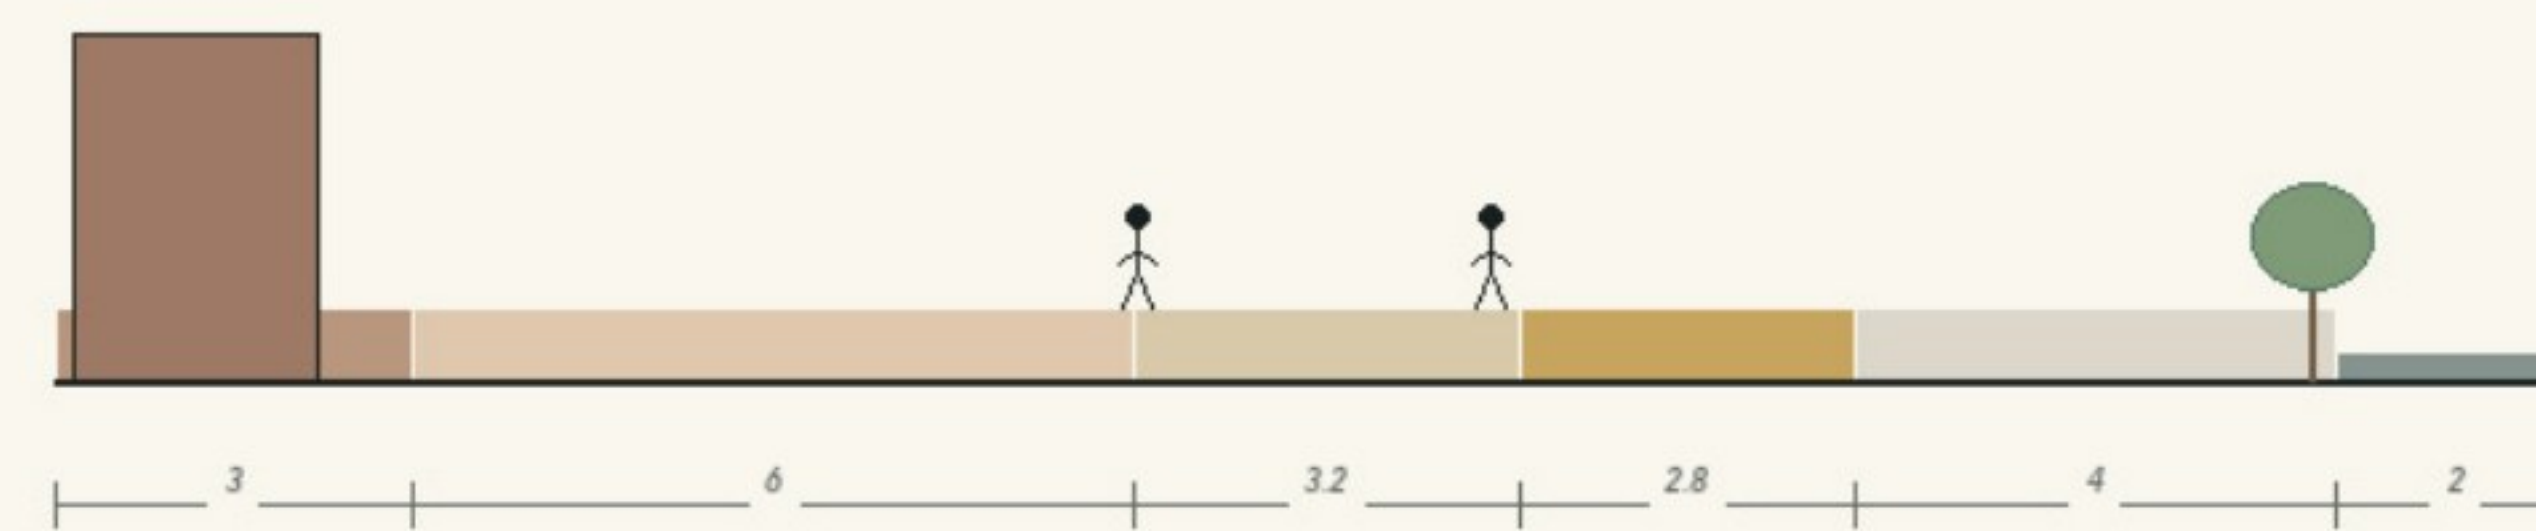


FF Step-free crossing

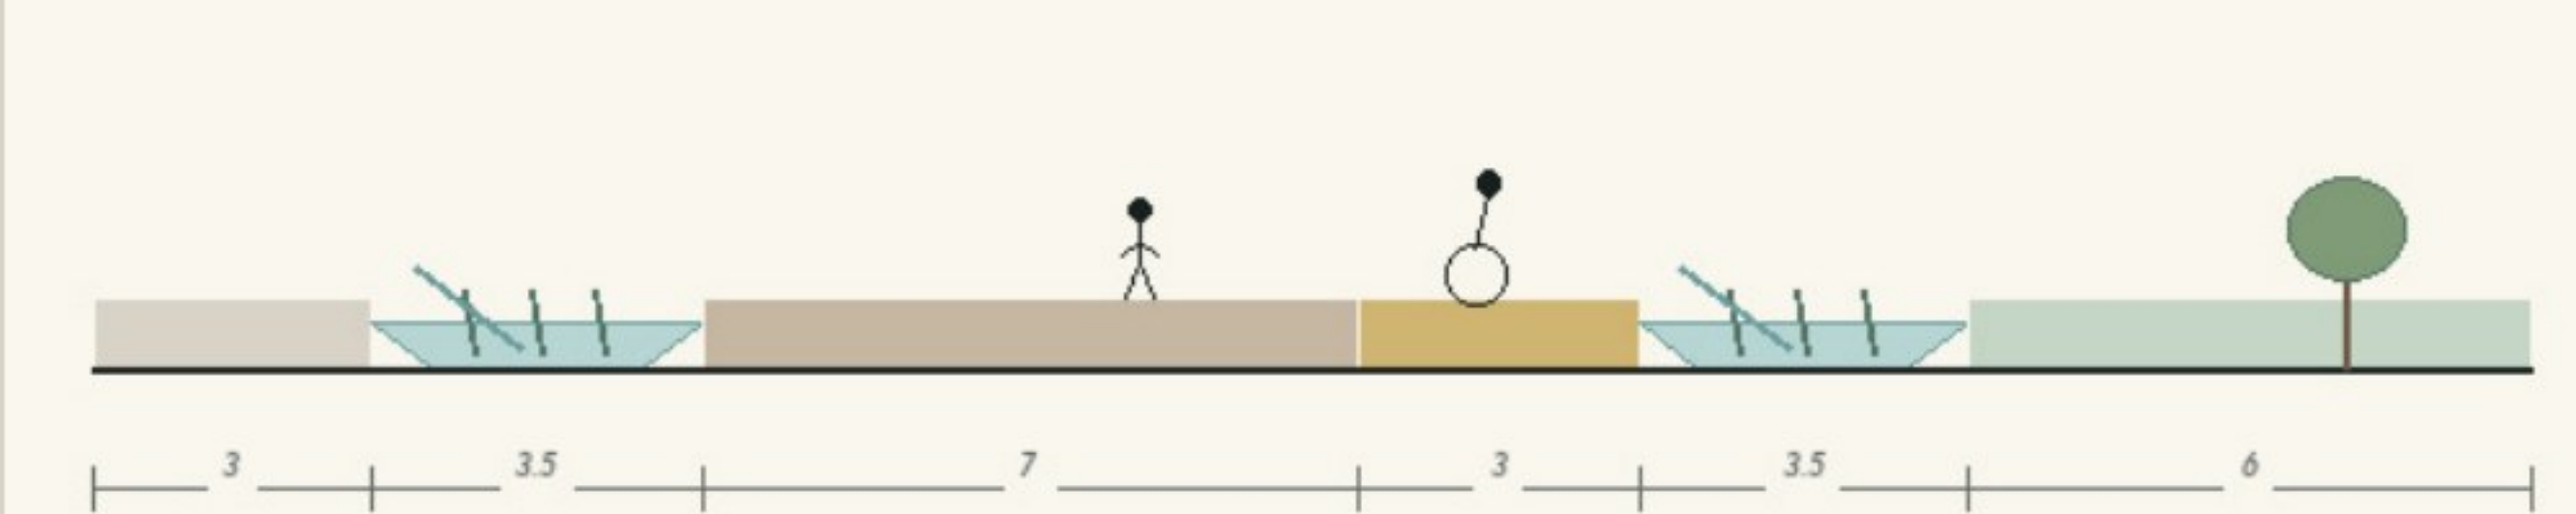

02 FROM NINE KILOMETRES TO ONE COURTYARD

One long line, three urban districts, three everyday scales

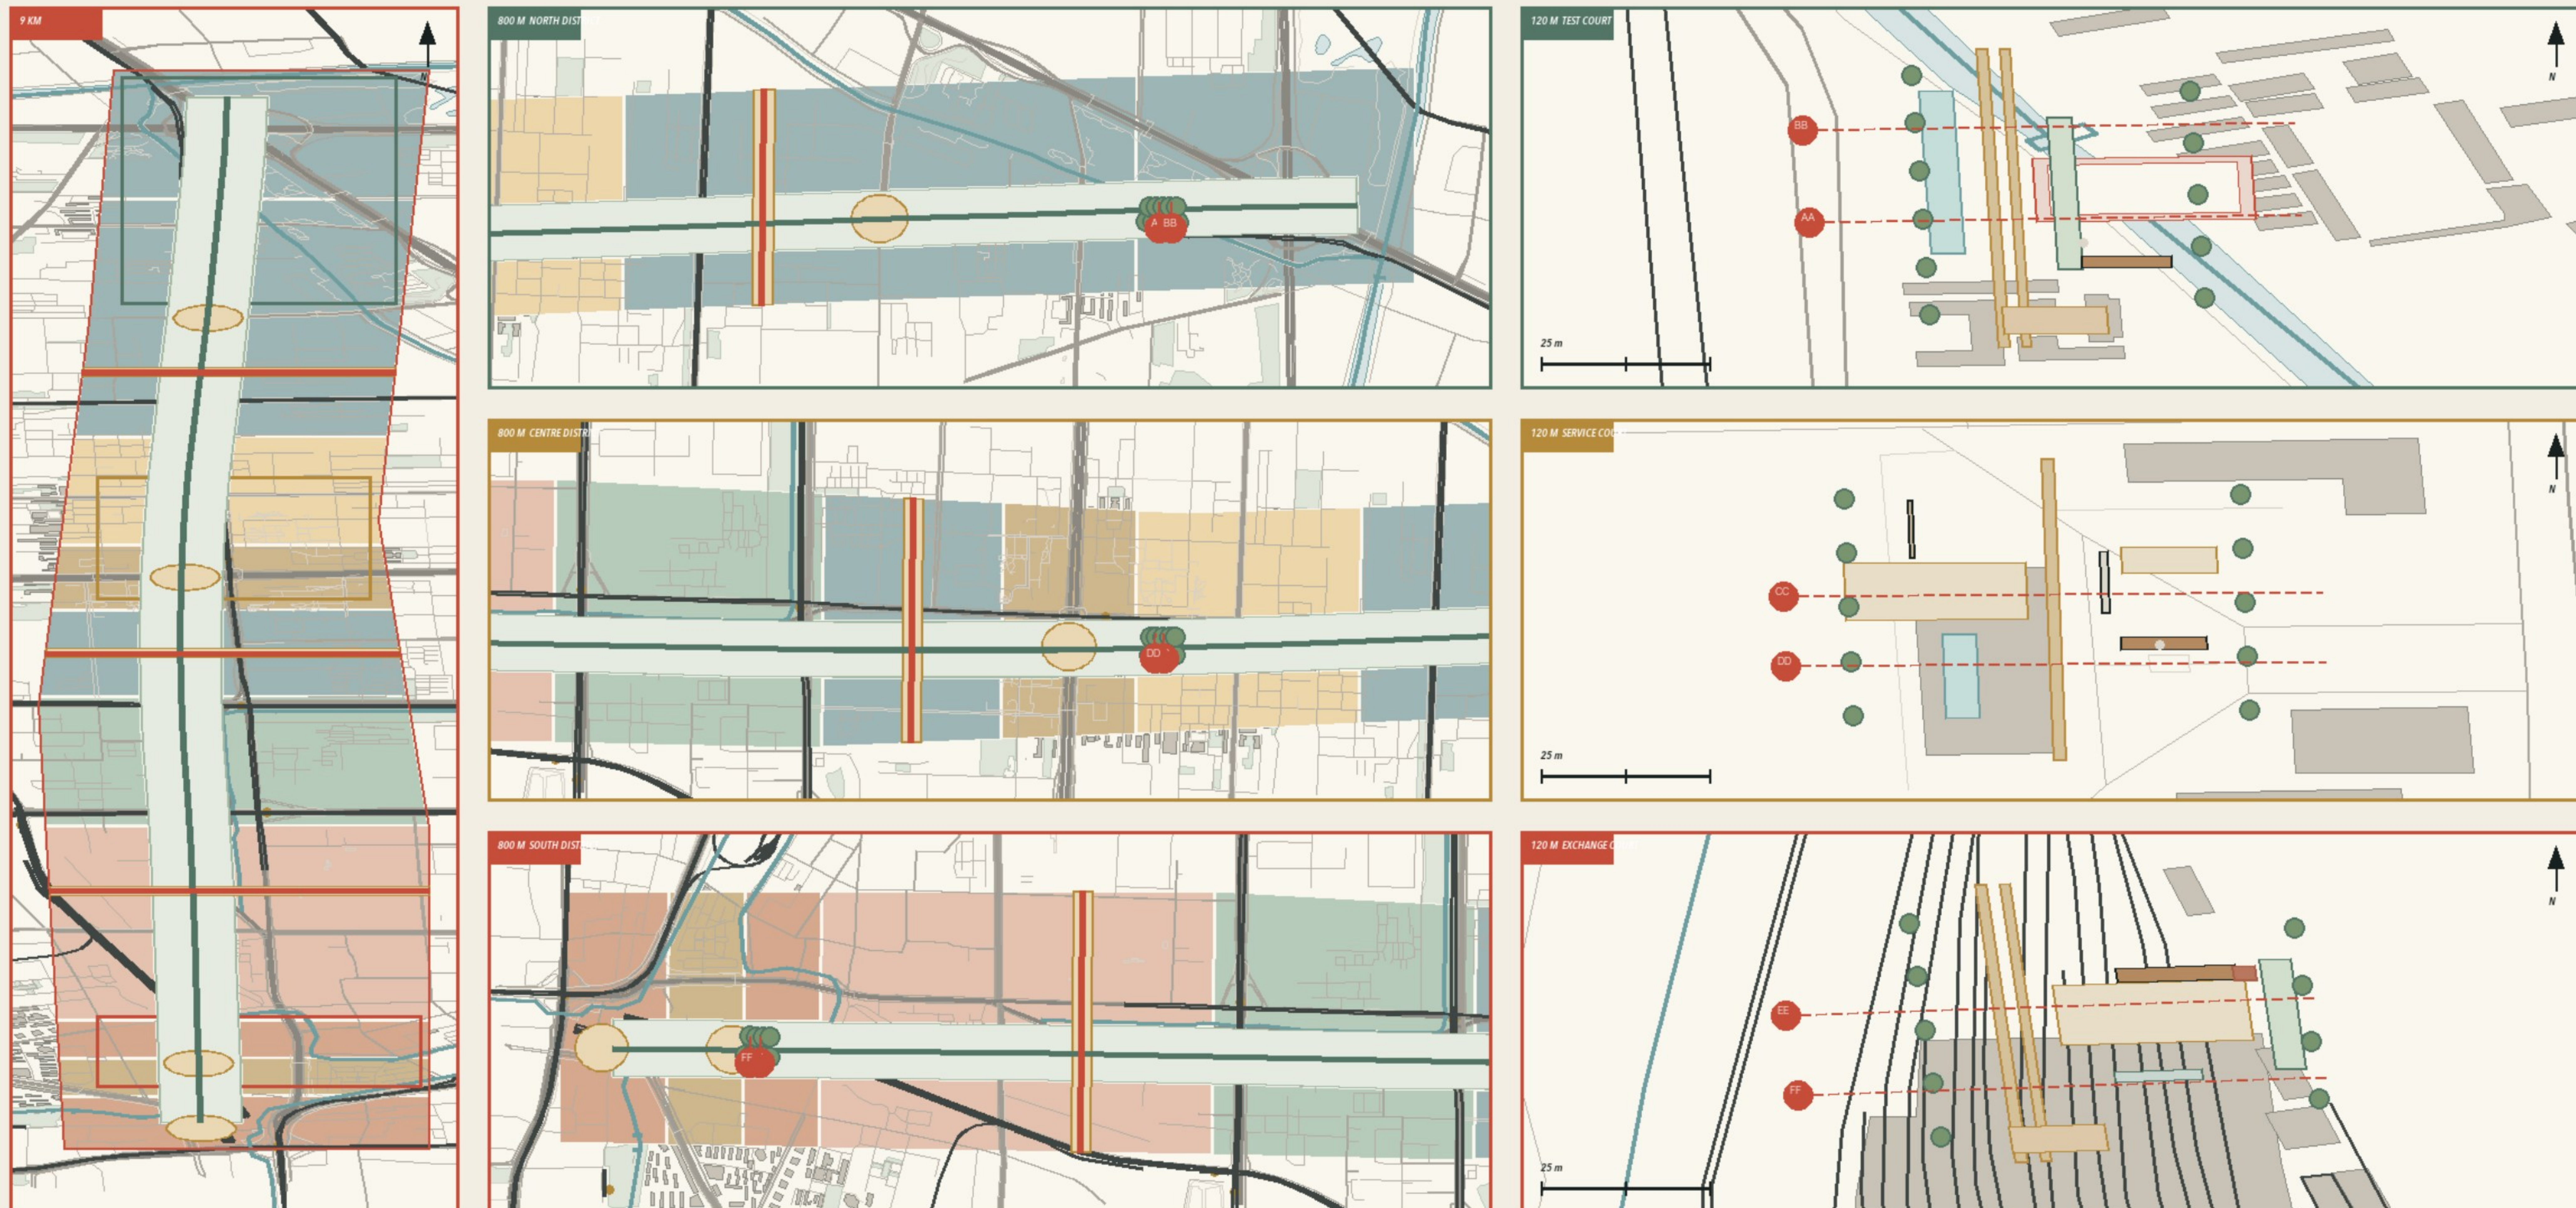

CONCEPT DESIGN PROVISIONAL BOUNDARY OSM FOR CONTEXT ONLY

Scale structure informed by REN AXIS (CC BY 4.0); redrawn for this proposal

ONE PARK, THREE COURTYARDS

RAILWAY COMMONS / RESEARCH · SERVICE · EXCHANGE




● RESEARCH GARDEN

● STAFFED SERVICE

● EVERYDAY EXCHANGE

SPATIAL-LANGUAGE COMPOSITE / COURTYARDS ARE NOT SHOWN AT TRUE DISTANCE OR SCALE

OPEN-CITY-AI / HAIDIAN

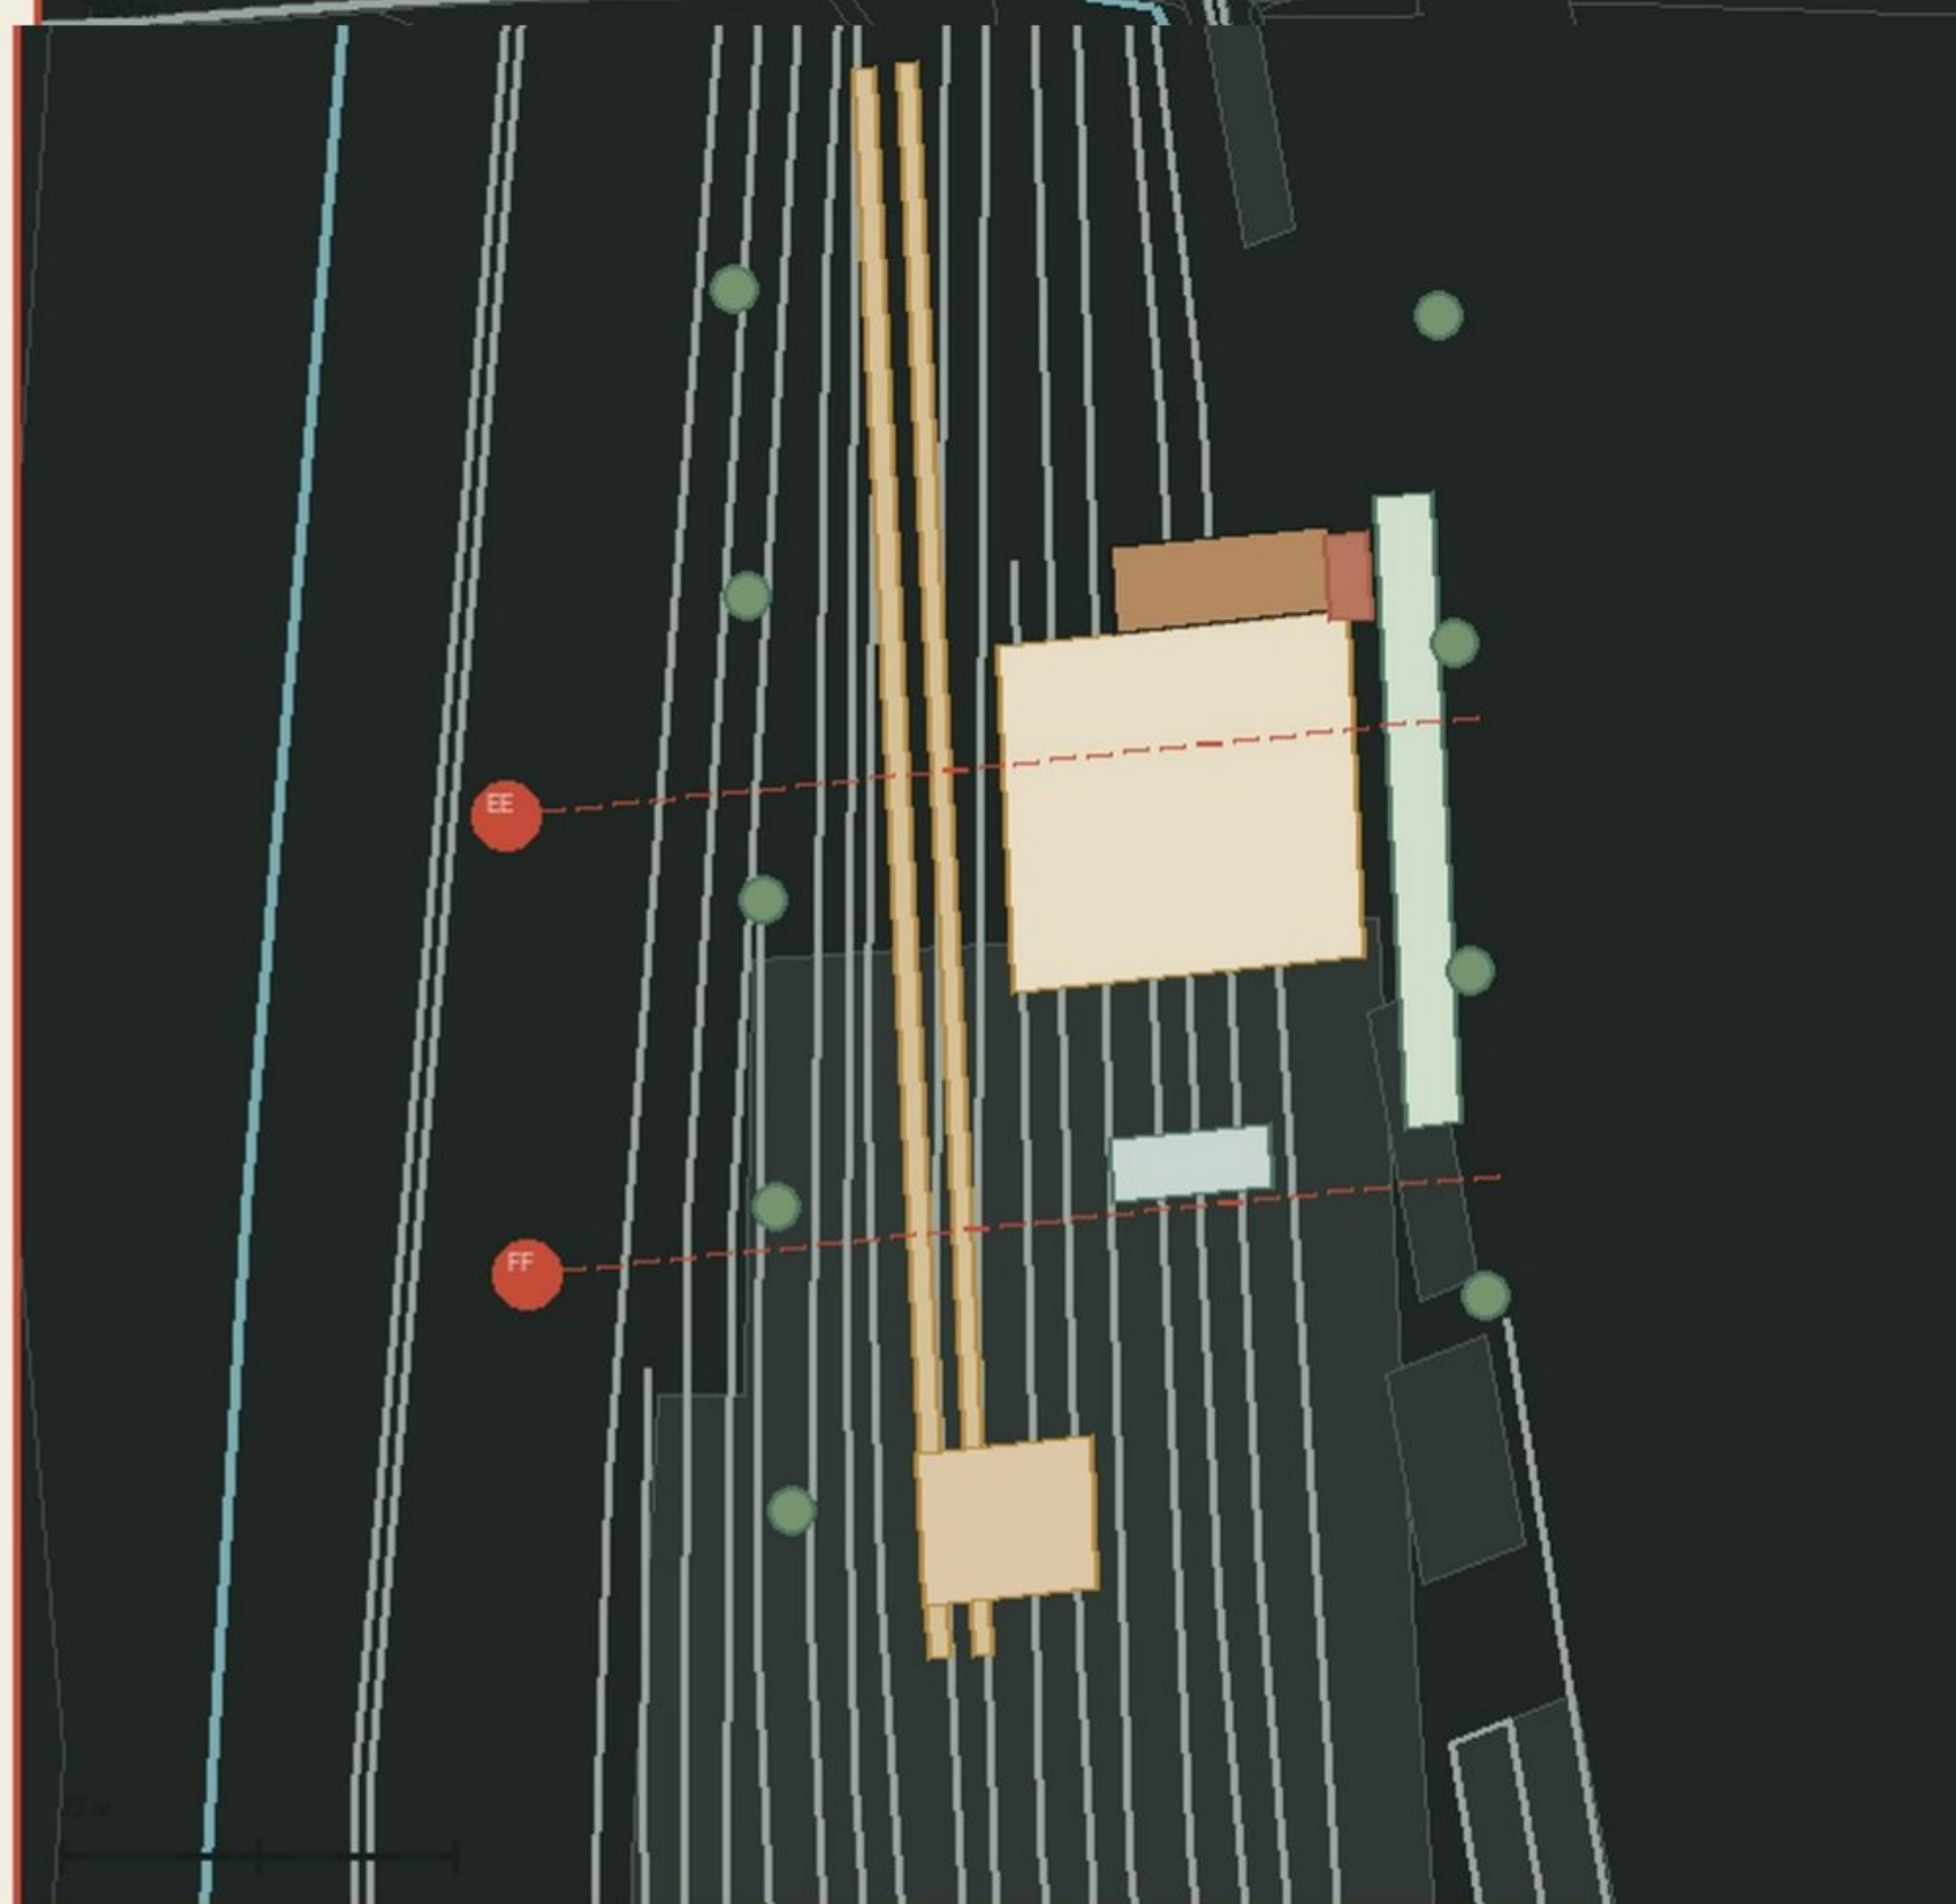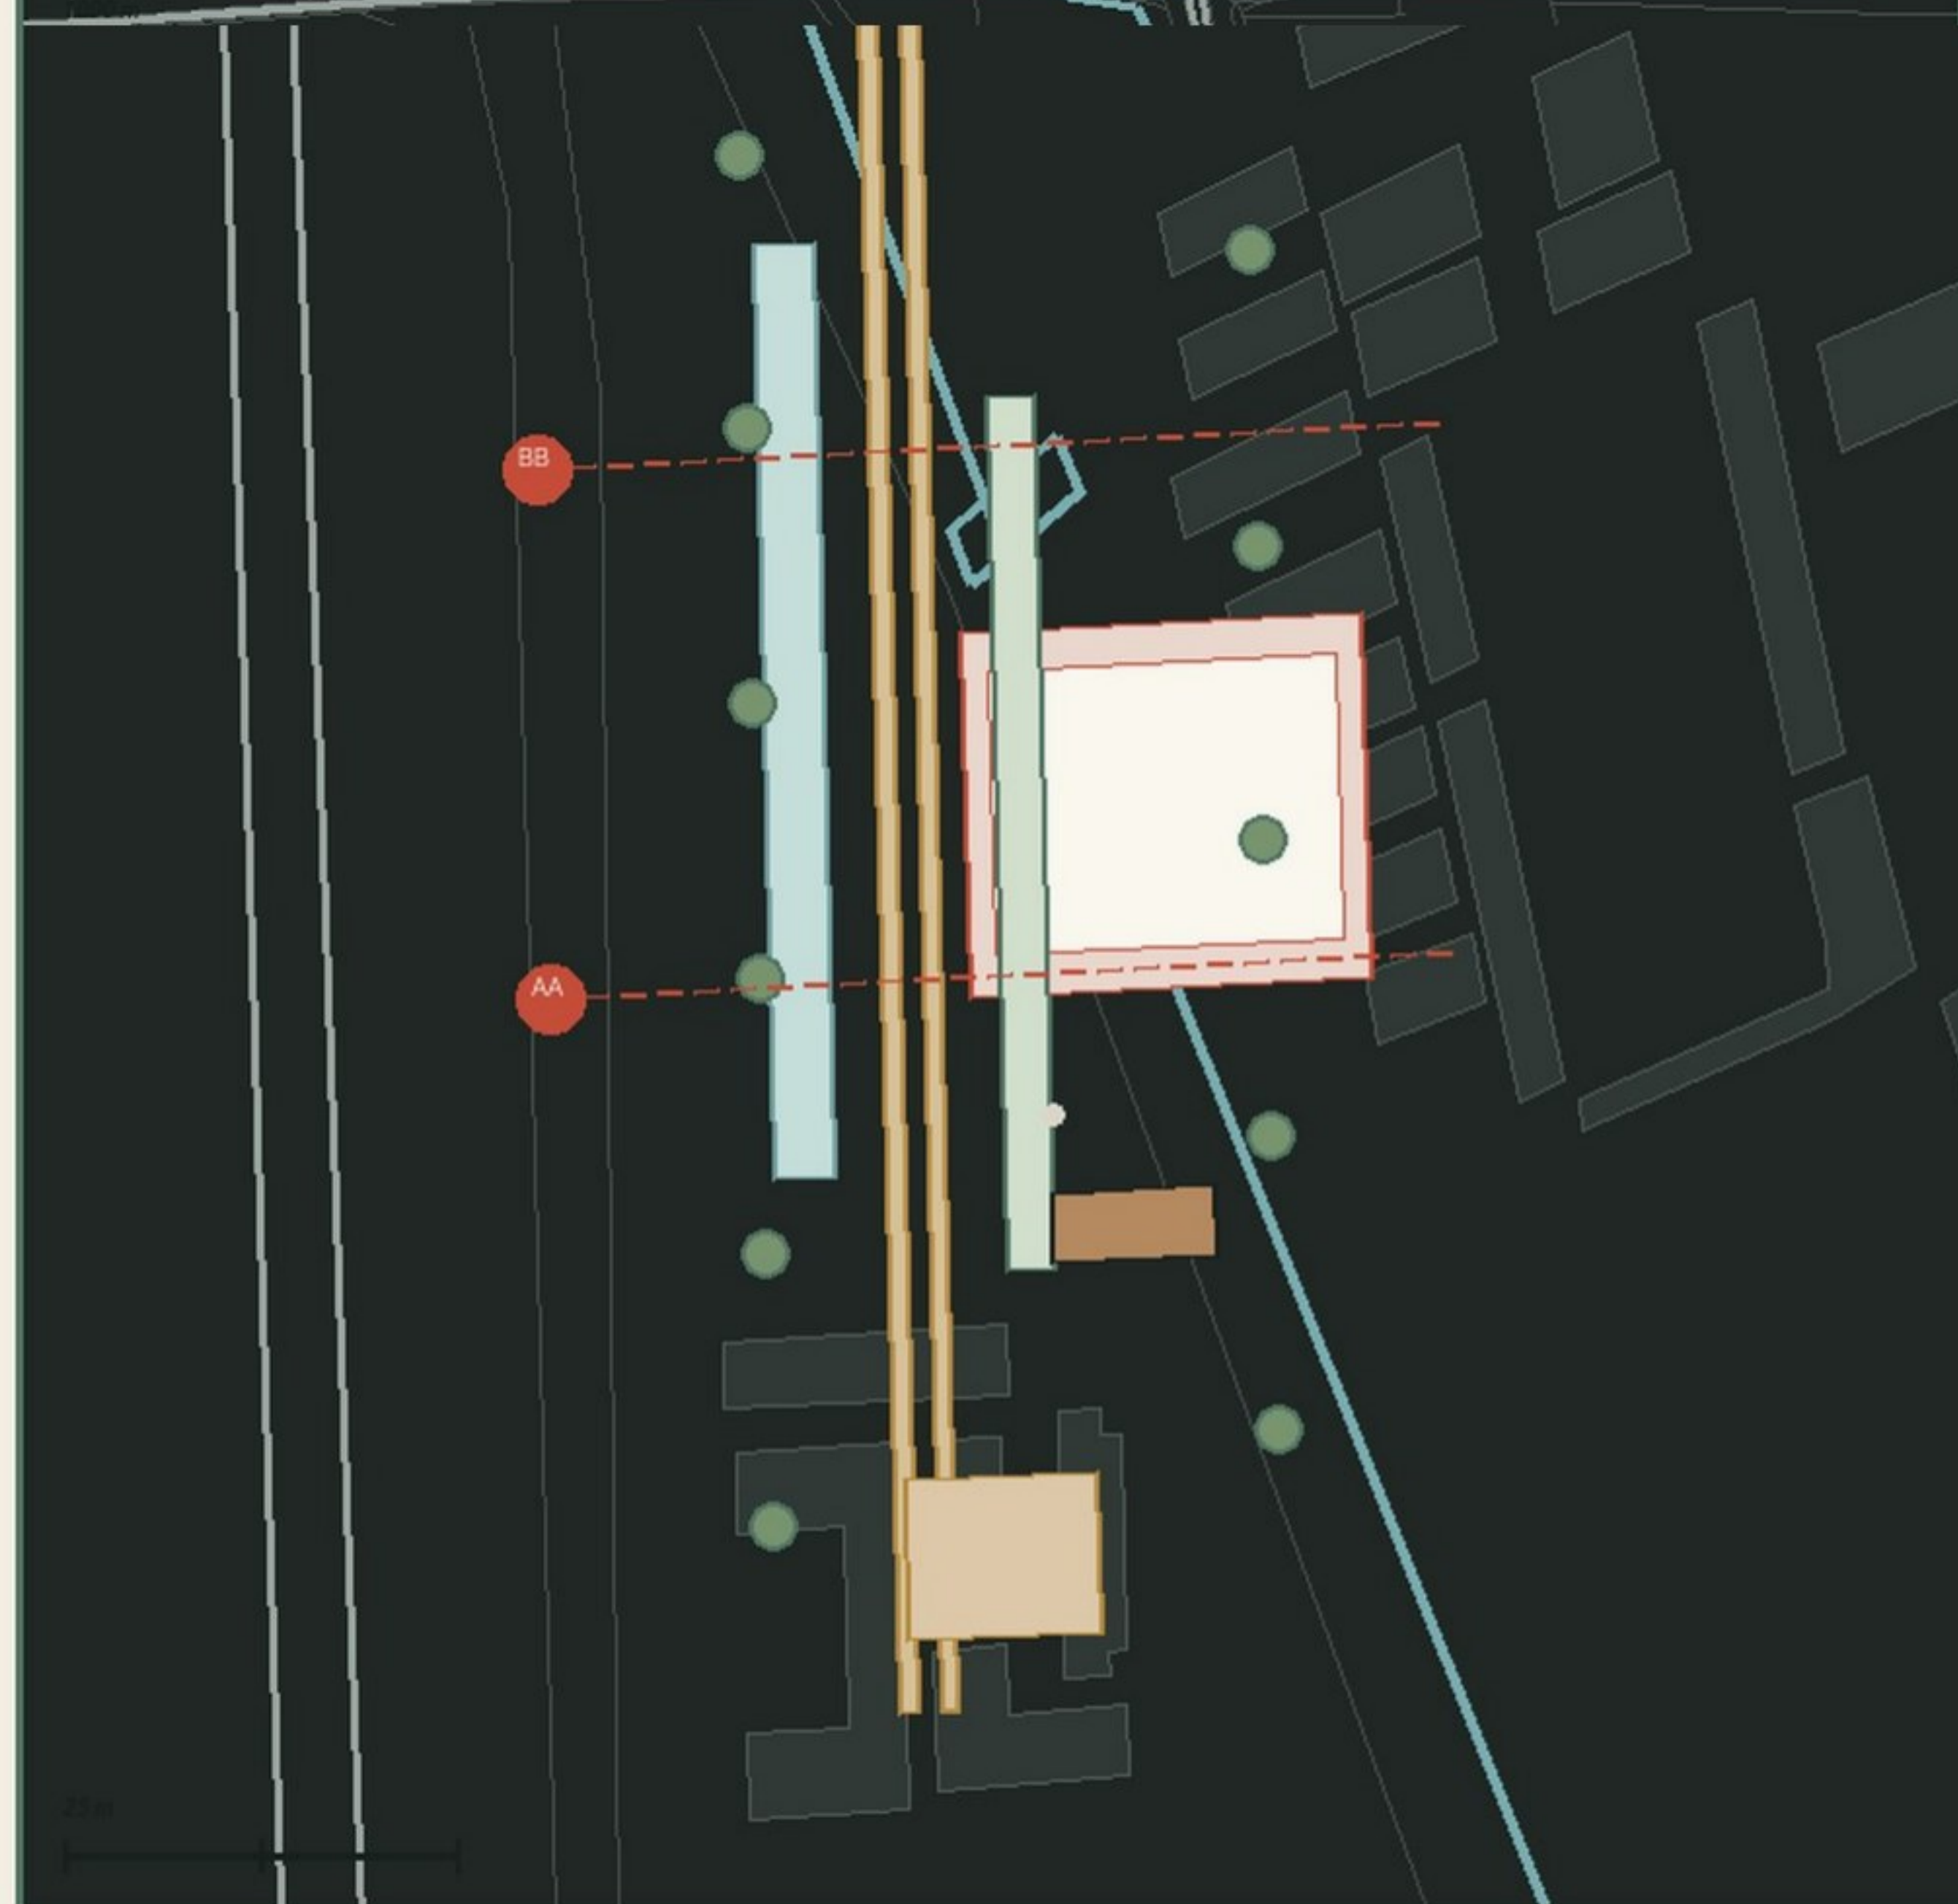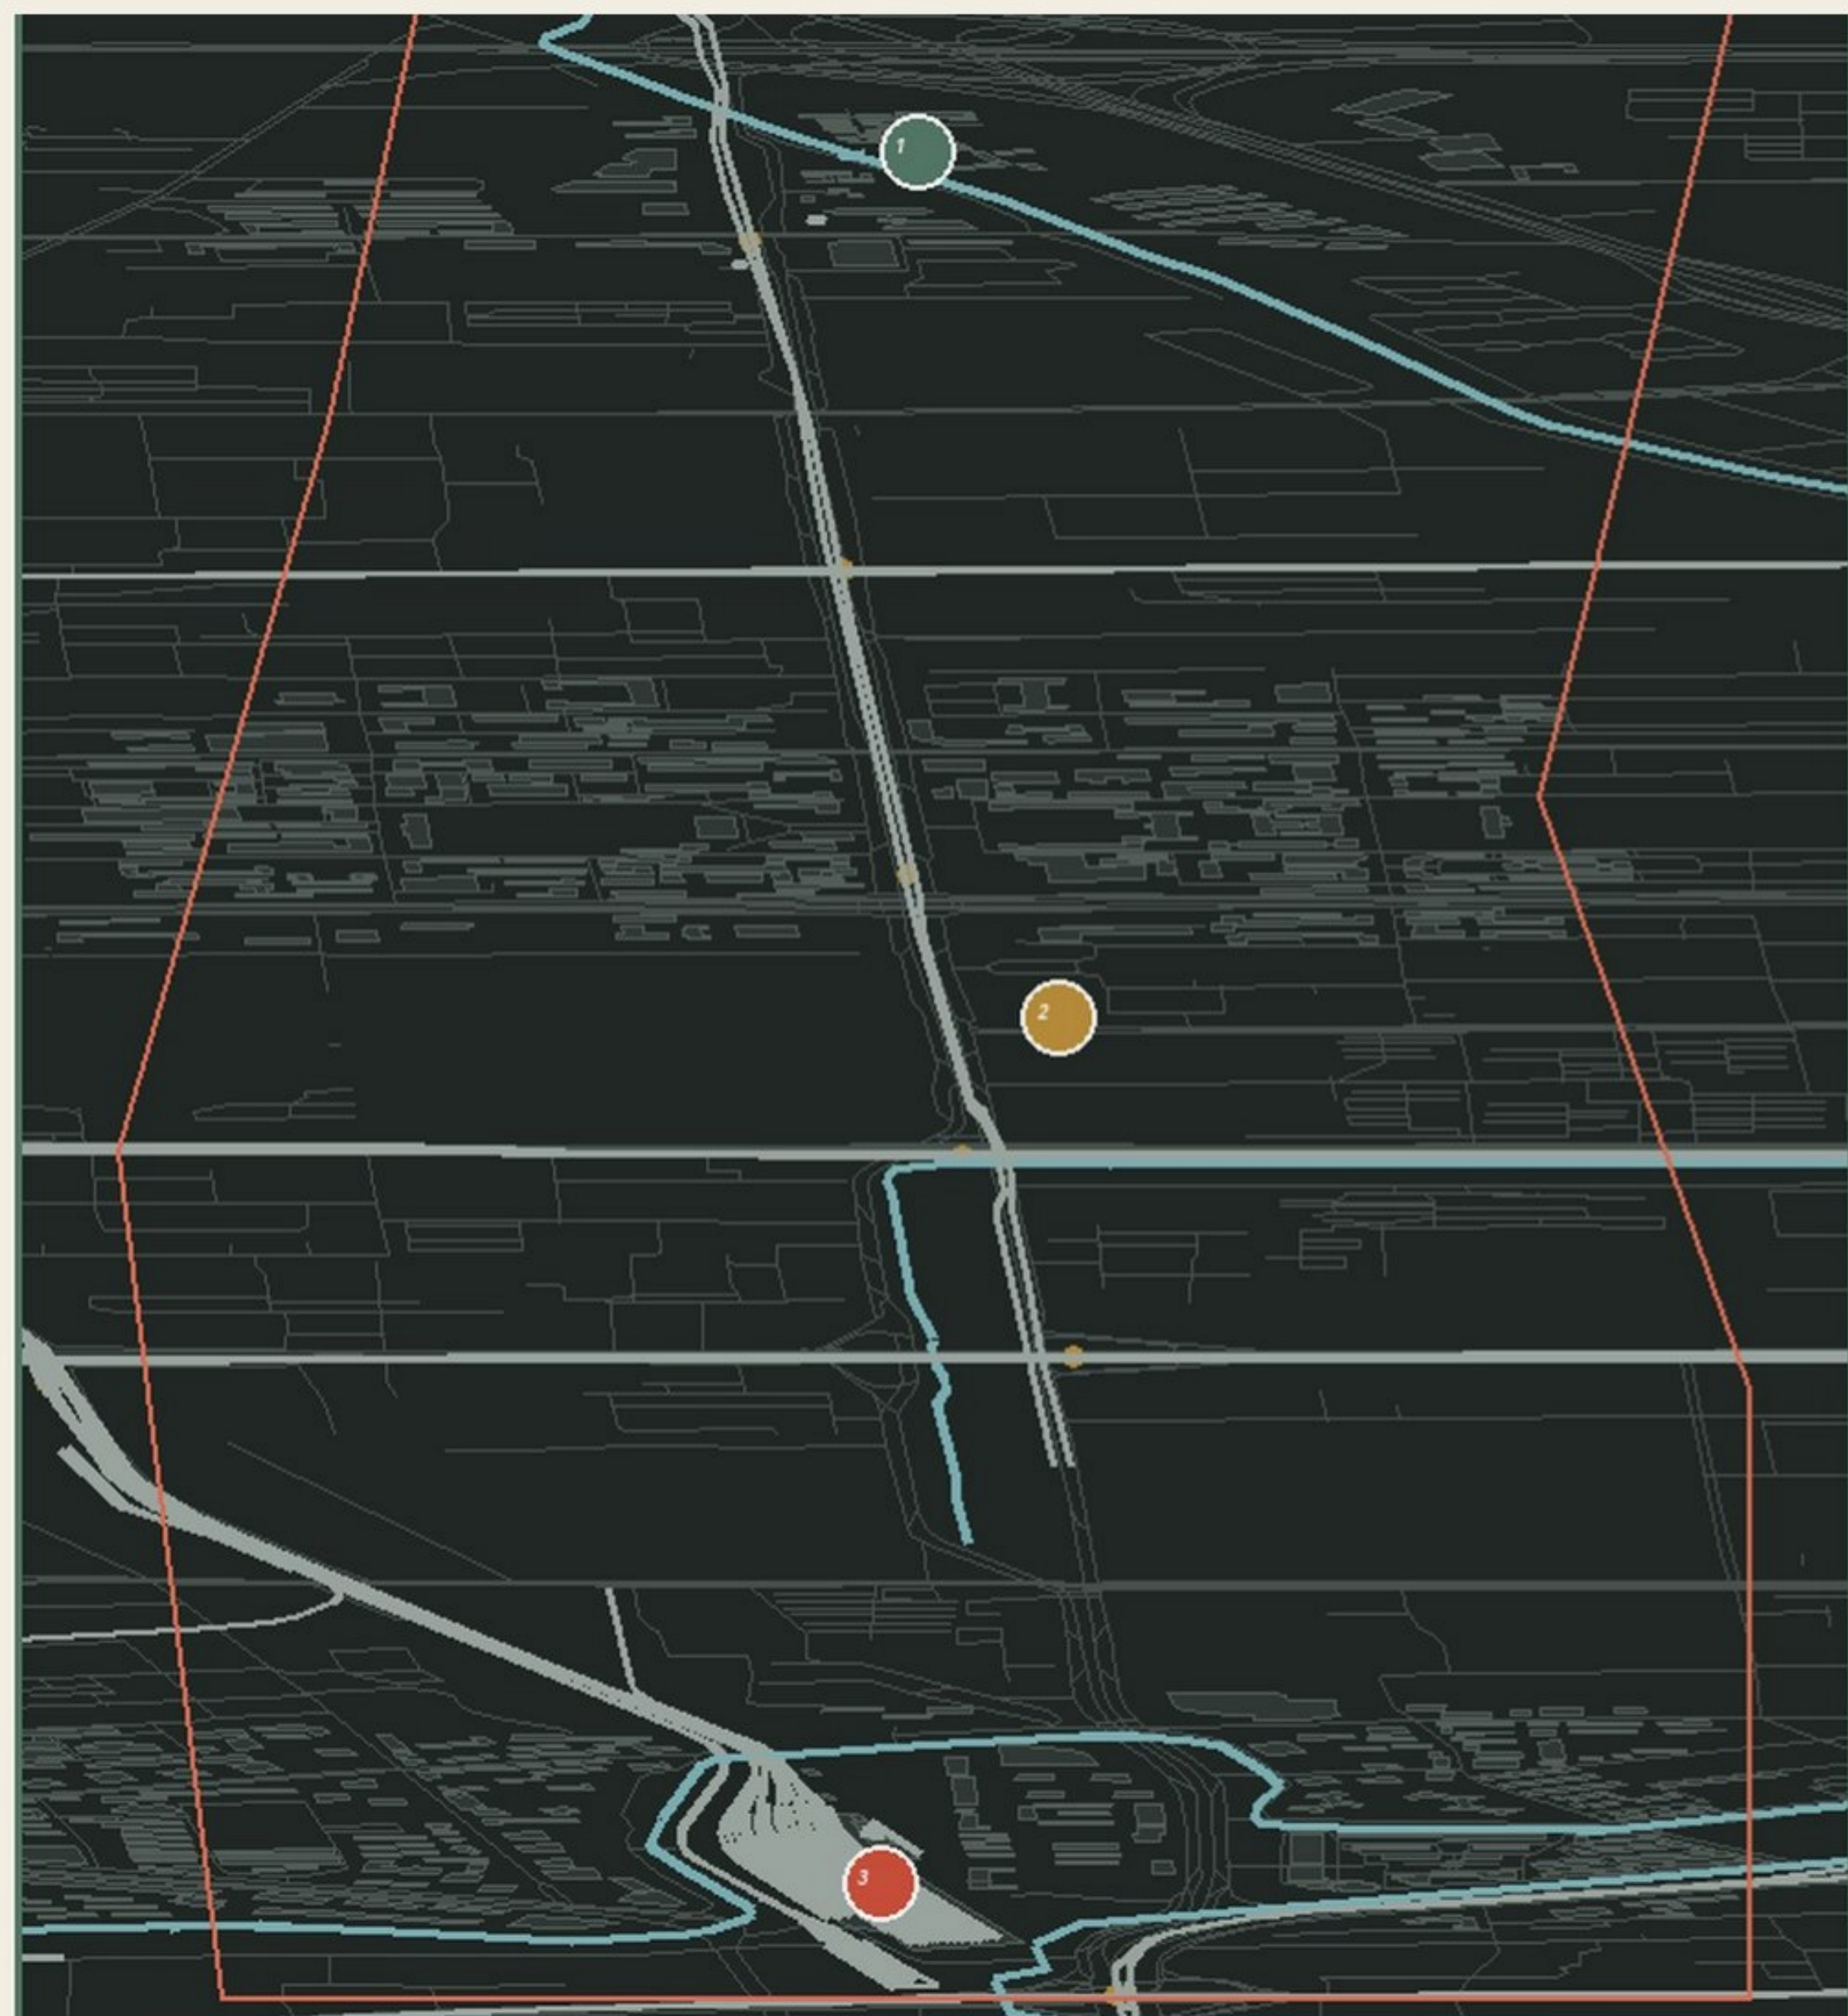

3.2 m

2.8 m

3.5 m

500 m

14 / 6

9