



总体设计图册

九公里折成三幅城市图，已建、公开计划与本案增量同图阅读


01 北段 众智园与小月河

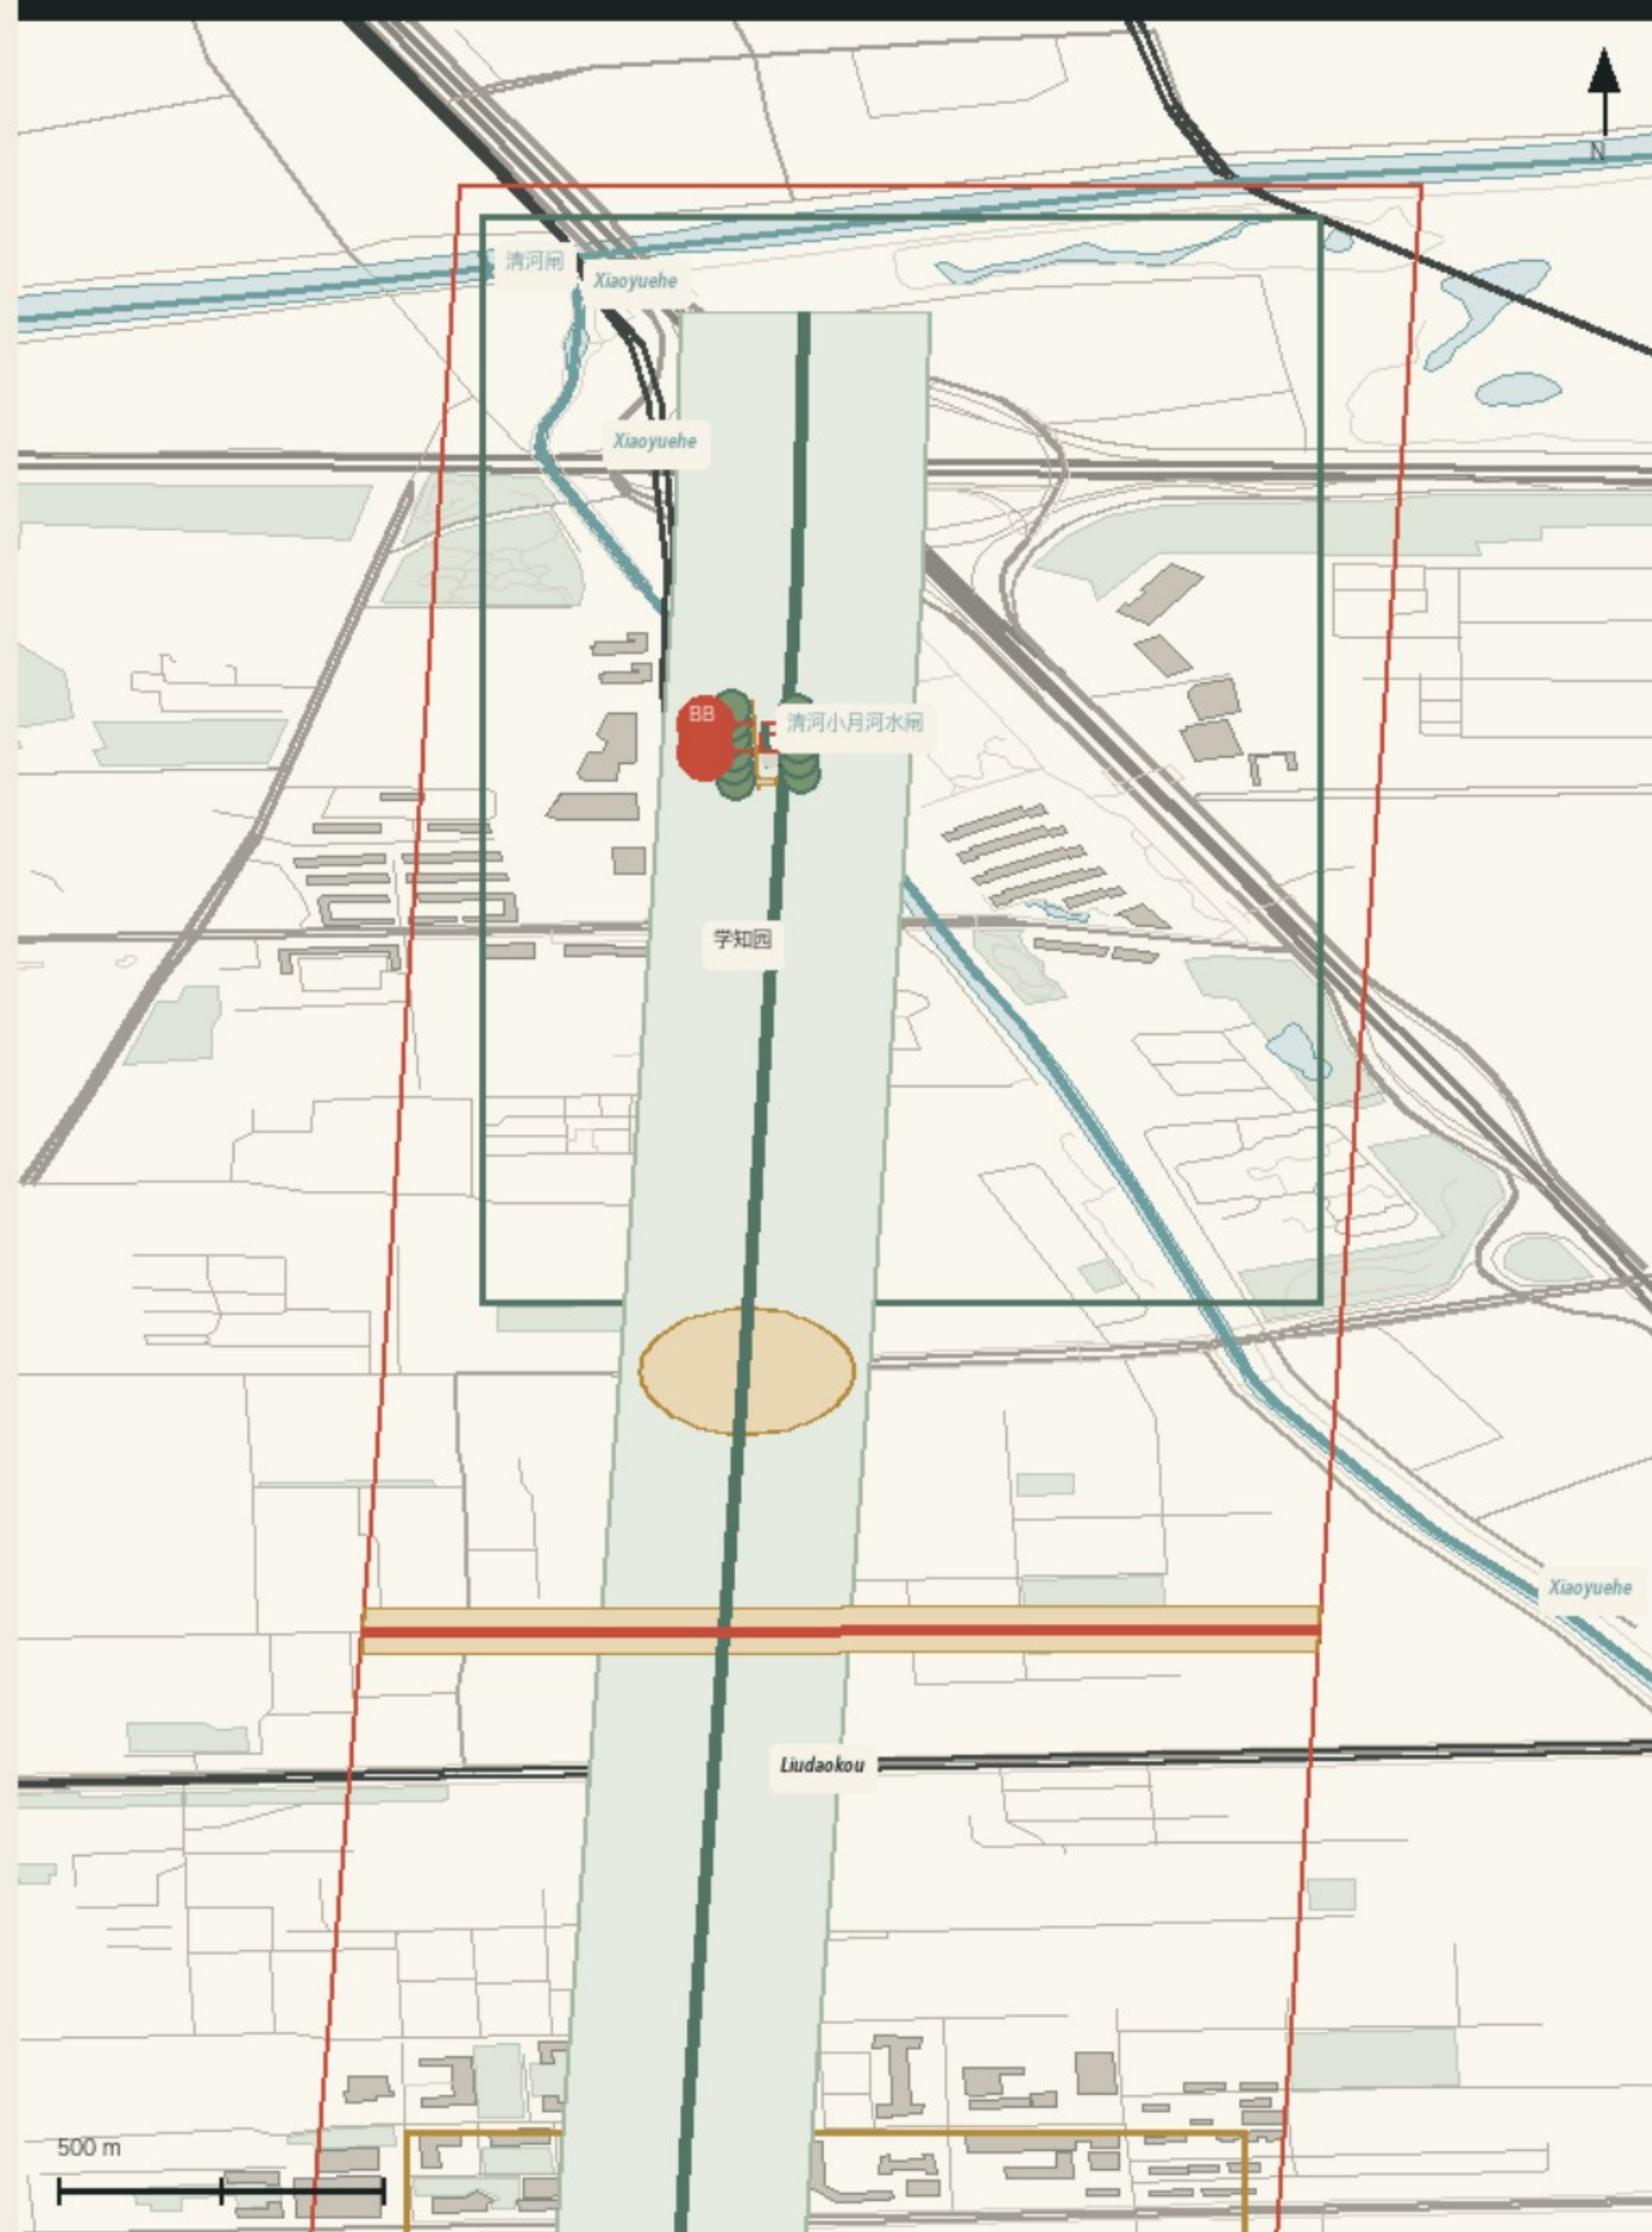

02 中段 AI 原点与学院桥

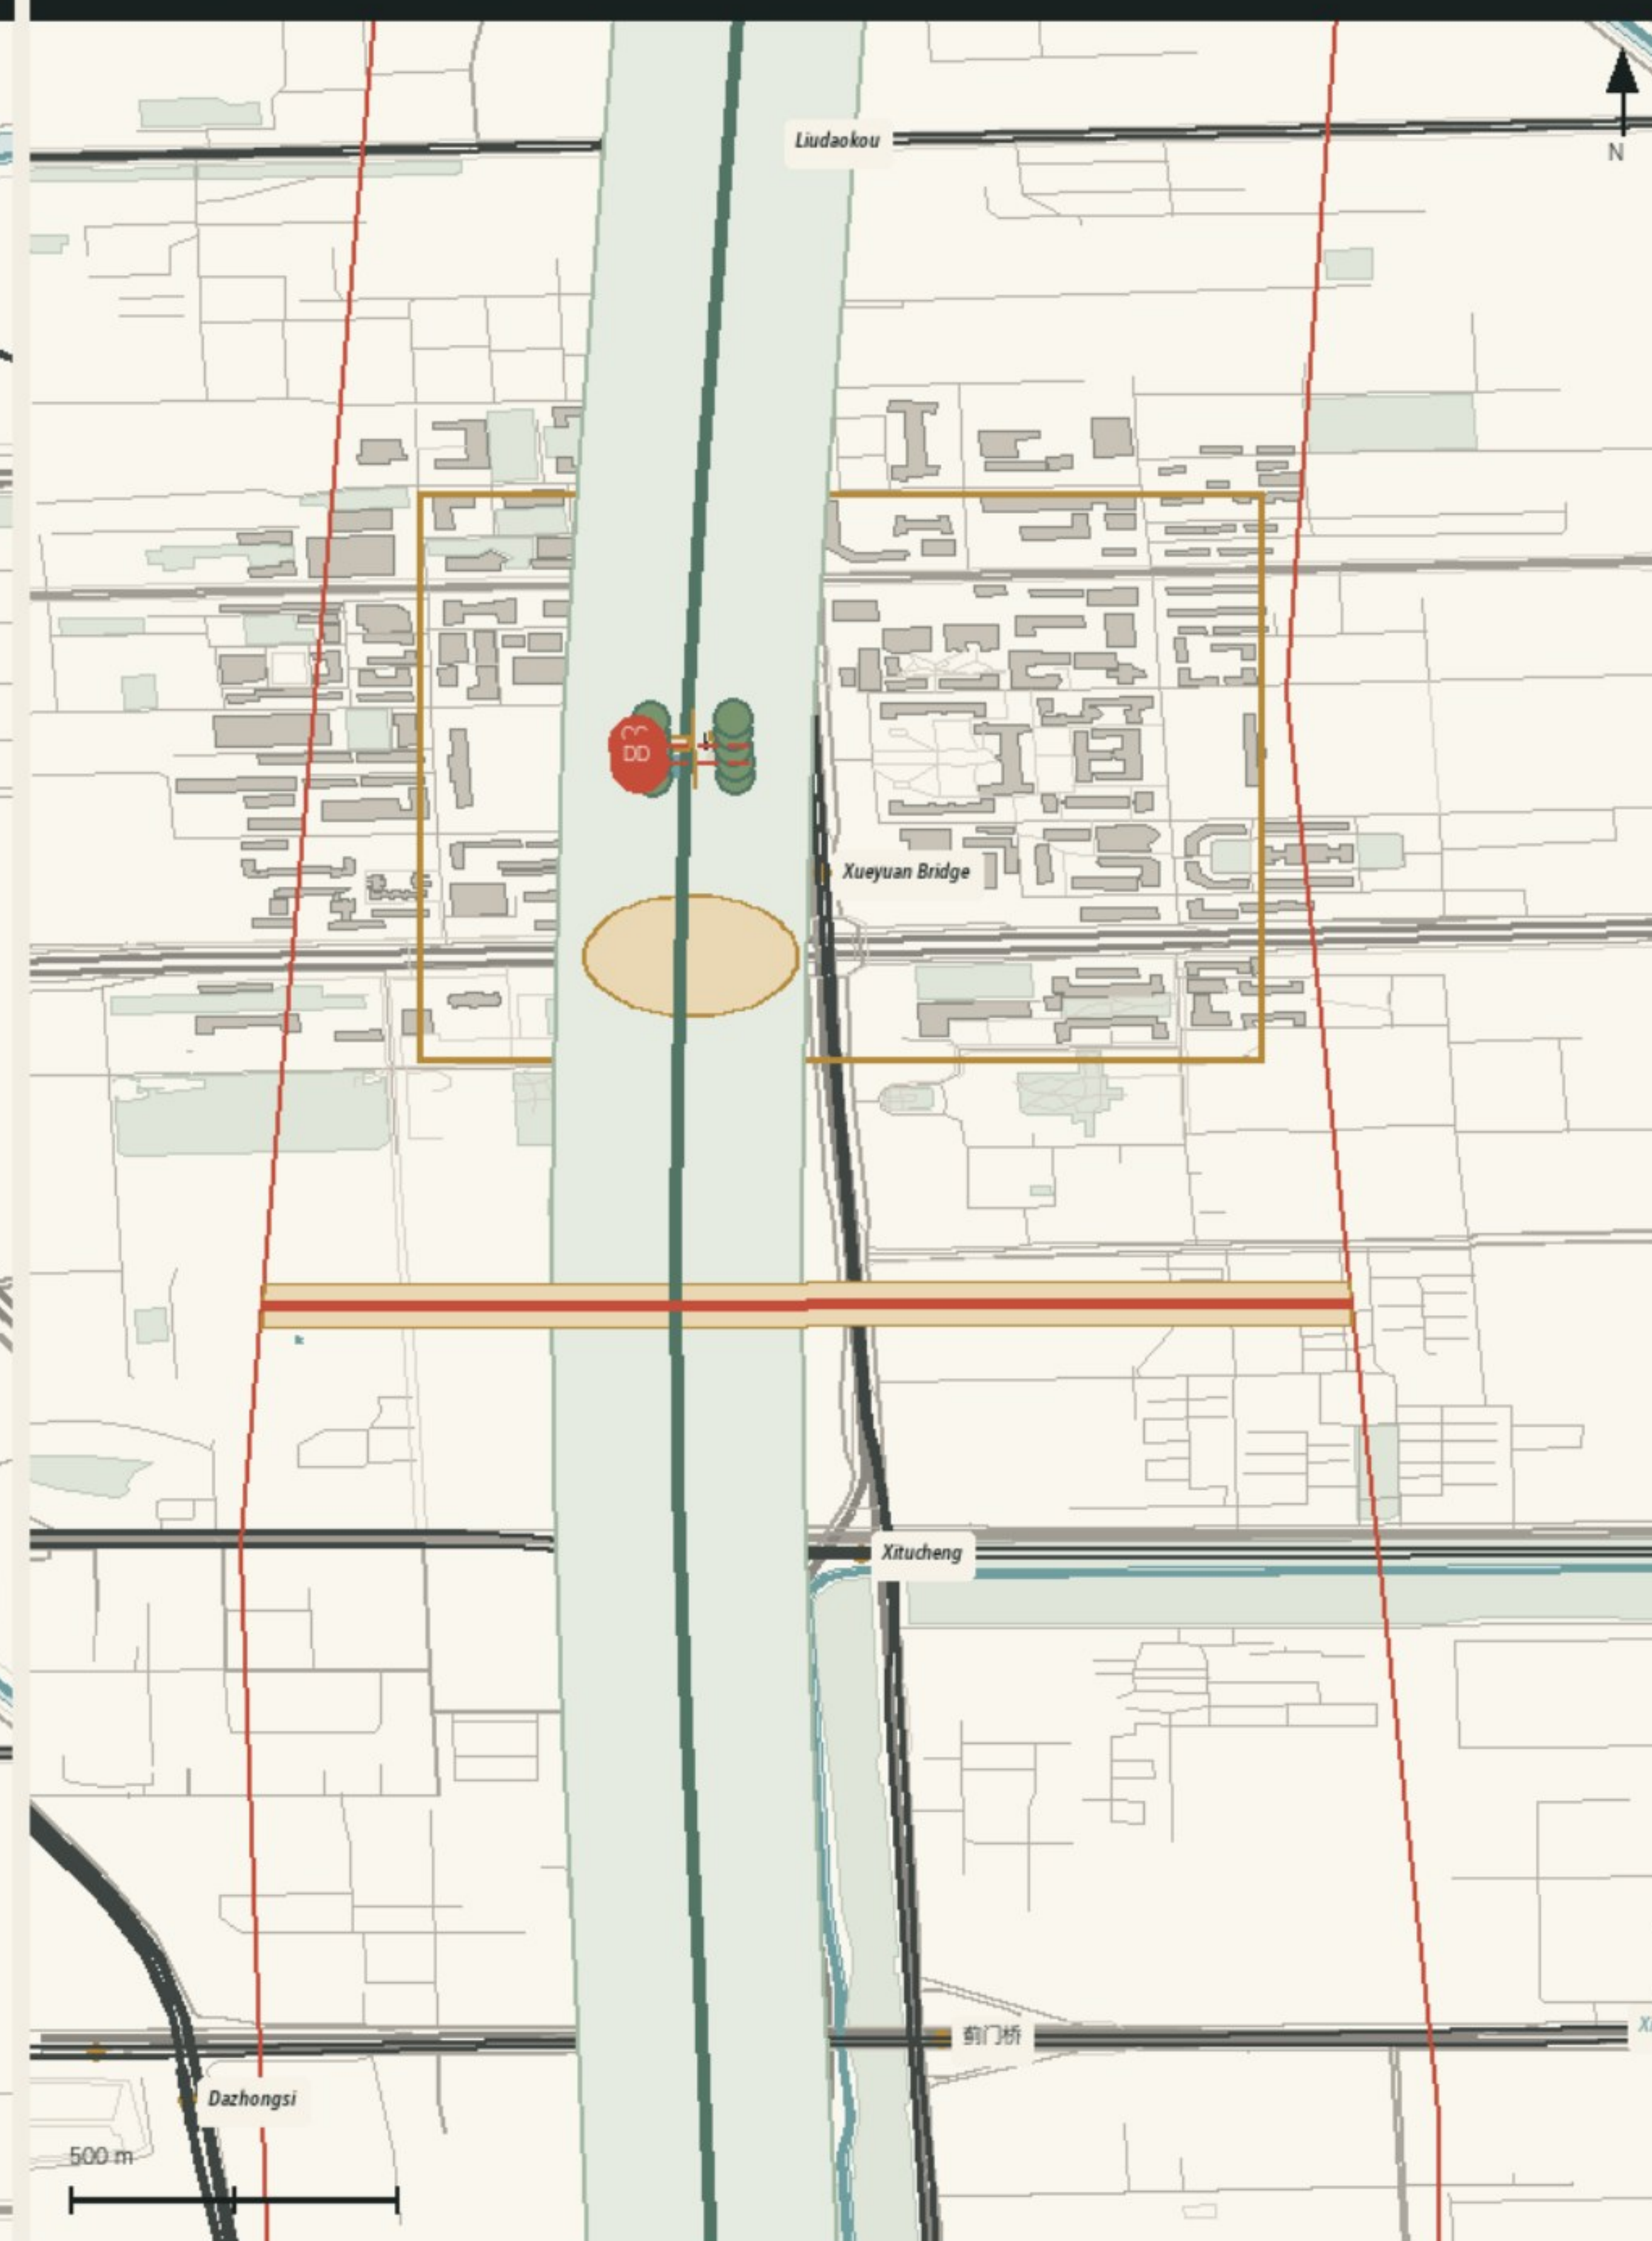

03 南段 大钟寺与交通大学

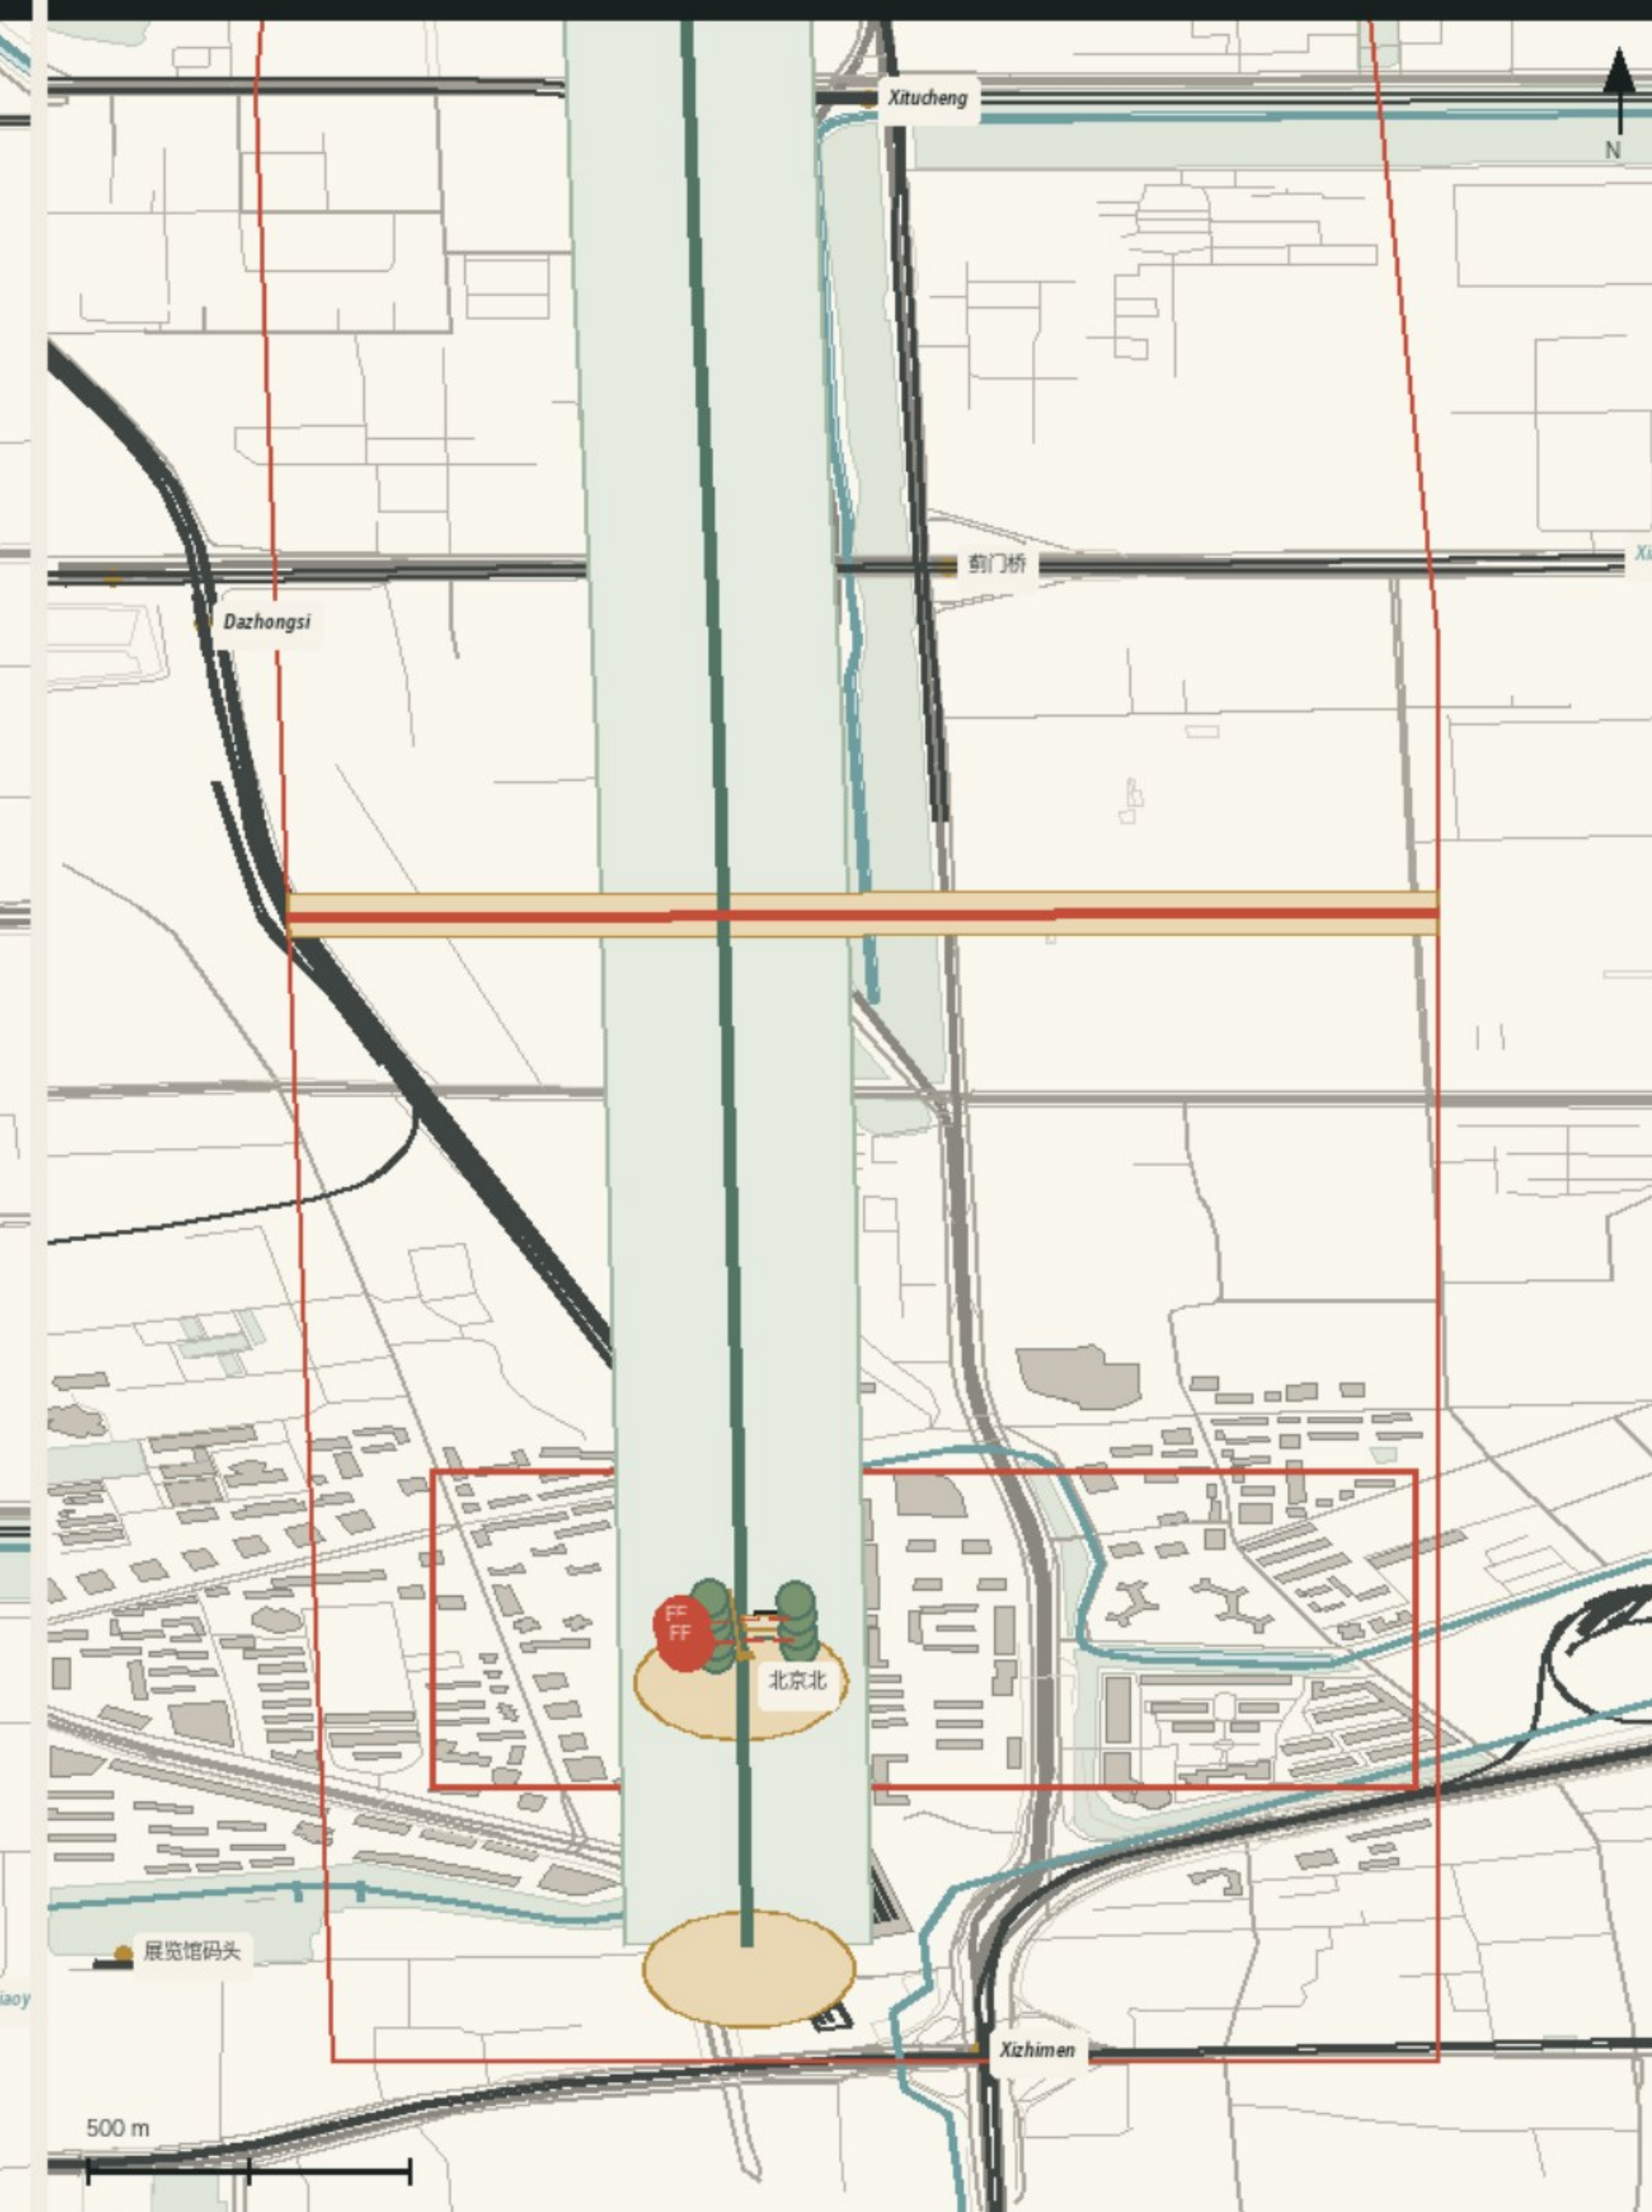




概念方案 暂定边界 OSM 仅作参考语境

© OpenStreetMap contributors ODbL 1.0






03 三处重点地区
同一比例尺的平面、剖切线与日常界面

01 众智园试验院

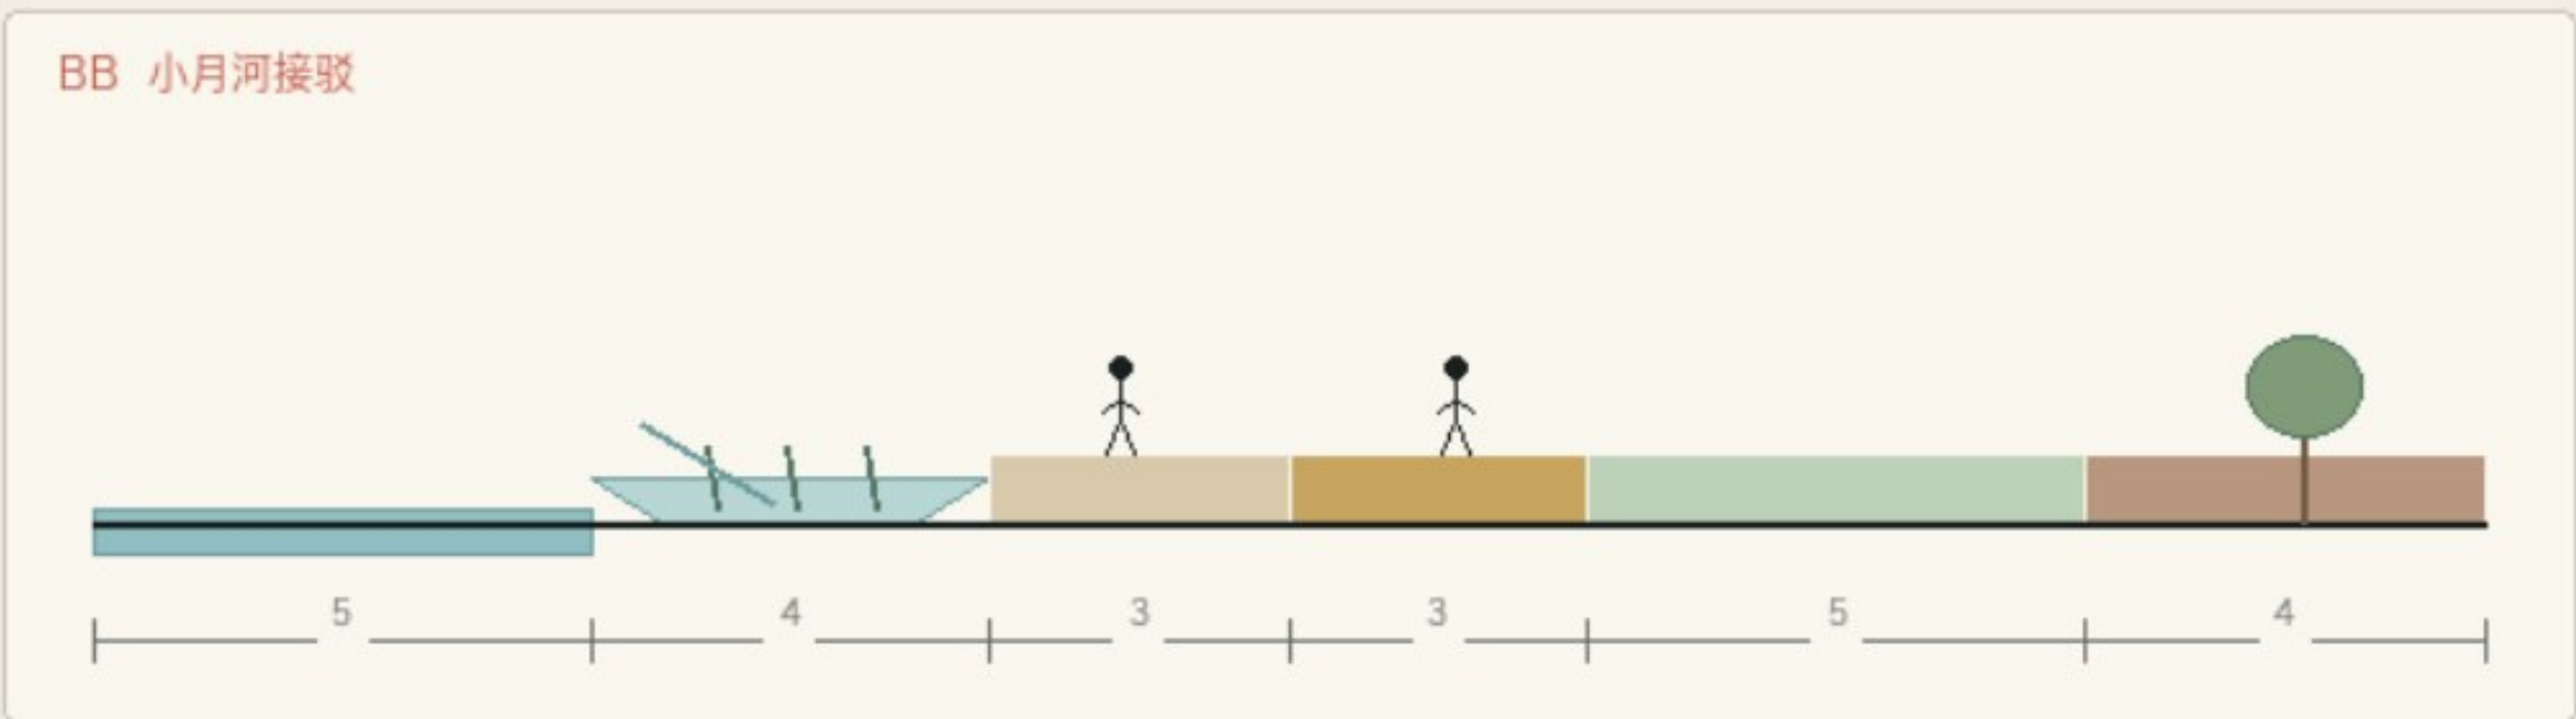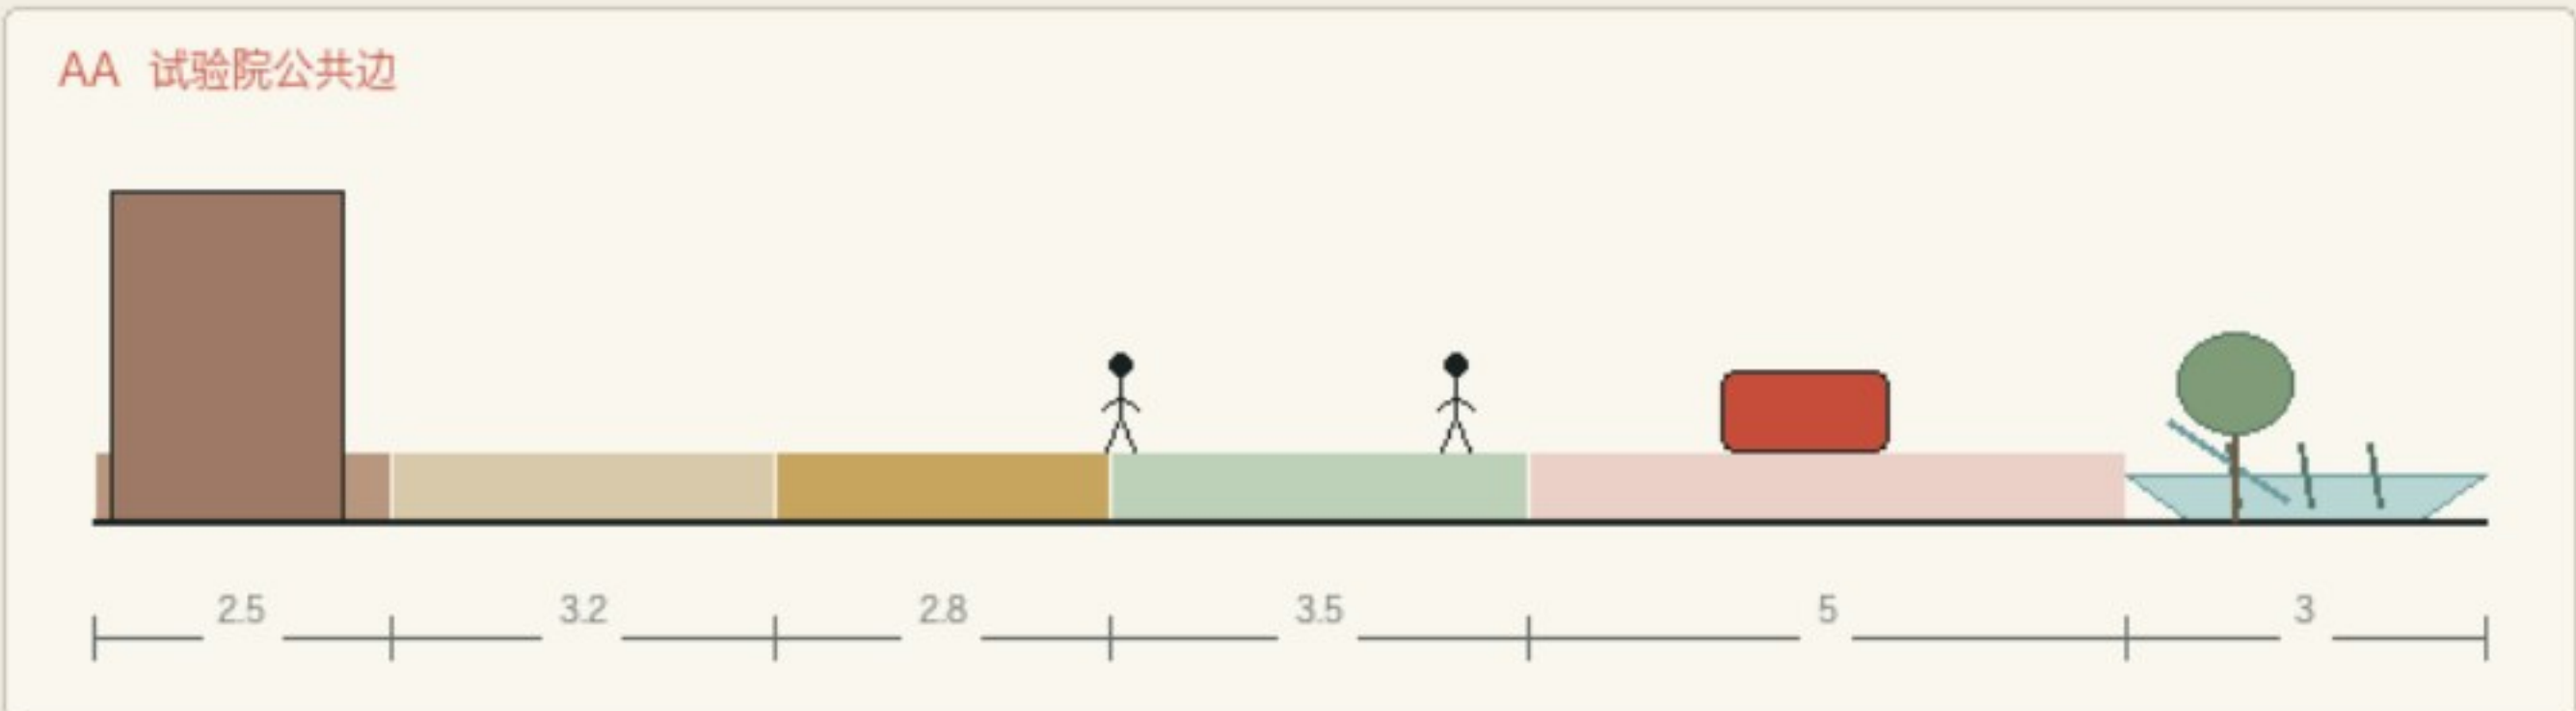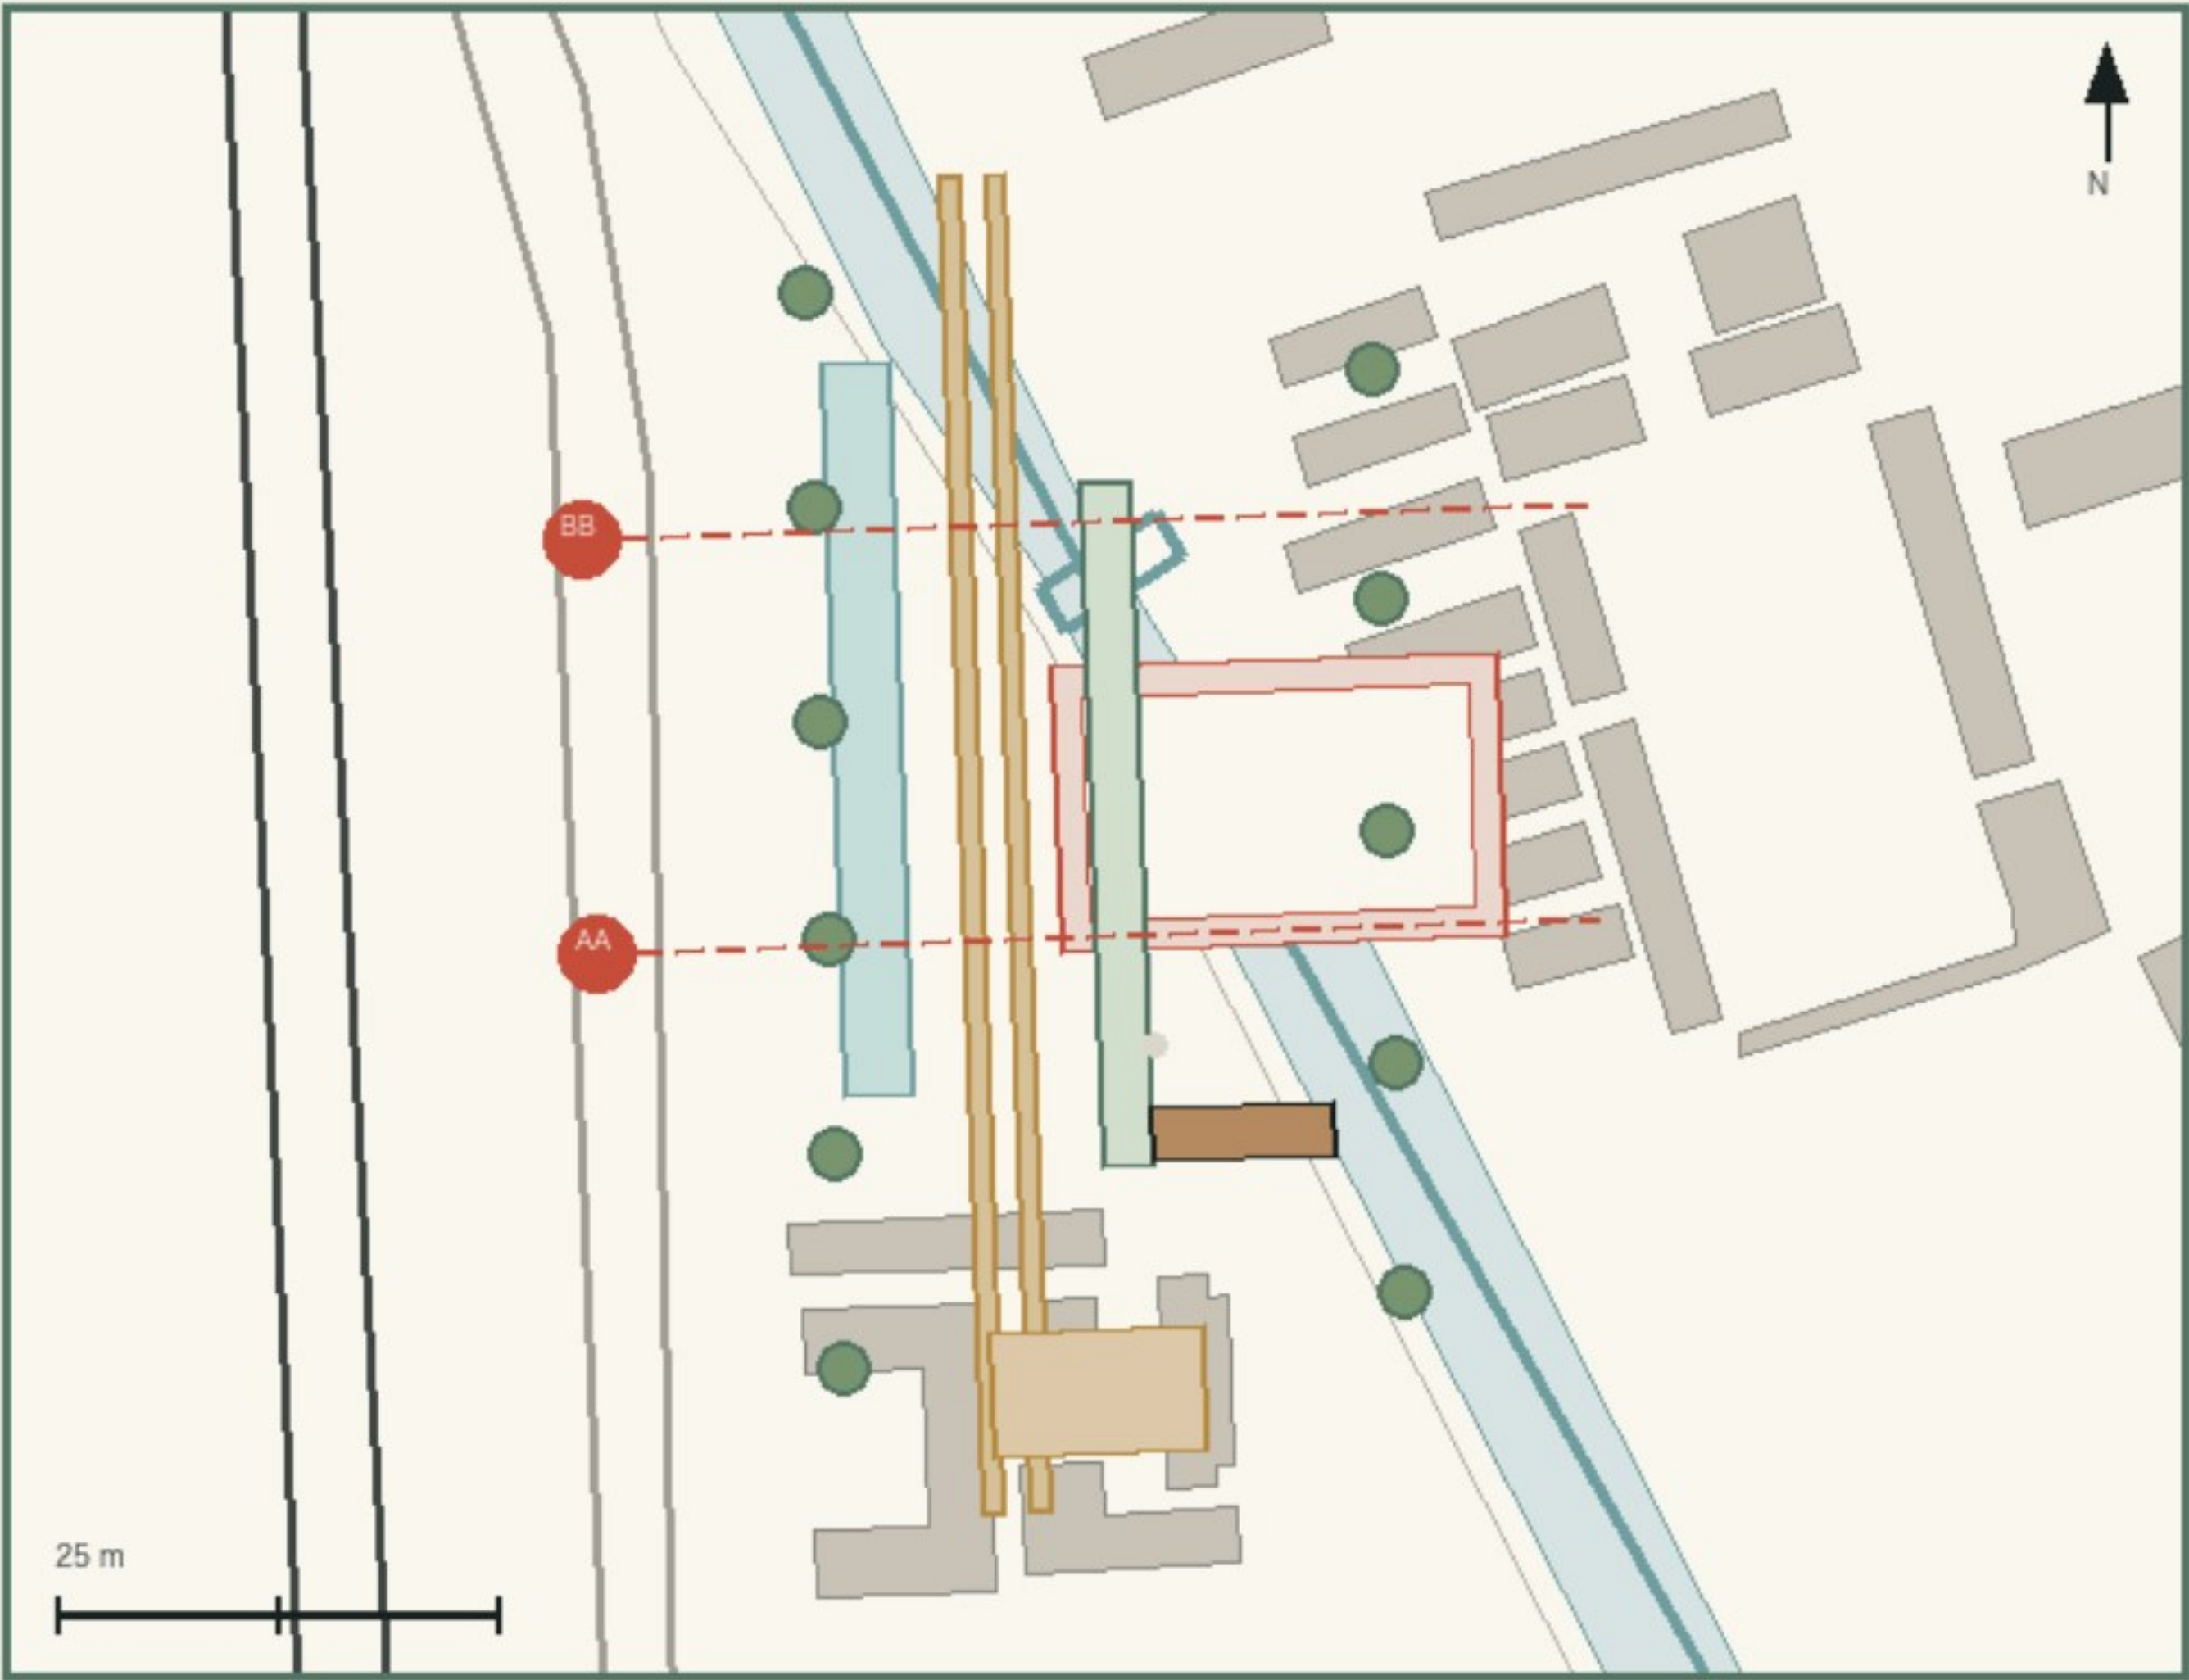




公共步行 铺装 雨庭 可撤构筑 试验边

02 AI 原点服务院

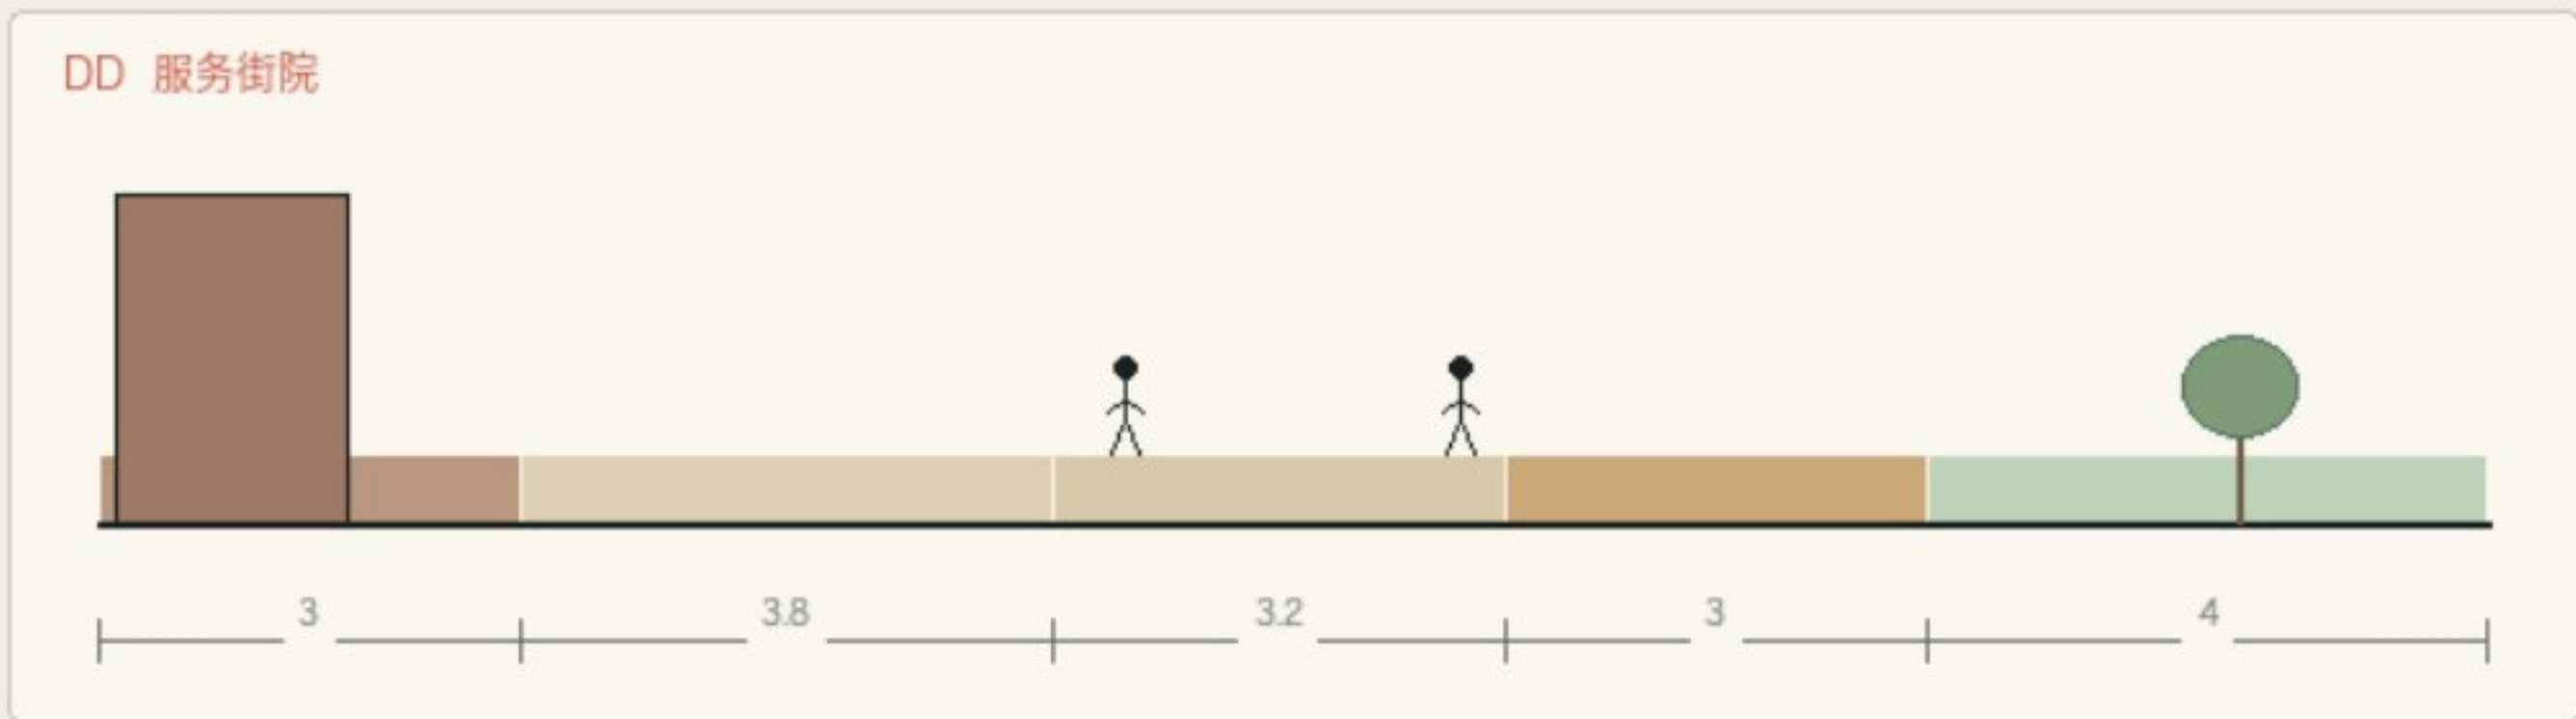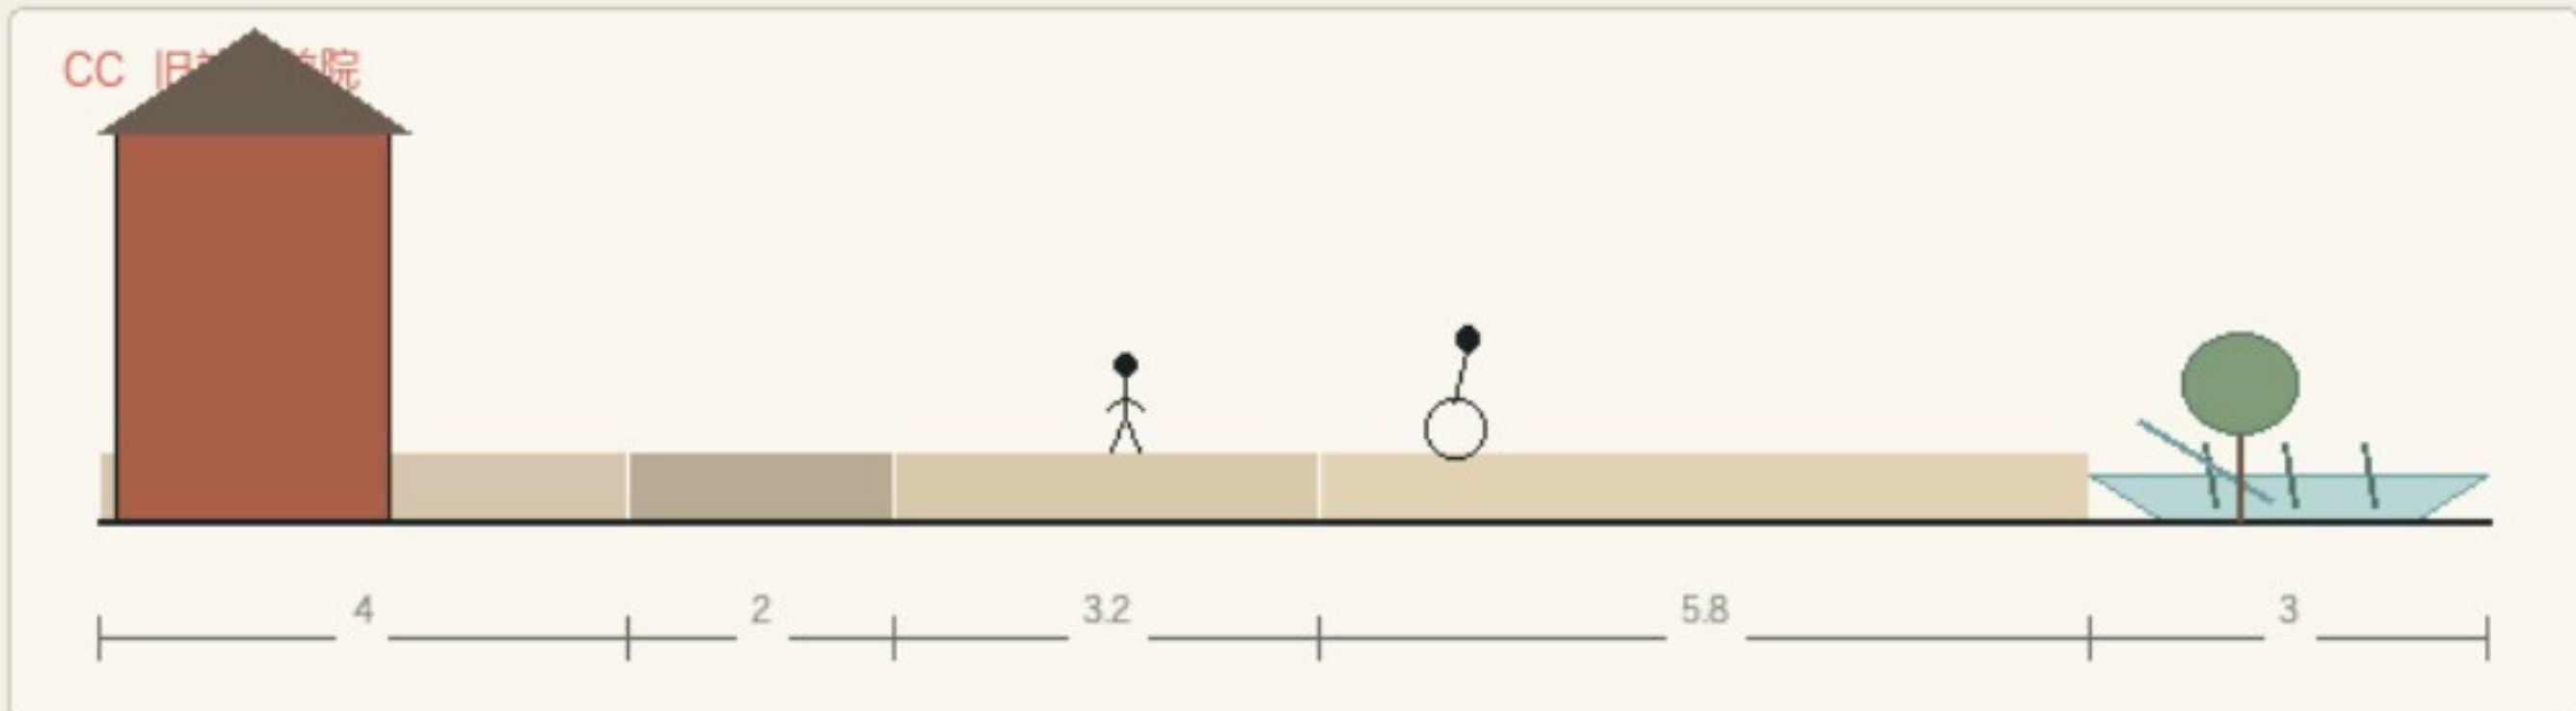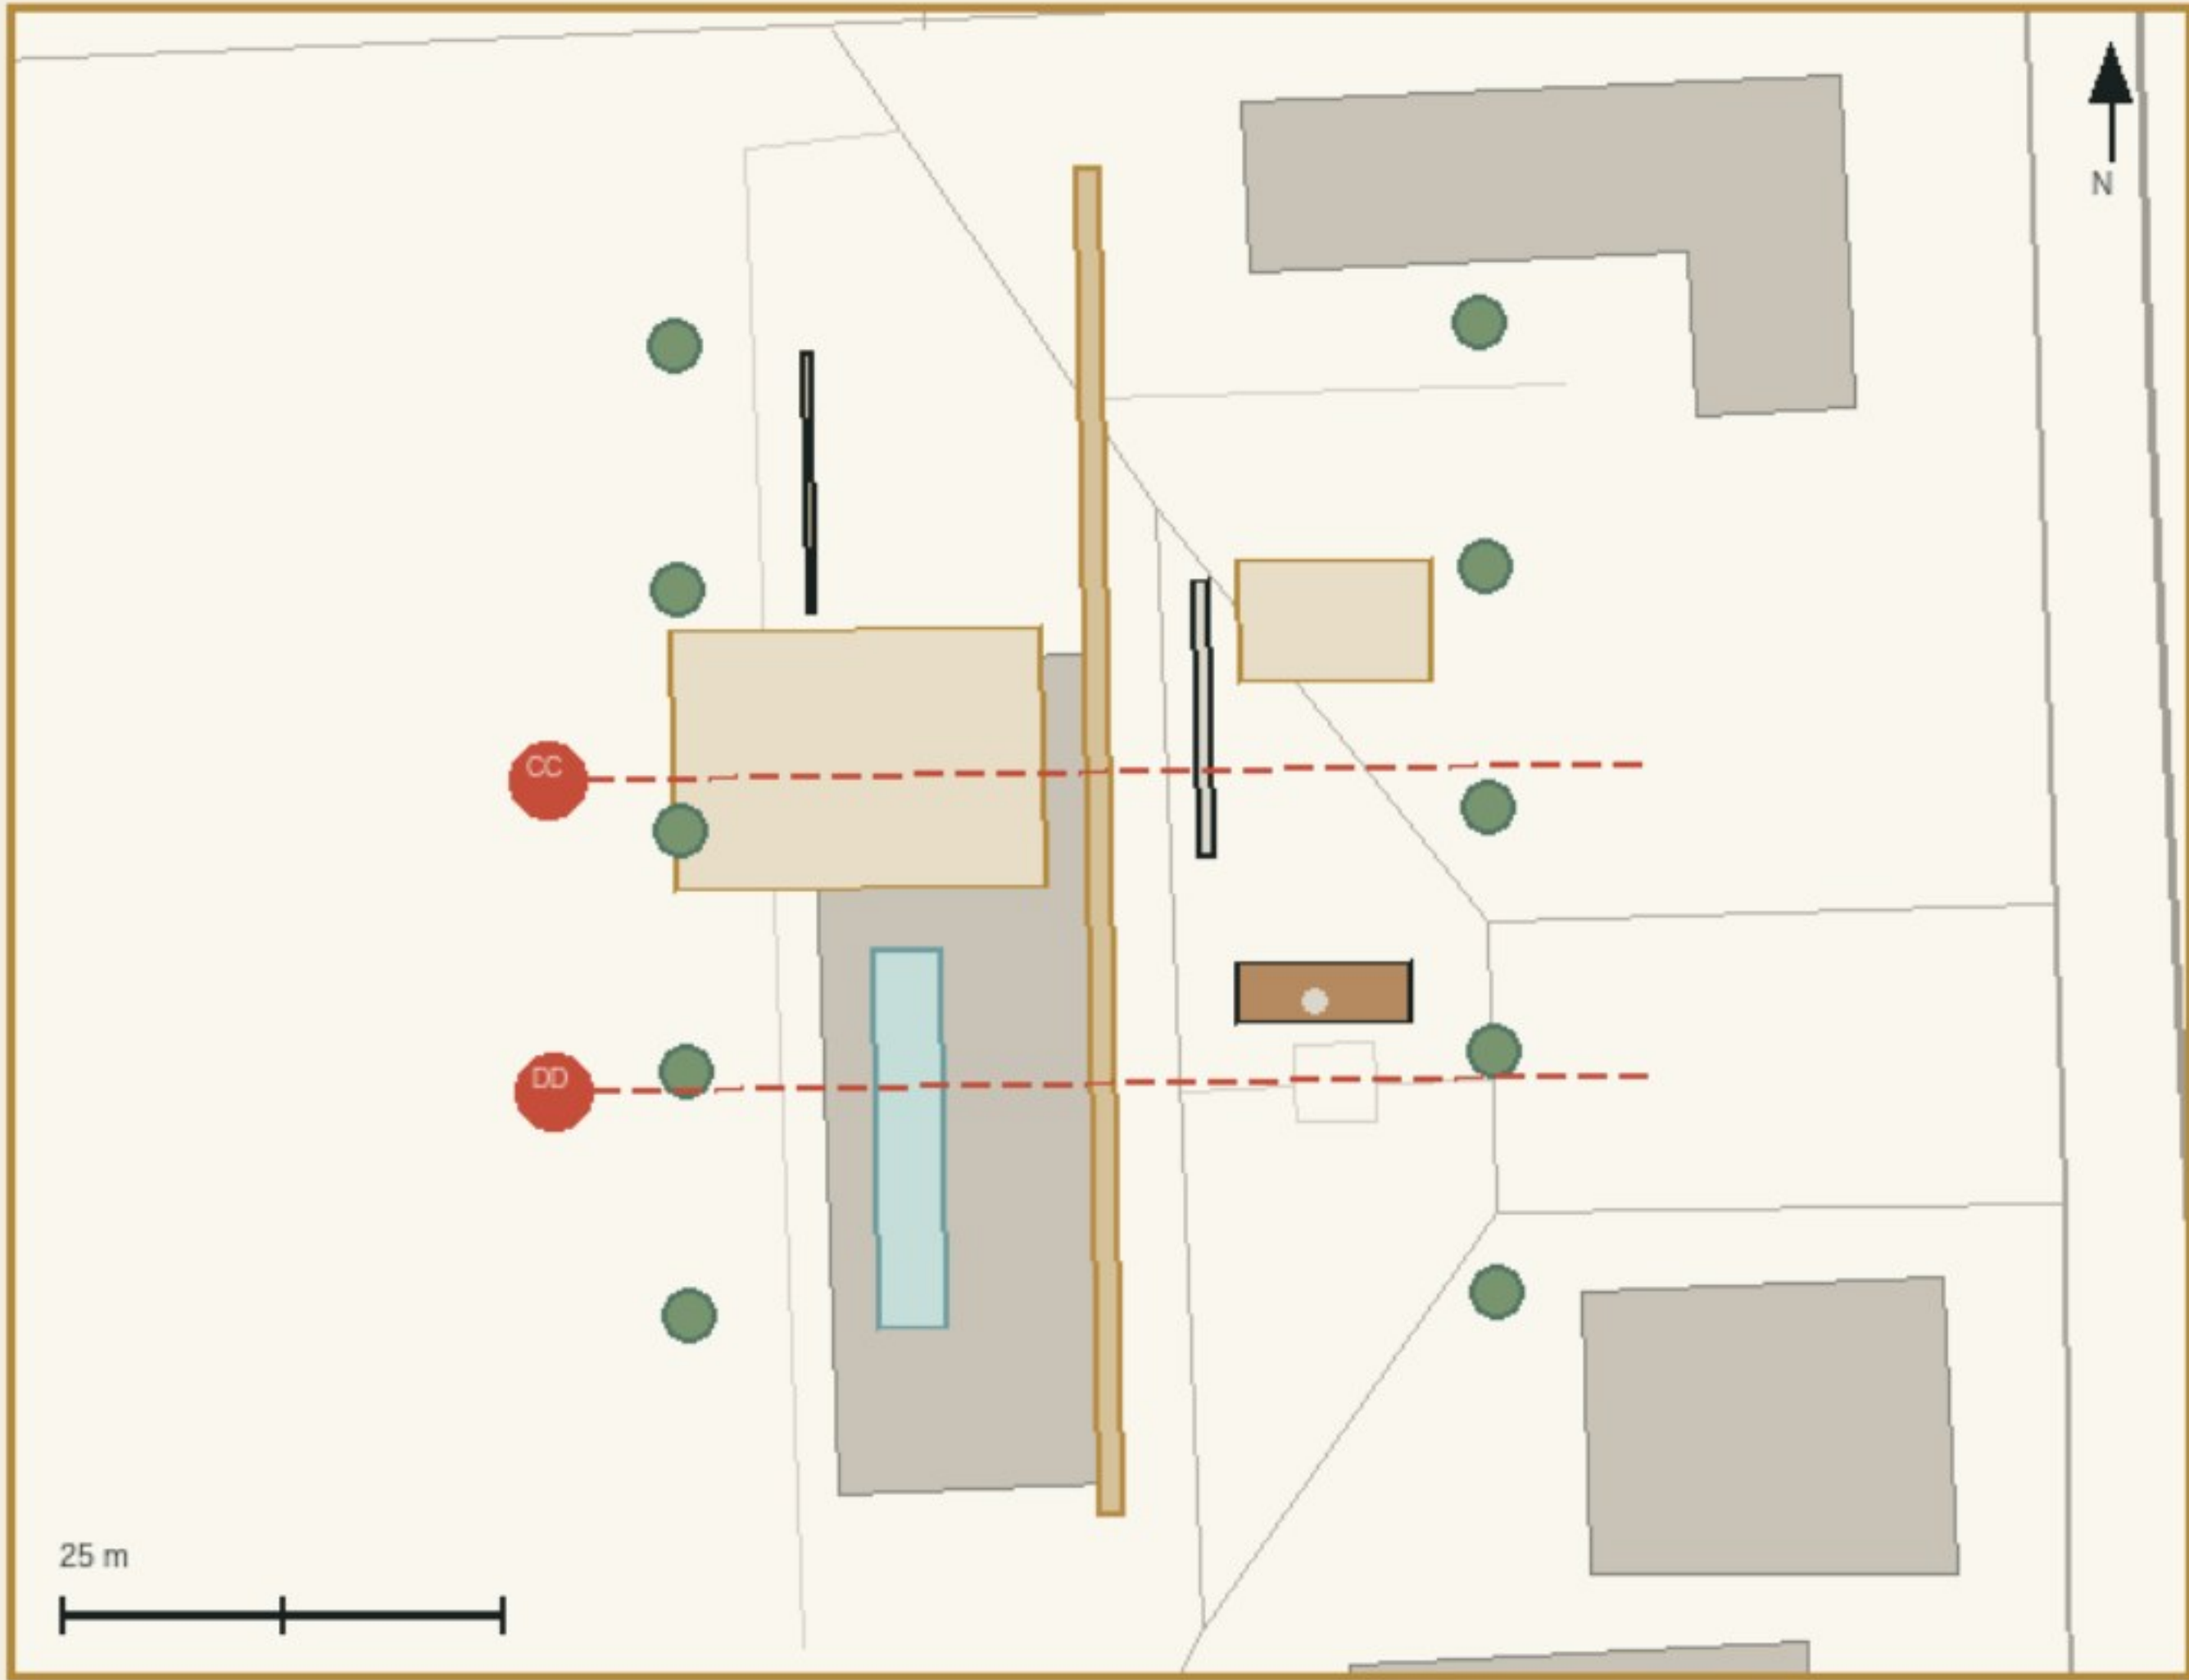

公共步行 铺装 雨庭 可撤构筑 试验边

03 大钟寺交换院

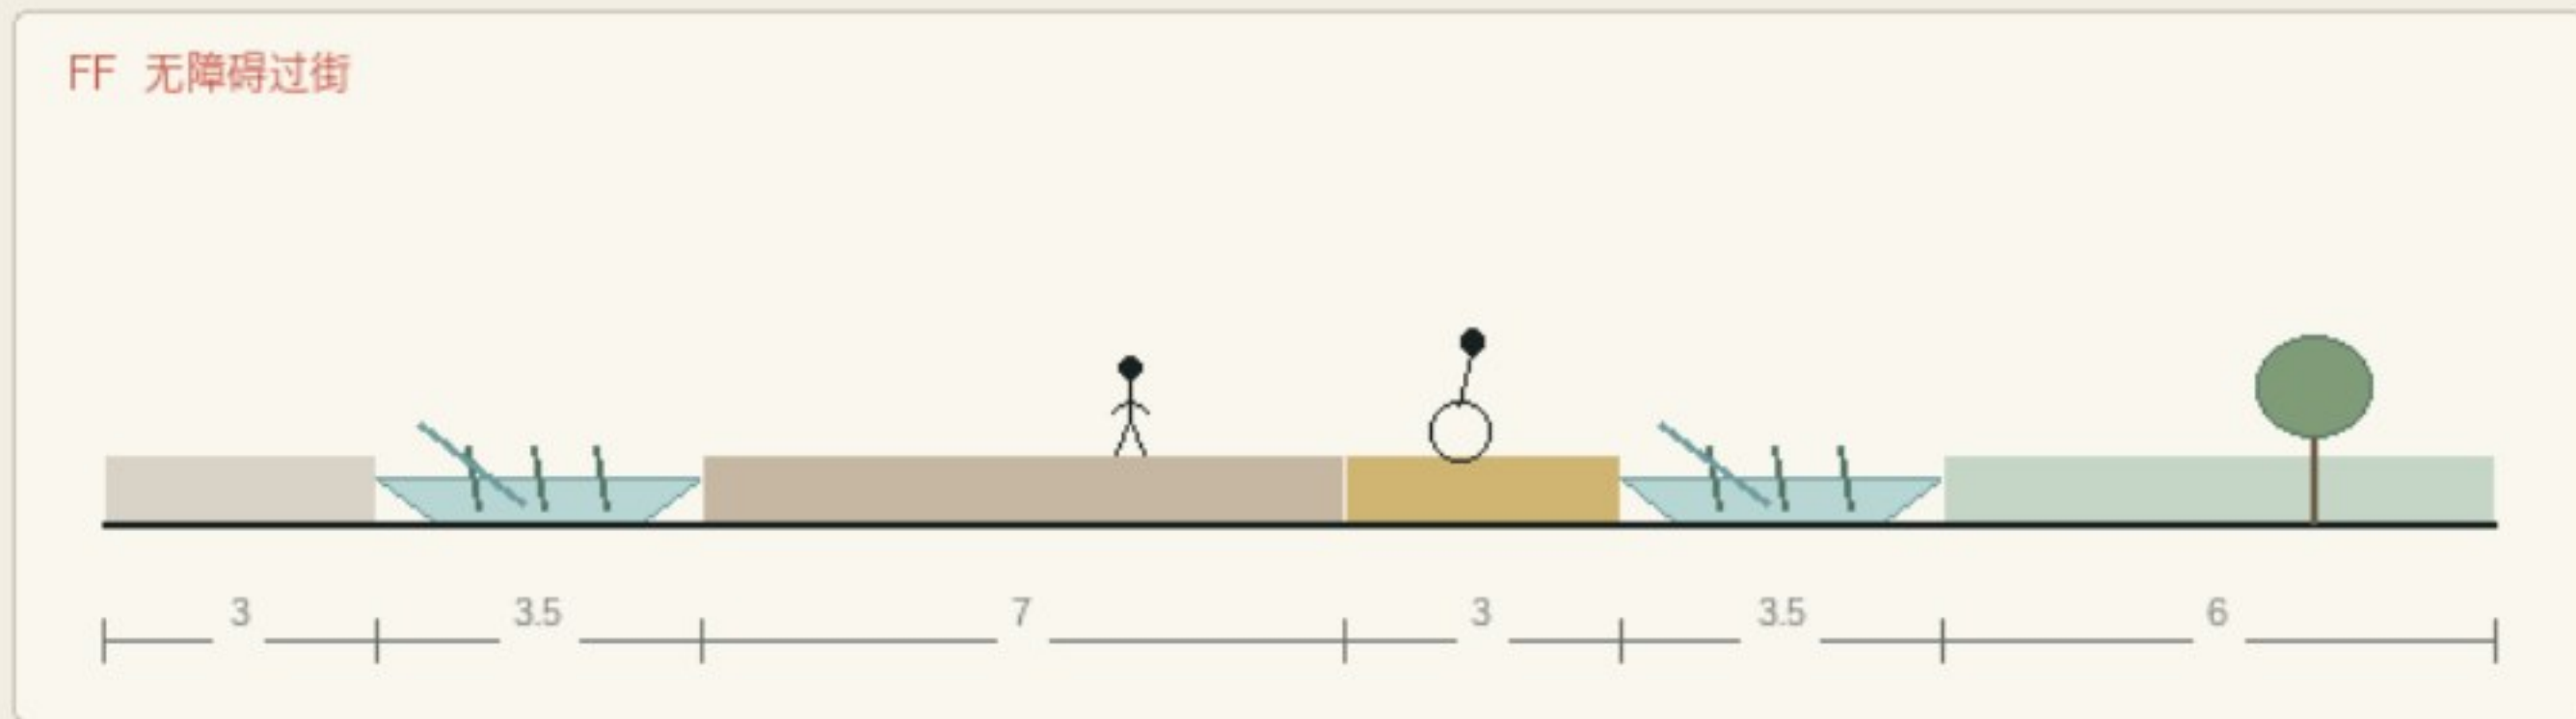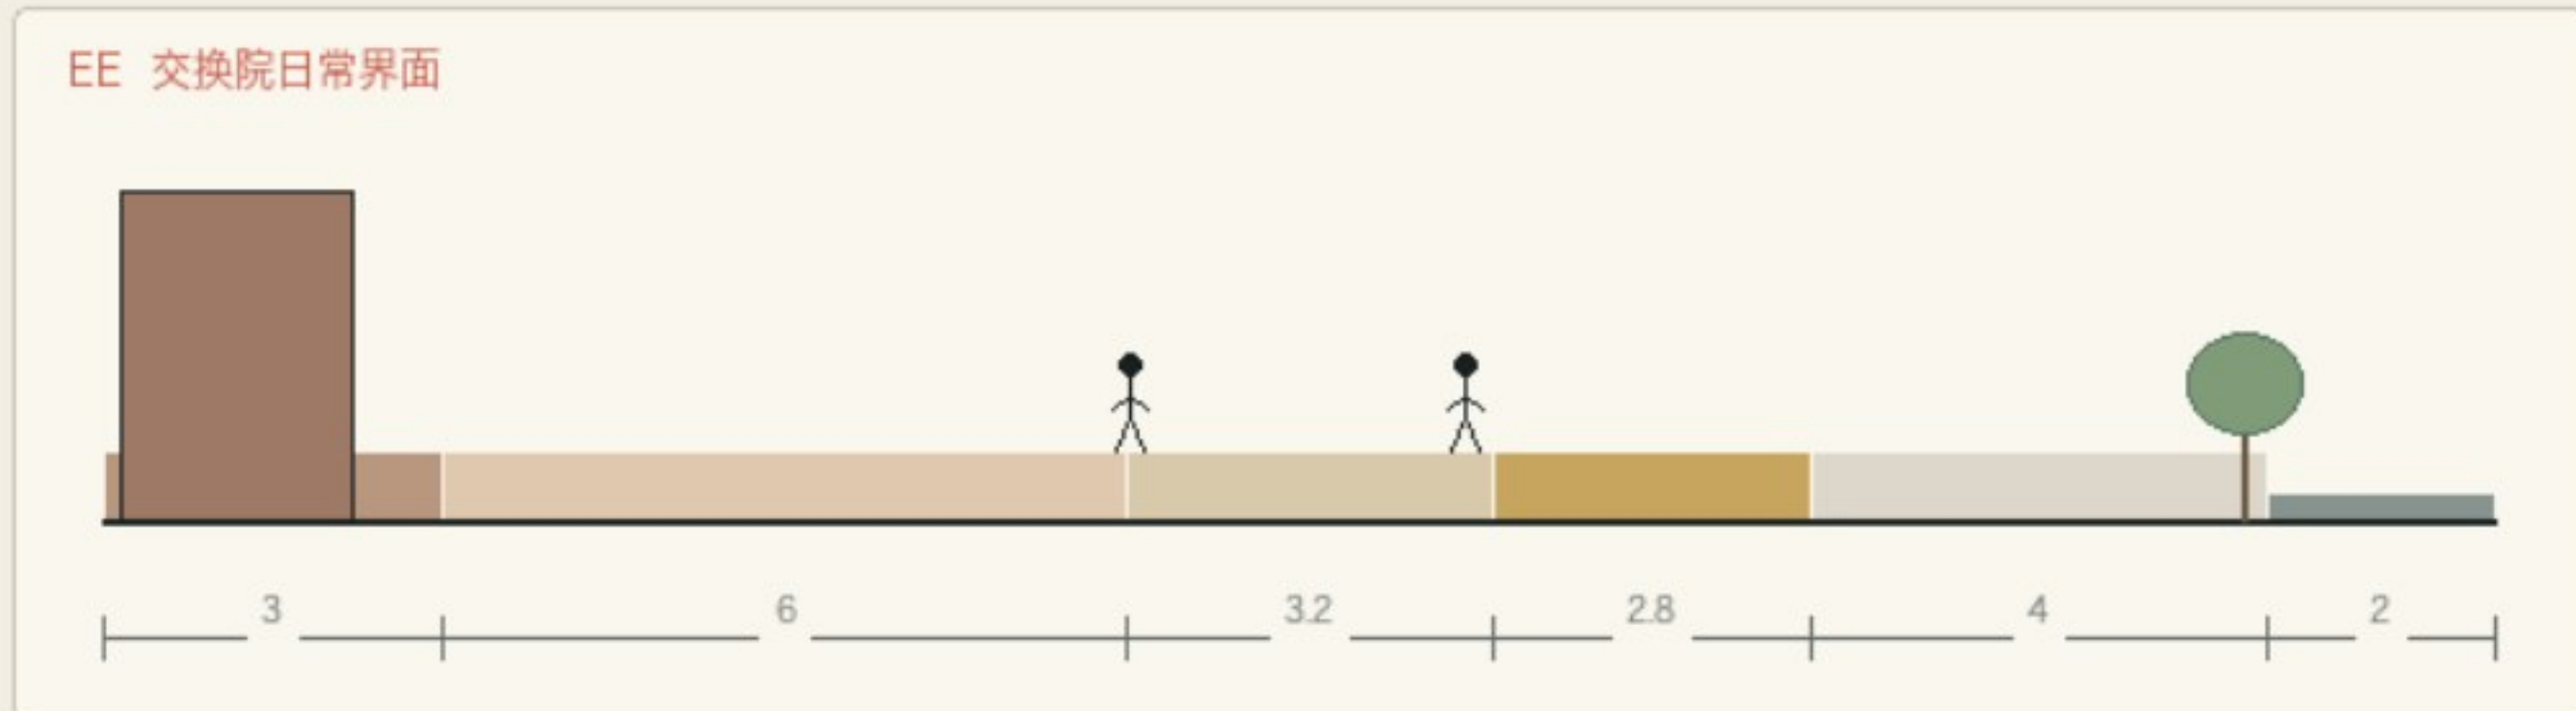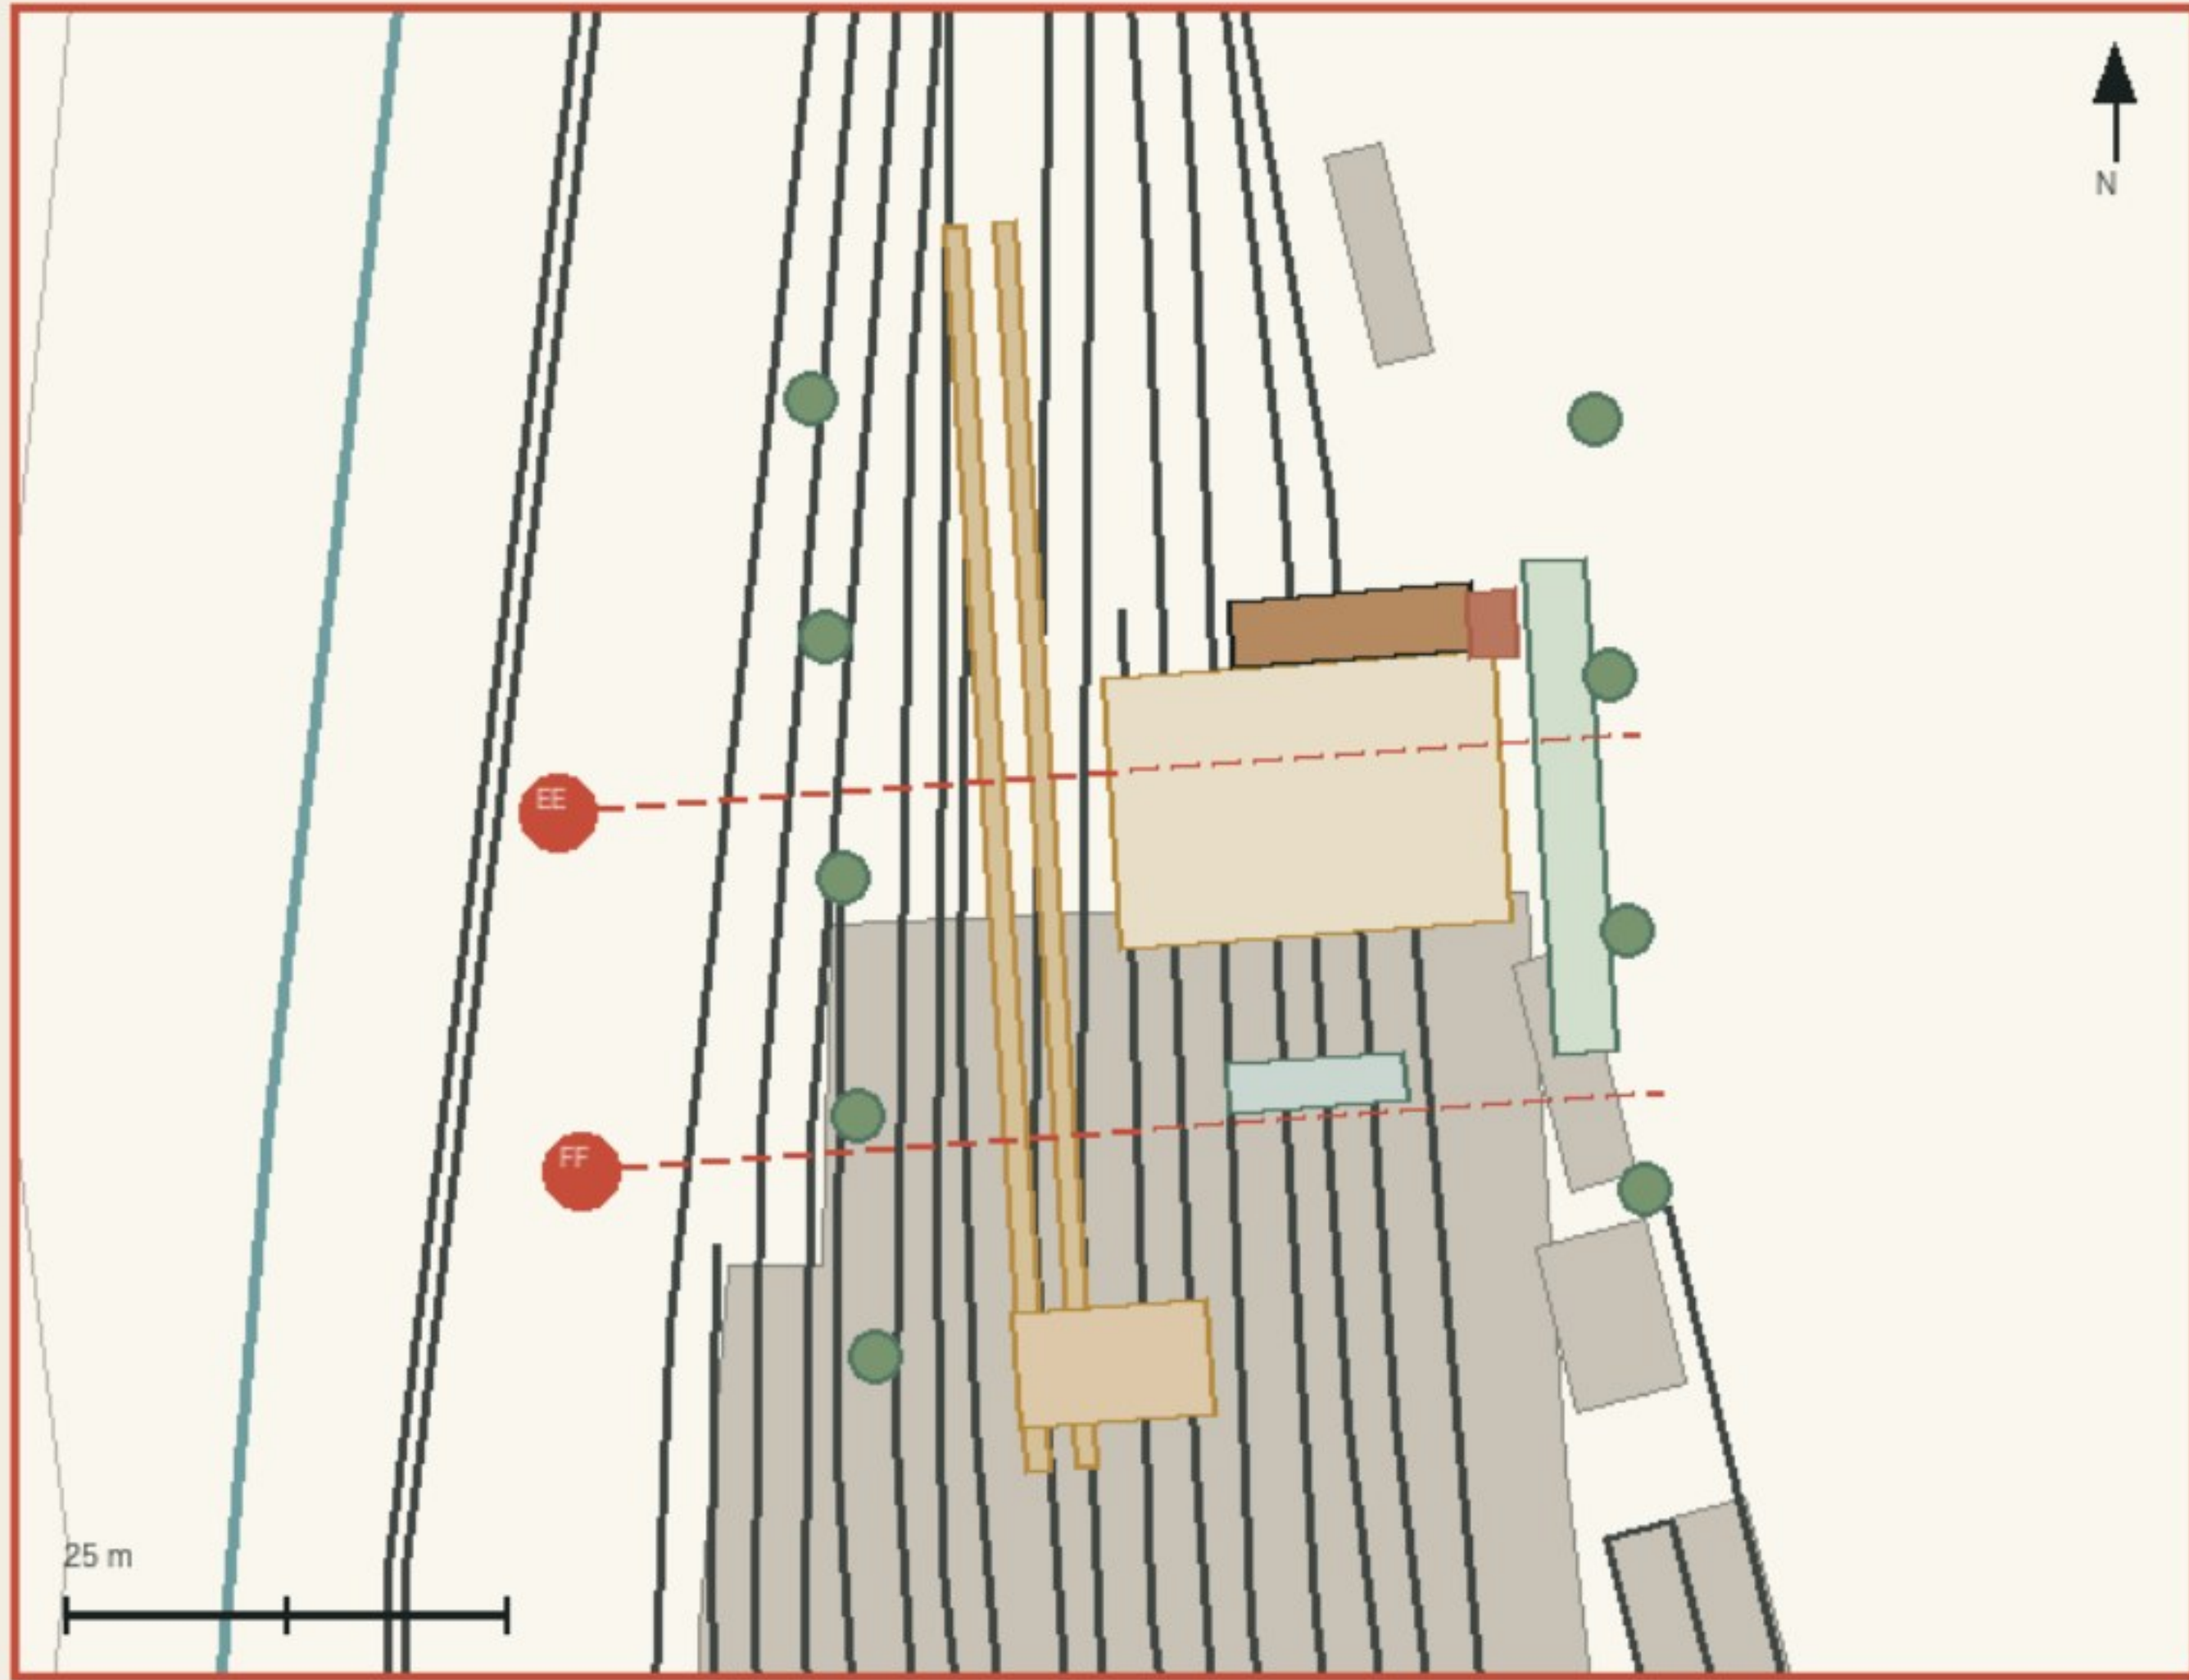

公共步行 铺装 雨庭 可撤构筑 试验边

概念方案 暂定边界 OSM 仅作参考语境

Working dimensions Concept design 1:200 section logic




08 可拆、可修、可替换

八个构件：原型、材料层、连接节点与维护路径

JINGZHANG OPEN BELT

FIELD KIT / 08

C01 树荫棚

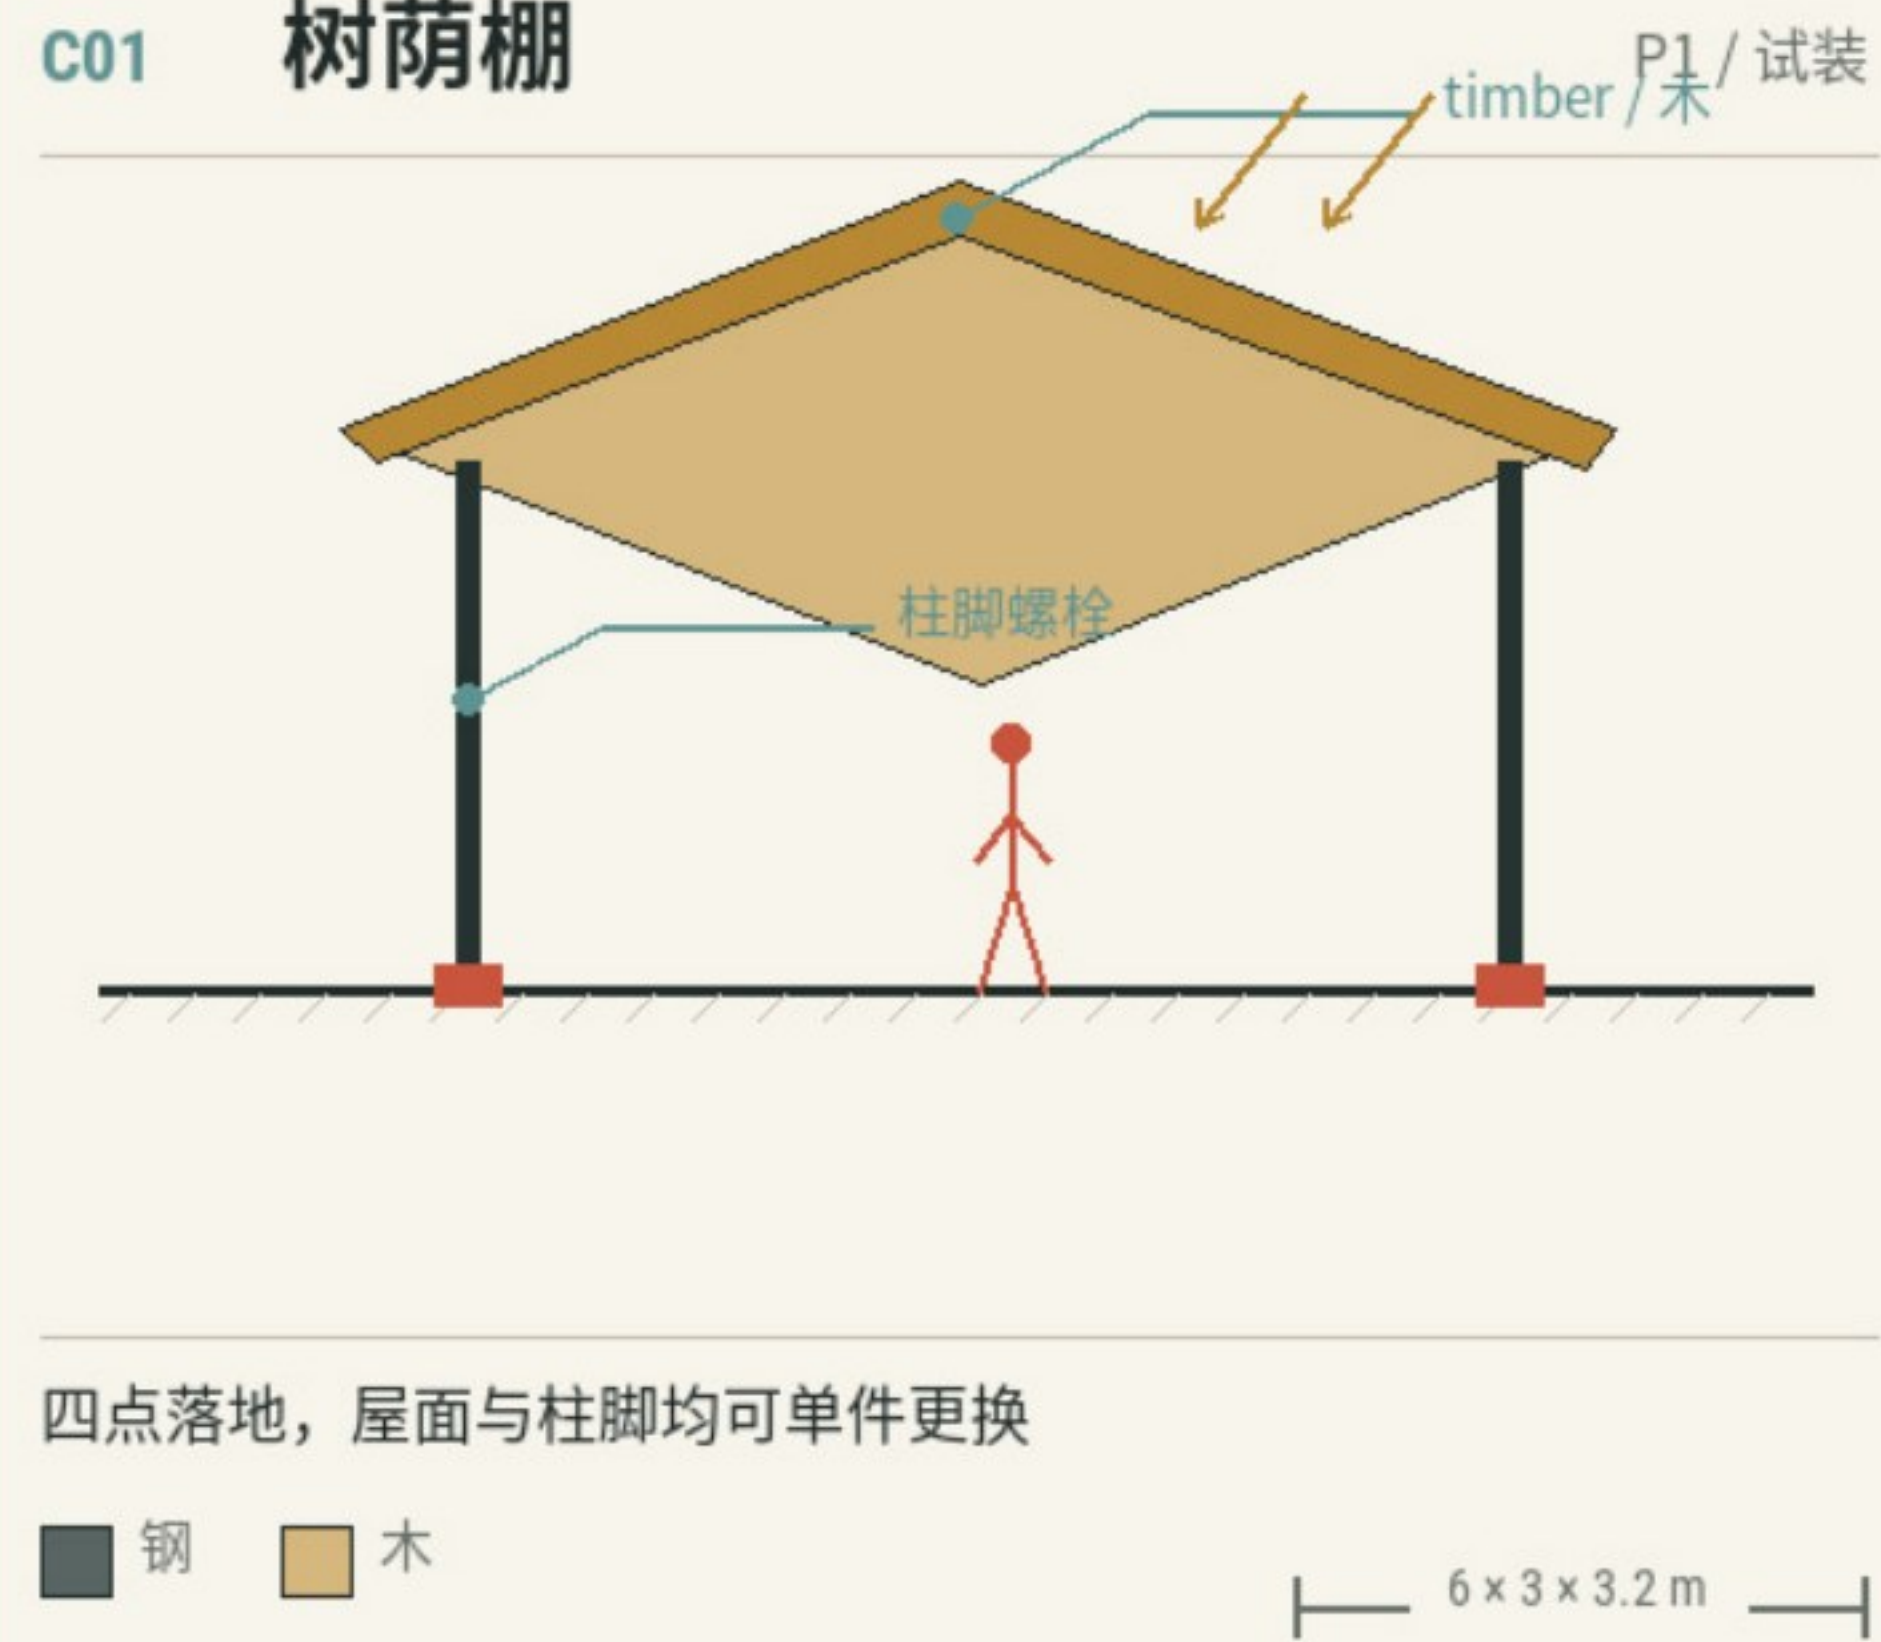


四点落地，屋面与柱脚均可单件更换

■ 钢 ■ 木

6 x 3 x 3.2 m

C02 三种高度长凳

P1 / 试装

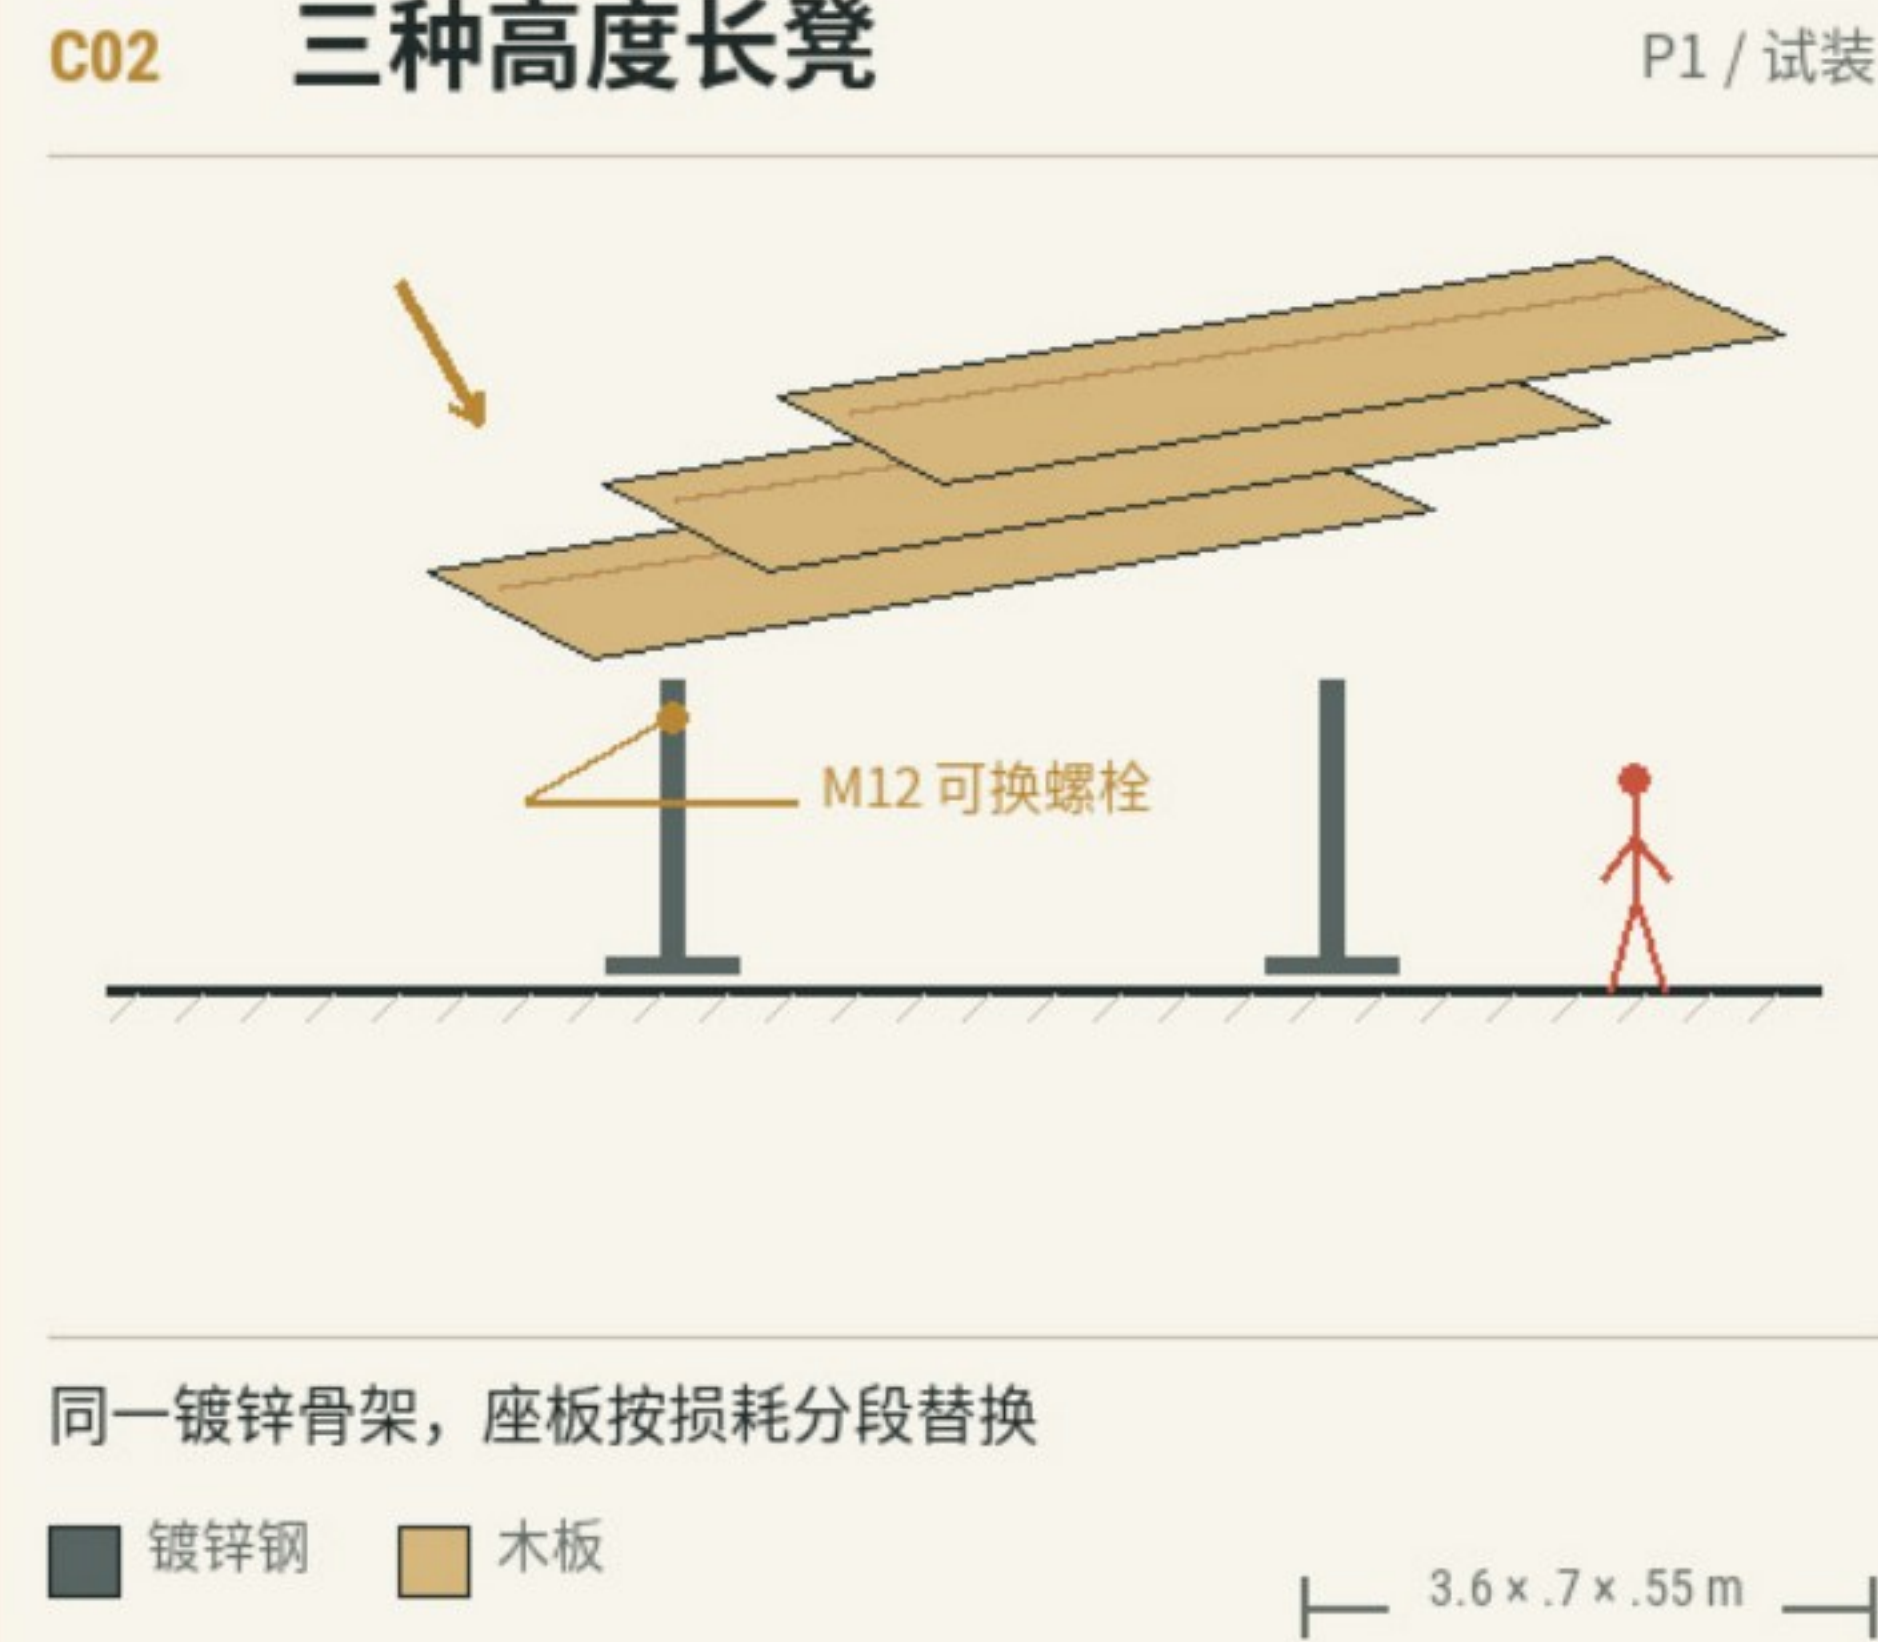


同一镀锌骨架，座板按损耗分段替换

■ 镀锌钢 ■ 木板

3.6 x .7 x .55 m

C03 雨庭边

P1 / 雨季

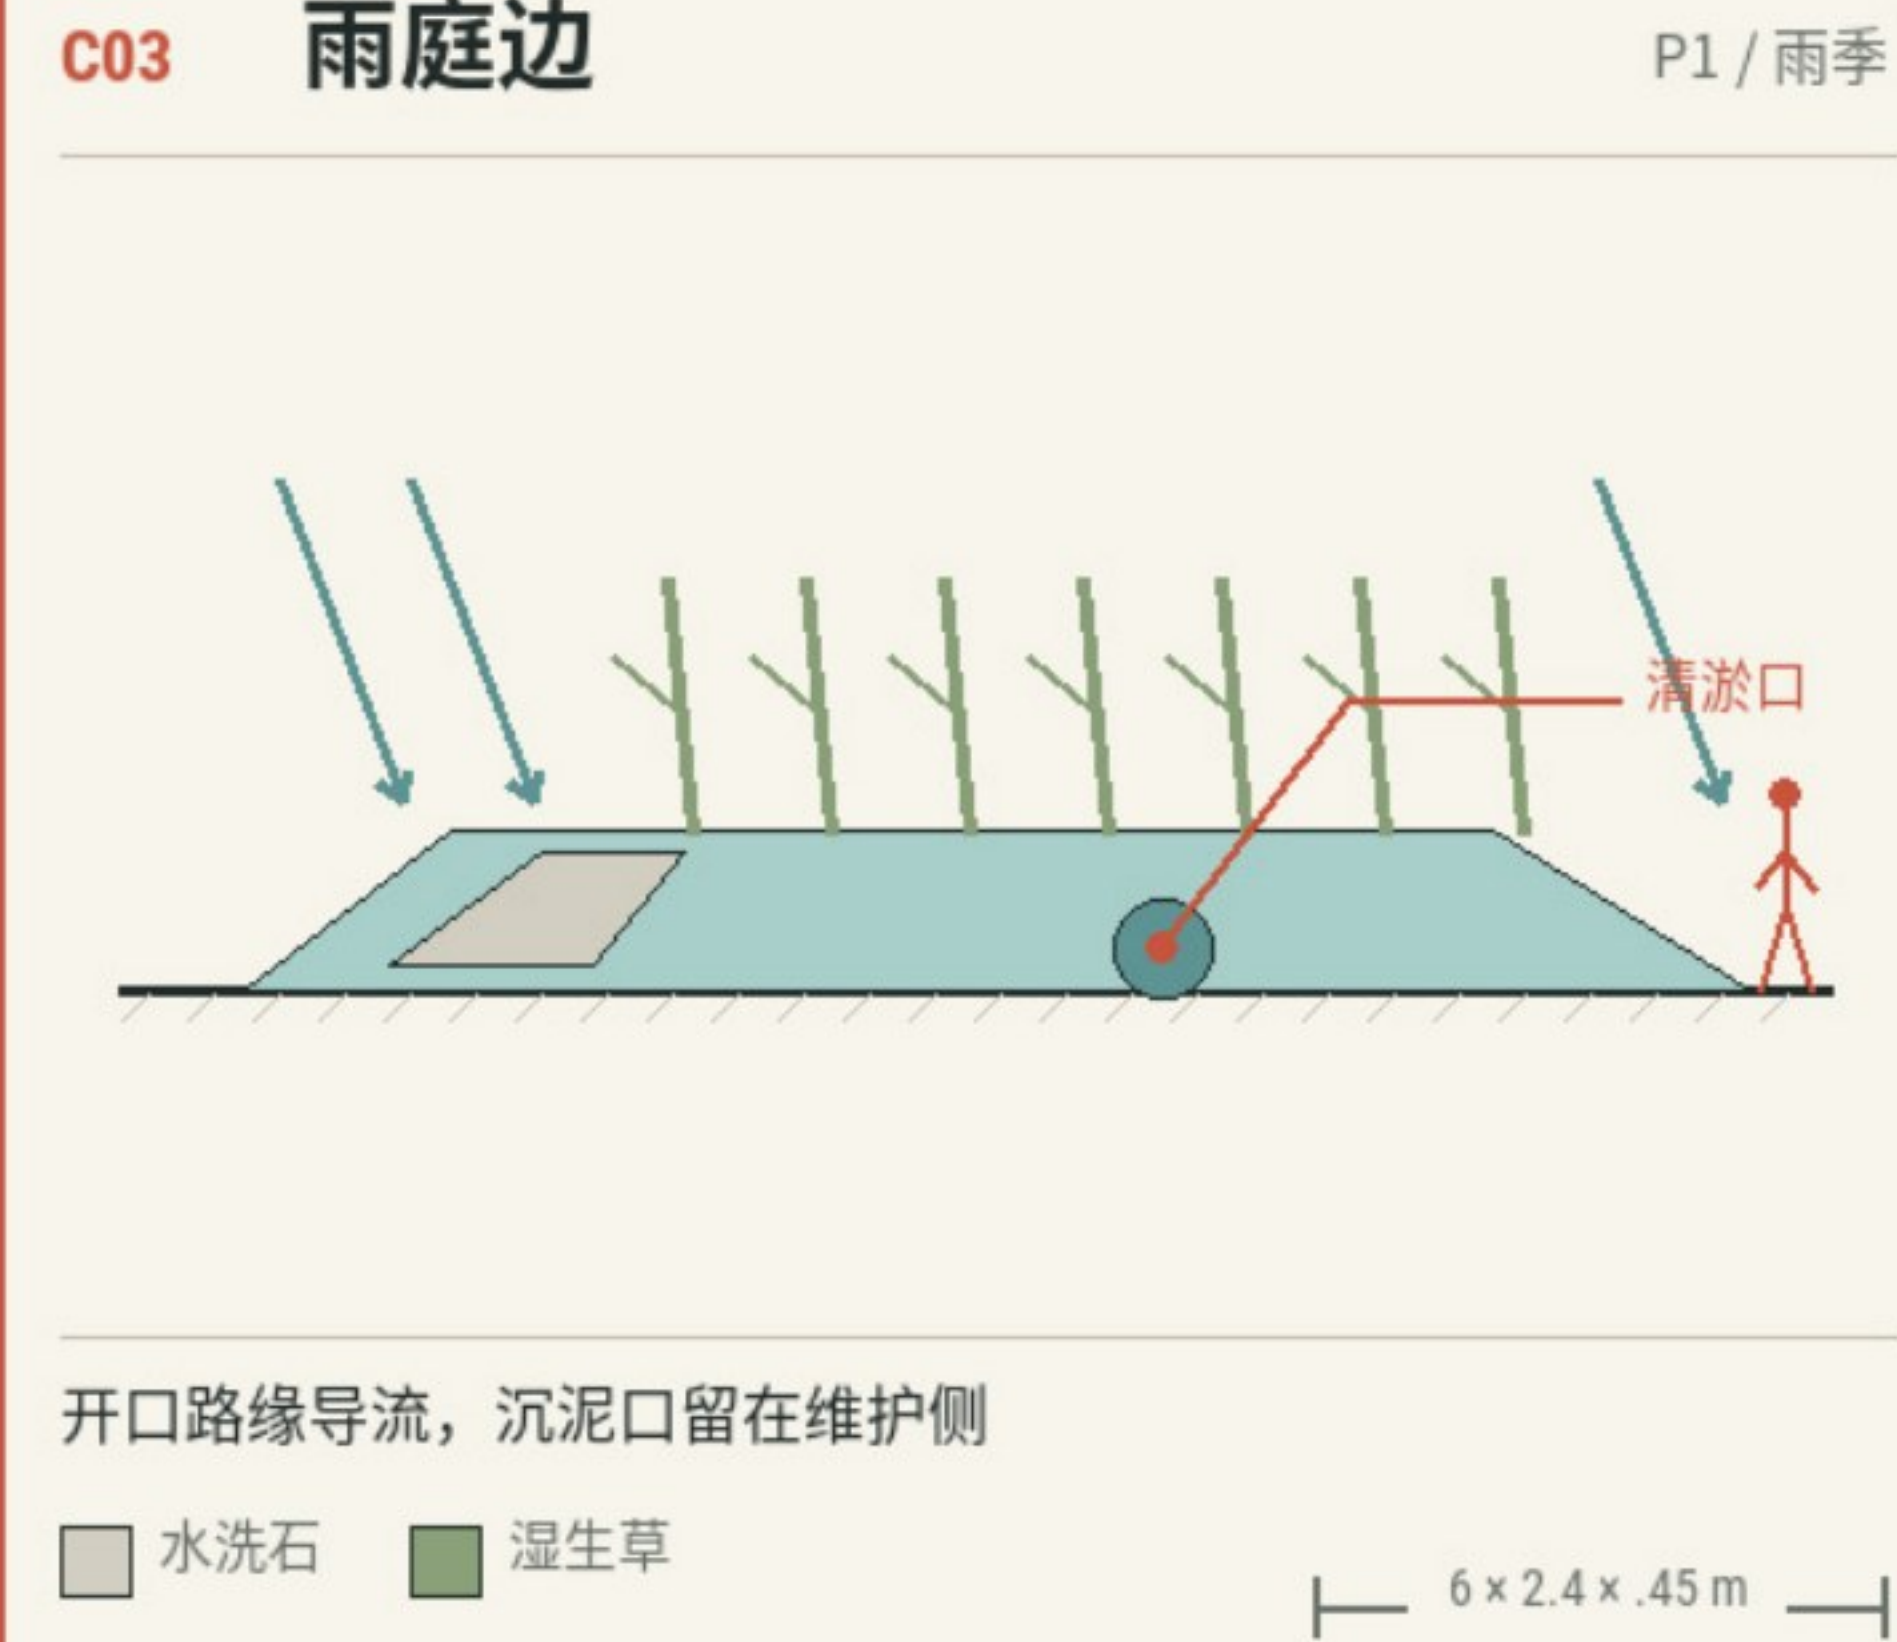

开口路缘导流，沉泥口留在维护侧

■ 水洗石 ■ 湿生草

6 x 2.4 x .45 m

C04 遗产阅读架

P2 / 常设




旧钢轨作基座，非电子展板可随内容更新

■ 旧轨 ■ 夹板

2.4 x .45 x 1.15 m

C05 有人服务桌

P1 / 活动

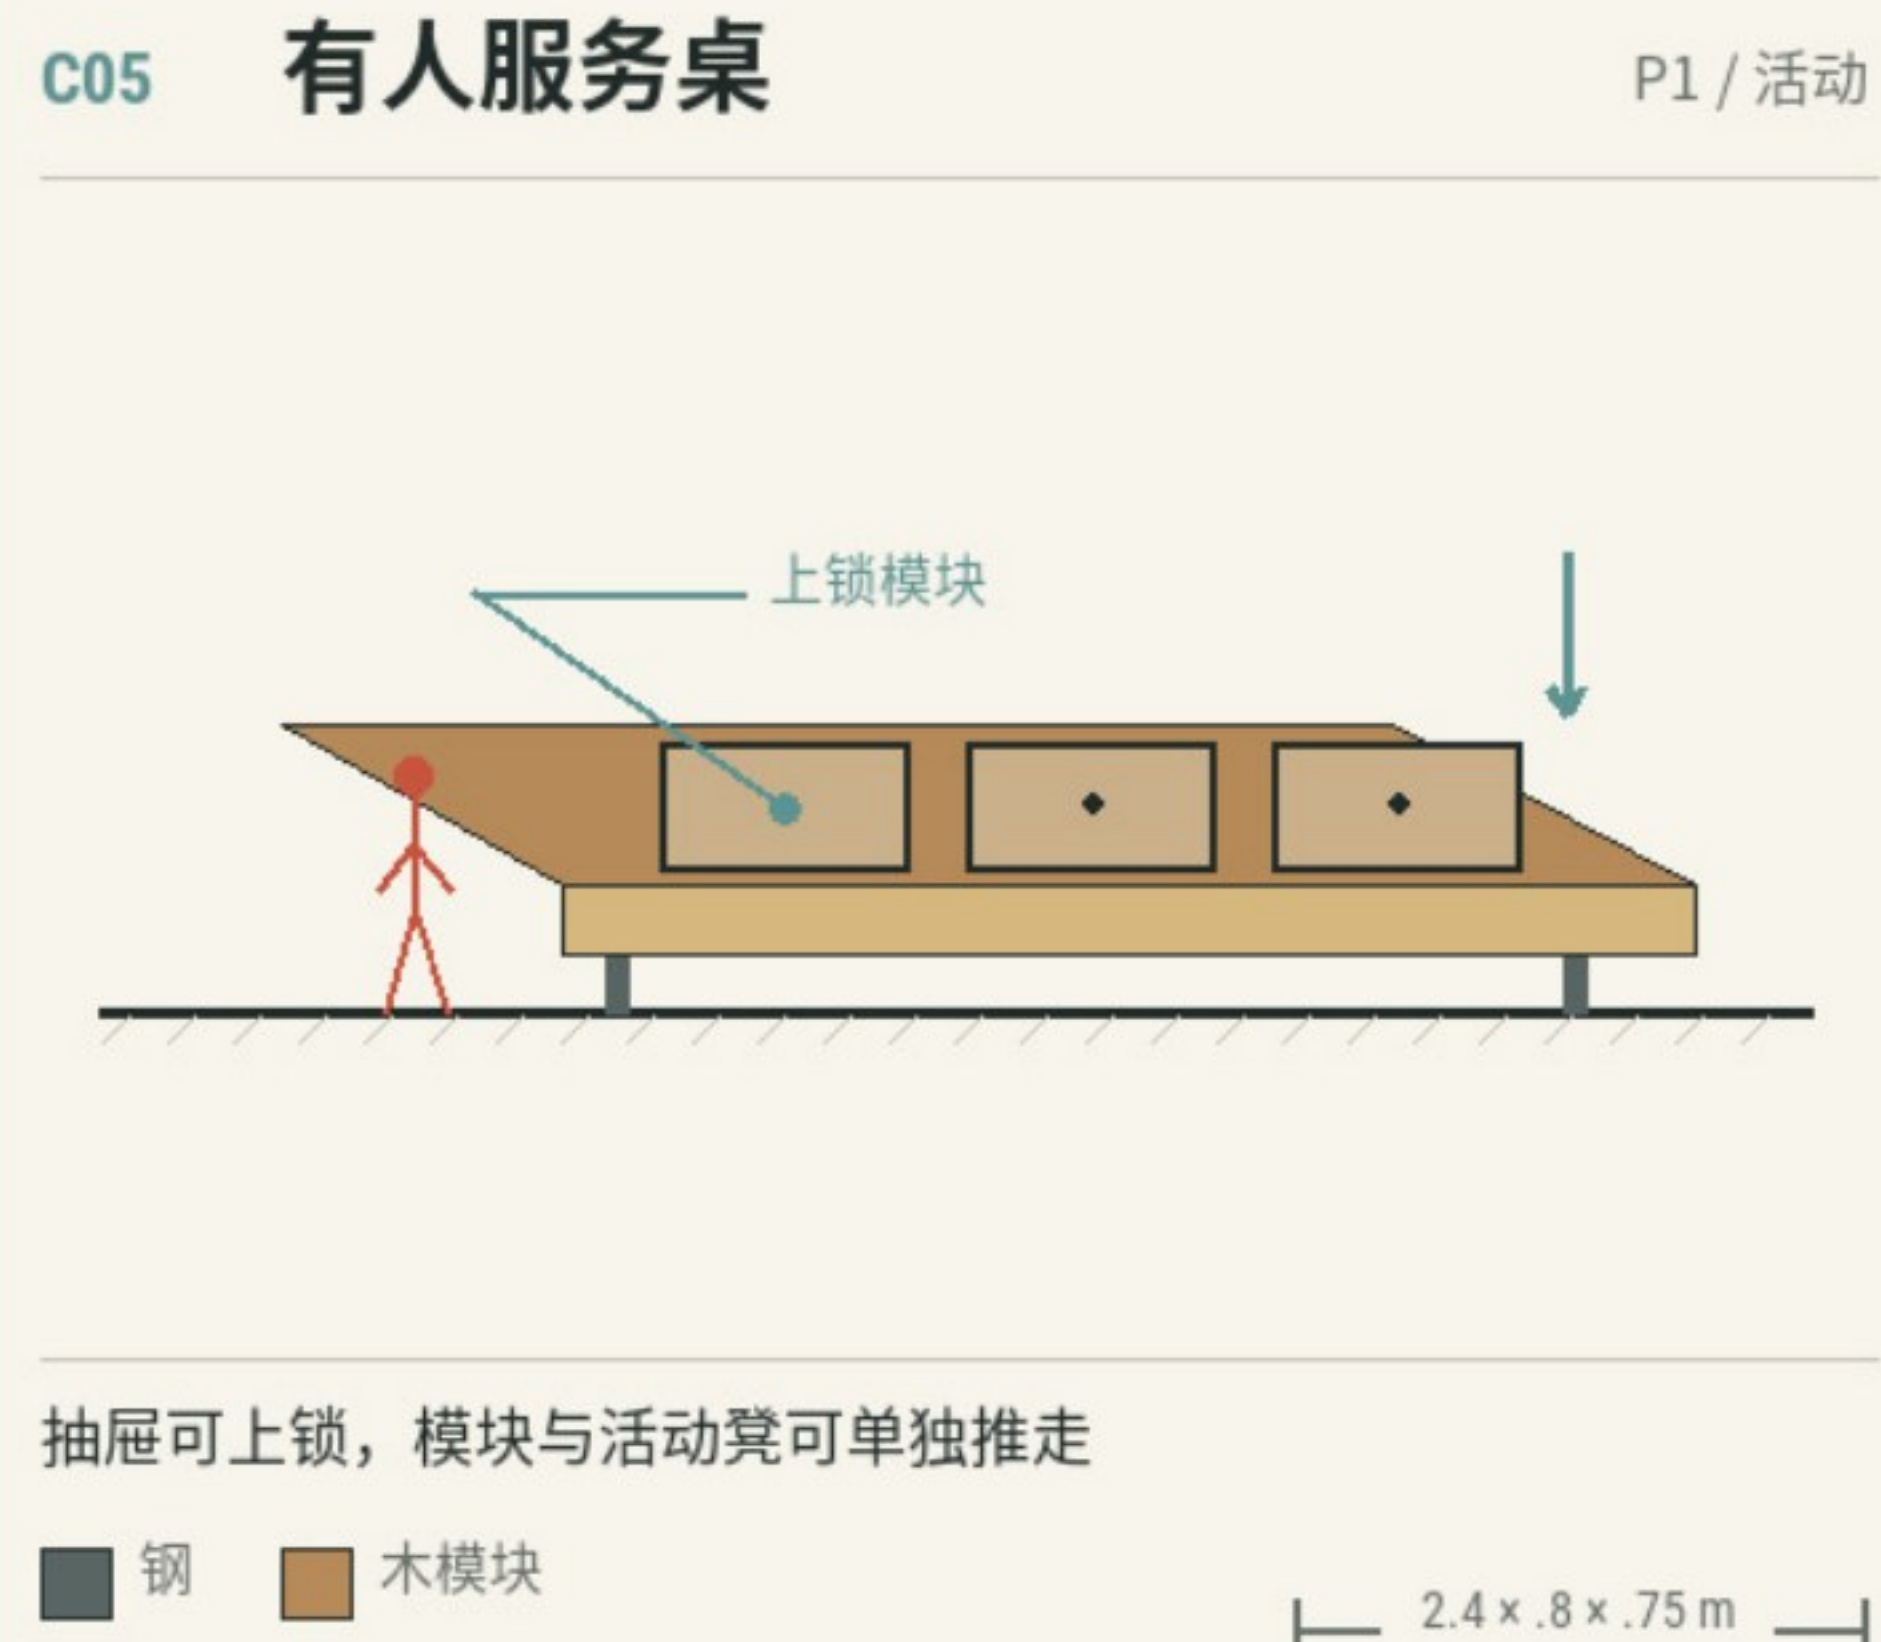


抽屉可上锁，模块与活动凳可单独推走

■ 钢 ■ 木模块

2.4 x .8 x .75 m

C06 可视试验边

P0 / 快装

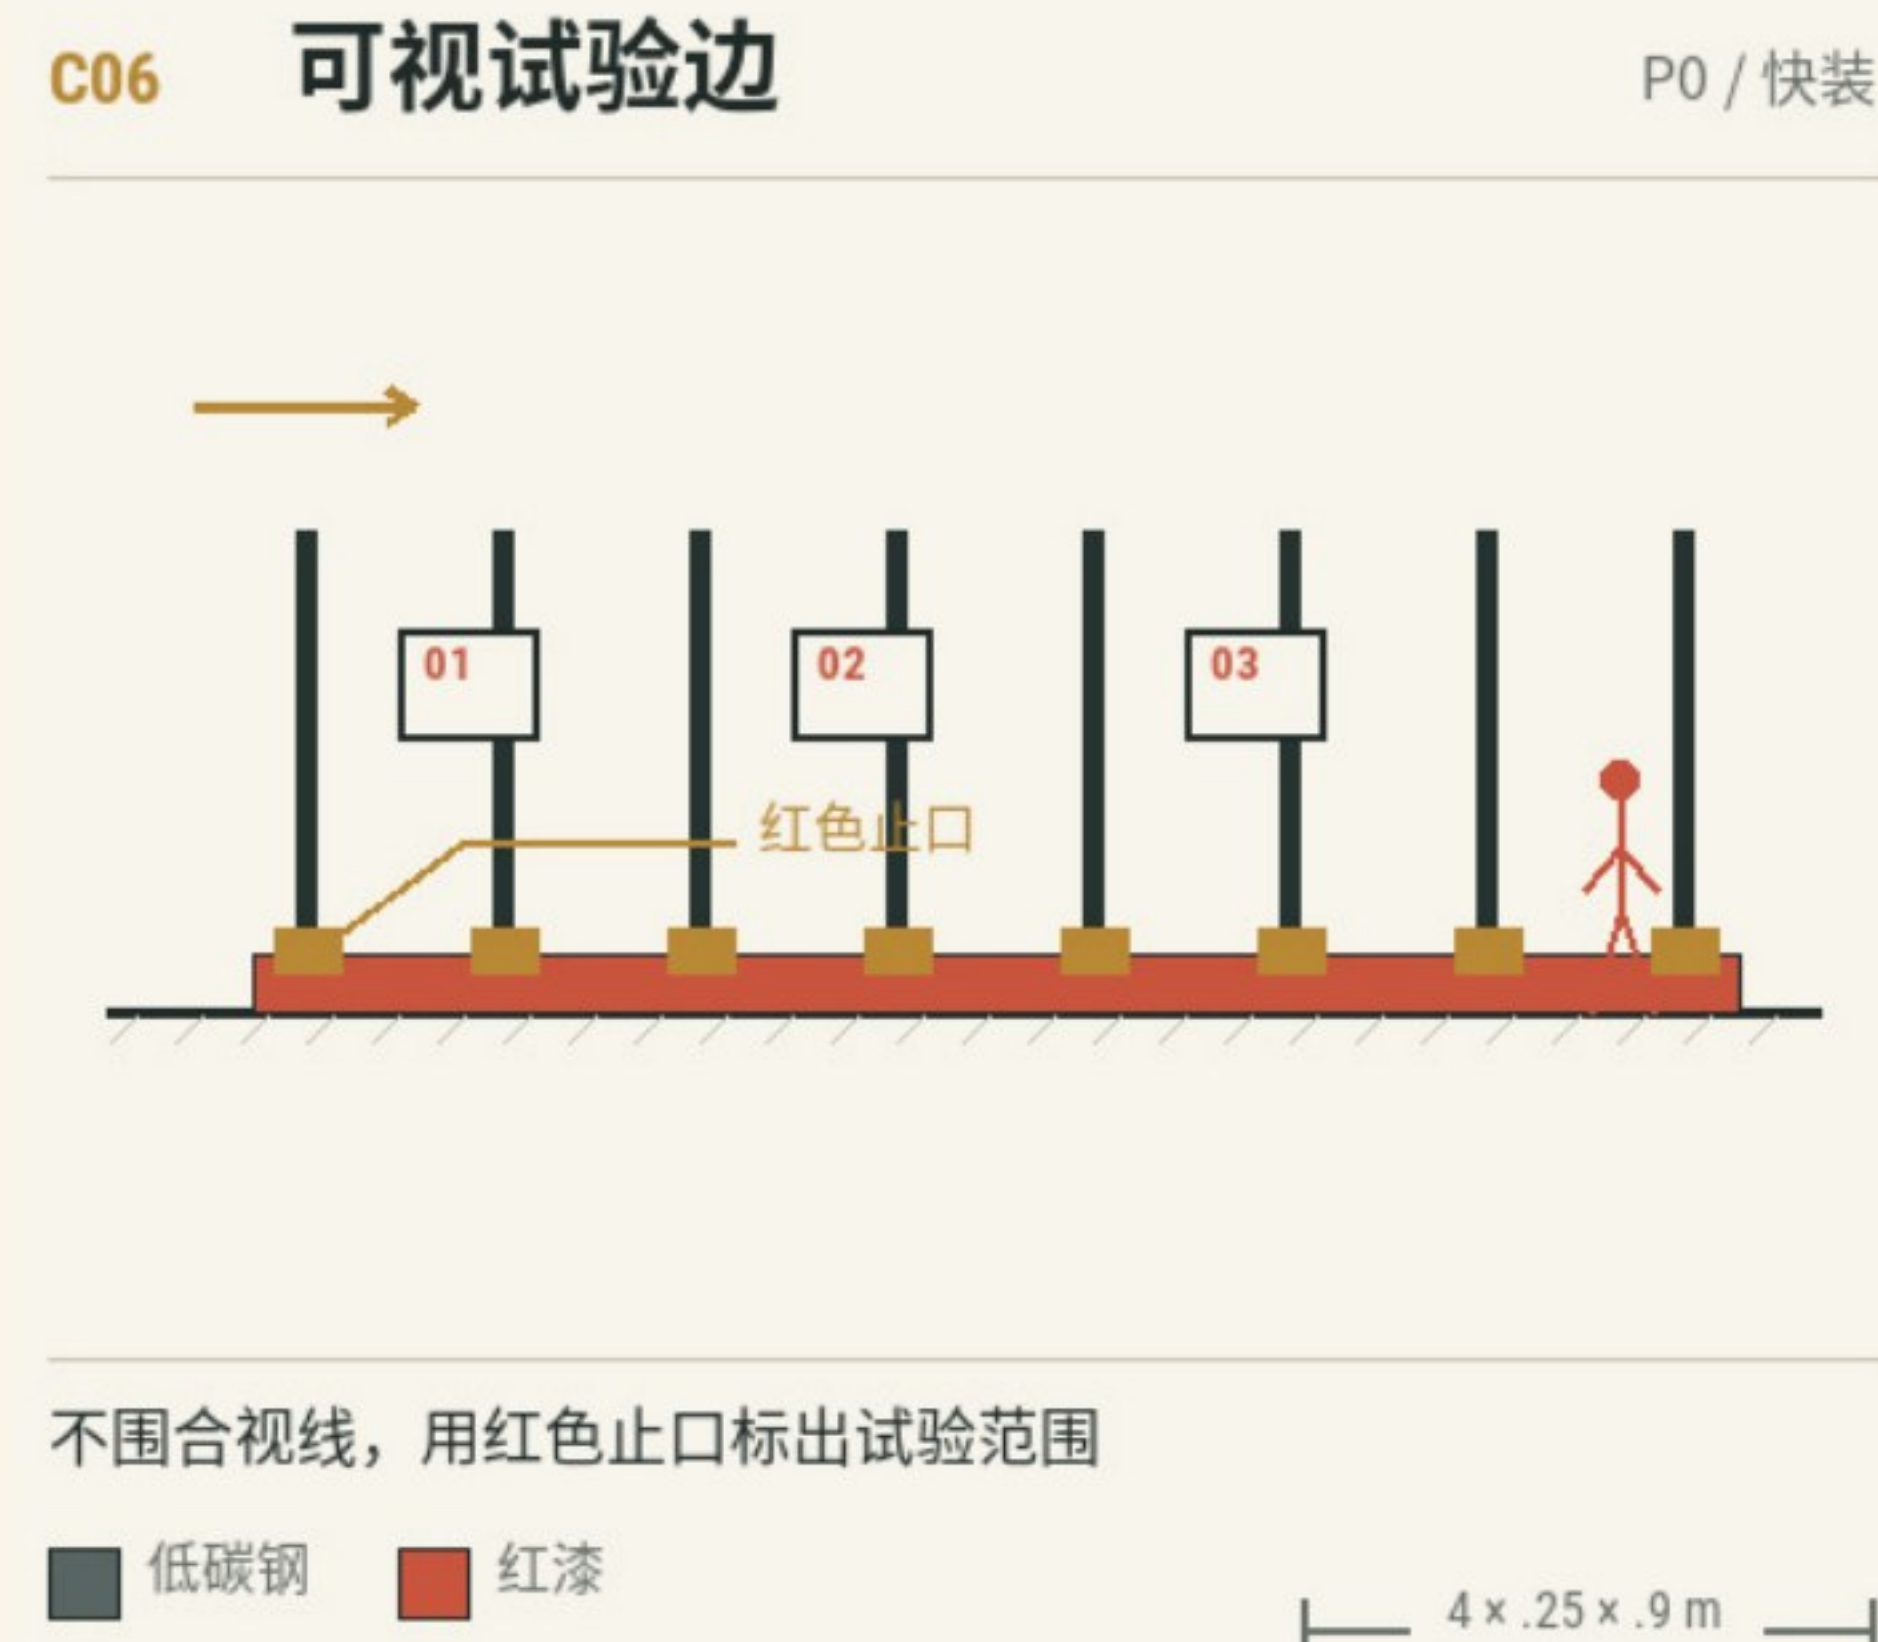

不围合视线，用红色止口标出试验范围

■ 低碳钢 ■ 红漆

4 x .25 x .9 m

C07 人工呼叫柱

P1 / 服务



触觉标记、低压按钮，接入有人值守点

■ 钢壳 ■ 触点

.35 x .35 x 1.35 m

C08 遮光夜灯

P1 / 夜间










暖光只照步行面，灯头可换并设分时回路

■ 钢杆 ■ 暖光

.35 x .35 x 3.6 m

慢行、蓝绿与六条剖面


先把公共路线和过街接上，再布置试验与服务

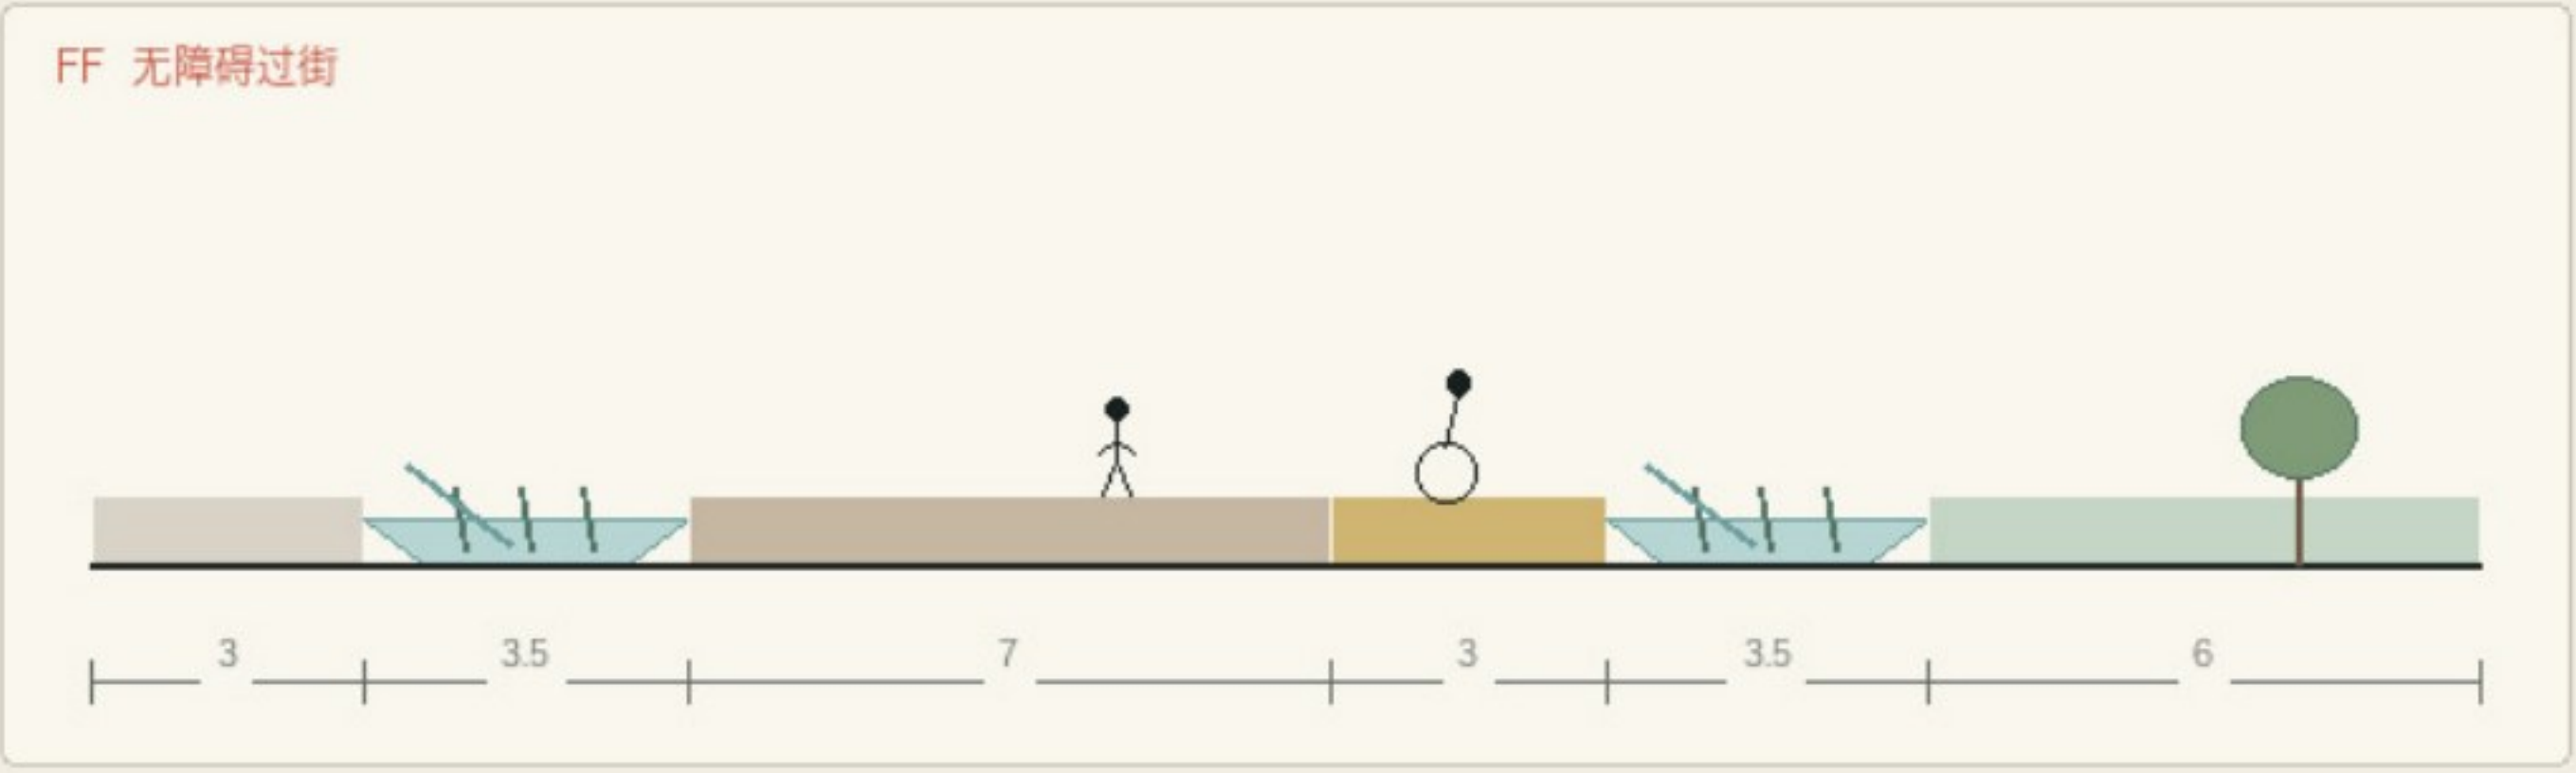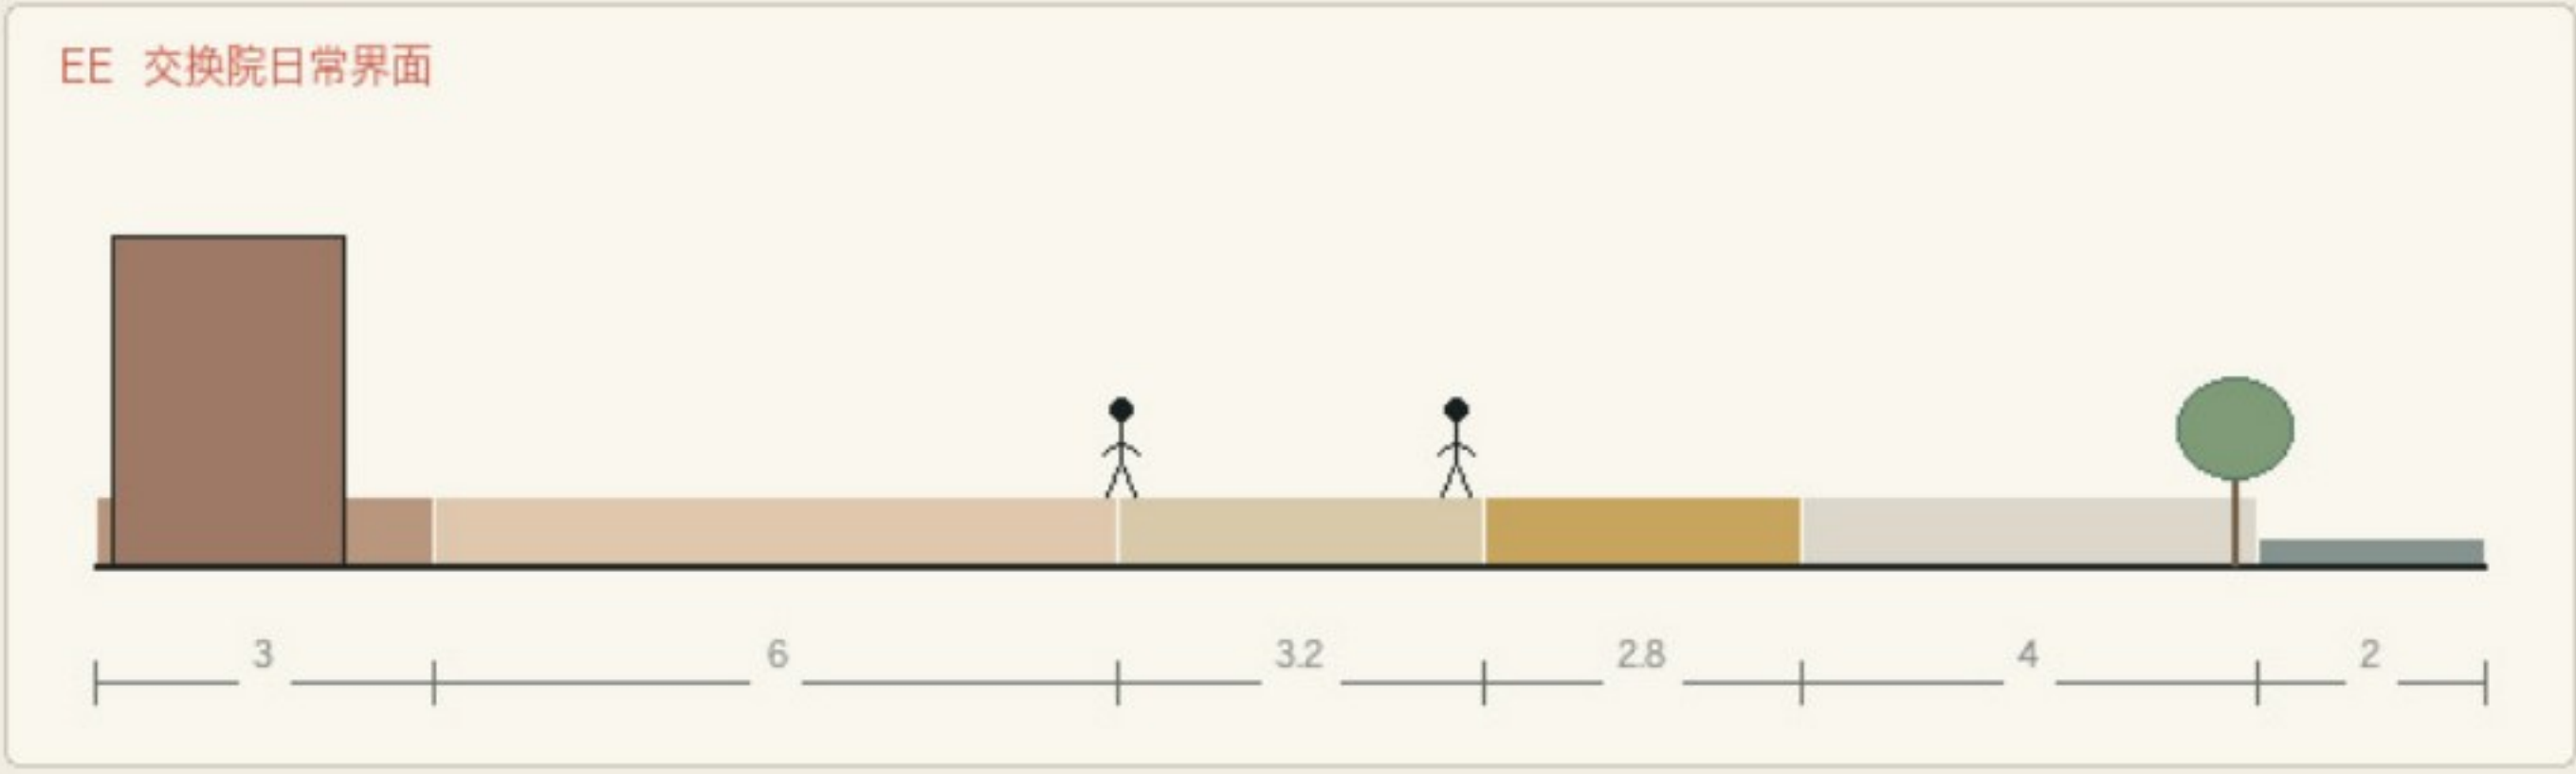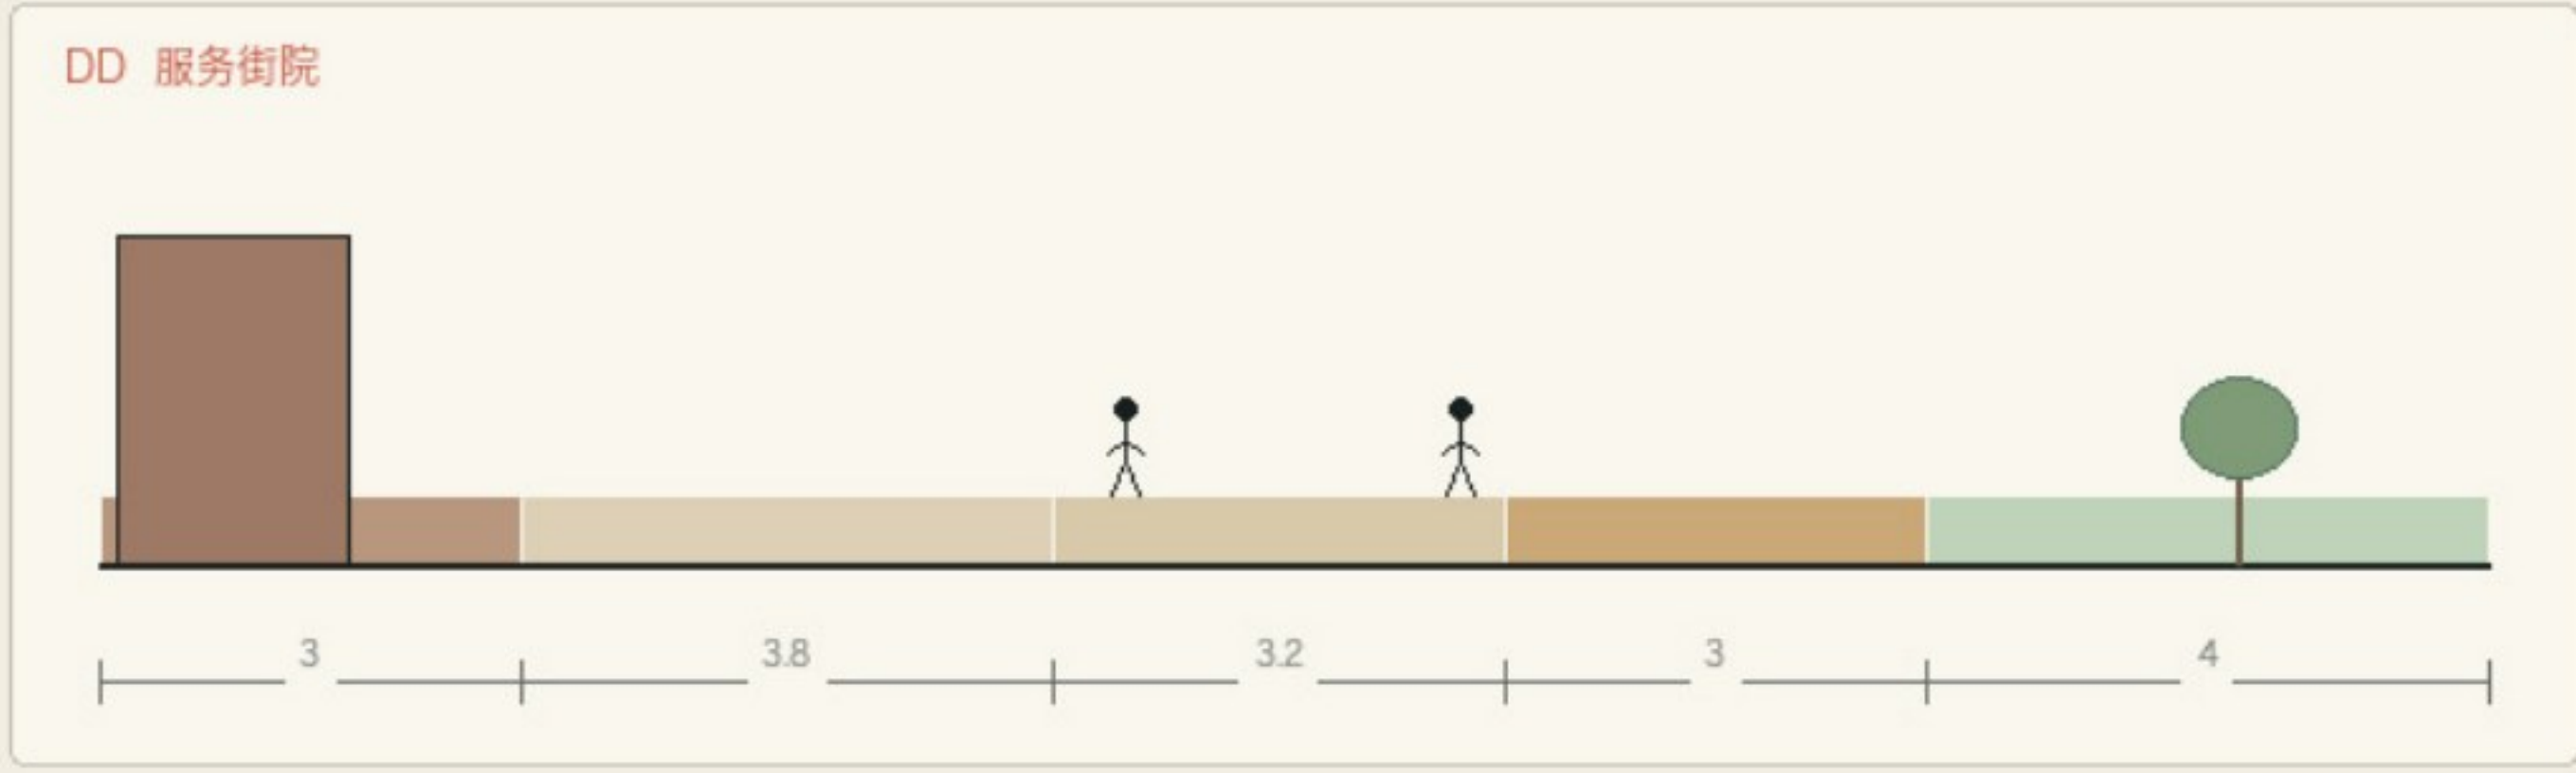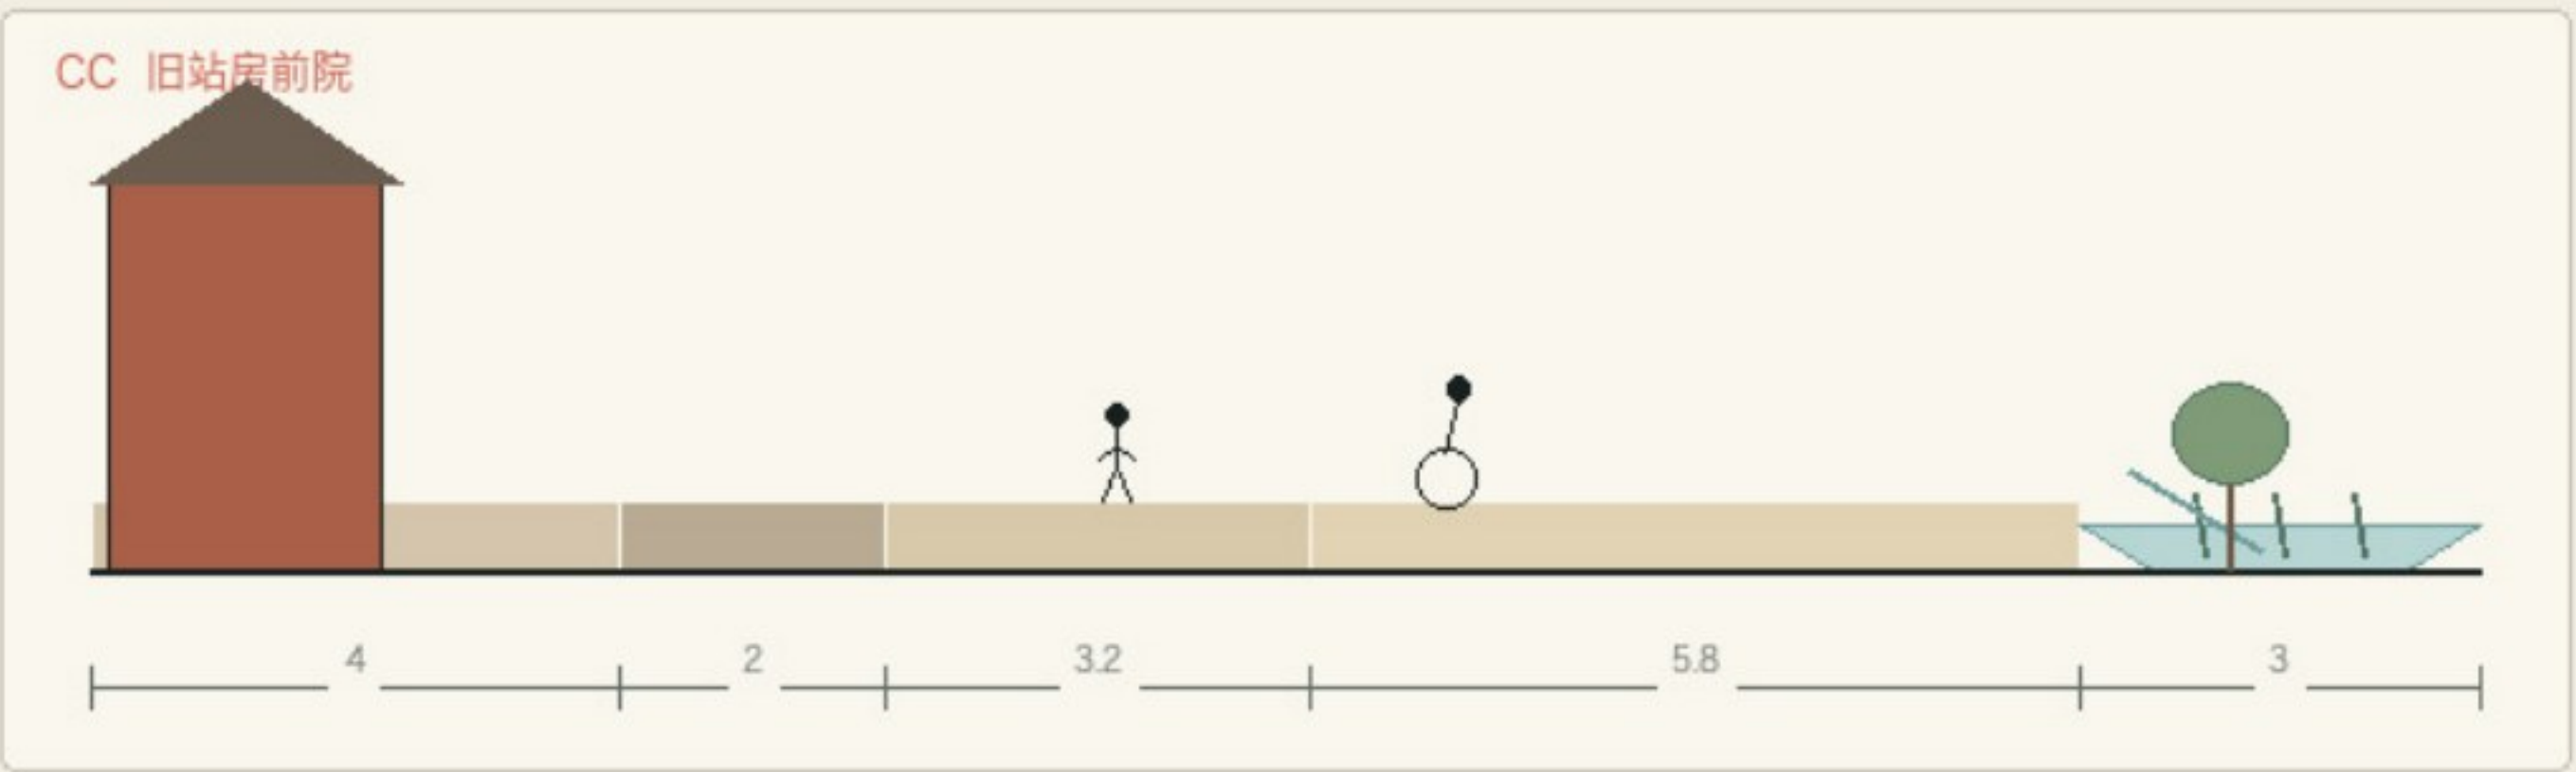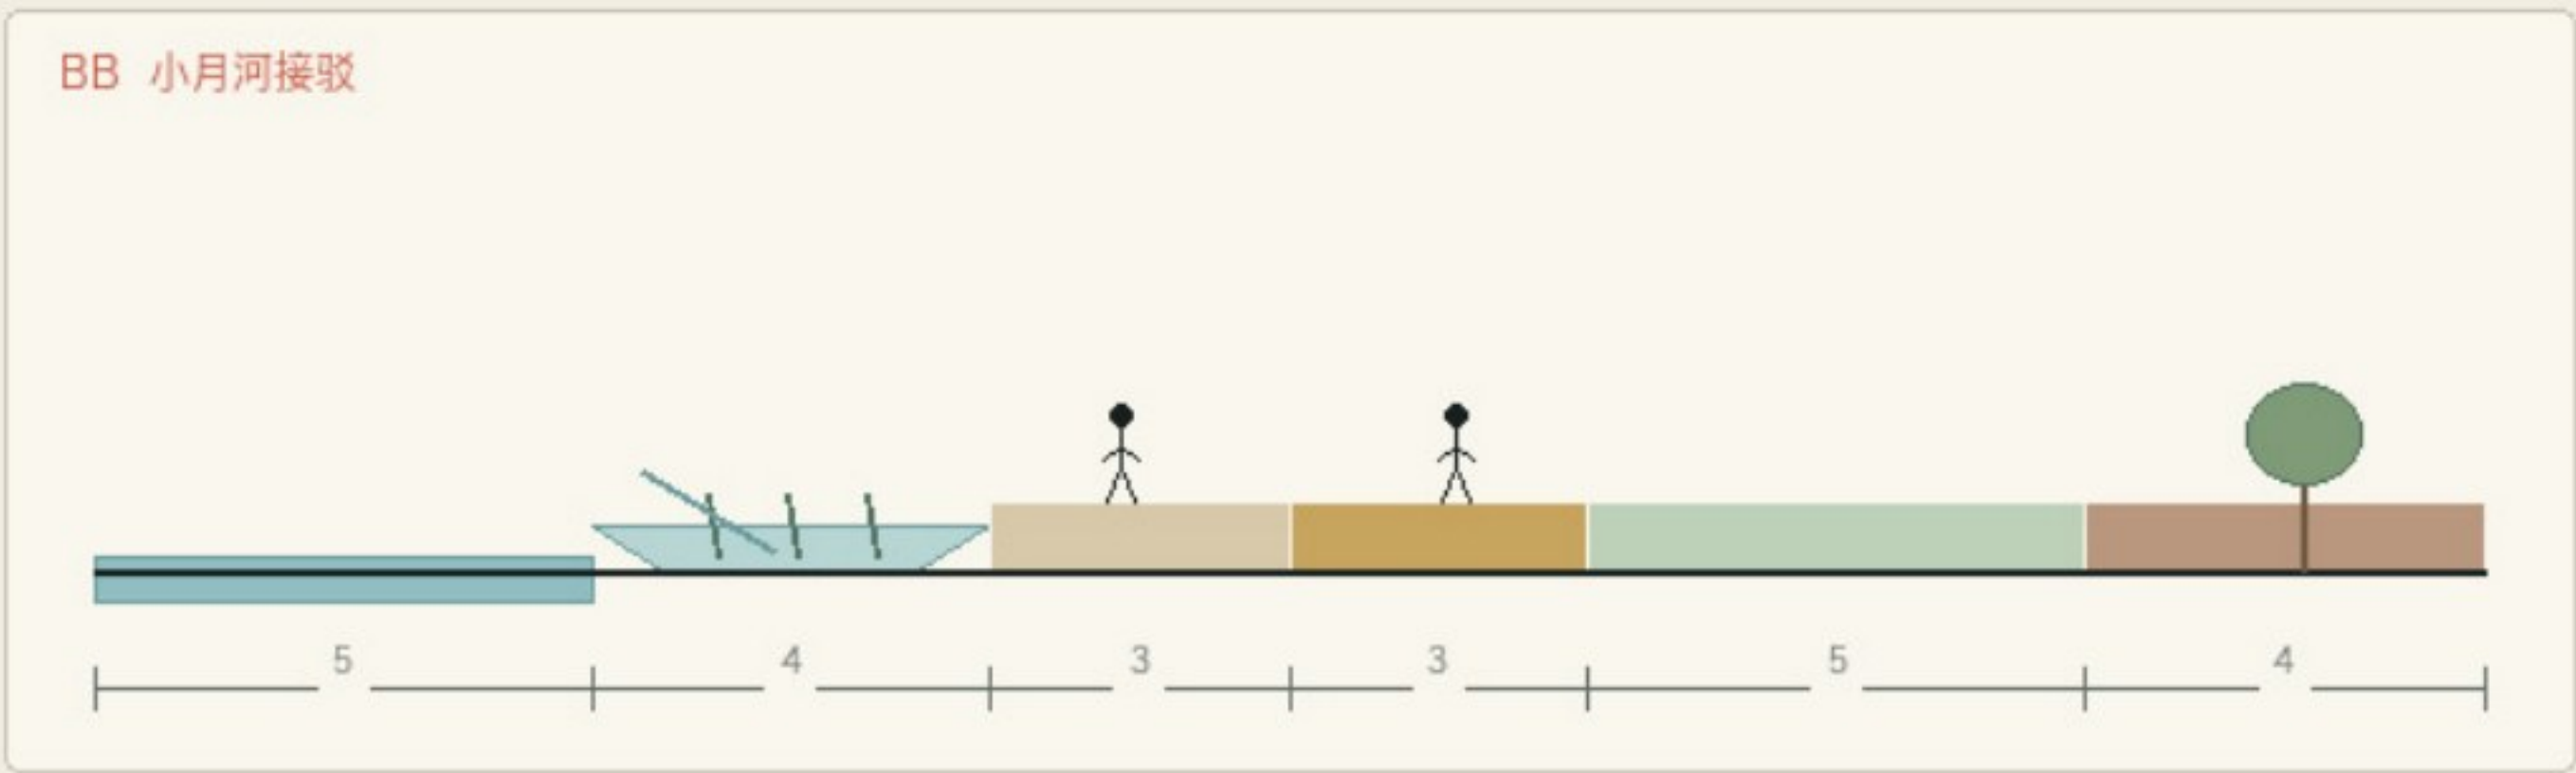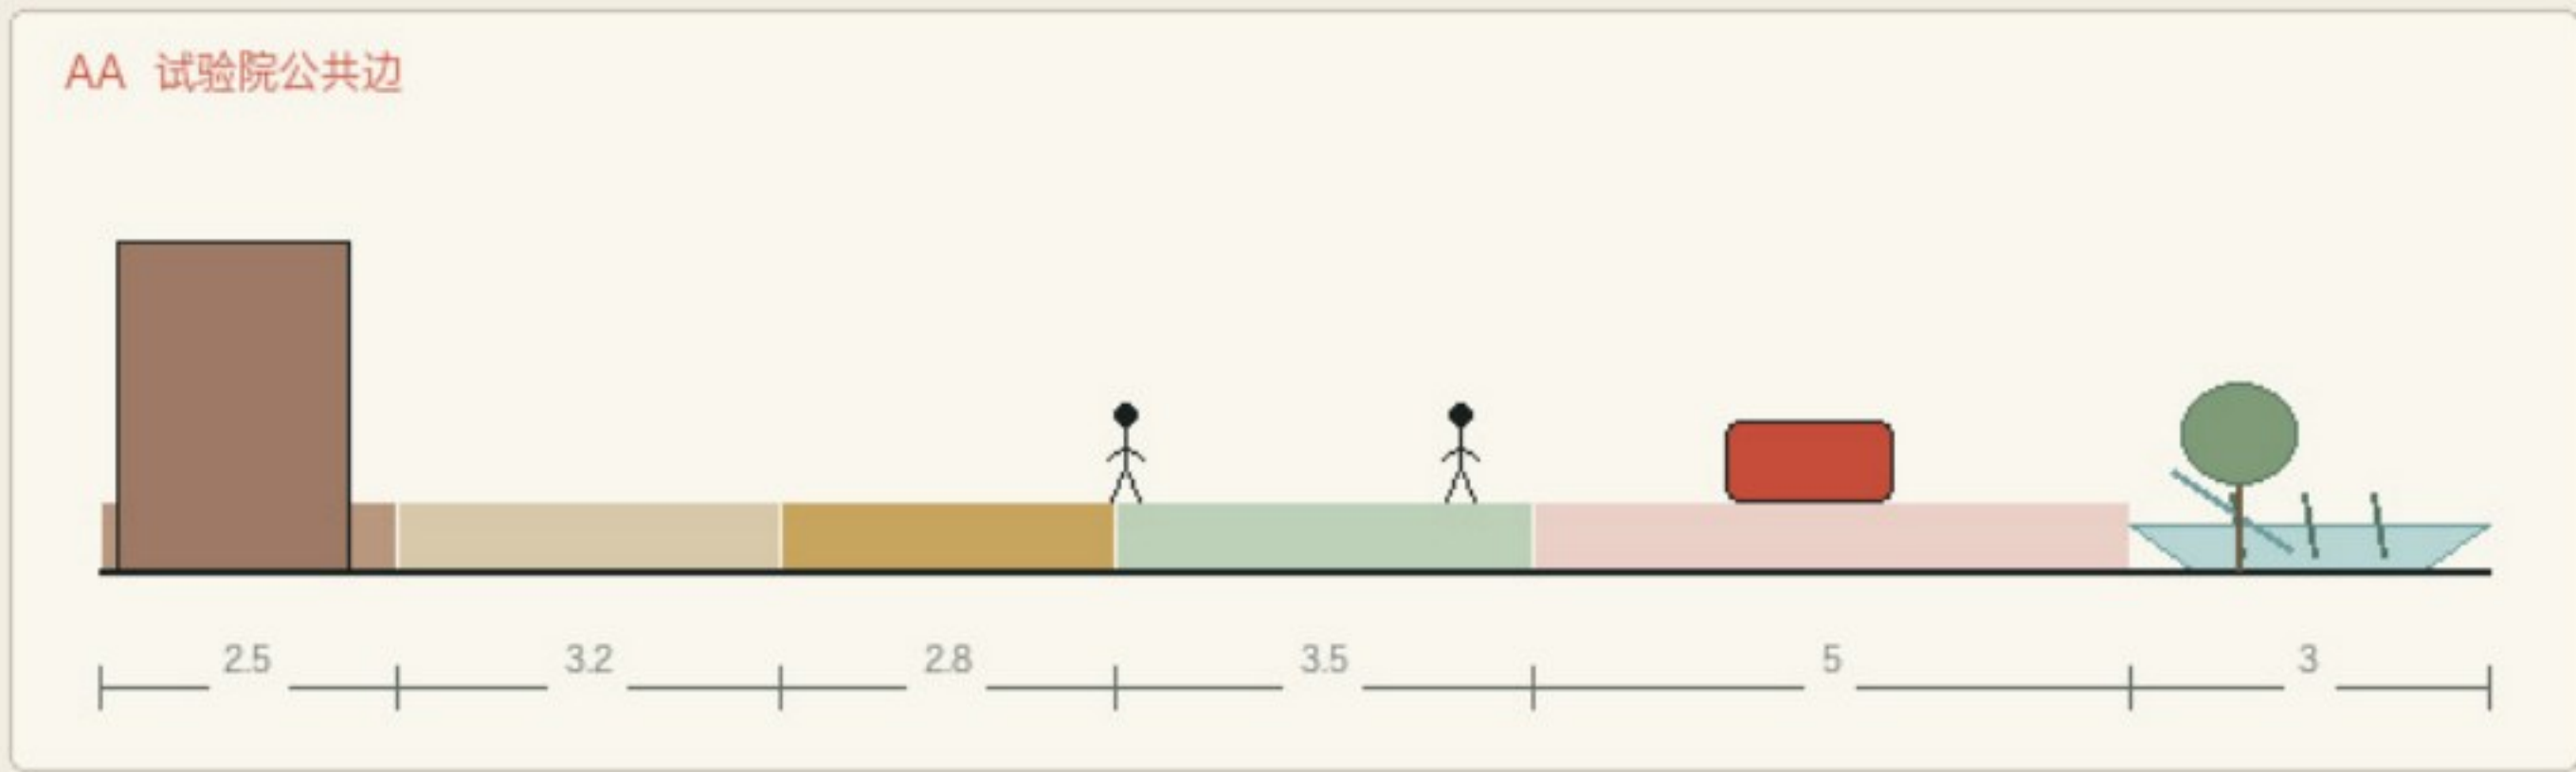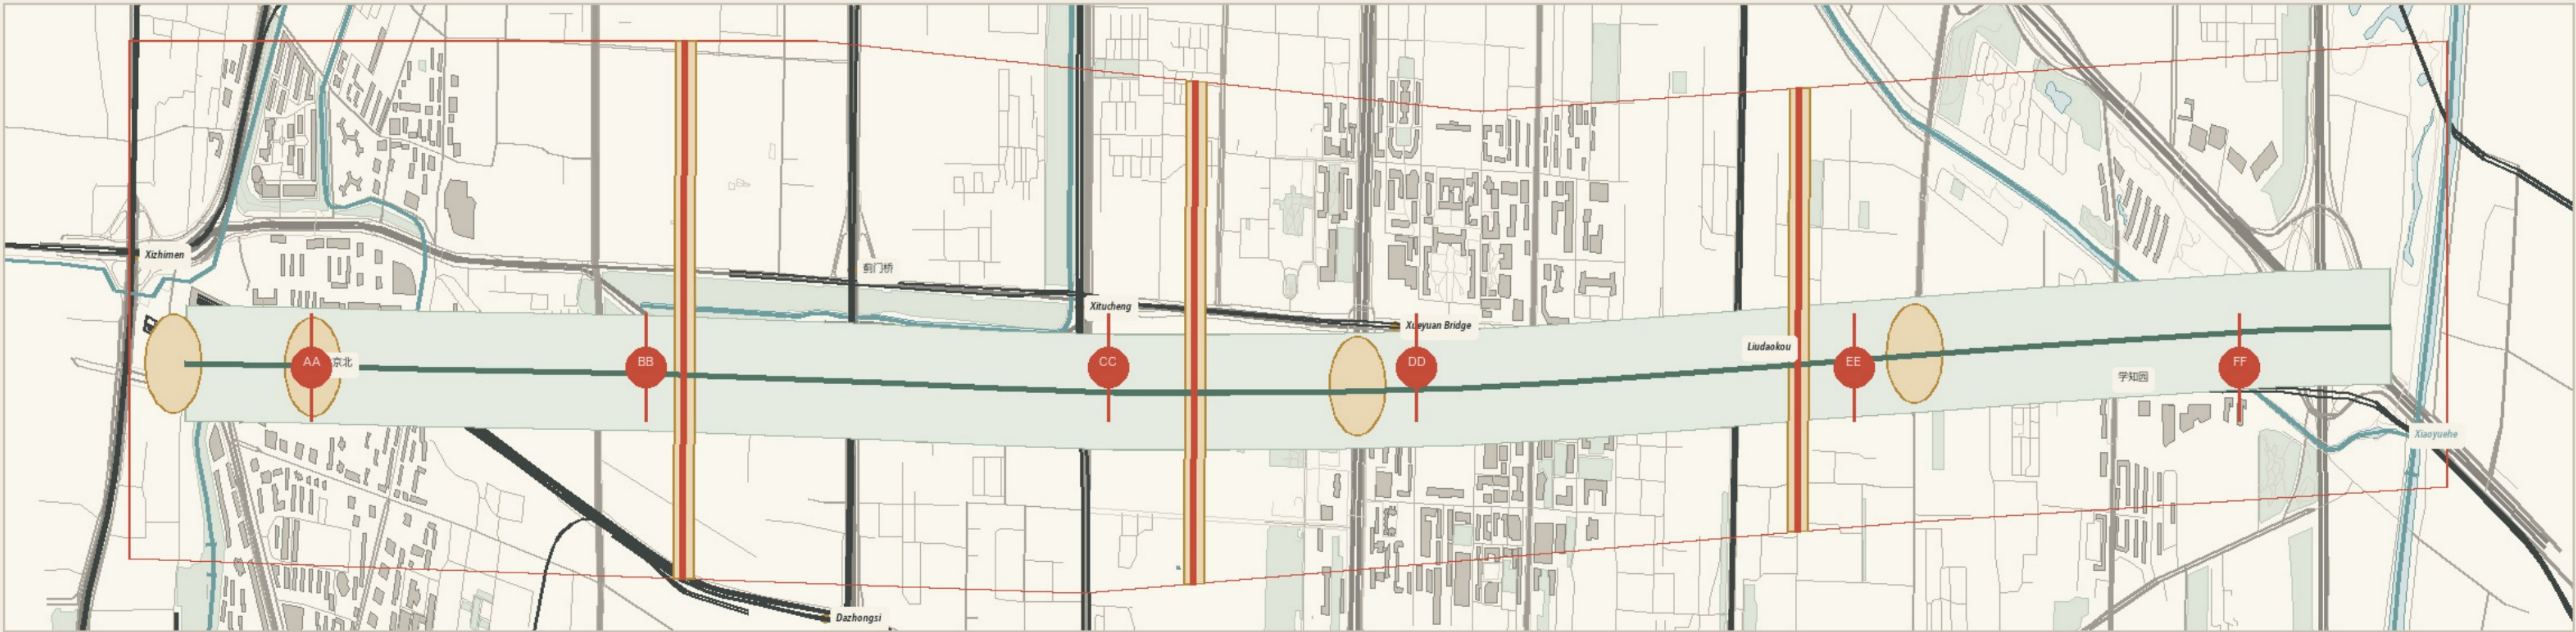

02

从九公里到一座院子

一张长线、三段街区、三个日常尺度

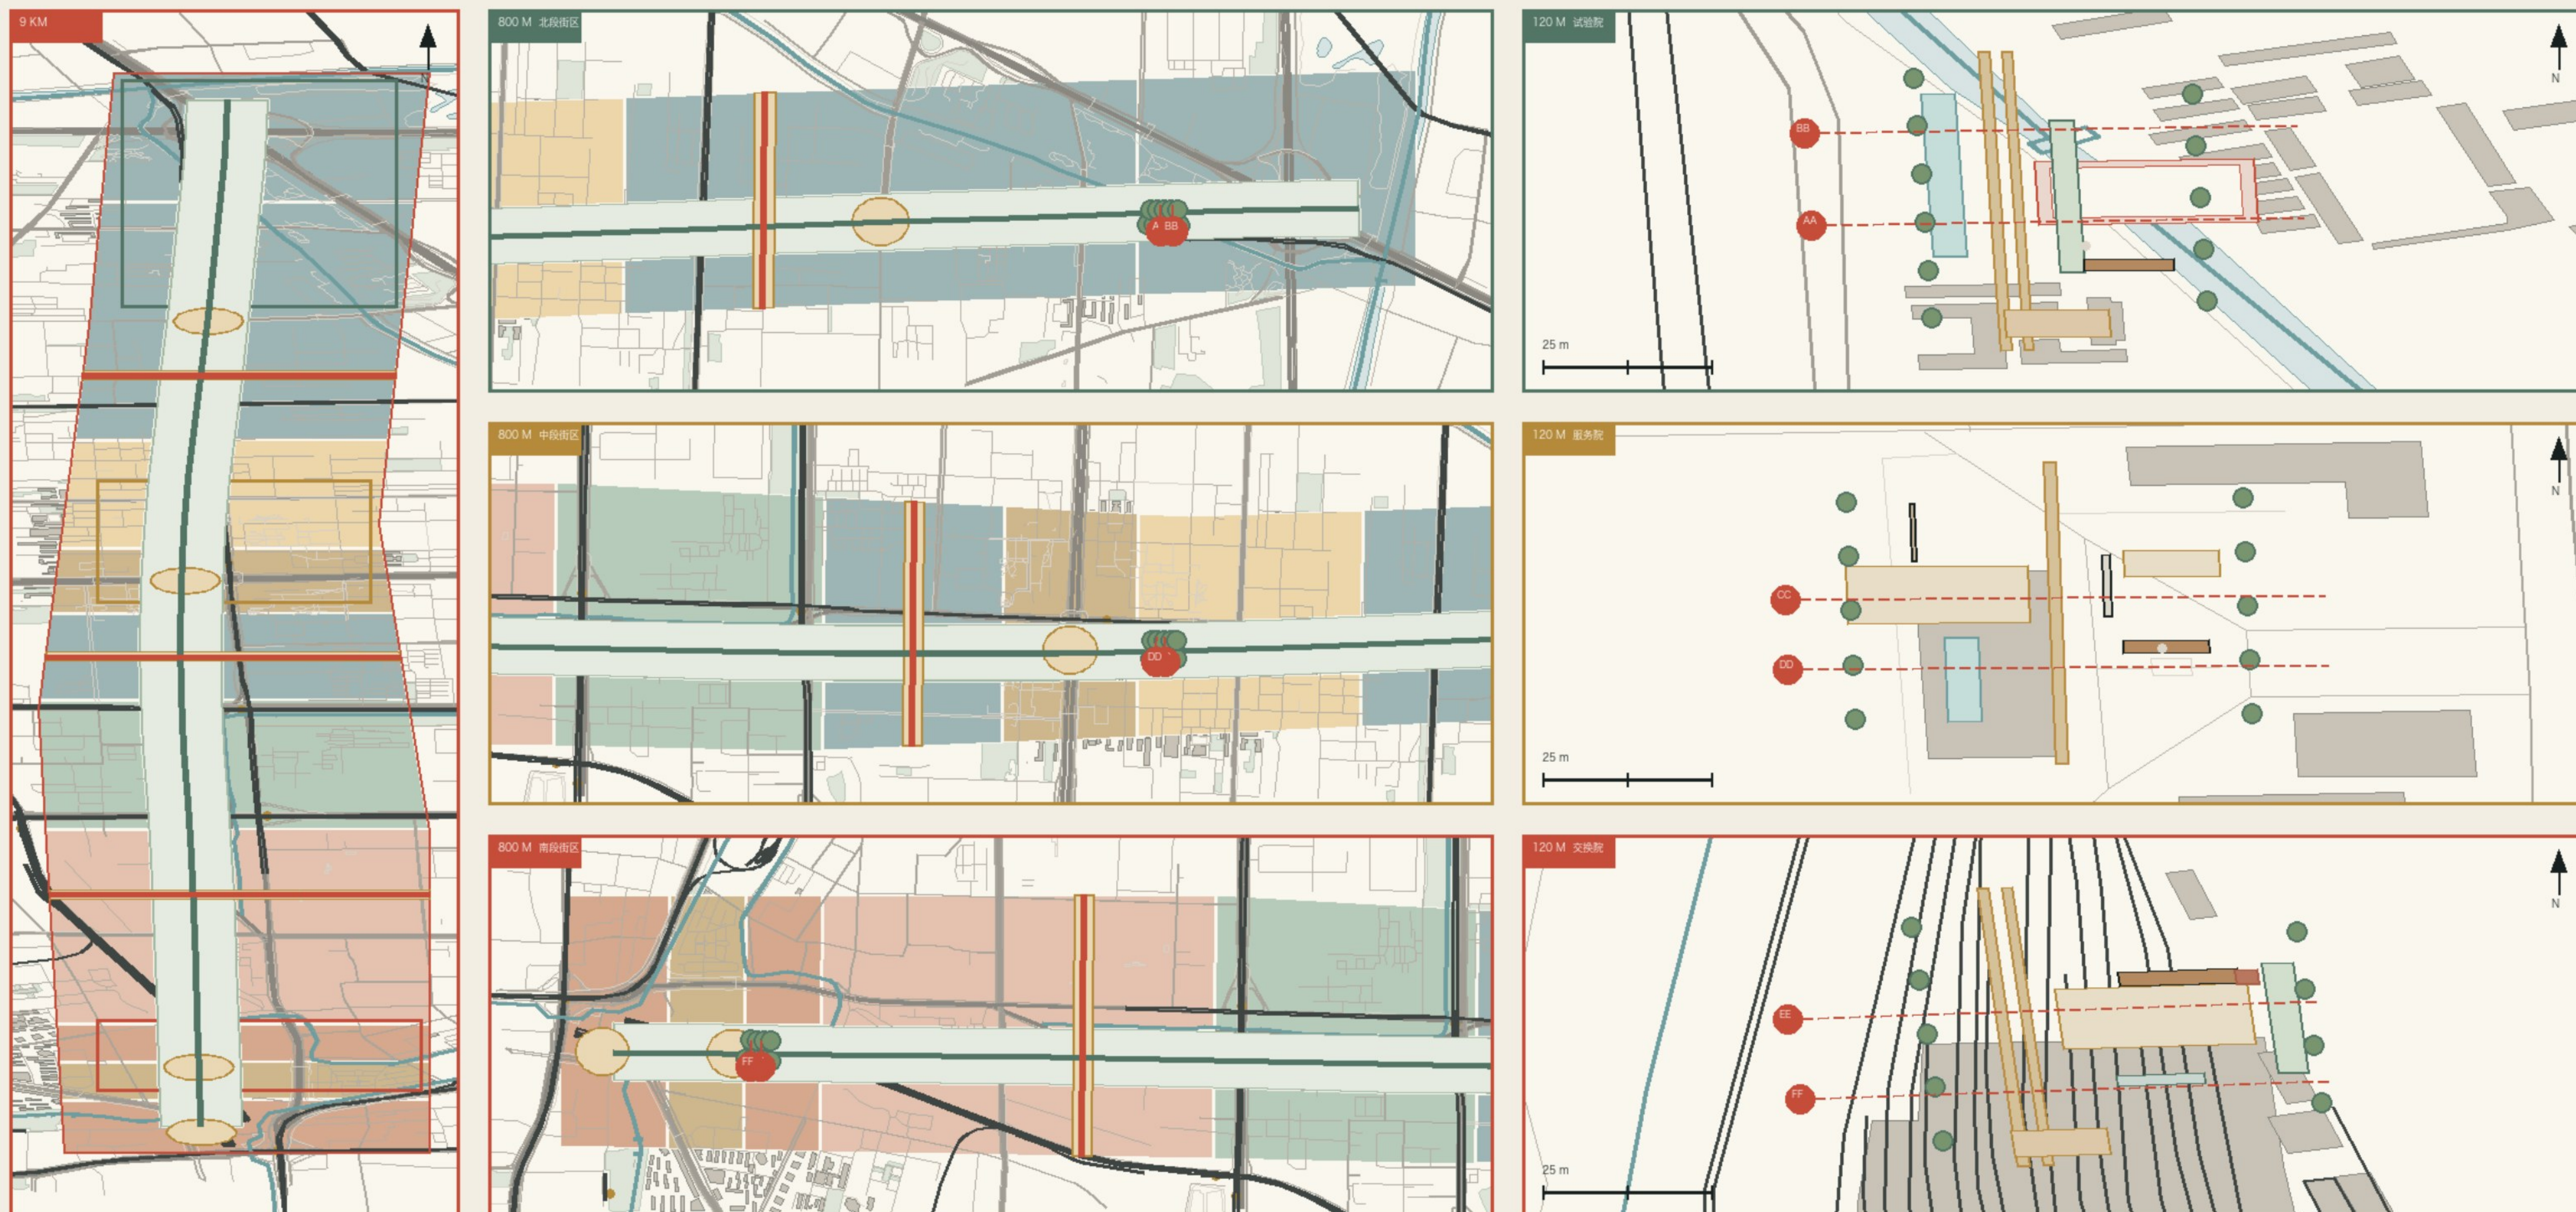

概念方案 暂定边界 OSM 仅作参考语境

Scale structure informed by REN AXIS (CC BY 4.0); redrawn for this proposal

一条公园，三座院落

RAILWAY COMMONS / RESEARCH · SERVICE · EXCHANGE





● 研究雨庭

● 有人服务

● 日常交换

空间语言合成图 | 三院落并置展示，不代表实际相邻关系或比例

OPEN-CITY-AI / HAIDIAN

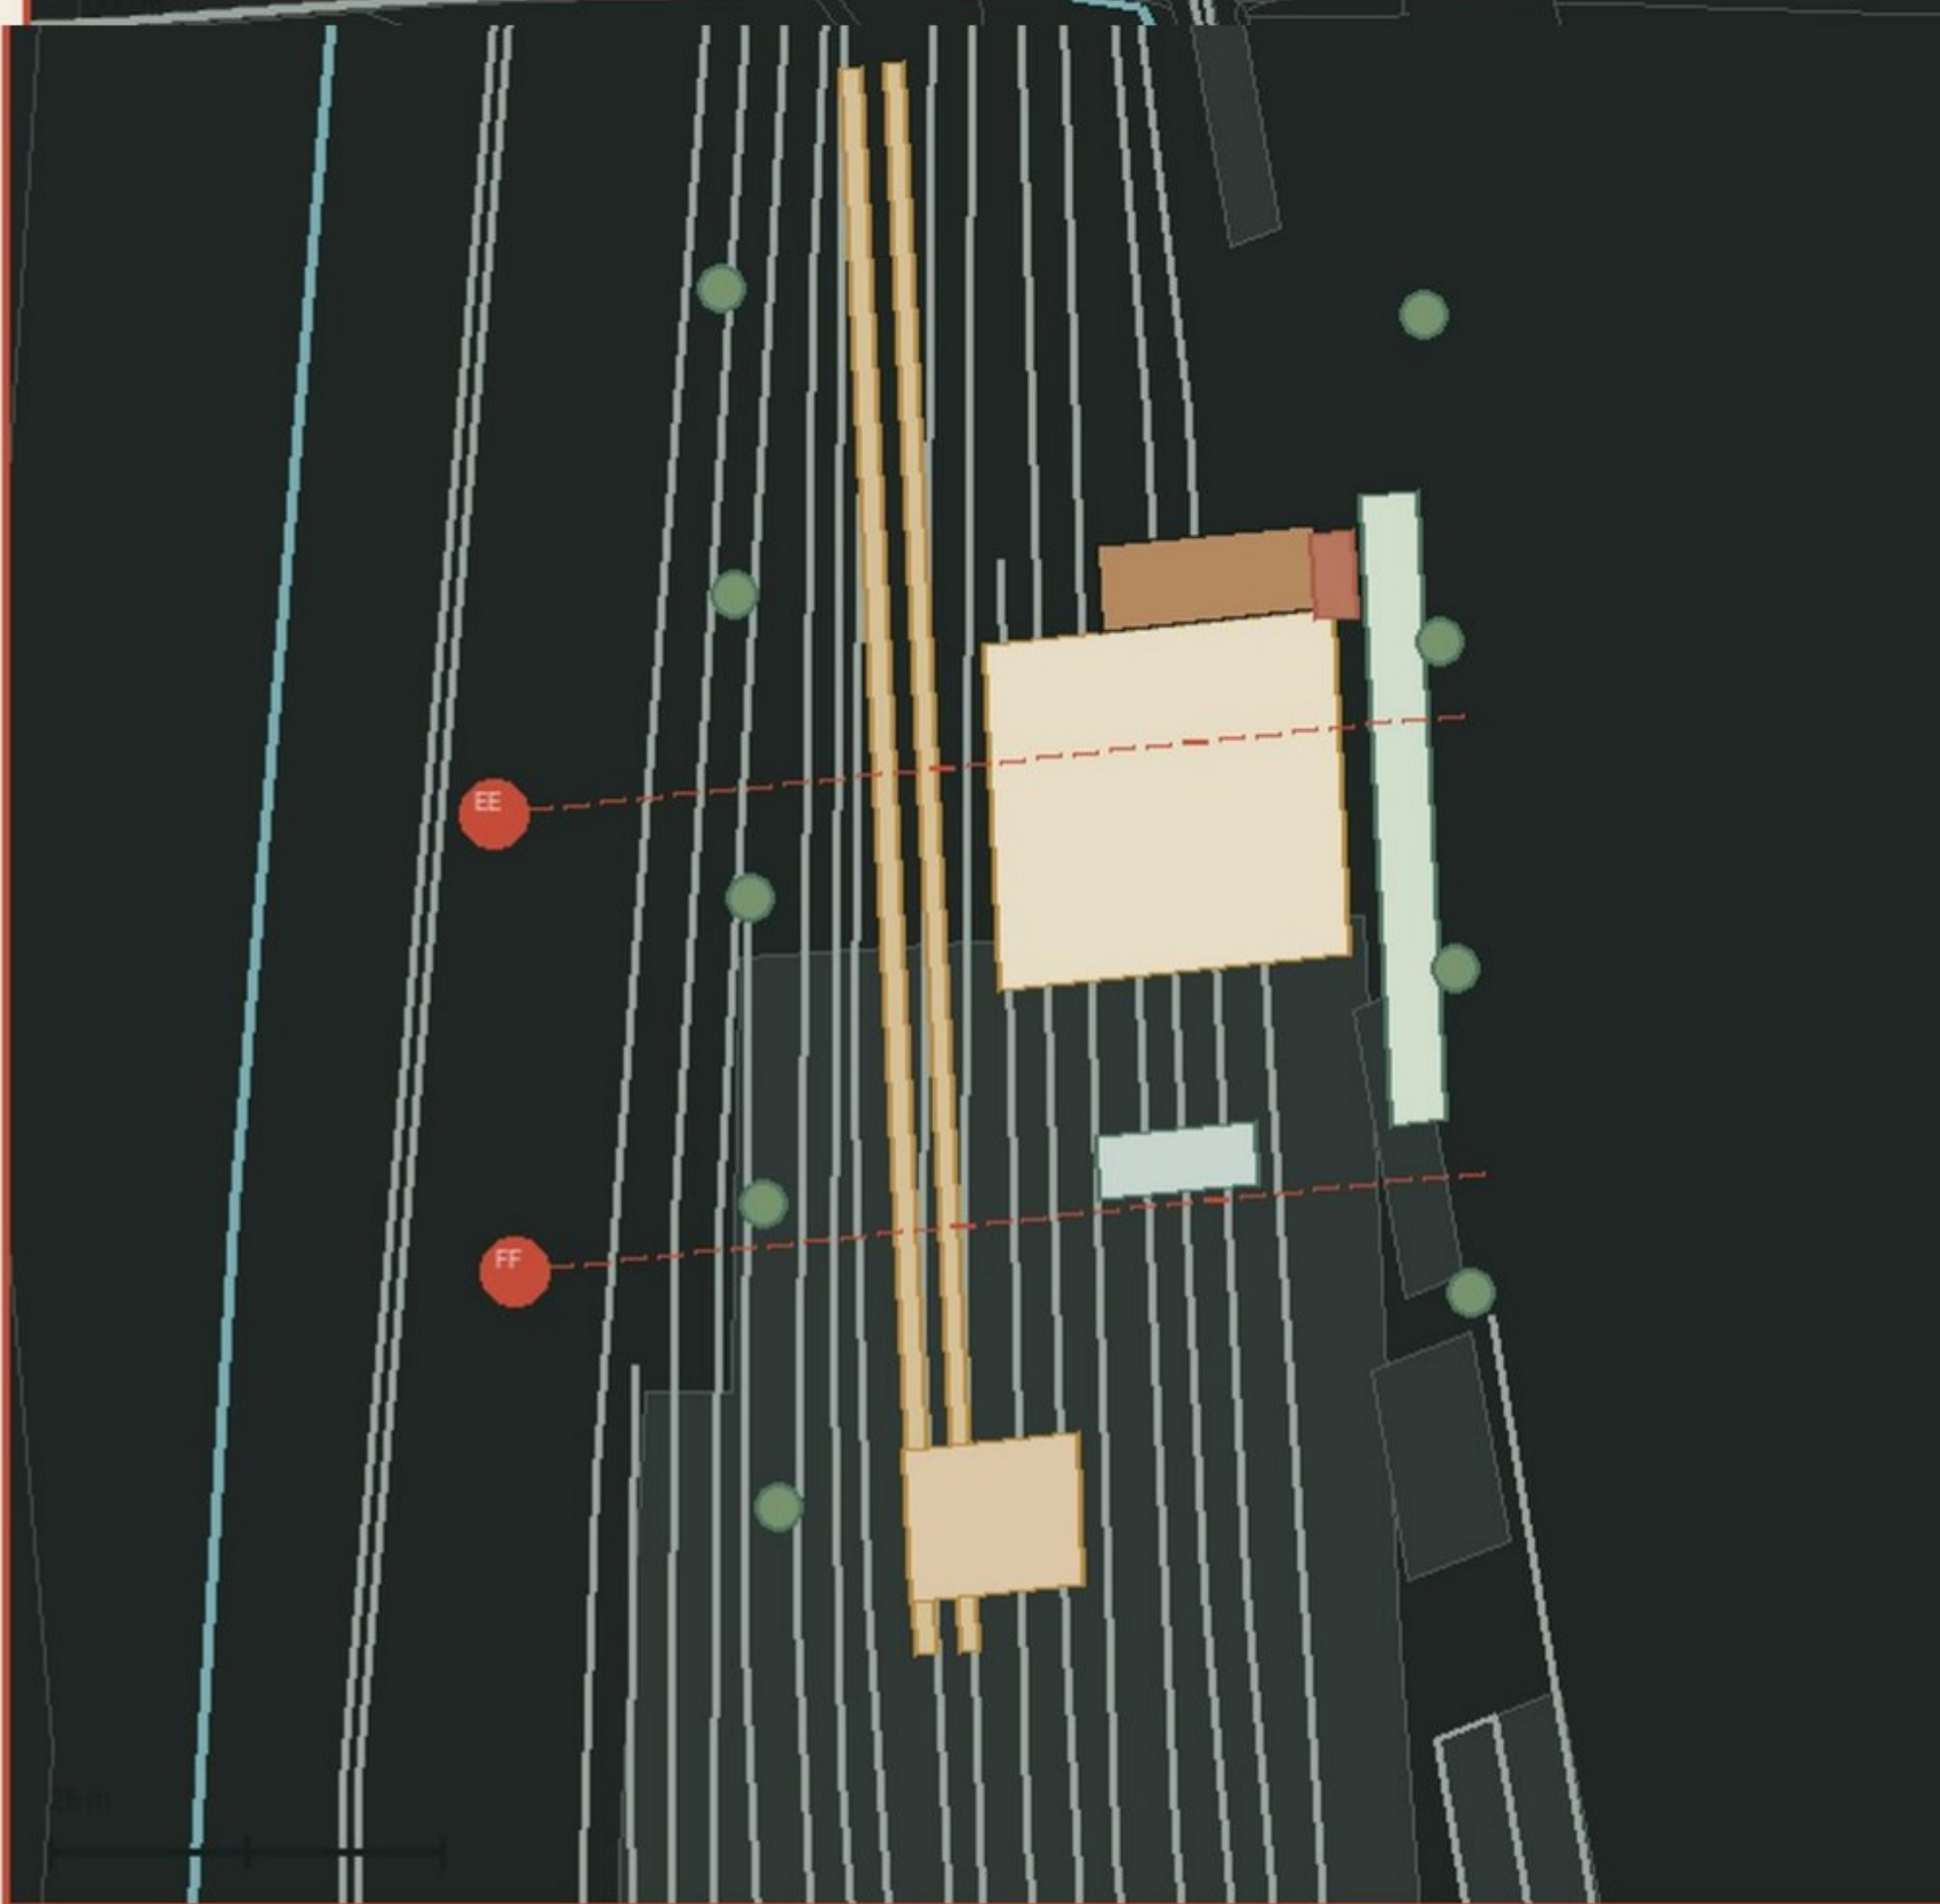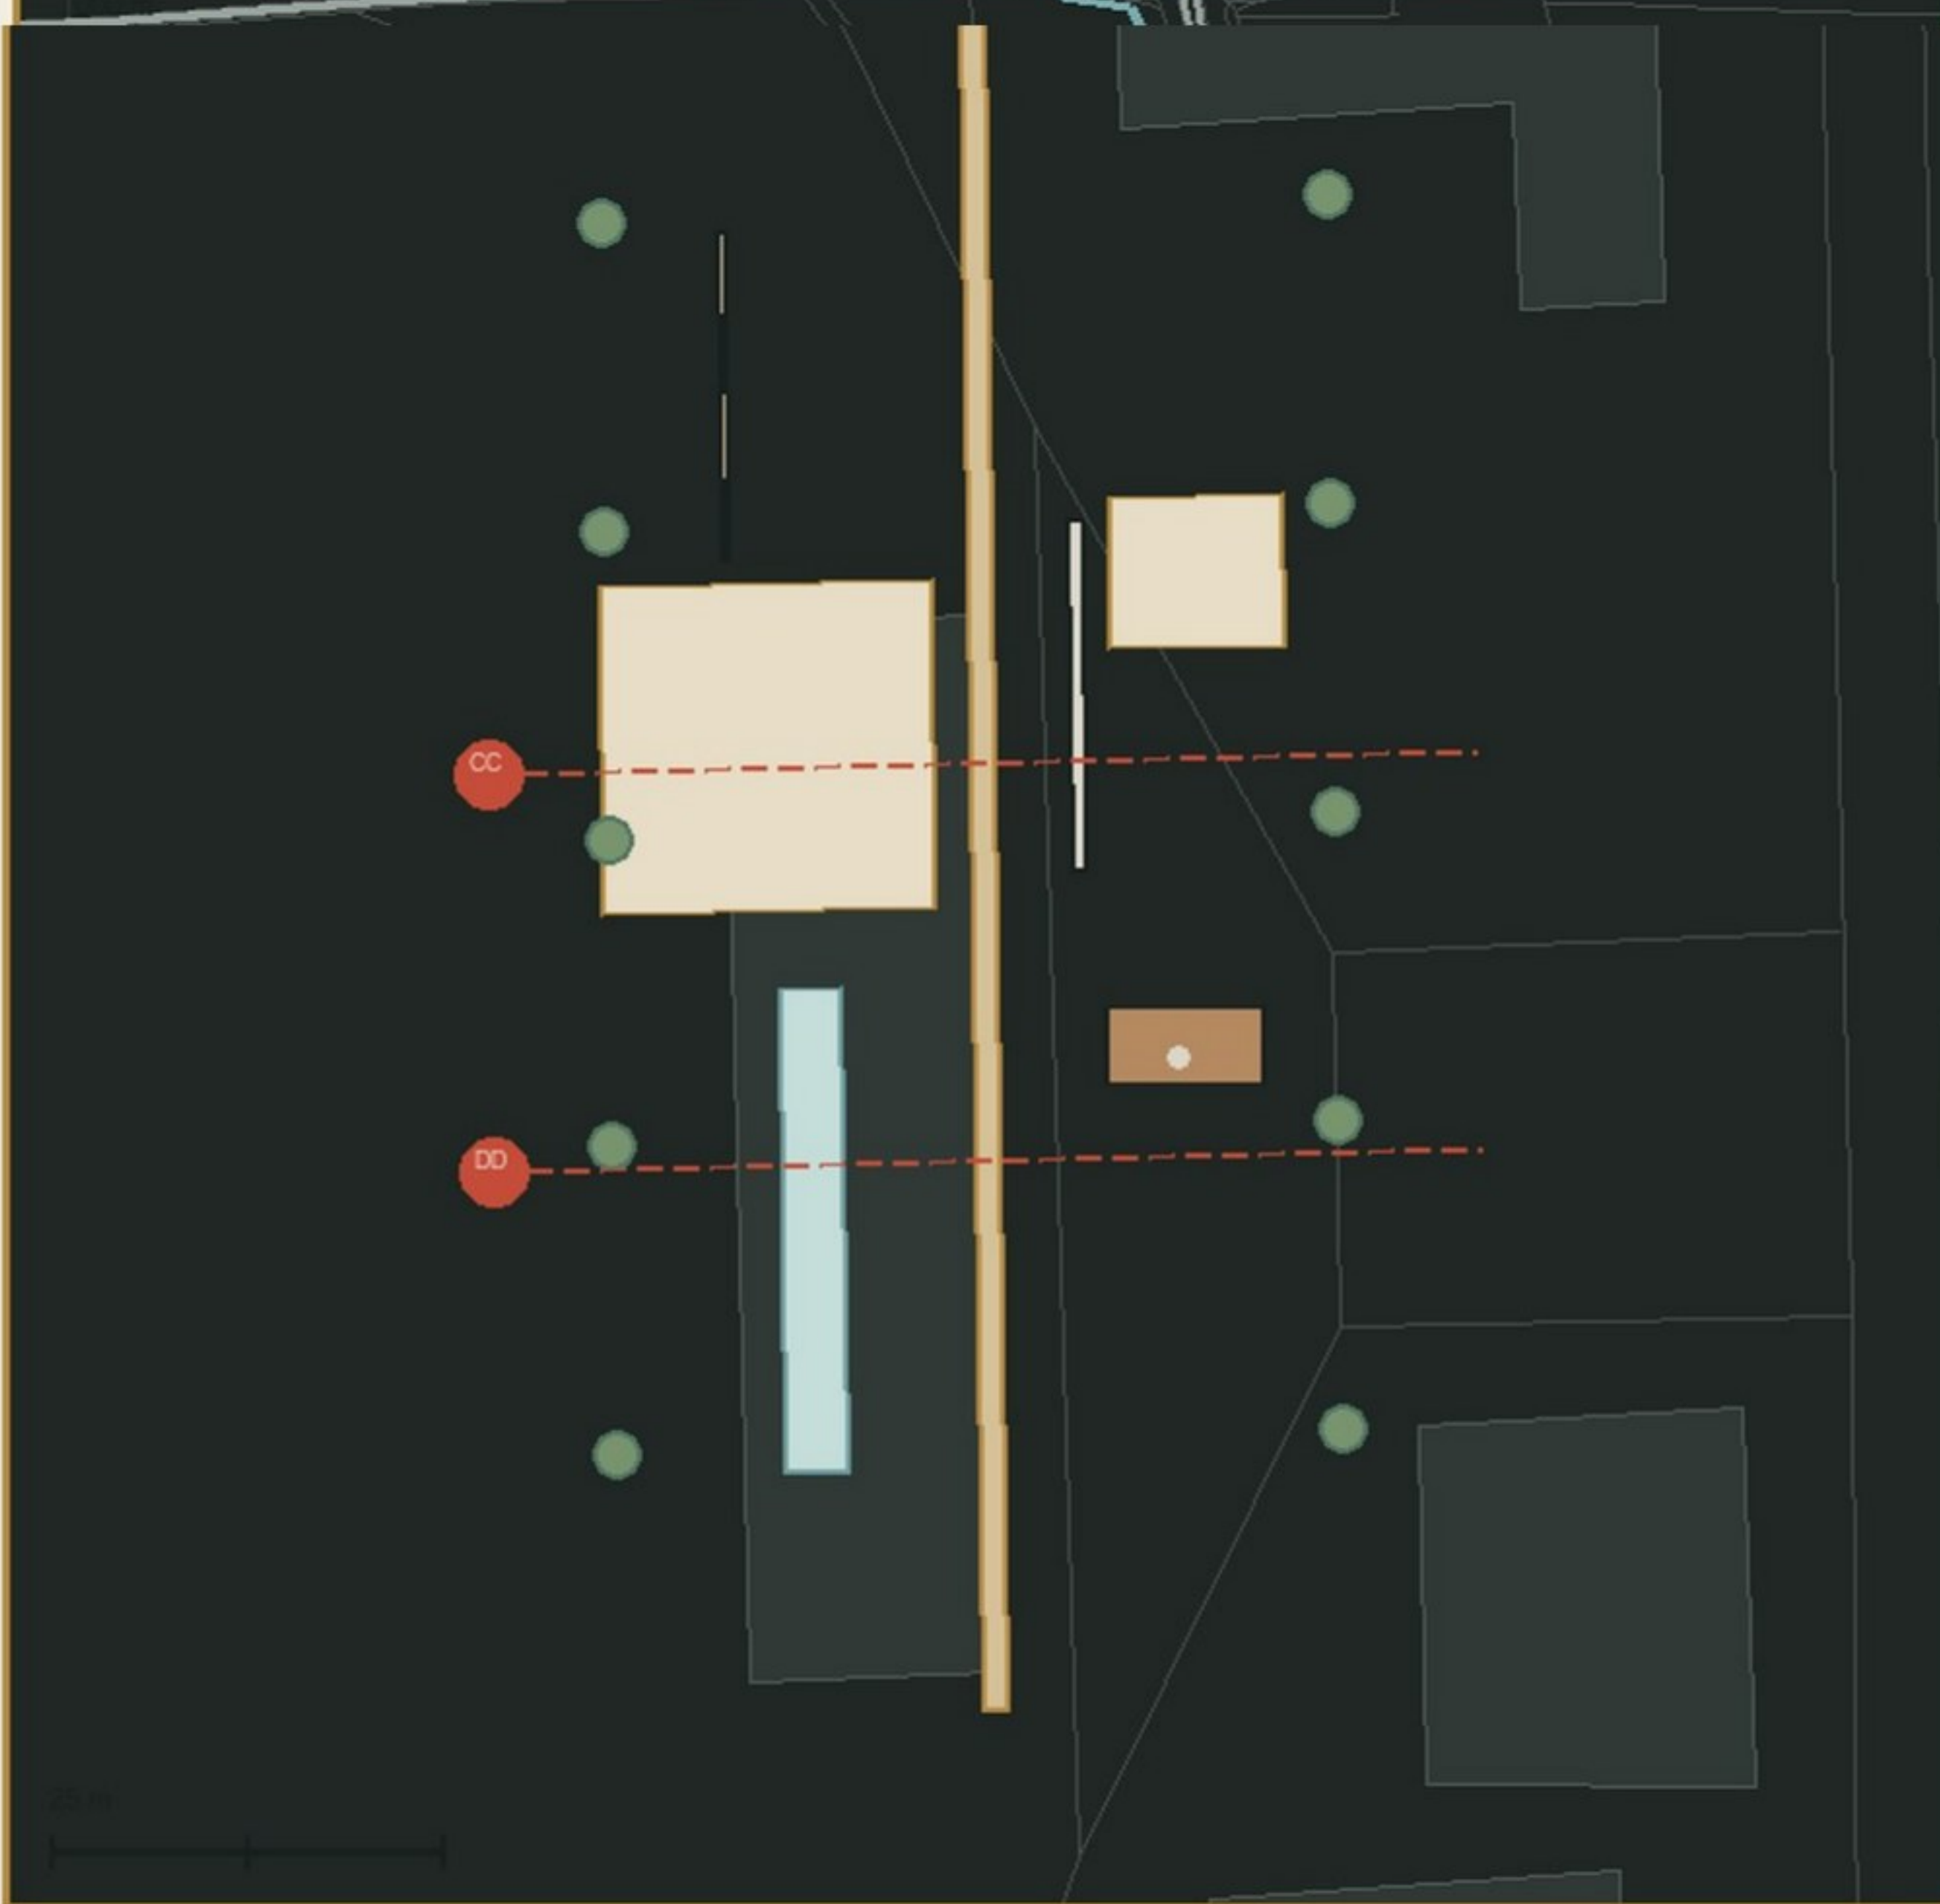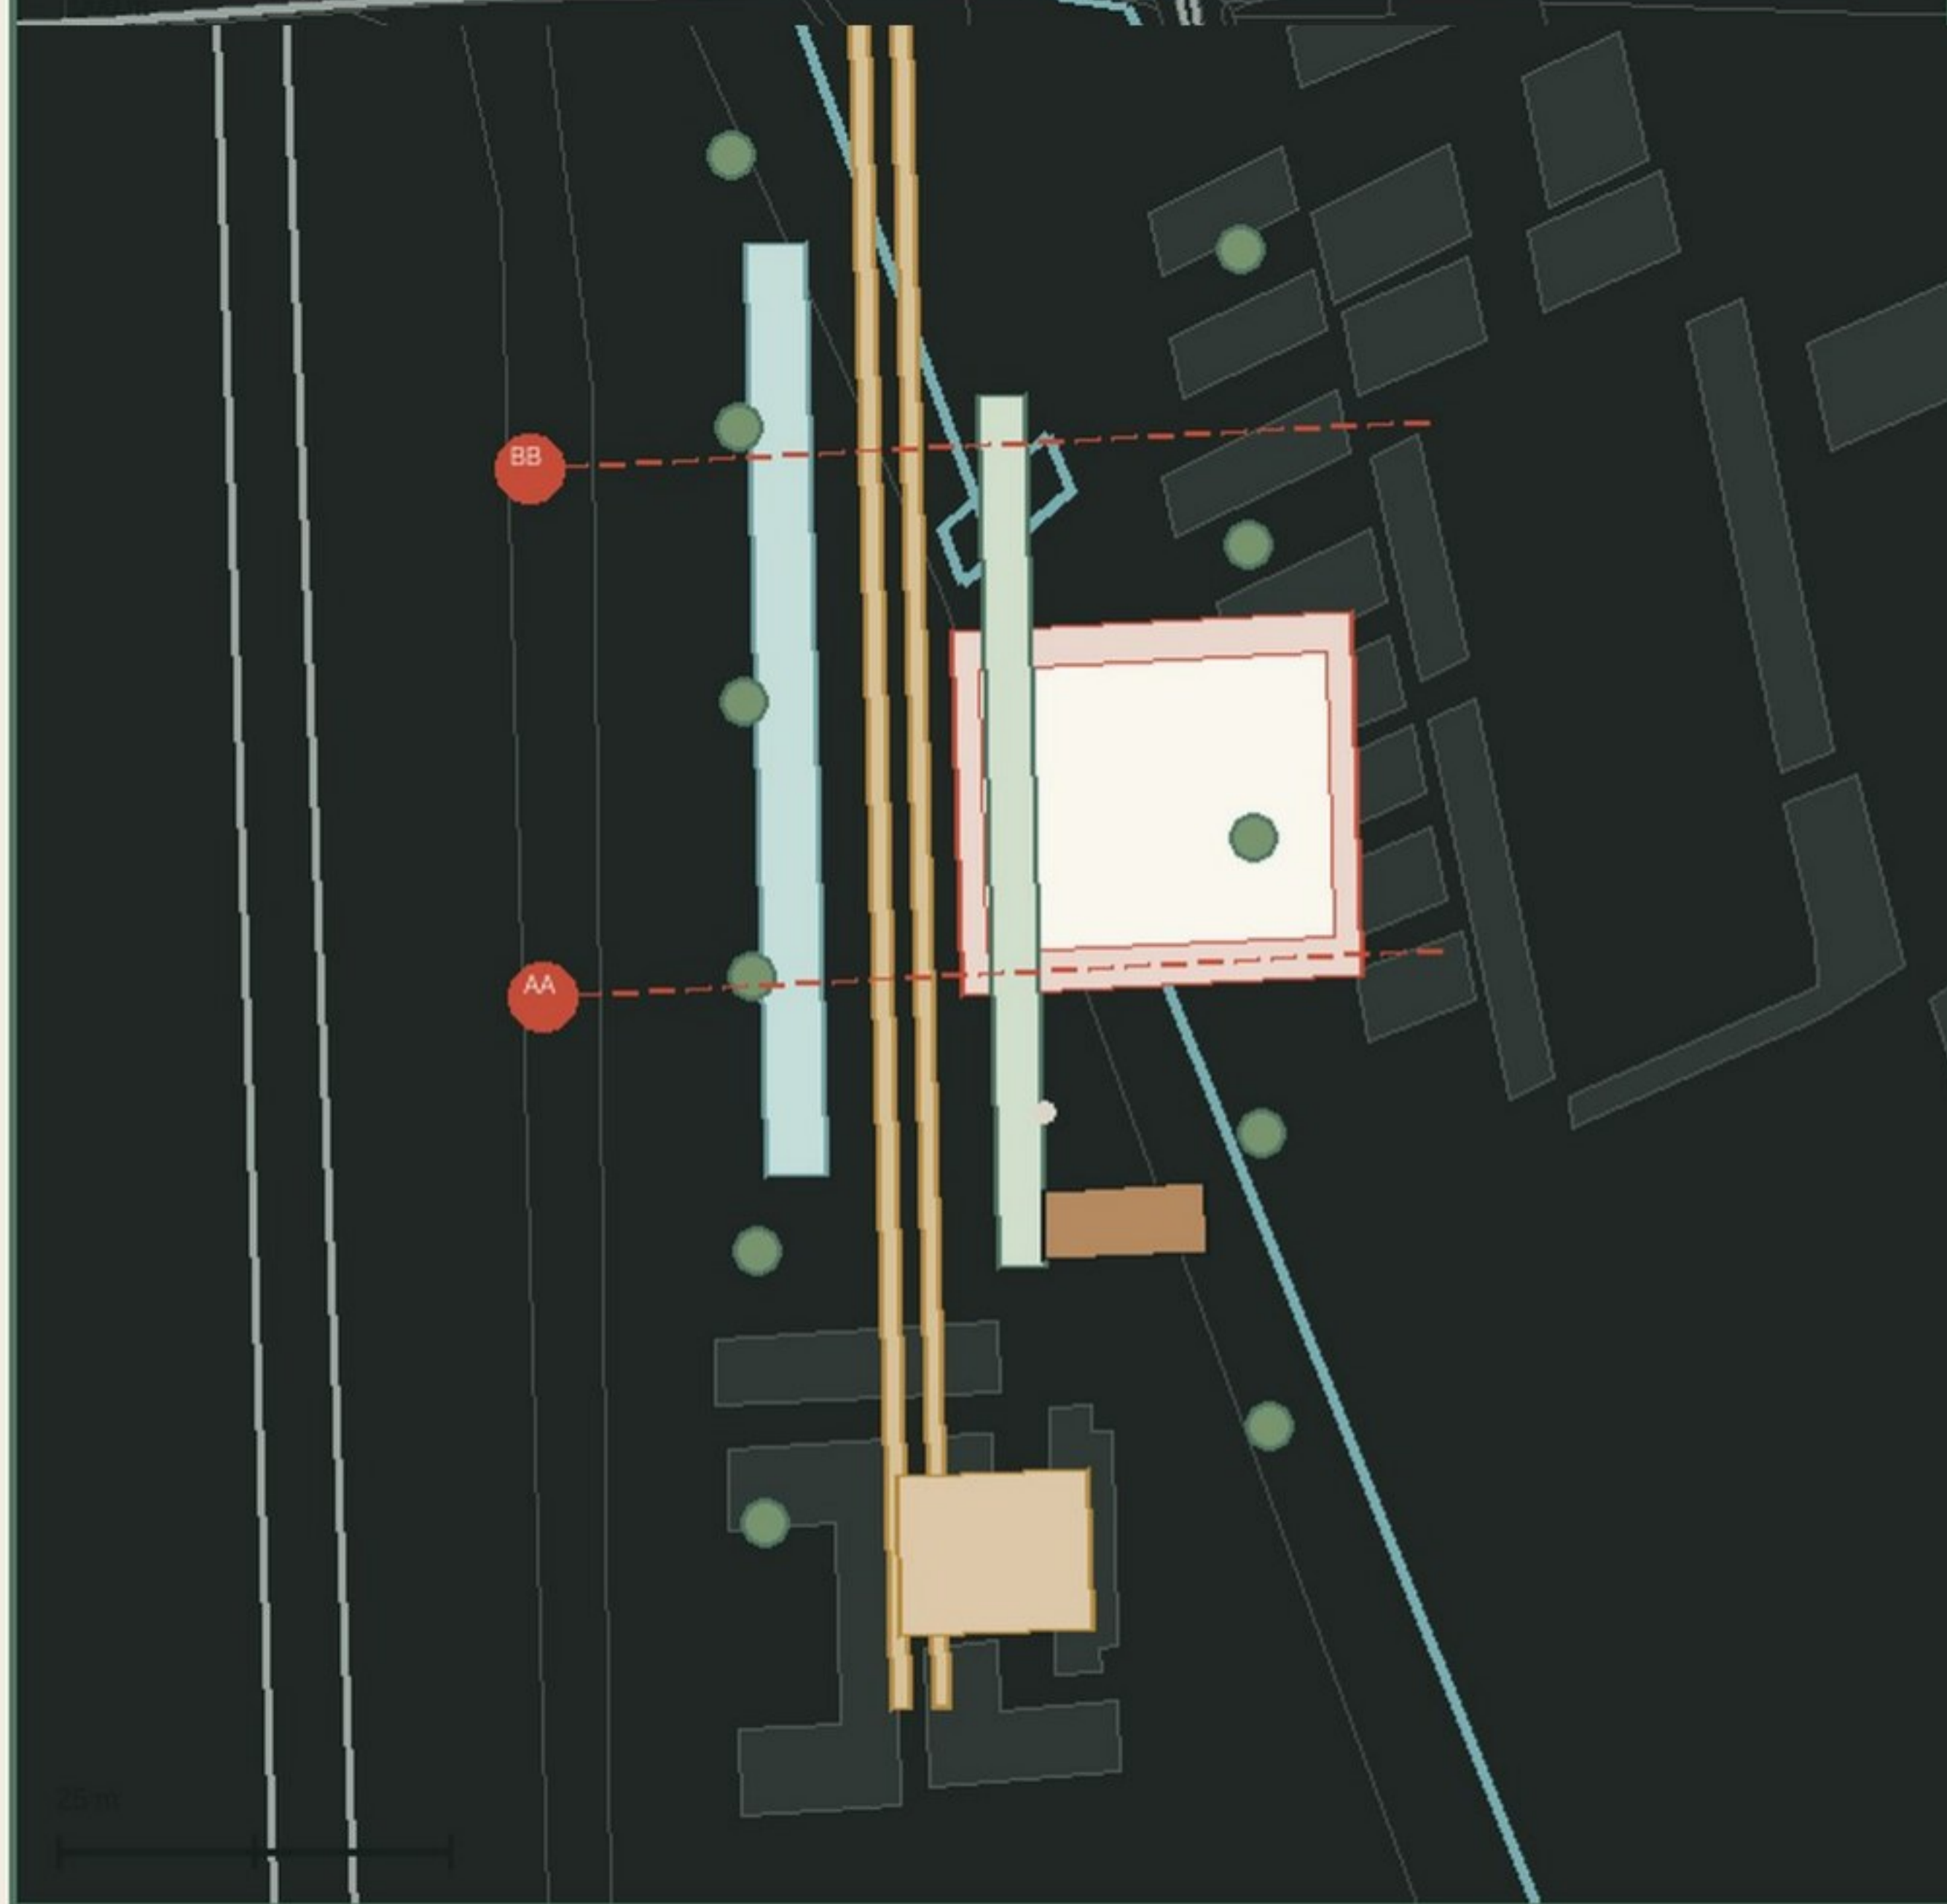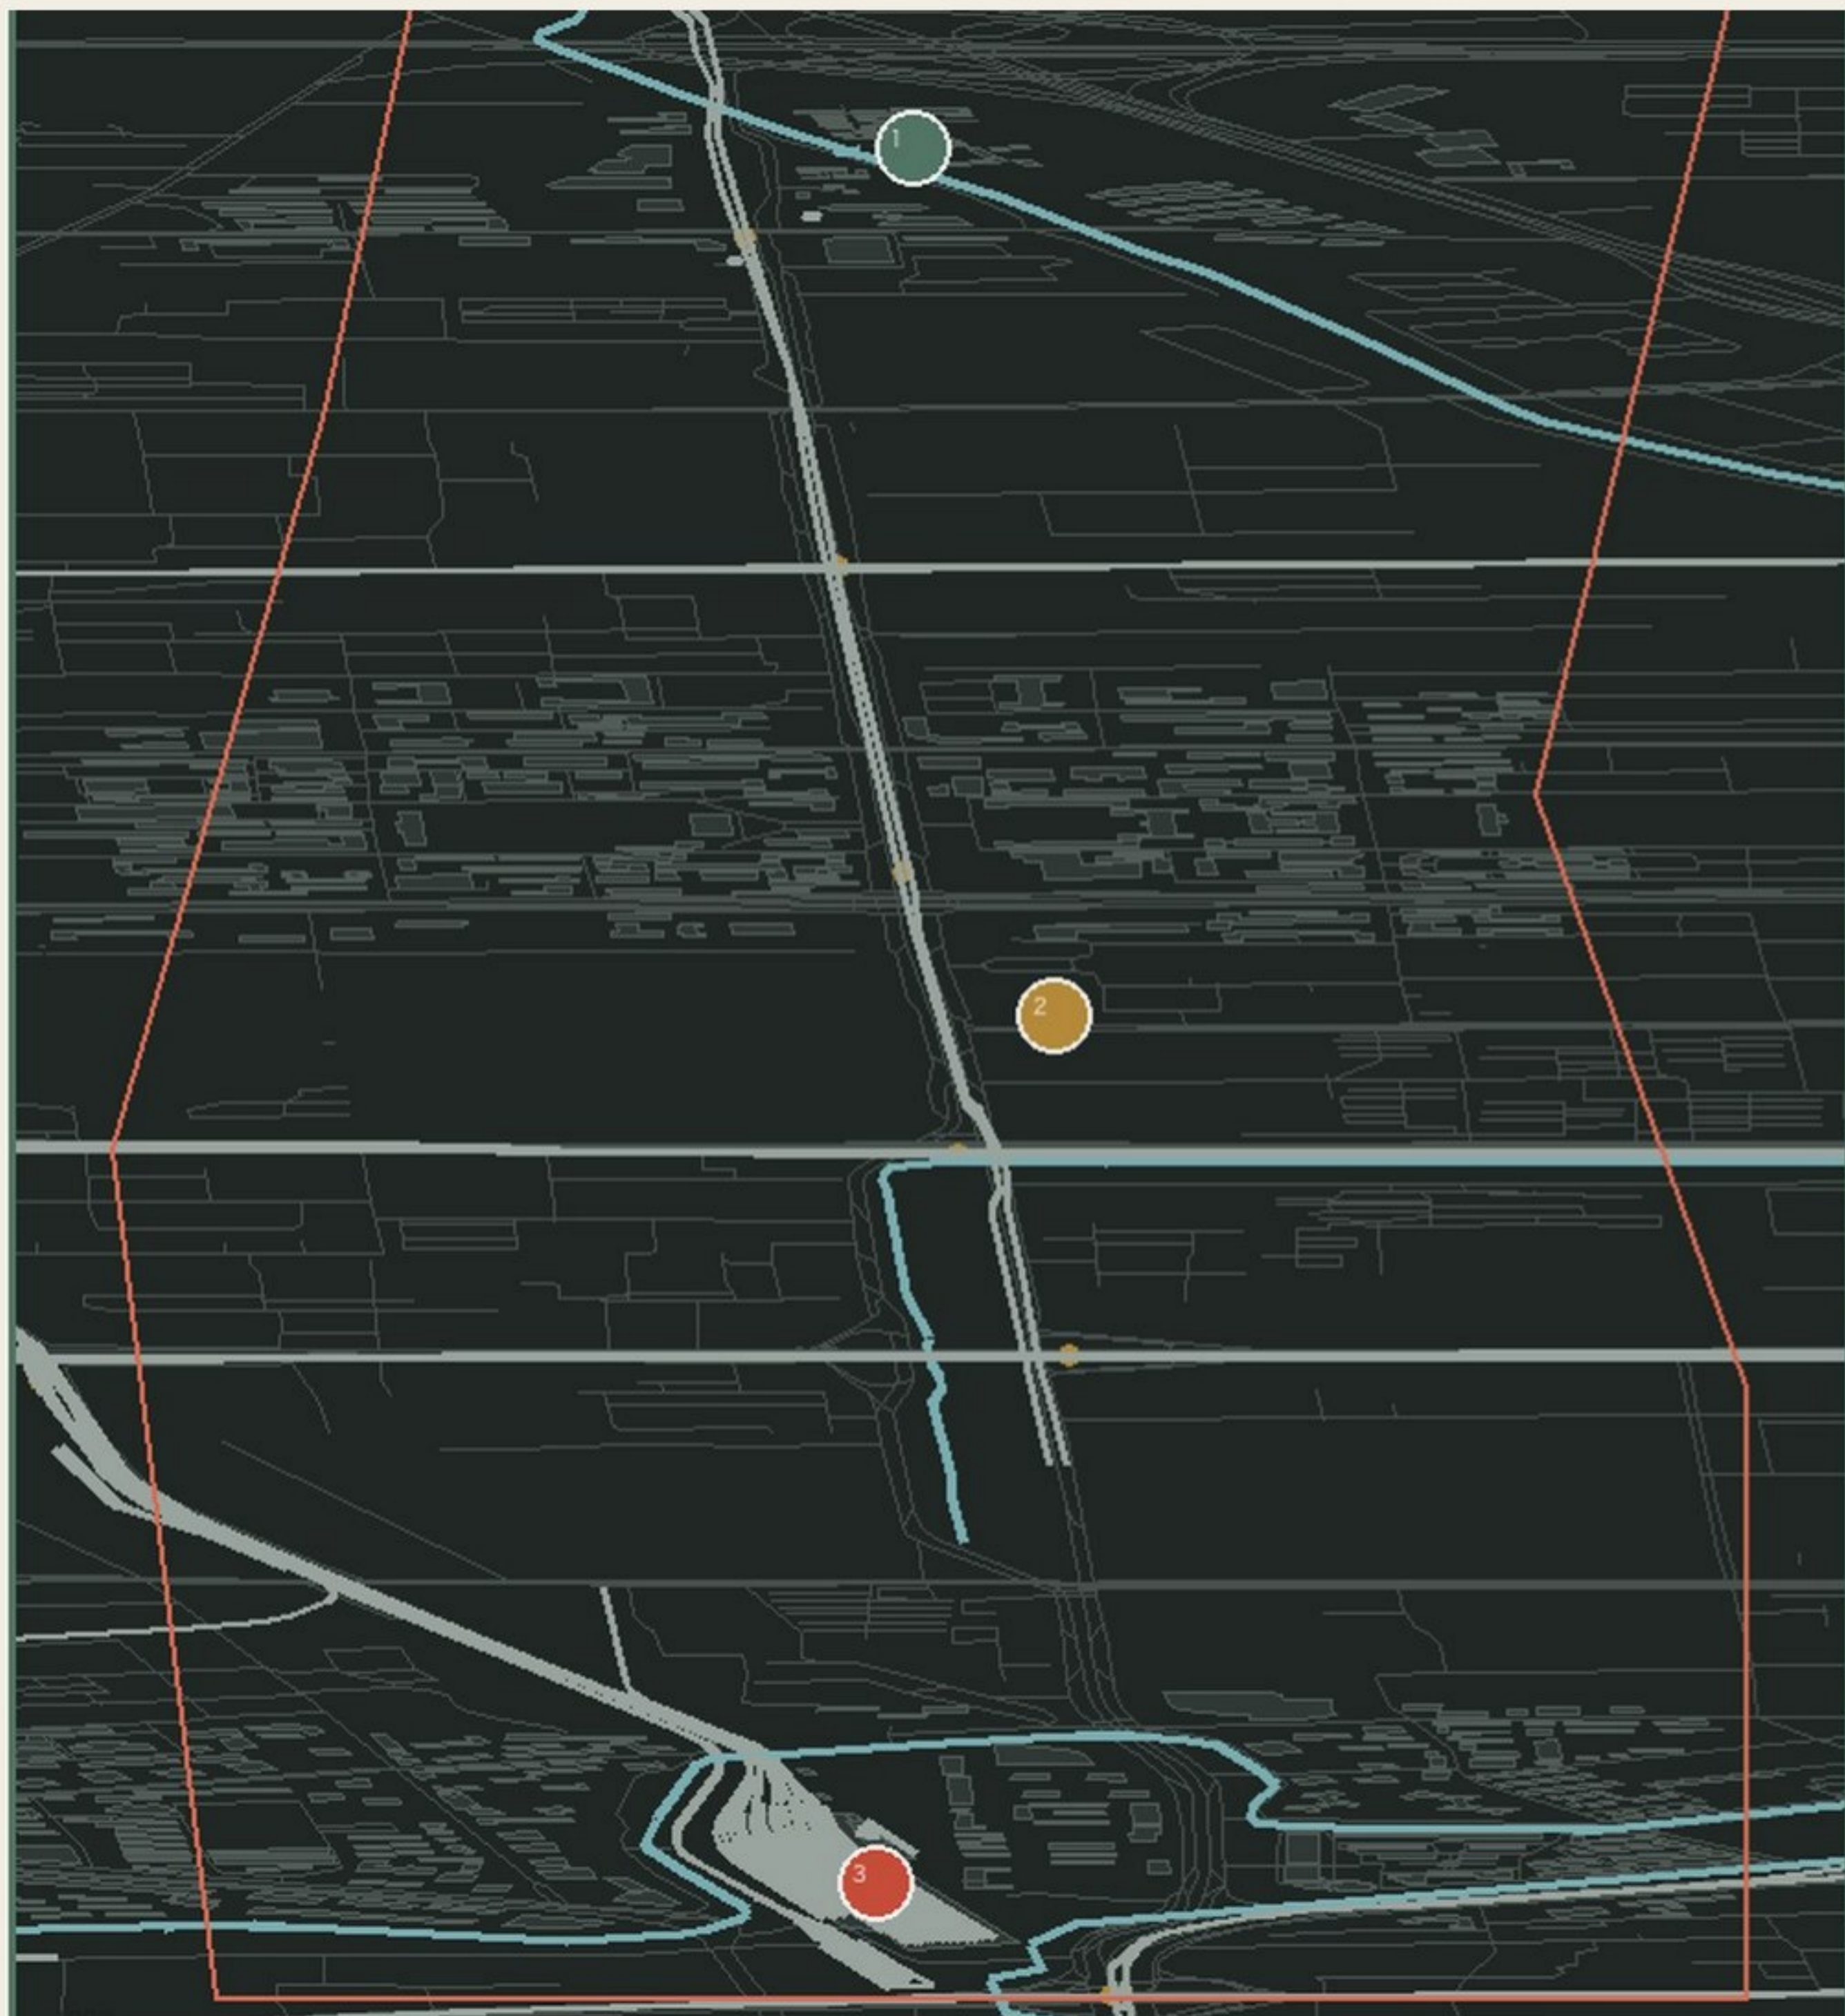

3.2 m

2.8 m

3.5 m

500 m

14 / 6

9