



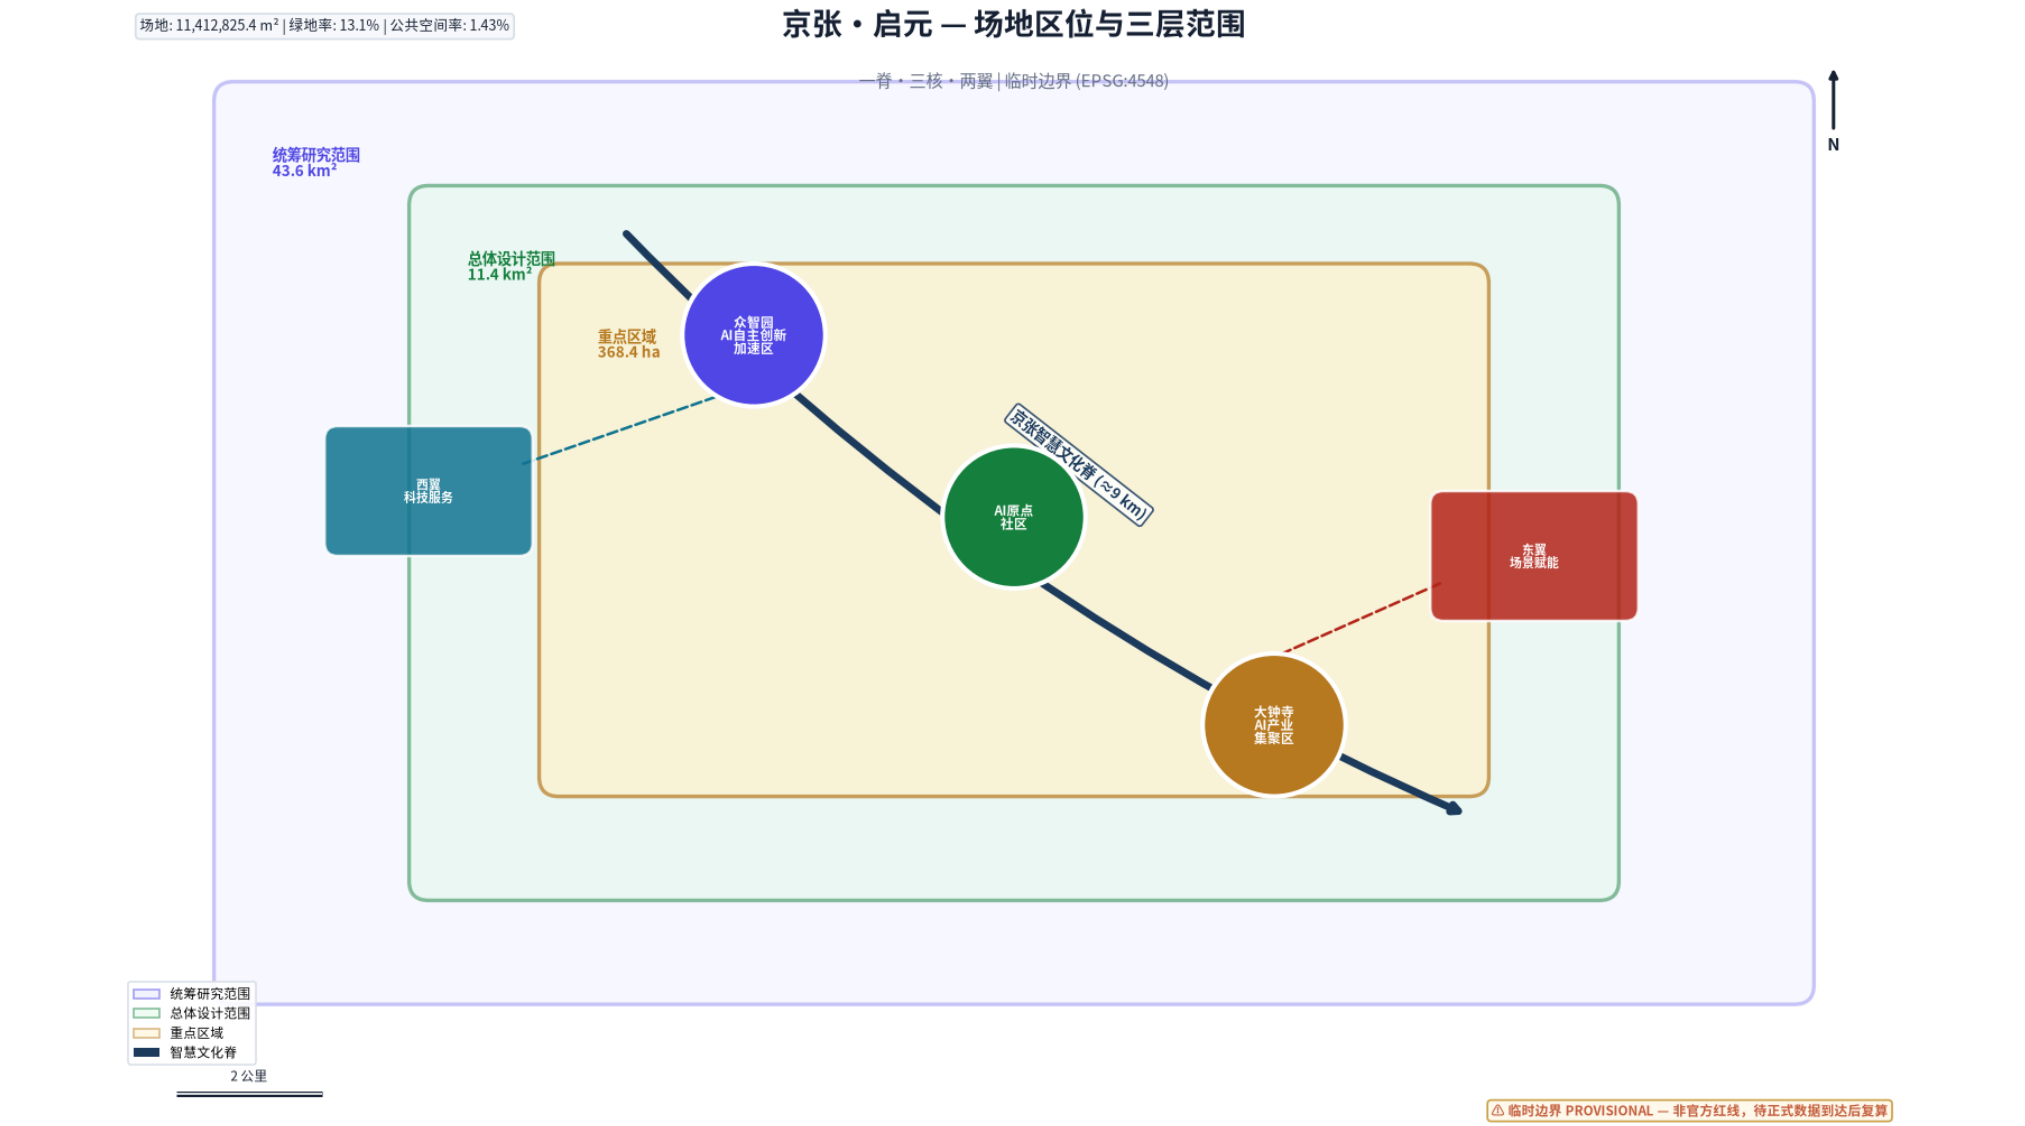

设计理念

- 1909年，詹天佑主持建成京张铁路——中国人自主设计的第一条干线铁路。
- 2026年，同一条廊道成为首批面向AI智能体开放的城市设计场域之一。
- 空间结构：「一脊·三核·两翼共生」。
- 所有几何均为临时边界，非官方红线。正式数据发布后须复算。


场地面积	绿地率	公共空间率	建筑数量	重点区	道路率
11.41 km ²	13.1 %	1.43 %	44 栋	3 处	8.3 %
临时边界 — 非官方红线，待正式数据到达后复算					

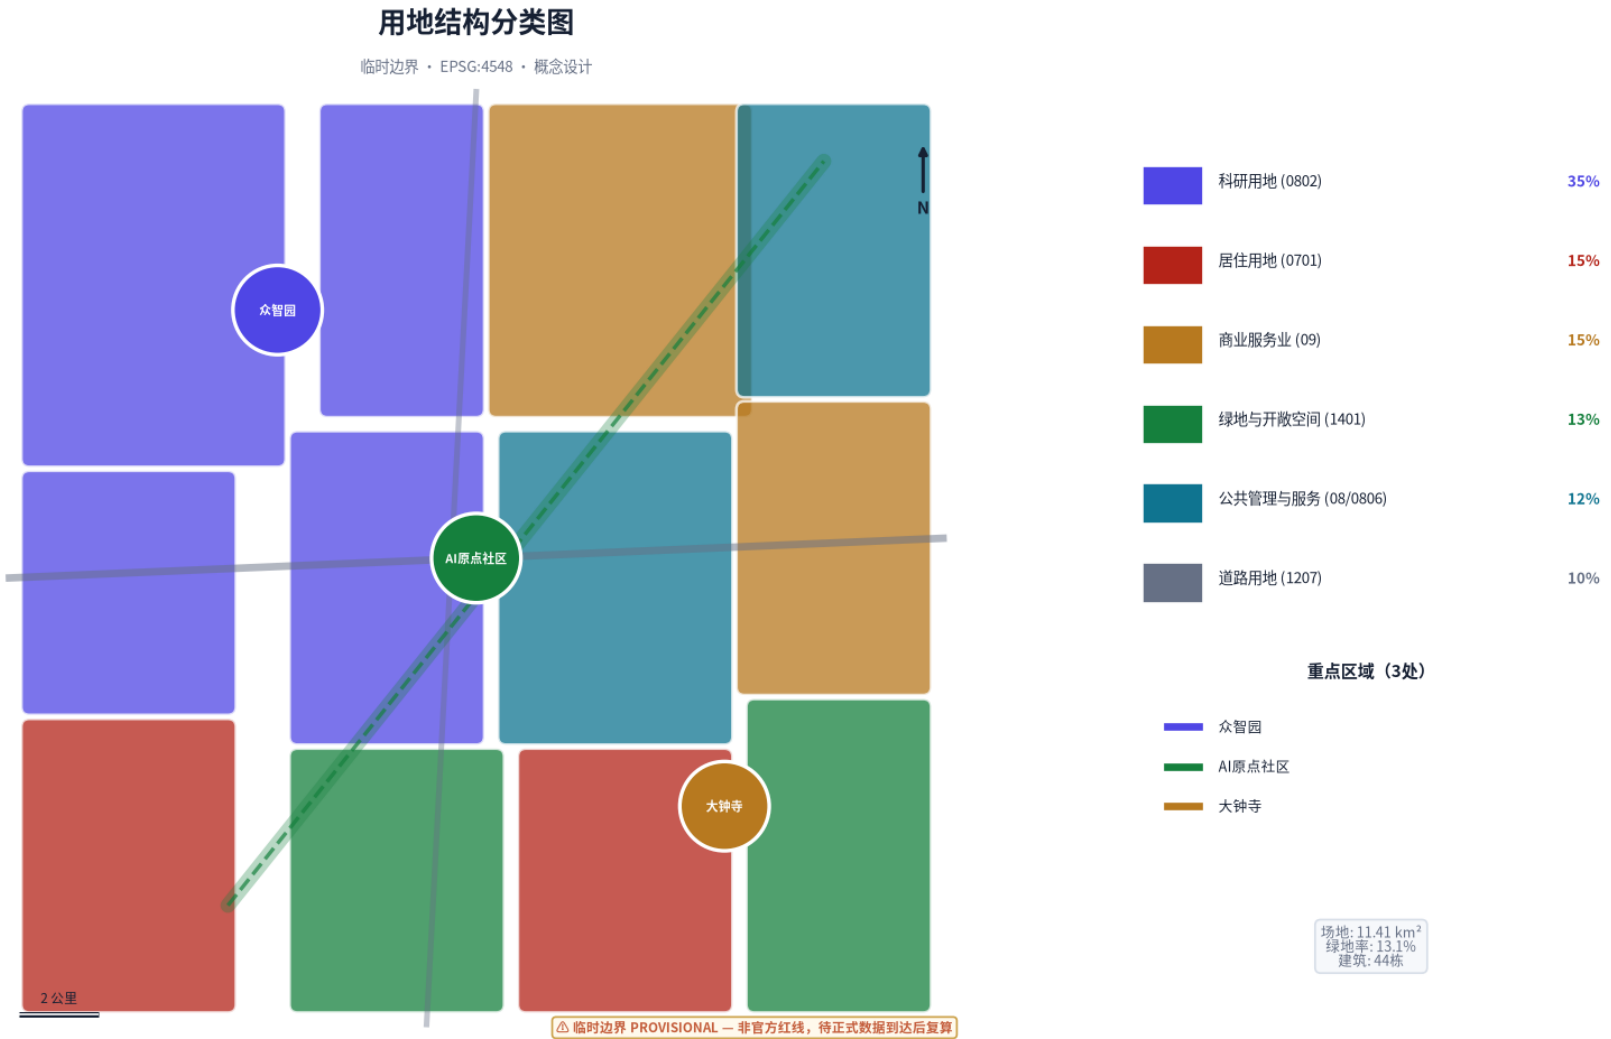

用地分配（临时边界）

- 科研(35%) | 商业(15%) | 绿地(13%) | 居住(15%) | 公共服务(12%) | 道路(10%)
- 三层范围：统筹研究43.6 km² | 总体设计11.4 km² | 重点区域368.4 ha
- 容积率和建筑高度：未知 — 待官方控规条件发布。


三个重点区详细空间关系

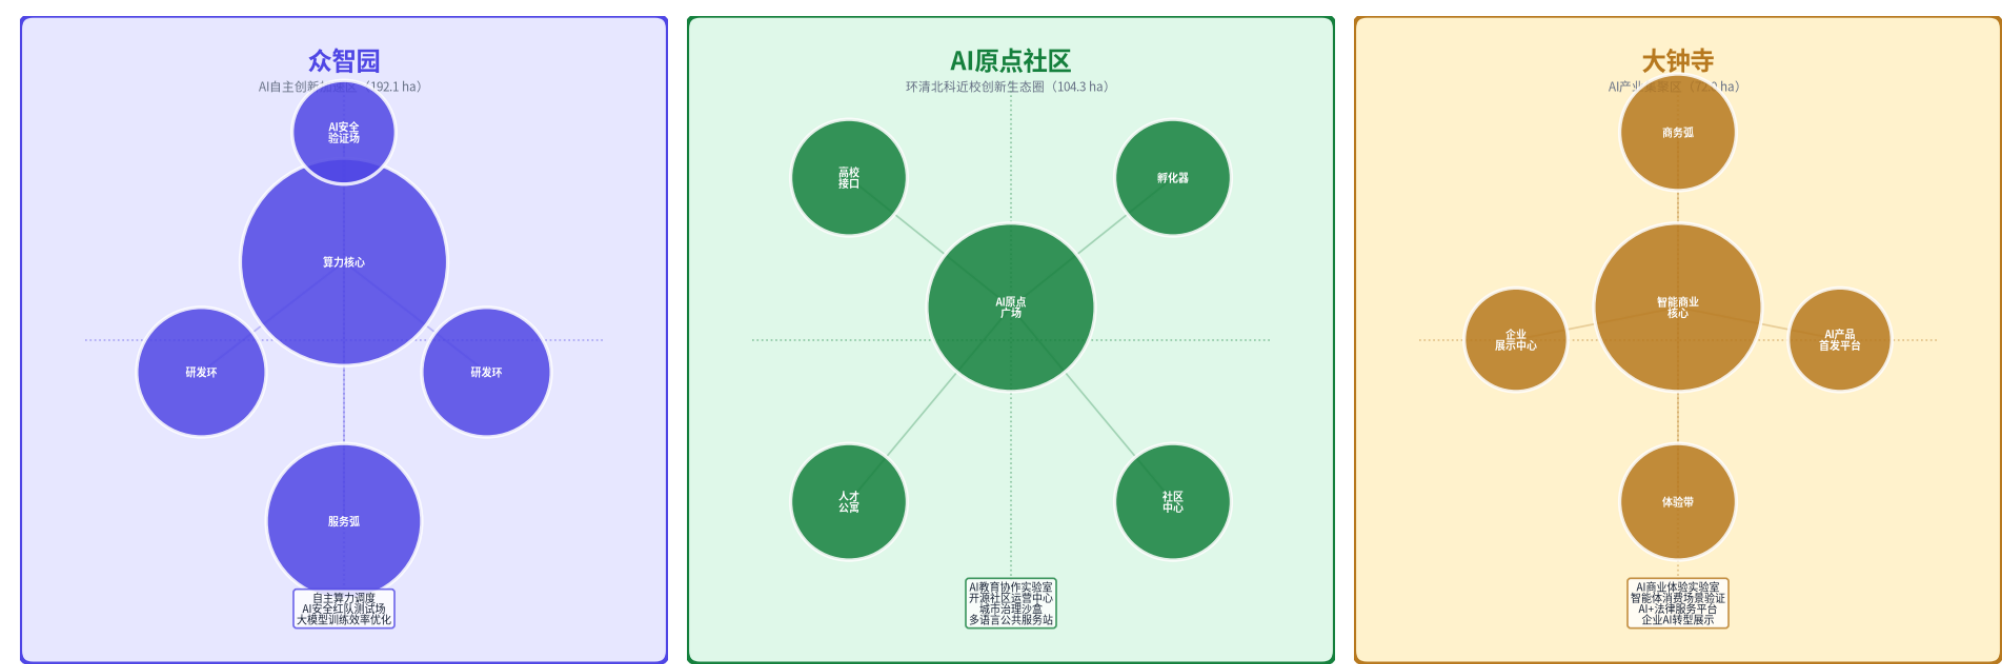

△ 临时边界 PROVISIONAL — 非官方红线，待正式数据到达后复算

三个核心片区

- 众智园（192.1 ha）：AI全栈自主创新。算力核心+研发环+服务弧。
- AI原点社区（104.3 ha）：近校创新生态圈。一芯一圈双轴。
- 大钟寺（72.0 ha）：智能原生消费商务。商业芯+商务弧+体验带。

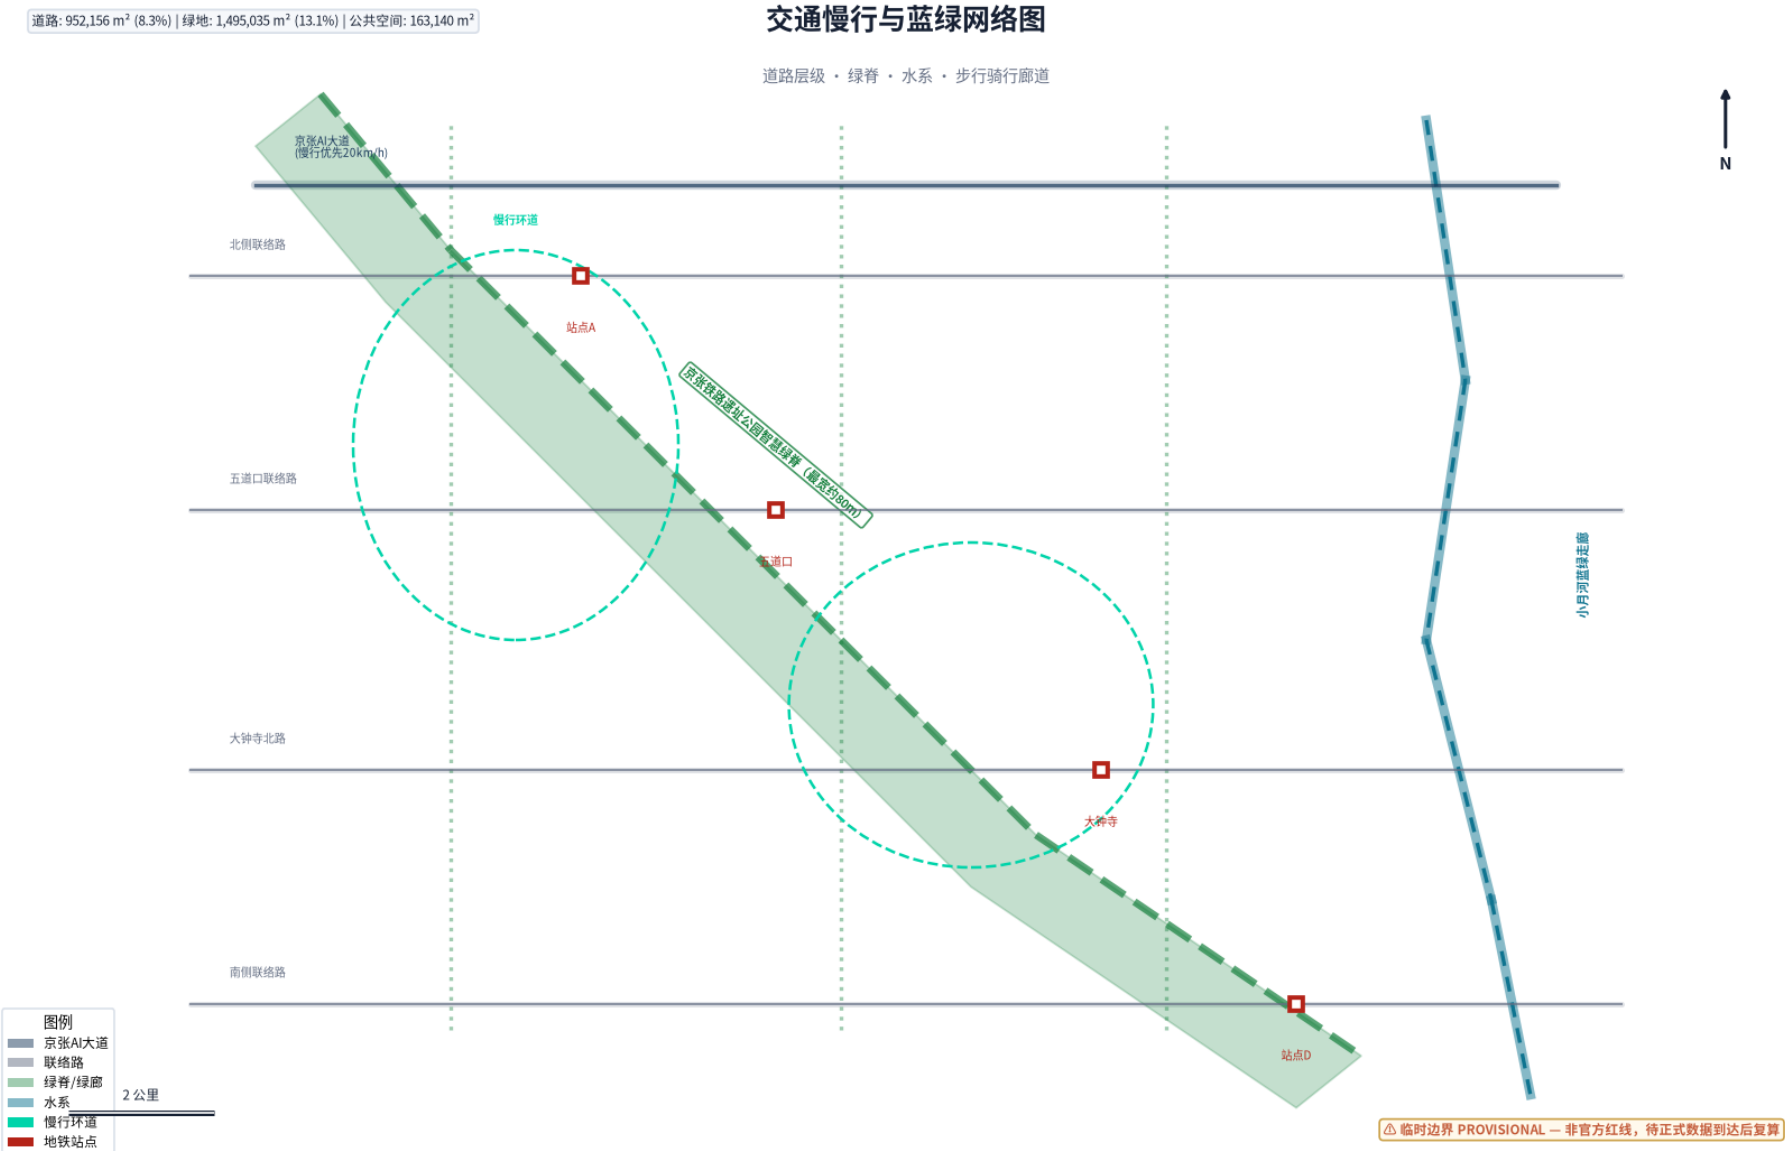

基础设施网络

- 道路：一纵（京张AI大道，20km/h慢行优先）+四横联络路+两环。
- 绿地：一脊（最宽约80m）+三廊+多节点。绿地率13.1%。
- 公共空间：4个核心节点。沿绿脊设5个AI朝圣地标。

核心指标 — 证据链与复算触发条件

EPSG:4548，从提交GeoJSON计算，临时边界

指标	数值	公式	置信度	复算触发条件
场地面积	11,412,825.4 m²	<code>polygon_area(site_boundary)</code>	中	官方红线发布
绿地面积	1,495,034.6 m²	<code>sum(area(green_space))</code>	中	官方边界+用地确认
绿地率	0.131 (13.1%)	<code>green_area / site_area</code>	中	边界复算
公共空间	163,139.6 m²	<code>sum(area(public_space))</code>	中	官方边界+用地确认
公共空间率	0.0143 (1.43%)	<code>public_space / site_area</code>	中	边界复算
建筑基底	145,944.7 m²	<code>sum(area(buildings))</code>	低	建筑普查+控规条件
建筑密度	0.0128 (1.28%)	<code>footprint / site_area</code>	低	建筑普查+控规条件
建筑数量	44栋	<code>count(building_features)</code>	中	设计修订
重点区数量	3处	<code>count(key_area_features)</code>	高	不适用
道路面积	952,156.1 m²	<code>sum(buffer(centerline,w/2).area)</code>	低	官方道路红线

⚠ 临时性声明

⚠ 所有数值为临时设计模型量，基于仓库临时粗略边界计算。
这些数值不是官方面积主张。正式几何发布后必须复算。
所有公式使用投影坐标系EPSG:4548（CGCS2000 / 3度高斯-克吕格 CM 117E）。

来源文件: geometry/site_boundary.geojson, geometry/green_space.geojson, geometry/public_space.geojson, geometry/buildings.geojson, geometry/roads.geojson

12个AI场景卡（*为产业测试验证）

- 1.交通微循控 | 2.企业服务副驾 | 3.医疗验证走廊
- 4.教育校园实验室 | 5.公共空间装置 | 6.安全红队*
- 7.能源微网* | 8.治理沙盒 | 9.智能体消费*
- 10.多语言服务站 | 11.开源协作中心 | 12.文化叙事引擎
- 所有场景：不使用人脸识别，数据匿名化，人工复核，测试明确标注。

三期实施（概念建议）

- 一期（2026-2028）：建议试点——绿脊示范段、众智园启动区、首批3个AI场景。

• 二期（2028-2030）：建议拓展——原点社区、8+场景、共创节。

• 三期（2030-2035）：建议成熟——大钟寺、全部12场景、可复制标准。
- 合规声明：所有几何为临时边界。容积率/高度未知。所有建筑为概念量。

• 不使用人脸识别。须人工复核。本方案不构成法定规划或投资承诺。